


Room 1 overall plan

Wall shelving above worktables


Z-001

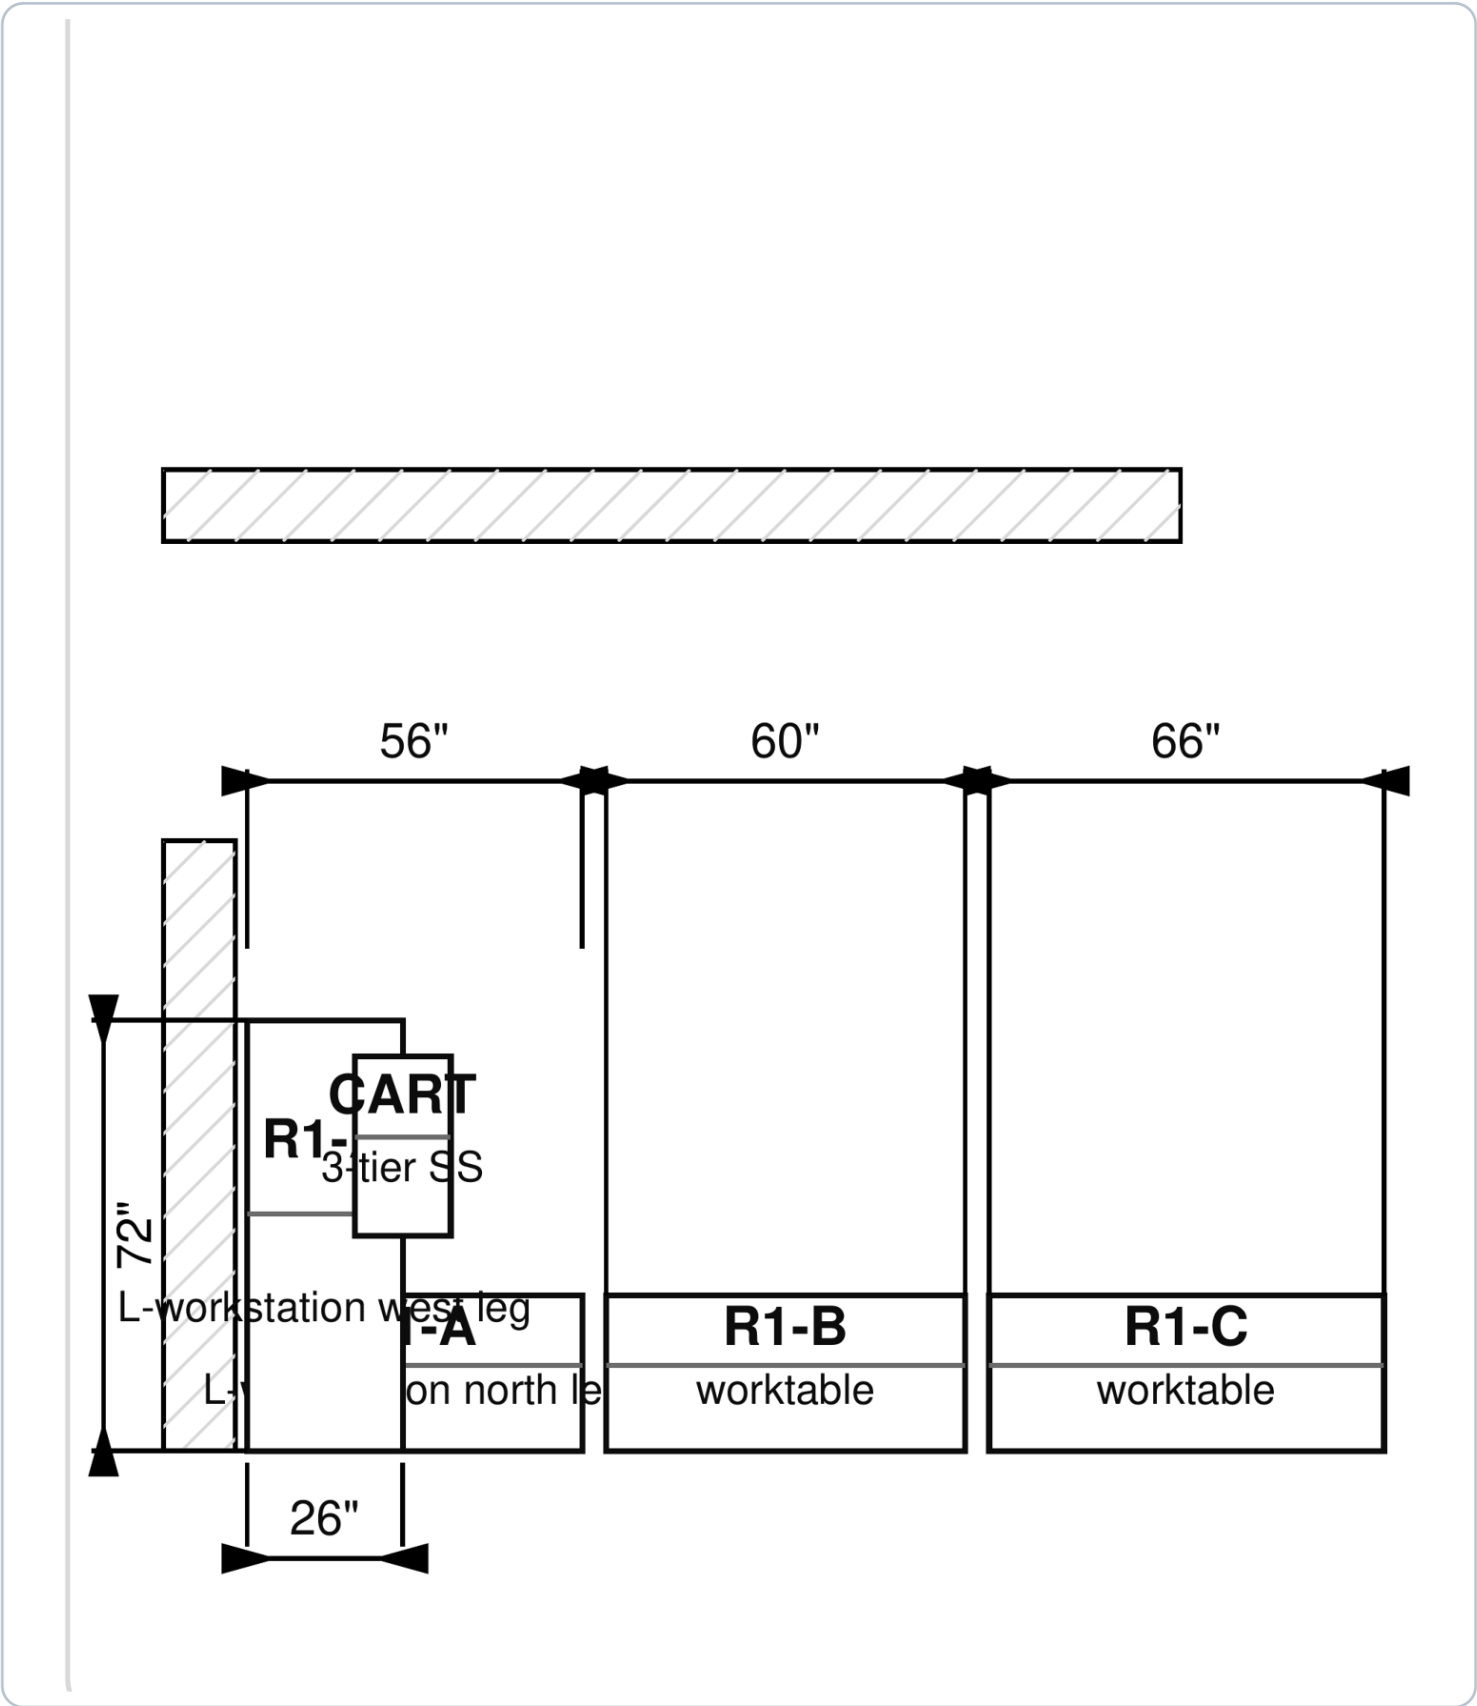

Room 2 overall plan

Fixed sink base, mobile station, support table, analyzer station


Z-002

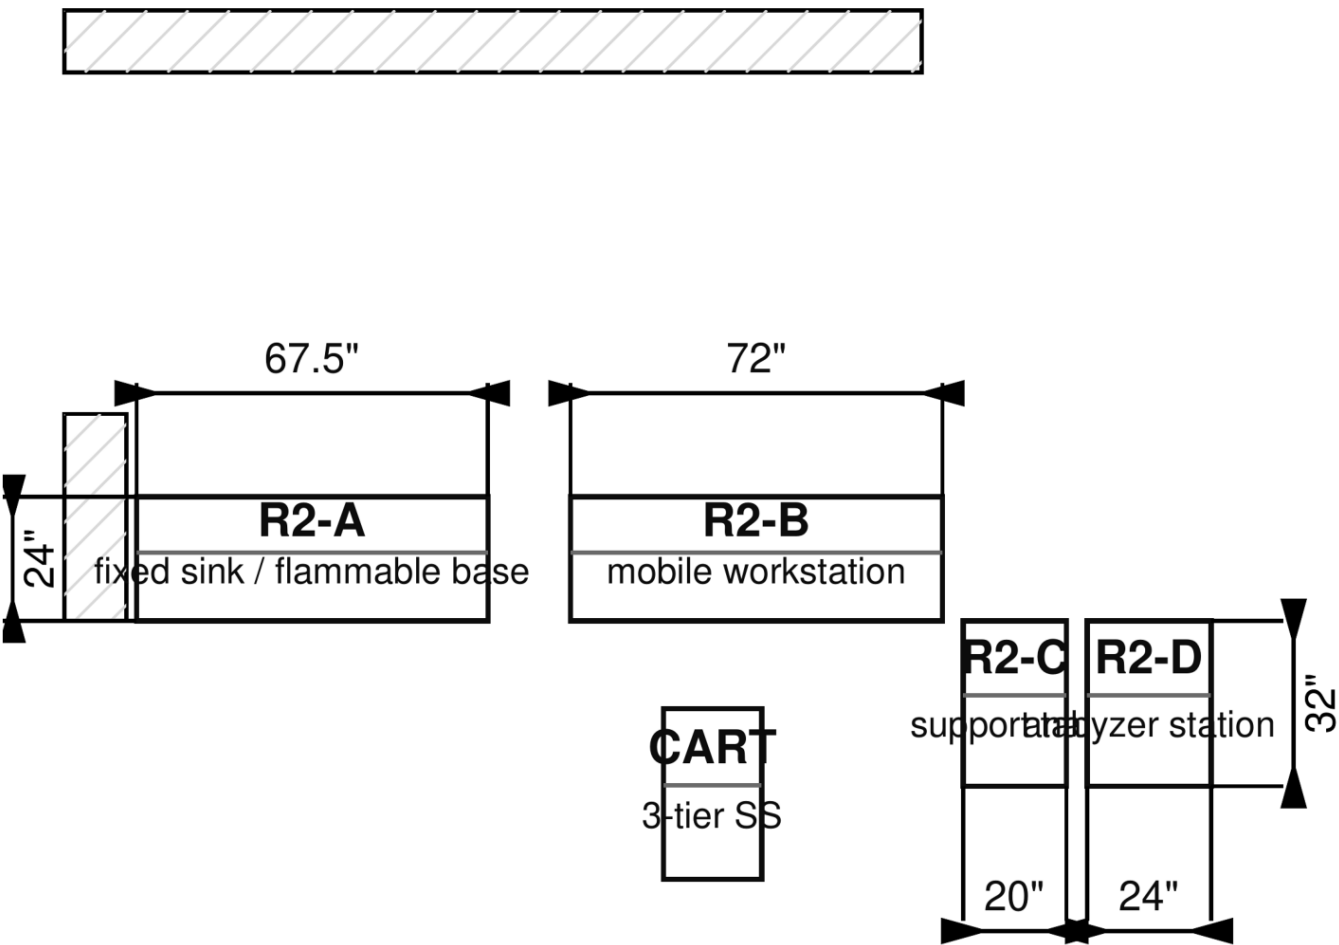

Room 3 overall plan

Two microscope benches and analyzer stand


Z-003

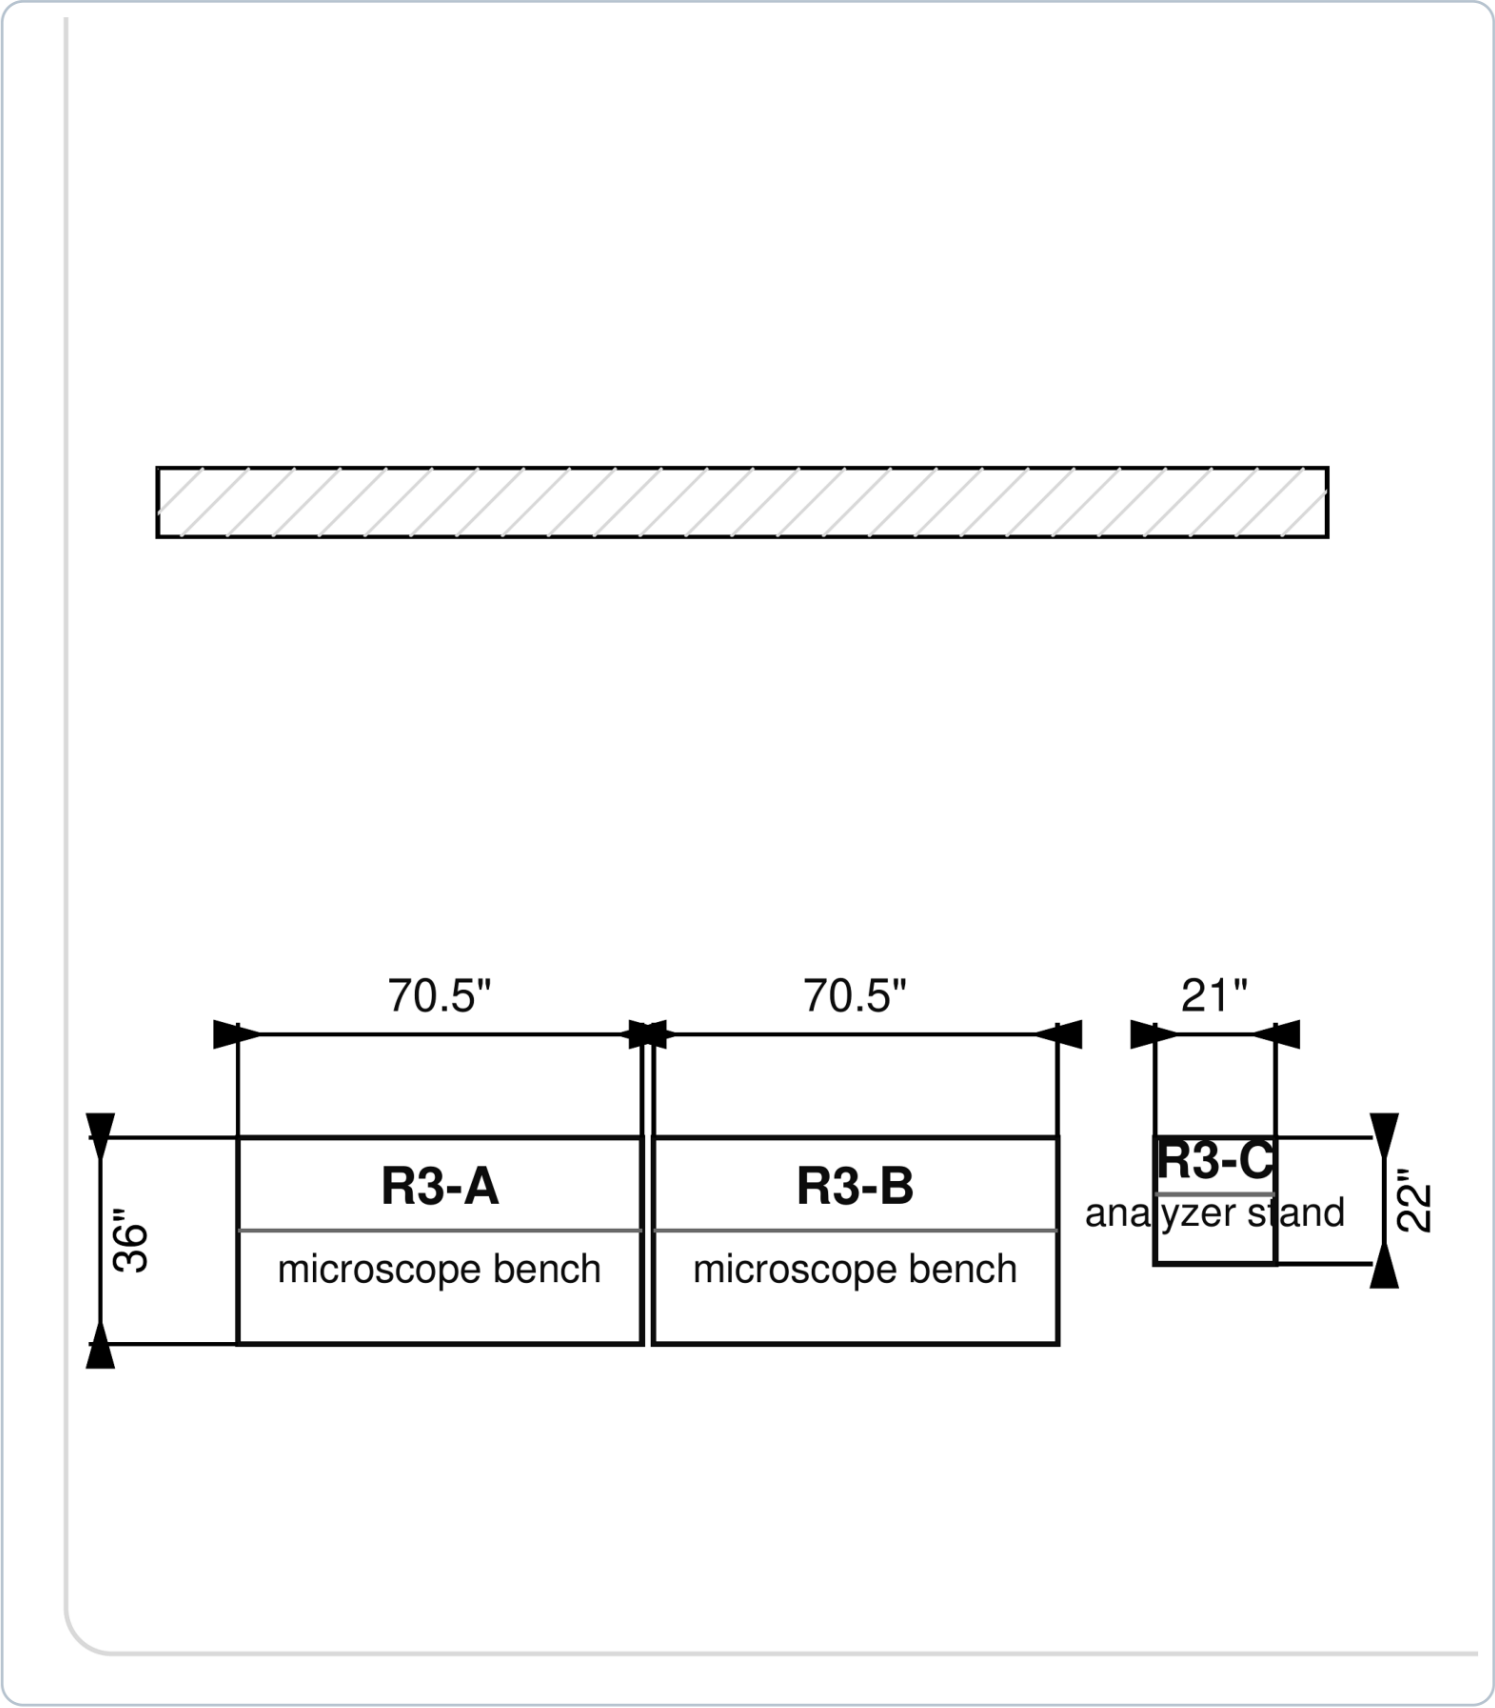

Room 4 overall plan

Main workstation and analyzer table


Z-004

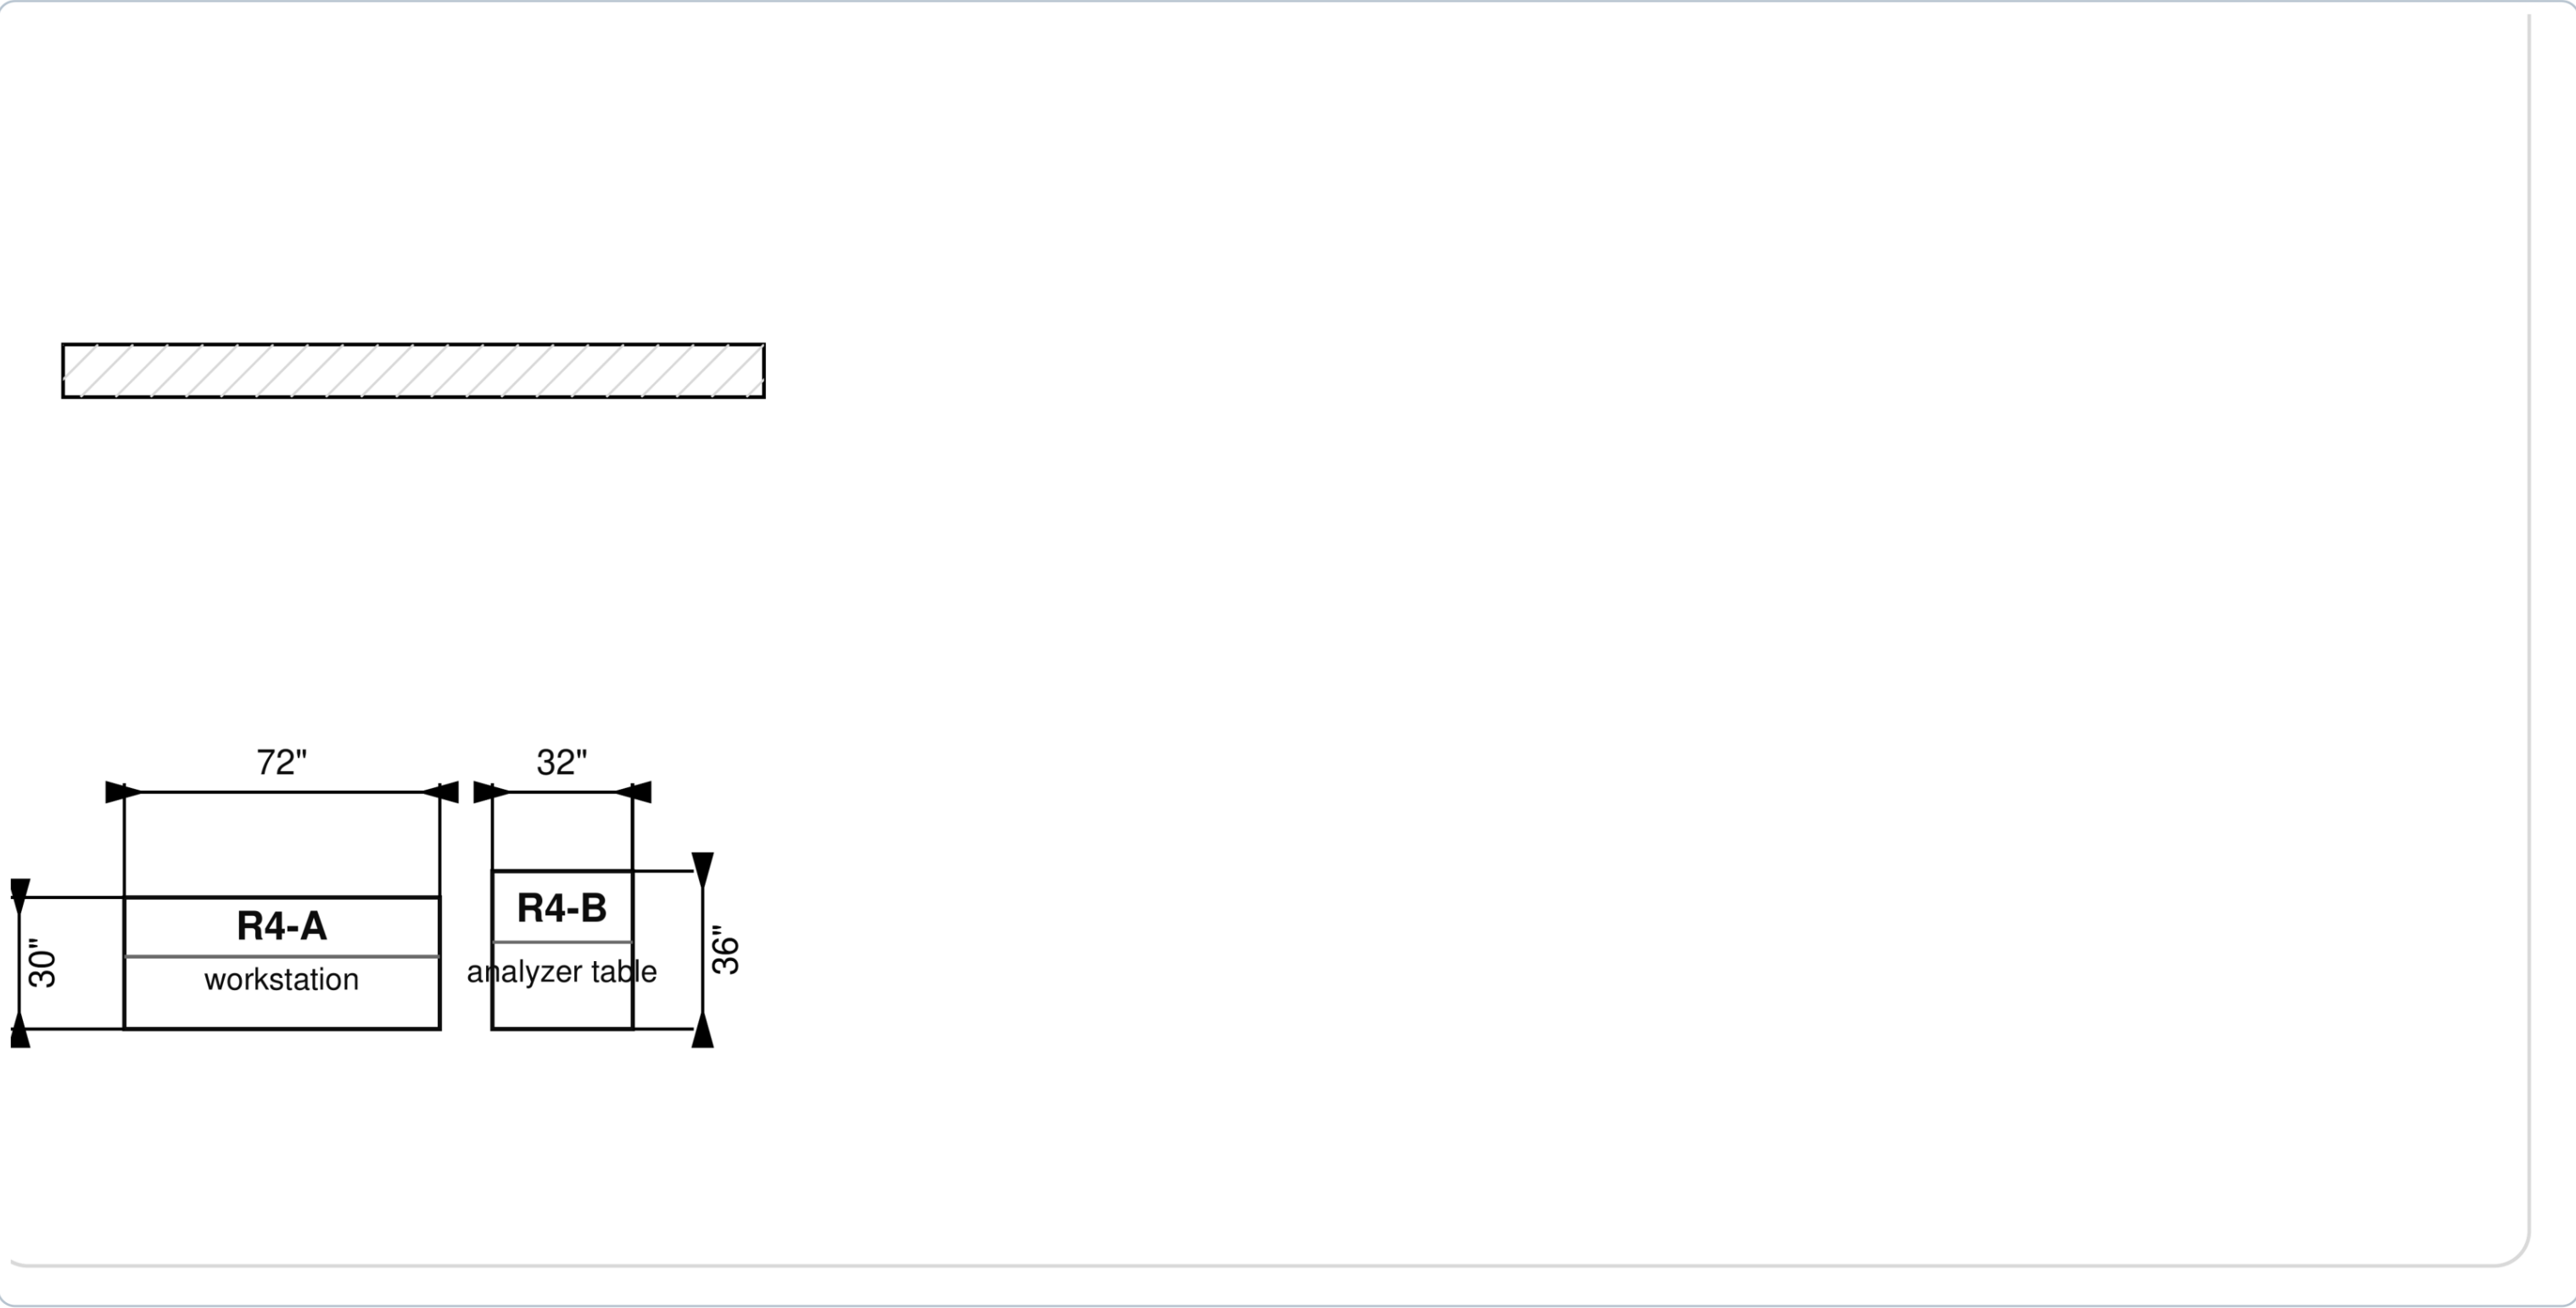

Detail 1 - Room 1 L workstation elevation

Approx. 56 in nominal run; 41 in work height


Z-005

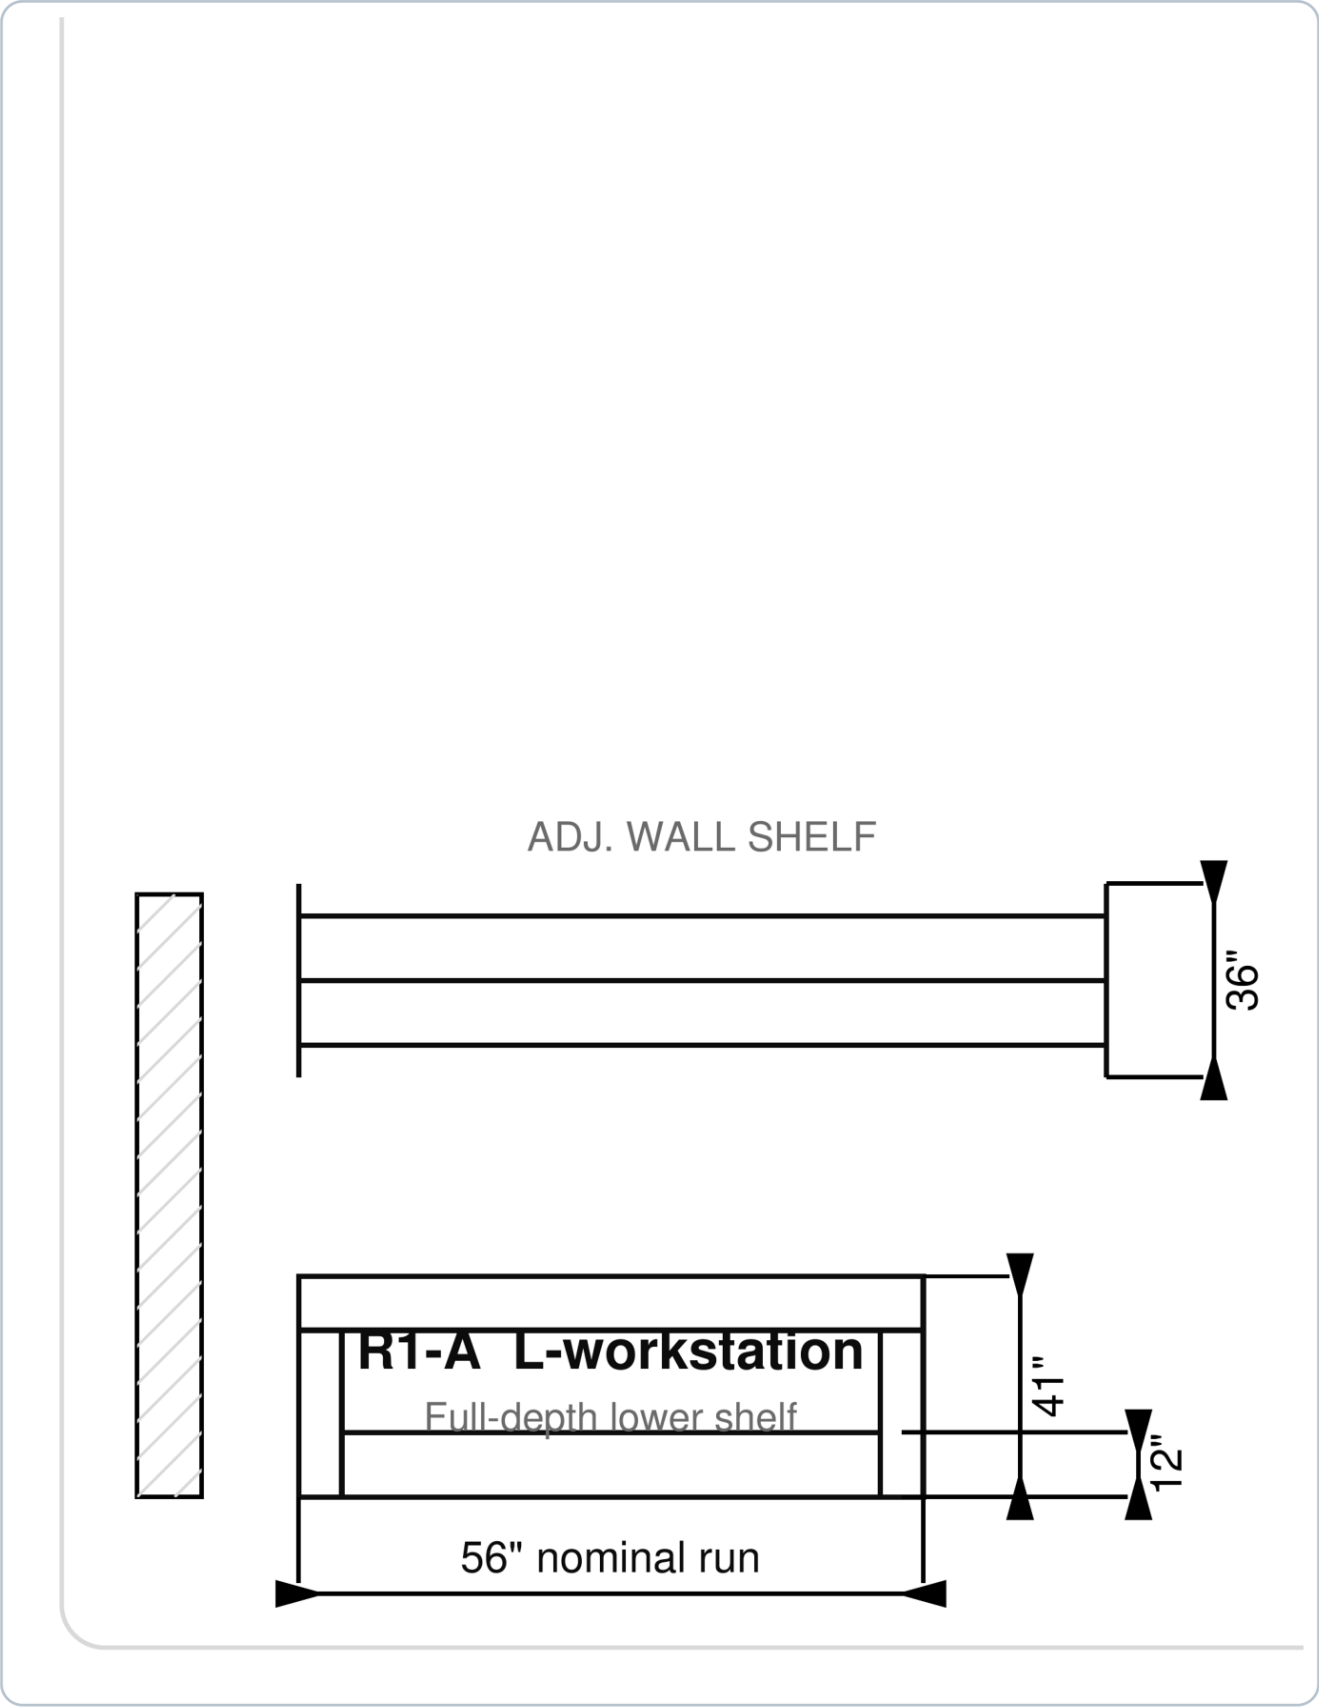

Detail 2 - Room 1 worktable elevation

Approx. 60 x 26; adjustable wall shelf above

Z-006

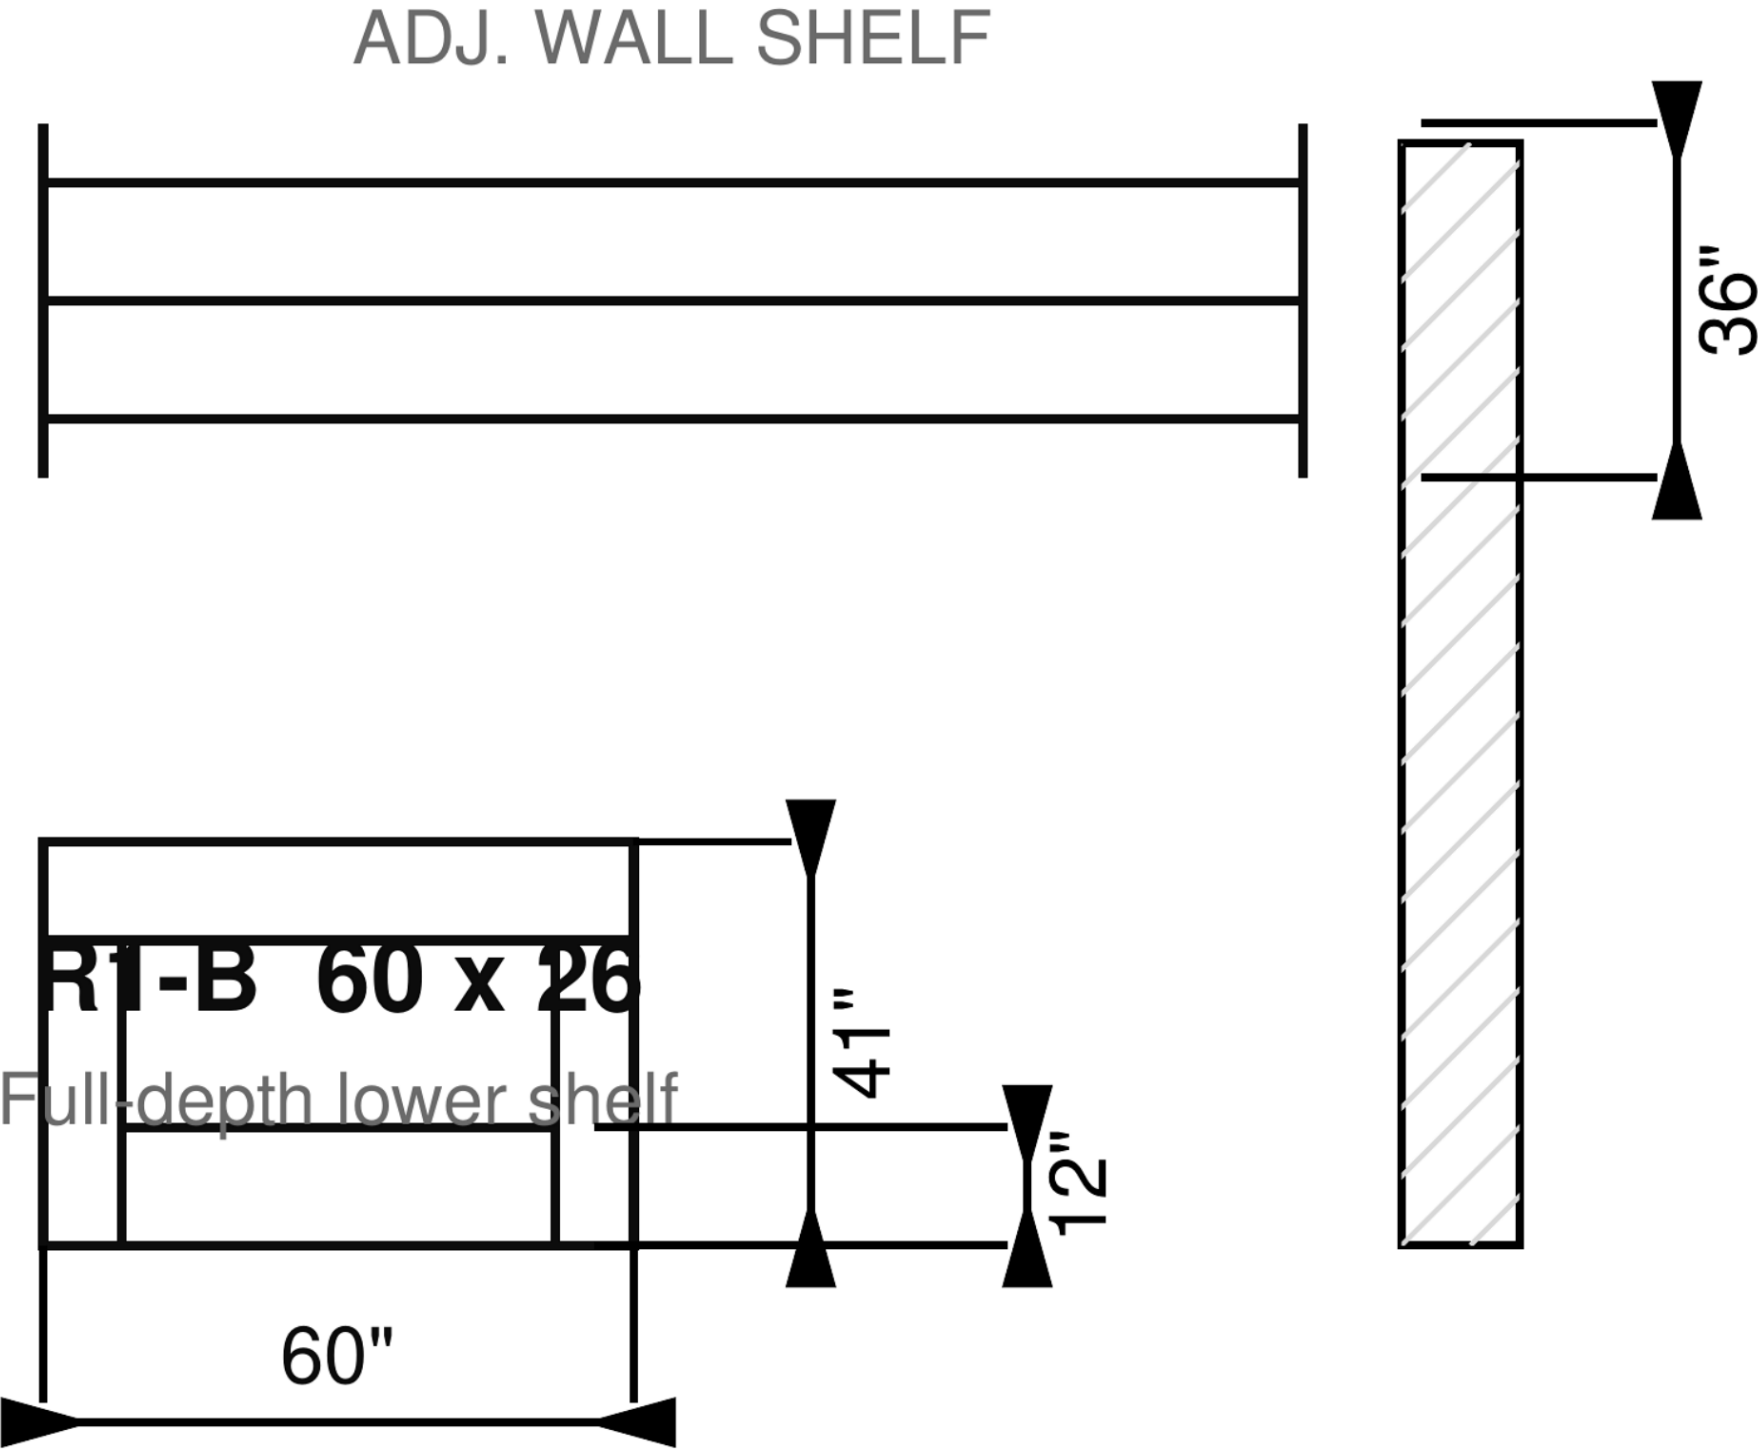




Detail 3 - Room 1 worktable elevation

Approx. 66 x 26; adjustable wall shelf above


Z-007

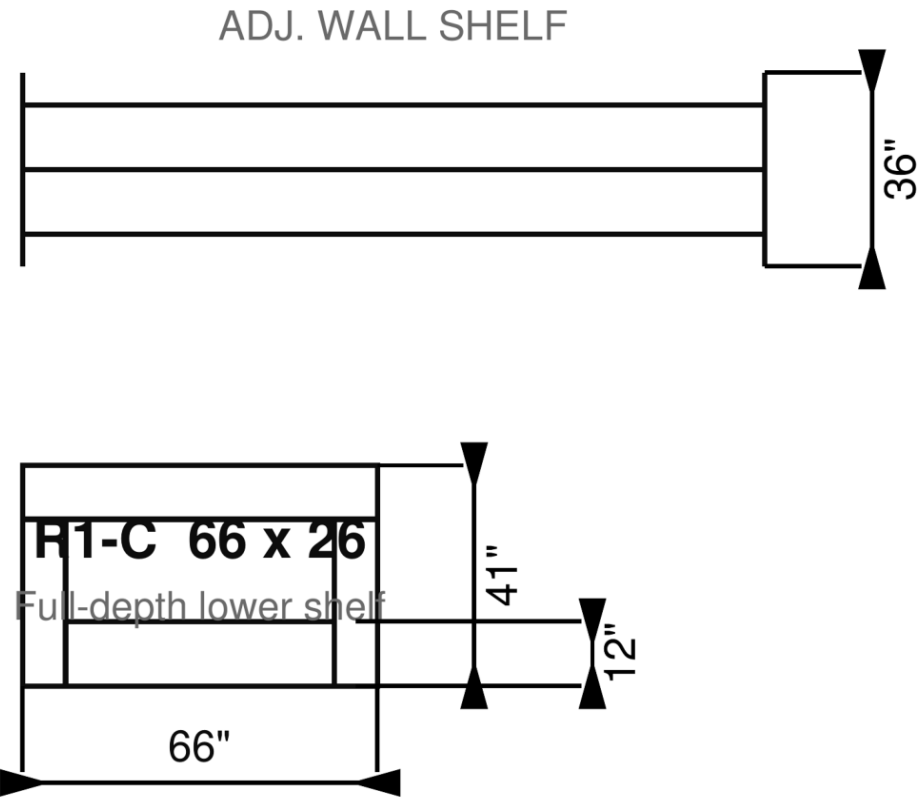

Detail 4 - Room 2 fixed sink / flammable base

Approx. 67.5 x 24 fixed casework with integral sink top

Z-008

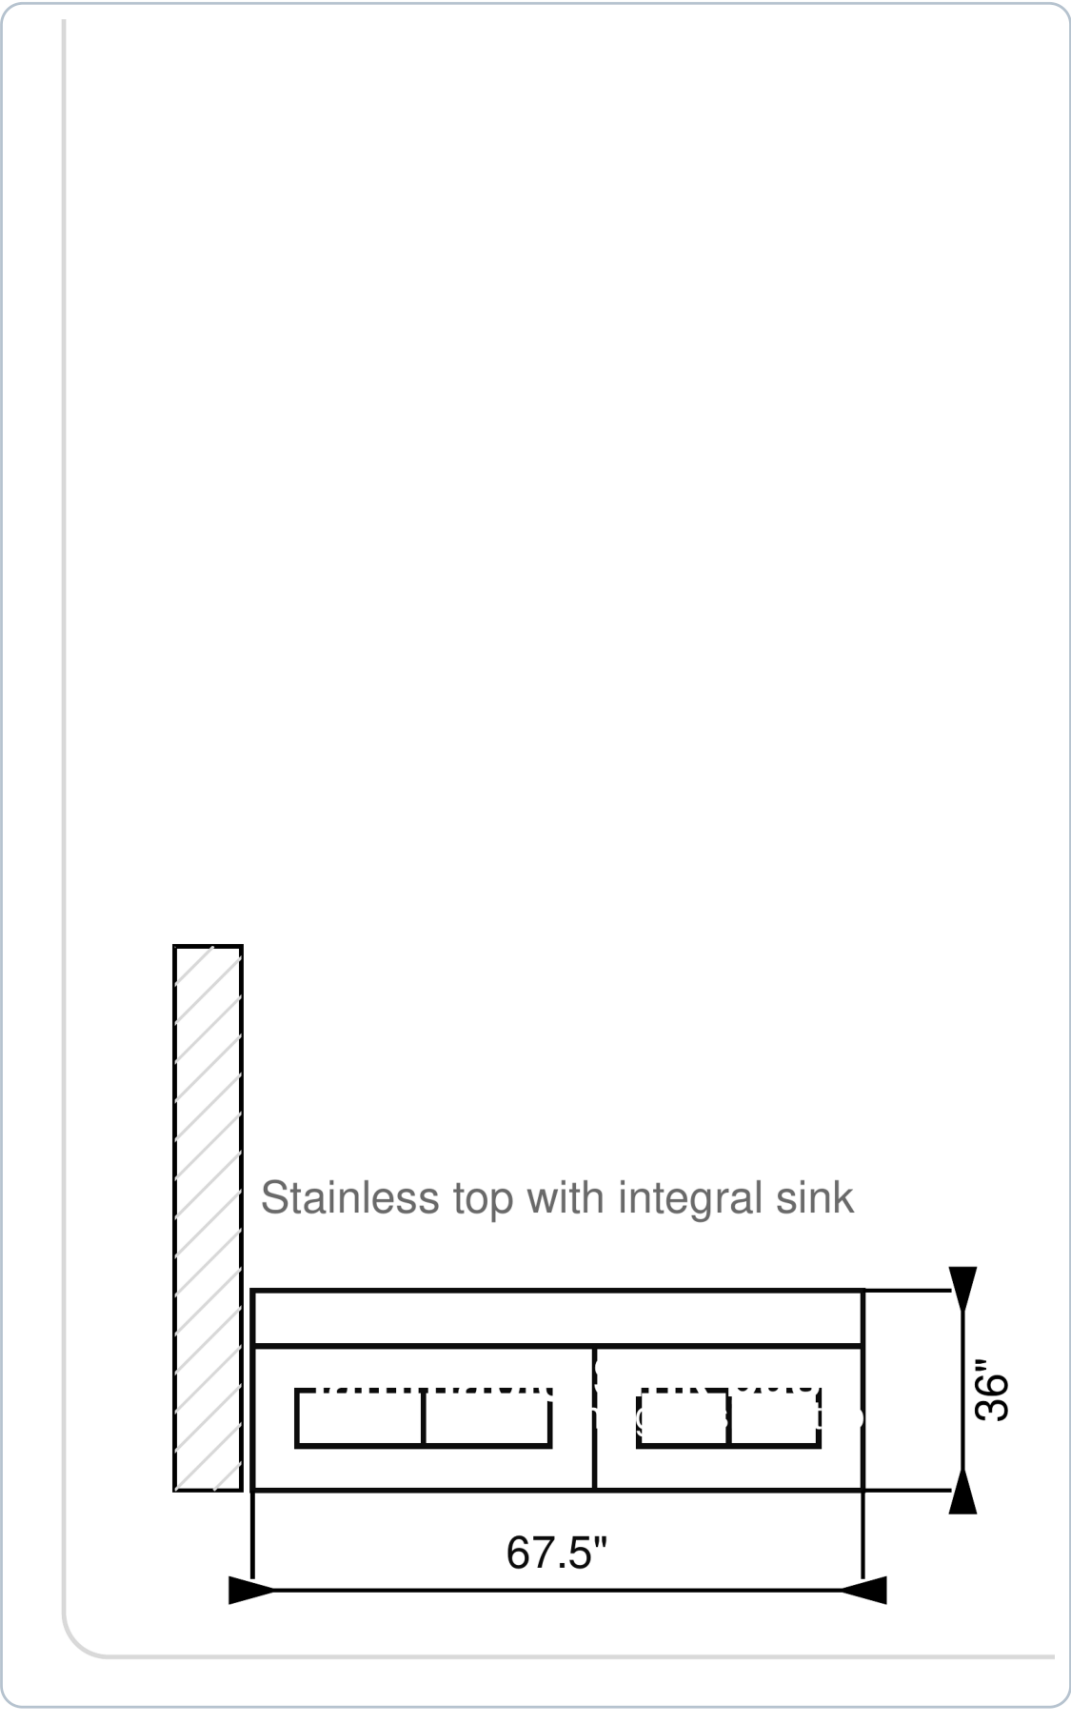




Detail 5 - Room 2 mobile workstation + support table

Approx. 72 x 24 plus 20 x 24 support table

Z-009


22" clear below keyboard tray below top

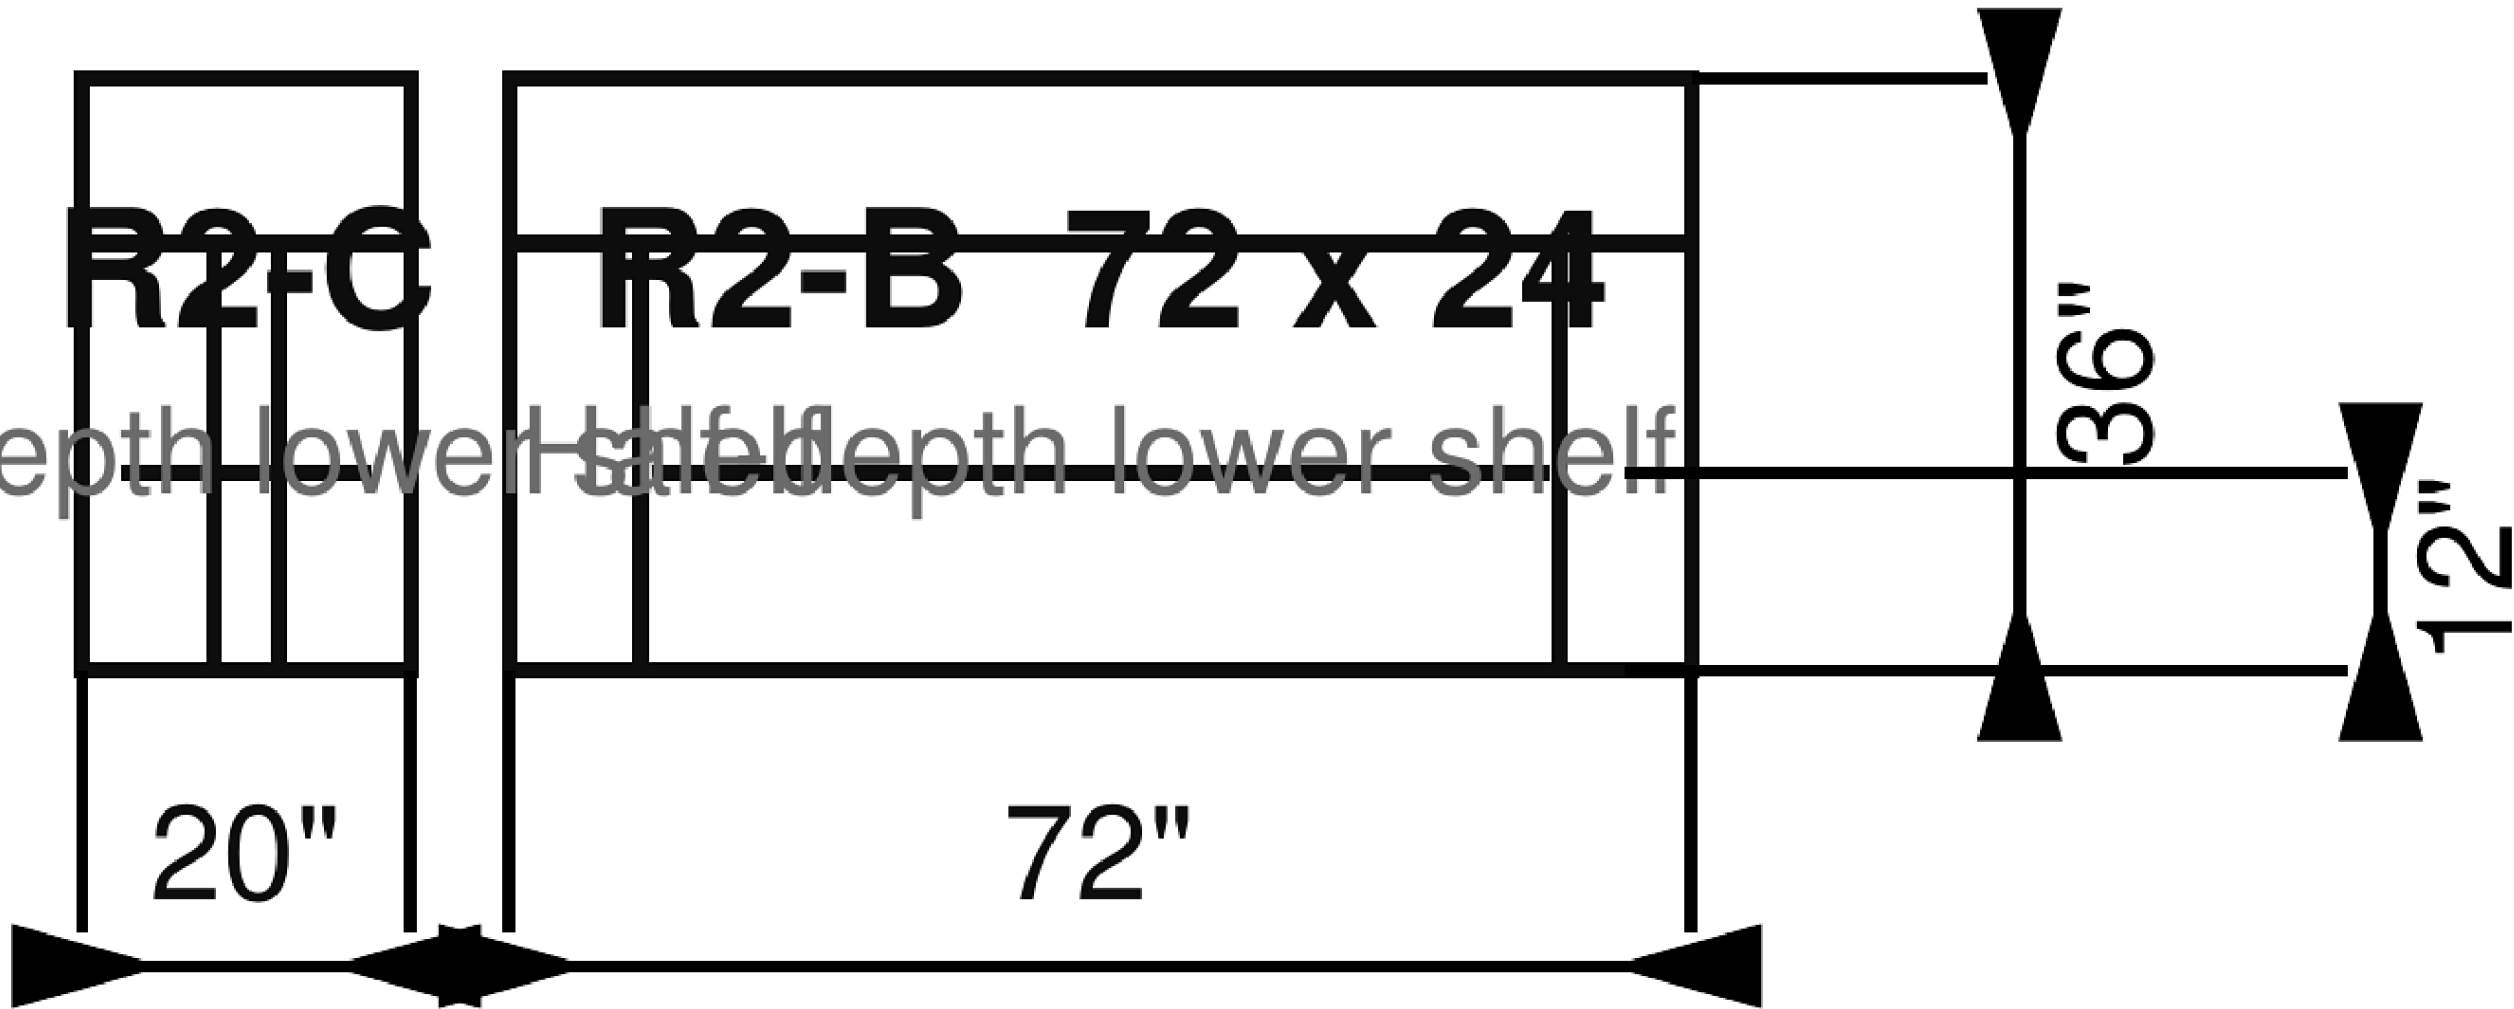

Detail 6 - Room 2 analyzer station

Approx. 24 x 24 x 49 with two lower shelves


Z-010

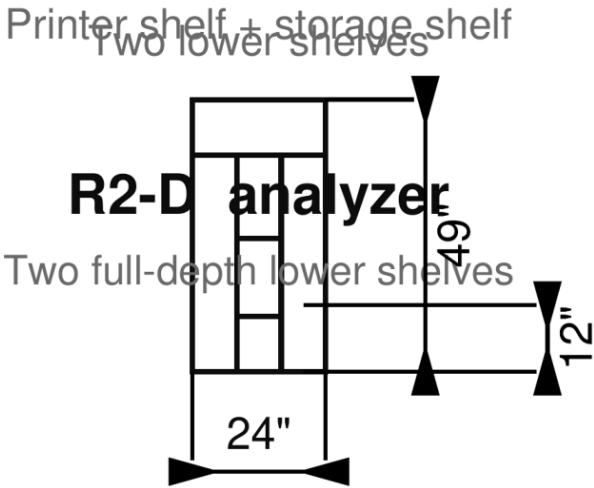


Detail 7 - Room 3 microscope bench elevation

Two 70 in benches shown as 141 in overall

Z-011

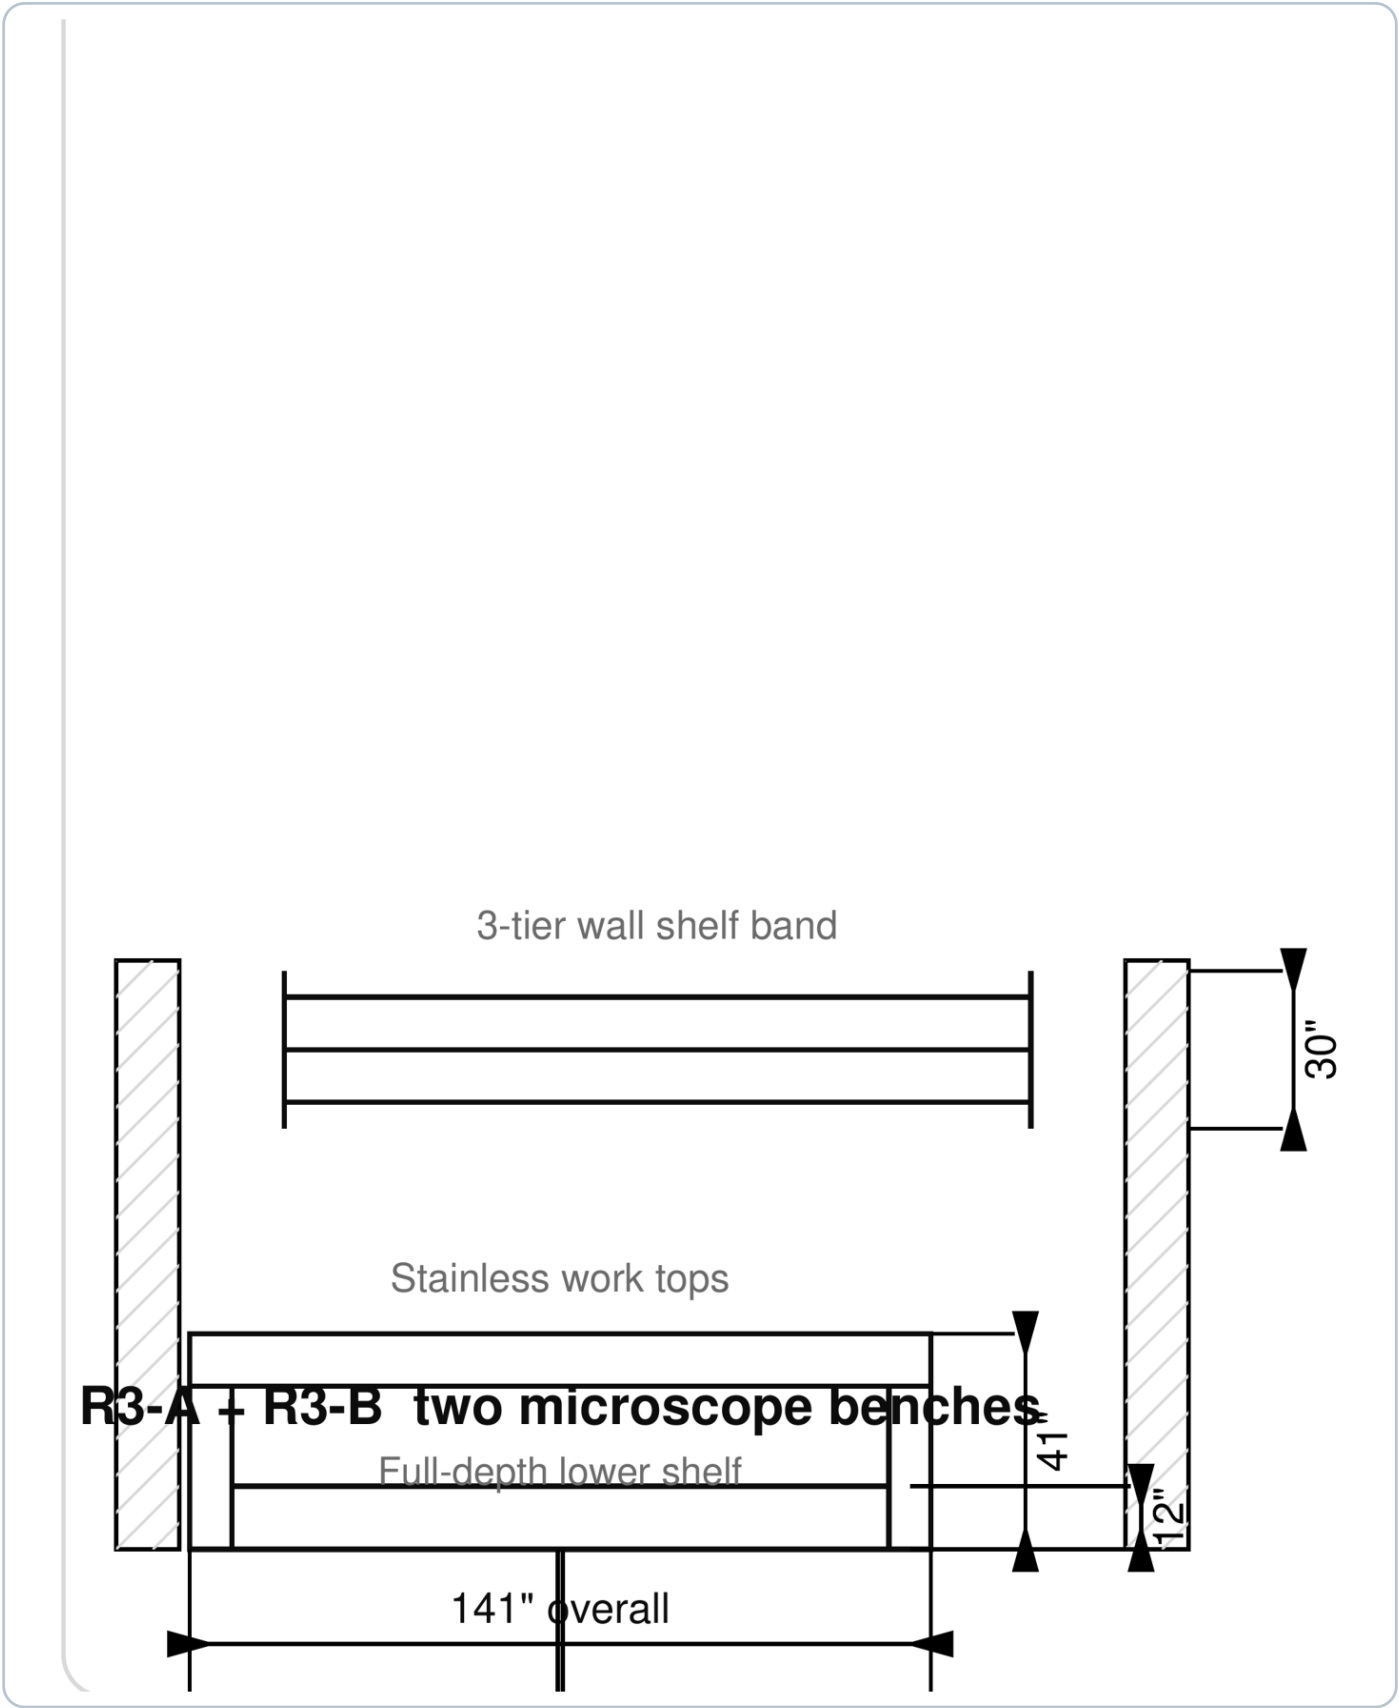


# Compact analyzer stand

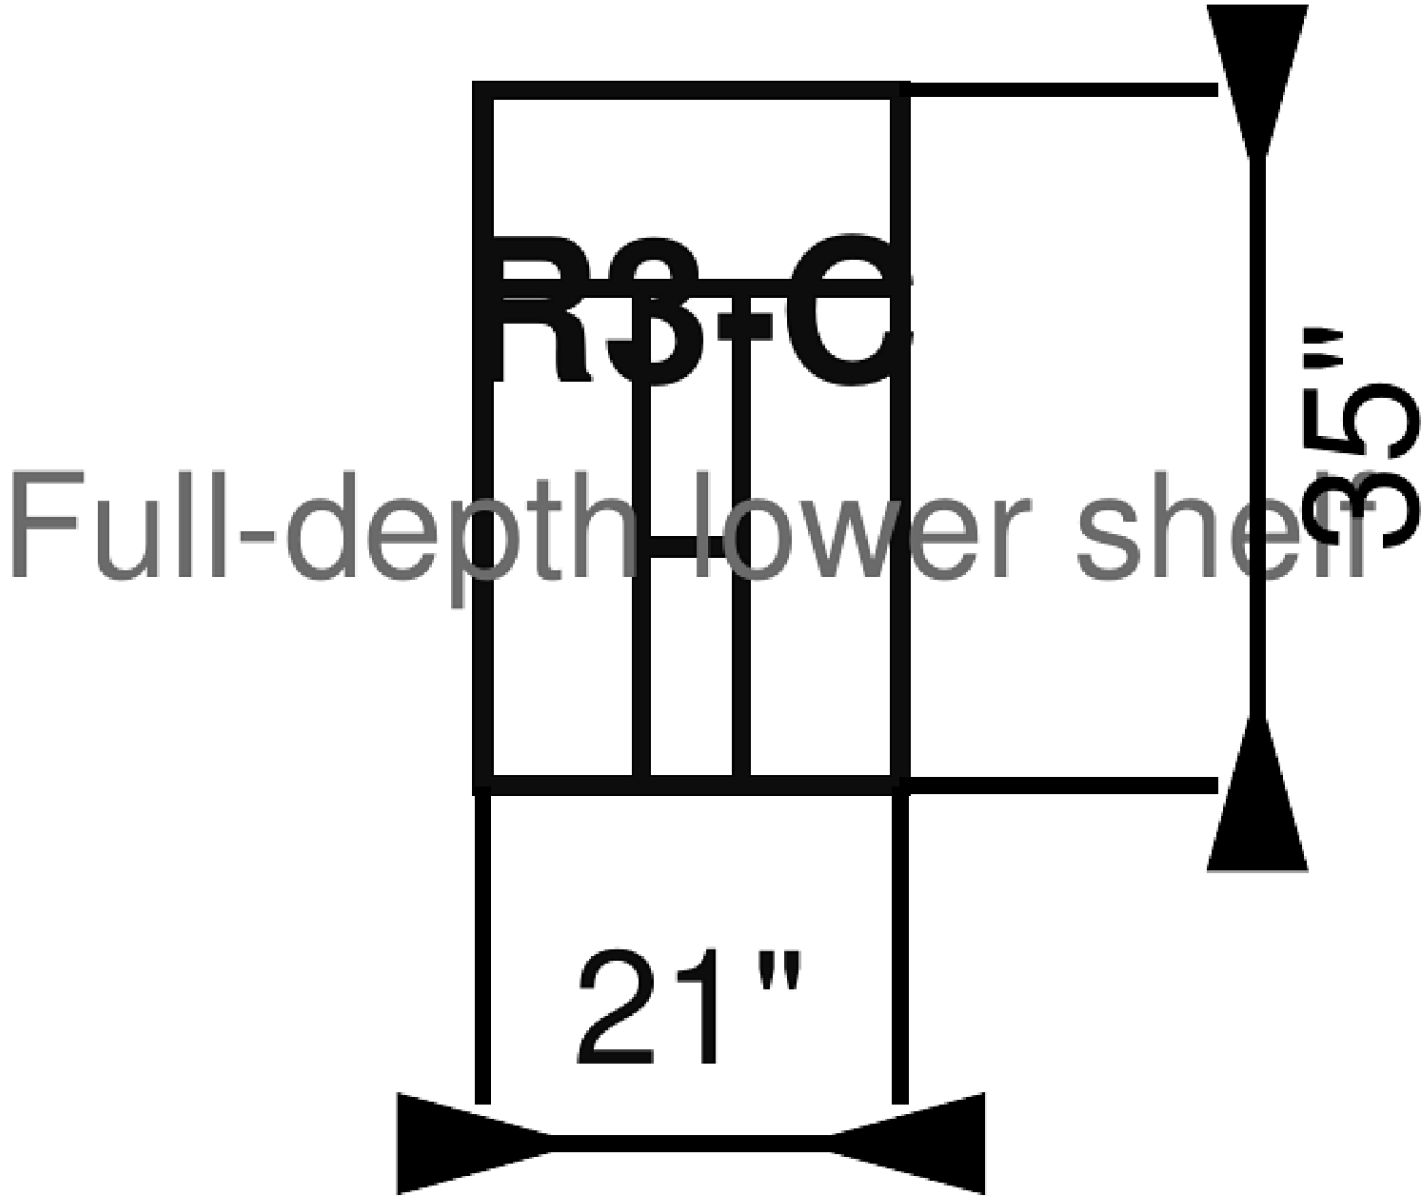

Detail 9 - Room 4 workstation elevation

Approx. 72 x 30 x 41 with wall shelf above

Z-013

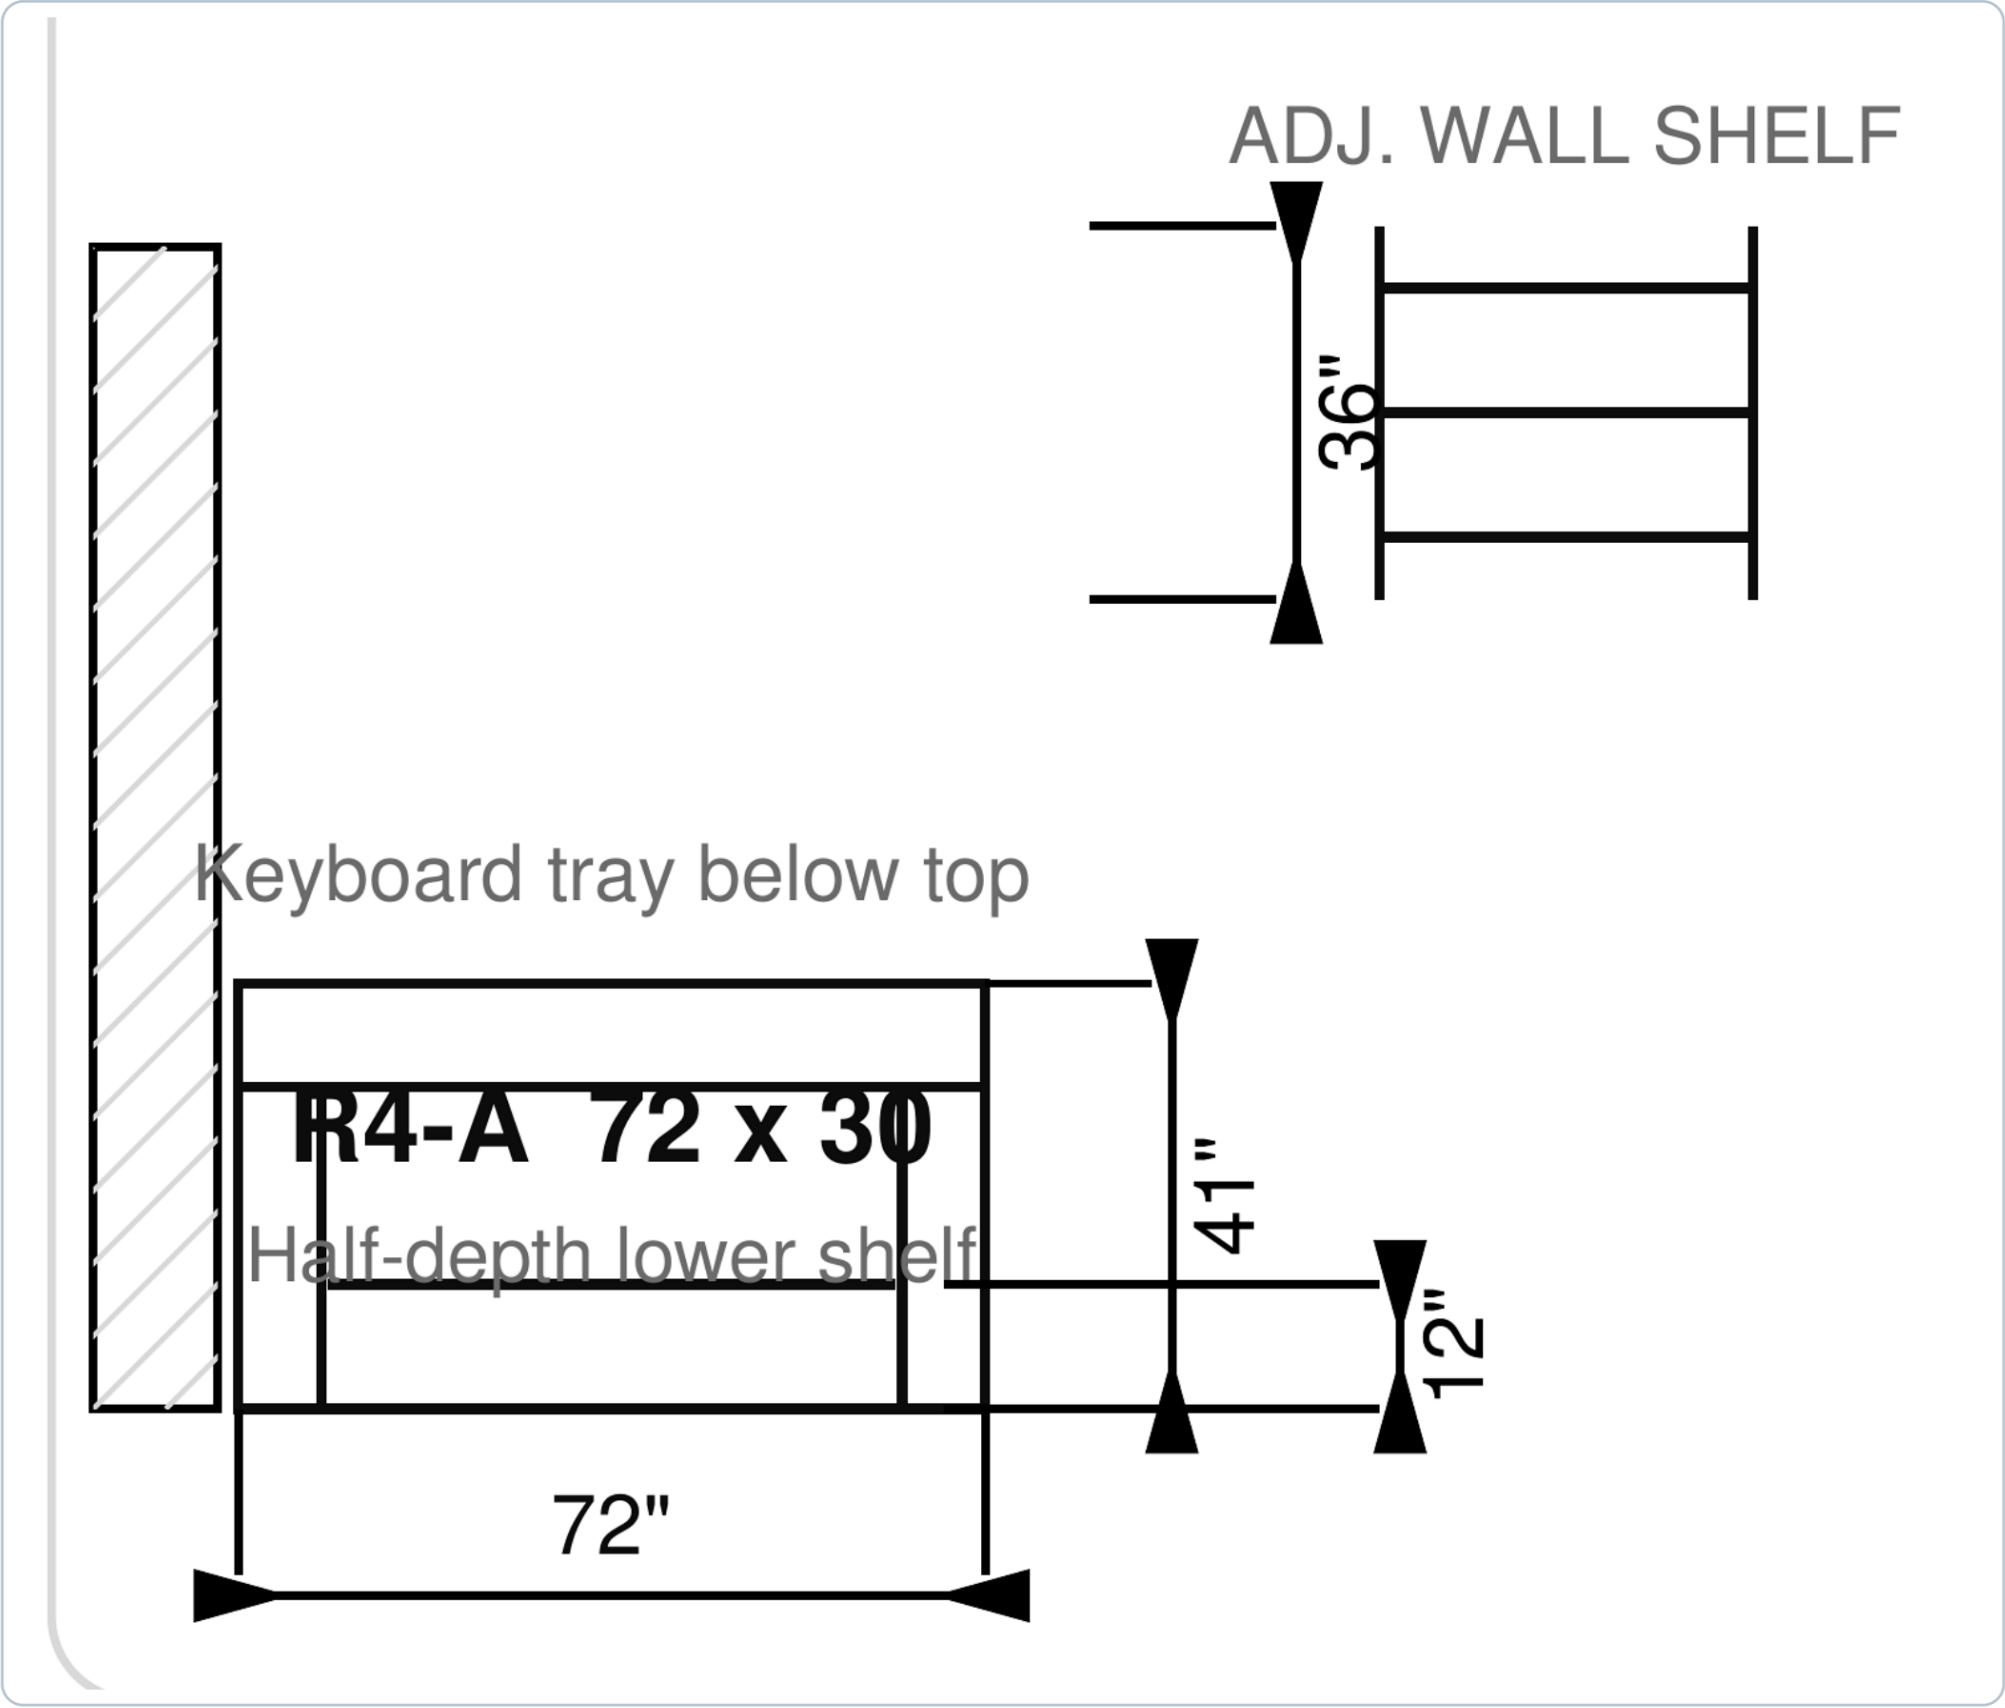

Keyboard tray below top

**R4-B 32 x 36**

Half-depth lower shelf

