


LEGEND

CONC.	=CONCRETE
ELEC.	=ELECTRIC
ELEV.	=ELEVATION
EX.	=EXISTING
R/W	=RIGHT-OF-WAY
SCD	=SEWER CLEAN OUT
IPF	=IRON PIPE FOUND
IRF	=IRON ROD FOUND
BM	=BENCHMARK
U	=UTILITY POLE (PP)
P	=PARKING METER (PM)
B	=BOLLARD
L	=LIGHT POLE (LP)
S	=STORM DRAIN MANHOLE (SDMH)
T	=TELEPHONE MANHOLE (TMH)
SM	=SANITARY MANHOLE (SMH)
EMH	=ELECTRIC MANHOLE (EMH)
GV	=GAS VALVE (GV)
WM	=WATER METER (WM)
GUY	=GUY
FH	=FIRE HYDRANT (FH)
WV	=WATER VALVE (WV)
SIGN	=SIGN
TELEPHONE PEDESTAL	=TELEPHONE PEDESTAL
MAILBOX	=MAILBOX
PUE	=PUBLIC UTILITY EASEMENT (PUE)
FO	=FIBER OPTIC
UG	=UNDERGROUND UTILITY
W	=WATER LINE
E	=UNDERGROUND ELECTRIC
S	=SEWER LINE
5	=NUMBER OF HANDICAP PARKING
6	=NUMBER OF REGULAR PARKING

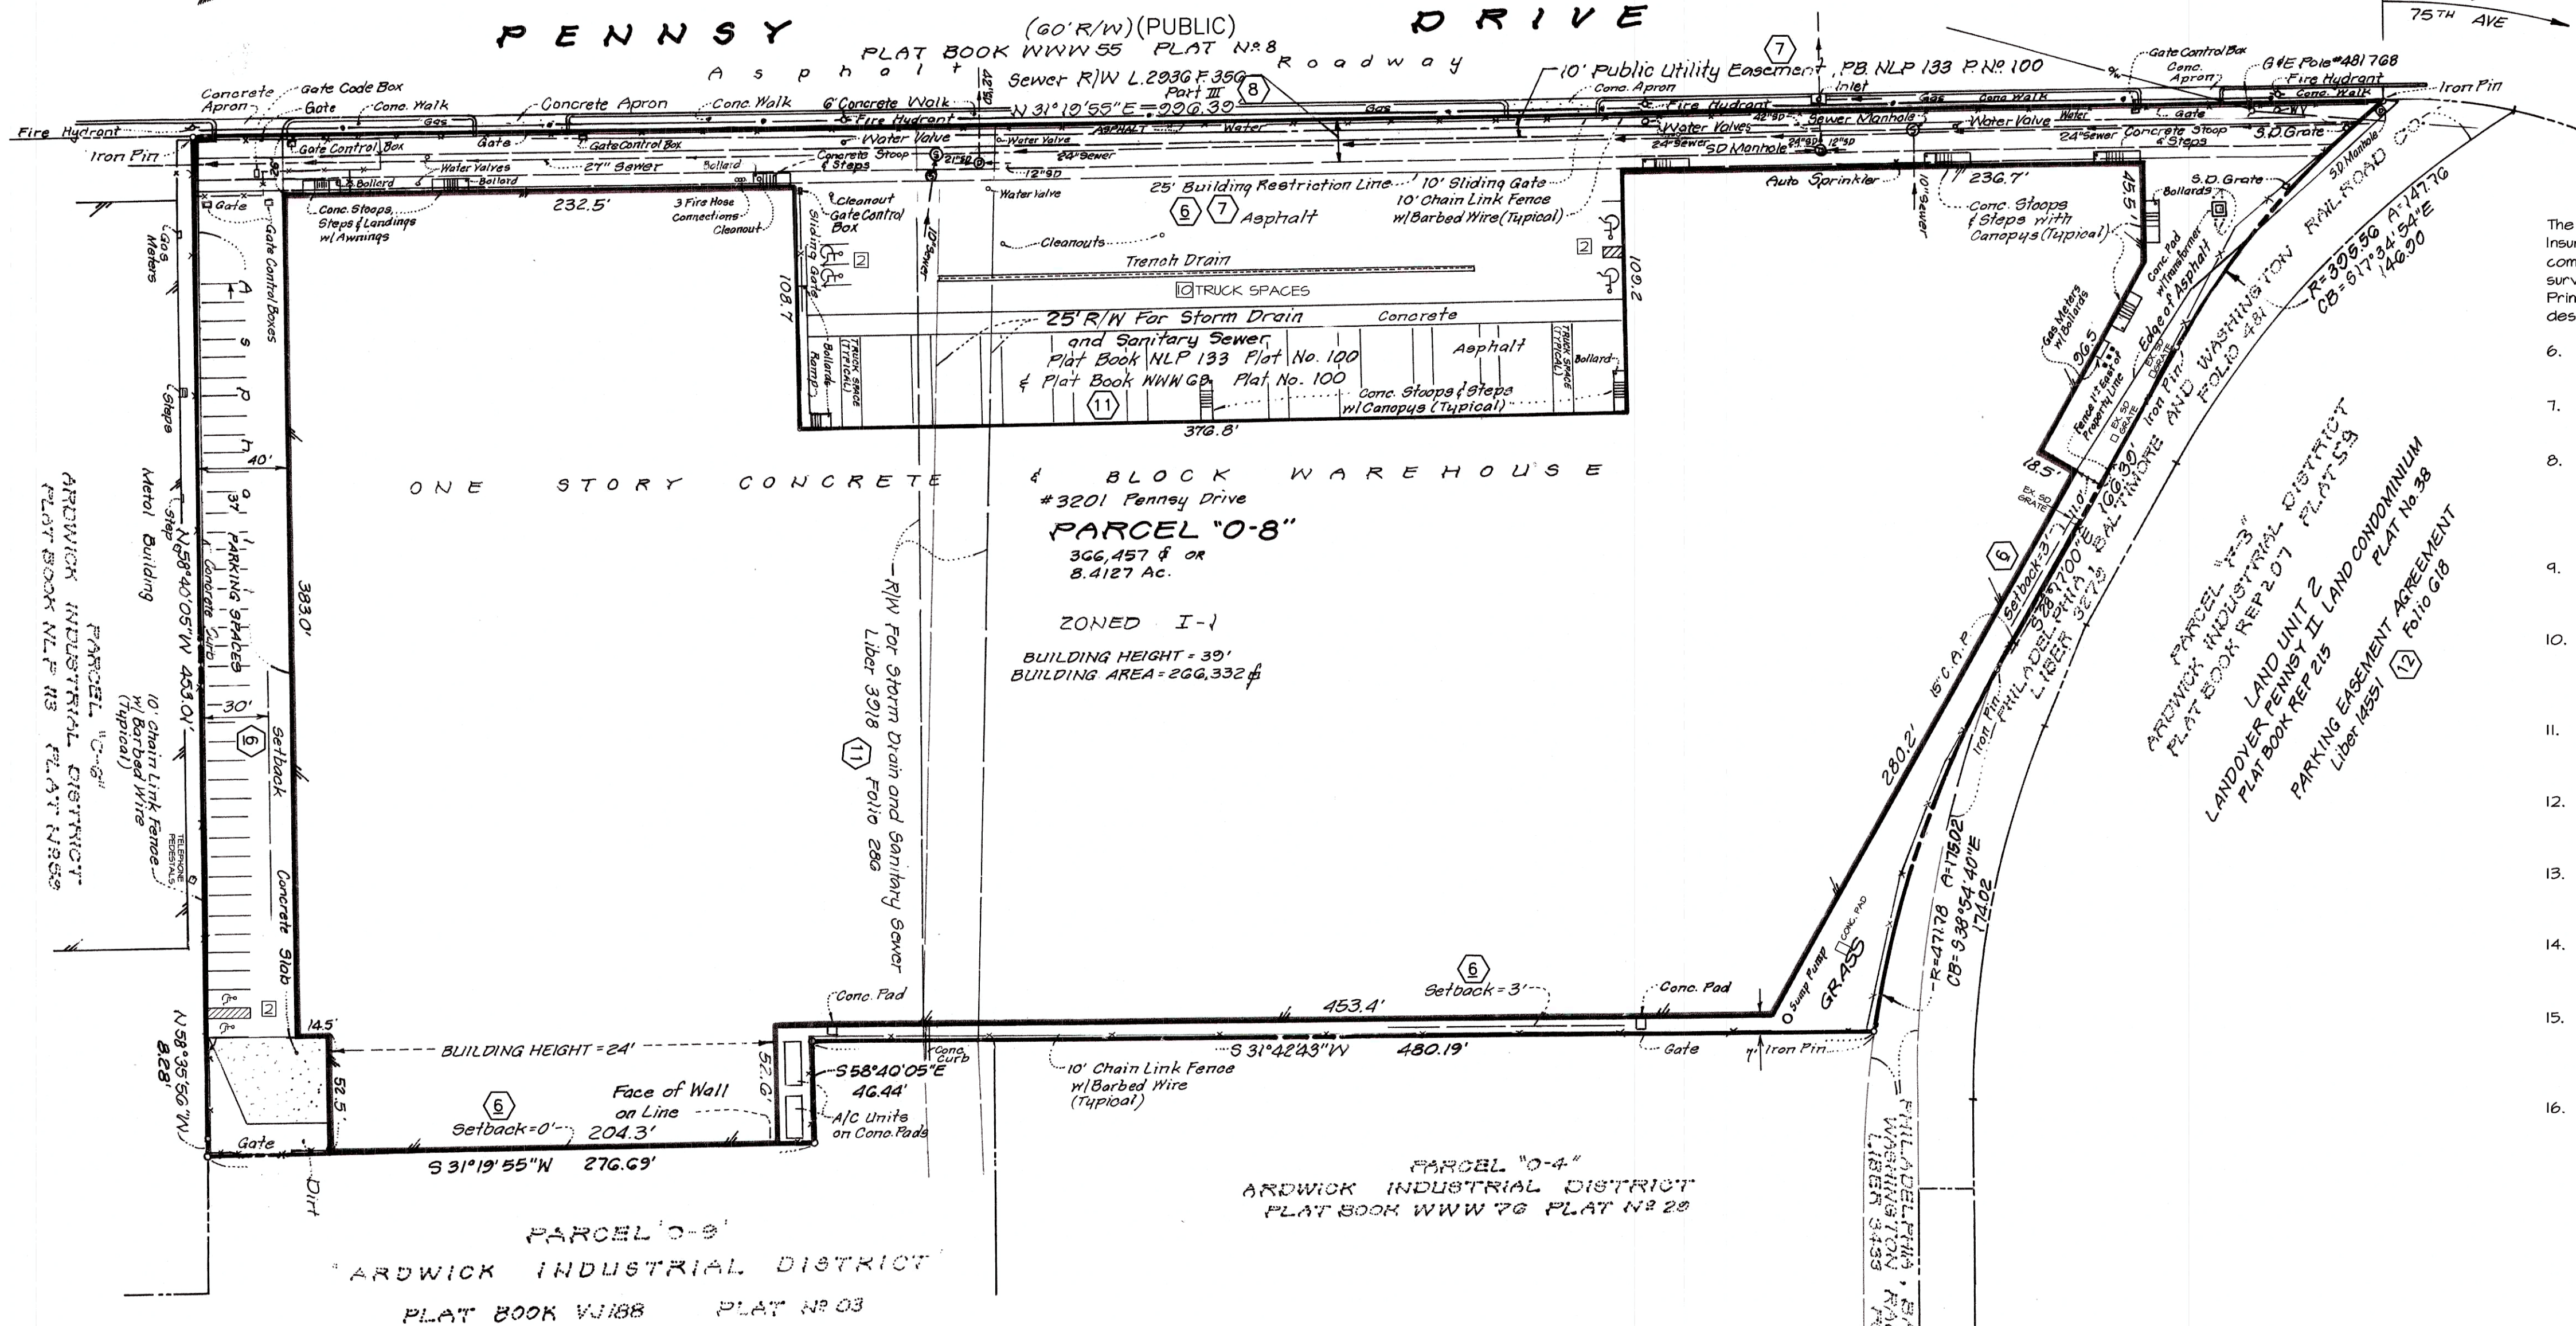

LEGAL DESCRIPTION


PARCEL ONE (3201 Pennsy Drive);

Parcel "O-8", containing 8.4127 acres, in a subdivision known as "PARCELS 'O-8' & 'O-9'" (Being a Resubdivision of Parcels 'O-5' & 'O-6' Arduick Industrial District) ARDUICK INDUSTRIAL DISTRICT" as per plat thereof recorded in Plat Book VJ 188 at Plat 3 among the Land Records of Prince George's County, Maryland.

Together with and subject to all easements, apurtenant rights and obligations contained in that certain Parking Easement Agreement, dated April 17, 2001, by and between Landover Pennsy II, LLC and Landover Pennsy, LLC recorded among said Land Records in Liber 14511 at Folio 618.

Tax ID Number 13-3269560 & 13-3269578

Parcel "O-8" as shown on the aforesaid Plat Book VJ 188, Plat No. 3 and shown hereon constitutes a mathematically closed figure.

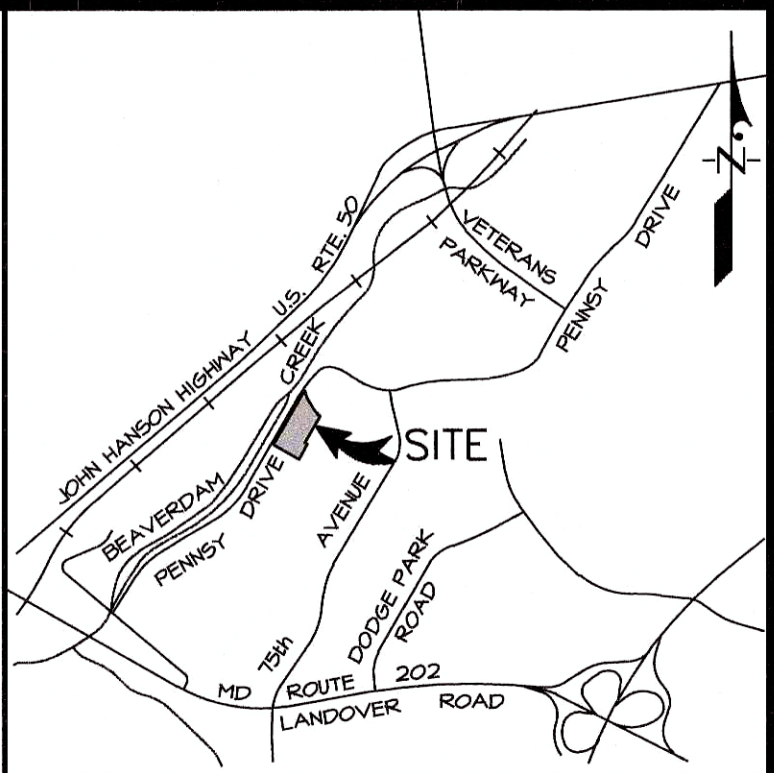

VICINITY MAP

SCALE: 1" = 2000'
ADC MAP BOOK:
WSSC 200' SHEET:

TITLE NOTES

The surveyor has examined Commonwealth Land Title Insurance Company's Commitment for Title Insurance No. DC2001704 with an effective date of August 28, 2020 and offers the following comments on Exceptions 6 through 16 and 18 of Schedule B - Section II contained therein (the surveyor has not conducted a Title Search; Recording references are to the Land Records of Prince George's County, Maryland. The Subject Property shown hereon is the same as that described as Parcel One in Exhibit "A" of the aforesaid Title Commitment.

- Minimum building restriction line per Owner's Dedication on plat recorded in Plat Book 108 at Plat No. 3. Shown per zoning ordinance.
- Twenty-five foot (25.0') building restriction line; and ten foot public utility easement per plat recorded in Plat Book N.L.P. 133 at Plat No. 100. Shown hereon.
- Twenty-foot (20.0') right of way for water and sewer granted to Washington Suburban Sanitary Commission by instrument dated January 17, 1964 and recorded in Liber 2436 at folio 356 and as shown on record plat and as shown on the Parcel O-8 Survey. Note: Liber and folio shown on record plat have been incorrectly designated as Liber 2436 at folio 337. Part Three is shown on survey.
- Agreement by and between Manor Real Estate Company and The Philadelphia, Baltimore and Washington Railroad Company dated and recorded in Liber 2457 at folio 224. The location cannot be determined from the record document.
- Agreement by and between Manor Real Estate Company and The Philadelphia, Baltimore and Washington Railroad Company dated November 13, 1968 and recorded November 18, 1968 in Liber 3658 at folio 357. The location cannot be determined from the record document.
- Right of Way Agreement(s) with Washington Suburban Sanitary Commission dated February 19, 1971 and recorded in Liber 3418 at folio 286, as shown on plat recorded in Plat Book WJWJ 69 at Plat No. 100. Shown on survey.
- Terms and provisions of Parking Easement Agreement, dated April 17, 2001, by and between Landover Pennsy II, LLC and Landover Pennsy, LLC, recorded in Liber 14551 at folio 618, as to Land Unit Two.
- Easement(s) to Baltimore Gas and Electric Company dated March 31, 1964, and recorded in Liber 2465 at folio 320. The location cannot be determined from the record document.
- Declaration of Covenants for Storm and Surface Water Facility and System Maintenance Facility to Prince George's County, Maryland, recorded in Liber 14853 at folio 254. The location cannot be determined from the record document.
- Easement(s) to the Chesapeake and Potomac Telephone Company of Baltimore City by instrument dated May 4, 1923, and recorded June 19, 1923, in Liber 144 at folio 480, as amended by instrument dated January 23, 1964, and recorded in Liber 2425 at folio 178. The location cannot be determined from the record document.
- Easement(s) to the Chesapeake and Potomac Telephone Company of Baltimore City by instrument dated July 10, 1930, and recorded November 5, 1930, in Liber 354 at folio 212 as amended by instrument dated January 23, 1964, and recorded in Liber 2425 at folio 178. The location cannot be determined from the record document.

GENERAL NOTES

- Subject property lies within Zone 'X', area of minimal flood hazard, and Zone 'AE', as shown on Federal Emergency Management Agency Flood Insurance Rate Maps for Prince George's County, Maryland on Community Panel No. 24033C0142E effective September 16, 2016.
- Observable evidence of utilities on and adjacent to the subject property are shown hereon per Item 5.E.iv of the Minimum Standard Detail Requirements for ALTA/NSPS Land Title Surveys. Subsurface utilities may not be shown.
- The subject property has four driveway access points to Pennsy Drive (a 60' public right-of-way) as shown hereon.
- No evidence of cemeteries or burial grounds was observed on the subject property.
- No evidence of current earth moving work, building construction or building additions was observed on the subject property.
- The surveyor is not aware of any proposed changes in street right of way lines; no evidence was observed of recent street or sidewalk construction or repairs.
- No evidence of site use as a solid waste dump, sump or sanitary landfill was observed on the subject property.
- No evidence was observed indicating the delineation or identification of local wetlands in the performance of this survey.
- The following improvements are noted as overlapping with the adjacent properties thereby constituting a possible encroachment. The ownership of the improvements is not determined.
- Chain link fence along the easterly, southerly and westerly line of Parcel "O-8".

ZONING NOTE:

The surveyor has been provided a Preliminary Zoning Compliance Report dated December 11, 2020 prepared by Global Zoning, Job # GZ-10526, for reference in the preparation of this survey. Following is a synopsis of the site requirements contained within said report. The surveyor makes no statement regarding site compliance with zoning regulations;

Zone I-1, Light Industrial:	
Setbacks Required:	Front = 25' Provided = 26'
	Side adjoining non-residential = No minimum, 30' aggregate plus 1/3 foot per 1 foot of building height above 30 feet.
	Provided = +/- 11', 51 feet aggregate
	Rear adjoining non-residential = none required, except 1/3 foot per 1 foot of building height above 30 feet.
	Provided = +/- 3 feet
Building Height:	No maximum.
Density:	Minimum 10% Green Space. Provided = +/- 1% (see Note below)
Parking:	Required = 3 spaces first 1,500 sq. ft. + 1 space per additional 1,500 sq. ft. up to 100,000 sq. ft. plus 0.20 spaces for each 1,000 sq. ft. of floor area over 100,000 sq. ft., 103 Spaces Required (Building = 266,332 sq. ft.)
	Provided = 109 spaces, of which 6 are marked handi-cap.

NOTE: from The Preliminary Zoning Compliance Report;
It is noted that the existing Green Area and Parking are deficient for 3201 Pennsy Drive; however, the Building is currently occupied by the Department of Treasury. Per Section 27-121, the Zoning Requirements are not applicable to buildings occupied by Federal or State agencies. In the event that a private tenant were to move into the space, the Property would be Legal Nonconforming due to Green Area and Parking deficiencies"

SURVEYOR'S CERTIFICATE

To: BCI IV PENNSY LOGISTICS CENTER LLC, a Delaware limited liability company; BCI IV LOC LENDER LLC, a Delaware limited liability company; Commonwealth Land Title Insurance Company; and their respective successors and/or assigns as their interests may appear;


This is to certify that this map or plat and the survey on which it is based were made in accordance with the 2016 Minimum Standard Detail Requirements for ALTA/NSPS Land Title Surveys, jointly established and adopted by ALTA and NSPS, and includes Items 1, 2, 3, 4, 6(a), 6(b), 7(a), 7(b)(1), 7(c), 8, 9, 11 (as to observable evidence per 5.E.iv), 13, 14, 16, 17, 18, and 19 of Table 'A' thereof. The field work was completed on October 16, 2020.

15 Dec 20
Date

Mark E. Powell
Professional Land Surveyor
Maryland No. 21153
Renews 01-28-2021

I hereby certify that this survey was prepared by me or under my responsible charge in compliance with the requirements set forth in COMAR 09.13.06.12 and I am a duly licensed Professional Land Surveyor under the laws of the State of Maryland.

ALTA/NSPS LAND TITLE SURVEY ARDWICK INDUSTRIAL DISTRICT PARCEL "O-8" KENT DISTRICT No. 13 PRINCE GEORGE'S COUNTY, MARYLAND

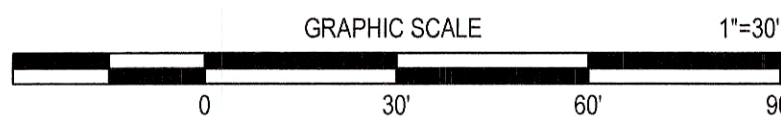

11721 WOODMORE ROAD, SUITE 200 MITCHELLVILLE, MARYLAND 20721	
BEN DYER ASSOCIATES, INC. Engineers / Surveyors / Planners TELEPHONE (301) 430-2000	
COPYRIGHT © 2020 BEN DYER ASSOCIATES, INC.	
12/15/20	Revise Surveyor's Certificate
12/14/20	Revised per attorney comments
DATE	DESCRIPTION
REVISIONS	
SCALE: 1"=30'	DATE: NOVEMBER, 2020
BY: J-69004	9.001-Y

J:\LD7-PRG\69004-LD7\survey\ALTA\ND-Parcel-08-2020-ALTA.dwg; 12/15/2020 11:46:52 AM, tmet