

F

E

D

C

B

A

9/20/2025 3:54:33 PM

Autodesk Docs\DCFM East - Milwaukee EHRM (R24)T24_1804375\03_VA MilEHRM_C.dwt

35% SCHEMATIC DESIGN SUBMISSION	5.17.21
65% DESIGN DEVELOPMENT SUBMISSION	6.15.21
65% DESIGN DEVELOPMENT RESUBMISSION	8.25.21
Revisions:	Date:

CONSULTANT




THE FUTURE IS IT'S STARTING
15 SUNNEN DRIVE
SUITE 104
ST. LOUIS, MO 63143
P: 314.645.1132 F: 314.645.1173
PROJECT #18004375.03

ARCHITECT/ENGINEER OF RECORD



Romanyk Consulting
Focusing on what matters
Romanyk Consulting Corp. www.romanykconsulting.com
3308 Preston Road, Suite 350-164, Plano, Texas 75093

STAMP

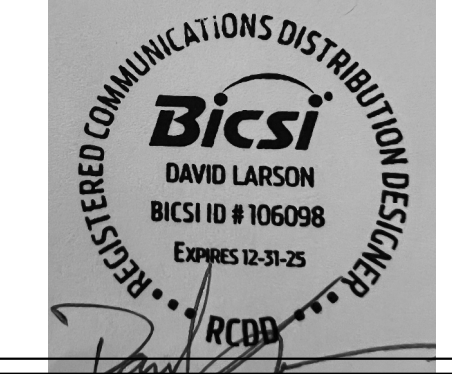

REGISTERED COMMUNICATIONS DISTRIBUTION DESIGNER
DAVID CARSON
BICS1 ID # 106098
Expires 12-31-25

Office of Construction and Facilities Management

VA U.S. Department of Veterans Affairs

Drawing Title
TECHNOLOGY SITE PLAN

Approved:

Phase
FINAL BID DOCUMENTS

Sprinklered
FULLY SPRINKLERED

Project Title
EHRM INFRASTRUCTURE UPGRADES - MILWAUKEE, WI

Location
5000 W. NATIONAL AVENUE MILWAUKEE, WI

Issue Date
SEPTEMBER 05, 2025


Checked
PHINIE

Drawn
MAIBEJ

Project Number
695-21-700

Building Number
00

Drawing Number
T1003

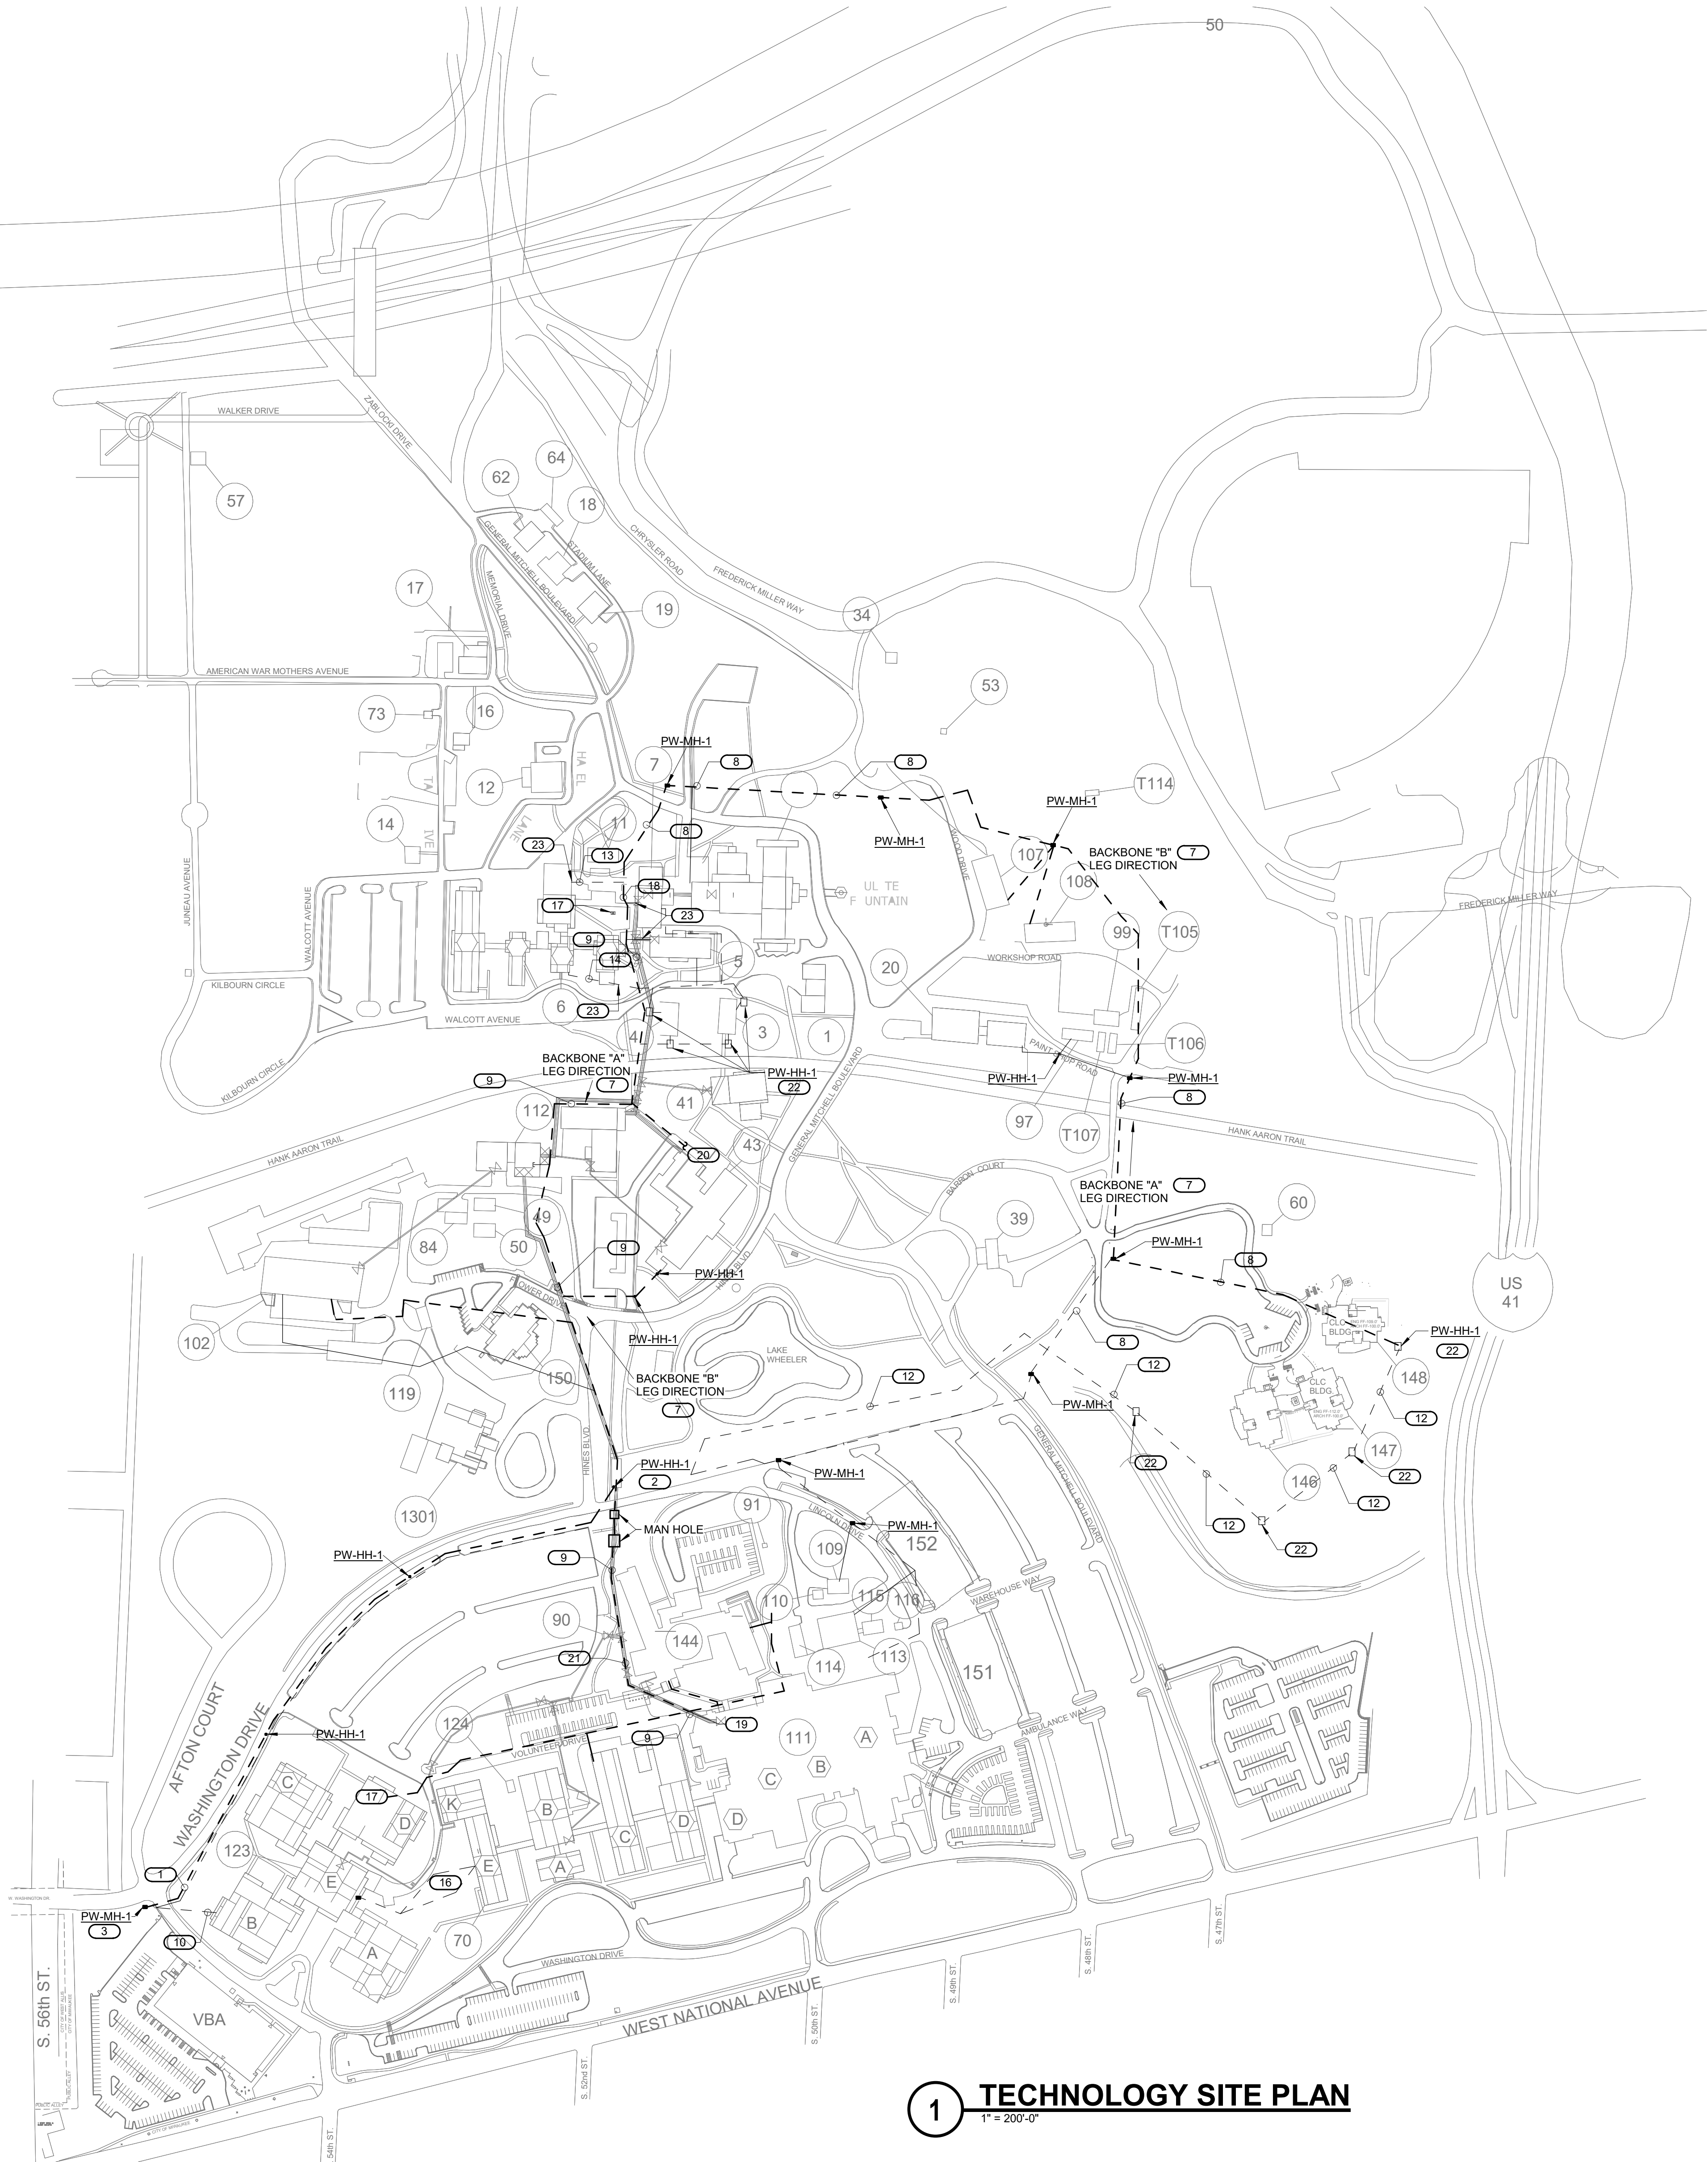

F

E

D

C

B


A

9/2/2025 3:54:33 PM


Autodesk Docs\DCFM East - Milwaukee EHRM (R24)T24_1804375\03_VA Milwaukee_C.dwg

- SHEET NOTES:**
1. REMOVE ALL NETWORK CABLING TO POINTS OF TERMINATION IN ASSOCIATED DATA CLOSET. REFER TO FLOOR PLANS AND SHEET T1001 FOR TR ROOM LOCATIONS.
 2. REFER TO ARCHITECTURAL PHASING PLANS FOR WHEN EXISTING CABLING IS ALLOWED TO BE DEMOLISHED.
 3. FOR ALL EXISTING WIRELESS ACCESS POINTS AND SURVEILLANCE CAMERAS, DEVICES SHALL REMAIN. SCOPE OF WORK INCLUDES CABLE REPLACEMENT ONLY. COORDINATE WITH COR FOR ANY DOWNTIME OF DEVICES.
 4. EXISTING LOCATIONS OF WORK AREA, OUTLETS SHOWN ON THIS SHEET MAY NOT NECESSARILY BE IN THE EXACT LOCATION AS IDENTIFIED.

- KEYNOTES:** (#)
1. WALL MOUNTED RACK TO BE DEMOLISHED AFTER NEW RACK IS INSTALLED.

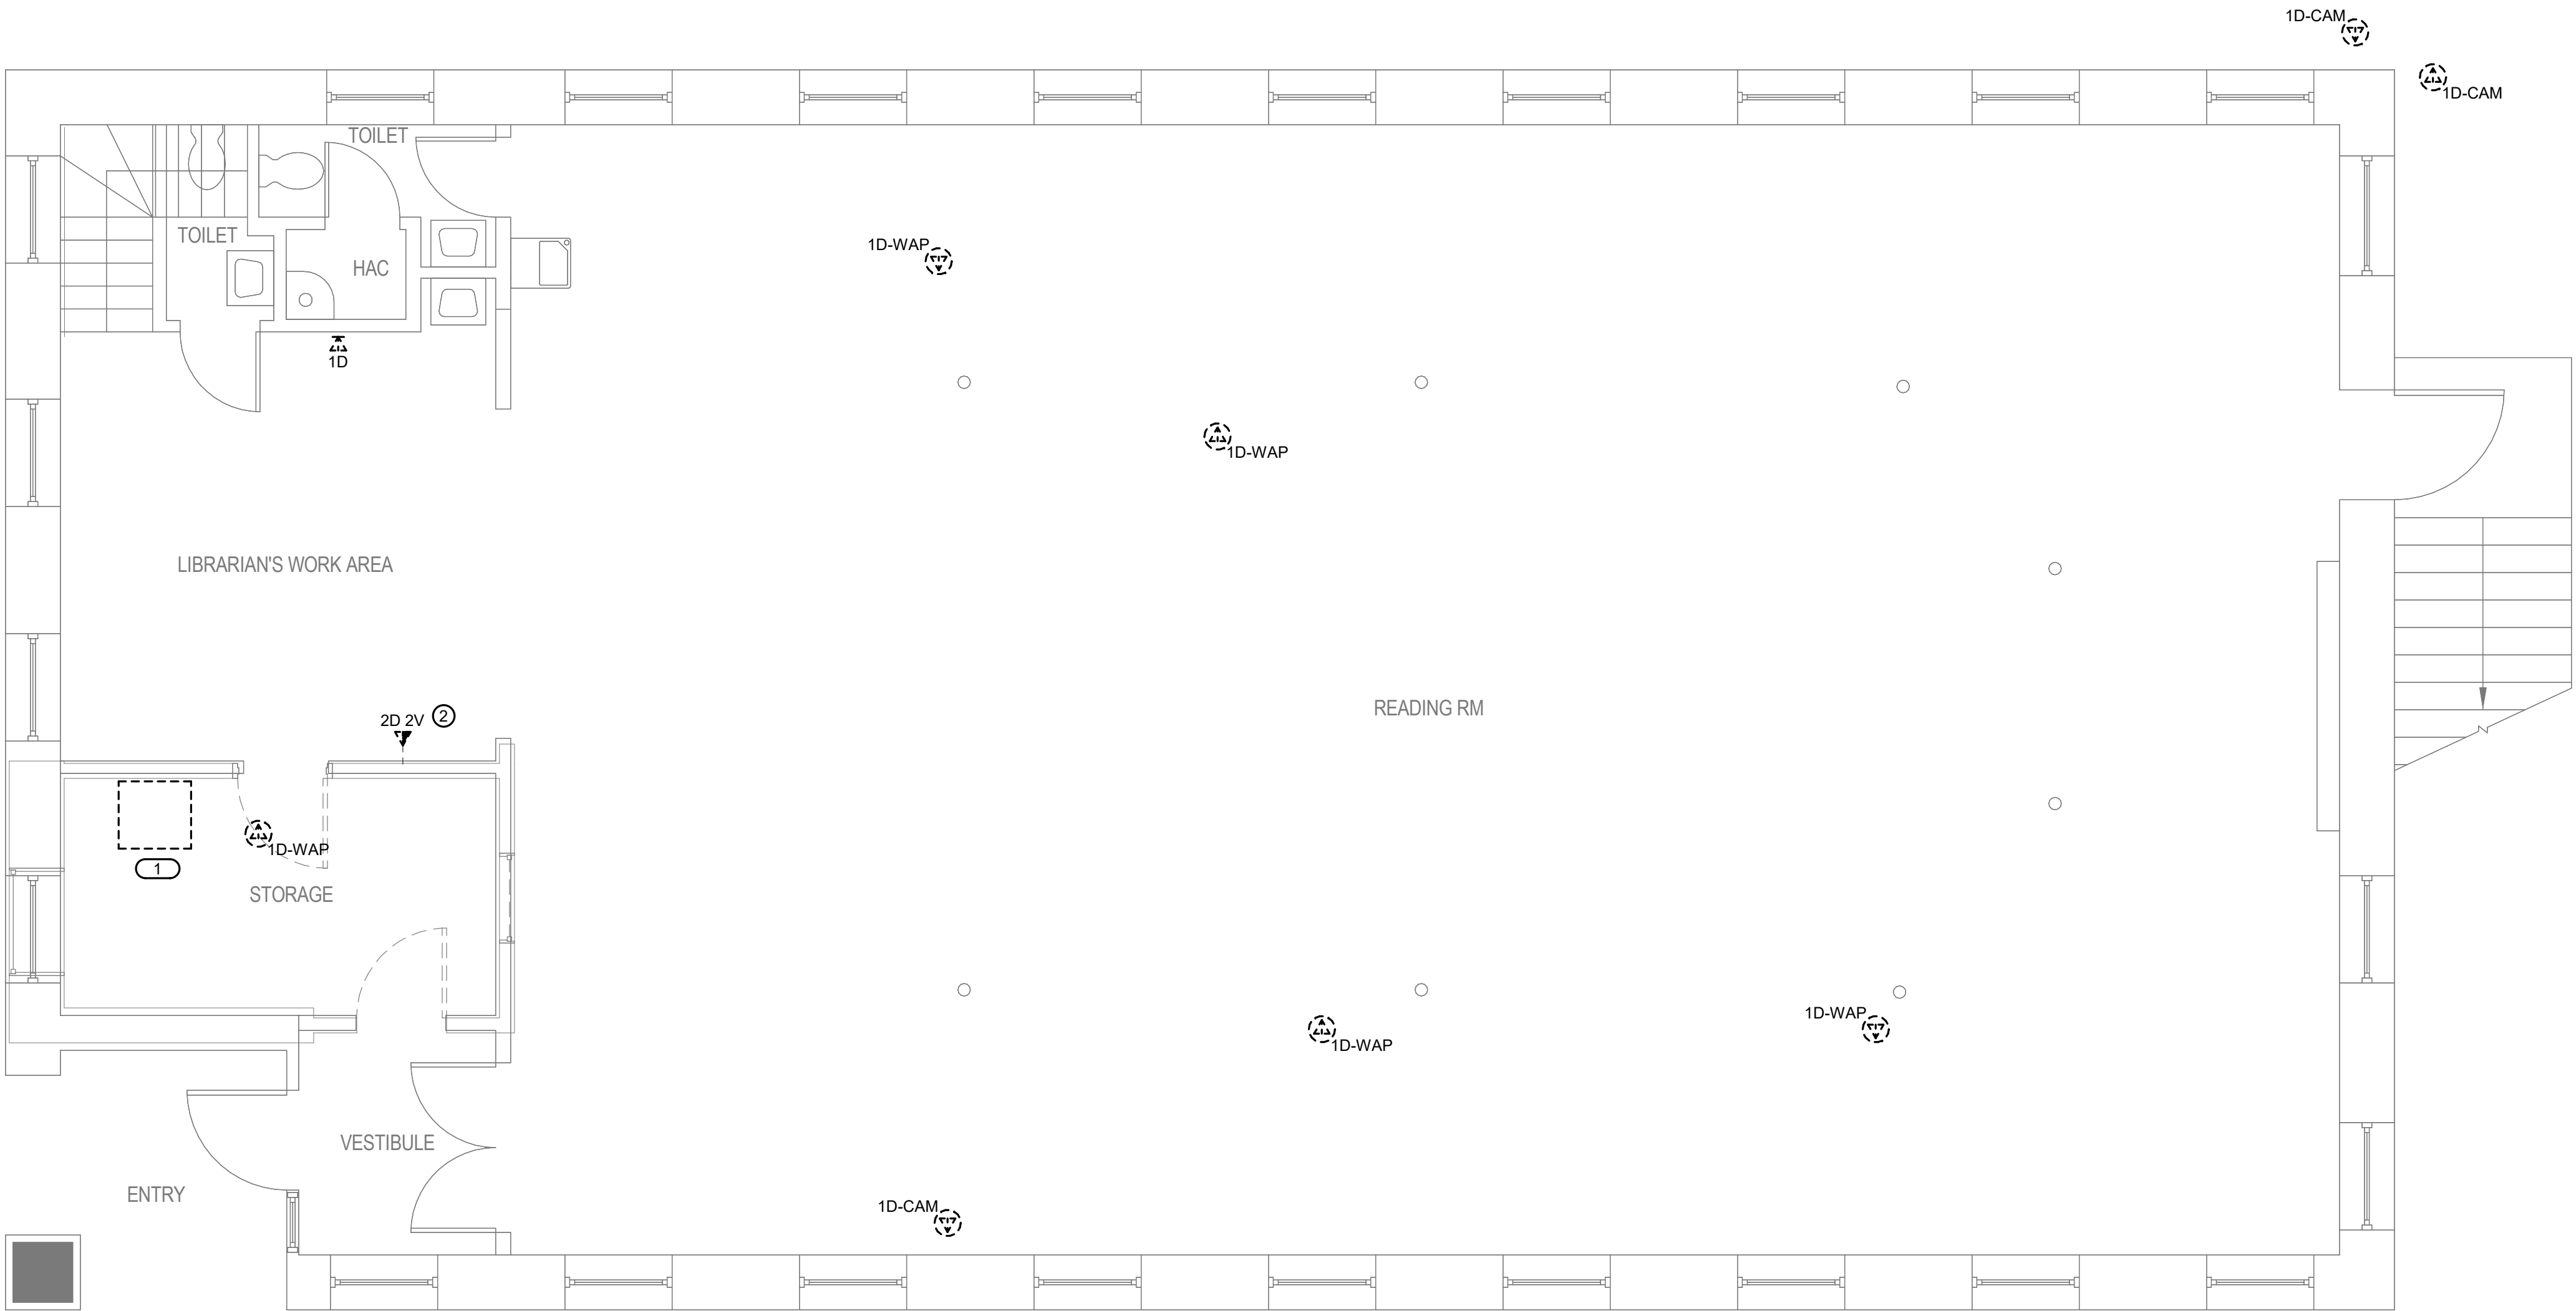

1 BUILDING 03 FIRST FLOOR DEMOLITION PLAN - TECHNOLOGY
1/4" = 1'-0"

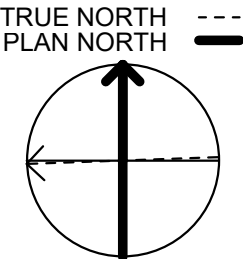

35% SCHEMATIC DESIGN SUBMISSION	5.17.21
65% DESIGN DEVELOPMENT SUBMISSION	6.15.21
65% DESIGN DEVELOPMENT RESUBMISSION	8.25.21
Revisions:	Date:

CONSULTANT

IMEG

15 SUNNEN DRIVE
SUITE 104
ST. LOUIS, MO 63143
P: 314.645.1132 F: 314.645.1173
PROJECT #18004375.03

ARCHITECT/ENGINEER OF RECORD

Romanyk Consulting
Focusing on what matters

Romanyk Consulting Corp. www.romanykconsulting.com
3308 Preston Road, Suite 350-164, Plano, Texas 75093

STAMP

Bicsi
DAVID LARSON
BICS1 ID # 106098
EXPIRES 12-31-25
REGISTERED COMMUNICATIONS DISTRIBUTION DESIGNER
RCDD

Office of
Construction
and Facilities
Management

VA U.S. Department
of Veterans Affairs

Drawing Title
BUILDING 03 FIRST FLOOR DEMO PLAN -
TECHNOLOGY

Approved:

Phase
FINAL BID DOCUMENTS

Sprinklered

Project Title
EHRM INFRASTRUCTURE
UPGRADES - MILWAUKEE, WI

Location
5000 W. NATIONAL AVENUE MILWAUKEE, WI

Issue Date
SEPTEMBER 05, 2025

Checked
PHINIE

Drawn
MAIBEJ

Project Number
695-21-700

Building Number
03

Drawing Number
03-TD101

32'
16'
8'
0'
Graphic Scale: 1/16" = 1'-0"

16'
8'
4'
0'
Graphic Scale: 1/8" = 1'-0"

2'
1'
8"
4"
0'
Graphic Scale: 3/32" = 1'-0"

4'
2'
1'
0'
Graphic Scale: 1/4" = 1'-0"

4'
2'
1'
0'
Graphic Scale: 3/8" = 1'-0"

4'
2'
1'
0'
Graphic Scale: 1/2" = 1'-0"

6"
3"
1'
0'
Graphic Scale: 3/4" = 1'-0"

2'
1'
6"
0'
Graphic Scale: 1" = 1'-0"

1' 6"
1'
6"
0'
Graphic Scale: 1 1/2" = 1'-0"

F

E

D

C


B

A


9/3/2025 3:54:33 PM

Autodesk Docs\OCF\East - Milwaukee EHRM (R24)T24_1804375\03_VA Milwaukee C.d

- SHEET NOTES:**
1. REMOVE ALL NETWORK CABLING TO POINTS OF TERMINATION IN ASSOCIATED DATA CLOSET. REFER TO FLOOR PLANS AND SHEET T1001 FOR TR ROOM LOCATIONS.
 2. REFER TO ARCHITECTURAL PHASING PLANS FOR WHEN EXISTING CABLING IS ALLOWED TO BE DEMOLISHED.
 3. FOR ALL EXISTING WIRELESS ACCESS POINTS AND SURVEILLANCE CAMERAS, DEVICES SHALL REMAIN. SCOPE OF WORK INCLUDES CABLE REPLACEMENT ONLY. COORDINATE WITH COR FOR ANY DOWNTIME OF DEVICES. EXISTING LOCATIONS OF WORK AREA, OUTLETS SHOWN ON THIS SHEET MAY NOT NECESSARILY BE IN THE EXACT LOCATION AS IDENTIFIED.
 - 4.

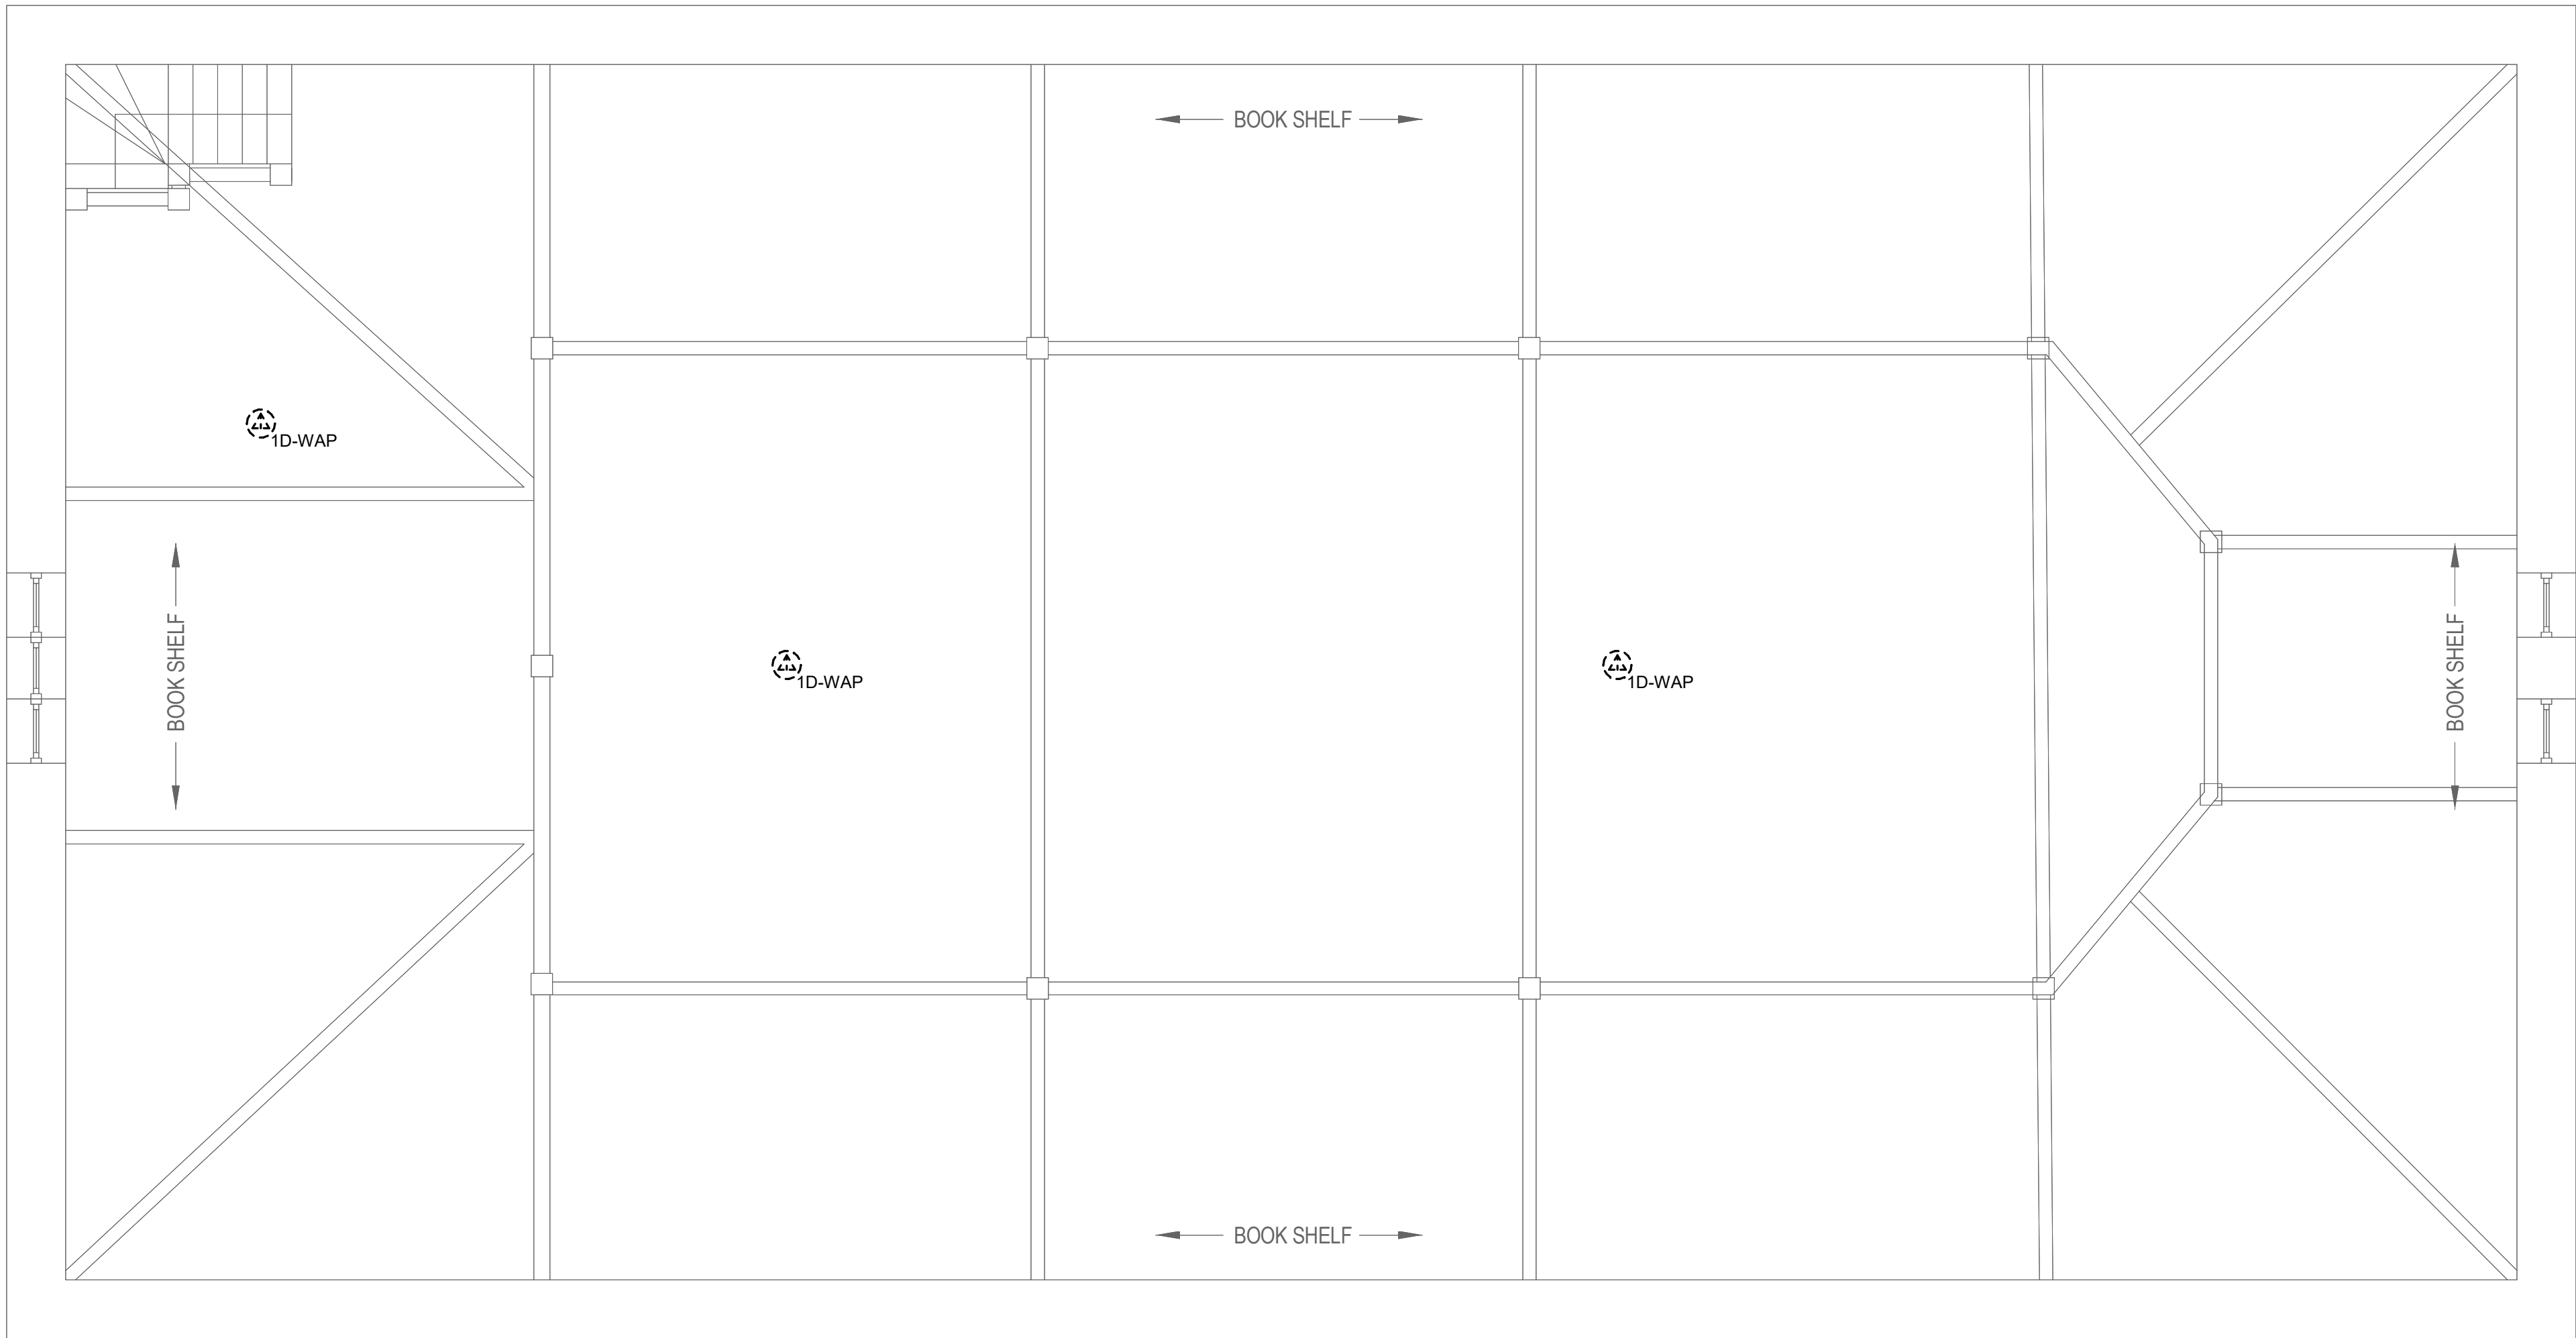

1 BUILDING 03 SECOND FLOOR DEMOLITION PLAN - TECHNOLOGY
1/4" = 1'-0"

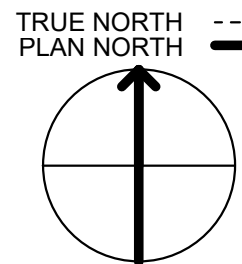

35% SCHEMATIC DESIGN SUBMISSION	5.17.21
65% DESIGN DEVELOPMENT SUBMISSION	6.15.21
65% DESIGN DEVELOPMENT RESUBMISSION	8.25.21
Revisions:	Date:

CONSULTANT

IMEG

THE FUTURE IS NOW
15 SUNNEN DRIVE
SUITE 104
ST. LOUIS, MO 63143
P: 314.645.1132 F: 314.645.1173
PROJECT #18004375.03

ARCHITECT/ENGINEER OF RECORD

Romanyk Consulting
Focusing on what matters

Romanyk Consulting Corp. www.romanykconsulting.com
3308 Preston Road, Suite 350-164, Plano, Texas 75093

STAMP

Bicsi
DAVID LARSON
BICS1 ID # 106098
EXPIRES 12-31-25
REGISTERED COMMUNICATIONS DISTRIBUTION DESIGNER
RCDD

Office of
Construction
and Facilities
Management

VA U.S. Department
of Veterans Affairs

Drawing Title
BUILDING 03 SECOND FLOOR DEMO PLAN -
TECHNOLOGY

Approved:

Phase
FINAL BID DOCUMENTS

Sprinklered

Project Title
EHRM INFRASTRUCTURE
UPGRADES - MILWAUKEE, WI

Location
5000 W. NATIONAL AVENUE, MILWAUKEE, WI

Issue Date
SEPTEMBER 05, 2025








Checked
PHINIE

Drawn
MAIBEJ

Project Number
695-21-700

Building Number
03

Drawing Number
03-TD102

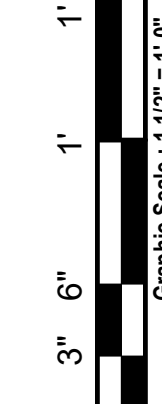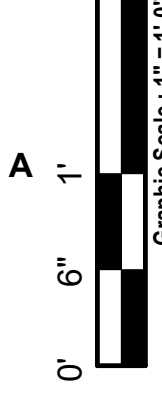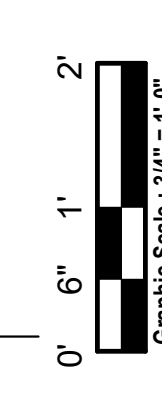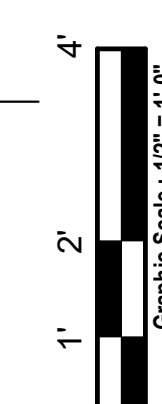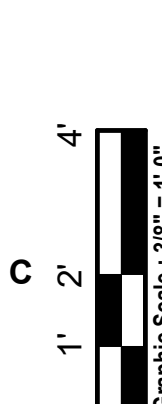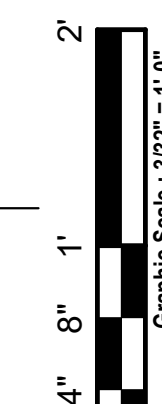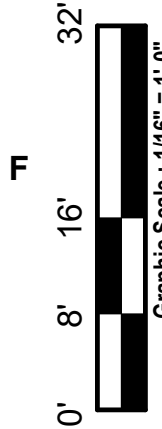

F

E

D

C

B

A

9/2/2025 3:54:34 PM


Autodesk Docs\DCFM East - Milwaukee EHRM (R24)T24_1804375.03_VA MilwEHRM_C.rvt

SHEET NOTES:



1. REFER TO 1/TN400 FOR TECHNOLOGY ROUGH IN DETAIL.
2. ALL NETWORK CABLES ON THIS SHEET SHALL TERMINATE IN TE-3-1454.
3. REFER TO CIVIL DRAWINGS AND T1003 FOR ADDITIONAL PATHWAY INFORMATION.
4. CONTRACTOR TO PROVIDE NEW J-HOOK ROUTES FOR ALL NEW CABLING. J-HOOK SIZE AND QUANTITY TO BE PER MANUFACTURER RECOMMENDATIONS.
5. REFER TO TN500-TN509 FOR RISER DIAGRAMS. REFER TO SHEET TN402 FOR PENETRATION DETAILS.
6. THESE DRAWINGS MAKE THE BEST ATTEMPT TO IDENTIFY EXISTING DATA DROPS/WORK AREA OUTLETS. AS LONG AS THE TOTAL NEWLY INSTALLED DATA DROP COUNT DOES NOT VARY +/- 10% IDENTIFIED ON THESE DRAWINGS, THE CONTRACTOR'S SCOPE SHALL BE UNCHANGED.
7. NEW WORK AREA OUTLETS SHALL BE LOCATED IN EXISTING BOXES. WORK AREA OUTLETS SHOWN ON THIS SHEET MAY NOT BE IN THE EXACT LOCATION AS IDENTIFIED.
8. CONTRACTOR TO INCLUDE AN ALLOWANCE FOR 10% ADDITIONAL 2-PORTS CAT6A INFORMATION OUTLETS IN THEIR PROPOSAL FOR THIS SHEET. FUTURE INFORMATION OUTLET LOCATIONS WILL BE DETERMINED BY THE VA AT A LATER DATE.

KEYNOTES: (P)

1. EXISTING BACKBONE ENTRY POINT. PROTECT IN PLACE. DEMOLISH EXISTING FIBER OPTIC CABLE TO POINTS OF TERMINATION AFTER REDUNDANT PATH IS INSTALLED AND OPERATIONAL. REFER TO ARCHITECTURAL PHASING PLAN FOR ADDITIONAL INFORMATION. CONDUIT ENTERS ON LOWER LEVEL.

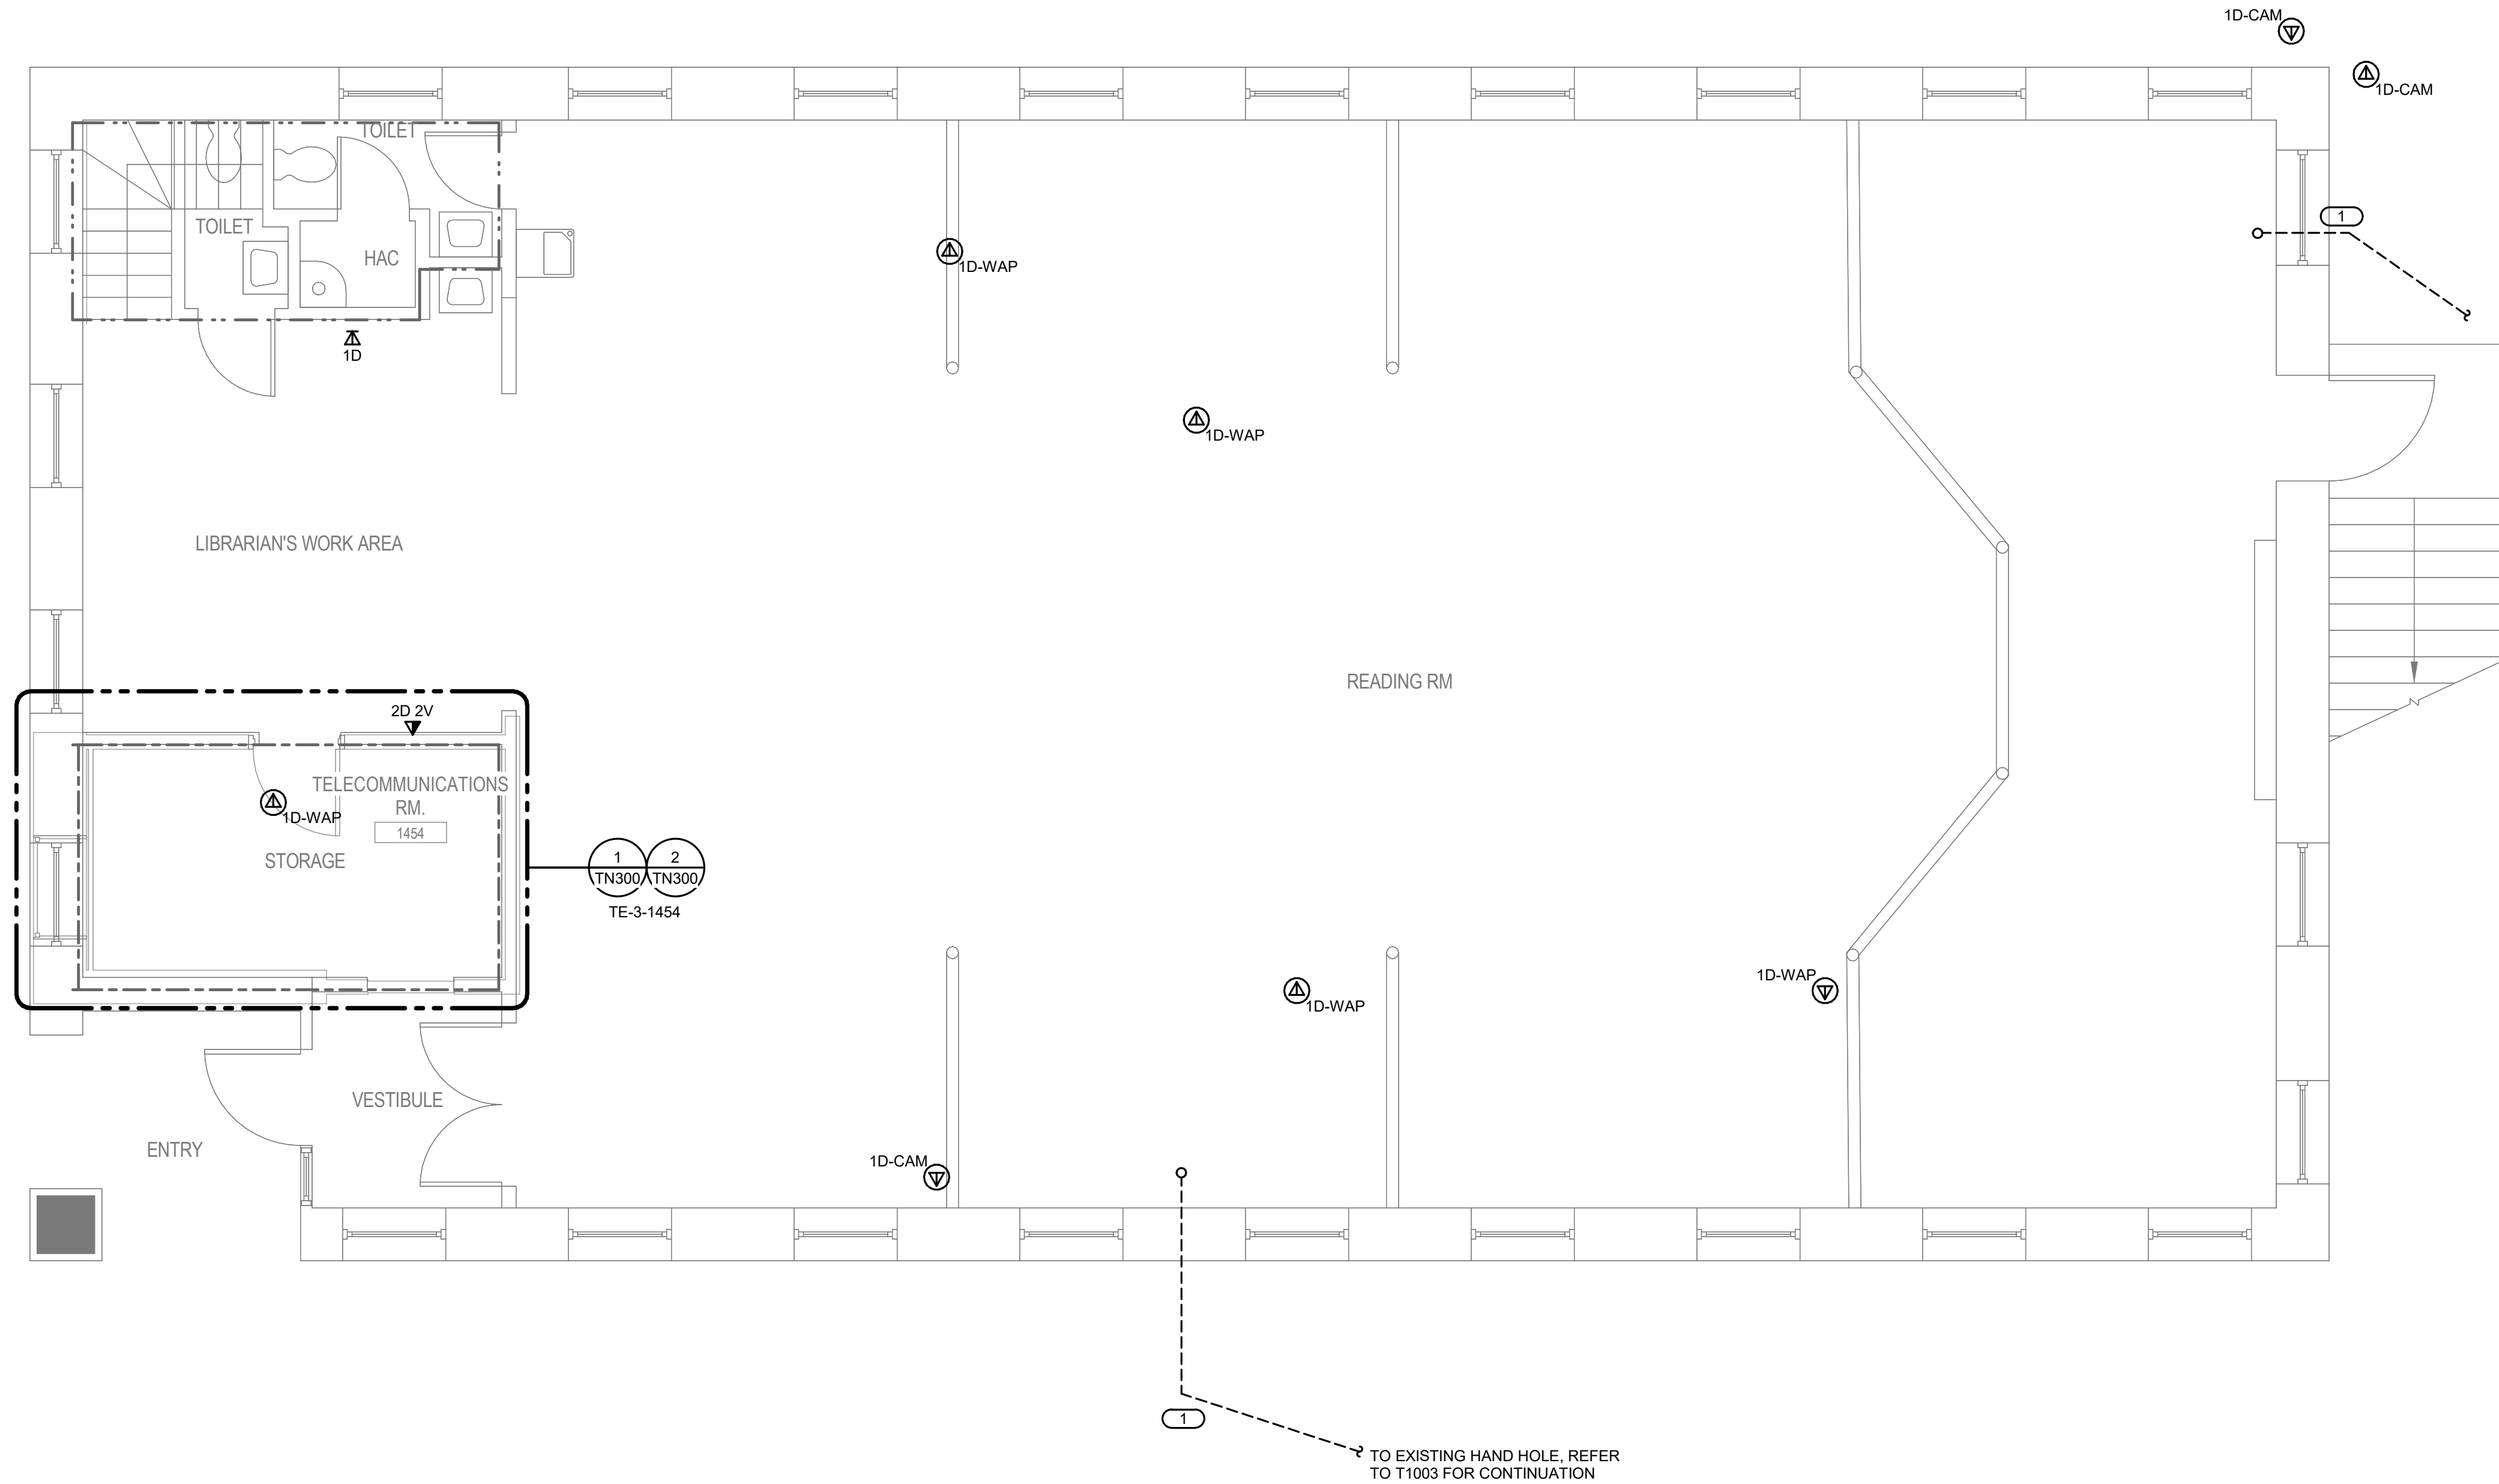

1 BUILDING 03 FIRST FLOOR PLAN - TECHNOLOGY
1/4" = 1'-0"

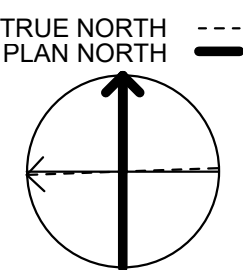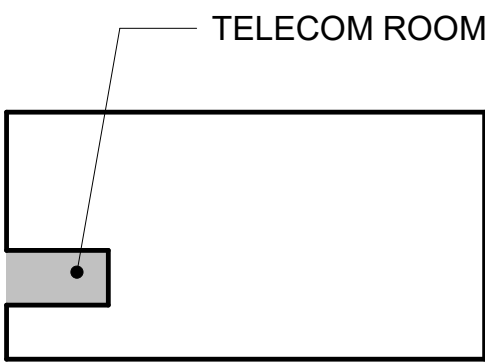

35% SCHEMATIC DESIGN SUBMISSION	5.17.21
65% DESIGN DEVELOPMENT SUBMISSION	6.15.21
65% DESIGN DEVELOPMENT RESUBMISSION	8.25.21
Revisions:	Date:

CONSULTANT

IMEG
15 SUNNEN DRIVE
SUITE 104
ST. LOUIS, MO 63143
P: 314.645.1132 F: 314.645.1173
PROJECT #18004375.03

ARCHITECT/ENGINEER OF RECORD

Romanyk Consulting
Focusing on what matters
Romanyk Consulting Corp. www.romanykconsulting.com
3308 Preston Road, Suite 350-164, Plano, Texas 75093

STAMP

Bicsi
DAVID LARSON
BICS1 ID # 106098
EXPIRES 12-31-25
REGISTERED COMMUNICATIONS DISTRIBUTION DESIGNER

Office of
Construction
and Facilities
Management

VA U.S. Department
of Veterans Affairs

Drawing Title BUILDING 03 FIRST FLOOR PLAN - TECHNOLOGY	Phase FINAL BID DOCUMENTS
Approved:	Sprinklered

Project Title EHRM INFRASTRUCTURE UPGRADES - MILWAUKEE, WI	Project Number 695-21-700
Location 5000 W. NATIONAL AVENUE, MILWAUKEE, WI	Building Number 03
Issue Date SEPTEMBER 05, 2025	Checked PHINIE
	Drawn MAIBEJ

Drawing Number 03-TN101	
----------------------------	--

F

E

D


C

B


A

9/3/2025 3:54:35 PM

Autodesk Docs\OCFM East - Milwaukee EHRM (R24)T24_1804375\03_VA Milwaukee C.dwt

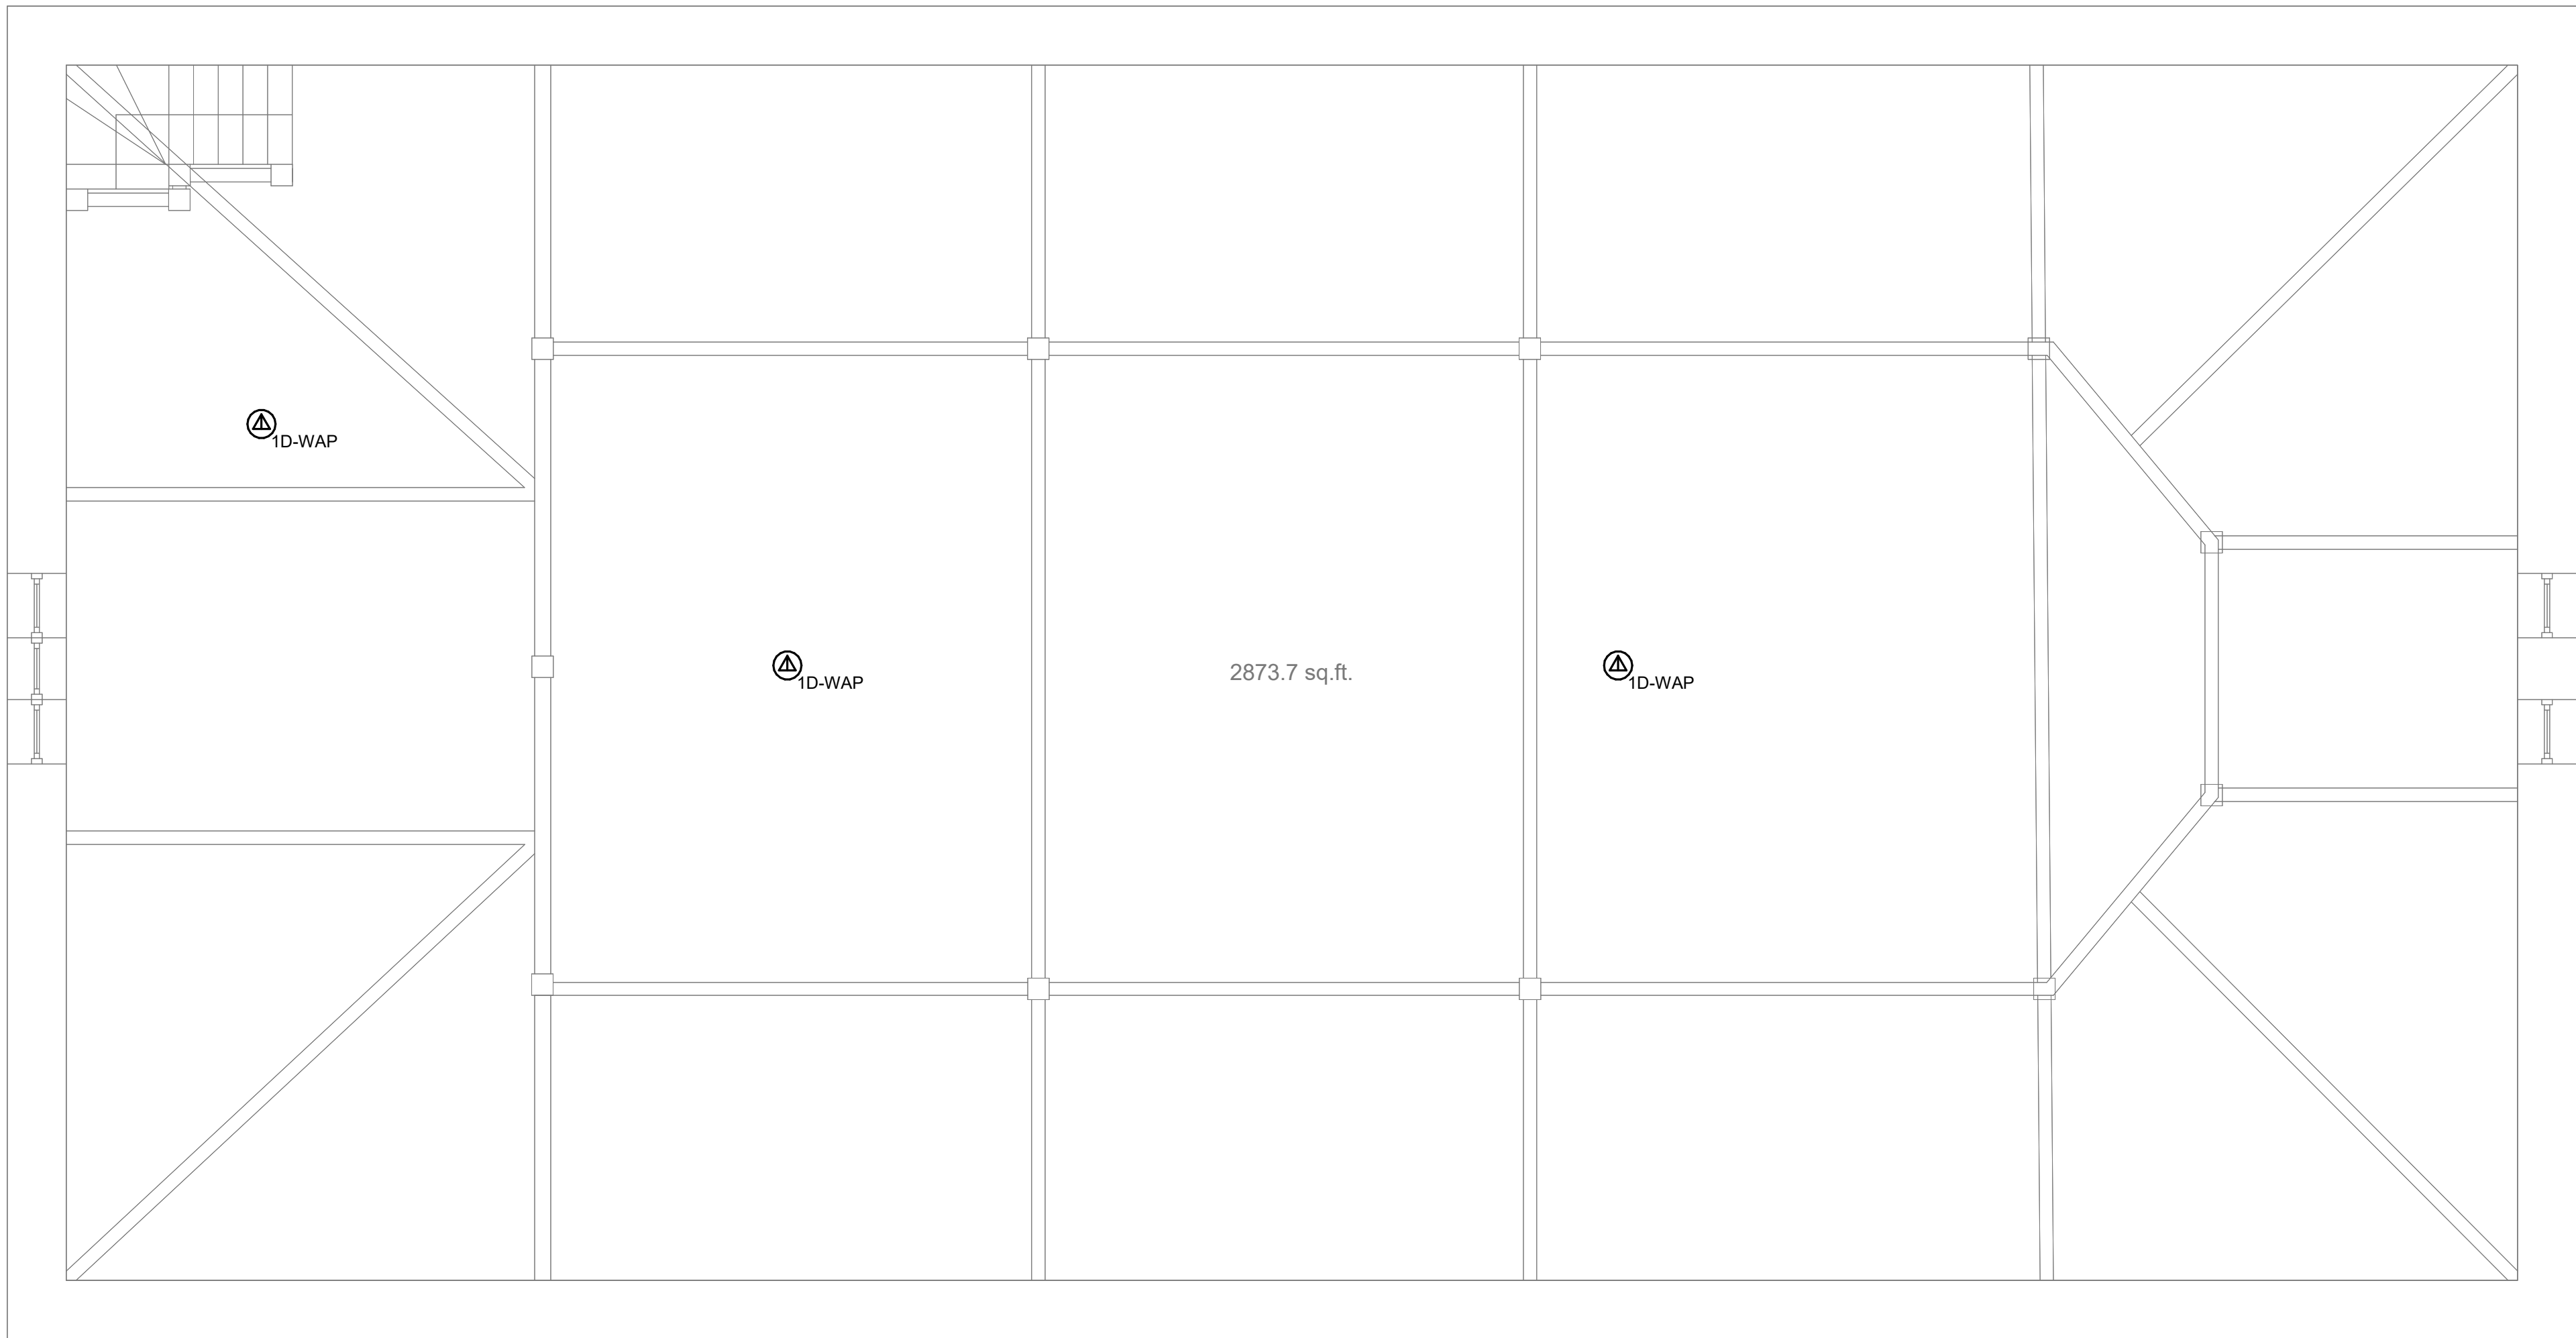

1 **BUILDING 03 SECOND FLOOR PLAN - TECHNOLOGY**
1/4" = 1'-0"

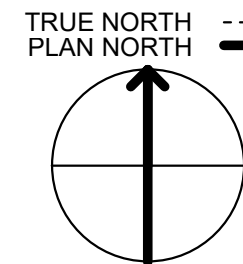

35% SCHEMATIC DESIGN SUBMISSION	5.17.21
65% DESIGN DEVELOPMENT SUBMISSION	6.15.21
65% DESIGN DEVELOPMENT RESUBMISSION	8.25.21
Revisions:	Date:

CONSULTANT



The Future is Full of Scale
www.imegcorp.com
15 SUNNEN DRIVE
SUITE 104
ST. LOUIS, MO 63143
P: 314.645.1132 F: 314.645.1173
PROJECT #18004375.03

ARCHITECT/ENGINEER OF RECORD



Romanyk Consulting
Focusing on what matters
Romanyk Consulting Corp. www.romanykconsulting.com
3308 Preston Road, Suite 350-164, Plano, Texas 75093

STAMP



Office of
Construction
and Facilities
Management

 U.S. Department
of Veterans Affairs

Drawing Title
BUILDING 03 SECOND FLOOR PLAN -
TECHNOLOGY

Approved:

Phase
FINAL BID DOCUMENTS

Sprinklered

Project Title
EHRM INFRASTRUCTURE
UPGRADES - MILWAUKEE, WI

Location
5000 W. NATIONAL AVENUE MILWAUKEE, WI

Issue Date
SEPTEMBER 05, 2025


Checked
PHINIE

Drawn
MAIBEJ

Project Number
695-21-700

Building Number
03

Drawing Number
03-TN102

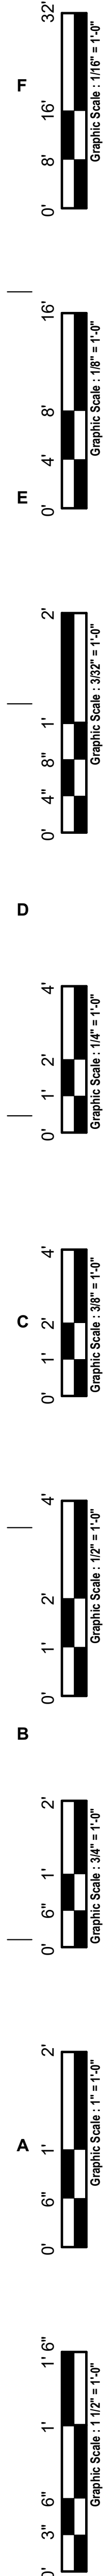

F

E

D

C


B

A

9/2/2025 3:54:38 PM

Autodesk Docs\DCFM East - Milwaukee EHRM (R24)T24_1804375\03_VA Milwaukee EHRM_C.dwt

- SHEET NOTES:**
1. REMOVE ALL NETWORK CABLING TO POINTS OF TERMINATION IN ASSOCIATED DATA CLOSET. REFER TO FLOOR PLANS AND SHEET T1001 FOR TR ROOM LOCATIONS.
 2. REFER TO ARCHITECTURAL PHASING PLANS FOR WHEN EXISTING CABLING IS ALLOWED TO BE DEMOLISHED.
 3. FOR ALL EXISTING WIRELESS ACCESS POINTS AND SURVEILLANCE CAMERAS, DEVICES SHALL REMAIN. SCOPE OF WORK INCLUDES CABLE REPLACEMENT ONLY. COORDINATE WITH COR FOR ANY DOWNTIME OF DEVICES. EXISTING LOCATIONS OF WORK AREA, OUTLETS SHOWN ON THIS SHEET MAY NOT NECESSARILY BE IN THE EXACT LOCATION AS IDENTIFIED.

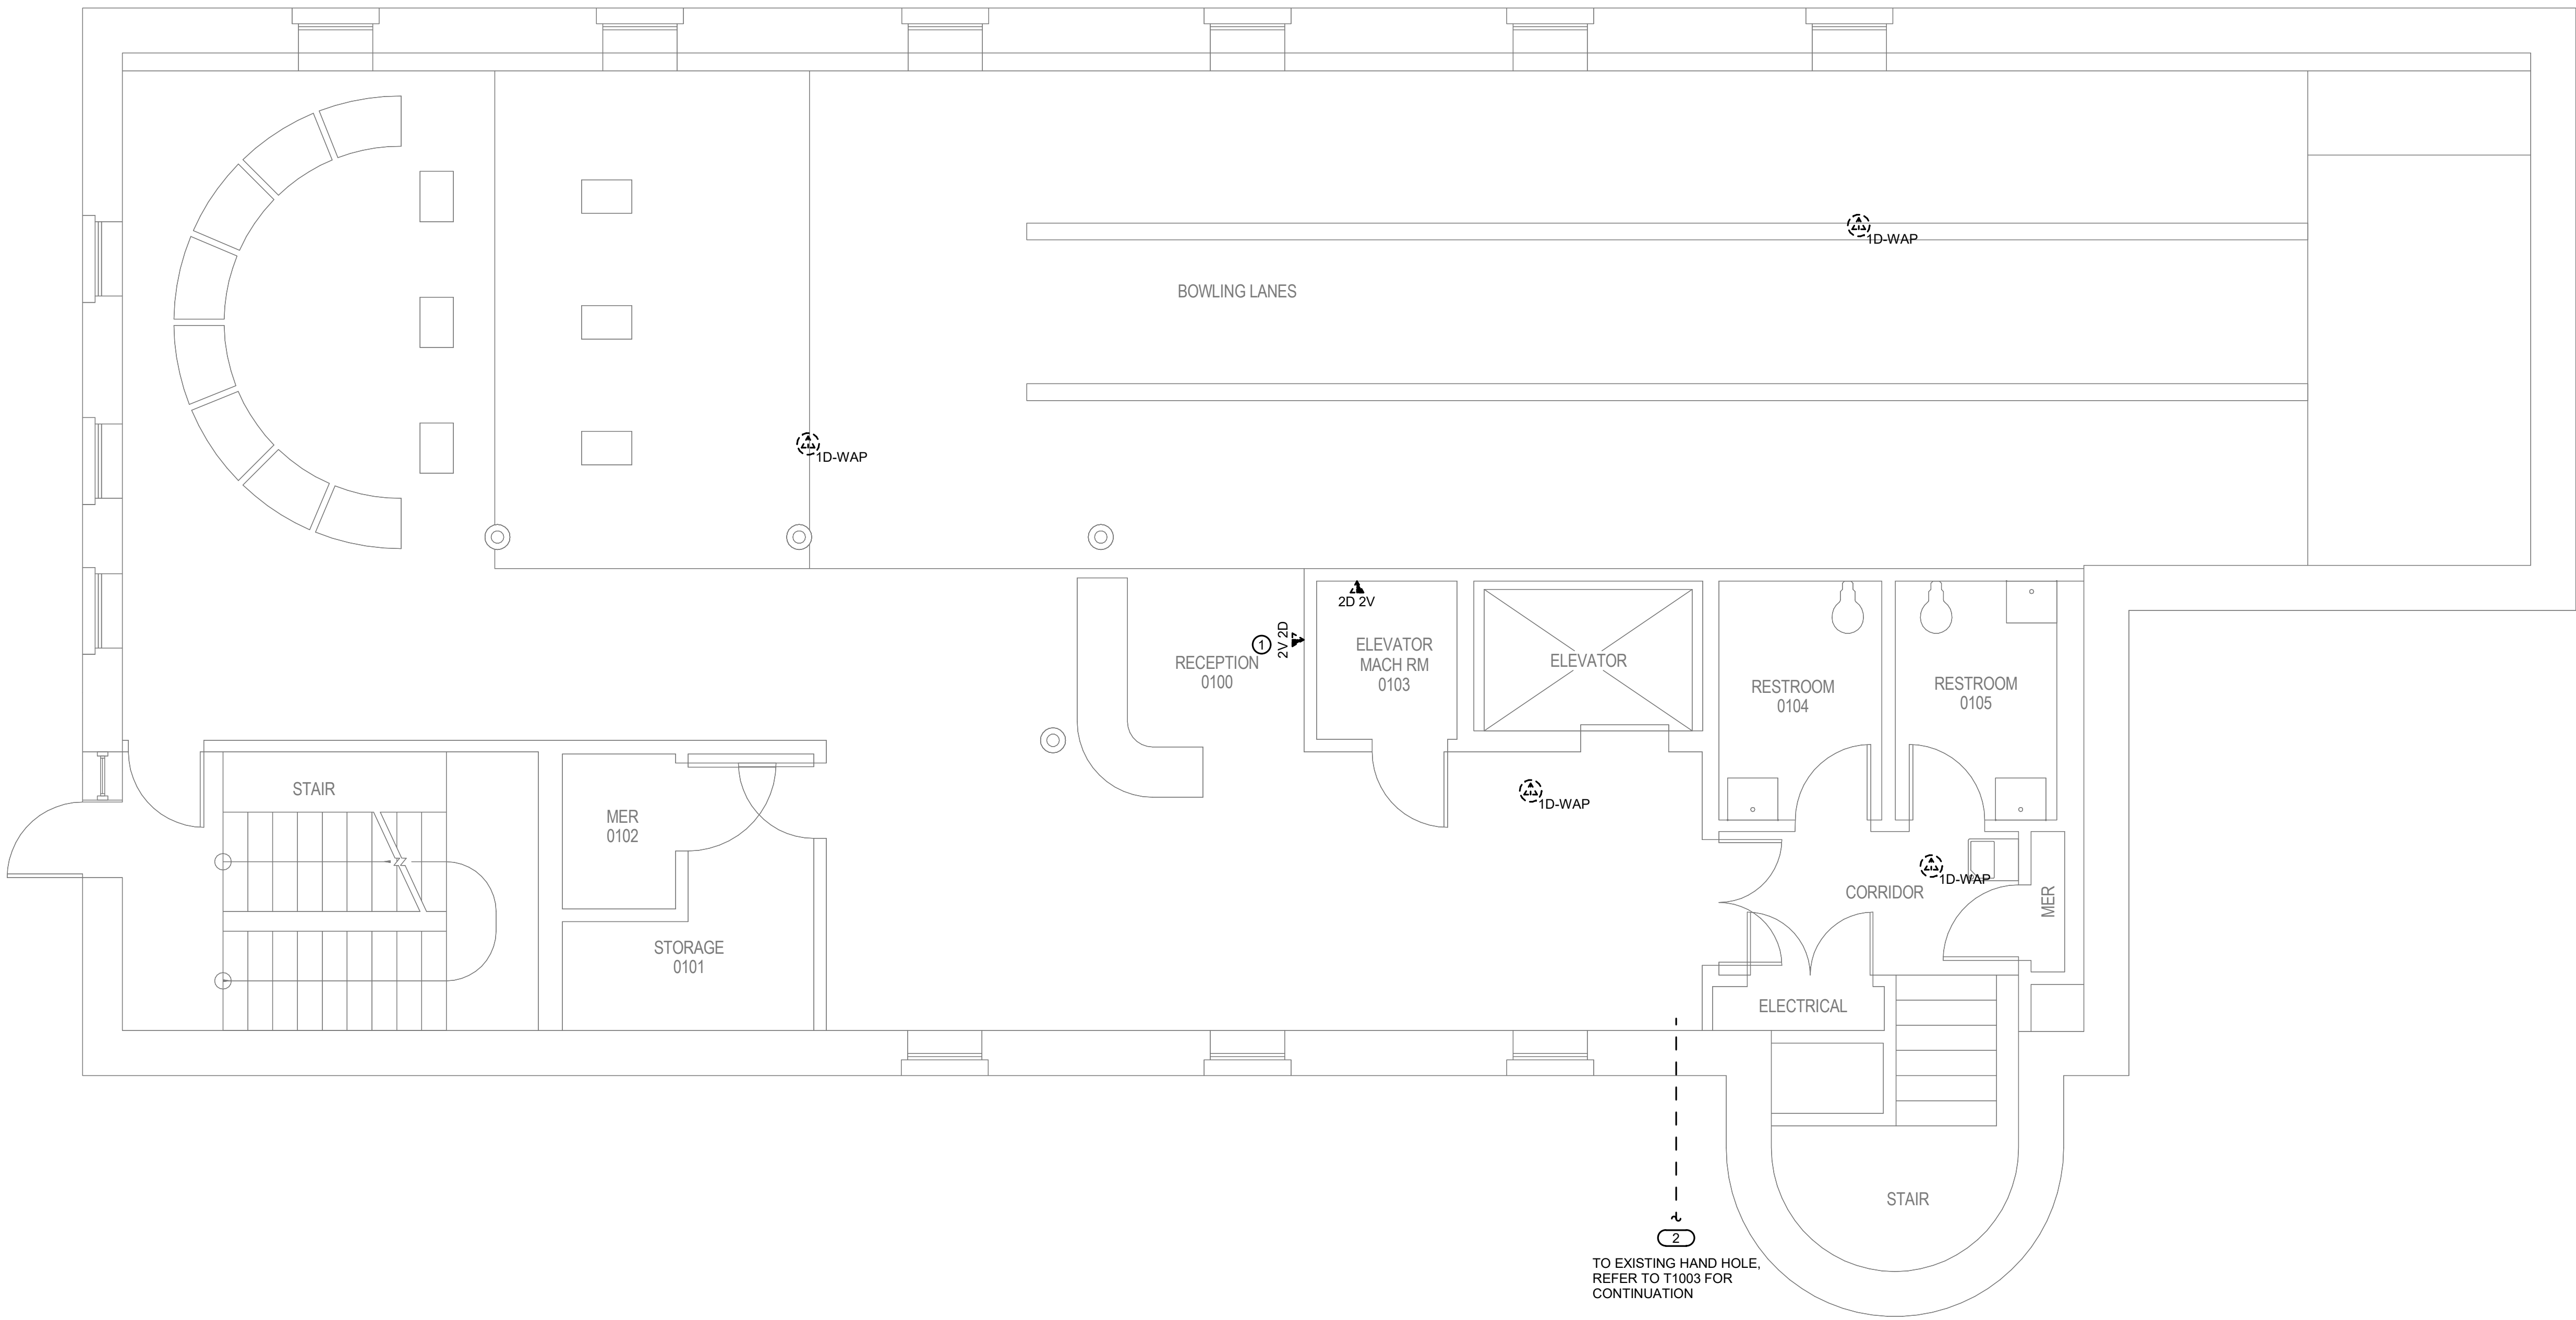

1 BUILDING 04 BASEMENT FLOOR DEMOLITION PLAN - TECHNOLOGY
1/4" = 1'-0"

35% SCHEMATIC DESIGN SUBMISSION	5.17.21
65% DESIGN DEVELOPMENT SUBMISSION	6.15.21
65% DESIGN DEVELOPMENT RESUBMISSION	8.25.21
Revisions:	Date:

CONSULTANT

IMEG
The Future is Here
15 SUNNEN DRIVE
SUITE 104
ST. LOUIS, MO 63143
P: 314.645.1132 F: 314.645.1173
PROJECT #18004375.03

ARCHITECT/ENGINEER OF RECORD

Romanyk Consulting
Focusing on what matters
Romanyk Consulting Corp. www.romanykconsulting.com
3308 Preston Road, Suite 350-164, Plano, Texas 75093

STAMP

Bicsi
DAVID LARSON
BICS1 ID # 106098
EXPIRES 12-31-25
REGISTERED COMMUNICATIONS DISTRIBUTION DESIGNER
RCDD

Office of
Construction
and Facilities
Management

VA U.S. Department
of Veterans Affairs

Drawing Title
BUILDING 04 BASEMENT DEMO PLAN -
TECHNOLOGY

Approved:

Phase
FINAL BID DOCUMENTS

Sprinklered
FULLY SPRINKLERED

Project Title
EHRM INFRASTRUCTURE
UPGRADES - MILWAUKEE, WI

Location
5000 W. NATIONAL AVENUE, MILWAUKEE, WI

Issue Date
SEPTEMBER 05, 2025









Checked
PHINIE

Drawn
MAIBEJ

Project Number
695-21-700

Building Number
04

Drawing Number
04-TD100

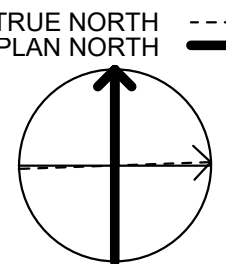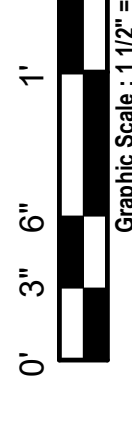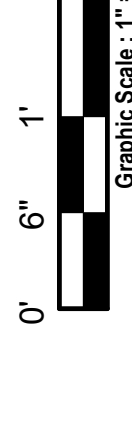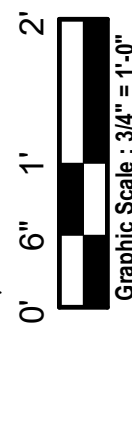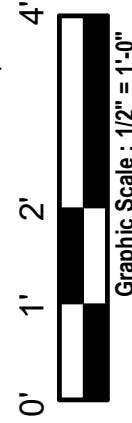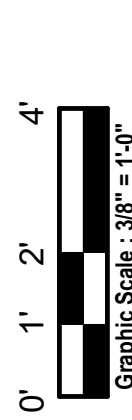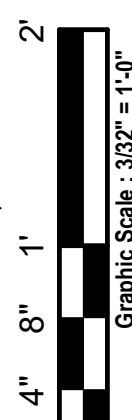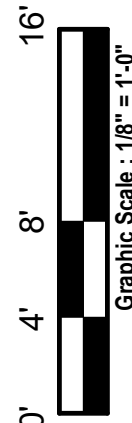

F

E

D

C


B

A


9/2/2025 3:54:37 PM

Autodesk Docs\DCFM East - Milwaukee EHRM (R24)T24_1804375\03_VA Milwaukee_C.dwt

- SHEET NOTES:**
1. REMOVE ALL NETWORK CABLING TO POINTS OF TERMINATION IN ASSOCIATED DATA CLOSET. REFER TO FLOOR PLANS AND SHEET T1001 FOR TR ROOM LOCATIONS.
 2. REFER TO ARCHITECTURAL PHASING PLANS FOR WHEN EXISTING CABLING IS ALLOWED TO BE DEMOLISHED.
 3. FOR ALL EXISTING WIRELESS ACCESS POINTS AND SURVEILLANCE CAMERAS, DEVICES SHALL REMAIN. SCOPE OF WORK INCLUDES CABLE REPLACEMENT ONLY. COORDINATE WITH COR FOR ANY DOWNTIME OF DEVICES. EXISTING LOCATIONS OF WORK AREA, OUTLETS SHOWN ON THIS SHEET MAY NOT NECESSARILY BE IN THE EXACT LOCATION AS IDENTIFIED.

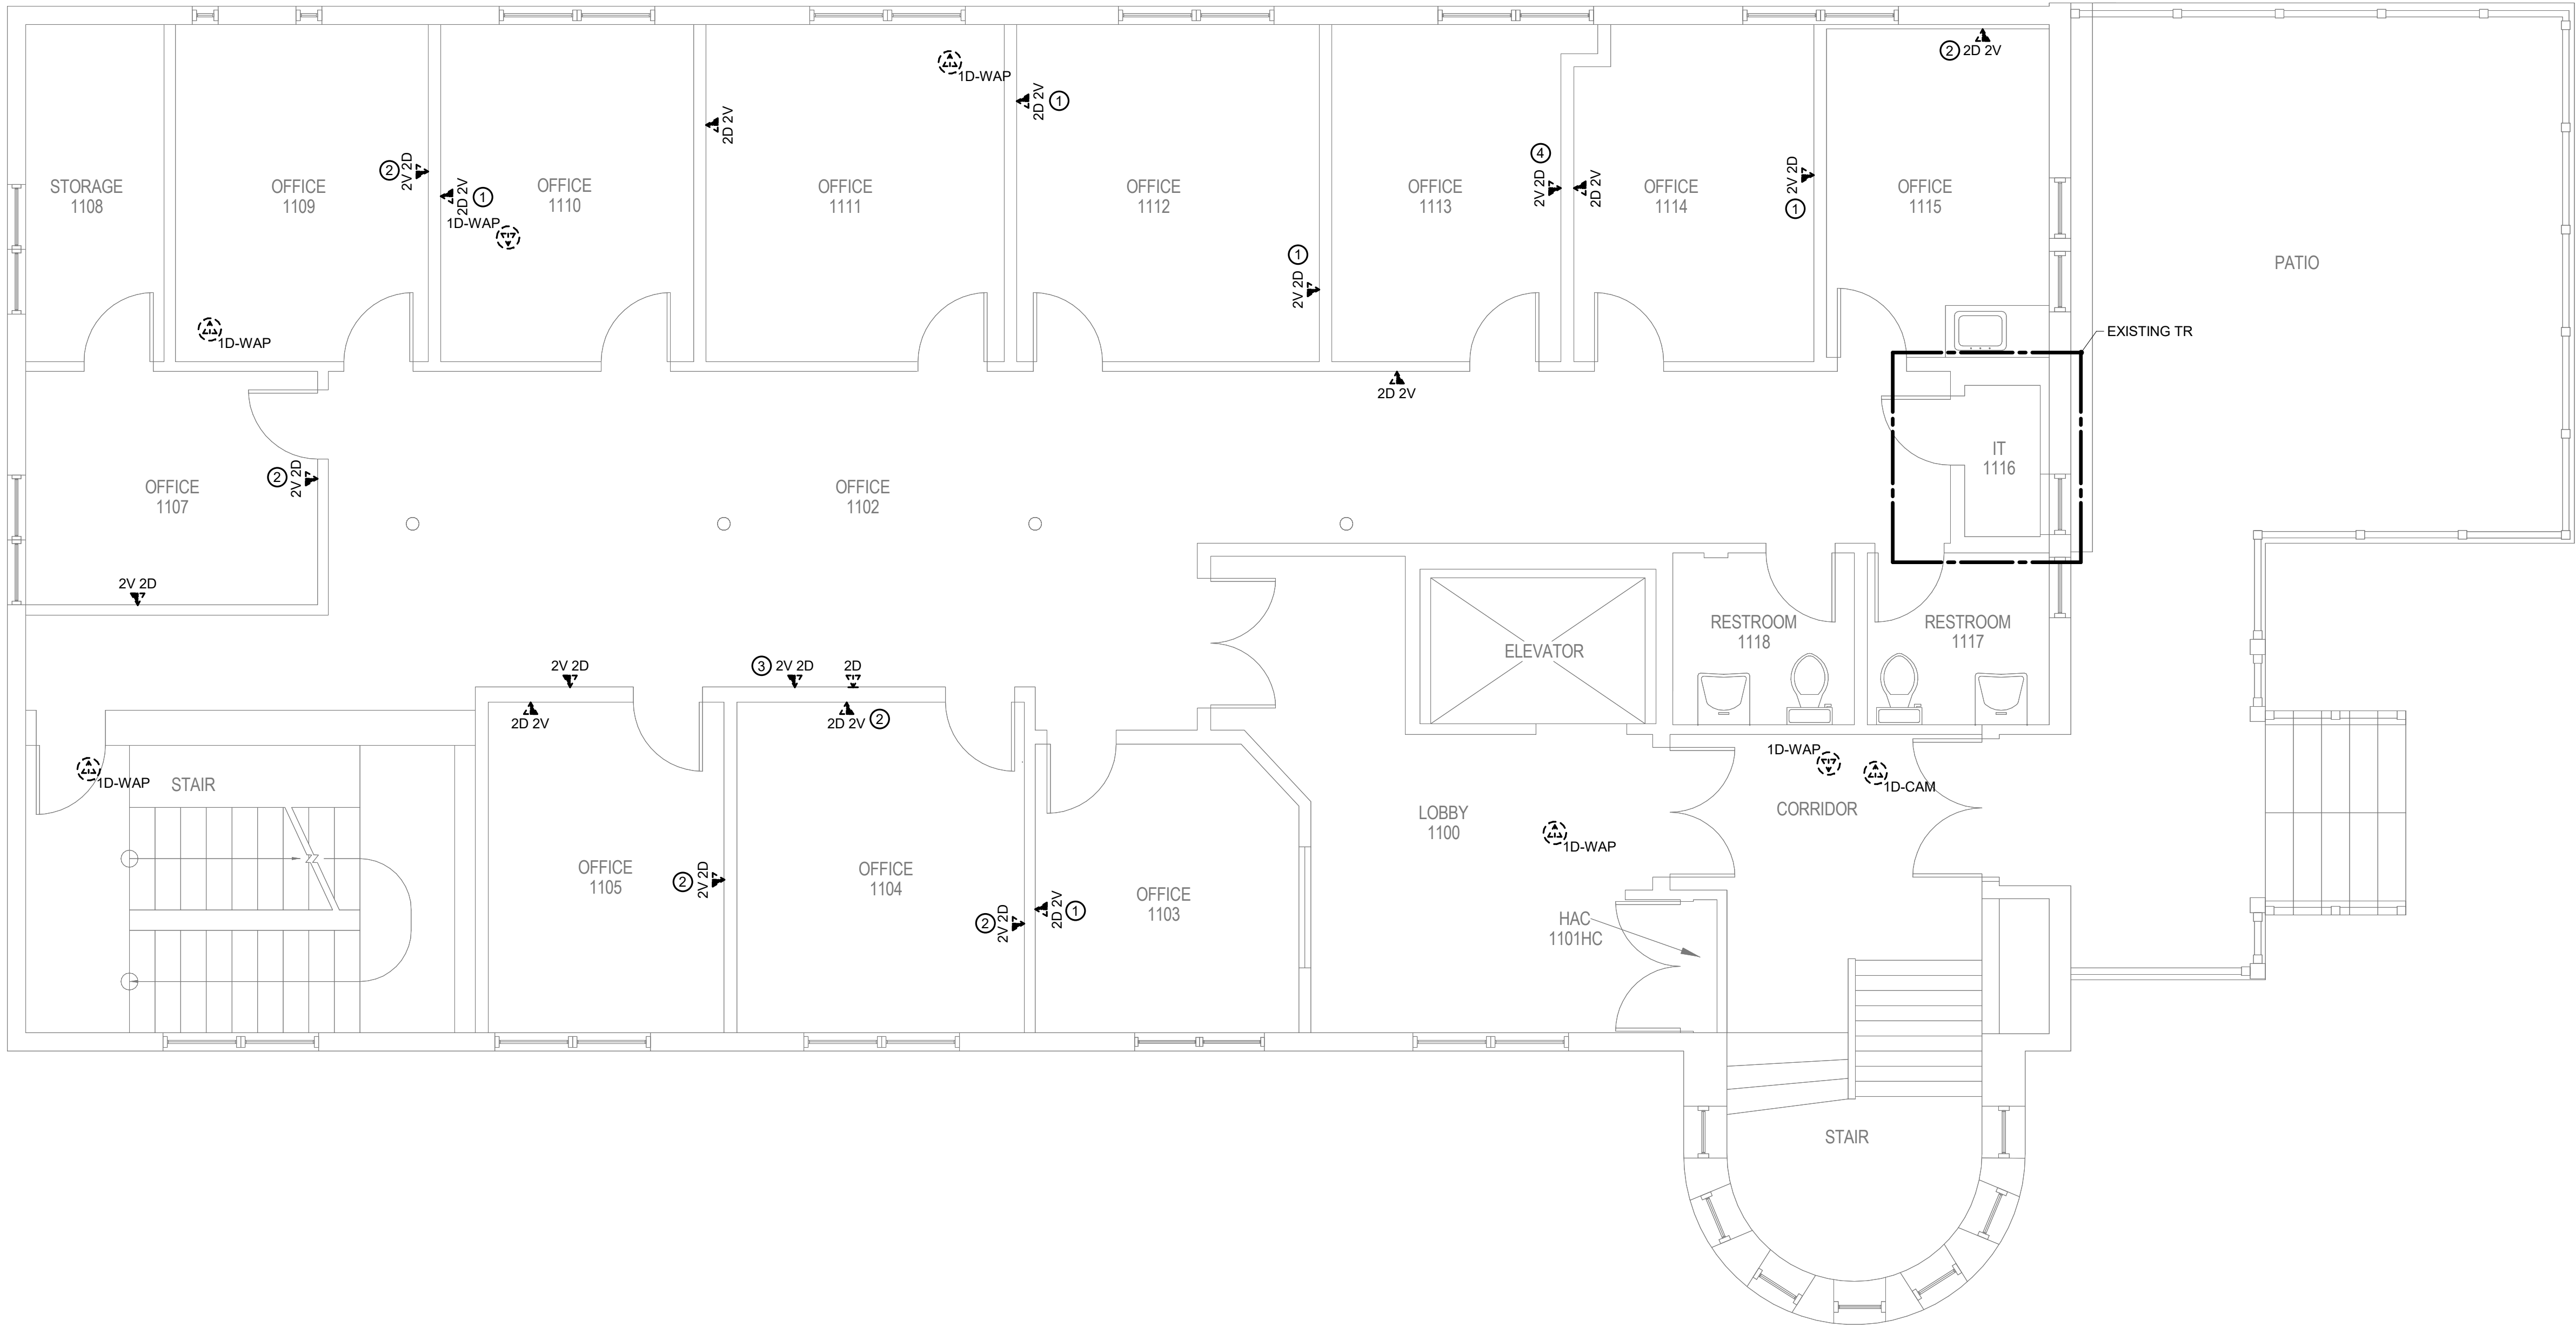

1 BUILDING 04 FIRST FLOOR DEMOLITION PLAN - TECHNOLOGY
1/4" = 1'-0"

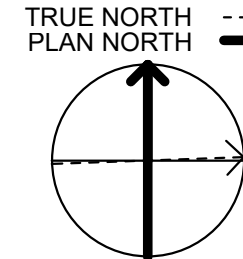

35% SCHEMATIC DESIGN SUBMISSION	5.17.21
65% DESIGN DEVELOPMENT SUBMISSION	6.15.21
65% DESIGN DEVELOPMENT RESUBMISSION	8.25.21
Revisions:	Date:

CONSULTANT

IMEG
15 SUNNEN DRIVE
SUITE 104
ST. LOUIS, MO 63143
P: 314.645.1132 F: 314.645.1173
PROJECT #1804375.03

ARCHITECT/ENGINEER OF RECORD

Romanyk Consulting
Focusing on what matters
Romanyk Consulting Corp. www.romanykconsulting.com
3308 Preston Road, Suite 350-164, Plano, Texas 75093

STAMP

Bicsi
DAVID LARSON
BICS1 ID # 106098
EXPIRES 12-31-25
REGISTERED COMMUNICATIONS DISTRIBUTION DESIGNER

Office of
Construction
and Facilities
Management

VA U.S. Department
of Veterans Affairs

Drawing Title
BUILDING 04 FIRST FLOOR DEMO PLAN -
TECHNOLOGY

Approved:

Phase
FINAL BID DOCUMENTS

Sprinklered
FULLY SPRINKLERED

Project Title
EHRM INFRASTRUCTURE
UPGRADES - MILWAUKEE, WI

Location
5000 W. NATIONAL AVENUE, MILWAUKEE, WI

Issue Date
SEPTEMBER 05, 2025

Checked
PHINIE

Drawn
MAIBEJ

Project Number
695-21-700

Building Number
04

Drawing Number
04-TD101

F

E

D

C


B

A


9/2/2025 3:54:38 PM

Autodesk Docs\DOCFM East - Milwaukee EHRM (R24)T24_1804375\03_VA Milwaukee_C.rvt

- SHEET NOTES:**
1. REMOVE ALL NETWORK CABLING TO POINTS OF TERMINATION IN ASSOCIATED DATA CLOSET. REFER TO FLOOR PLANS AND SHEET T1001 FOR TR ROOM LOCATIONS.
 2. REFER TO ARCHITECTURAL PHASING PLANS FOR WHEN EXISTING CABLING IS ALLOWED TO BE DEMOLISHED.
 3. FOR ALL EXISTING WIRELESS ACCESS POINTS AND SURVEILLANCE CAMERAS, DEVICES SHALL REMAIN. SCOPE OF WORK INCLUDES CABLE REPLACEMENT ONLY. COORDINATE WITH COR FOR ANY DOWNTIME OF DEVICES. EXISTING LOCATIONS OF WORK AREA OUTLETS SHOWN ON THIS SHEET MAY NOT NECESSARILY BE IN THE EXACT LOCATION AS IDENTIFIED.

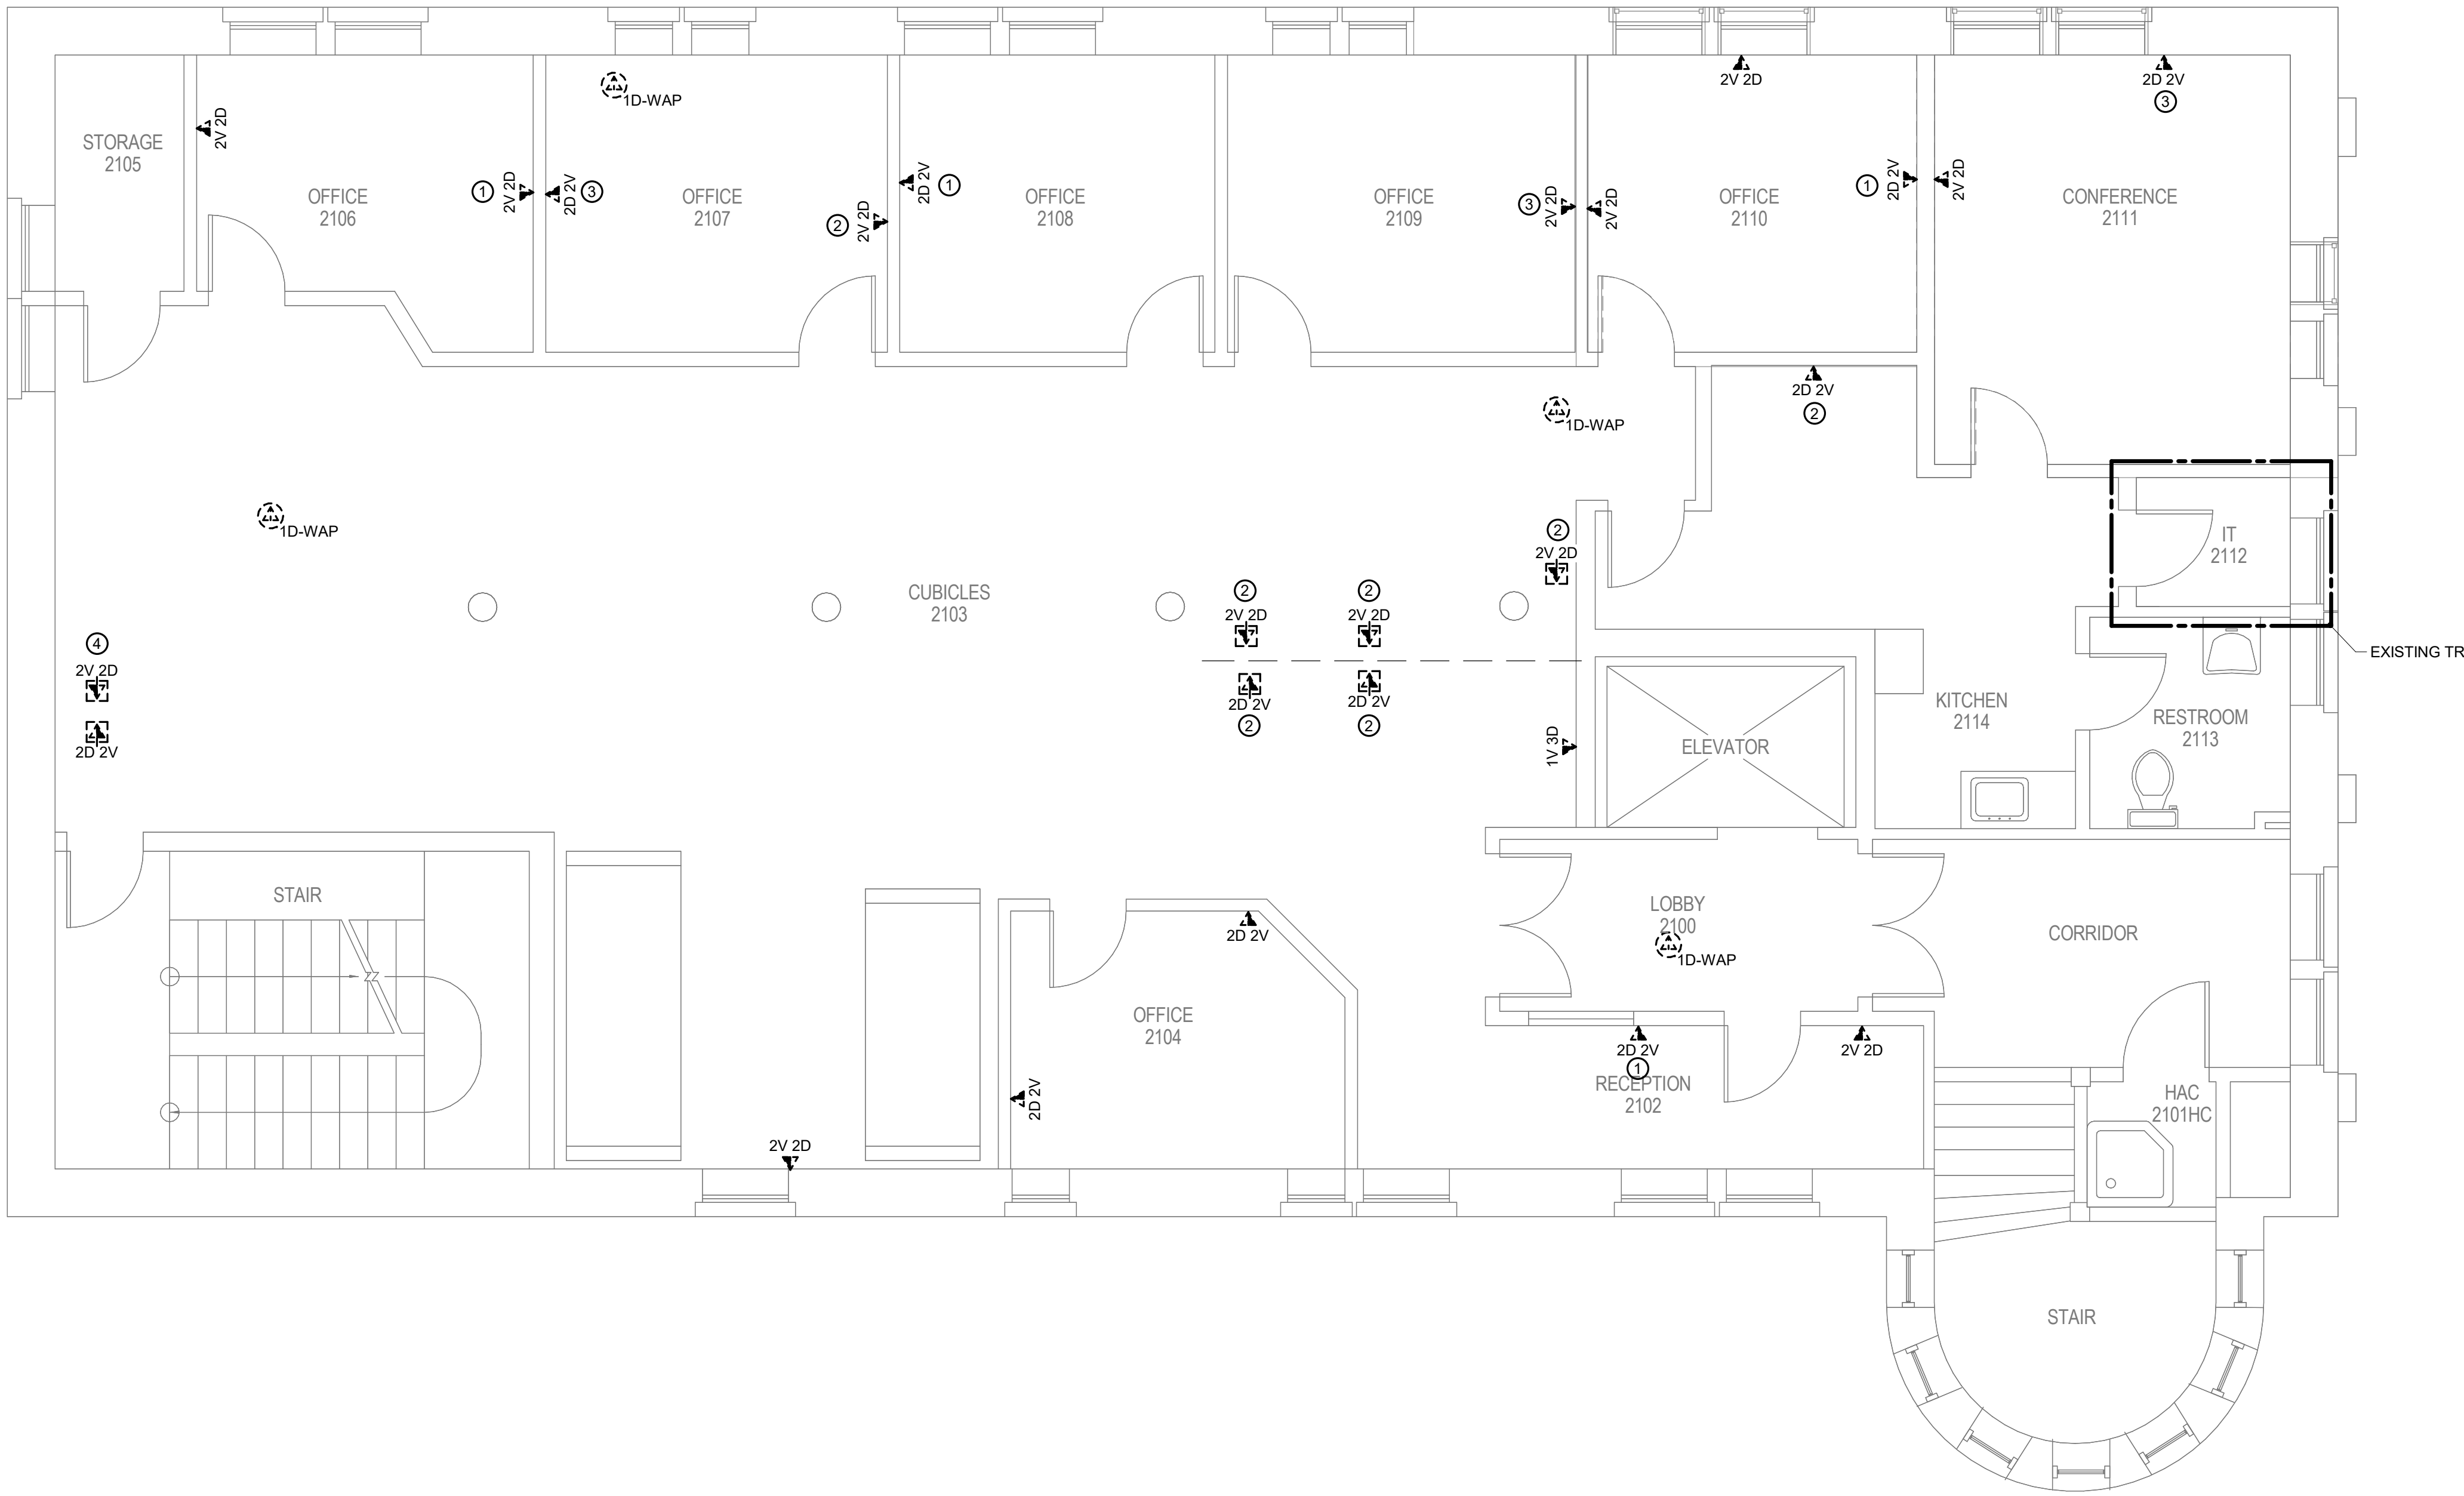

1 BUILDING 04 SECOND FLOOR DEMOLITION PLAN - TECHNOLOGY
1/4" = 1'-0"

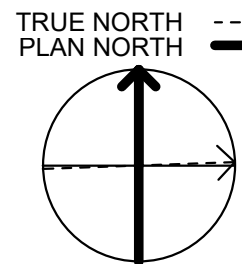

35% SCHEMATIC DESIGN SUBMISSION	5.17.21
65% DESIGN DEVELOPMENT SUBMISSION	6.15.21
65% DESIGN DEVELOPMENT RESUBMISSION	8.25.21
Revisions:	Date:

CONSULTANT

IMEG
The Future is Here
15 SUNNEN DRIVE
SUITE 104
ST. LOUIS, MO 63143
P: 314.645.1132 F: 314.645.1173
PROJECT #18004375.03

ARCHITECT/ENGINEER OF RECORD

Romanyk Consulting
Focusing on what matters
Romanyk Consulting Corp. www.romanykconsulting.com
3308 Preston Road, Suite 350-164, Plano, Texas 75093

STAMP

Bicsi
DAVID LARSON
BICS1 ID # 106098
EXPIRES 12-31-25
REGISTERED COMMUNICATIONS DISTRIBUTION DESIGNER
RCDD

Office of Construction and Facilities Management

VA U.S. Department of Veterans Affairs

Drawing Title
BUILDING 04 SECOND FLOOR DEMO PLAN - TECHNOLOGY

Approved:

Phase
FINAL BID DOCUMENTS

Sprinklered
FULLY SPRINKLERED

Project Title
EHRM INFRASTRUCTURE UPGRADES - MILWAUKEE, WI

Location
5000 W. NATIONAL AVENUE MILWAUKEE, WI

Issue Date
SEPTEMBER 05, 2025


Checked
PHINIE

Drawn
MAIBEJ

Project Number
695-21-700

Building Number
04

Drawing Number
04-TD102

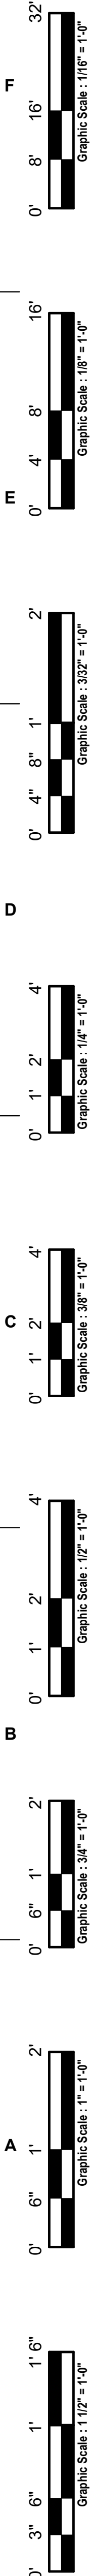

F

E

D

C


B

A


9/2/2025 3:54:39 PM

Autodesk Docs\DCFM East - Milwaukee EHRM (R24)T24_1804375\03_VA Milwaukee EHRM_C.rvt

- SHEET NOTES:**
1. ALL NETWORK CABLES ON THIS SHEET SHALL TERMINATE IN TR-4-2110.
 2. REFER TO CIVIL DRAWINGS AND T1003 FOR ADDITIONAL PATHWAY INFORMATION.
 3. CONTRACTOR TO PROVIDE NEW J-HOOK ROUTES FOR ALL NEW CABLING. J-HOOK SIZE AND QUANTITY TO BE PER MANUFACTURER RECOMMENDATIONS.
 4. REFER TO TN500-TN509 FOR RISER DIAGRAMS.
 5. REFER TO SHEET TN402 FOR PENETRATION DETAILS.
 6. THESE DRAWINGS MAKE THE BEST ATTEMPT TO IDENTIFY EXISTING DATA DROPS/WORK AREA OUTLETS. AS LONG AS THE TOTAL NEWLY INSTALLED DATA DROP COUNT DOES NOT VARY +/- 10% IDENTIFIED ON THESE DRAWINGS, THE CONTRACTOR'S SCOPE SHALL BE UNCHANGED.
 7. NEW WORK AREA OUTLETS SHALL BE LOCATED IN EXISTING BOXES. WORK AREA OUTLETS SHOWN ON THIS SHEET MAY NOT BE IN THE EXACT LOCATION AS IDENTIFIED.
 8. CONTRACTOR TO INCLUDE AN ALLOWANCE FOR 10% ADDITIONAL 2-PORTS CAT6A INFORMATION OUTLETS IN THEIR PROPOSAL FOR THIS SHEET. FUTURE INFORMATION OUTLET LOCATIONS WILL BE DETERMINED BY THE VA AT A LATER DATE.
- KEYNOTES:** C #
1. TWO (2) 4" CONDUITS TO BACKBONE PATH.
 2. EXISTING BACKBONE ENTRY POINT. PROTECT IN PLACE. DEMOLISH EXISTING FIBER OPTIC CABLE TO POINTS OF TERMINATION AFTER REDUNDANT PATH IS INSTALLED AND OPERATIONAL. REFER TO ARCHITECTURAL PHASING PLAN FOR ADDITIONAL INFORMATION. CONDUIT ENTERS ON LOWER LEVEL.

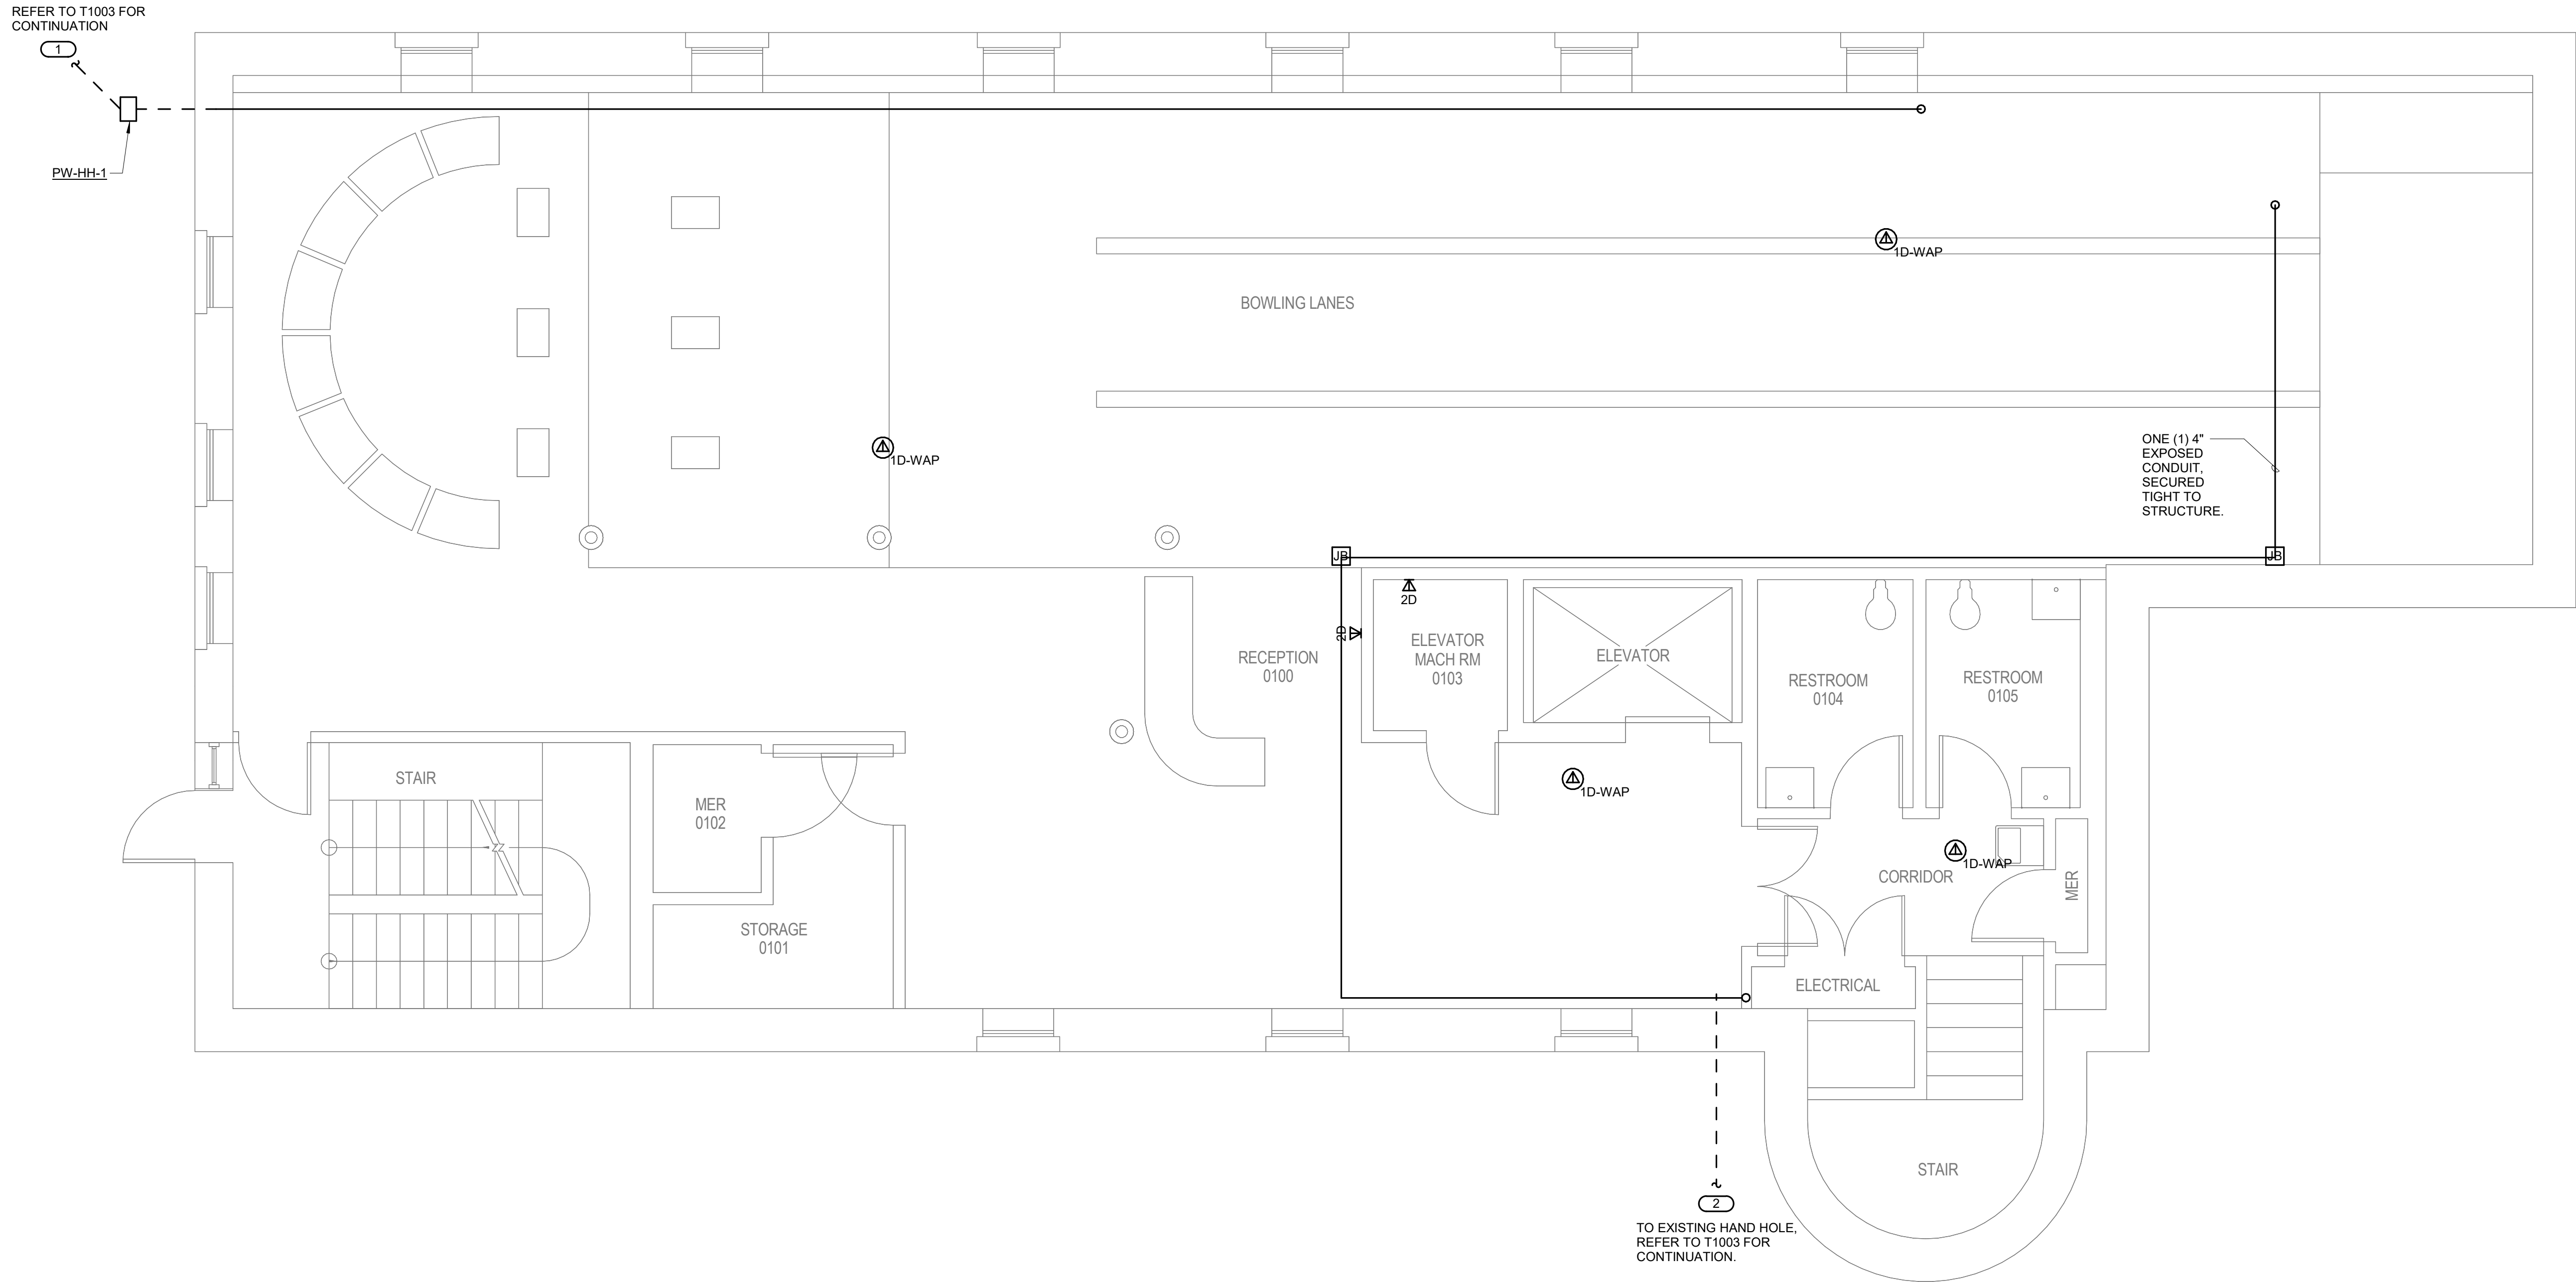

1 BUILDING 04 BASEMENT PLAN - TECHNOLOGY
1/4" = 1'-0"

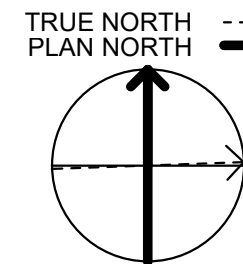

35% SCHEMATIC DESIGN SUBMISSION	5.17.21
65% DESIGN DEVELOPMENT SUBMISSION	6.15.21
65% DESIGN DEVELOPMENT RESUBMISSION	8.25.21
Revisions:	Date:

CONSULTANT

IMEG
The Future is a Better One
15 SUNNEN DRIVE
SUITE 104
ST. LOUIS, MO 63143
P: 314.645.1132 F: 314.645.1173
PROJECT #18004375.03

ARCHITECT/ENGINEER OF RECORD

Romanyk Consulting
Focusing on what matters

Romanyk Consulting Corp. www.romanykconsulting.com
3308 Preston Road, Suite 350-164, Plano, Texas 75093

STAMP

Bicsi
DAVID LARSON
BICS1 ID # 106098
EXPIRES 12-31-25
REGISTERED COMMUNICATIONS DISTRIBUTION DESIGNER
RCDD

Office of
Construction
and Facilities
Management

VA U.S. Department
of Veterans Affairs

Drawing Title
BUILDING 04 BASEMENT PLAN - TECHNOLOGY

Approved:

Phase
FINAL BID DOCUMENTS

Sprinklered
FULLY SPRINKLERED

Project Title
EHRM INFRASTRUCTURE
UPGRADES - MILWAUKEE, WI

Location
5000 W. NATIONAL AVENUE, MILWAUKEE, WI

Issue Date
SEPTEMBER 05, 2025


Checked
PHINIE


Drawn
MAIBEJ

Project Number
695-21-700

Building Number
04



Drawing Number
04-TN100

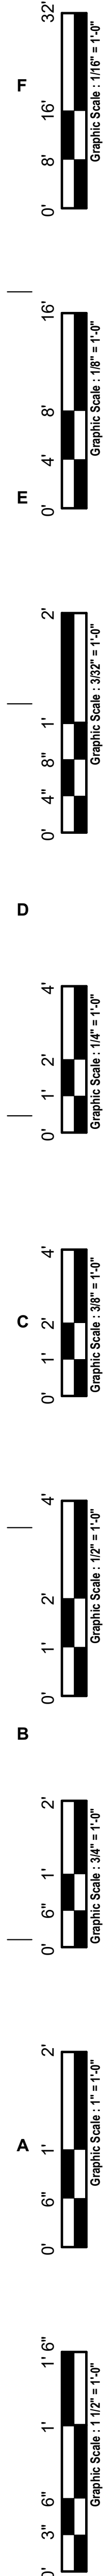

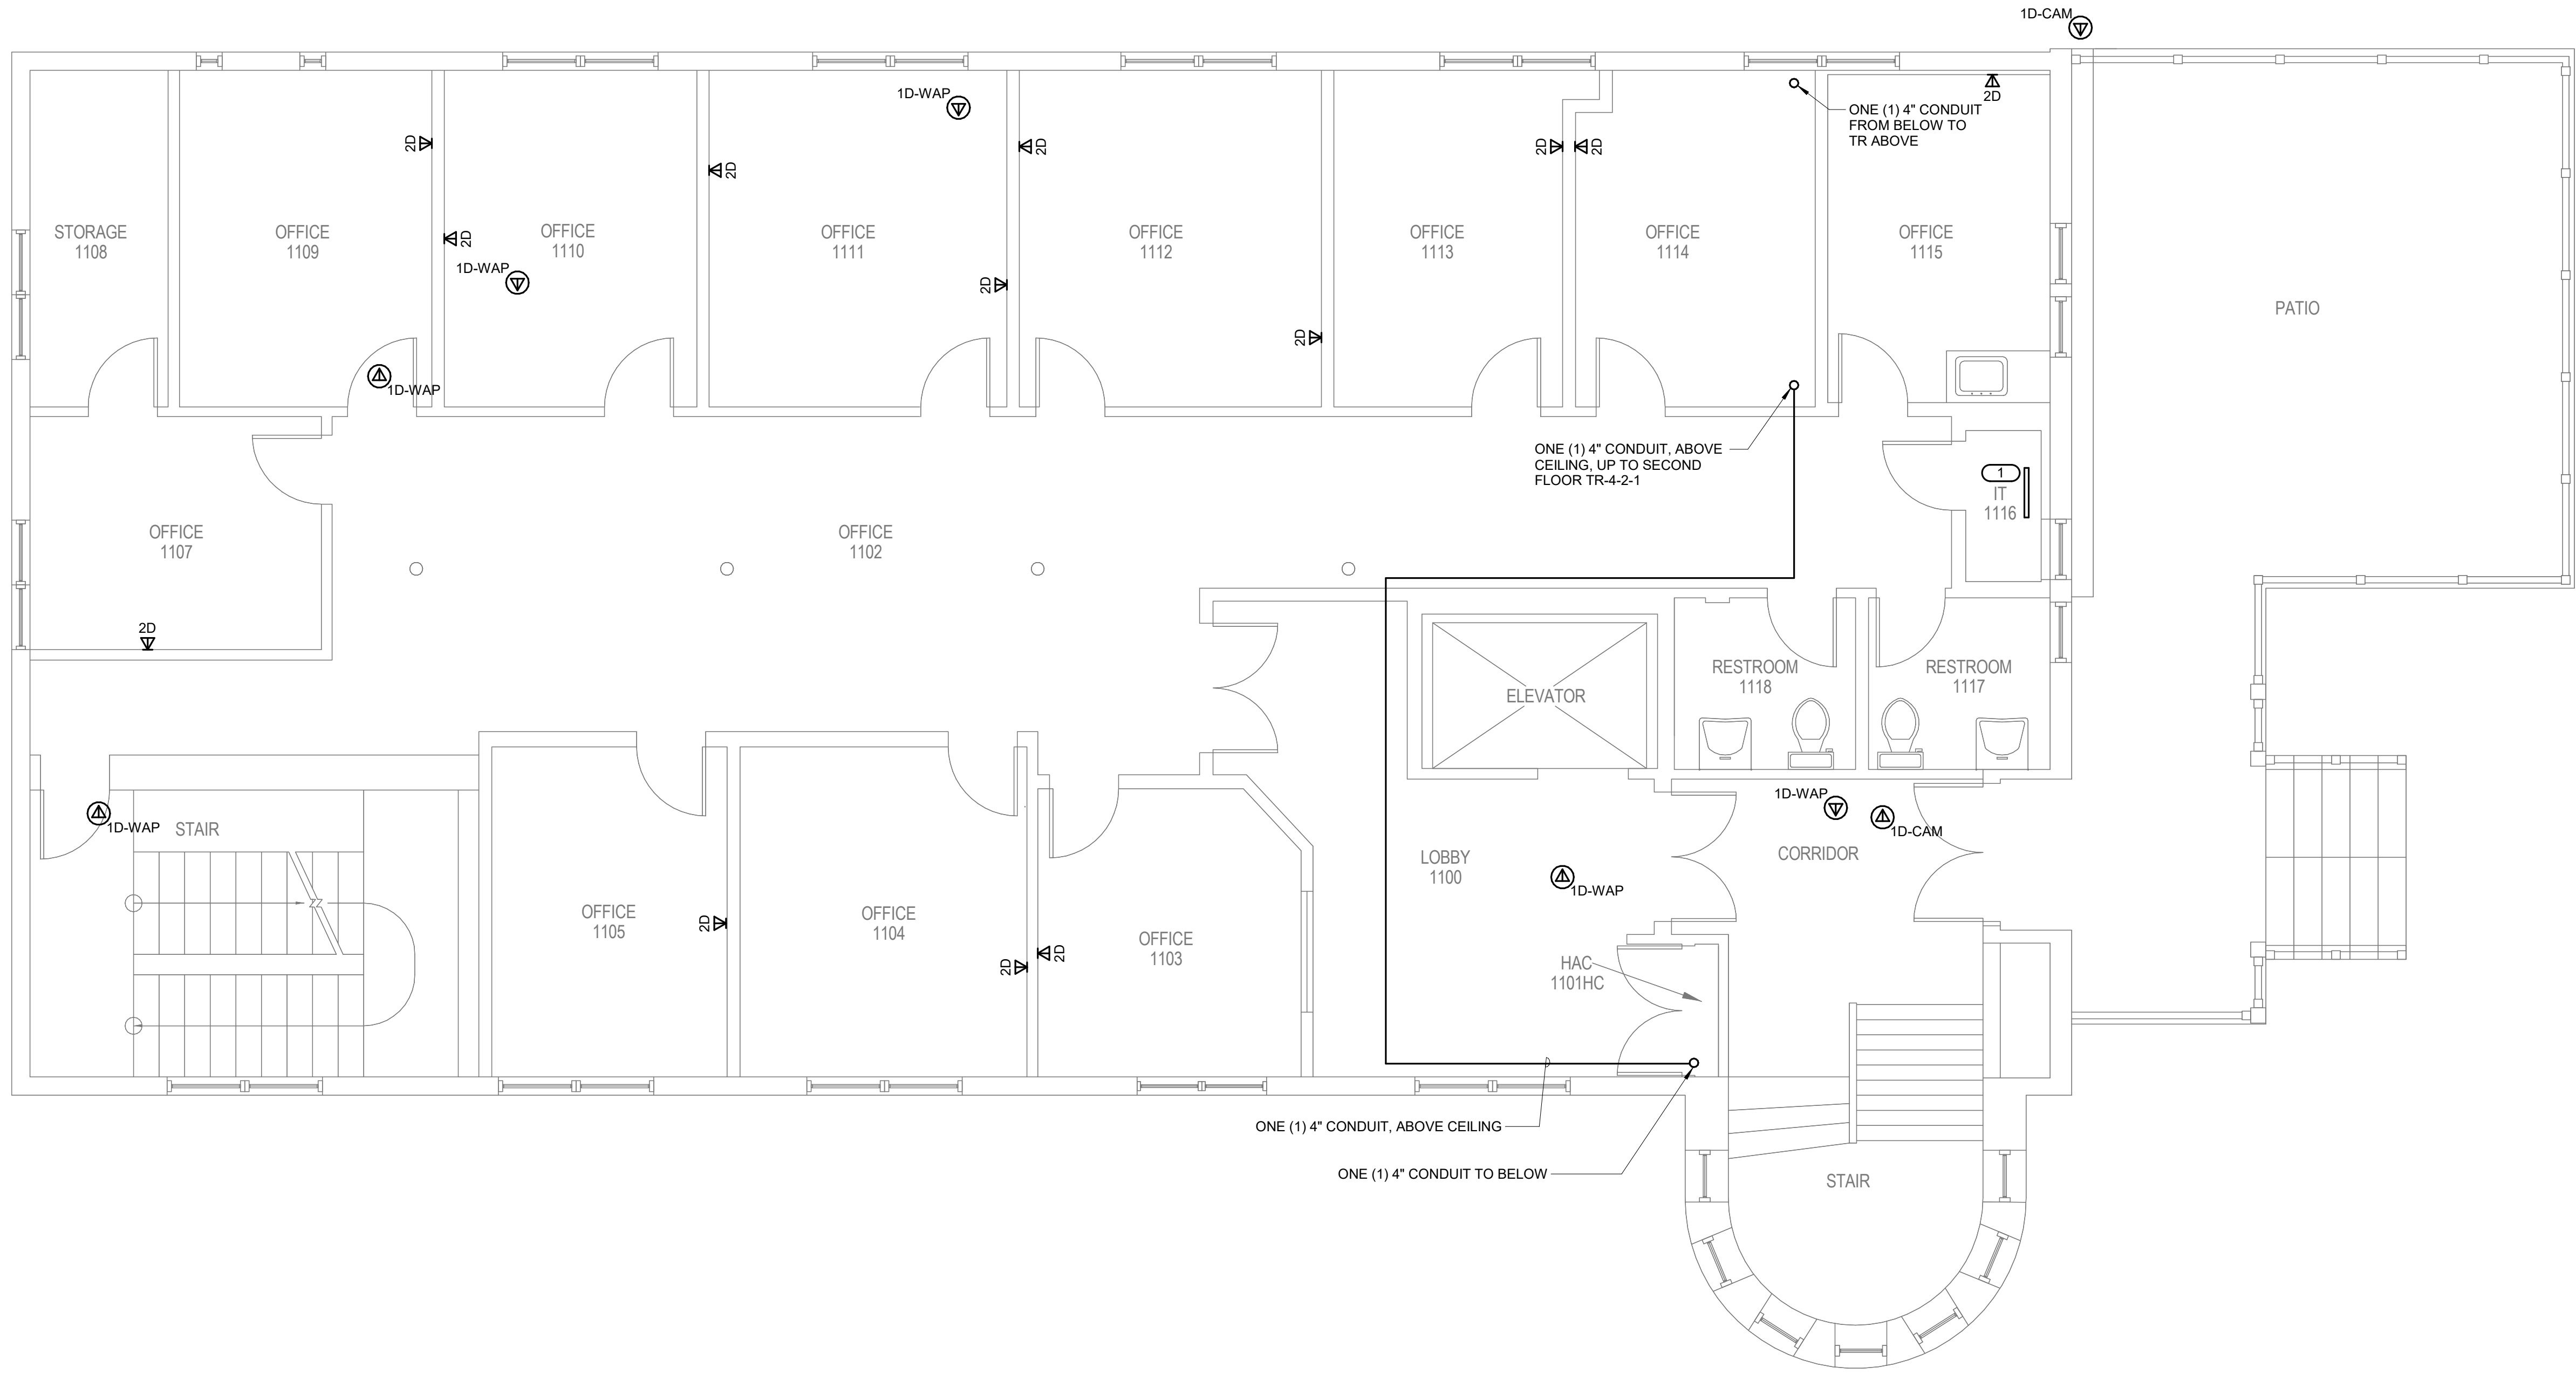

1 BUILDING 04 FIRST FLOOR PLAN - TECHNOLOGY
1/4" = 1'-0"

- SHEET NOTES:**
1. REFER TO 1/TN400 FOR TECHNOLOGY ROUGH IN DETAIL.
 2. ALL NETWORK CABLES ON THIS SHEET SHALL TERMINATE IN TR-4-2110.
 3. CONTRACTOR TO PROVIDE NEW J-HOOK ROUTES FOR ALL NEW CABLING. J-HOOK SIZE AND QUANTITY TO BE PER MANUFACTURER RECOMMENDATIONS.
 4. REFER TO TN500-TN509 FOR RISER DIAGRAMS.
 5. REFER TO SHEET TN400 FOR PENETRATION DETAILS.
 6. THESE DRAWINGS MAKE THE BEST ATTEMPT TO IDENTIFY EXISTING DATA DROPS/WORK AREA OUTLETS. AS LONG AS THE TOTAL NEWLY INSTALLED DATA DROP COUNT DOES NOT VARY +/- 10% IDENTIFIED ON THESE DRAWINGS, THE CONTRACTOR'S SCOPE SHALL BE UNCHANGED.
 7. NEW WORK AREA OUTLETS SHALL BE LOCATED IN EXISTING BOXES. WORK AREA OUTLETS SHOWN ON THIS SHEET MAY NOT BE IN THE EXACT LOCATION AS IDENTIFIED.
 8. CONTRACTOR TO INCLUDE AN ALLOWANCE FOR 10% ADDITIONAL 2-PORTS CAT6A INFORMATION OUTLETS IN THEIR PROPOSAL FOR THIS SHEET. FUTURE INFORMATION OUTLET LOCATIONS WILL BE DETERMINED BY THE VA AT A LATER DATE.
- KEYNOTES:** (#)
1. PROVIDE 25 PAIR VOICE COPPER CABLE FROM EXISTING WALL FIELD TO NEW TR, ROOM 2110.

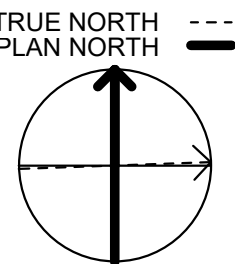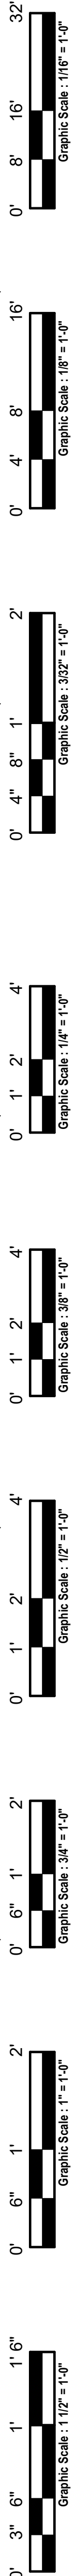

35% SCHEMATIC DESIGN SUBMISSION	5.17.21
65% DESIGN DEVELOPMENT SUBMISSION	6.15.21
65% DESIGN DEVELOPMENT RESUBMISSION	8.25.21
Revisions:	Date:

CONSULTANT

IMEG

15 SUNNEN DRIVE
SUITE 104
ST. LOUIS, MO 63143
P: 314.645.1132 F: 314.645.1173
PROJECT #18004375.03

ARCHITECT/ENGINEER OF RECORD

Romanyk Consulting
Focusing on what matters

Romanyk Consulting Corp. www.romanykconsulting.com
3308 Preston Road, Suite 350-164, Plano, Texas 75093

STAMP

Bicsi
DAVID LARSON
BICS1 ID # 106098
EXPIRES 12-31-25
REGISTERED COMMUNICATIONS DISTRIBUTION DESIGNER

Office of
Construction
and Facilities
Management

VA U.S. Department
of Veterans Affairs

Drawing Title
BUILDING 04 FIRST FLOOR PLAN - TECHNOLOGY

Approved:

Phase
FINAL BID DOCUMENTS

Sprinklered
FULLY SPRINKLERED

Project Title
EHRM INFRASTRUCTURE
UPGRADES - MILWAUKEE, WI

Location
5000 W. NATIONAL AVENUE MILWAUKEE, WI

Issue Date
SEPTEMBER 05, 2025

Checked
PHINIE

Drawn
MAIBEJ

Project Number
695-21-700

Building Number
04

Drawing Number
04-TN101

F

E

D

C


B

A


9/20/2025 3:54:41 PM

Autodesk Docs\DCFM East - Milwaukee EHRM (R24)T24_1804375\03_VA Milwaukee_C.dwt

- SHEET NOTES:**
1. REFER TO 1/TN400 FOR TECHNOLOGY ROUGH IN DETAIL.
 2. ALL NETWORK CABLES ON THIS SHEET SHALL TERMINATE IN TR-4-2110.
 3. CONTRACTOR TO PROVIDE NEW J-HOOK ROUTES FOR ALL NEW CABLING J-HOOK SIZE AND QUANTITY TO BE PER MANUFACTURER RECOMMENDATIONS.
 4. REFER TO TN500-TN509 FOR RISER DIAGRAMS.
 5. REFER TO SHEET TN402 FOR PENETRATION DETAILS.
 6. THESE DRAWINGS MAKE THE BEST ATTEMPT TO IDENTIFY EXISTING DATA DROPS/WORK AREA OUTLETS. AS LONG AS THE TOTAL NEWLY INSTALLED DATA DROP COUNT DOES NOT VARY +/- 10% IDENTIFIED ON THESE DRAWINGS, THE CONTRACTOR'S SCOPE SHALL BE UNCHANGED.
 7. NEW WORK AREA OUTLETS SHALL BE LOCATED IN EXISTING BOXES. WORK AREA OUTLETS SHOWN ON THIS SHEET MAY NOT BE IN THE EXACT LOCATION AS IDENTIFIED.
 8. CONTRACTOR TO INCLUDE AN ALLOWANCE FOR 10% ADDITIONAL 2-PORTS CAT6A INFORMATION OUTLETS IN THEIR PROPOSAL FOR THIS SHEET. FUTURE INFORMATION OUTLET LOCATIONS WILL BE DETERMINED BY THE VA AT A LATER DATE.

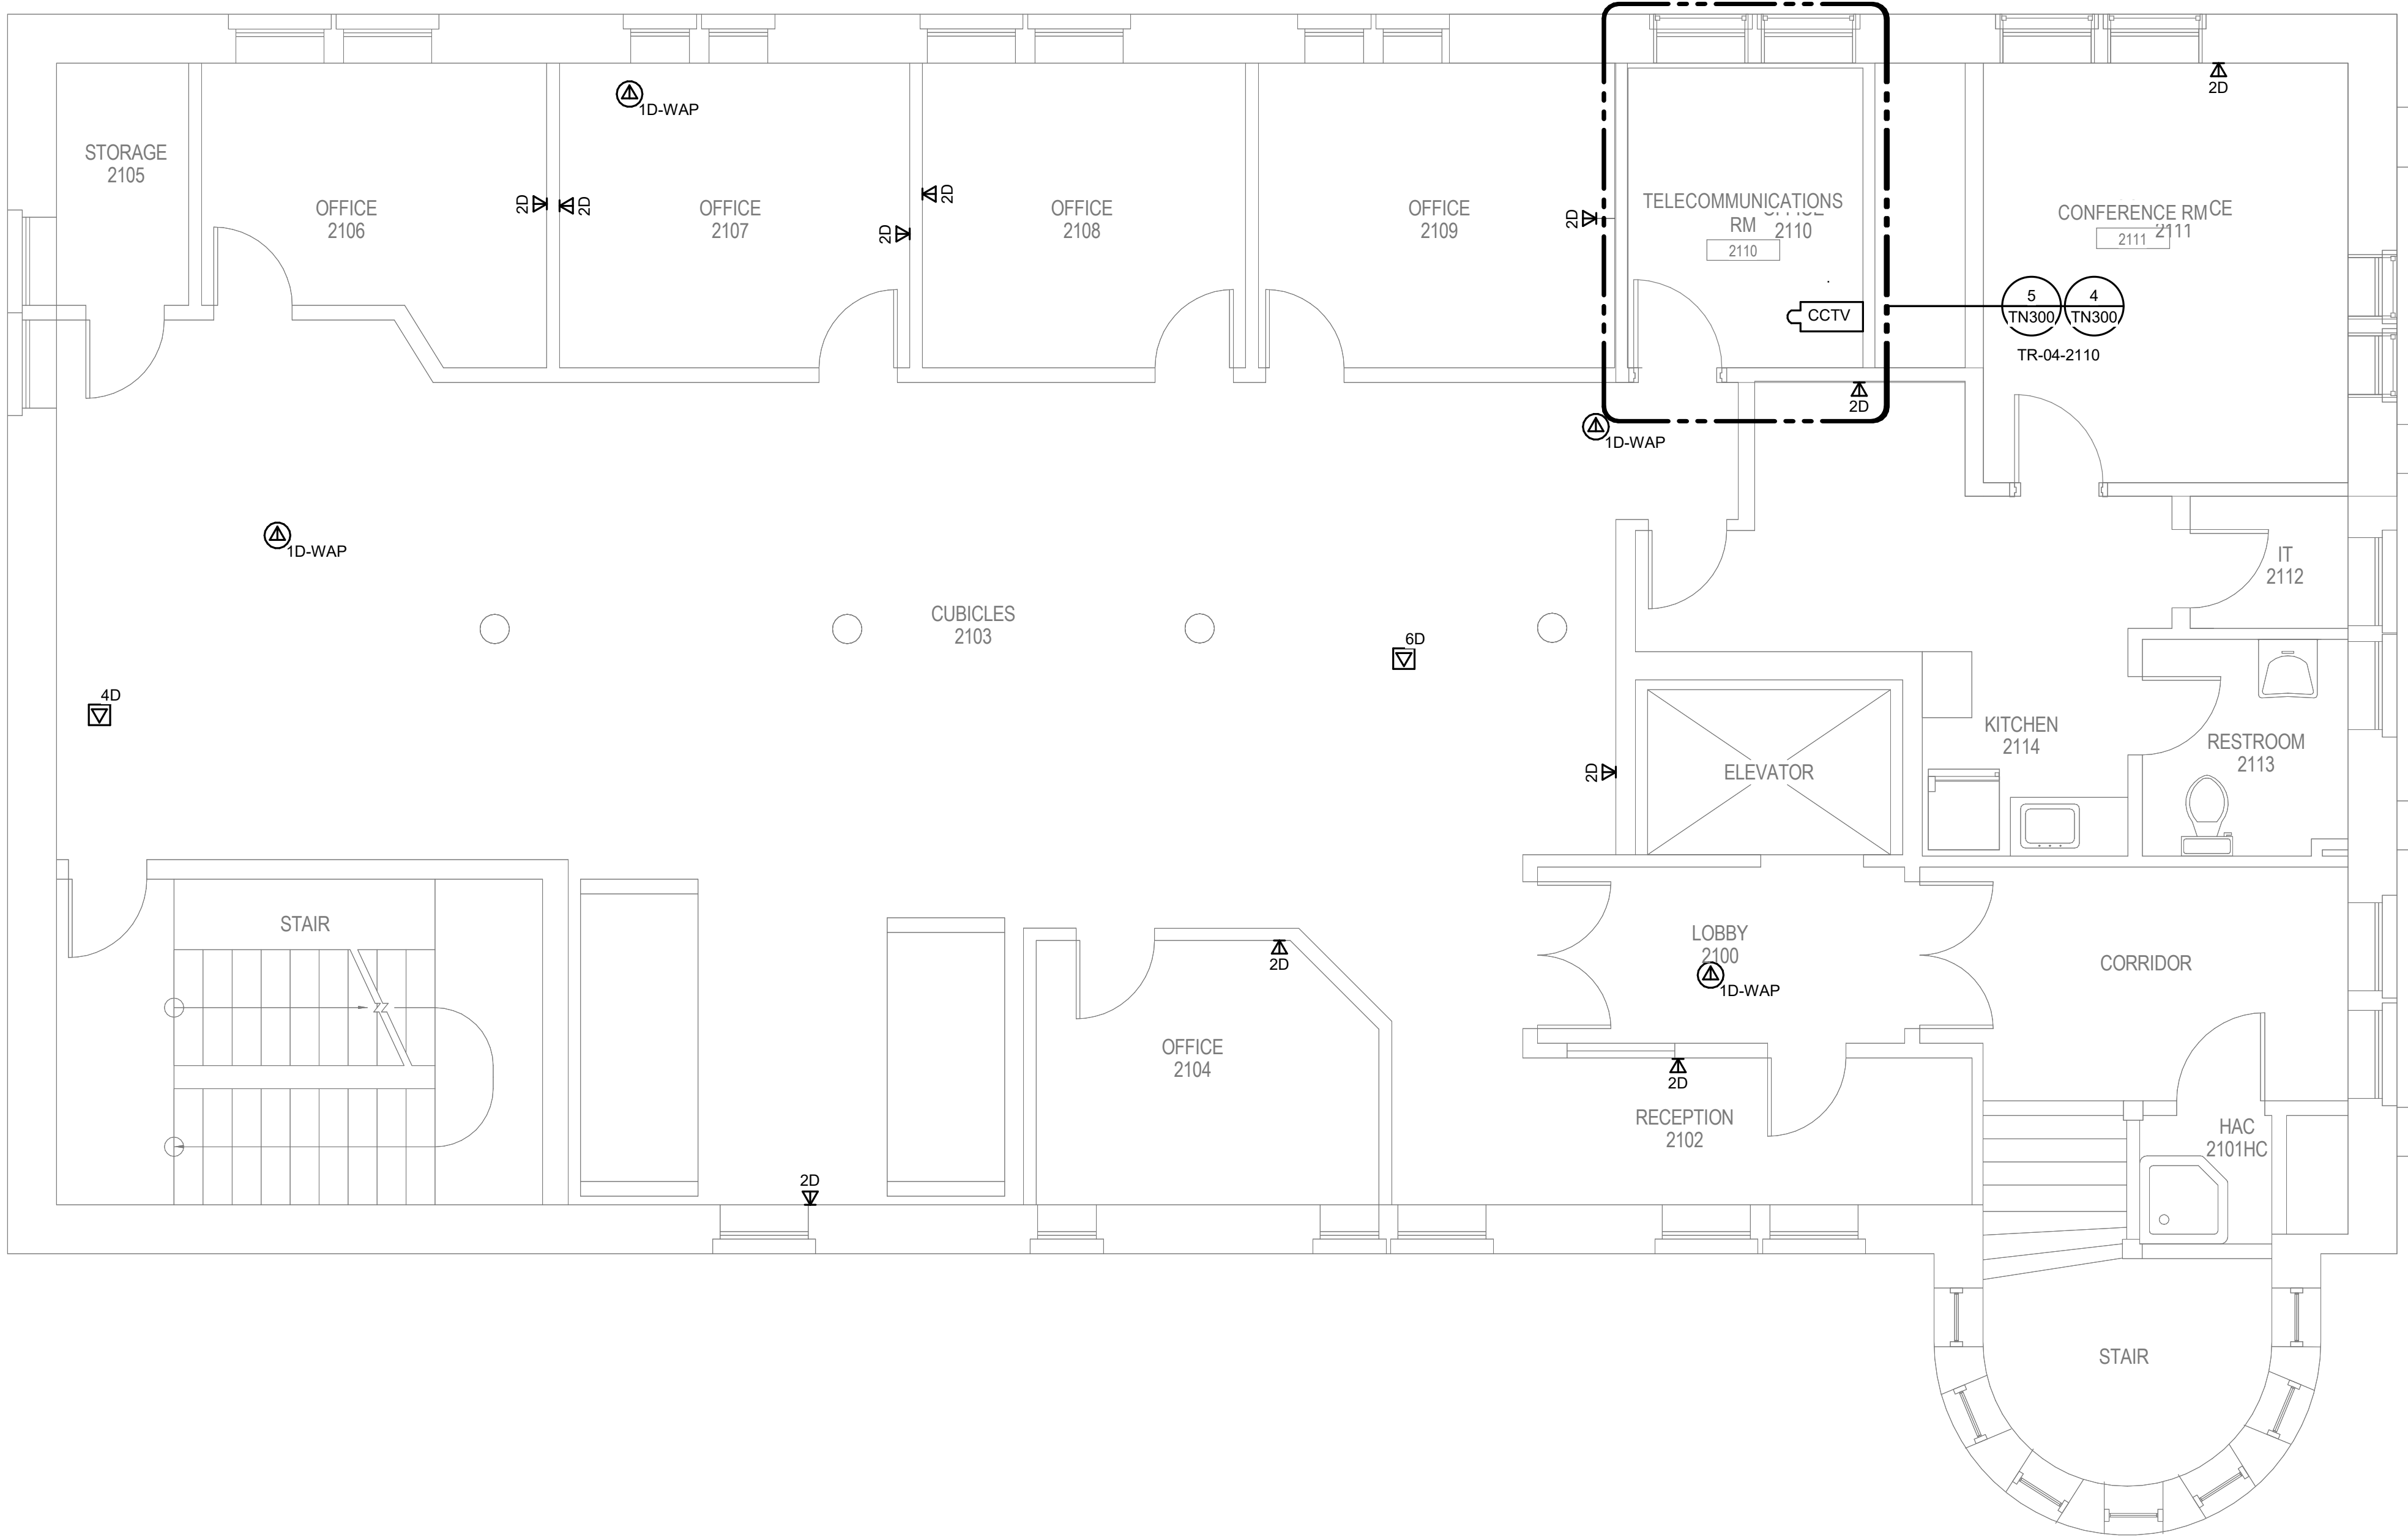

1 BUILDING 04 SECOND FLOOR PLAN - TECHNOLOGY
1/4" = 1'-0"

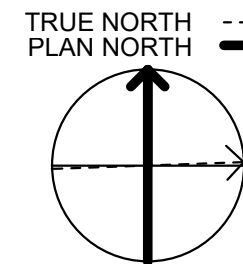

35% SCHEMATIC DESIGN SUBMISSION	5.17.21
65% DESIGN DEVELOPMENT SUBMISSION	6.15.21
65% DESIGN DEVELOPMENT RESUBMISSION	8.25.21
Revisions:	Date:

CONSULTANT

IMEG

THE FUTURE IS IT Solutions www.imegcorp.com
15 SUNNEN DRIVE
SUITE 104
ST. LOUIS, MO 63143
P: 314.645.1132 F: 314.645.1173
PROJECT #18004375.03

ARCHITECT/ENGINEER OF RECORD

Romanyk Consulting
Focusing on what matters

Romanyk Consulting Corp. www.romanykconsulting.com
3308 Preston Road, Suite 350-164, Plano, Texas 75093

STAMP

Bicsi
DAVID LARSON
BICS1 ID # 106098
EXPIRES 12-31-25
REGISTERED COMMUNICATIONS DISTRIBUTION DESIGNER

Office of
Construction
and Facilities
Management

VA U.S. Department
of Veterans Affairs

Drawing Title
BUILDING 04 SECOND FLOOR PLAN -
TECHNOLOGY

Approved:

Phase
FINAL BID DOCUMENTS

Sprinklered
FULLY SPRINKLERED

Project Title
EHRM INFRASTRUCTURE
UPGRADES - MILWAUKEE, WI

Location
5000 W. NATIONAL AVENUE MILWAUKEE, WI

Issue Date
SEPTEMBER 05, 2025

Checked
PHINIE

Drawn
MAIBEJ

Project Number
695-21-700

Building Number
04

Drawing Number
04-TN102

F

E

D

C











B

A


9/2/2025 3:54:42 PM

Autodesk Docs\DCFM East - Milwaukee EHRM (R24)T24_1804375.03_VA Milwaukee_C.dwt

- SHEET NOTES:**
1. REMOVE ALL NETWORK CABLING TO POINTS OF TERMINATION IN ASSOCIATED DATA CLOSET. REFER TO FLOOR PLANS AND SHEET T1001 FOR TR ROOM LOCATIONS.
 2. REFER TO ARCHITECTURAL PHASING PLANS FOR WHEN EXISTING CABLING IS ALLOWED TO BE DEMOLISHED.
 3. FOR ALL EXISTING WIRELESS ACCESS POINTS AND SURVEILLANCE CAMERAS, DEVICES SHALL REMAIN. SCOPE OF WORK INCLUDES CABLE REPLACEMENT ONLY. COORDINATE WITH COR FOR ANY DOWNTIME OF DEVICES.
 4. EXISTING LOCATIONS OF WORK AREA, OUTLETS SHOWN ON THIS SHEET MAY NOT NECESSARILY BE IN THE EXACT LOCATION AS IDENTIFIED.
- KEYNOTES: (C #)**
1. EXISTING DATA CLOSET, PROTECT IN PLACE.

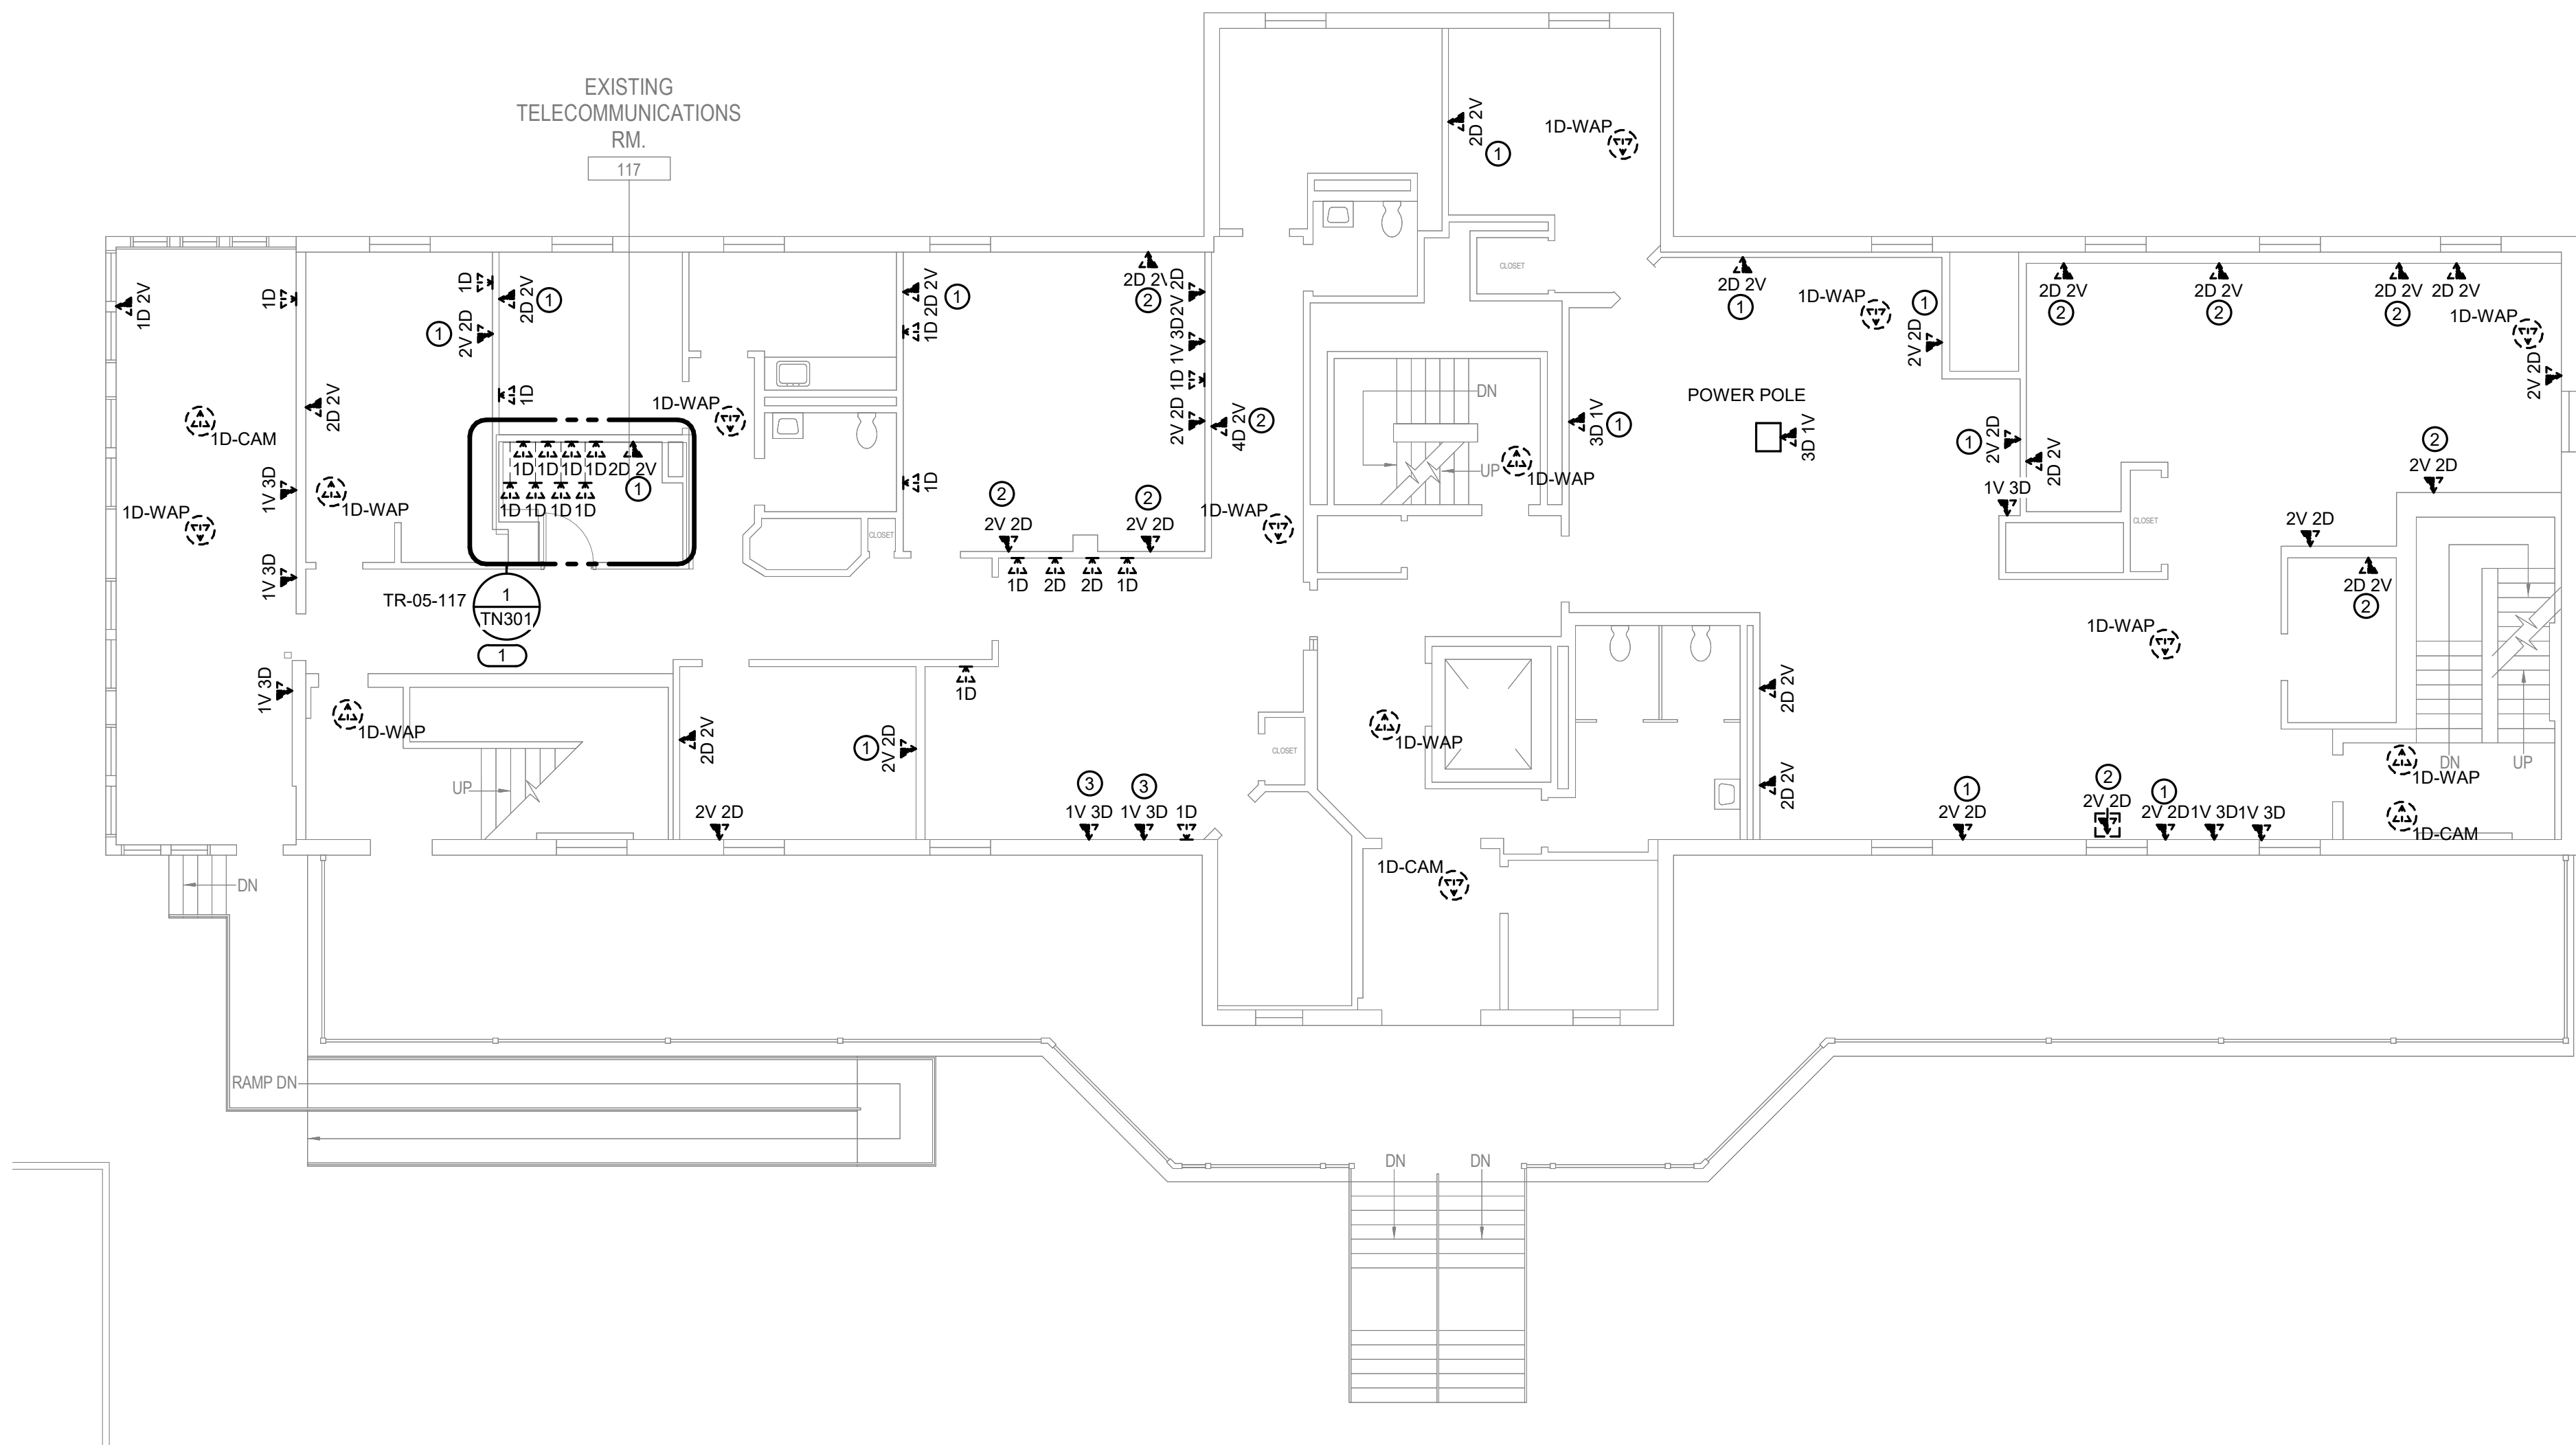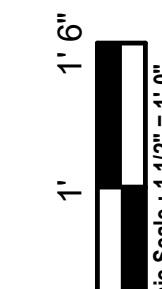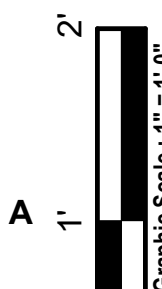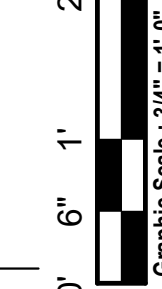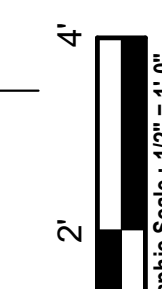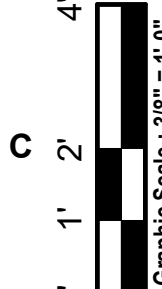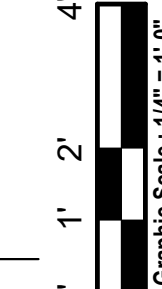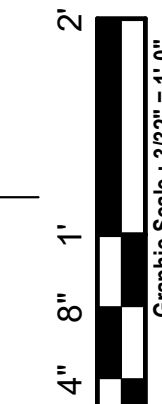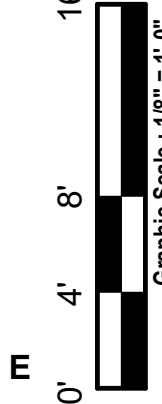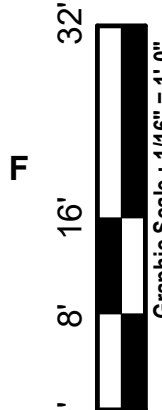

1 BUILDING 05 FIRST FLOOR DEMOLITION - TECHNOLOGY
1/8" = 1'-0"

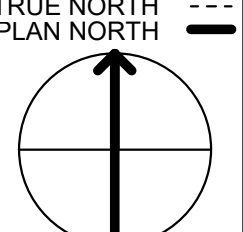

35% SCHEMATIC DESIGN SUBMISSION	5.17.21
65% DESIGN DEVELOPMENT SUBMISSION	6.15.21
65% DESIGN DEVELOPMENT RESUBMISSION	8.25.21
Revisions:	Date:

CONSULTANT

IMEG

THE FUTURE IS IT SERVICES www.imegcorp.com
15 SUNNEN DRIVE
SUITE 104
ST. LOUIS, MO 63143
P: 314.645.1132 F: 314.645.1173
PROJECT #18004375.03

ARCHITECT/ENGINEER OF RECORD

Romanyk Consulting
Focusing on what matters

Romanyk Consulting Corp. www.romanykconsulting.com
3308 Preston Road, Suite 350-164, Plano, Texas 75093

STAMP

Bicsi
DAVID LARSON
BICS1 ID # 106098
EXPIRES 12-31-25
REGISTERED COMMUNICATIONS DISTRIBUTION DESIGNER

Office of
Construction
and Facilities
Management

VA U.S. Department
of Veterans Affairs

Drawing Title
BUILDING 05 FIRST FLOOR DEMO -
TECHNOLOGY

Approved:

Phase
FINAL BID DOCUMENTS

Sprinklered
FULLY SPRINKLERED

Project Title
EHRM INFRASTRUCTURE
UPGRADES - MILWAUKEE, WI

Location
5000 W. NATIONAL AVENUE, MILWAUKEE, WI

Issue Date
SEPTEMBER 05, 2025

Checked
PHINIE

Drawn
MAIBEJ

Project Number
695-21-700

Building Number
05

Drawing Number
05-TD101

F

E

D

C










B

A


9/2/2025 3:54:43 PM

Autodesk Docs\DOCFM East - Milwaukee EHRM (R24)T24_1804375\03_VA Milwaukee_C.dwt

- SHEET NOTES:**
1. REMOVE ALL NETWORK CABLING TO POINTS OF TERMINATION IN ASSOCIATED DATA CLOSET. REFER TO FLOOR PLANS AND SHEET T1001 FOR TR ROOM LOCATIONS.
 2. REFER TO ARCHITECTURAL PHASING PLANS FOR WHEN EXISTING CABLING IS ALLOWED TO BE DEMOLISHED.
 3. FOR ALL EXISTING WIRELESS ACCESS POINTS AND SURVEILLANCE CAMERAS, DEVICES SHALL REMAIN. SCOPE OF WORK INCLUDES CABLE REPLACEMENT ONLY. COORDINATE WITH COR FOR ANY DOWNTIME OF DEVICES. EXISTING LOCATIONS OF WORK AREA OUTLETS SHOWN ON THIS SHEET MAY NOT NECESSARILY BE IN THE EXACT LOCATION AS IDENTIFIED.

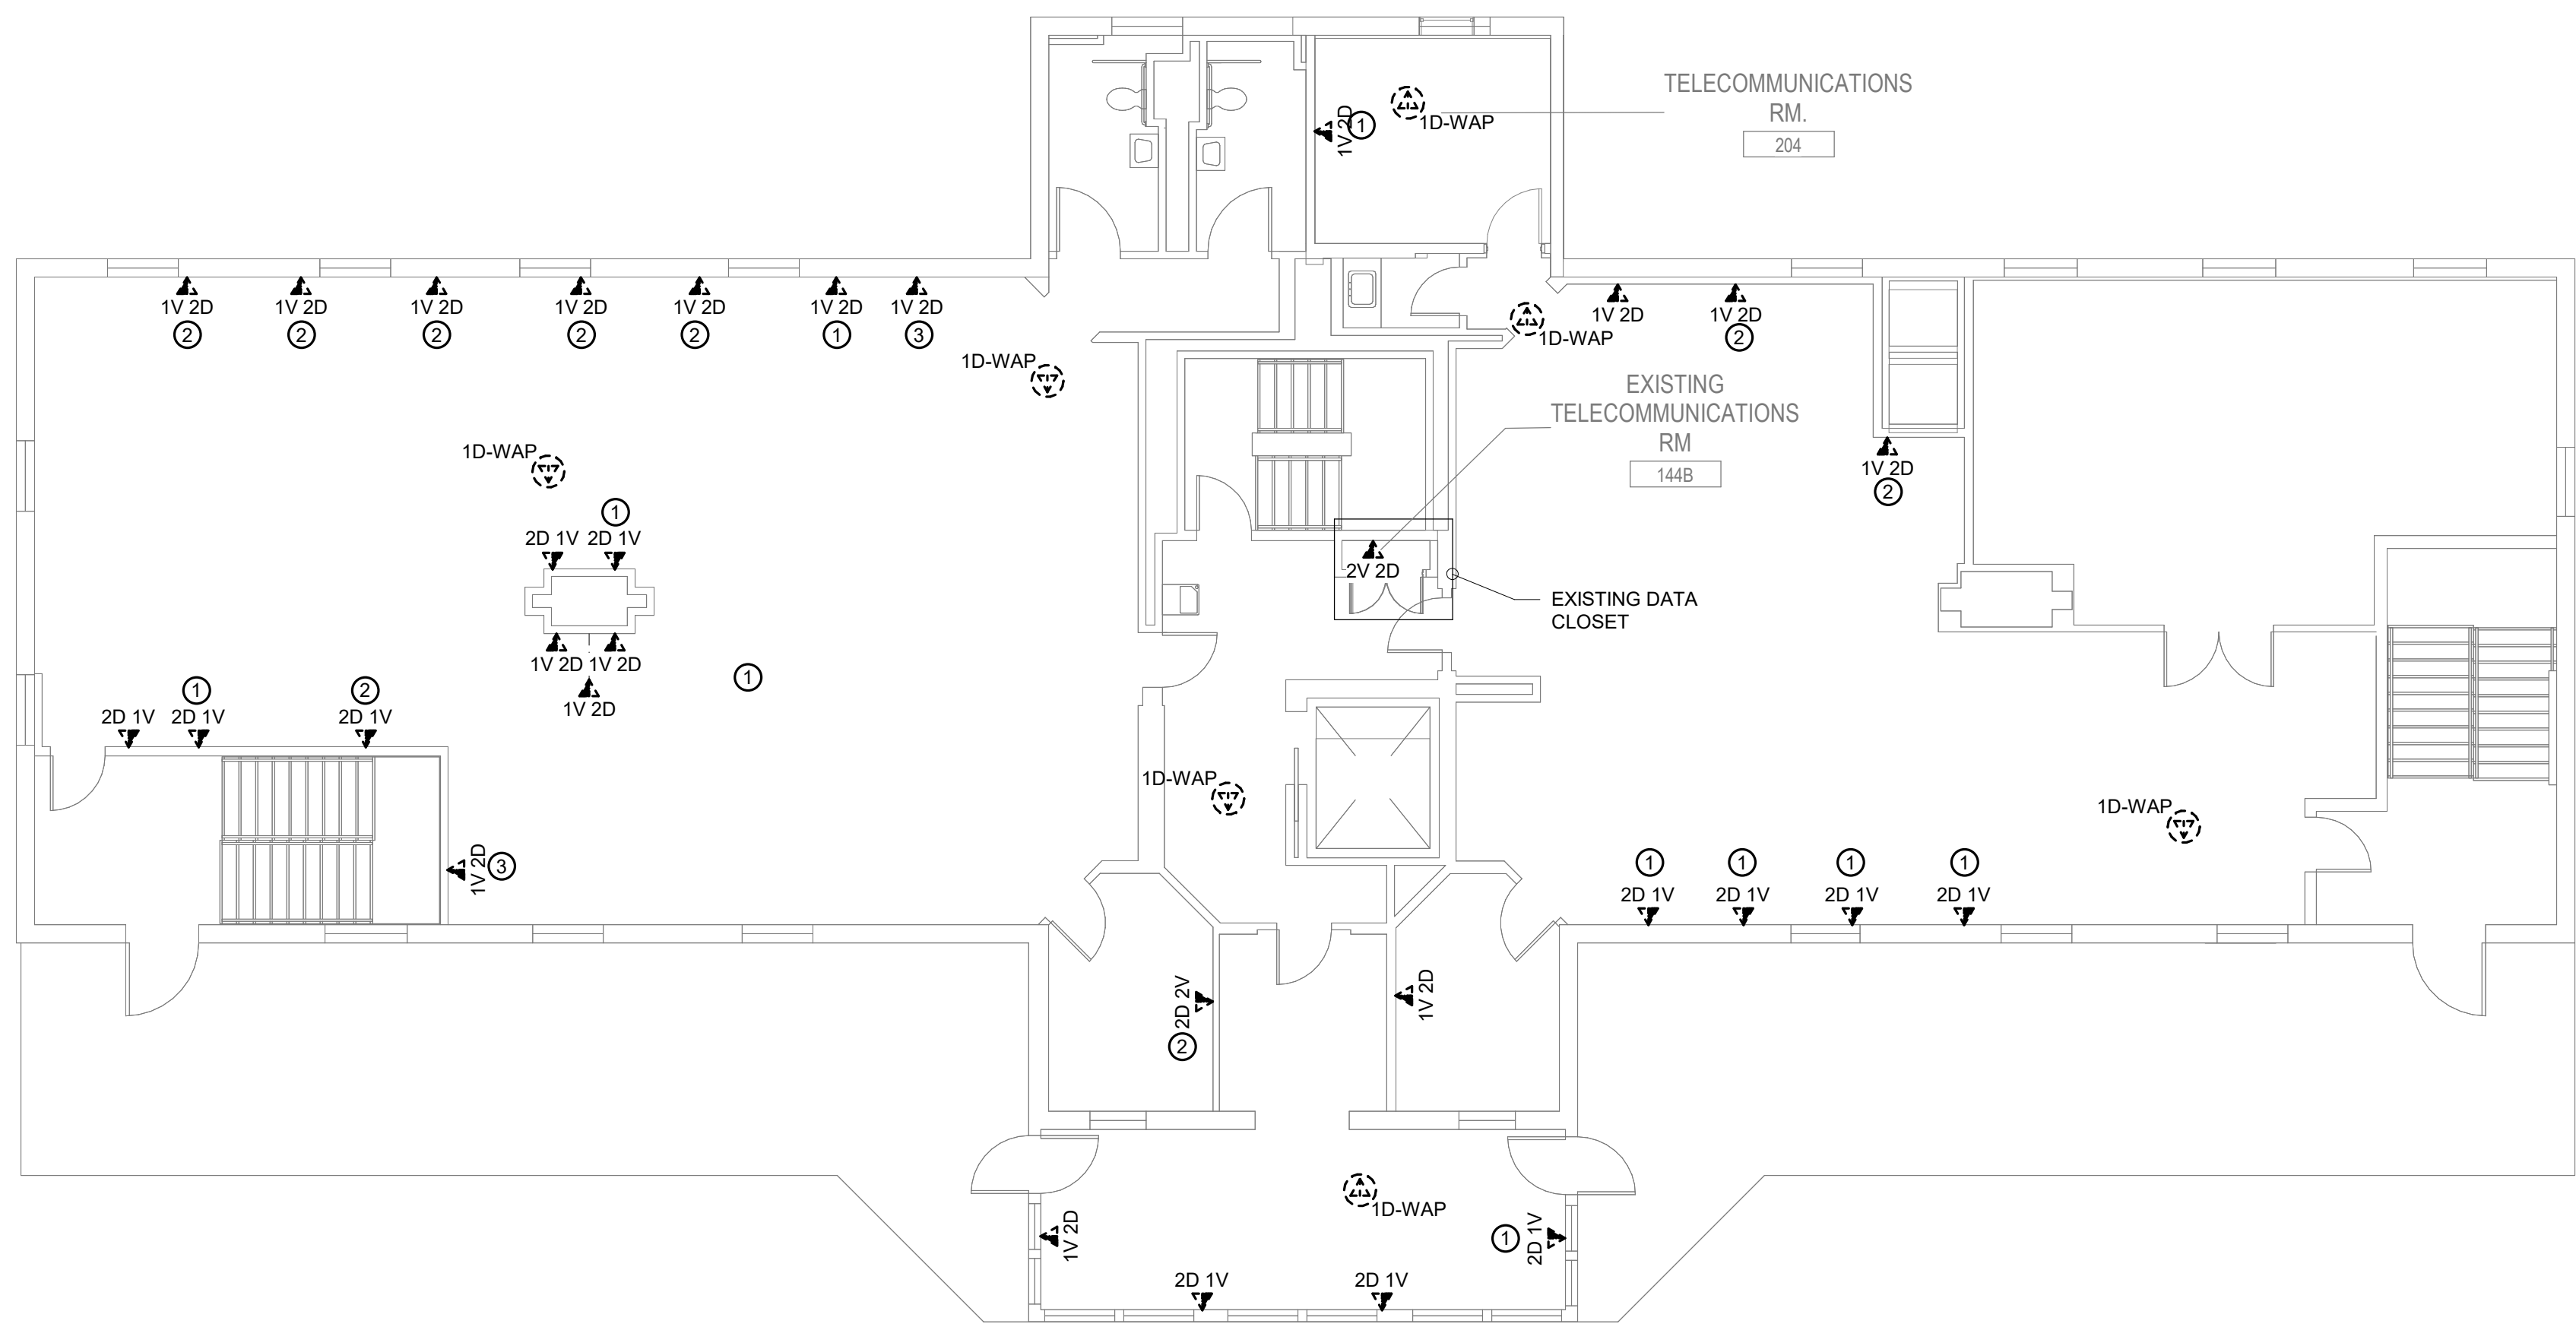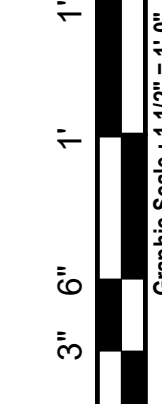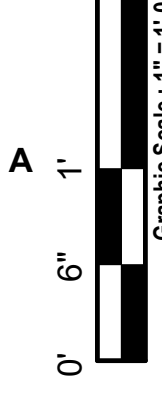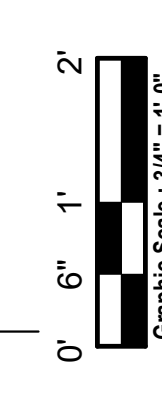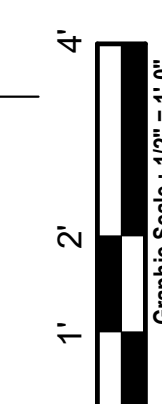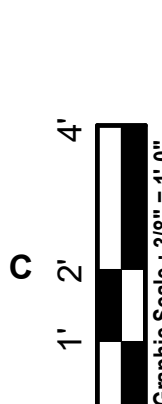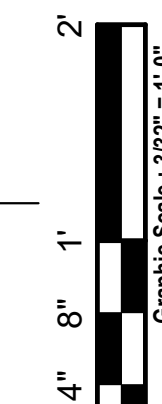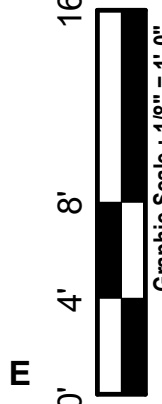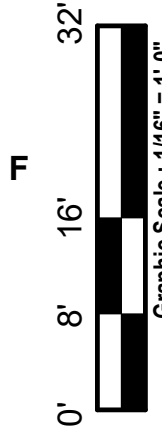

1 BUILDING 05 SECOND FLOOR DEMOLITION PLAN - TECHNOLOGY
1/8" = 1'-0"

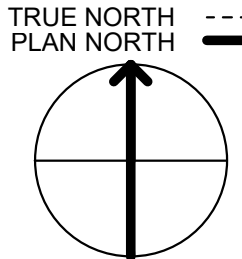

35% SCHEMATIC DESIGN SUBMISSION	5.17.21
65% DESIGN DEVELOPMENT SUBMISSION	6.15.21
65% DESIGN DEVELOPMENT RESUBMISSION	8.25.21
Revisions:	Date:

CONSULTANT

IMEG

15 SUNNEN DRIVE
SUITE 104
ST. LOUIS, MO 63143
P: 314.645.1132 F: 314.645.1173
PROJECT #18004375.03

ARCHITECT/ENGINEER OF RECORD

Romanyk Consulting
Focusing on what matters

Romanyk Consulting Corp. www.romanykconsulting.com
3308 Preston Road, Suite 350-164, Plano, Texas 75093

STAMP

Bicsi
DAVID LARSON
BICS1 ID # 106098
EXPIRES 12-31-25
REGISTERED COMMUNICATIONS DISTRIBUTION DESIGNER
RCDD

Office of
Construction
and Facilities
Management

VA U.S. Department
of Veterans Affairs

Drawing Title
**BUILDING 05 SECOND FLOOR DEMO PLAN -
TECHNOLOGY**

Approved:

Phase
FINAL BID DOCUMENTS

Sprinklered
FULLY SPRINKLERED

Project Title
**EHRM INFRASTRUCTURE
UPGRADES - MILWAUKEE, WI**

Location
5000 W. NATIONAL AVENUE MILWAUKEE, WI

Issue Date
SEPTEMBER 05, 2025

Checked
PHINIE

Drawn
MAIBEJ

Project Number
695-21-700

Building Number
05

Drawing Number
05-TD102

F

E

D

C


B

A


9/3/2025 3:54:44 PM

Autodesk Docs\DCFM East - Milwaukee EHRM (R24)T24_1804375\03_VA Milwaukee_C.dwt

- SHEET NOTES:**
1. REMOVE ALL NETWORK CABLING TO POINTS OF TERMINATION IN ASSOCIATED DATA CLOSET. REFER TO FLOOR PLANS AND SHEET T1001 FOR TR ROOM LOCATIONS.
 2. REFER TO ARCHITECTURAL PHASING PLANS FOR WHEN EXISTING CABLING IS ALLOWED TO BE DEMOLISHED.
 3. FOR ALL EXISTING WIRELESS ACCESS POINTS AND SURVEILLANCE CAMERAS, DEVICES SHALL REMAIN. SCOPE OF WORK INCLUDES CABLE REPLACEMENT ONLY. COORDINATE WITH COR FOR ANY DOWNTIME OF DEVICES. EXISTING LOCATIONS OF WORK AREA, OUTLETS SHOWN ON THIS SHEET MAY NOT NECESSARILY BE IN THE EXACT LOCATION AS IDENTIFIED.

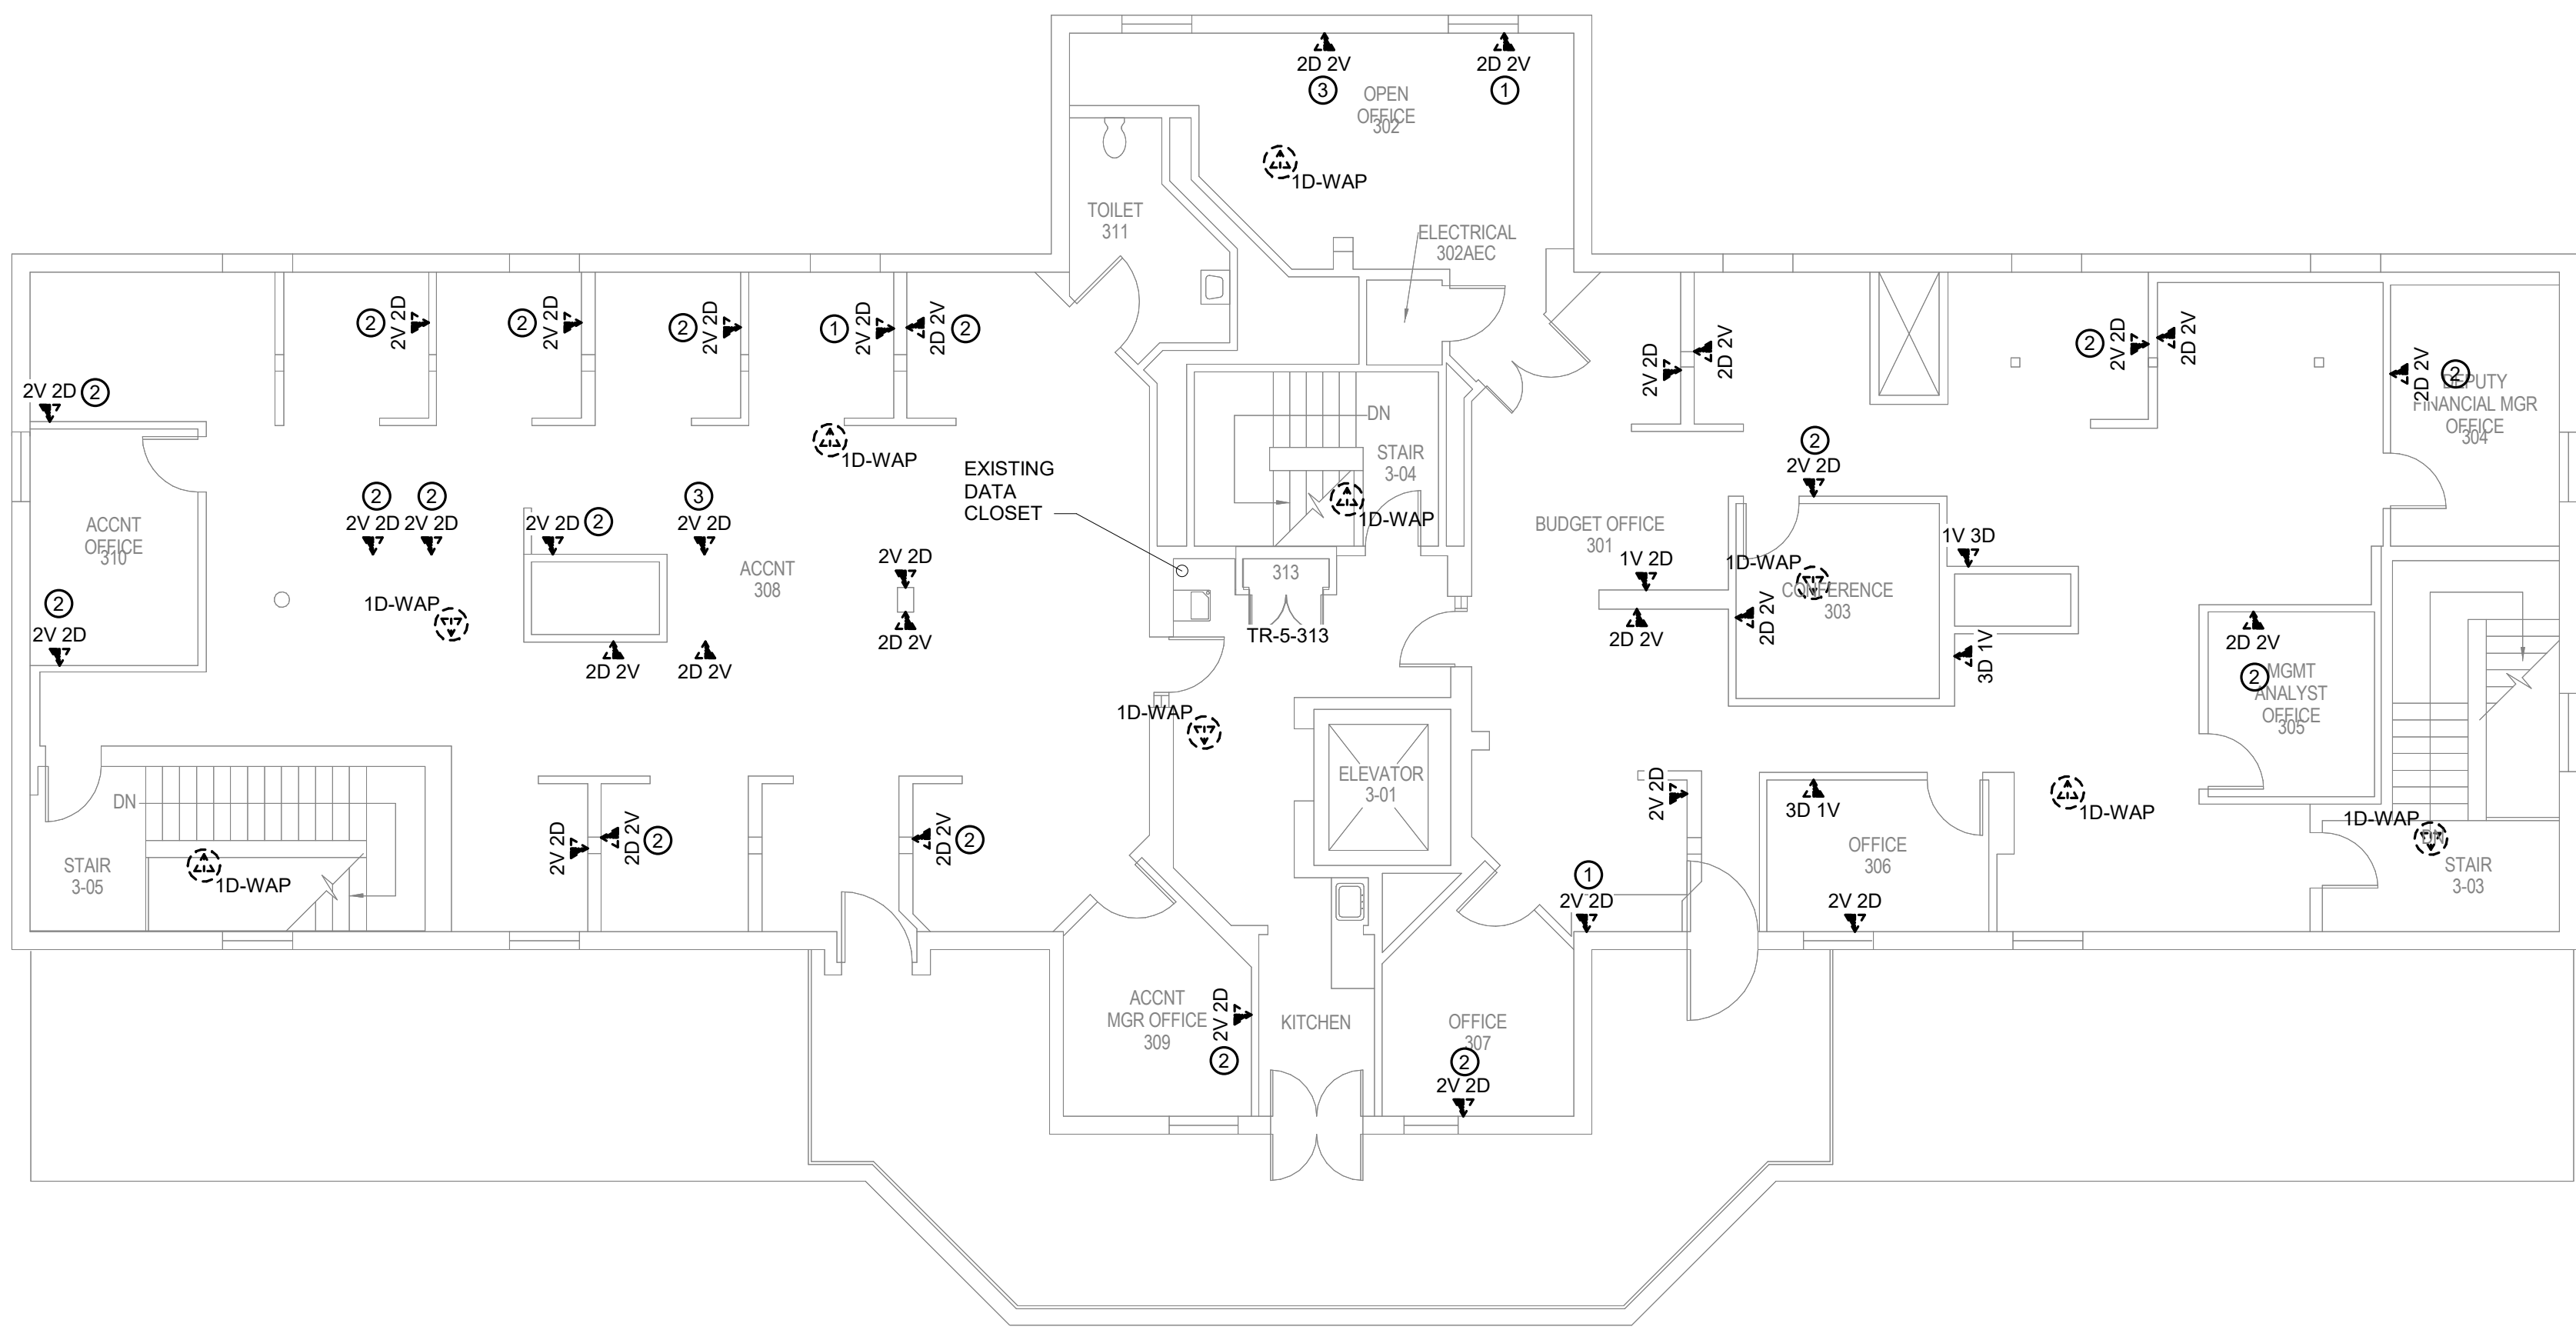

1 BUILDING 05 THIRD FLOOR DEMOLITION PLAN - TECHNOLOGY
1/8" = 1'-0"

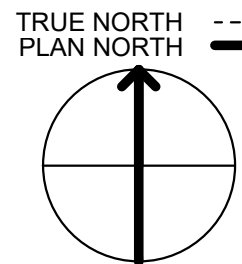

35% SCHEMATIC DESIGN SUBMISSION	5.17.21
65% DESIGN DEVELOPMENT SUBMISSION	6.15.21
65% DESIGN DEVELOPMENT RESUBMISSION	8.25.21
Revisions:	Date:

CONSULTANT

IMEG

15 SUNNEN DRIVE
SUITE 104
ST. LOUIS, MO 63143
P: 314.645.1132 F: 314.645.1173
PROJECT #18004375.03

ARCHITECT/ENGINEER OF RECORD

Romanyk Consulting
Focusing on what matters

Romanyk Consulting Corp. www.romanykconsulting.com
3308 Preston Road, Suite 350-164, Plano, Texas 75093

STAMP

Bicsi
DAVID LARSON
BICS1 ID # 106098
Expires 12-31-25

Office of
Construction
and Facilities
Management

VA U.S. Department
of Veterans Affairs

Drawing Title
BUILDING 05 THIRD FLOOR DEMO PLAN -
TECHNOLOGY

Approved:

Phase
FINAL BID DOCUMENTS

Sprinklered
FULLY SPRINKLERED

Project Title
EHRM INFRASTRUCTURE
UPGRADES - MILWAUKEE, WI

Location
5000 W. NATIONAL AVENUE MILWAUKEE, WI

Issue Date
SEPTEMBER 05, 2025

Checked
PHINIE

Drawn
MAIBEJ

Project Number
695-21-700

Building Number
05

Drawing Number
05-TD103

F

E

D

C











B

A

9/2/2025 3:54:46 PM


Autodesk Docs\OCCEM East - Milwaukee EHRM (R24)T24_1804375.03_VA MilVHRM_C.dwg

- SHEET NOTES:**
1. ALL NETWORK CABLES ON THIS SHEET SHALL TERMINATE IN TR-05-117.
 2. REFER TO CIVIL DRAWINGS AND T1003 FOR ADDITIONAL PATHWAY INFORMATION.
 3. CONTRACTOR TO PROVIDE NEW J-HOOK ROUTES FOR ALL NEW CABLING. J-HOOK SIZE AND QUANTITY TO BE PER MANUFACTURER RECOMMENDATIONS.
 4. REFER TO TN500-TN509 FOR RISER DIAGRAMS.
 5. REFER TO SHEET TN402 FOR PENETRATION DETAILS.
 6. THESE DRAWINGS MAKE THE BEST ATTEMPT TO IDENTIFY EXISTING DATA DROPS/WORK AREA OUTLETS. AS LONG AS THE TOTAL NEWLY INSTALLED DATA DROP COUNT DOES NOT VARY +/- 10% IDENTIFIED ON THESE DRAWINGS, THE CONTRACTOR'S SCOPE SHALL BE UNCHANGED.
 7. NEW WORK AREA OUTLETS SHALL BE LOCATED IN EXISTING BOXES. WORK AREA OUTLETS SHOWN ON THIS SHEET MAY NOT BE IN THE EXACT LOCATION AS IDENTIFIED.
 8. CONTRACTOR TO INCLUDE AN ALLOWANCE FOR 10% ADDITIONAL 2-PORTS CAT6A INFORMATION OUTLETS IN THEIR PROPOSAL FOR THIS SHEET. FUTURE INFORMATION OUTLET LOCATIONS WILL BE DETERMINED BY THE VA AT A LATER DATE.
- KEYNOTES:** (#)
1. ACCESS CONTROL PANEL LOCATION. GO TO COORDINATE EXACT LOCATION AND HEIGHT WITH COR TO RE-CONNECT TO SWITCHRACK TE IN SAME ROOM WITH CAT6A CABLE AS NECESSARY.
 2. EXISTING BACKBONE ENTRY POINT. PROTECT IN PLACE. DEMOLISH EXISTING FIBER OPTIC CABLE TO POINTS OF TERMINATION AFTER REDUNDANT PATH IS INSTALLED AND OPERATIONAL. REFER TO ARCHITECTURAL PHASING PLAN FOR ADDITIONAL INFORMATION. CONDUIT ENTERS ON LOWER LEVEL.

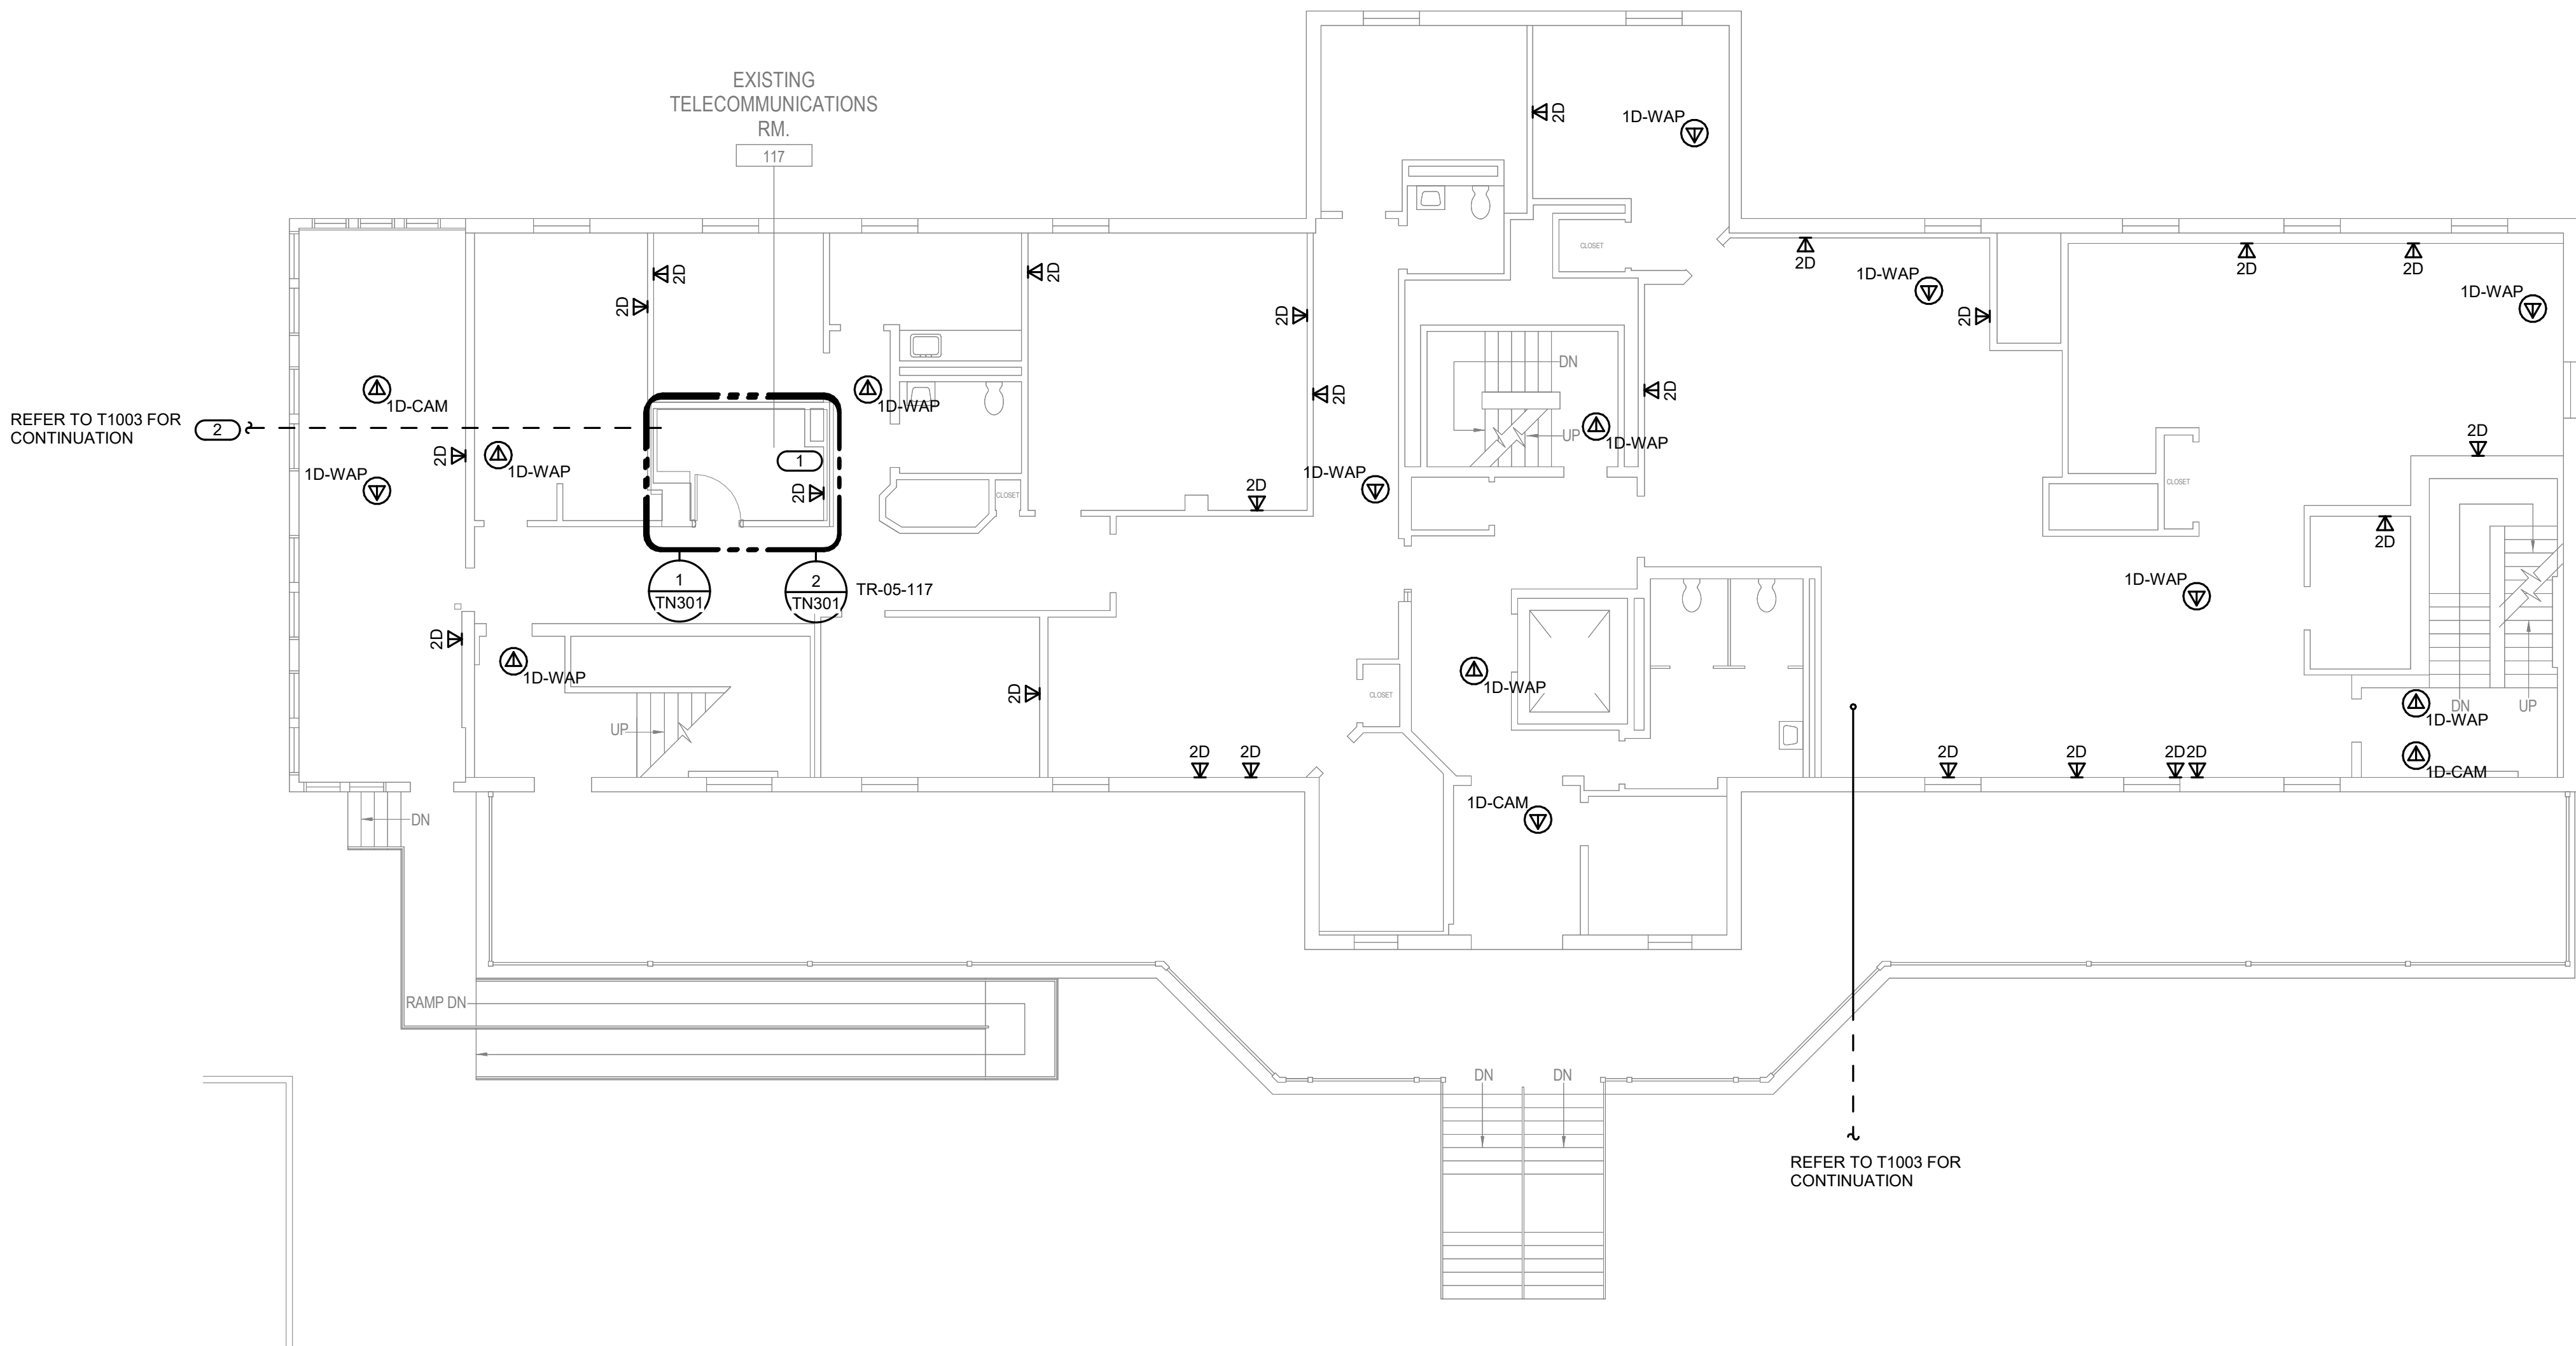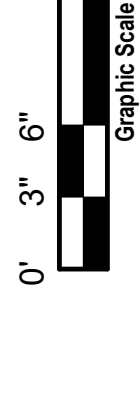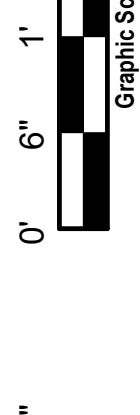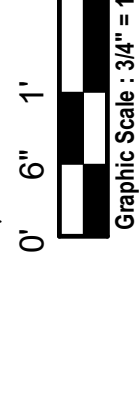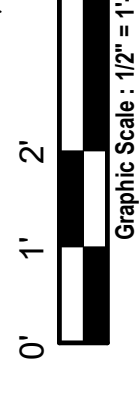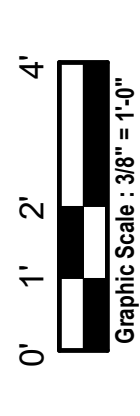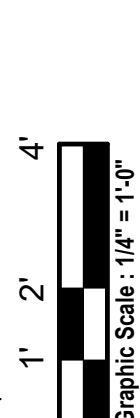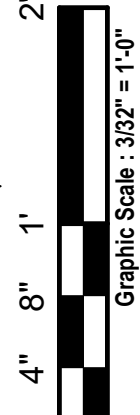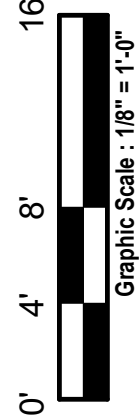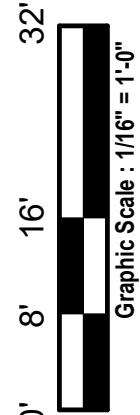


1 BUILDING 05 FIRST FLOOR PLAN - TECHNOLOGY
1/8" = 1'-0"

TELECOM ROOM LOCATION

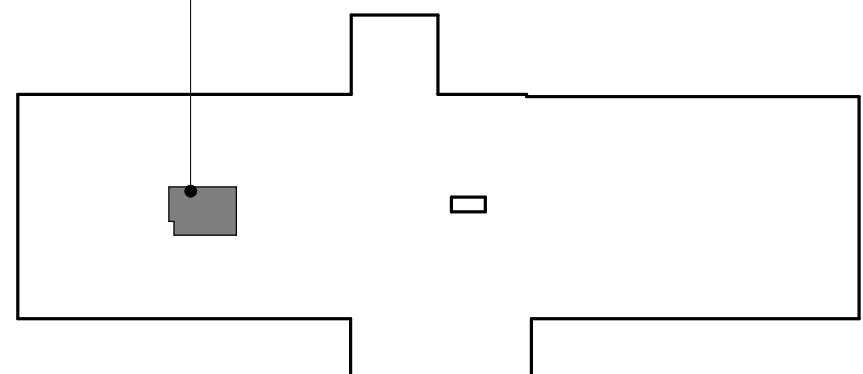

KEY PLAN - BLDG 5 1ST
NTS

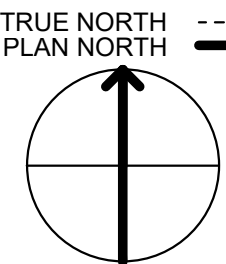

35% SCHEMATIC DESIGN SUBMISSION	5.17.21
65% DESIGN DEVELOPMENT SUBMISSION	6.15.21
65% DESIGN DEVELOPMENT RESUBMISSION	8.25.21
Revisions:	Date:

CONSULTANT

IMEG

THE FUTURE IS IT'S HERE
15 SUNNEN DRIVE
SUITE 104
ST. LOUIS, MO 63143
P: 314.645.1132 F: 314.645.1173
PROJECT #18004375.03

ARCHITECT/ENGINEER OF RECORD

Romanyk Consulting
Focusing on what matters

Romanyk Consulting Corp. www.romanykconsulting.com
3308 Preston Road, Suite 350-164, Plano, Texas 75093

STAMP

Bicsi
DAVID LARSON
BICS1 ID # 106098
EXPIRES 12-31-25
REGISTERED COMMUNICATIONS DISTRIBUTION DESIGNER
RCDD

Office of
Construction
and Facilities
Management

VA U.S. Department
of Veterans Affairs

Drawing Title
BUILDING 05 FIRST FLOOR PLAN - TECHNOLOGY

Approved:

Phase
FINAL BID DOCUMENTS

Sprinklered
FULLY SPRINKLERED

Project Title
EHRM INFRASTRUCTURE
UPGRADES - MILWAUKEE, WI

Location
5000 W. NATIONAL AVENUE MILWAUKEE, WI

Issue Date
SEPTEMBER 05, 2025

Checked
PHINIE

Drawn
MAIBEJ

Project Number
695-21-700

Building Number
05

Drawing Number
05-TN101

F

E

D

C










B

A


9/2/2025 3:54:46 PM

Autodesk Docs\DCFM East - Milwaukee EHRM (R24)T24_1804375\03_VA Milwaukee_C.dwg

- SHEET NOTES:**
1. REFER TO 1/TN400 FOR TECHNOLOGY ROUGH IN DETAIL.
 2. ALL NETWORK CABLES ON THIS SHEET SHALL TERMINATE IN TR-5-204.
 3. CONTRACTOR TO PROVIDE NEW J-HOOK ROUTES FOR ALL NEW CABLING. J-HOOK SIZE AND QUANTITY TO BE PER MANUFACTURER RECOMMENDATIONS.
 4. REFER TO TN500-TN600 FOR RISER DIAGRAMS.
 5. REFER TO SHEET TN402 FOR PENETRATION DETAILS.
 6. THESE DRAWINGS MAKE THE BEST ATTEMPT TO IDENTIFY EXISTING DATA DROPS/WORK AREA OUTLETS. AS LONG AS THE TOTAL NEWLY INSTALLED DATA DROP COUNT DOES NOT VARY +/- 10% IDENTIFIED ON THESE DRAWINGS, THE CONTRACTOR'S SCOPE SHALL BE UNCHANGED.
 7. NEW WORK AREA OUTLETS SHALL BE LOCATED IN EXISTING BOXES. WORK AREA OUTLETS SHOWN ON THIS SHEET MAY NOT BE IN THE EXACT LOCATION AS IDENTIFIED.
 8. CONTRACTOR TO INCLUDE AN ALLOWANCE FOR 10% ADDITIONAL 2-PORTS CAT6A INFORMATION OUTLETS IN THEIR PROPOSAL FOR THIS SHEET. FUTURE INFORMATION OUTLET LOCATIONS WILL BE DETERMINED BY THE VA AT A LATER DATE.

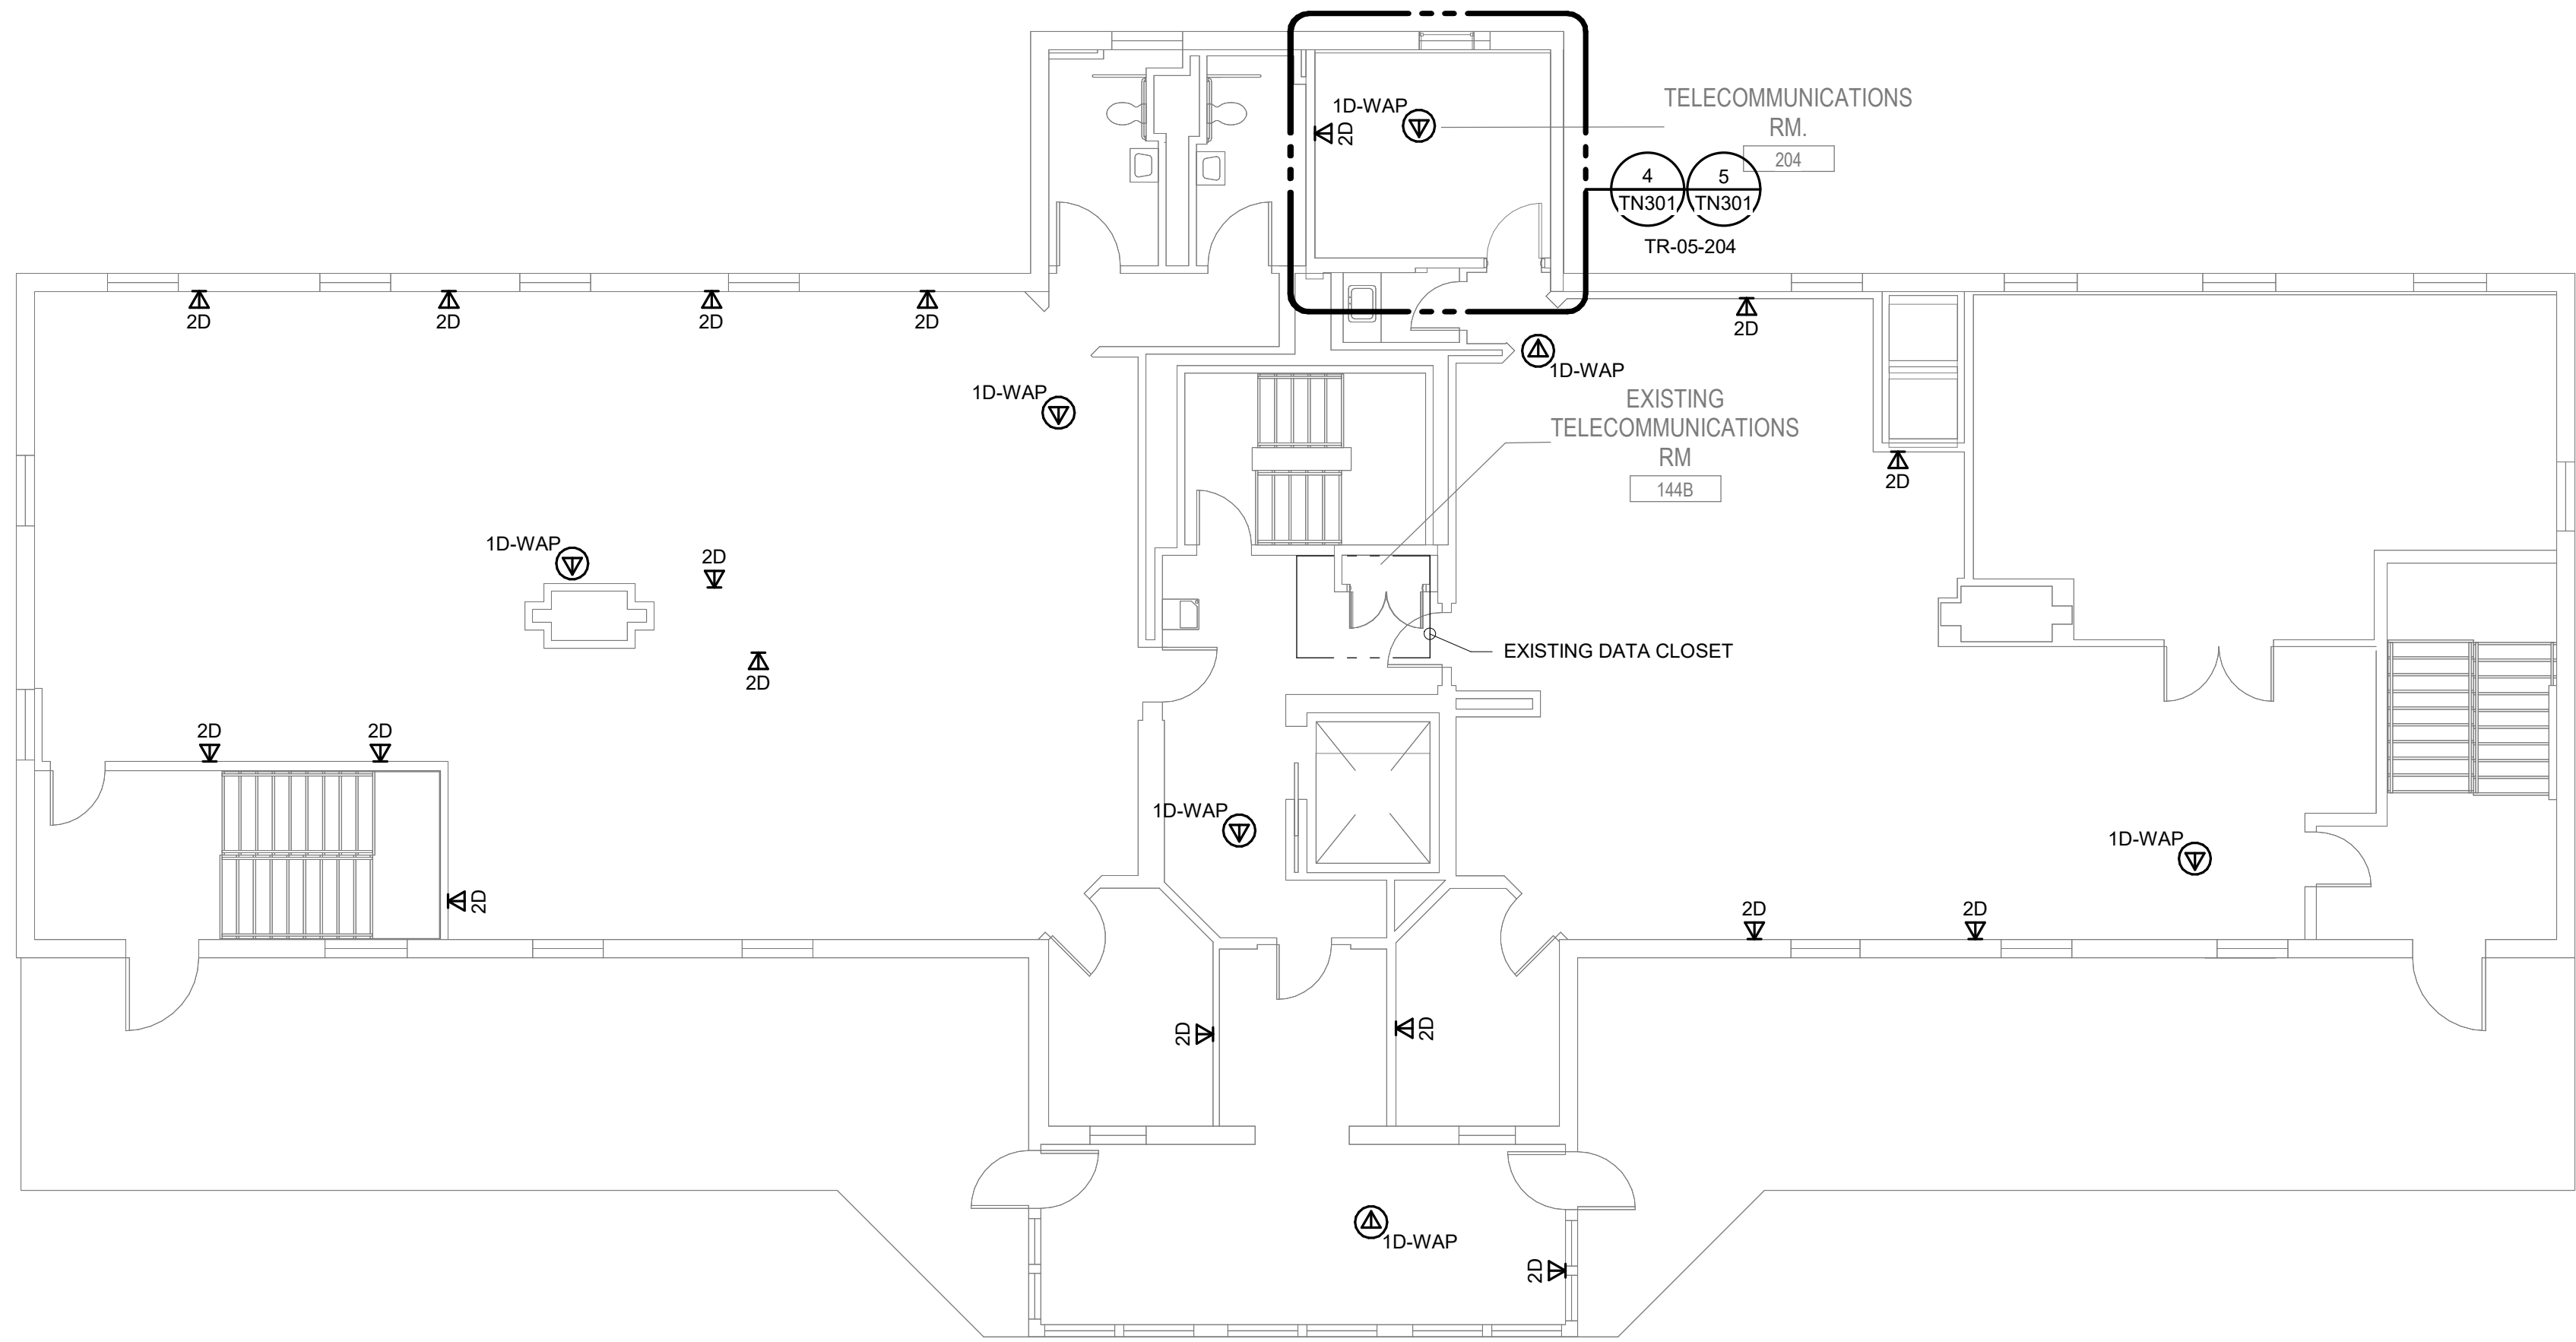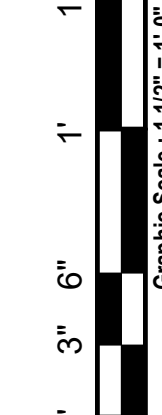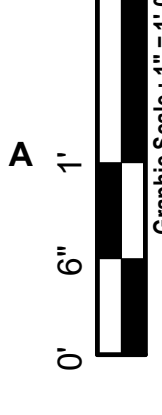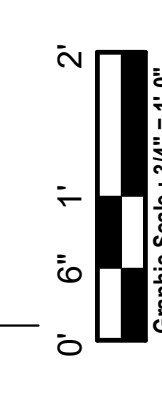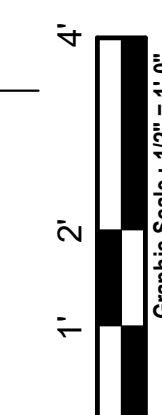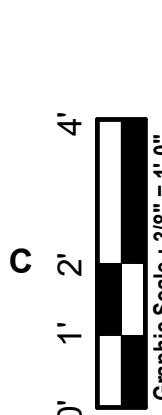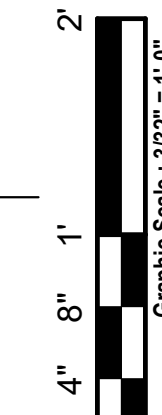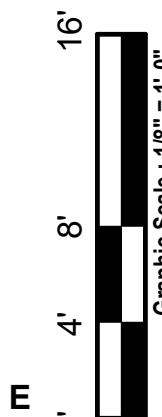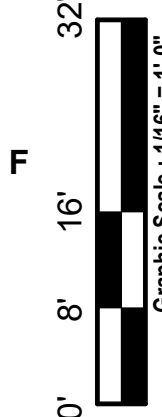

1 BUILDING 05 SECOND FLOOR PLAN - TECHNOLOGY
1/8" = 1'-0"

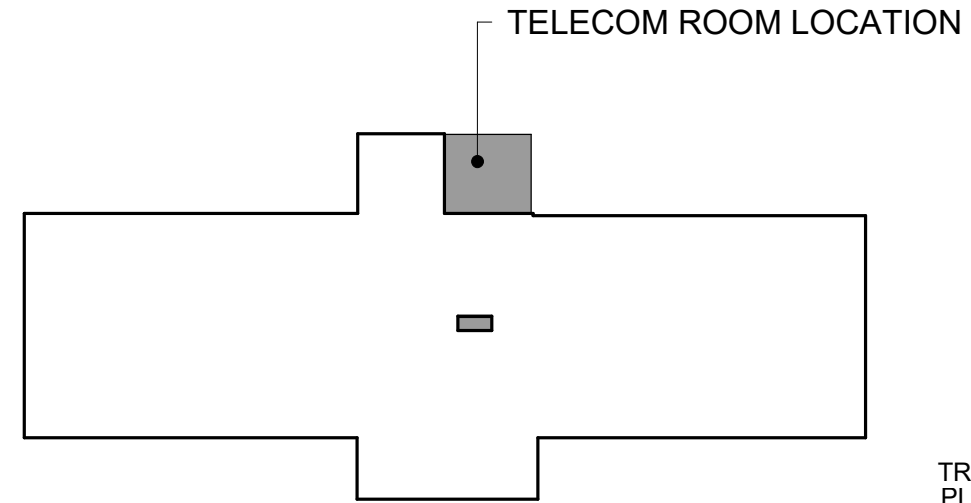

KEY PLAN - BLDG 5 2ND



35% SCHEMATIC DESIGN SUBMISSION	5.17.21
65% DESIGN DEVELOPMENT SUBMISSION	6.15.21
65% DESIGN DEVELOPMENT RESUBMISSION	8.25.21
Revisions:	Date:

CONSULTANT

IMEG

THE FUTURE IS IT'S HERE! www.imegcorp.com
15 SUNNEN DRIVE
SUITE 104
ST. LOUIS, MO 63143
P: 314.645.1132 F: 314.645.1173
PROJECT #18004375.03

ARCHITECT/ENGINEER OF RECORD

Romanyk Consulting
Focusing on what matters

Romanyk Consulting Corp. www.romanykconsulting.com
3308 Preston Road, Suite 350-164, Plano, Texas 75093

STAMP

Bicsi
DAVID LARSON
BICS1 ID # 106098
EXPIRES 12-31-25
REGISTERED COMMUNICATIONS DISTRIBUTION DESIGNER
RCDD

Office of
Construction
and Facilities
Management

VA U.S. Department
of Veterans Affairs

Drawing Title
**BUILDING 05 SECOND FLOOR PLAN -
TECHNOLOGY**

Approved:

Phase
FINAL BID DOCUMENTS

Sprinklered
FULLY SPRINKLERED

Project Title
**EHRM INFRASTRUCTURE
UPGRADES - MILWAUKEE, WI**

Location
5000 W. NATIONAL AVENUE, MILWAUKEE, WI

Issue Date
SEPTEMBER 05, 2025

Checked
PHINIE











Drawn
MAIBEJ

Project Number
695-21-700


Building Number
05

Drawing Number
05-TN102


- SHEET NOTES:**
1. ALL NETWORK CABLES ON THIS SHEET SHALL TERMINATE IN TR-05-204.
 2. CONTRACTOR TO PROVIDE NEW J-HOOK ROUTES FOR ALL NEW CABLING. J-HOOK SIZE AND QUANTITY TO BE PER MANUFACTURER RECOMMENDATIONS.
 3. REFER TO TNS00-TN600 FOR RISER DIAGRAMS.
 4. REFER TO SHEET TN402 FOR PENETRATION DETAILS.
 5. THESE DRAWINGS MAKE THE BEST ATTEMPT TO IDENTIFY EXISTING DATA DROPS/WORK AREA OUTLETS. AS LONG AS THE TOTAL NEWLY INSTALLED DATA DROP COUNT DOES NOT VARY +/- 10% IDENTIFIED ON THESE DRAWINGS, THE CONTRACTOR'S SCOPE SHALL BE UNCHANGED.
 6. NEW WORK AREA OUTLETS SHALL BE LOCATED IN EXISTING BOXES. WORK AREA OUTLETS SHOWN ON THIS SHEET MAY NOT BE IN THE EXACT LOCATION AS IDENTIFIED.
 7. CONTRACTOR TO INCLUDE AN ALLOWANCE FOR 10% ADDITIONAL 2-PORTS CAT6A INFORMATION OUTLETS IN THEIR PROPOSAL FOR THIS SHEET. FUTURE INFORMATION OUTLET LOCATIONS WILL BE DETERMINED BY THE VA AT A LATER DATE.
- KEYNOTES:** C #
1. USE EXISTING CLOSET AS CABLE PASS-THRU FOR HORIZONTAL CABLES ON 3RD FLOOR TO TERMINATE IN CLOSET ON LEVEL 2.

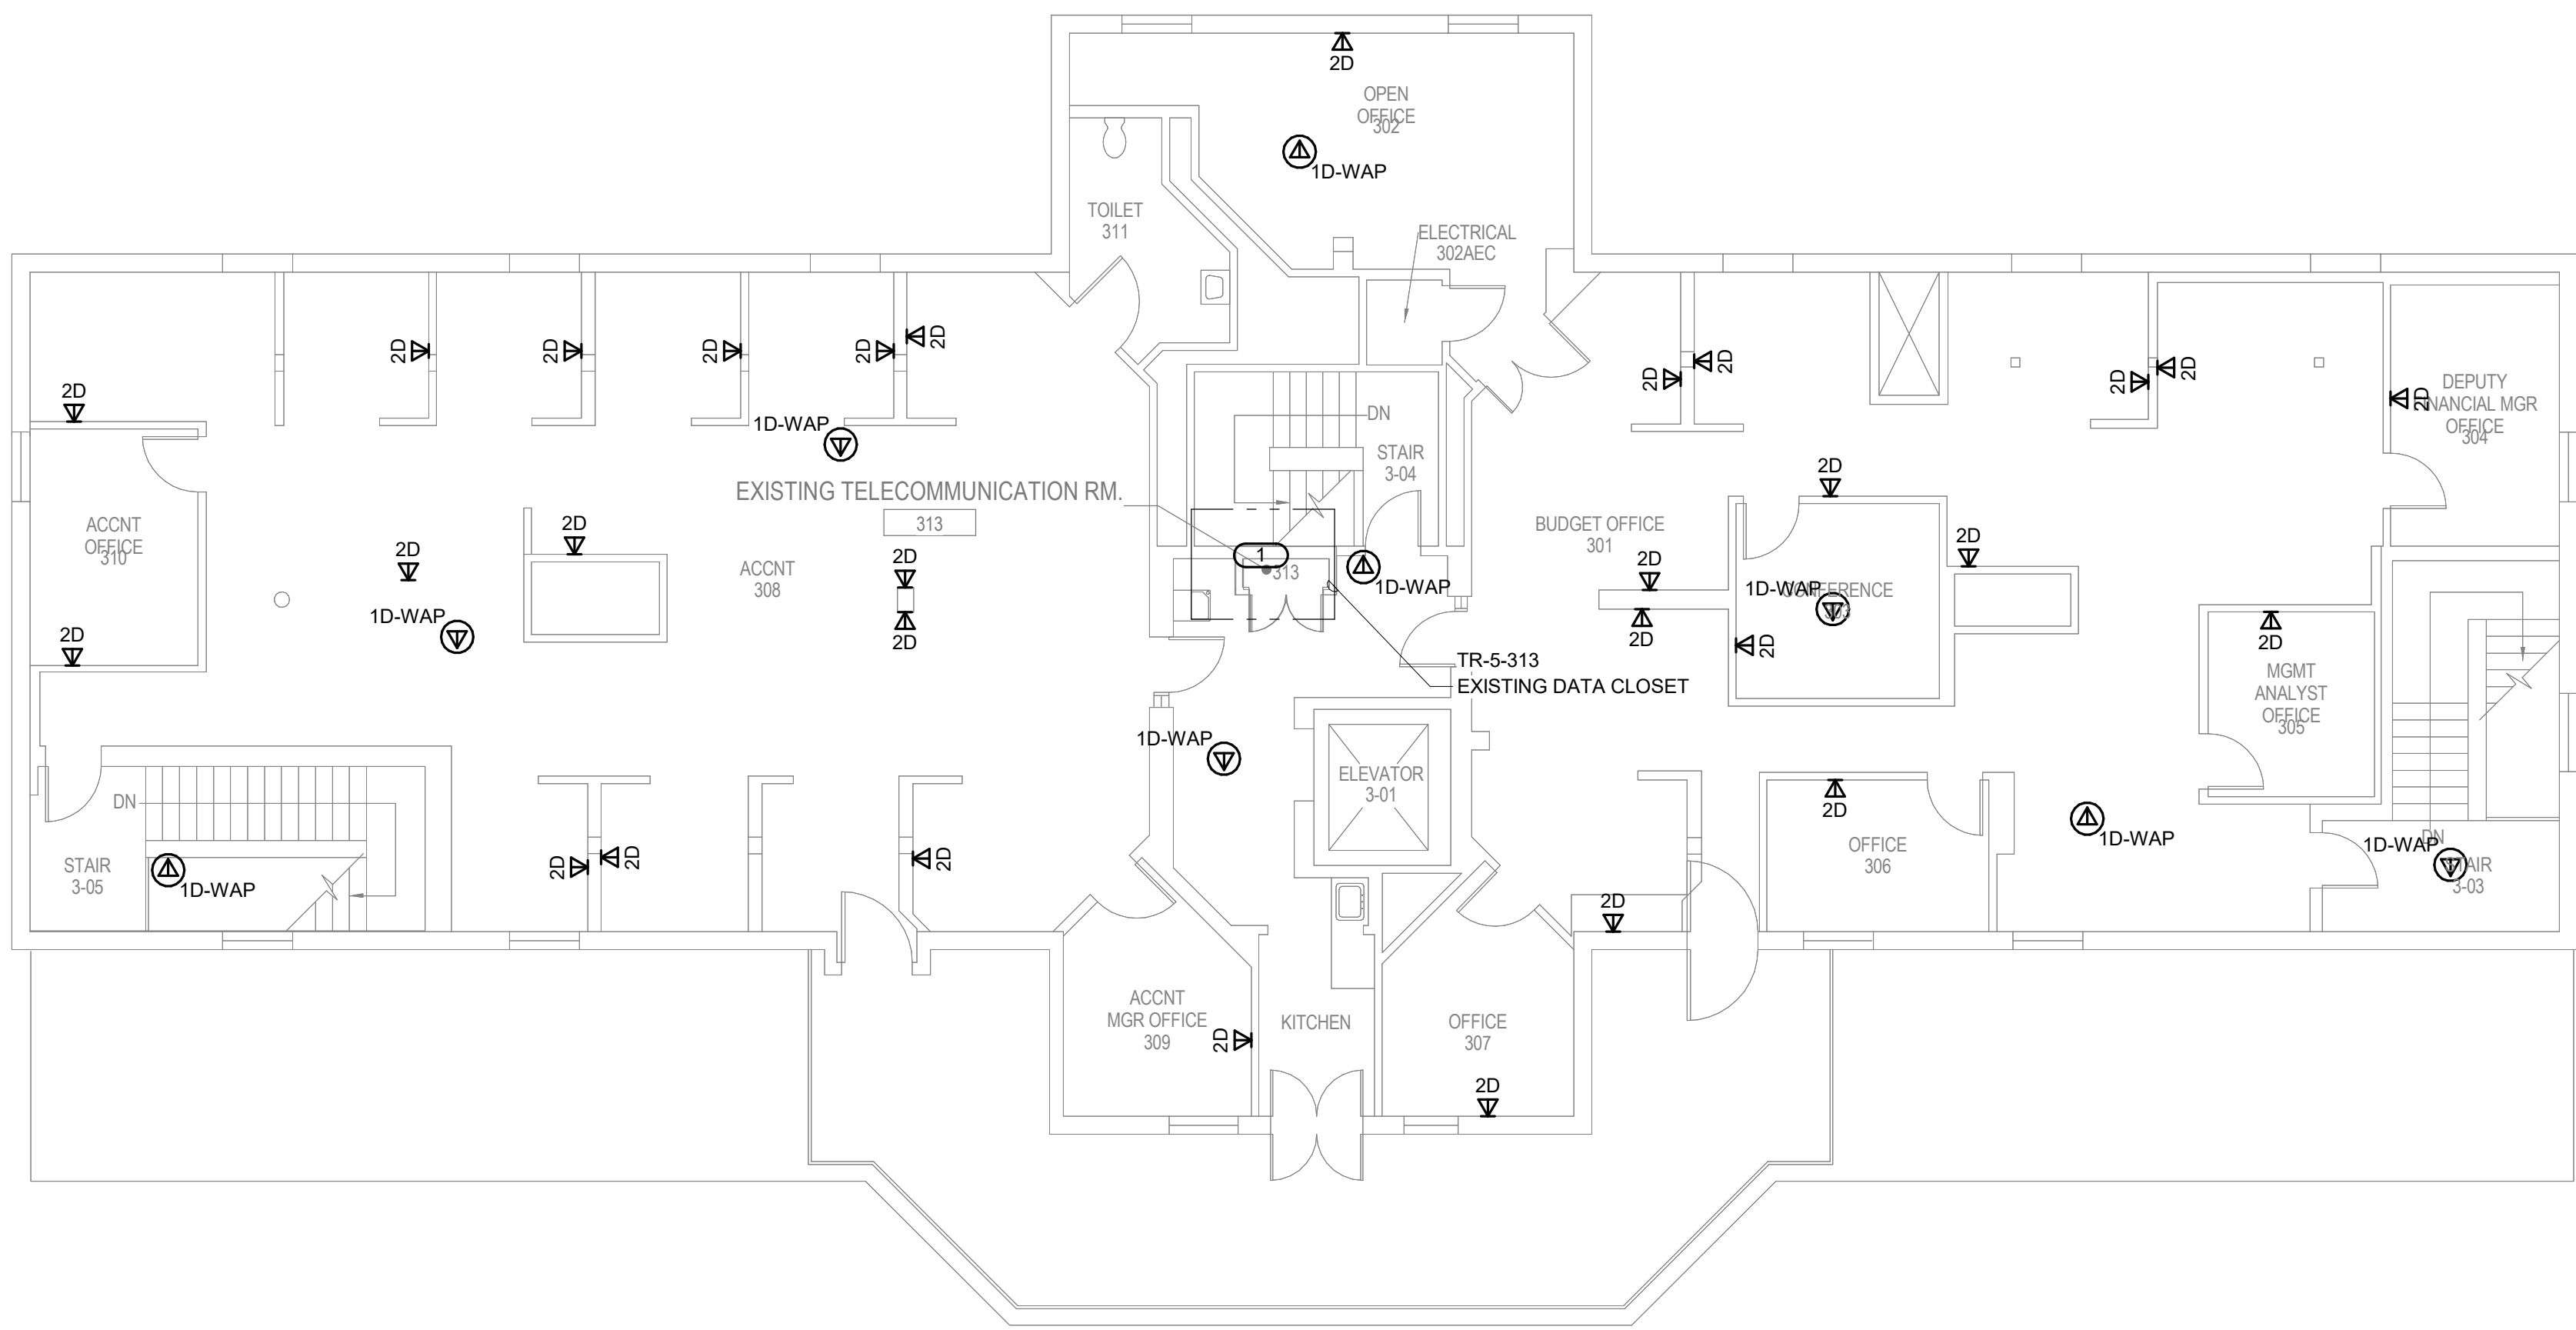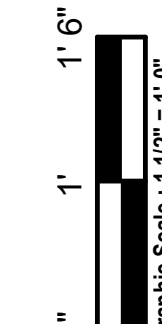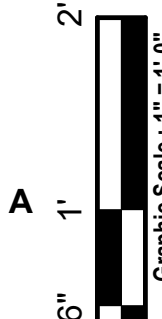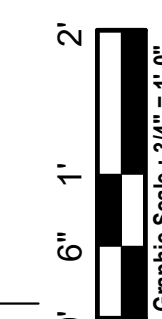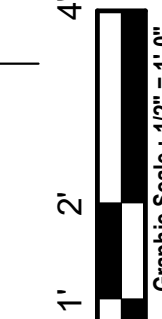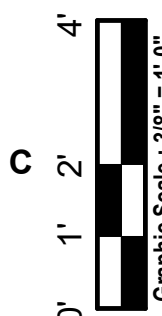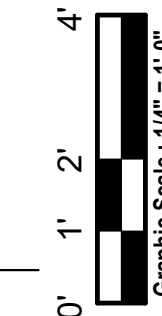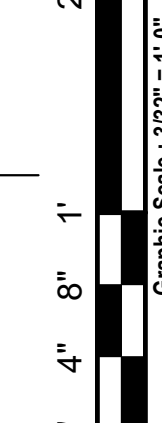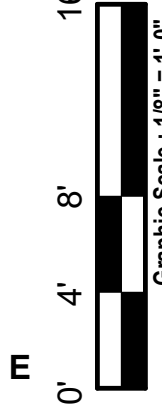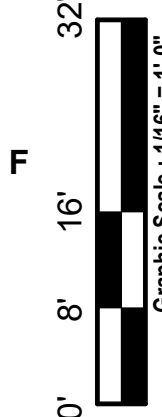

1 BUILDING 05 THIRD FLOOR PLAN - TECHNOLOGY
1/8" = 1'-0"

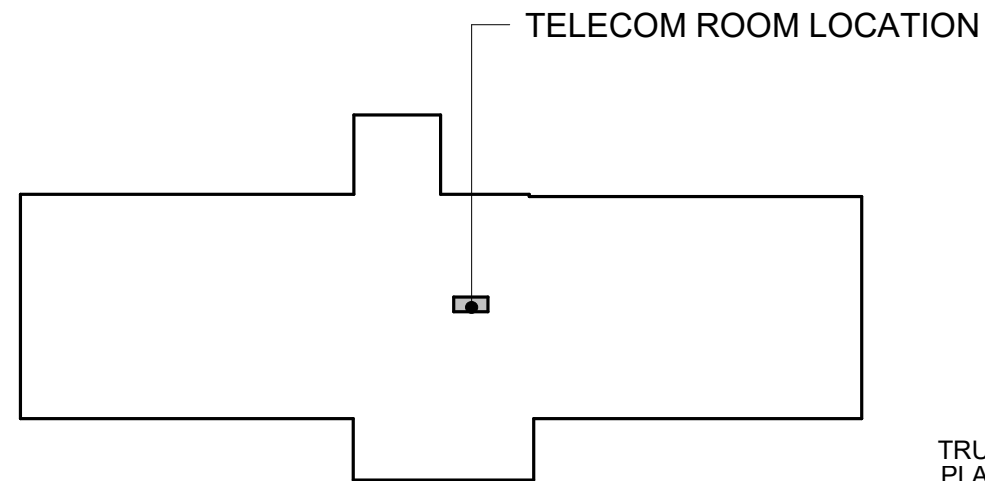

KEY PLAN - BLDG 5
NTS

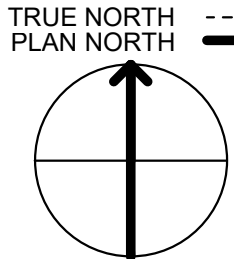

35% SCHEMATIC DESIGN SUBMISSION	5.17.21
65% DESIGN DEVELOPMENT SUBMISSION	6.15.21
65% DESIGN DEVELOPMENT RESUBMISSION	8.25.21
Revisions:	Date:

CONSULTANT

IMEG

15 SUNNEN DRIVE
SUITE 104
ST. LOUIS, MO 63143
P: 314.645.1132 F: 314.645.1173
PROJECT #18004375.03

ARCHITECT/ENGINEER OF RECORD

Romanyk Consulting
Focusing on what matters

Romanyk Consulting Corp. www.romanykconsulting.com
3308 Preston Road, Suite 350-164, Plano, Texas 75093

STAMP

Bicsi
DAVID LARSON
BICS1 ID # 106098
Expires 12-31-25
REGISTERED COMMUNICATIONS DISTRIBUTION DESIGNER
RCDD

Office of
Construction
and Facilities
Management

VA U.S. Department
of Veterans Affairs

Drawing Title
**BUILDING 05 THIRD FLOOR PLAN -
TECHNOLOGY**

Approved:

Phase
FINAL BID DOCUMENTS

Sprinklered
FULLY SPRINKLERED

Project Title
**EHRM INFRASTRUCTURE
UPGRADES - MILWAUKEE, WI**

Location
5000 W. NATIONAL AVENUE, MILWAUKEE, WI

Issue Date
SEPTEMBER 05, 2025

Checked
PHINIE

Drawn
MAIBEJ

Project Number
695-21-700

Building Number
05

Drawing Number
05-TN103

F

E

D


C

B

A


9/2/2025 3:54:48 PM

Autodesk Docs\DCFM East - Milwaukee EHRM (R24)T24_1804375\03_VA Milwaukee EHRM_C.dwg

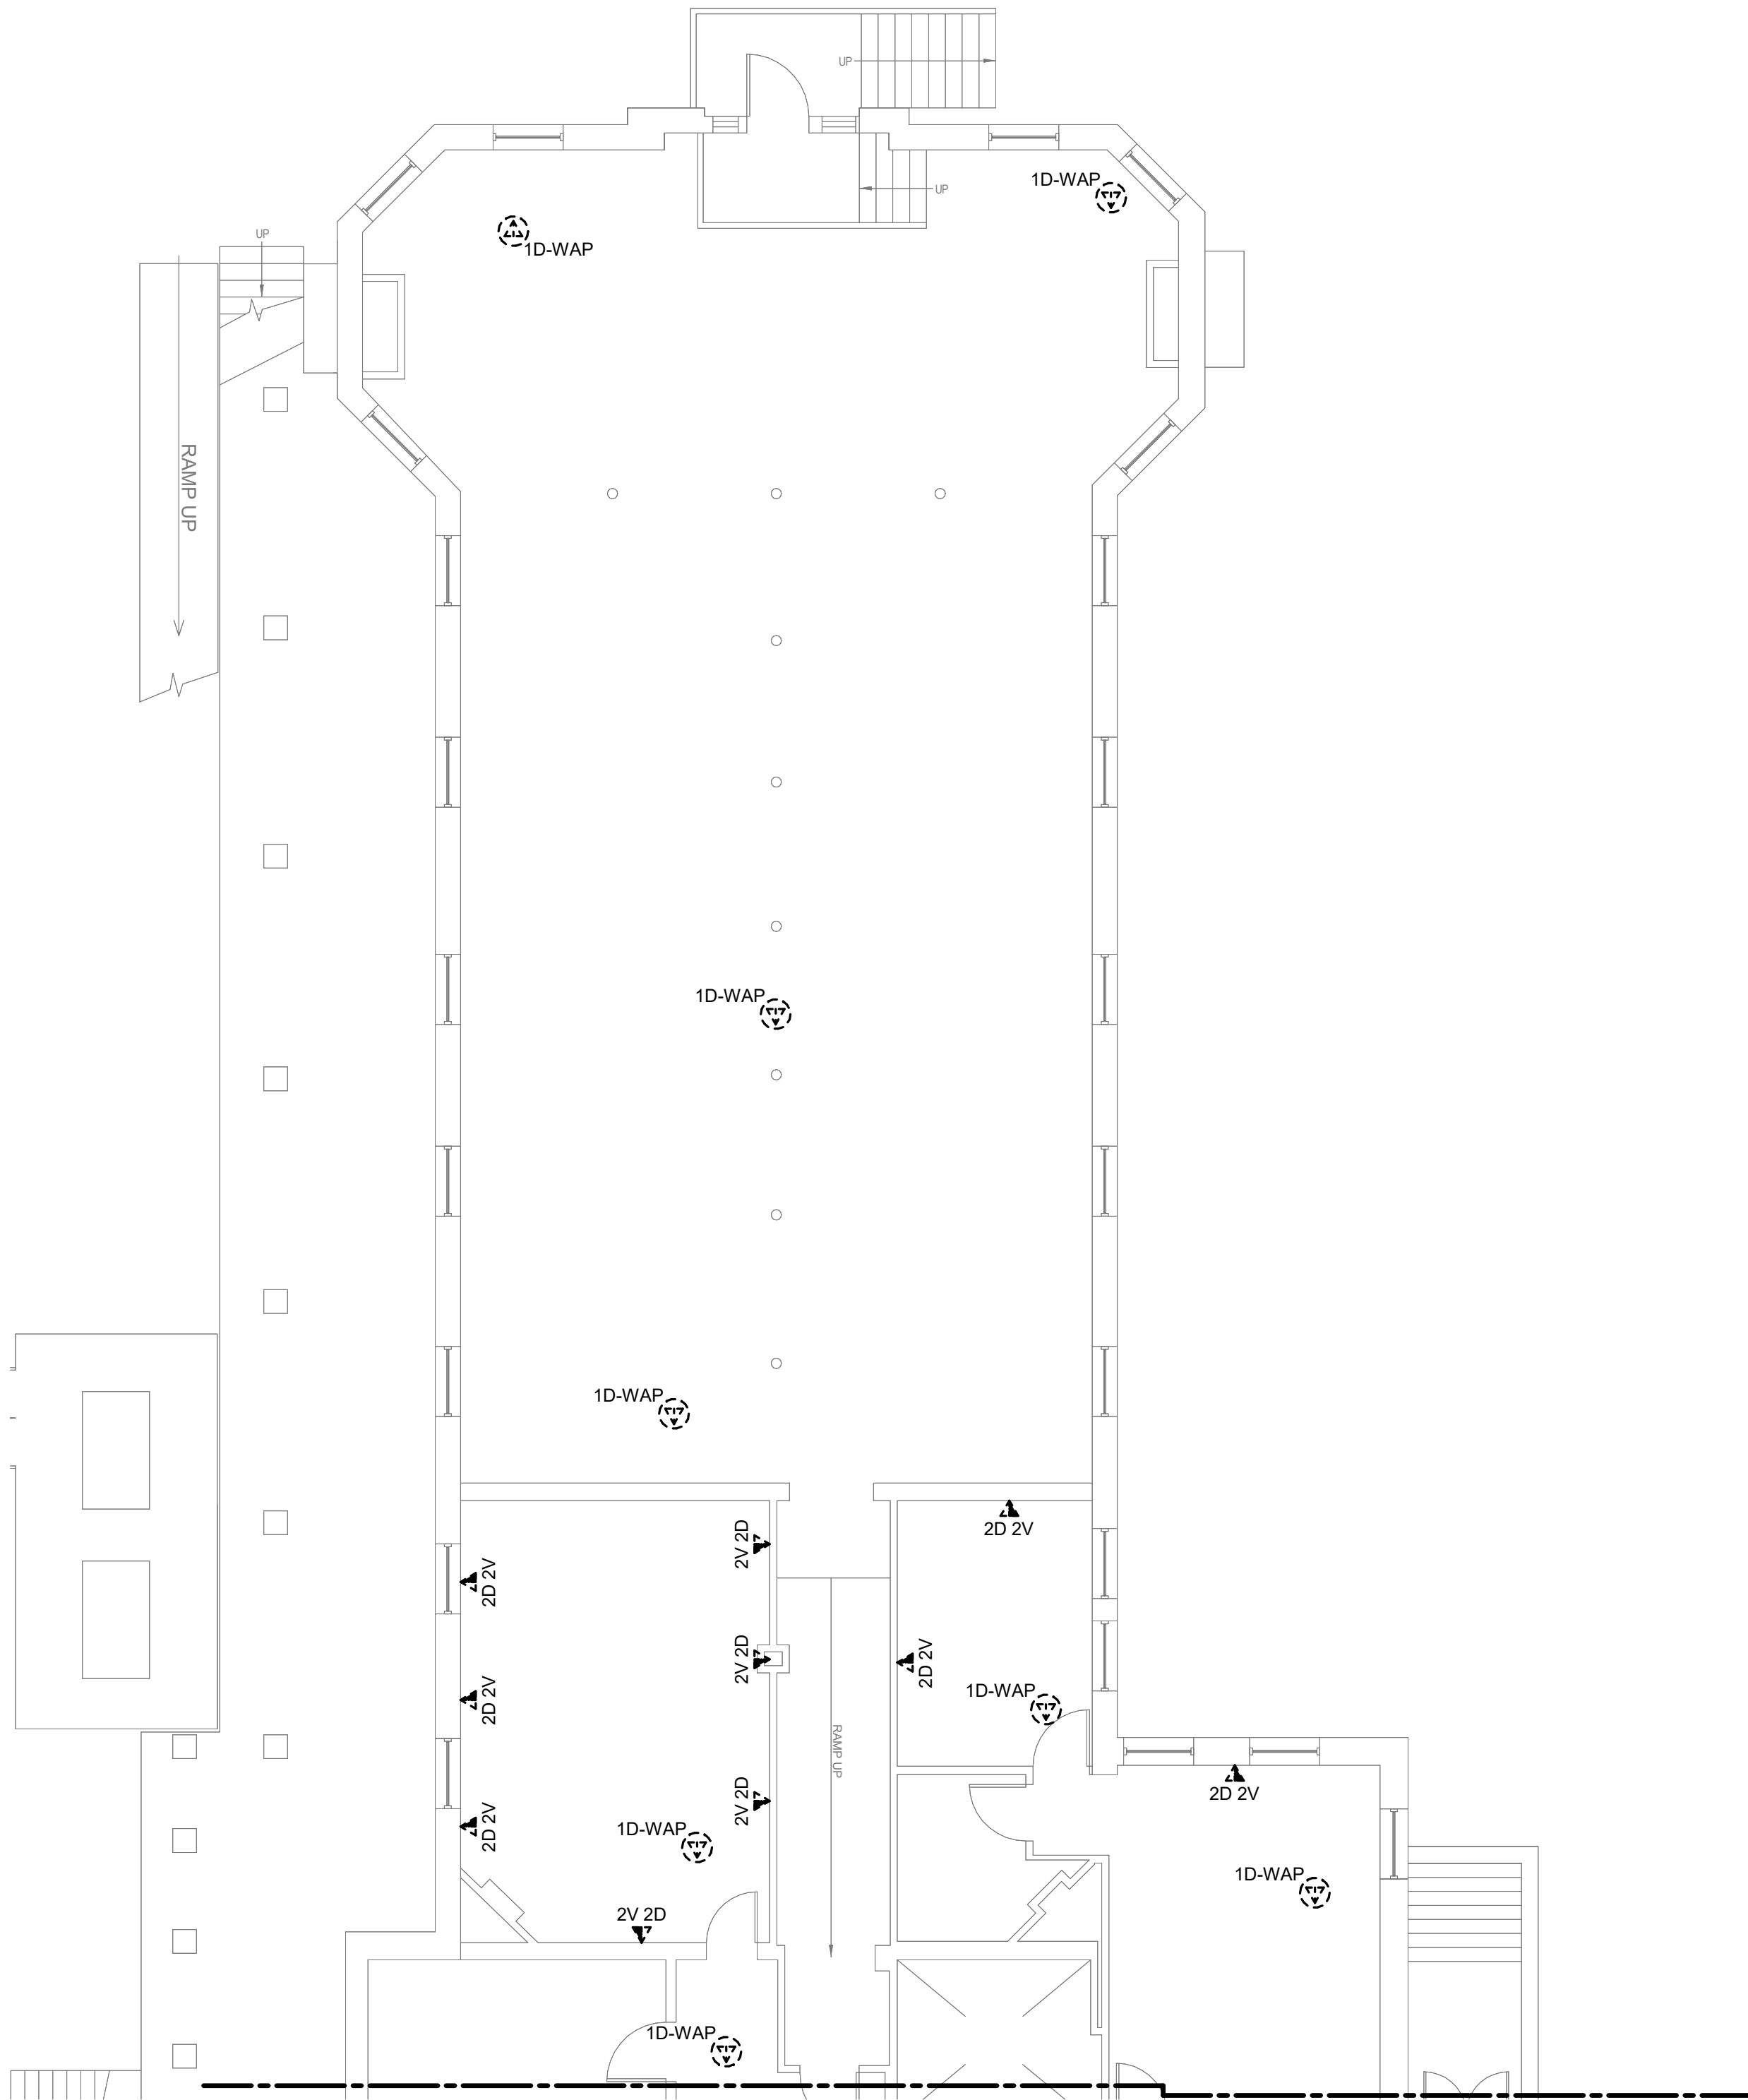

1 BUILDING 06 BASEMENT FLOOR DEMOLITION PLAN - TECHNOLOGY - AREA A NORTH

1/8" = 1'-0"

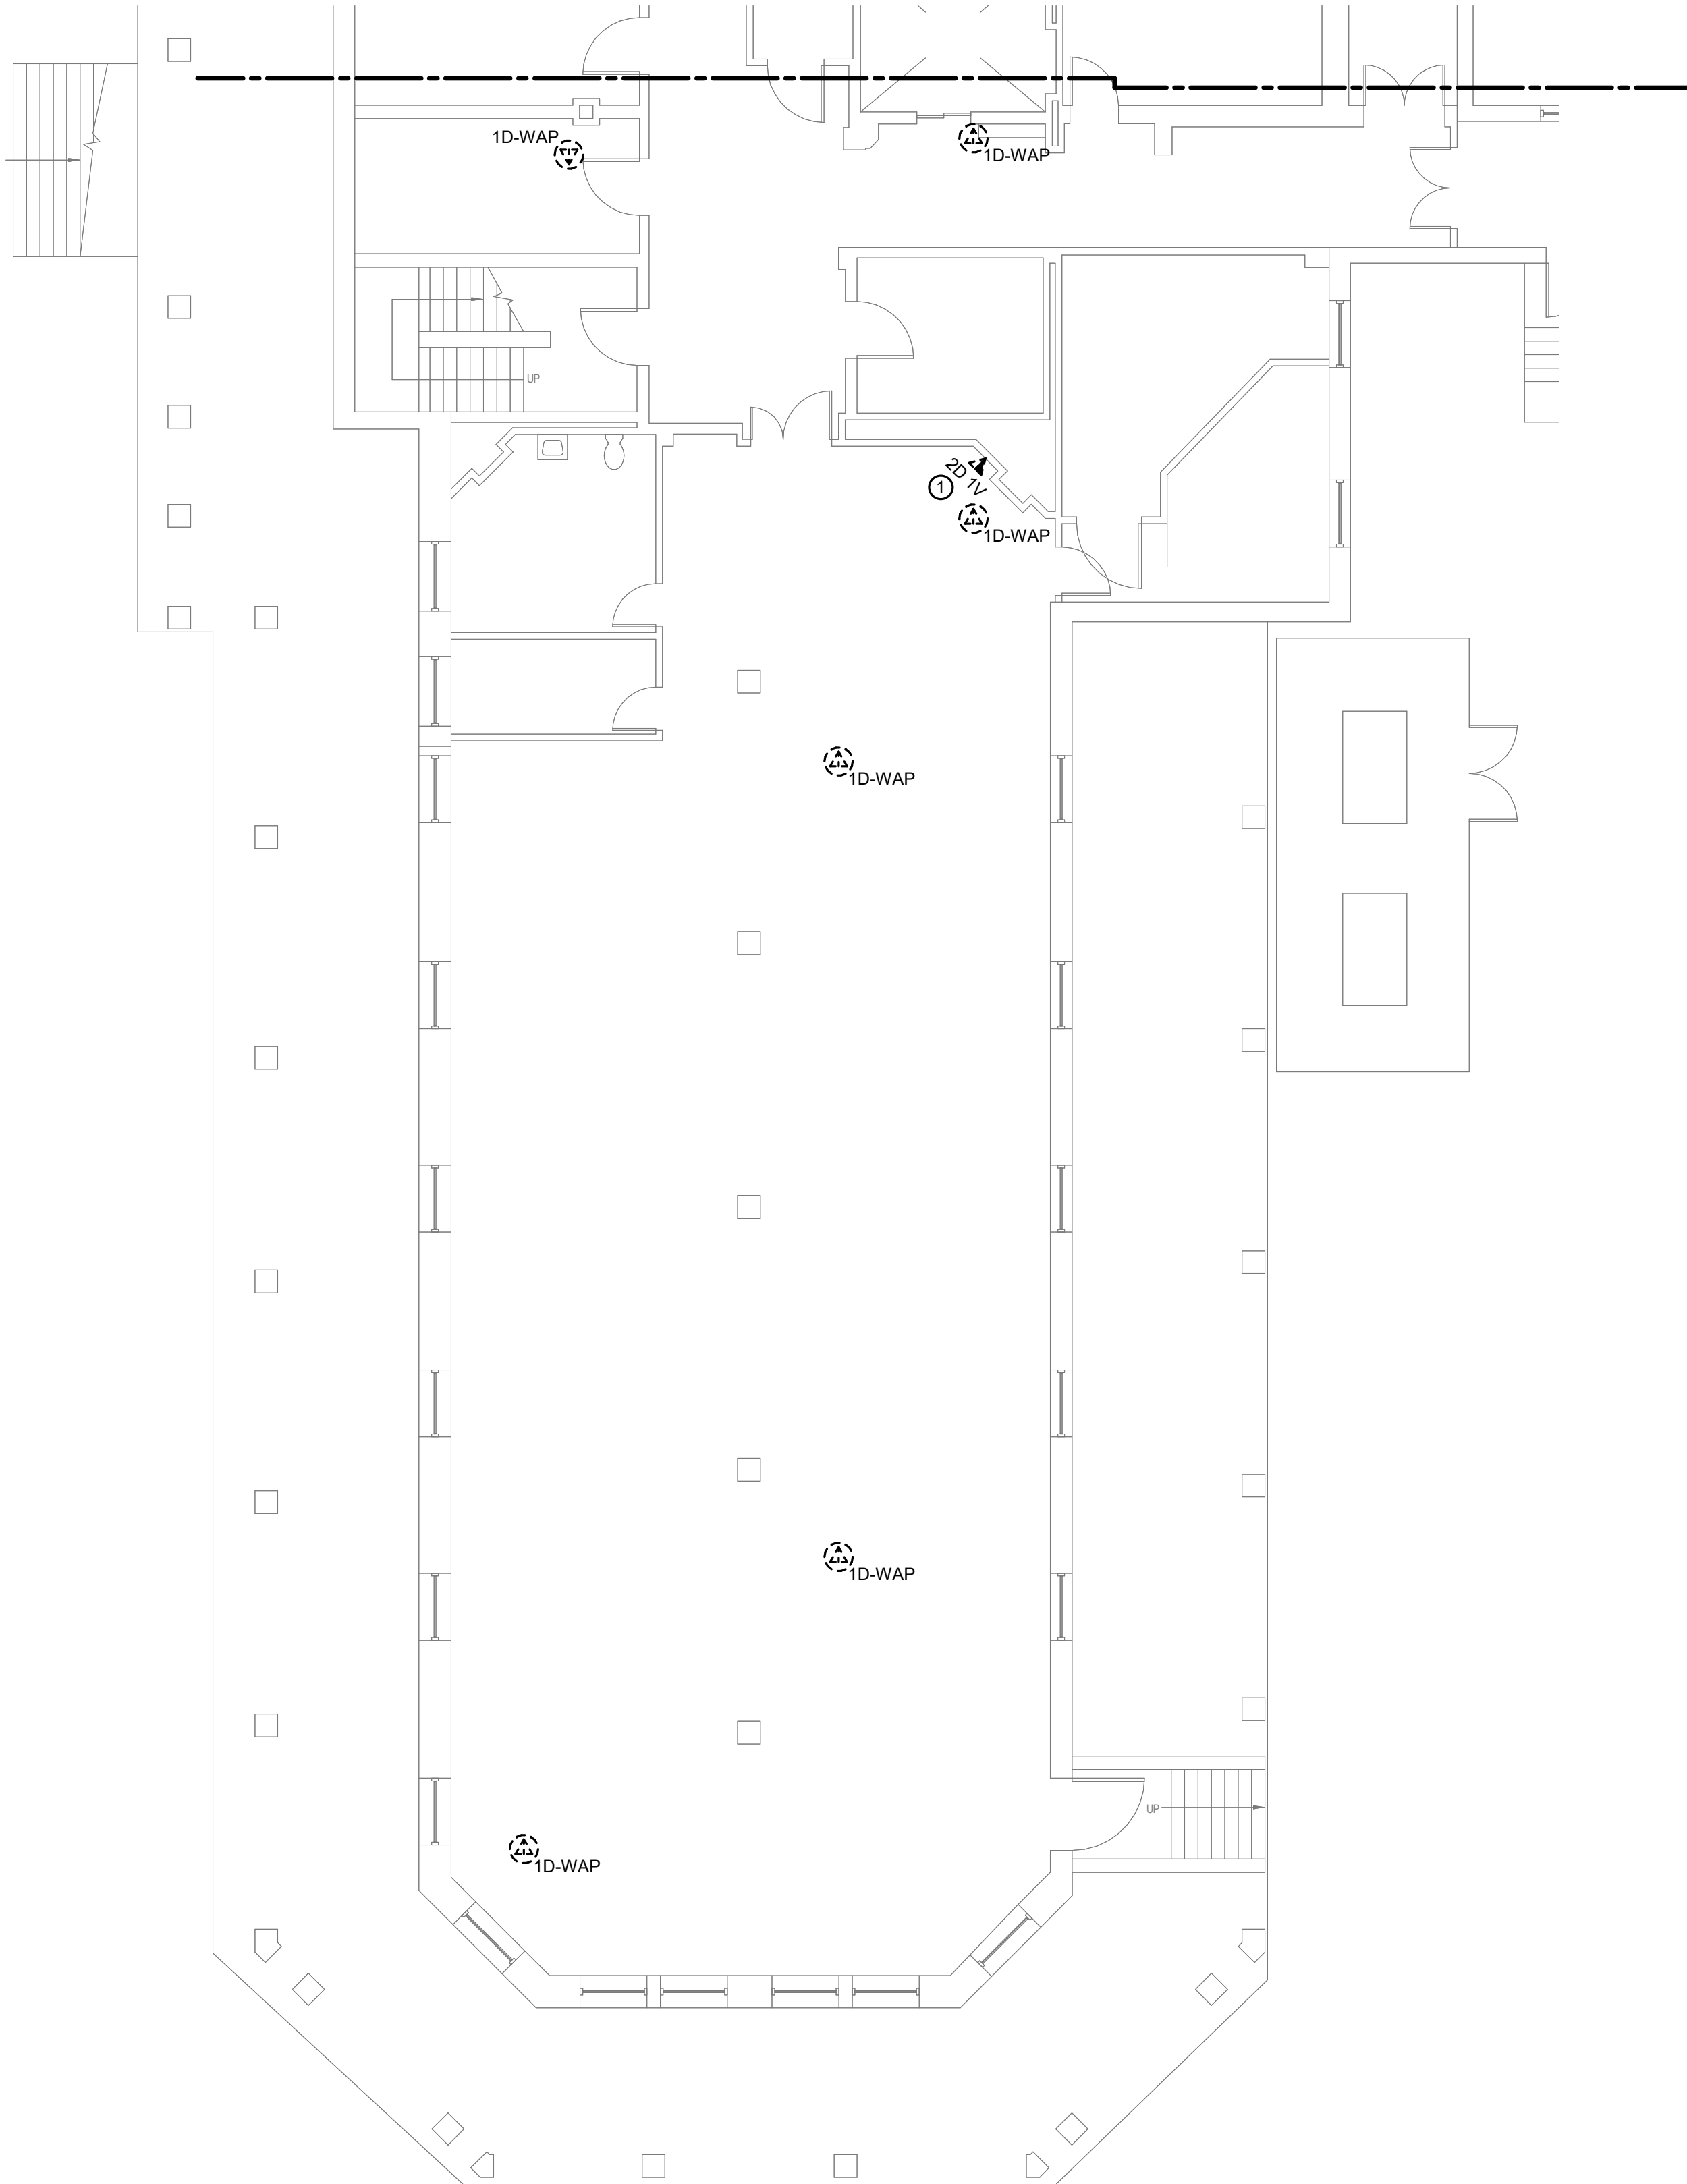

2 BUILDING 06 BASEMENT FLOOR DEMOLITION PLAN - TECHNOLOGY - AREA A SOUTH

1/8" = 1'-0"

- SHEET NOTES:**
1. REMOVE ALL NETWORK CABLING TO POINTS OF TERMINATION IN ASSOCIATED DATA CLOSET. REFER TO FLOOR PLANS AND SHEET T1001 FOR TR ROOM LOCATIONS.
 2. REFER TO ARCHITECTURAL PHASING PLANS FOR WHEN EXISTING CABLING IS ALLOWED TO BE DEMOLISHED.
 3. FOR ALL EXISTING WIRELESS ACCESS POINTS AND SURVEILLANCE CAMERAS, DEVICES SHALL REMAIN. SCOPE OF WORK INCLUDES CABLE REPLACEMENT ONLY. COORDINATE WITH COR FOR ANY DOWNTIME OF DEVICES. EXISTING LOCATIONS OF WORK AREA, OUTLETS SHOWN ON THIS SHEET MAY NOT NECESSARILY BE IN THE EXACT LOCATION AS IDENTIFIED.

32'
16'
8'
0'

Graphic Scale: 1/16" = 1'-0"

16'
8'
4'
0'

Graphic Scale: 1/8" = 1'-0"

2'
1'
8"
4"
0'

Graphic Scale: 3/32" = 1'-0"

4'
2'
1'
0'

Graphic Scale: 1/4" = 1'-0"

4'
2'
1'
0'

Graphic Scale: 3/8" = 1'-0"

4'
2'
1'
0'

Graphic Scale: 1/2" = 1'-0"

6"
3"
1'
0'


Graphic Scale: 3/4" = 1'-0"

2'
1'
0'

Graphic Scale: 1" = 1'-0"

6"
3"
1'
0'

Graphic Scale: 1 1/2" = 1'-0"

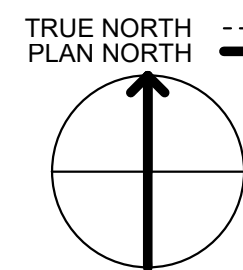

35% SCHEMATIC DESIGN SUBMISSION	5.17.21
65% DESIGN DEVELOPMENT SUBMISSION	6.15.21
65% DESIGN DEVELOPMENT RESUBMISSION	8.25.21
Revisions:	Date:

CONSULTANT

IMEG

15 SUNNEN DRIVE
SUITE 104
ST. LOUIS, MO 63143
P: 314.645.1132 F: 314.645.1173
PROJECT #18004375.03

ARCHITECT/ENGINEER OF RECORD

Romanyk Consulting
Focusing on what matters

Romanyk Consulting Corp. www.romanykconsulting.com
3308 Preston Road, Suite 350-164, Plano, Texas 75093

STAMP

Bicsi
DAVID LARSON
BICS1 ID # 106098
EXPIRES 12-31-25
REGISTERED COMMUNICATIONS DISTRIBUTION DESIGNER

Office of
Construction
and Facilities
Management

VA U.S. Department
of Veterans Affairs

Drawing Title
BUILDING 06 BASEMENT DEMO PLAN -
TECHNOLOGY - AREA A

Approved:

Phase
FINAL BID DOCUMENTS

Sprinklered
FULLY SPRINKLERED

Project Title
EHRM INFRASTRUCTURE
UPGRADES - MILWAUKEE, WI

Location
5000 W. NATIONAL AVENUE, MILWAUKEE, WI

Issue Date
SEPTEMBER 05, 2025

Checked
PHINIE

Drawn
MAIBEJ

Project Number
695-21-700

Building Number
06

Drawing Number
06-TD100A

F

E

D

C


B

A











9/3/2025 3:54:49 PM

Autodesk Docs\DOCFM East - Milwaukee EHRM (R24)T24_1804375\03_VA Milwaukee_C.dwg

- SHEET NOTES:**
1. REMOVE ALL NETWORK CABLING TO POINTS OF TERMINATION IN ASSOCIATED DATA CLOSET. REFER TO FLOOR PLANS AND SHEET T1001 FOR TR ROOM LOCATIONS.
 2. REFER TO ARCHITECTURAL PHASING PLANS FOR WHEN EXISTING CABLING IS ALLOWED TO BE DEMOLISHED.
 3. FOR ALL EXISTING WIRELESS ACCESS POINTS AND SURVEILLANCE CAMERAS, DEVICES SHALL REMAIN. SCOPE OF WORK INCLUDES CABLE REPLACEMENT ONLY. COORDINATE WITH COR FOR ANY DOWNTIME OF DEVICES.
 4. EXISTING LOCATIONS OF WORK AREA, OUTLETS SHOWN ON THIS SHEET MAY NOT NECESSARILY BE IN THE EXACT LOCATION AS IDENTIFIED.

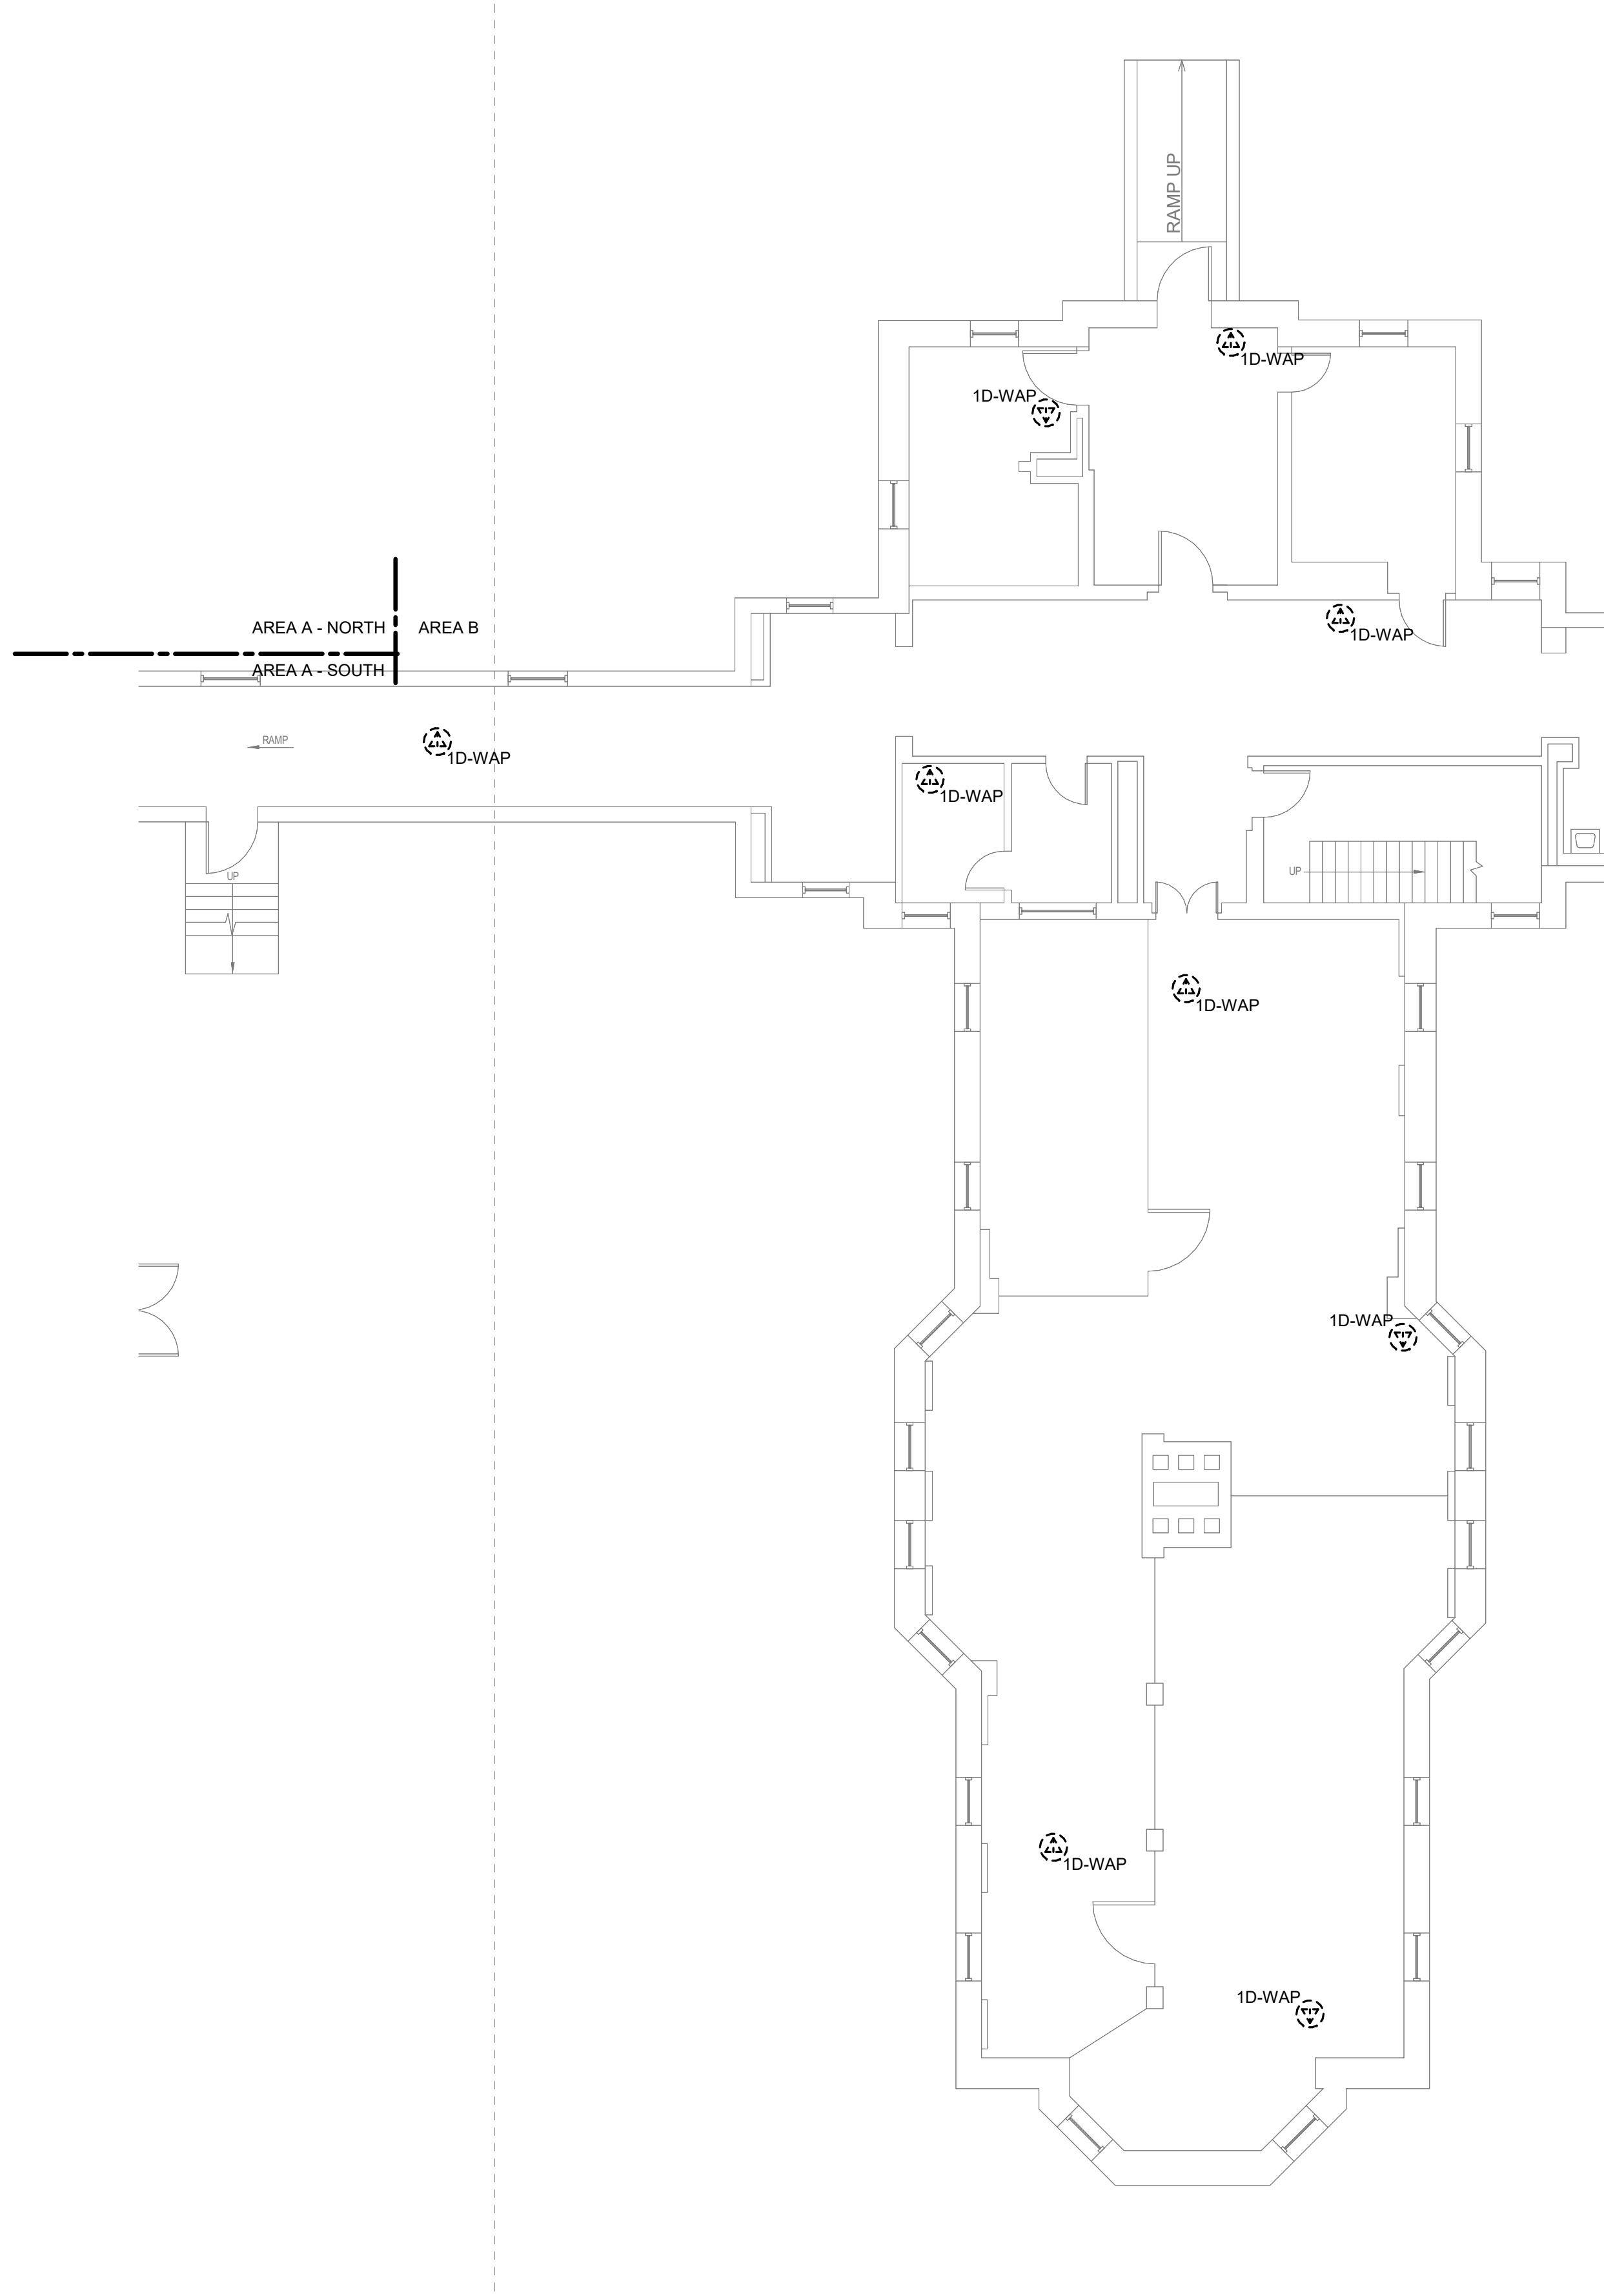

1 BUILDING 06 BASEMENT FLOOR DEMOLITION PLAN - TECHNOLOGY - AREA B
1/8" = 1'-0"

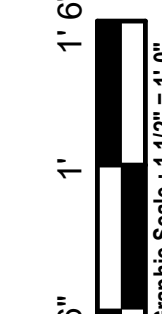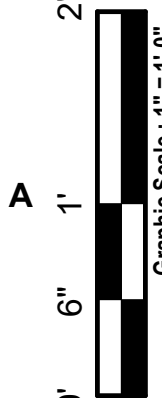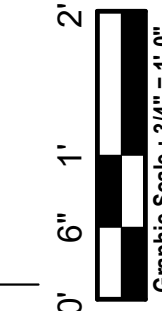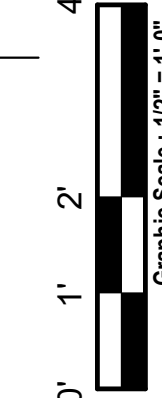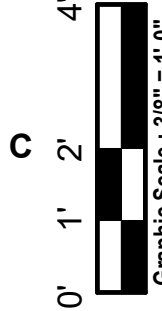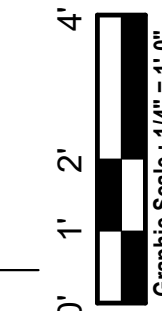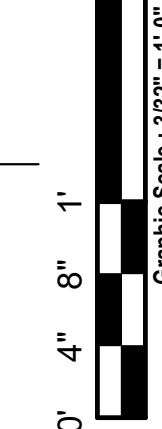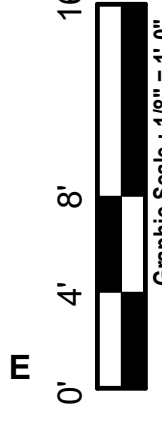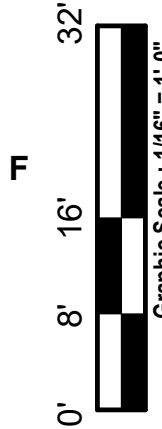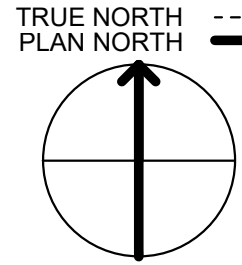

35% SCHEMATIC DESIGN SUBMISSION	5.17.21
65% DESIGN DEVELOPMENT SUBMISSION	6.15.21
65% DESIGN DEVELOPMENT RESUBMISSION	8.25.21
Revisions:	Date:

CONSULTANT

IMEG

THE FUTURE IS IT Solutions www.imegcorp.com
15 SUNNEN DRIVE
SUITE 104
ST. LOUIS, MO 63143
P: 314.645.1132 F: 314.645.1173
PROJECT #18004375.03

ARCHITECT/ENGINEER OF RECORD

Romanyk Consulting
Focusing on what matters

Romanyk Consulting Corp. www.romanykconsulting.com
3308 Preston Road, Suite 350-164, Plano, Texas 75093

STAMP

Bicsi
DAVID LARSON
BICS1 ID # 106098
EXPIRES 12-31-25
REGISTERED COMMUNICATIONS DISTRIBUTION DESIGNER
RCDD

Office of
Construction
and Facilities
Management

VA U.S. Department
of Veterans Affairs

Drawing Title
BUILDING 06 BASEMENT DEMO PLAN -
TECHNOLOGY - AREA B

Approved:

Phase
FINAL BID DOCUMENTS

Sprinklered
FULLY SPRINKLERED

Project Title
EHRM INFRASTRUCTURE
UPGRADES - MILWAUKEE, WI

Location
5000 W. NATIONAL AVENUE MILWAUKEE, WI

Issue Date
SEPTEMBER 05, 2025


Checked
PHINIE

Drawn
MAIBEJ

Project Number
695-21-700

Building Number
06

Drawing Number
06-TD100B

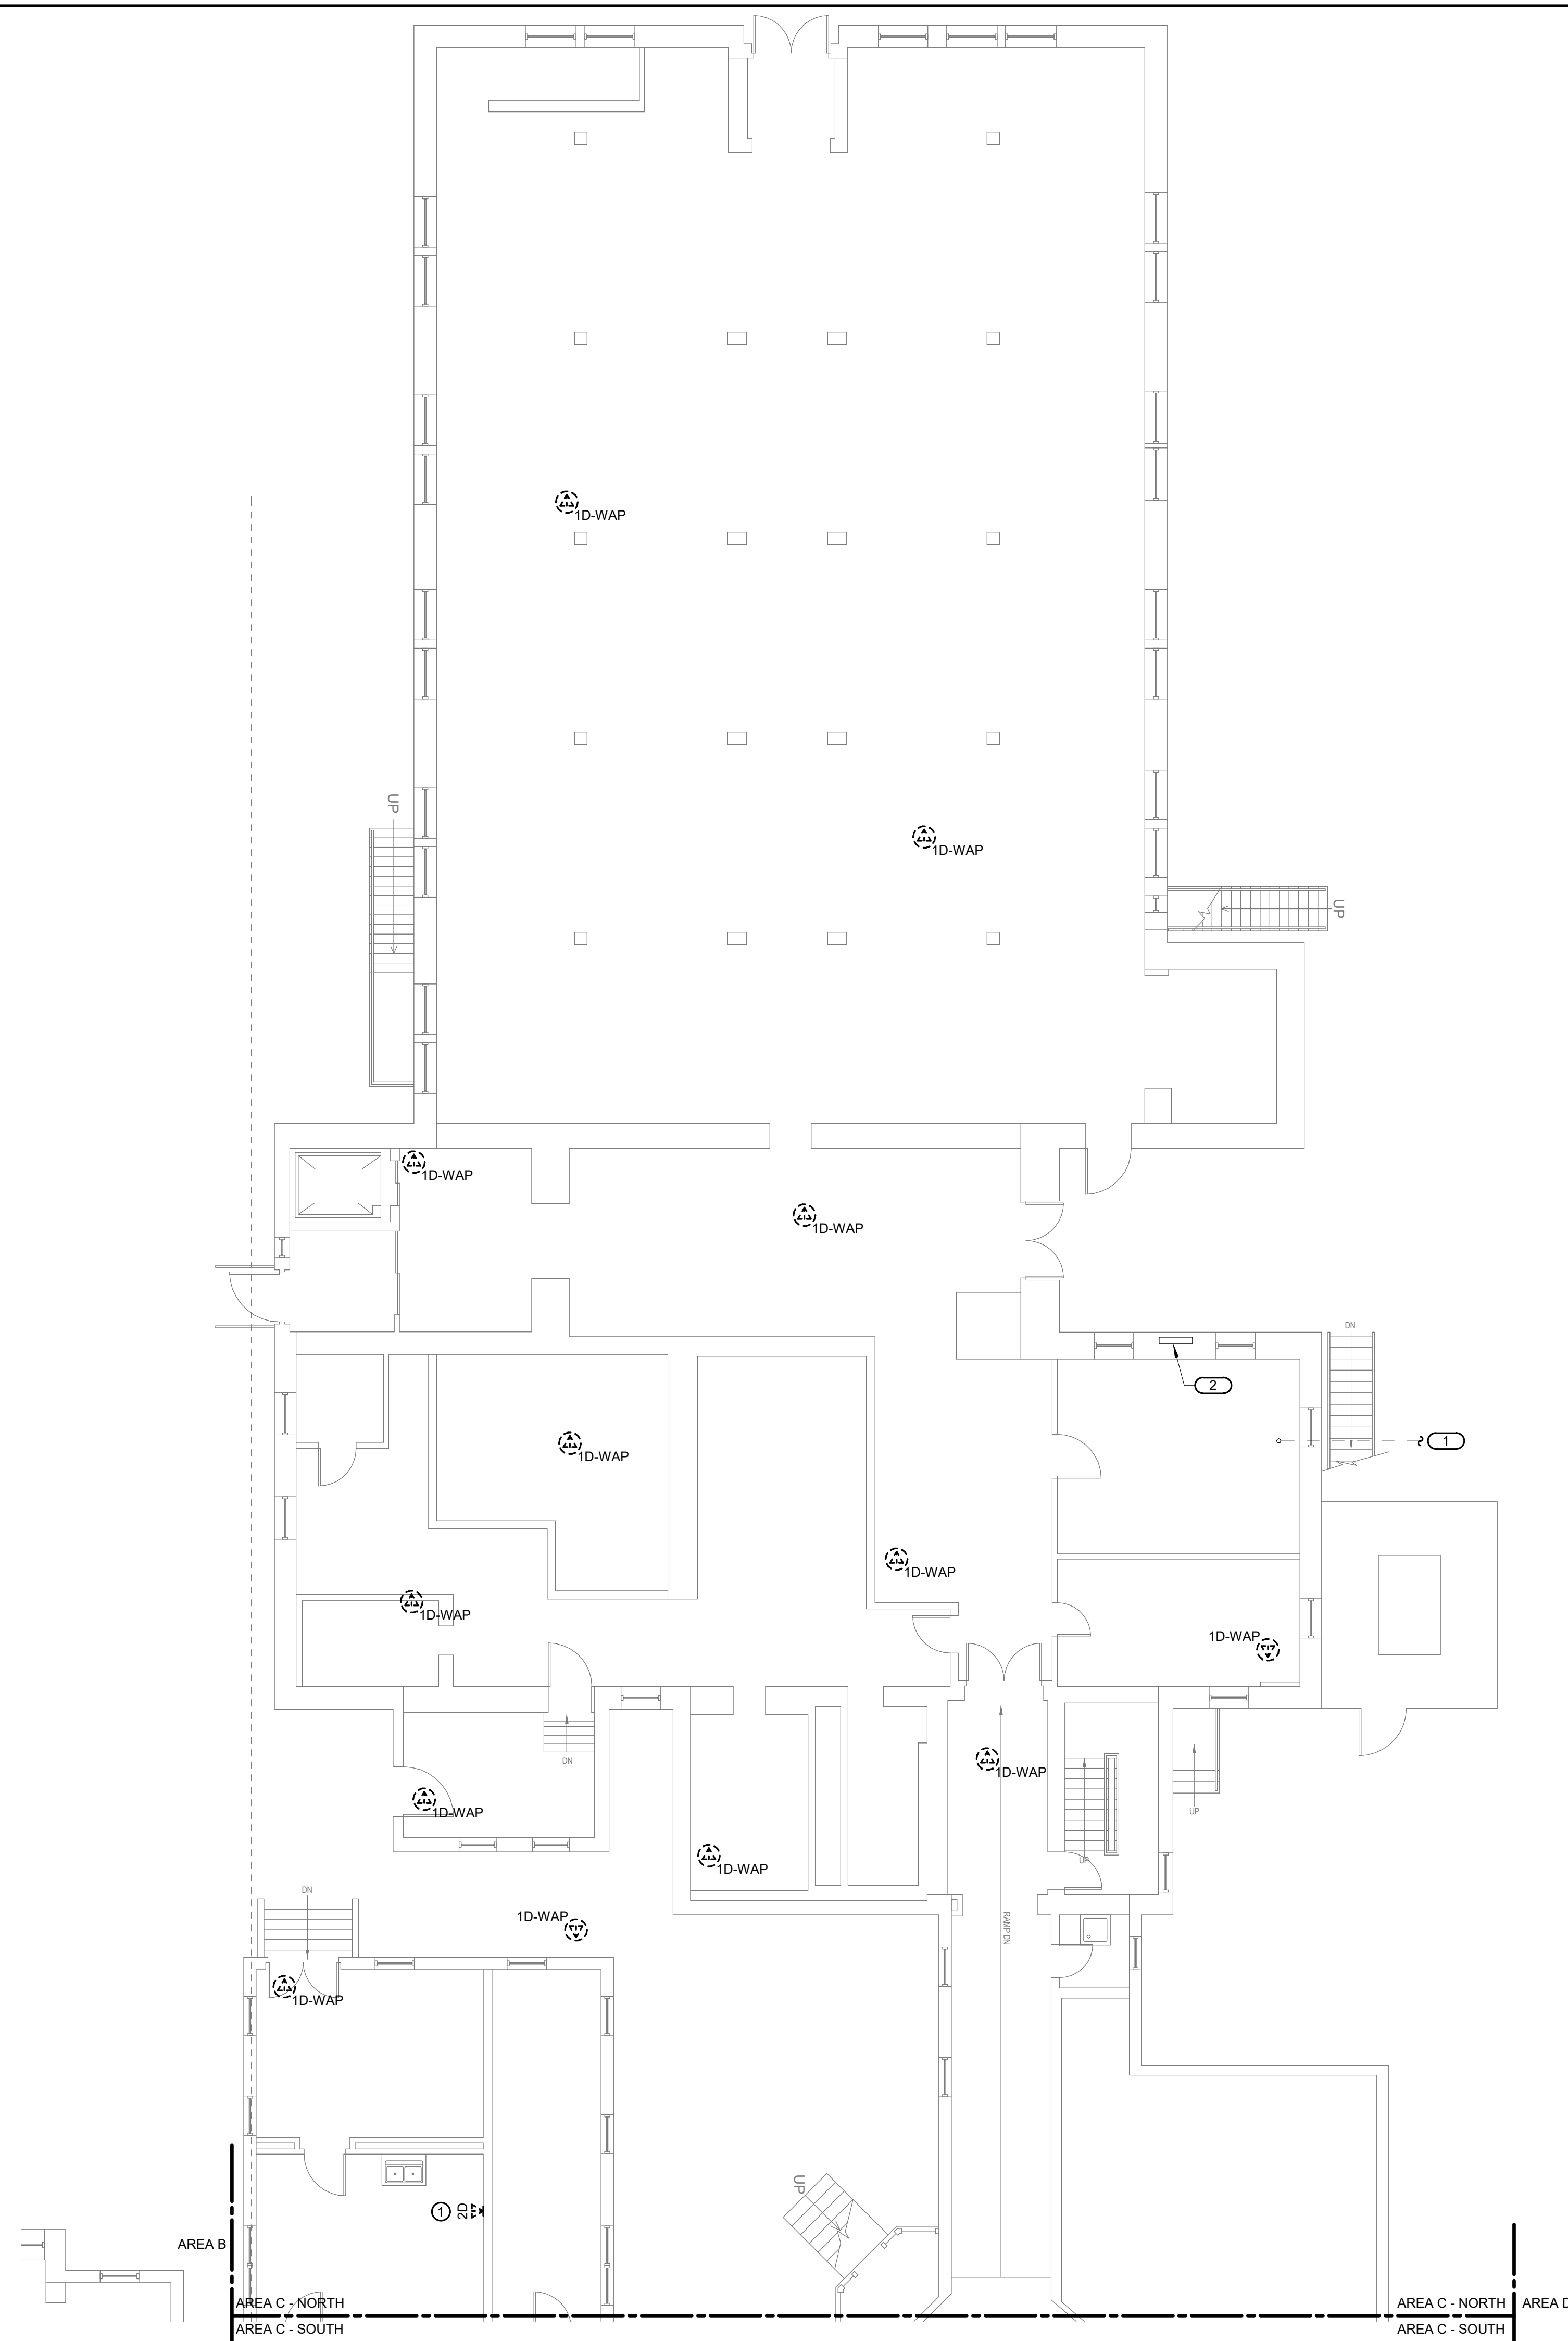

F

E

D

C


B

A










9/2/2025 3:54:52 PM

Autodesk Docs\DOCFM East - Milwaukee EHRM (R24)T24_1804375\03_VA Milwaukee_C.dwt

- SHEET NOTES:**
1. REMOVE ALL NETWORK CABLING TO POINTS OF TERMINATION IN ASSOCIATED DATA CLOSET. REFER TO FLOOR PLANS AND SHEET T1001 FOR TR ROOM LOCATIONS.
 2. REFER TO ARCHITECTURAL PHASING PLANS FOR WHEN EXISTING CABLING IS ALLOWED TO BE DEMOLISHED.
 3. FOR ALL EXISTING WIRELESS ACCESS POINTS AND SURVEILLANCE CAMERAS, DEVICES SHALL REMAIN. SCOPE OF WORK INCLUDES CABLE REPLACEMENT ONLY. COORDINATE WITH COR FOR ANY DOWNTIME OF DEVICES.
 4. EXISTING LOCATIONS OF WORK AREA, OUTLETS SHOWN ON THIS SHEET MAY NOT NECESSARILY BE IN THE EXACT LOCATION AS IDENTIFIED.

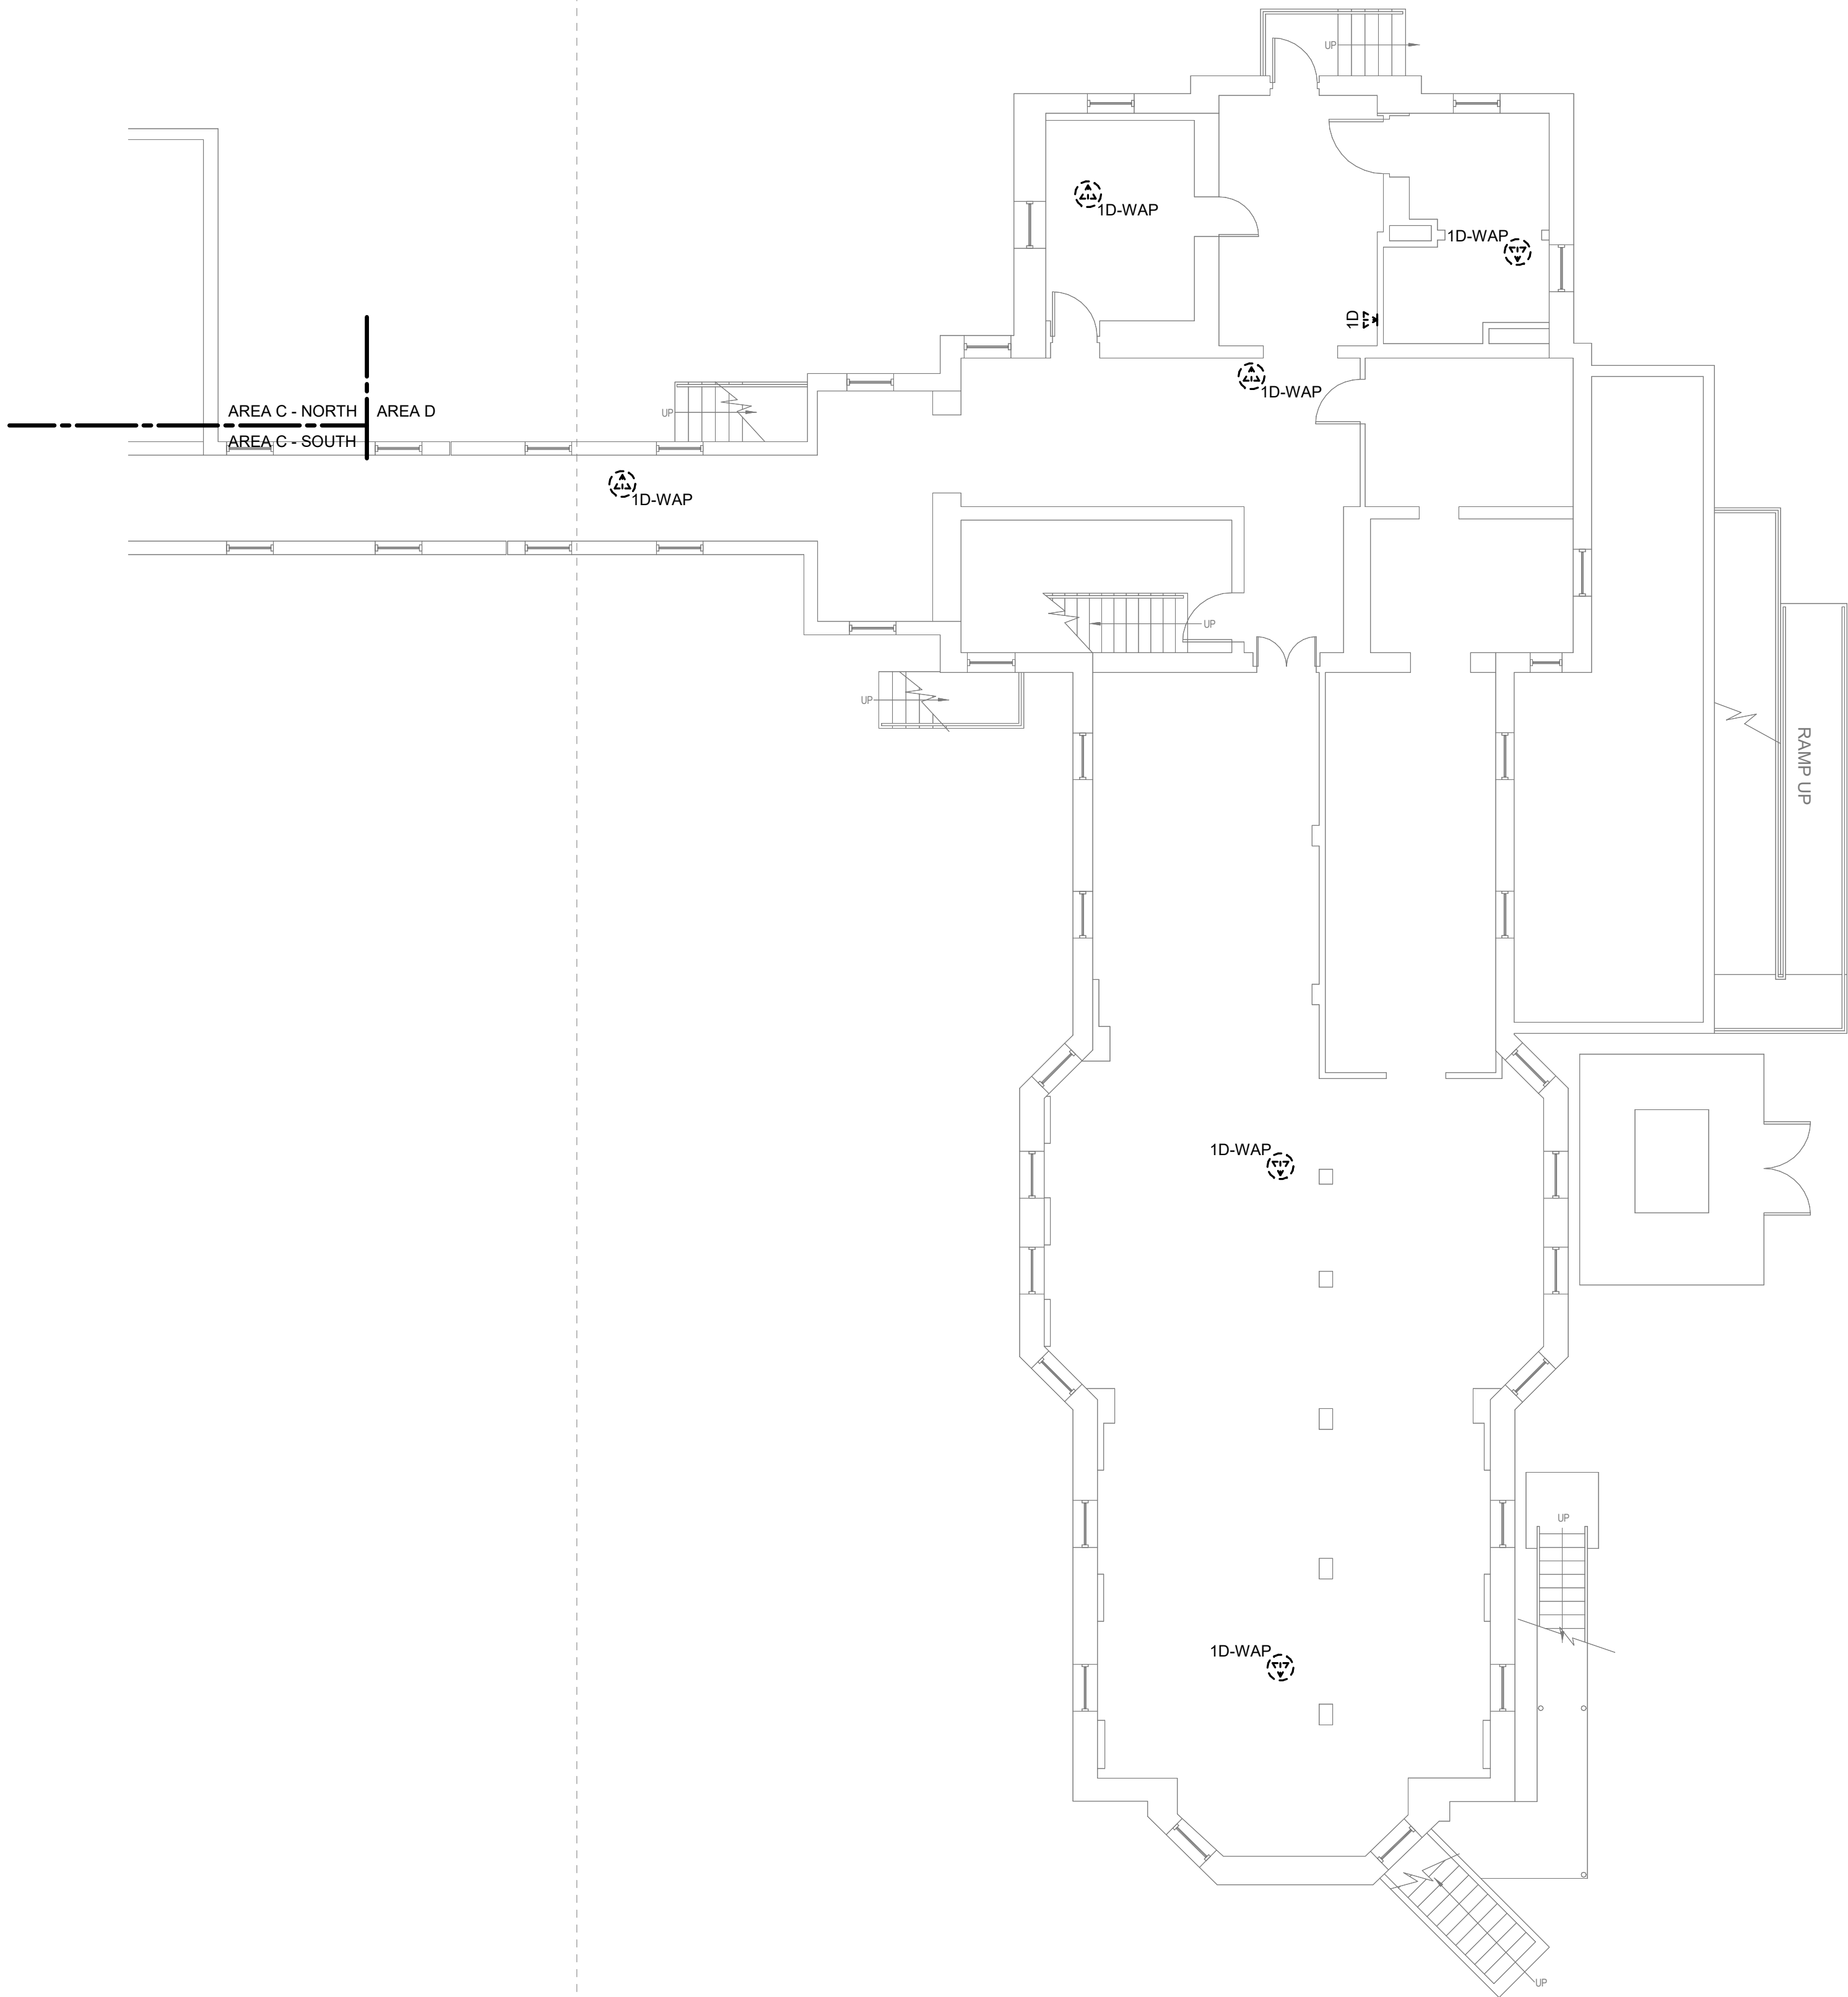

1 BUILDING 06 BASEMENT FLOOR DEMOLITION PLAN - TECHNOLOGY - AREA D
1/8" = 1'-0"

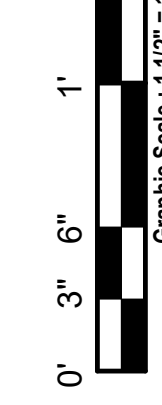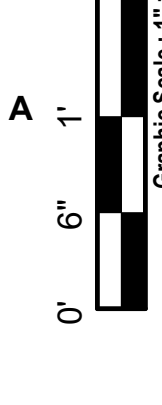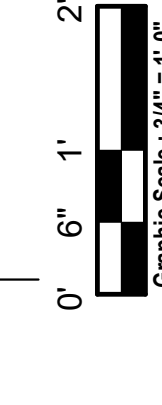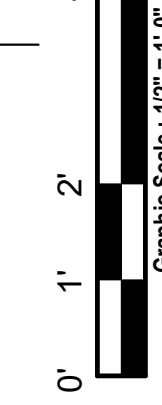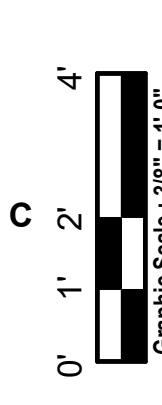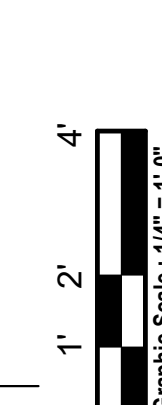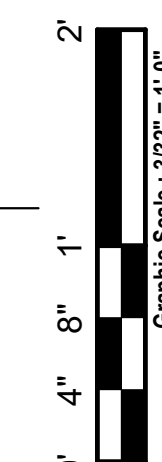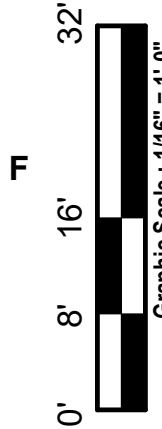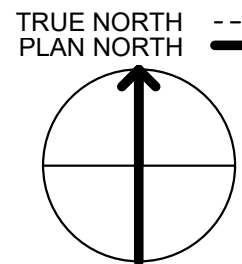

35% SCHEMATIC DESIGN SUBMISSION	5.17.21
65% DESIGN DEVELOPMENT SUBMISSION	6.15.21
65% DESIGN DEVELOPMENT RESUBMISSION	8.25.21
Revisions:	Date:

CONSULTANT

IMEG

15 SUNNEN DRIVE
SUITE 104
ST. LOUIS, MO 63143
P: 314.645.1132 F: 314.645.1173
PROJECT #18004375.03

ARCHITECT/ENGINEER OF RECORD

Romanyk Consulting
Focusing on what matters

Romanyk Consulting Corp. www.romanykconsulting.com
3308 Preston Road, Suite 350-164, Plano, Texas 75093

STAMP

Bicsi
DAVID LARSON
BICS1 ID # 106098
EXPIRES 12-31-25
REGISTERED COMMUNICATIONS DISTRIBUTION DESIGNER
RCDD

Office of
Construction
and Facilities
Management

VA U.S. Department
of Veterans Affairs

Drawing Title
BUILDING 06 BASEMENT DEMO PLAN -
TECHNOLOGY - AREA D

Approved:

Phase
FINAL BID DOCUMENTS

Sprinklered
FULLY SPRINKLERED

Project Title
EHRM INFRASTRUCTURE
UPGRADES - MILWAUKEE, WI

Location
5000 W. NATIONAL AVENUE, MILWAUKEE, WI

Issue Date
SEPTEMBER 05, 2025

Checked
PHINIE

Drawn
MAIBEJ

Project Number
695-21-700

Building Number
06

Drawing Number
06-TD100D

1. REMOVE ALL NETWORK CABLING TO POINTS OF TERMINATION IN ASSOCIATED DATA CLOSET. REFER TO FLOOR PLANS AND SHEET T1001 FOR TR ROOM LOCATIONS.
2. REFER TO ARCHITECTURAL PHASING PLANS FOR WHERE EXISTING CABLING IS ALLOWED TO BE DEMOLISHED.
3. FOR ALL EXISTING WIRELESS ACCESS POINTS AND SURVEILLANCE CAMERAS, DEVICES SHALL REMAIN. SCOPE OF WORK INCLUDES CABLE REPLACEMENT ONLY. COORDINATE WITH COR FOR ANY DOWNTIME OF DEVICES.
4. EXISTING LOCATIONS OF WORK AREA OUTLETS SHOWN ON THIS SHEET MAY NOT NECESSARILY BE IN THE EXACT LOCATION AS IDENTIFIED.



TRUE NORTH
PLAN NORTH



35% SCHEMATIC DESIGN SUBMISSION	5.17.21
65% DESIGN DEVELOPMENT SUBMISSION	6.15.21
65% DESIGN DEVELOPMENT RESUBMISSION	8.25.21
Revisions:	Date:



The FUTURE. Built Smarter www.jmegcorp.com
15 SUNNEN DRIVE
SUITE 104
ST. LOUIS, MO 63143
P: 314.645.1132 F: 314.645.1173
PROJECT #18004375.03



Romanyk Consulting

Focusing on what matters

Romanyk Consulting Corp. www.romanykconsulting.com
3308 Preston Road, Suite 350-164, Plano, Texas 75093

VAU.S. Department
of Veterans Affairs

Approved:

Sprinklered	FULLY SPRINKLERED
-------------	-------------------

Location	5000 W. NATIONAL AVENUE MILWAUKEE, WI
-----------------	---------------------------------------

Location	5000 W. NATIONAL AVENUE MILWAUKEE, WI
-----------------	---------------------------------------

Issue Date
SEPTEMBER 05, 2025

Checked
PHINIE


Drawn
MAIBEJ

Building Number	06
-----------------	----

Drawing Number
06-TD101A

SHEET NOTES:

1. REMOVE ALL NETWORK CABLING TO POINTS OF TERMINATION IN ASSOCIATED DATA CLOSET. REFER TO FLOOR PLANS AND SHEET T1001 FOR TR ROOM LOCATIONS.
2. REFER TO ARCHITECTURAL PHASING PLANS FOR WHEN EXISTING CABLING IS ALLOWED TO BE REMOVED.
3. FOR ALL EXISTING WIRELESS ACCESS POINTS AND SURVEILLANCE CAMERAS, DEVICES SHALL REMAIN. SCOPE OF WORK INCLUDES CABLE REPLACEMENT ONLY. COORDINATE WITH COR FOR ANY DOWNTIME OF DEVICES.
4. EXISTING LOCATIONS OF WORK AREA OUTLETS SHOWN ON THIS SHEET MAY NOT NECESSARILY BE IN THE EXACT LOCATION AS IDENTIFIED.

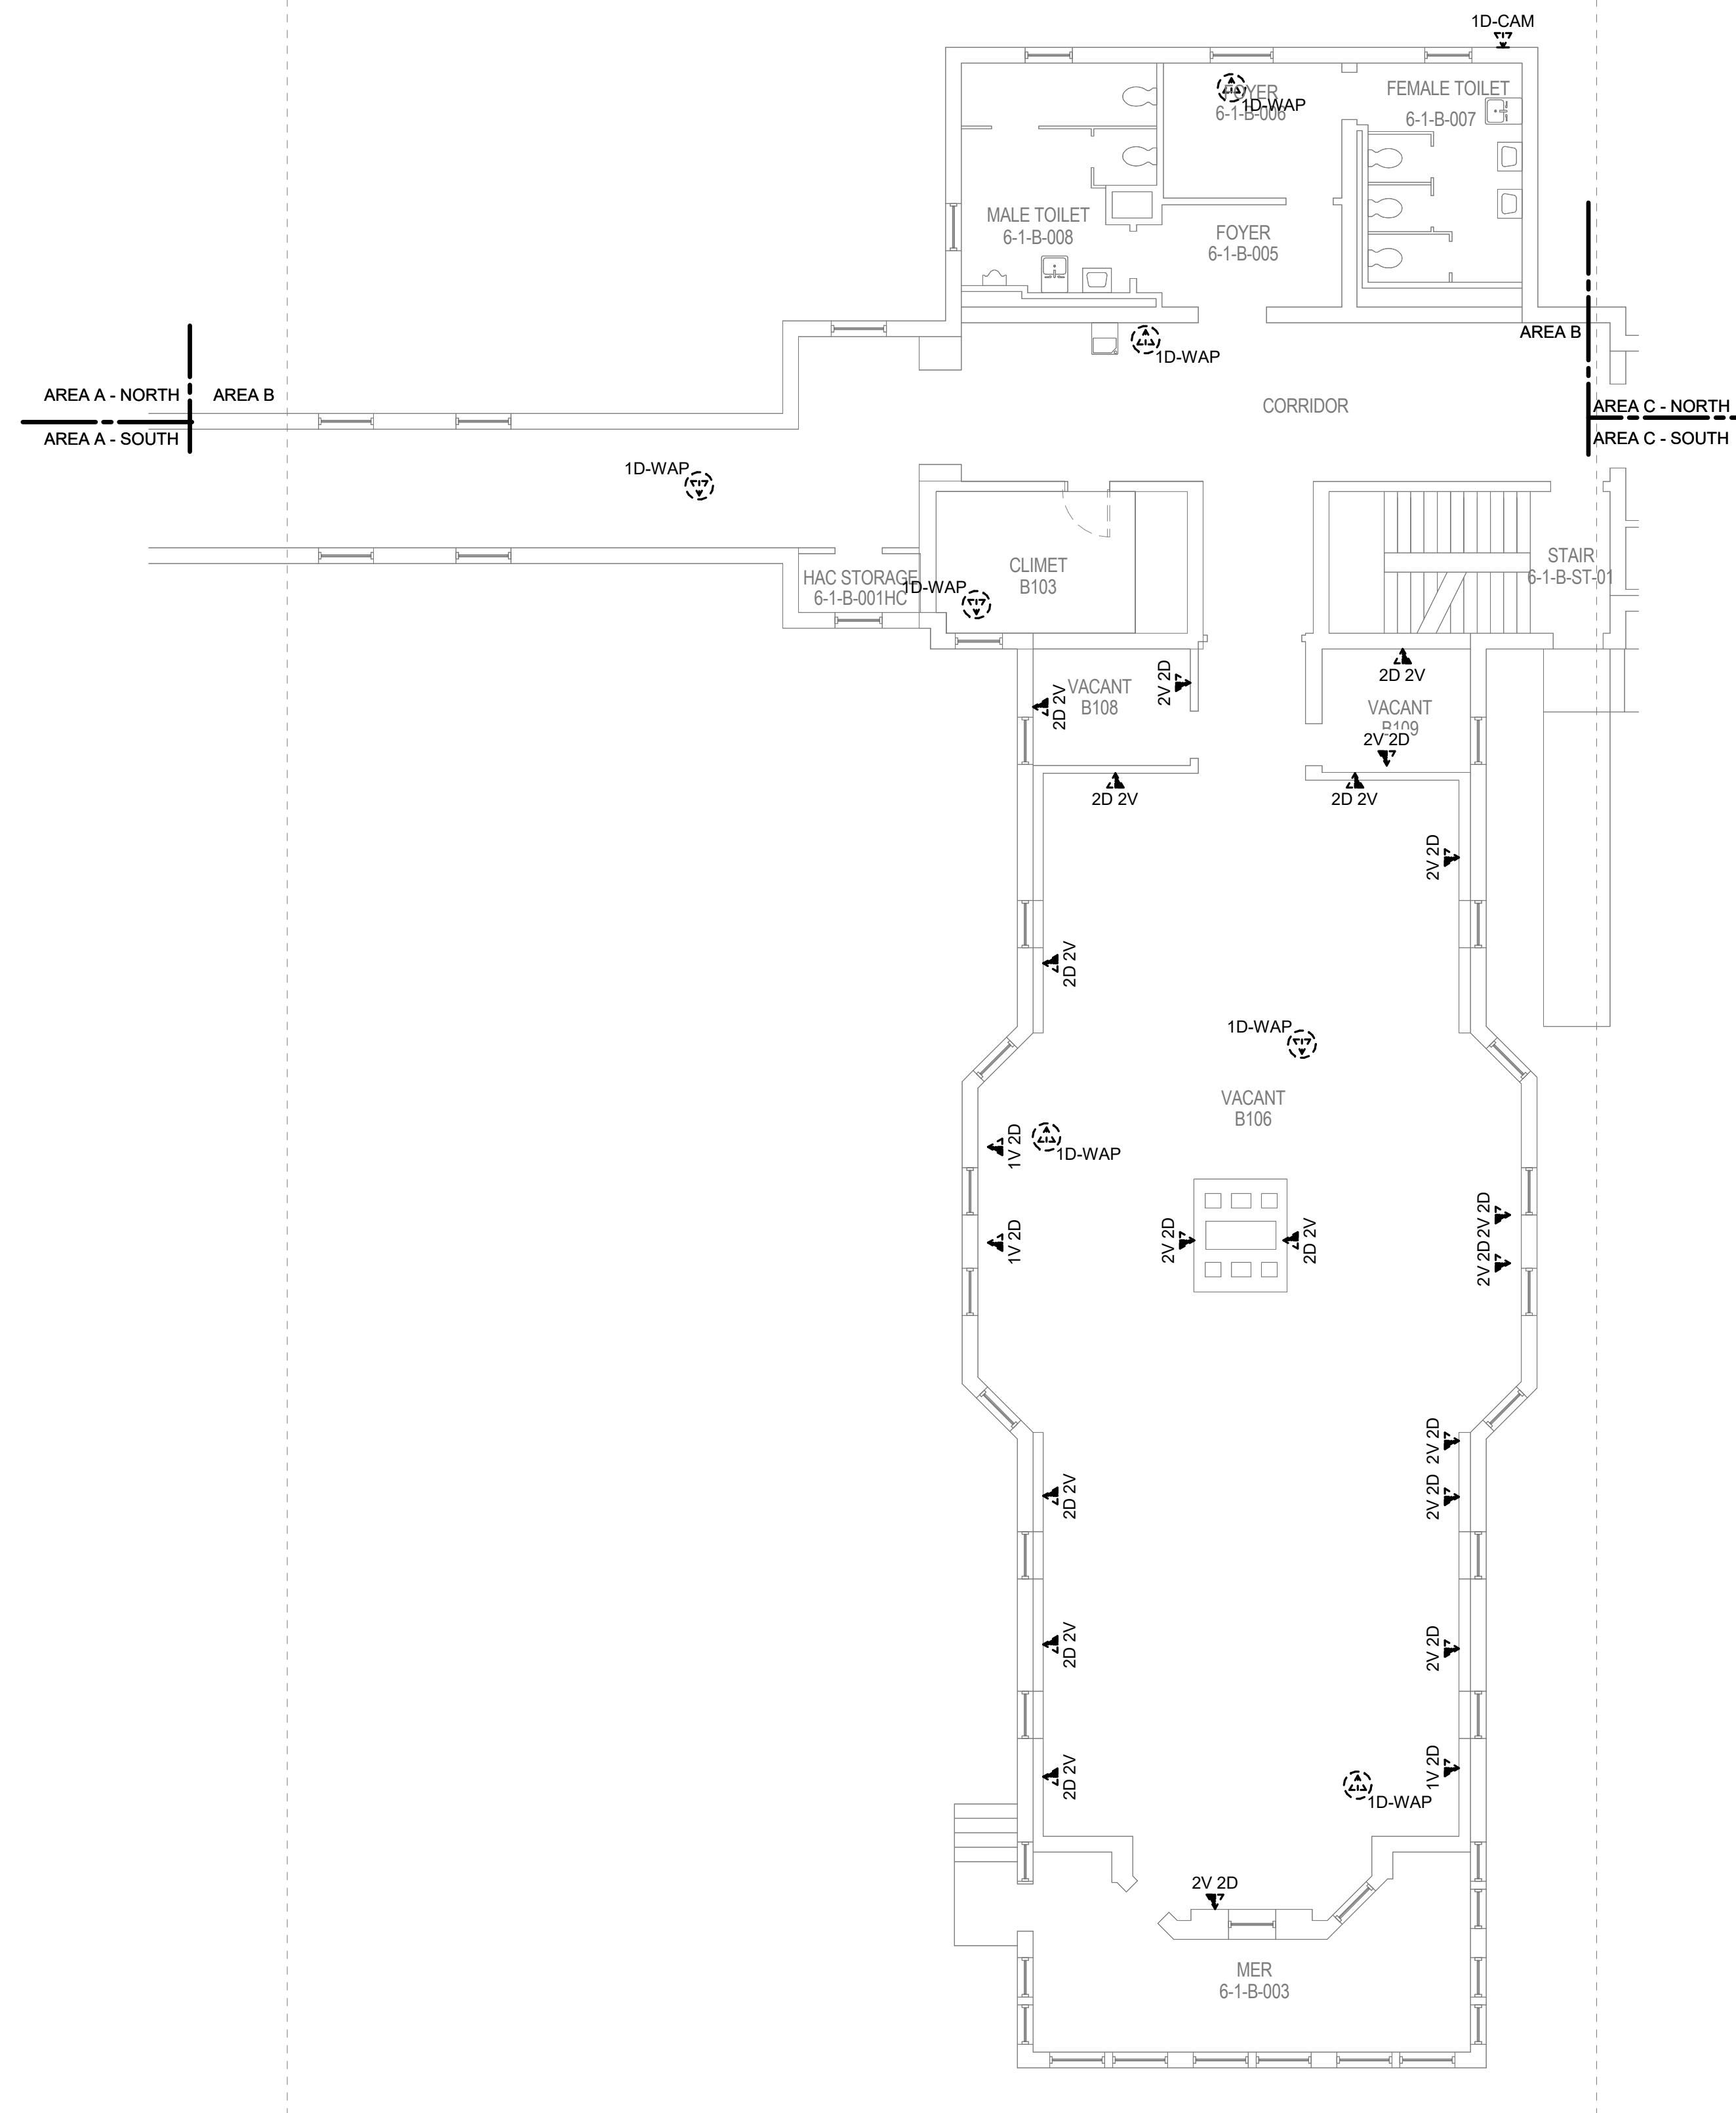

1 BUILDING 06 FIRST FLOOR DEMOLITION PLAN - TECHNOLOGY - AREA B
1/8" = 1'-0"

35% SCHEMATIC DESIGN SUBMISSION	5.17.21
65% DESIGN DEVELOPMENT SUBMISSION	6.15.21
65% DESIGN DEVELOPMENT RESUBMISSION	8.25.21
Revisions:	Date:

CONSULTANT

 **IMEG**

The Future. Built Smarter. www.imegcorp.com

15 SUNSHINE DRIVE
SUITE 104
ST. LOUIS, MO 63143
P: 314.645.1132 F: 314.645.1173
PROJECT #18004375.03

ARCHITECT/ENGINEER OF RECORD

 **Romanyk Consulting**
Focusing on what matters
 Romanyk Consulting Corp. www.romanykconsulting.com
 3308 Preston Road, Suite 350-164, Plano, Texas 75093

Office of
Construction
and Facilities
Management

VA U.S. Department
of Veterans Affairs

Drawing Title BUILDING 06 FIRST FLOOR DEMO PLAN - TECHNOLOGY - AREA B
Approved:
S

Phase	FINAL BID DOCUMENTS
Sprinklered	FULLY SPRINKLERED

Project Title EHRM INFRASTRUCTURE UPGRADES - MILWAUKEE, WI		
Location 5000 W. NATIONAL AVENUE MILWAUKEE, WI		
Issue Date SEPTEMBER 05, 2025	Checked PHINIE	Drawn MAIBEJ

Project Number 695-21-700
Building Number 06
Drawing Number 06-TD101B

F

E

D

C

B

A

9/2/2025 3:54:57 PM

Autodesk Docs\DCFM East - Milwaukee EHRM (R24)T24_1804375.03_VA MilWEHRM_C.dwt

A

B

C

D

E

F

A

Autodesk Docs\DCFM East - Milwaukee EHRM (R24)T24_1804375.03_VA MilWEHRM_C.dwt

10

9

8

7

6


5

4


3

2

1

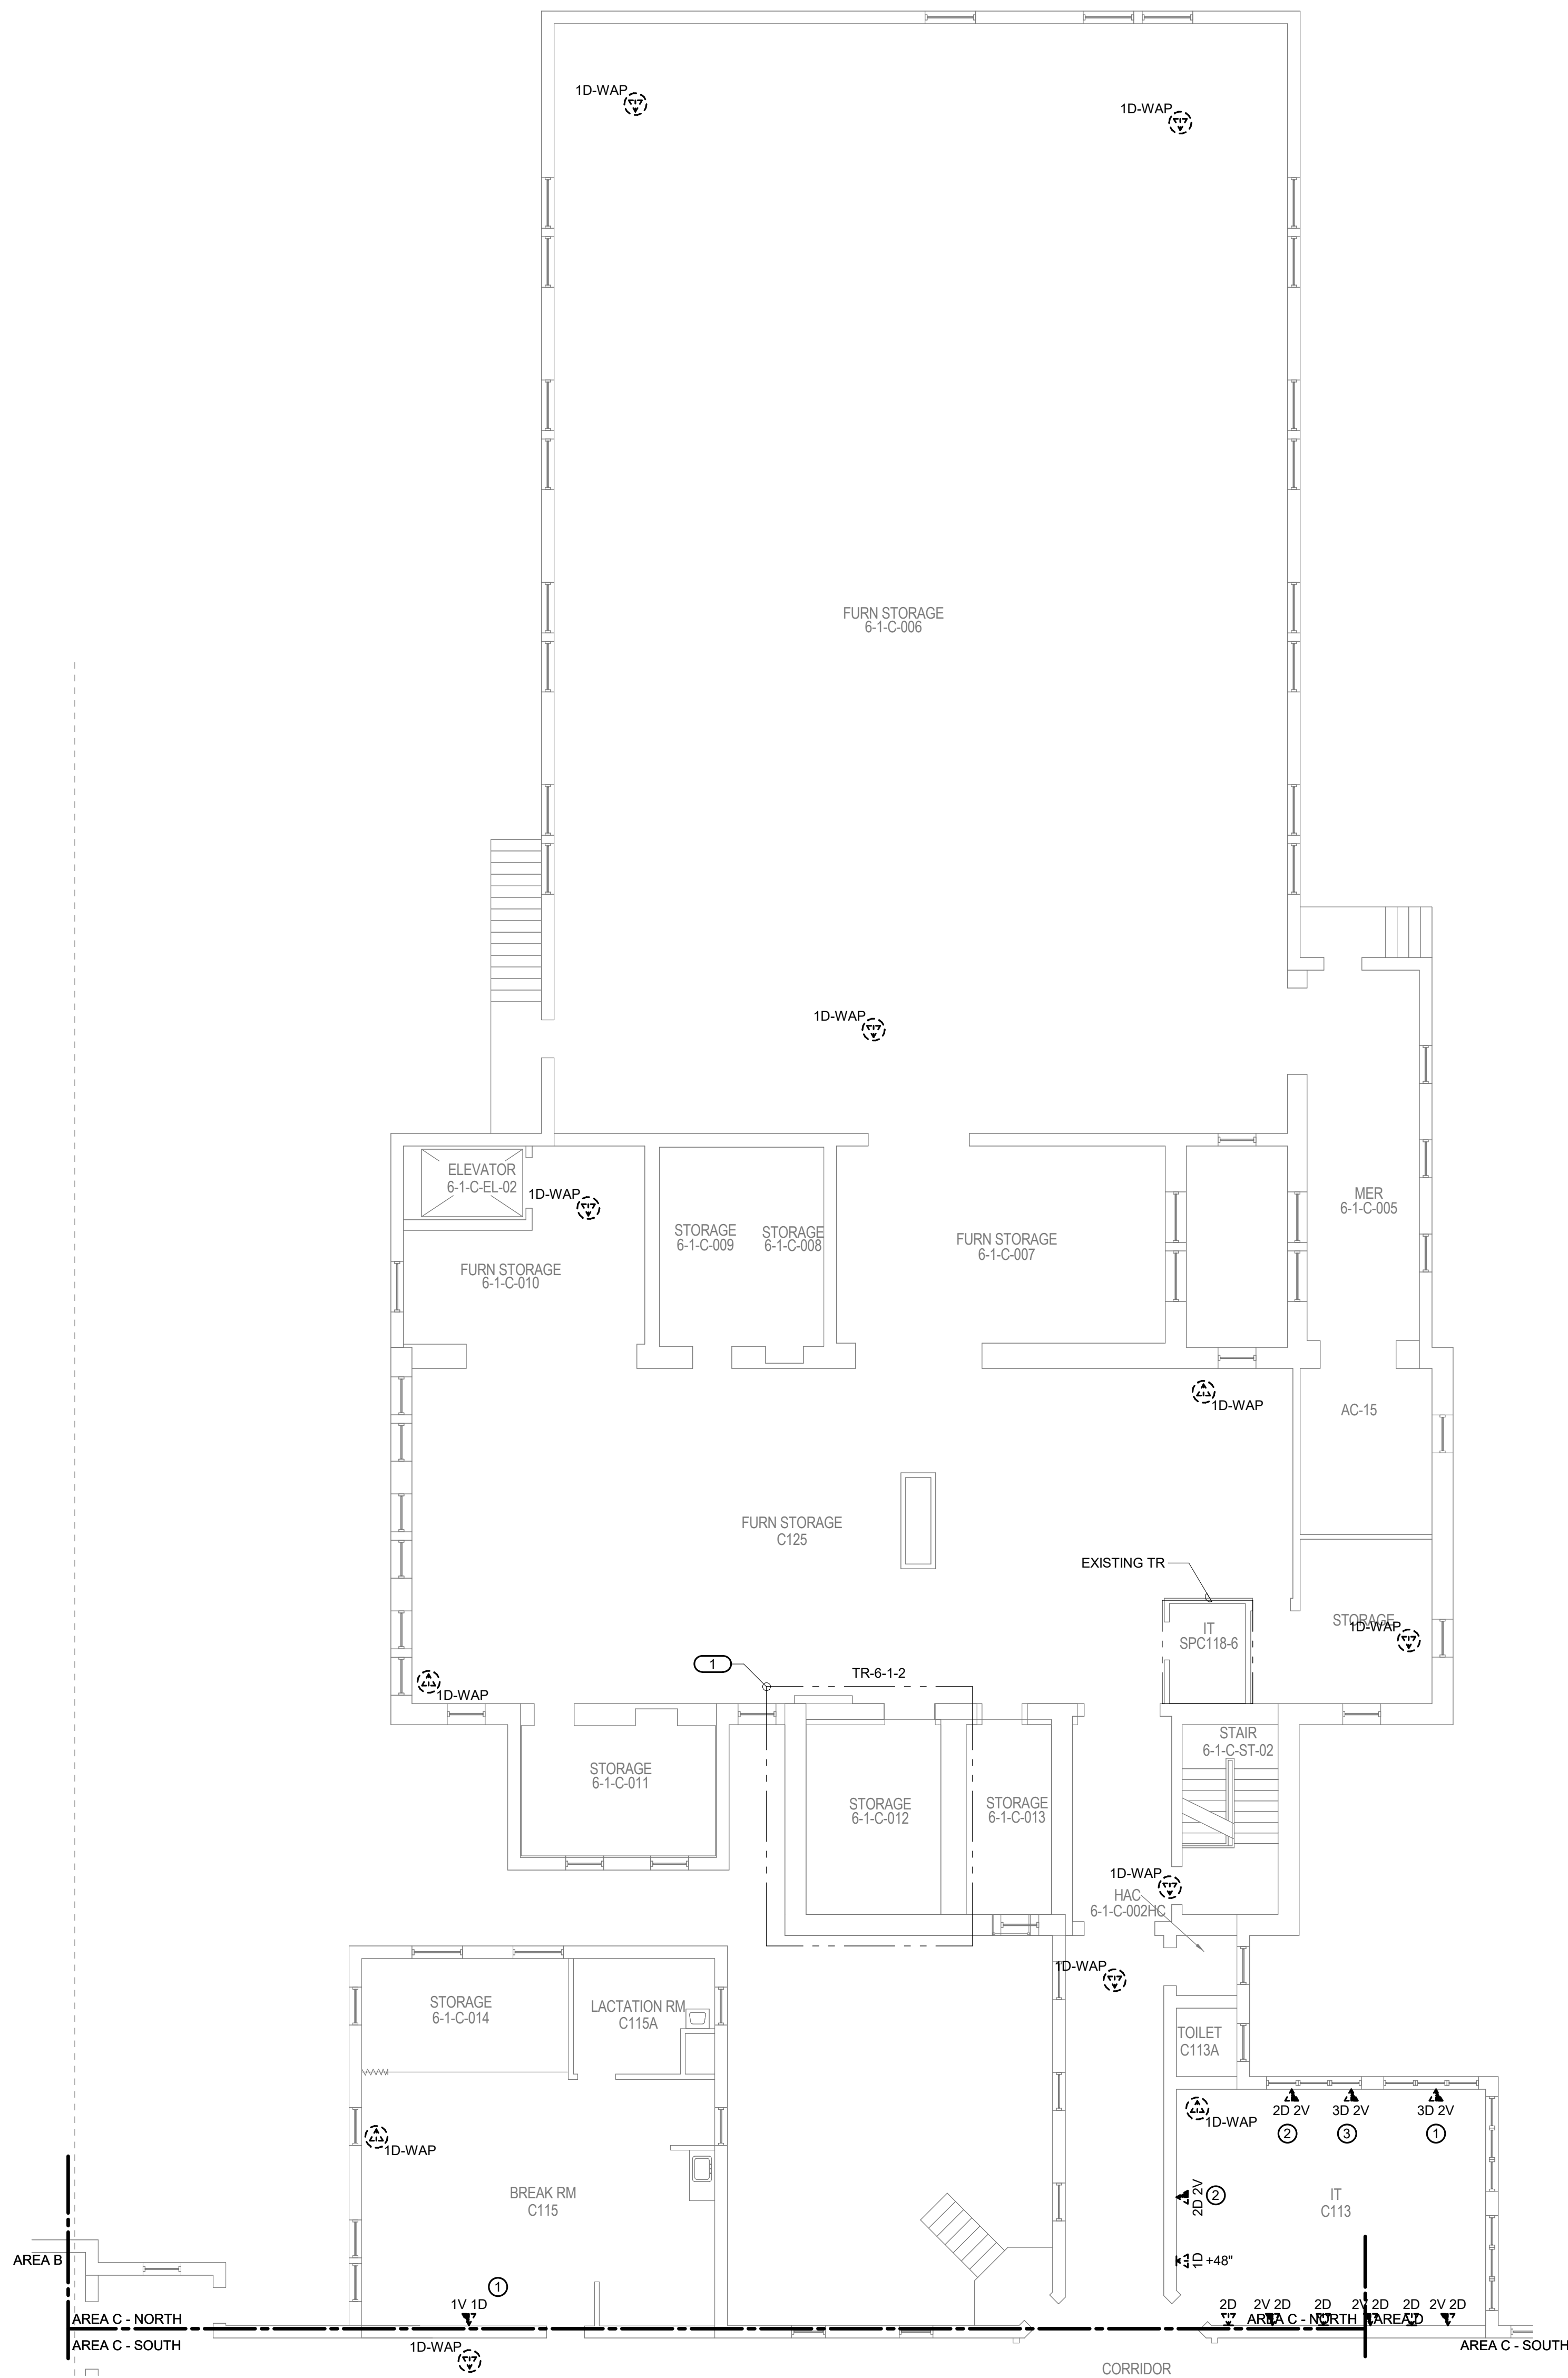

1 BUILDING 06 FIRST FLOOR DEMOLITION PLAN - TECHNOLOGY - AREA C NORTH
1/8" = 1'-0"

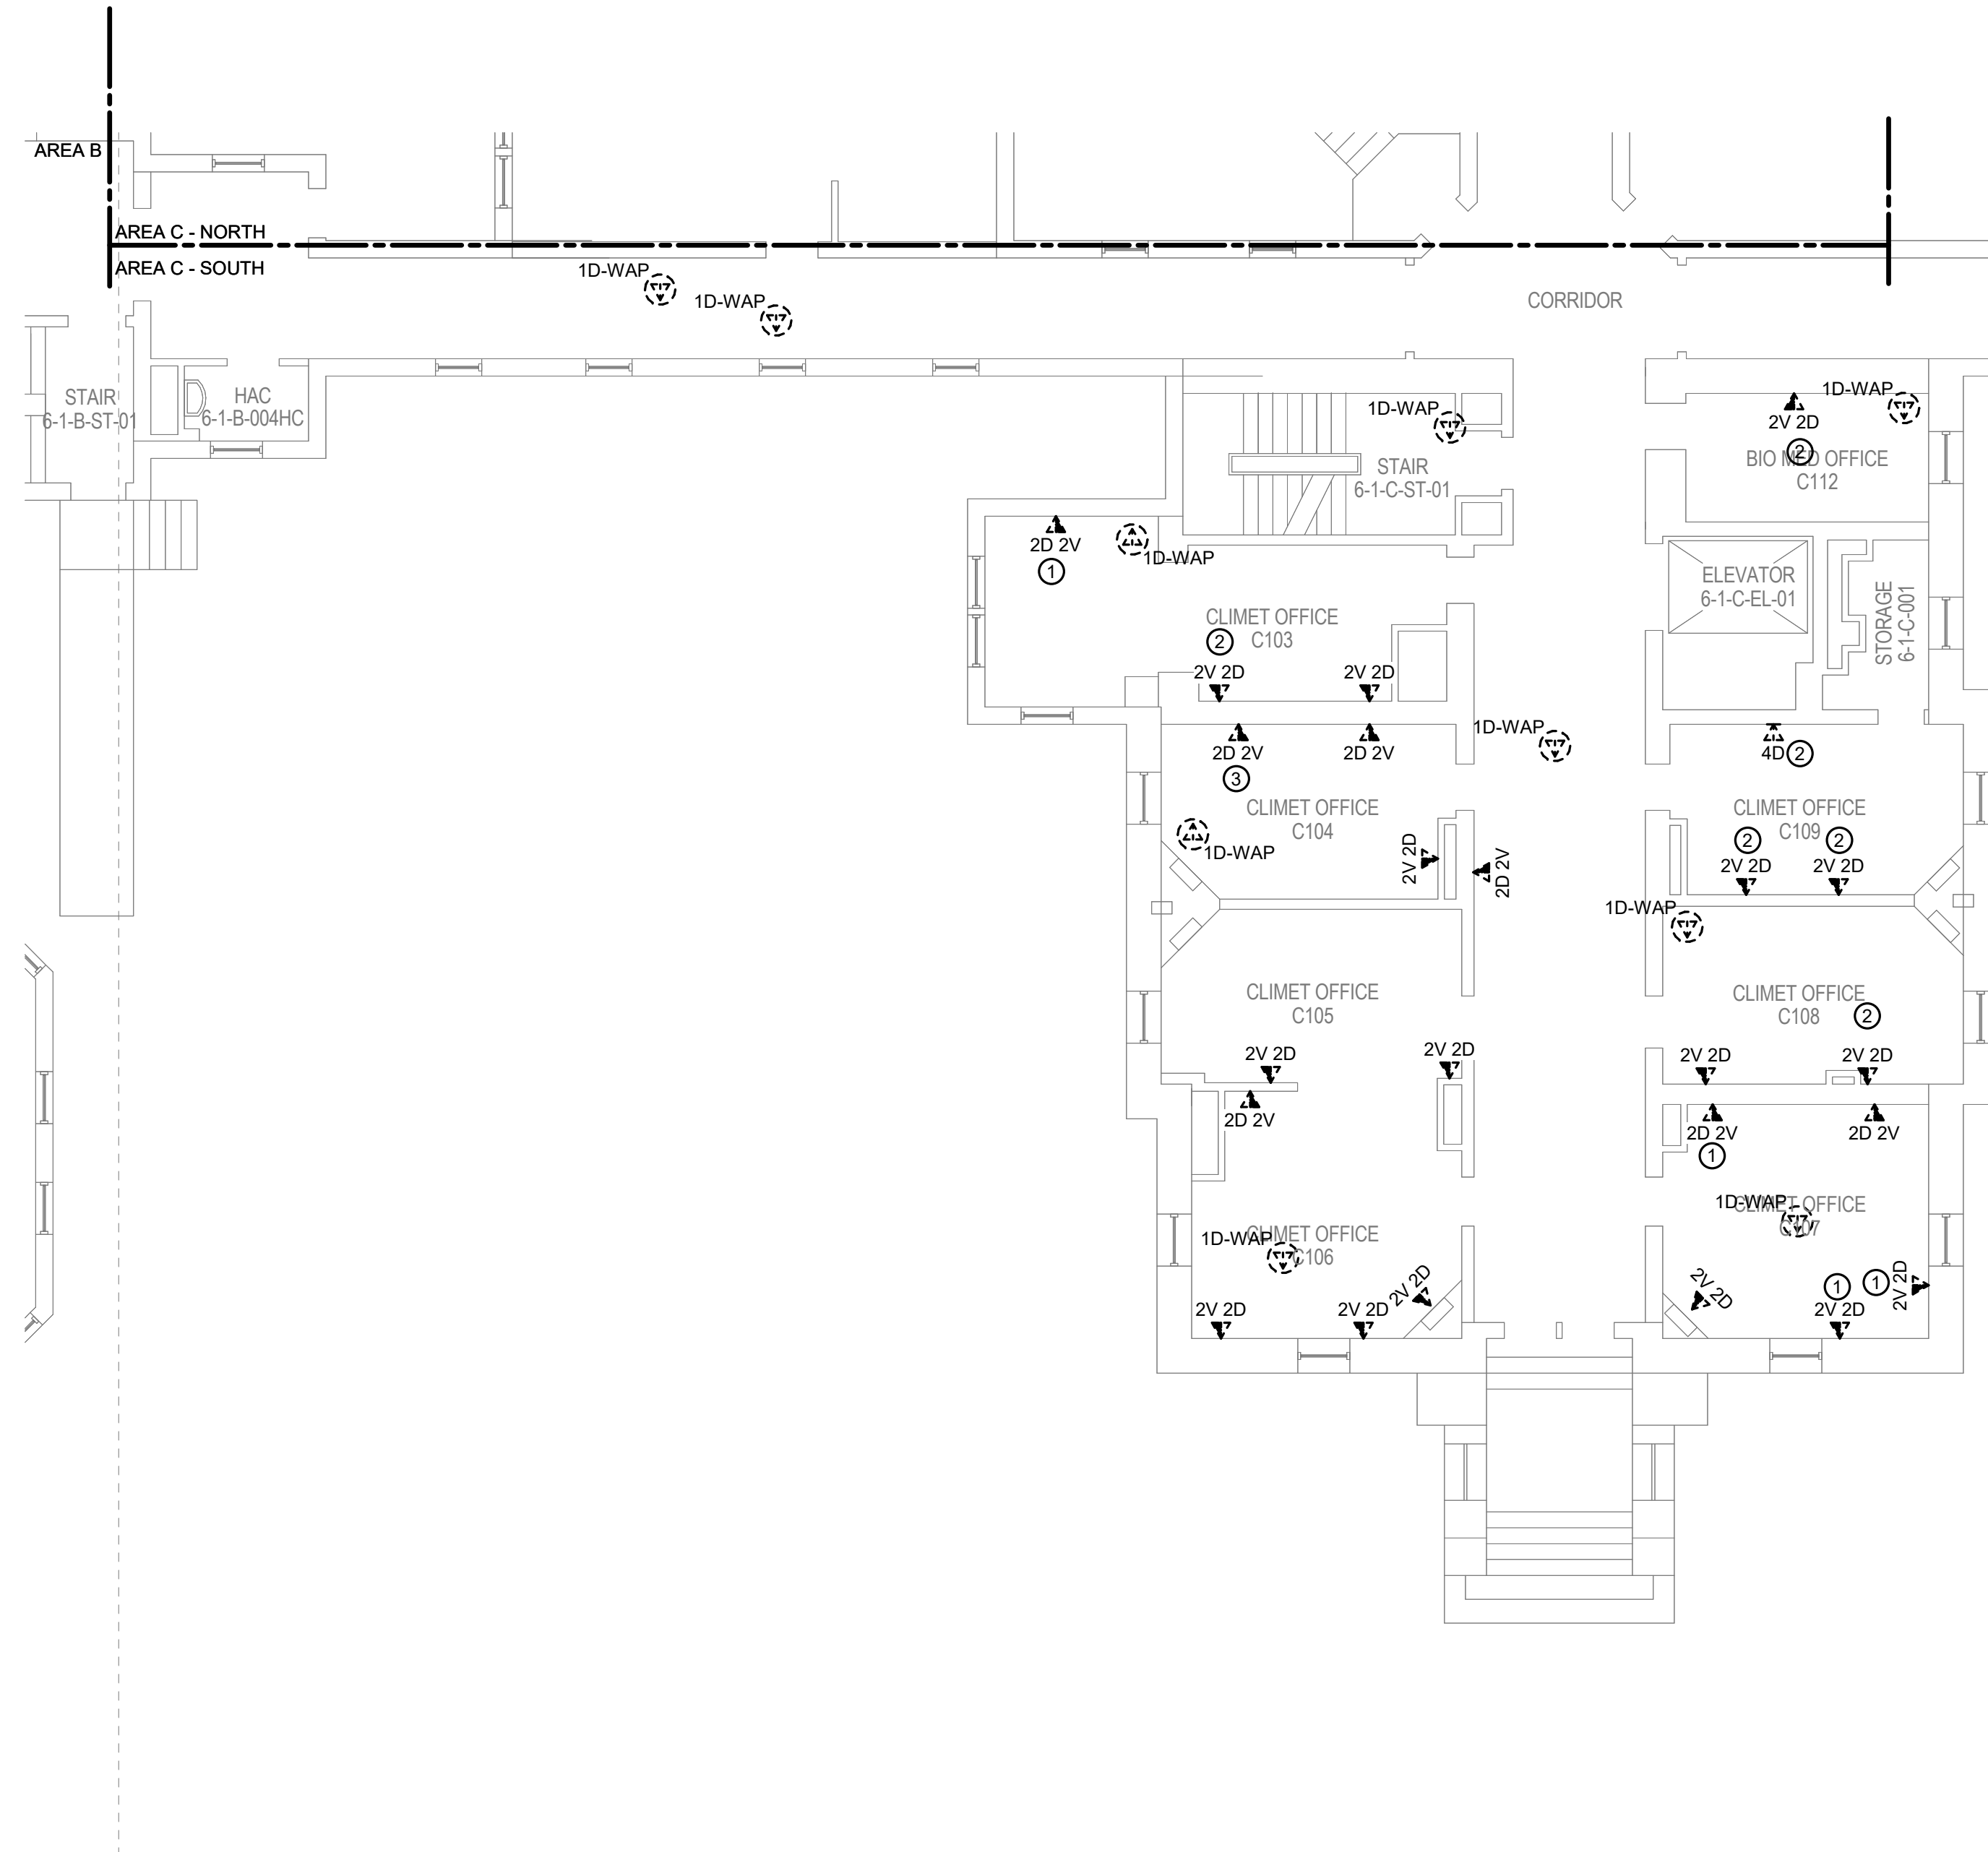

2 BUILDING 06 FIRST FLOOR DEMOLITION PLAN - TECHNOLOGY - AREA C SOUTH
1/8" = 1'-0"

- SHEET NOTES:**
1. REMOVE ALL NETWORK CABLING TO POINTS OF TERMINATION IN ASSOCIATED DATA CLOSET. REFER TO FLOOR PLANS AND SHEET T1001 FOR TR ROOM LOCATIONS.
 2. REFER TO ARCHITECTURAL PHASING PLANS FOR WHEN EXISTING CABLING IS ALLOWED TO BE DEMOLISHED.
 3. FOR ALL EXISTING WIRELESS ACCESS POINTS AND SURVEILLANCE CAMERAS, DEVICES SHALL REMAIN. SCOPE OF WORK INCLUDES CABLE REPLACEMENT ONLY. COORDINATE WITH COR FOR ANY DOWNTIME OF DEVICES. EXISTING LOCATIONS OF WORK AREA, OUTLETS SHOWN ON THIS SHEET MAY NOT NECESSARILY BE IN THE EXACT LOCATION AS IDENTIFIED.
- KEYNOTES:**
1. ASBESTOS ABATEMENT TO TAKE PLACE IN THESE TWO (2) ROOMS. REFER TO ARCHITECTURAL PLANS AND SPECIFICATIONS.

Graphic Scale: 1/16" = 1'-0"

Graphic Scale: 1/8" = 1'-0"

Graphic Scale: 3/32" = 1'-0"

Graphic Scale: 1/4" = 1'-0"


Graphic Scale: 3/8" = 1'-0"

Graphic Scale: 1/2" = 1'-0"

Graphic Scale: 3/4" = 1'-0"

Graphic Scale: 1" = 1'-0"

Graphic Scale: 1 1/2" = 1'-0"

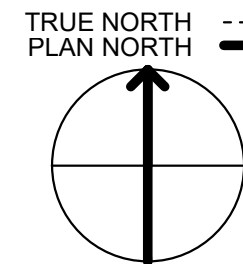

35% SCHEMATIC DESIGN SUBMISSION	5.17.21
65% DESIGN DEVELOPMENT SUBMISSION	6.15.21
65% DESIGN DEVELOPMENT RESUBMISSION	8.25.21
Revisions:	Date:

CONSULTANT

IMEG

15 SUNNEN DRIVE
SUITE 104
ST. LOUIS, MO 63143
P: 314.645.1132 F: 314.645.1173
PROJECT #18004375.03

ARCHITECT/ENGINEER OF RECORD

Romanyk Consulting
Focusing on what matters

Romanyk Consulting Corp. www.romanykconsulting.com
3308 Preston Road, Suite 350-164, Plano, Texas 75093

STAMP

Bicsi
DAVID LARSON
BICS1 ID # 106098
EXPIRES 12-31-25

Office of
Construction
and Facilities
Management

VA U.S. Department
of Veterans Affairs

Drawing Title
BUILDING 06 FIRST FLOOR DEMO PLAN -
TECHNOLOGY - AREA C

Approved:

Phase
FINAL BID DOCUMENTS

Sprinklered
FULLY SPRINKLERED

Project Title
EHRM INFRASTRUCTURE
UPGRADES - MILWAUKEE, WI

Location
5000 W. NATIONAL AVENUE, MILWAUKEE, WI

Issue Date
SEPTEMBER 05, 2025

Checked
PHINE

Drawn
MAIBEJ


Project Number
695-21-700

Building Number
06

Drawing Number
06-TD101C

SHEET NOTES:

1. REMOVE ALL NETWORK CABLING TO POINTS OF TERMINATION IN ASSOCIATED DATA CLOSET. REFER TO FLOOR PLANS AND SHEET T1001 FOR TR ROOM LOCATIONS.
2. REFER TO ARCHITECTURAL PHASING PLANS FOR WHEN EXISTING CABLING IS ALLOWED TO BE REMOVED.
3. FOR ALL EXISTING WIRELESS ACCESS POINTS AND SURVEILLANCE CAMERAS, DEVICES SHALL REMAIN. SCOPE OF WORK INCLUDES CABLE REPLACEMENT ONLY. COORDINATE WITH COR FOR ANY DOWNTIME OF DEVICES.
4. EXISTING LOCATIONS OF WORK AREA OUTLETS SHOWN ON THIS SHEET MAY NOT NECESSARILY BE IN THE EXACT LOCATION AS IDENTIFIED.

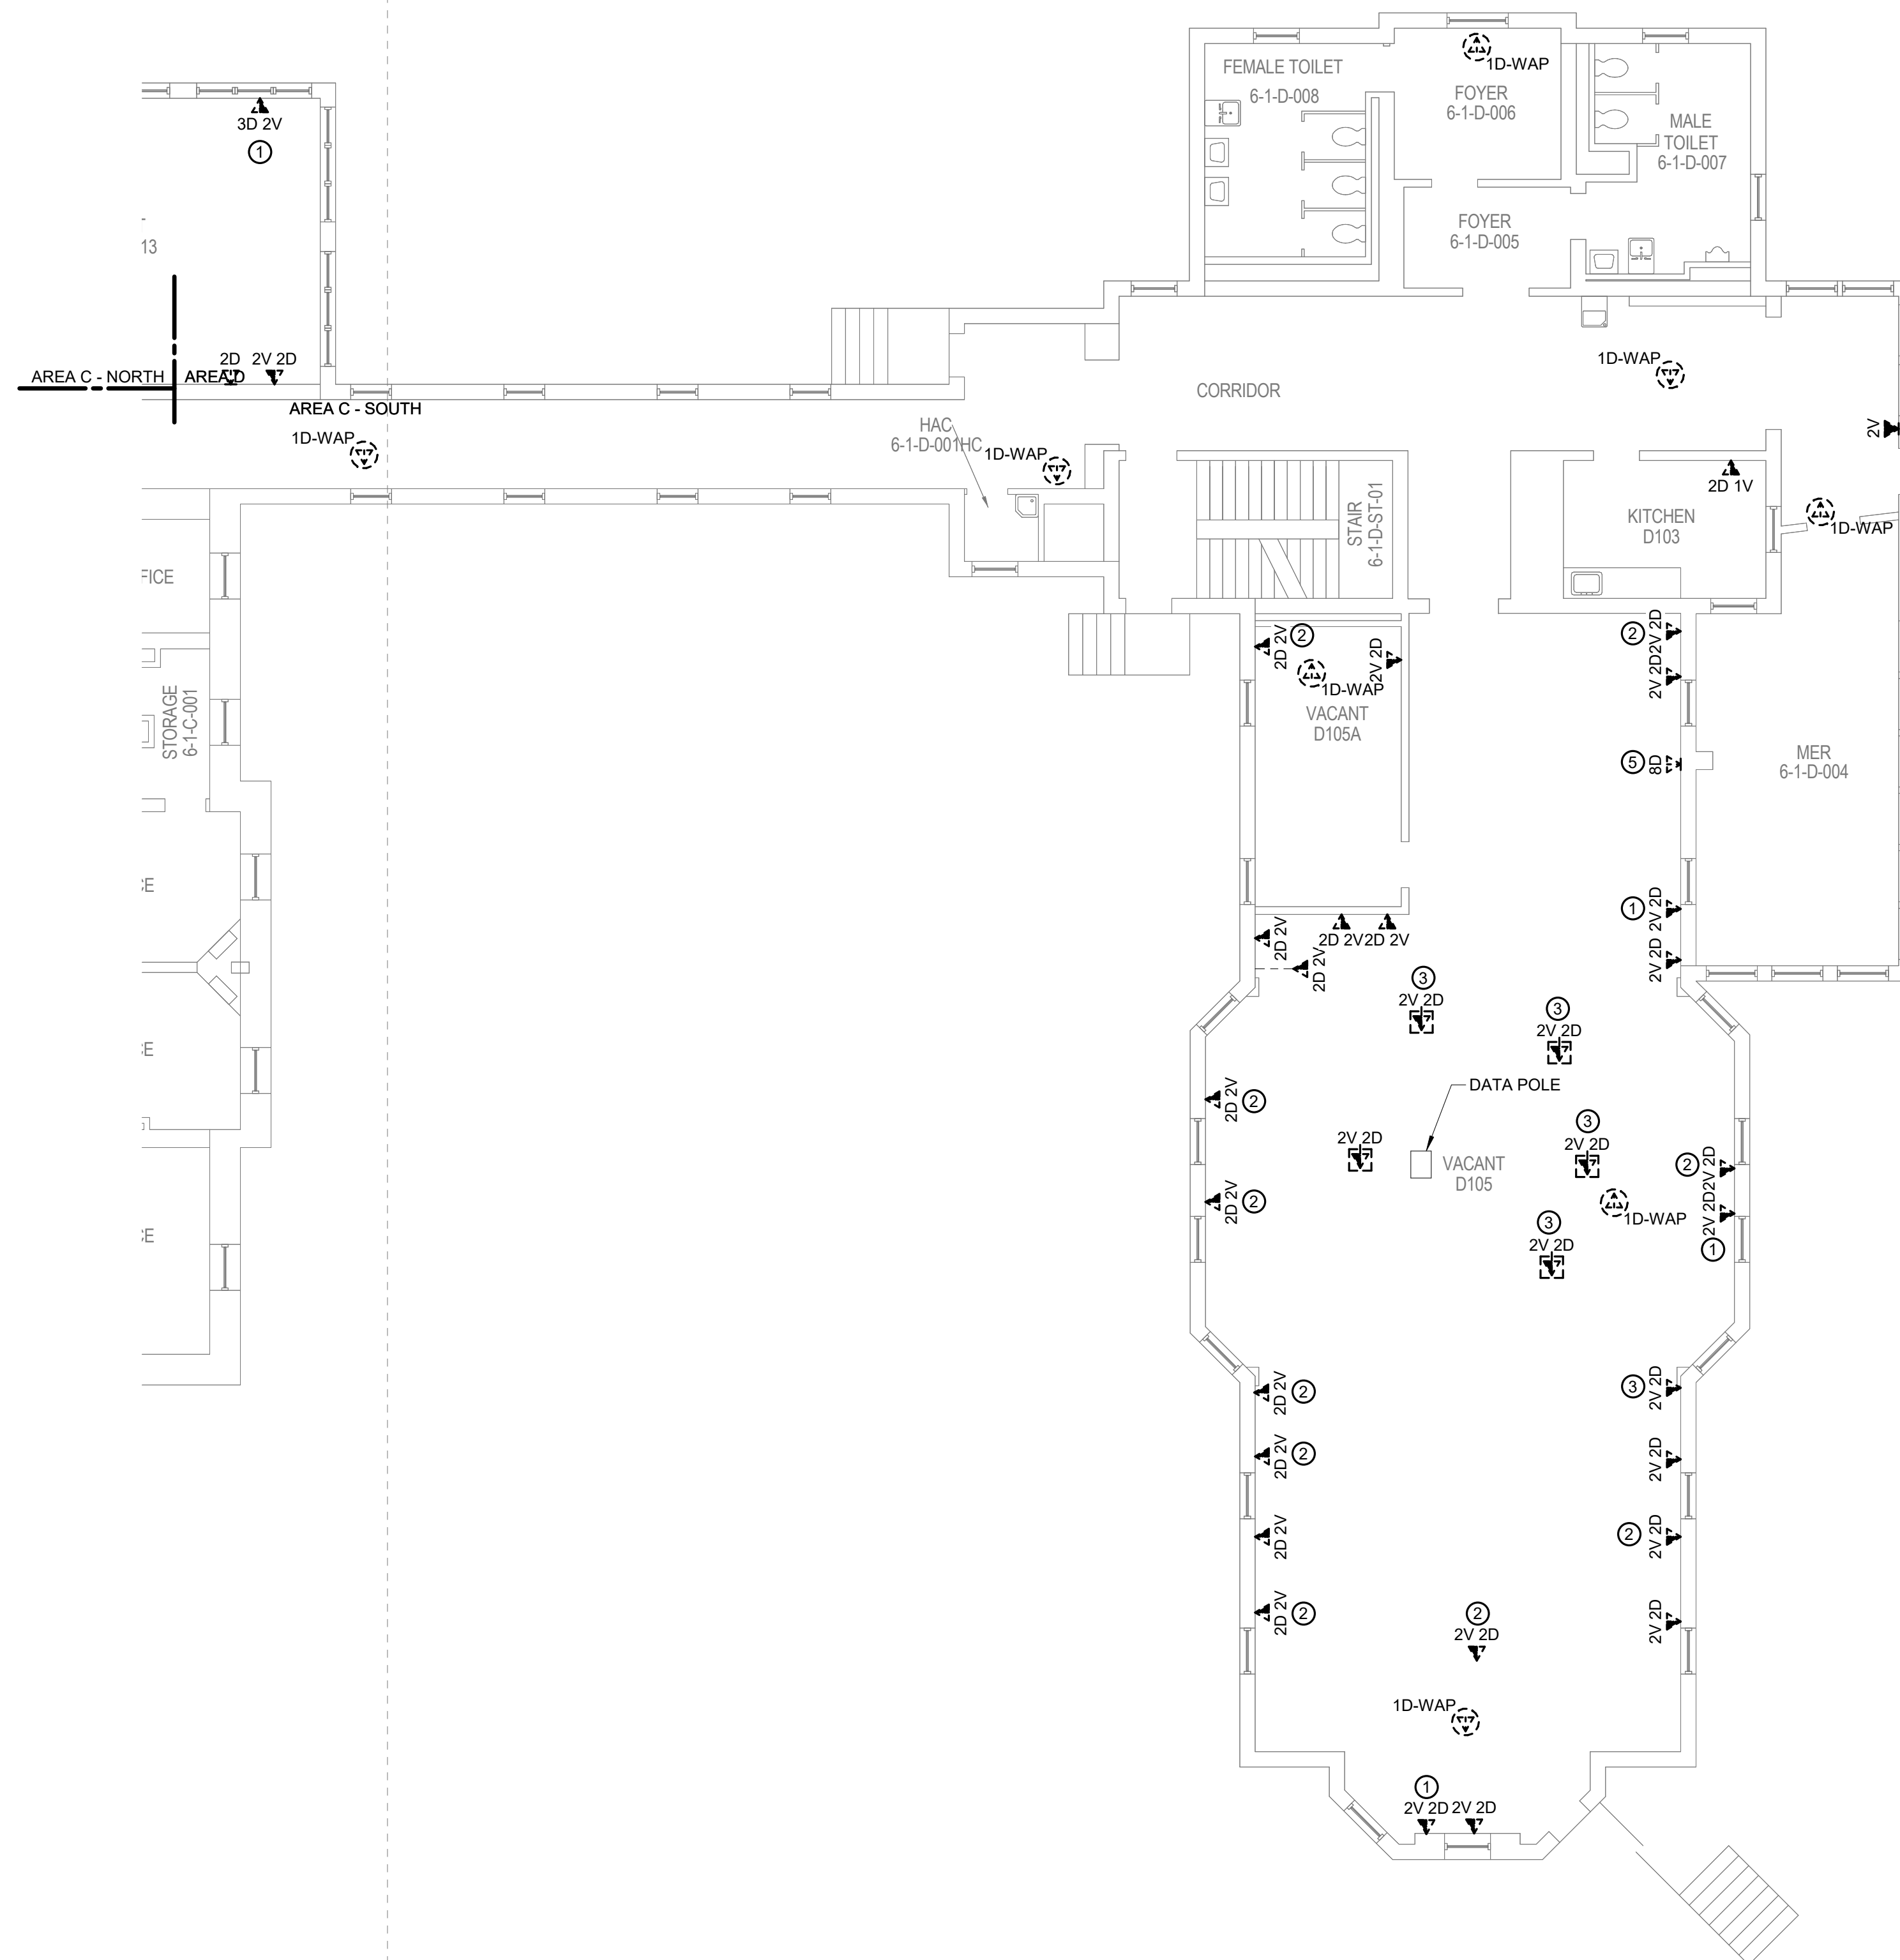

1 BUILDING 06 FIRST FLOOR DEMOLITION PLAN - TECHNOLOGY - AREA D
1/8" = 1'-0"

TRUE NORTH
PLAN NORTH



35% SCHEMATIC DESIGN SUBMISSION	5.17.21
65% DESIGN DEVELOPMENT SUBMISSION	6.15.21
65% DESIGN DEVELOPMENT RESUBMISSION	8.25.21
Revisions:	Date:

CONSULTANT

 **IMEG**

The Future Built Smarter www.imegcorp.com

15 SUNNEN DRIVE
SUITE 104
ST. LOUIS, MO 63143
P: 314.645.1132 F: 314.645.1173
PROJECT #18004375.03

ARCHITECT/ENGINEER OF RECORD

 **Romanyk Consulting**
 Focusing on what matters

Romanyk Consulting Corp. www.romanykconsulting.com
 3308 Preston Road, Suite 350-164, Plano, Texas 75093

Office of
Construction
and Facilities
Management

VA U.S. Department
of Veterans Affairs

Drawing Title BUILDING 06 FIRST FLOOR DEMO PLAN - TECHNOLOGY - AREA D
Approved:
S

Phase	FINAL BID DOCUMENTS
Sprinklered	FULLY SPRINKLERED

Project Title EHRM INFRASTRUCTURE UPGRADES - MILWAUKEE, WI		
Location 5000 W. NATIONAL AVENUE MILWAUKEE, WI		
Issue Date SEPTEMBER 05, 2025	Checked PHINIE	Drawn MAIBEJ

Project Number 695-21-700
Building Number 06
Drawing Number 06-TD101D

F

E

D

C


B

A


9/2/2025 3:55:01 PM

Autodesk Docs\DOCFM East - Milwaukee EHRM (R24)T24_1804375\03_VA Milwaukee_C.dwt

- SHEET NOTES:**
1. REMOVE ALL NETWORK CABLING TO POINTS OF TERMINATION IN ASSOCIATED DATA CLOSET. REFER TO FLOOR PLANS AND SHEET T1001 FOR TR ROOM LOCATIONS.
 2. REFER TO ARCHITECTURAL PHASING PLANS FOR WHEN EXISTING CABLING IS ALLOWED TO BE DEMOLISHED.
 3. FOR ALL EXISTING WIRELESS ACCESS POINTS AND SURVEILLANCE CAMERAS, DEVICES SHALL REMAIN. SCOPE OF WORK INCLUDES CABLE REPLACEMENT ONLY. COORDINATE WITH COR FOR ANY DOWNTIME OF DEVICES. EXISTING LOCATIONS OF WORK AREA OUTLETS SHOWN ON THIS SHEET MAY NOT NECESSARILY BE IN THE EXACT LOCATION AS IDENTIFIED.

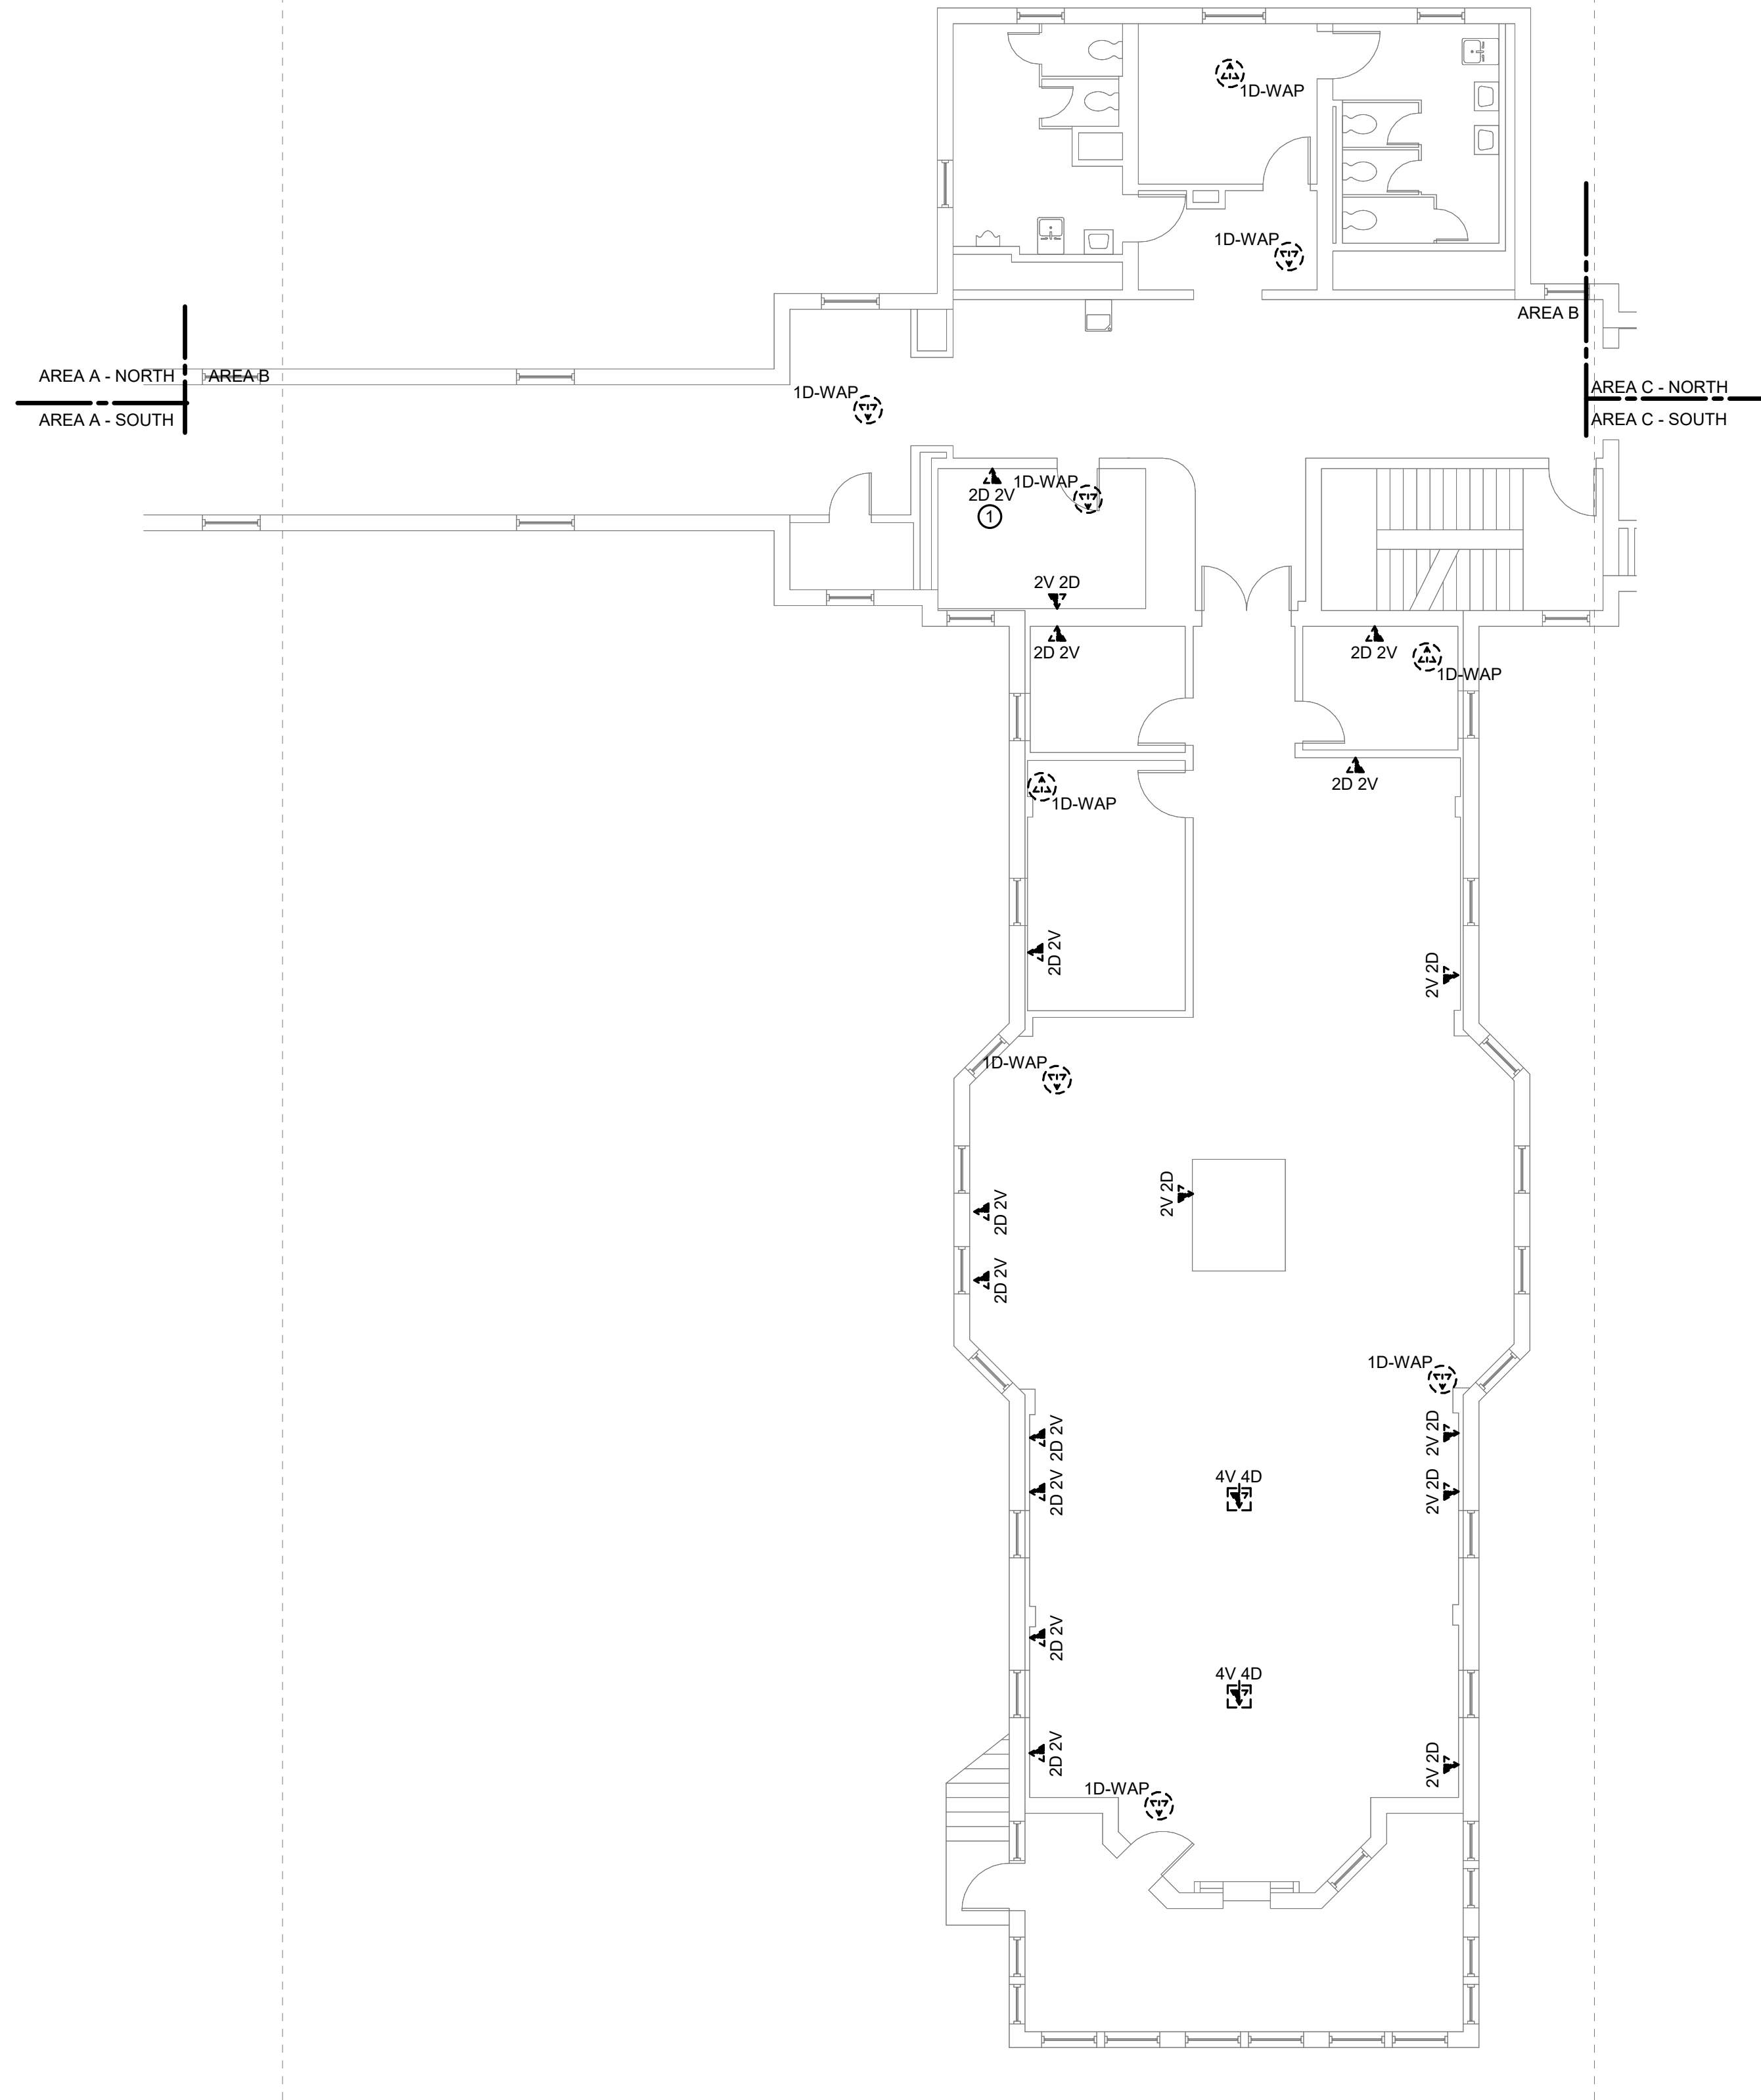

1 BUILDING 06 SECOND FLOOR DEMOLITION PLAN - TECHNOLOGY - AREA B
1/8" = 1'-0"

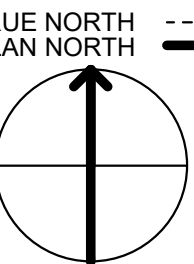

35% SCHEMATIC DESIGN SUBMISSION	5.17.21
65% DESIGN DEVELOPMENT SUBMISSION	6.15.21
65% DESIGN DEVELOPMENT RESUBMISSION	8.25.21
Revisions:	Date:

CONSULTANT

IMEG

THE FUTURE IS IT'S HERE... www.imegcorp.com
15 SUNNEN DRIVE
SUITE 104
ST. LOUIS, MO 63143
P: 314.645.1132 F: 314.645.1173
PROJECT #18004375.03

ARCHITECT/ENGINEER OF RECORD

Romanyk Consulting
Focusing on what matters

Romanyk Consulting Corp. www.romanykconsulting.com
3308 Preston Road, Suite 350-164, Plano, Texas 75093

STAMP

Bicsi
DAVID LARSON
BICS1 ID # 106098
EXPIRES 12-31-25
REGISTERED COMMUNICATIONS DISTRIBUTION DESIGNER

Office of
Construction
and Facilities
Management

VA U.S. Department
of Veterans Affairs

Drawing Title
BUILDING 06 SECOND FLOOR DEMO PLAN -
TECHNOLOGY - AREA B

Approved:

Phase
FINAL BID DOCUMENTS

Sprinklered
FULLY SPRINKLERED

Project Title
EHRM INFRASTRUCTURE
UPGRADES - MILWAUKEE, WI

Location
5000 W. NATIONAL AVENUE, MILWAUKEE, WI

Issue Date
SEPTEMBER 05, 2025








Checked
PHINIE


Drawn
MAIBEJ

Project Number
695-21-700

Building Number
06

Drawing Number
06-TD102B

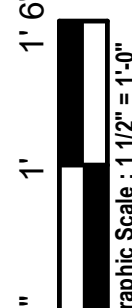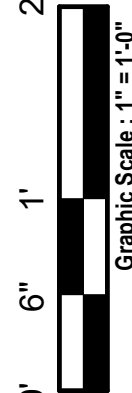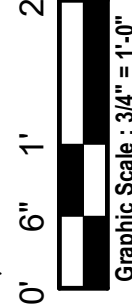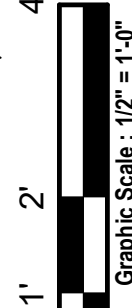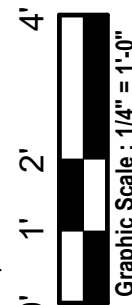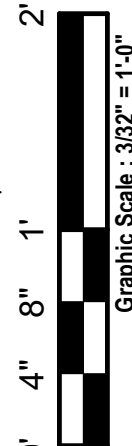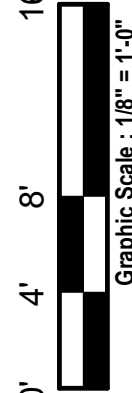

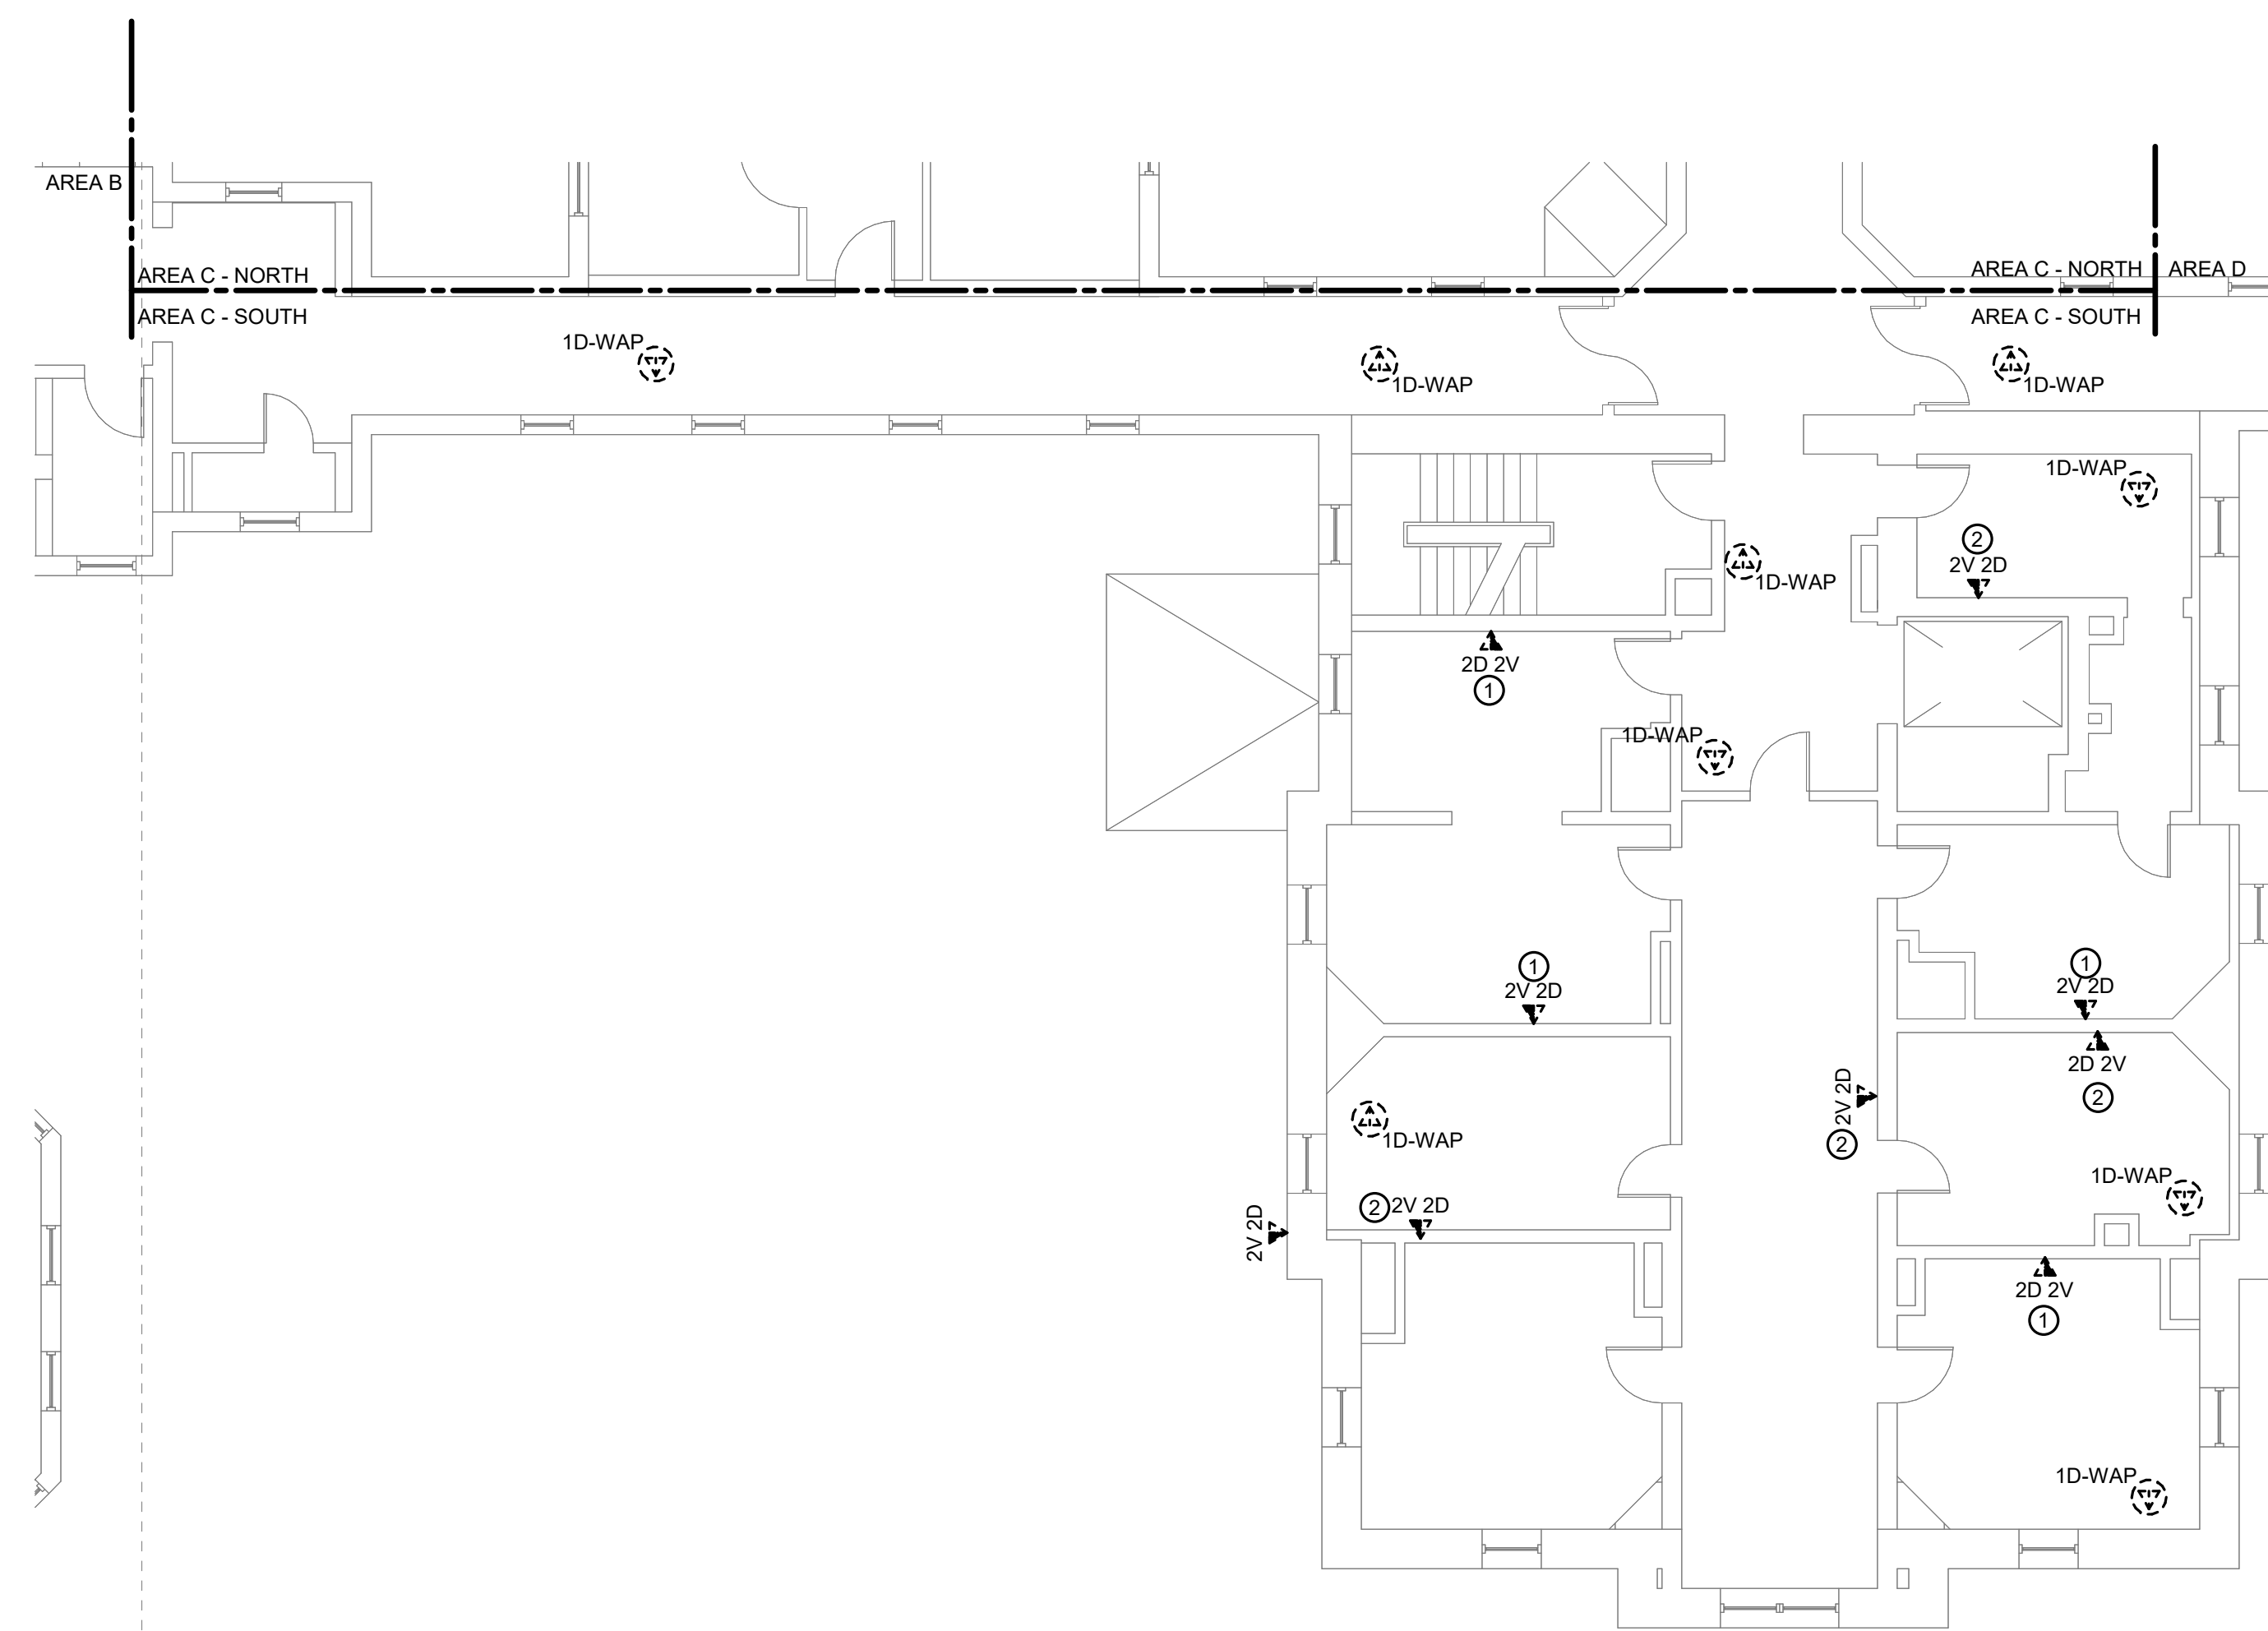

TRUE NORTH
PLAN NORTH



Project Number	695-21-700
Building Number	06
Drawing Number	06-TD102C

F

E

D

C


B

A


9/3/2025 3:55:04 PM

Autodesk Docs\DOCFM East - Milwaukee EHRM (R24)T24_1804375\03_VA Milwaukee_C.dwg

- SHEET NOTES:**
1. REMOVE ALL NETWORK CABLING TO POINTS OF TERMINATION IN ASSOCIATED DATA CLOSET. REFER TO FLOOR PLANS AND SHEET T1001 FOR TR ROOM LOCATIONS.
 2. REFER TO ARCHITECTURAL PHASING PLANS FOR WHEN EXISTING CABLING IS ALLOWED TO BE DEMOLISHED.
 3. FOR ALL EXISTING WIRELESS ACCESS POINTS AND SURVEILLANCE CAMERAS, DEVICES SHALL REMAIN. SCOPE OF WORK INCLUDES CABLE REPLACEMENT ONLY. COORDINATE WITH COR FOR ANY DOWNTIME OF DEVICES. EXISTING LOCATIONS OF WORK AREA, OUTLETS SHOWN ON THIS SHEET MAY NOT NECESSARILY BE IN THE EXACT LOCATION AS IDENTIFIED.

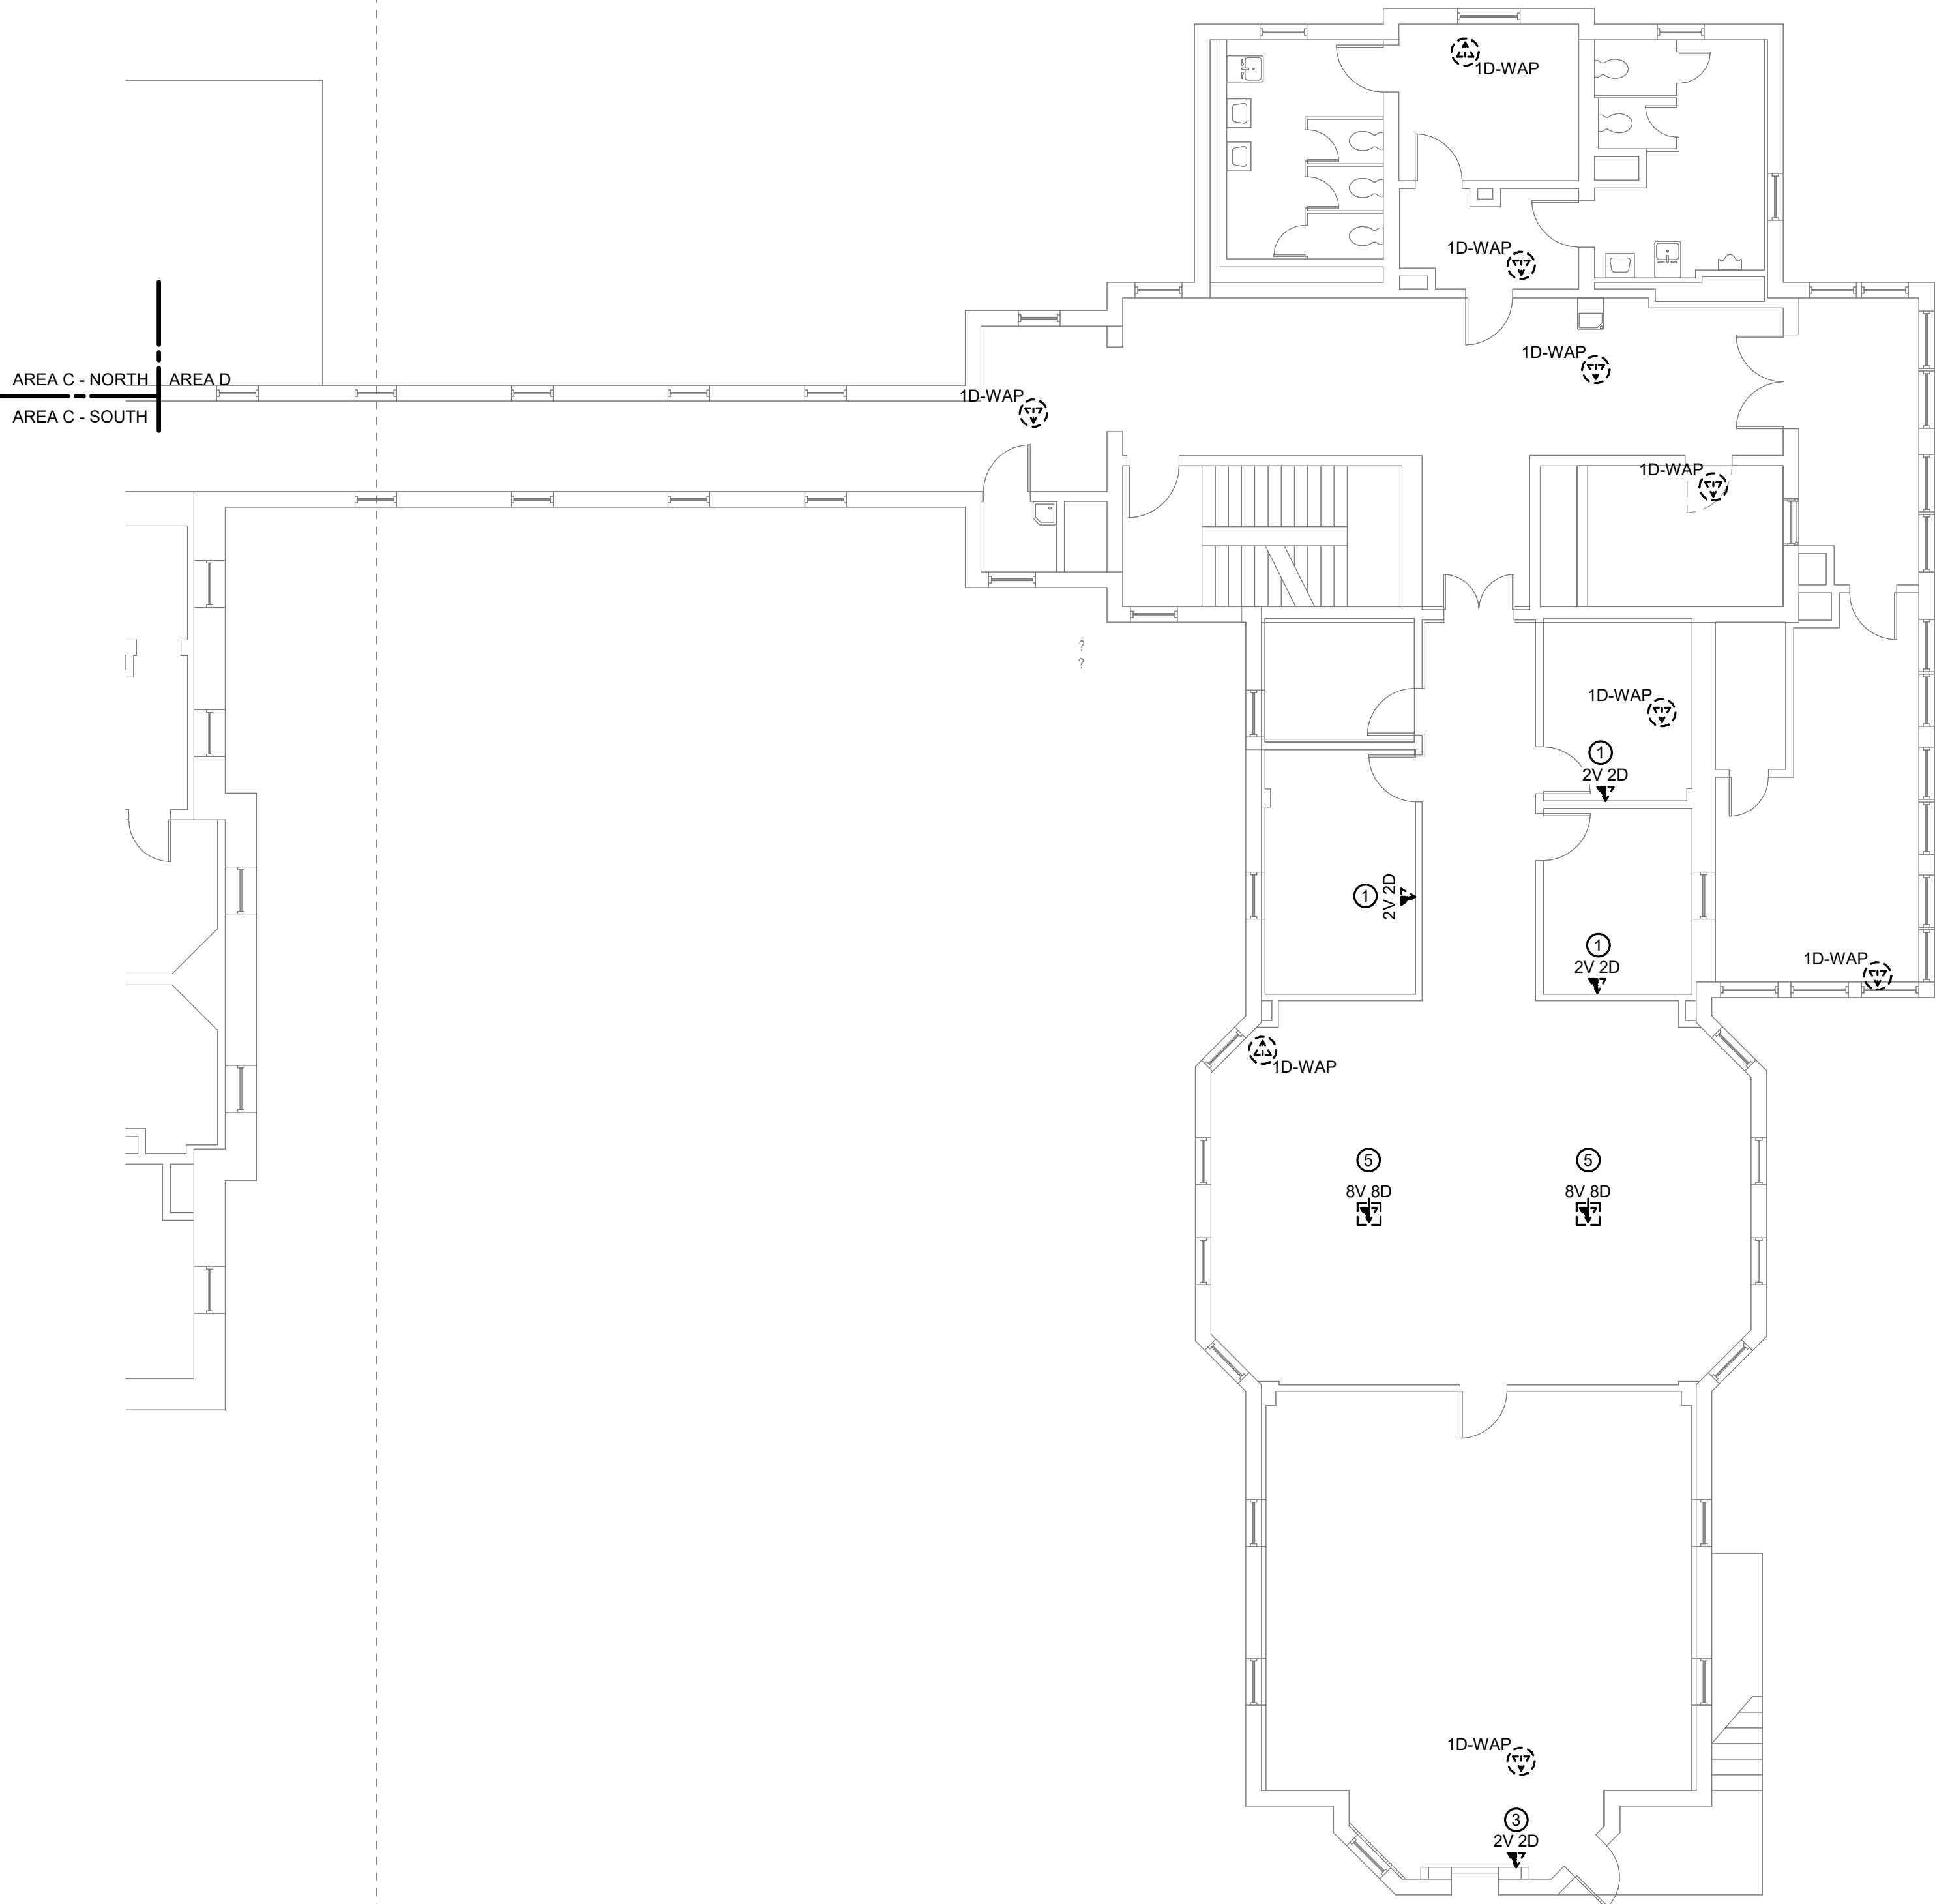

1 BUILDING 06 SECOND FLOOR DEMOLITION PLAN - TECHNOLOGY - AREA D
1/8" = 1'-0"

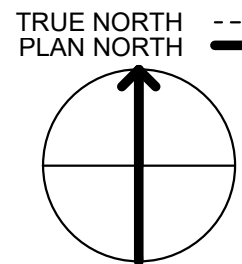

35% SCHEMATIC DESIGN SUBMISSION	5.17.21
65% DESIGN DEVELOPMENT SUBMISSION	6.15.21
65% DESIGN DEVELOPMENT RESUBMISSION	8.25.21
Revisions:	Date:

CONSULTANT

IMEG

15 SUNNEN DRIVE
SUITE 104
ST. LOUIS, MO 63143
P: 314.645.1132 F: 314.645.1173
PROJECT #18004375.03

ARCHITECT/ENGINEER OF RECORD

Romanyk Consulting
Focusing on what matters

Romanyk Consulting Corp. www.romanykconsulting.com
3308 Preston Road, Suite 350-164, Plano, Texas 75093

STAMP

Bicsi
DAVID LARSON
BICS1 ID # 106098
EXPIRES 12-31-25
REGISTERED COMMUNICATIONS DISTRIBUTION DESIGNER
RCDD

Office of
Construction
and Facilities
Management

VA U.S. Department
of Veterans Affairs

Drawing Title
BUILDING 06 SECOND FLOOR DEMO PLAN -
TECHNOLOGY - AREA D

Approved:

Phase
FINAL BID DOCUMENTS

Sprinklered
FULLY SPRINKLERED

Project Title
EHRM INFRASTRUCTURE
UPGRADES - MILWAUKEE, WI

Location
5000 W. NATIONAL AVENUE, MILWAUKEE, WI

Issue Date
SEPTEMBER 05, 2025


Checked
PHINIE


Drawn
MAIBEJ

Project Number
695-21-700

Building Number
06


Drawing Number
06-TD102D

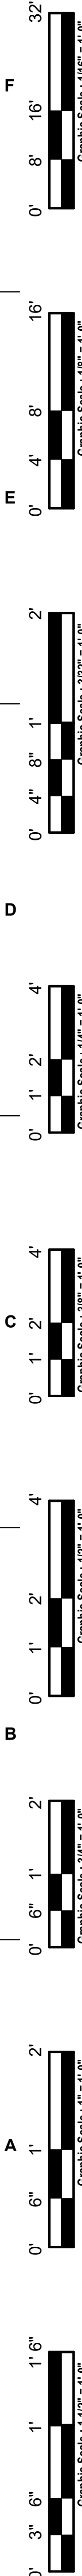

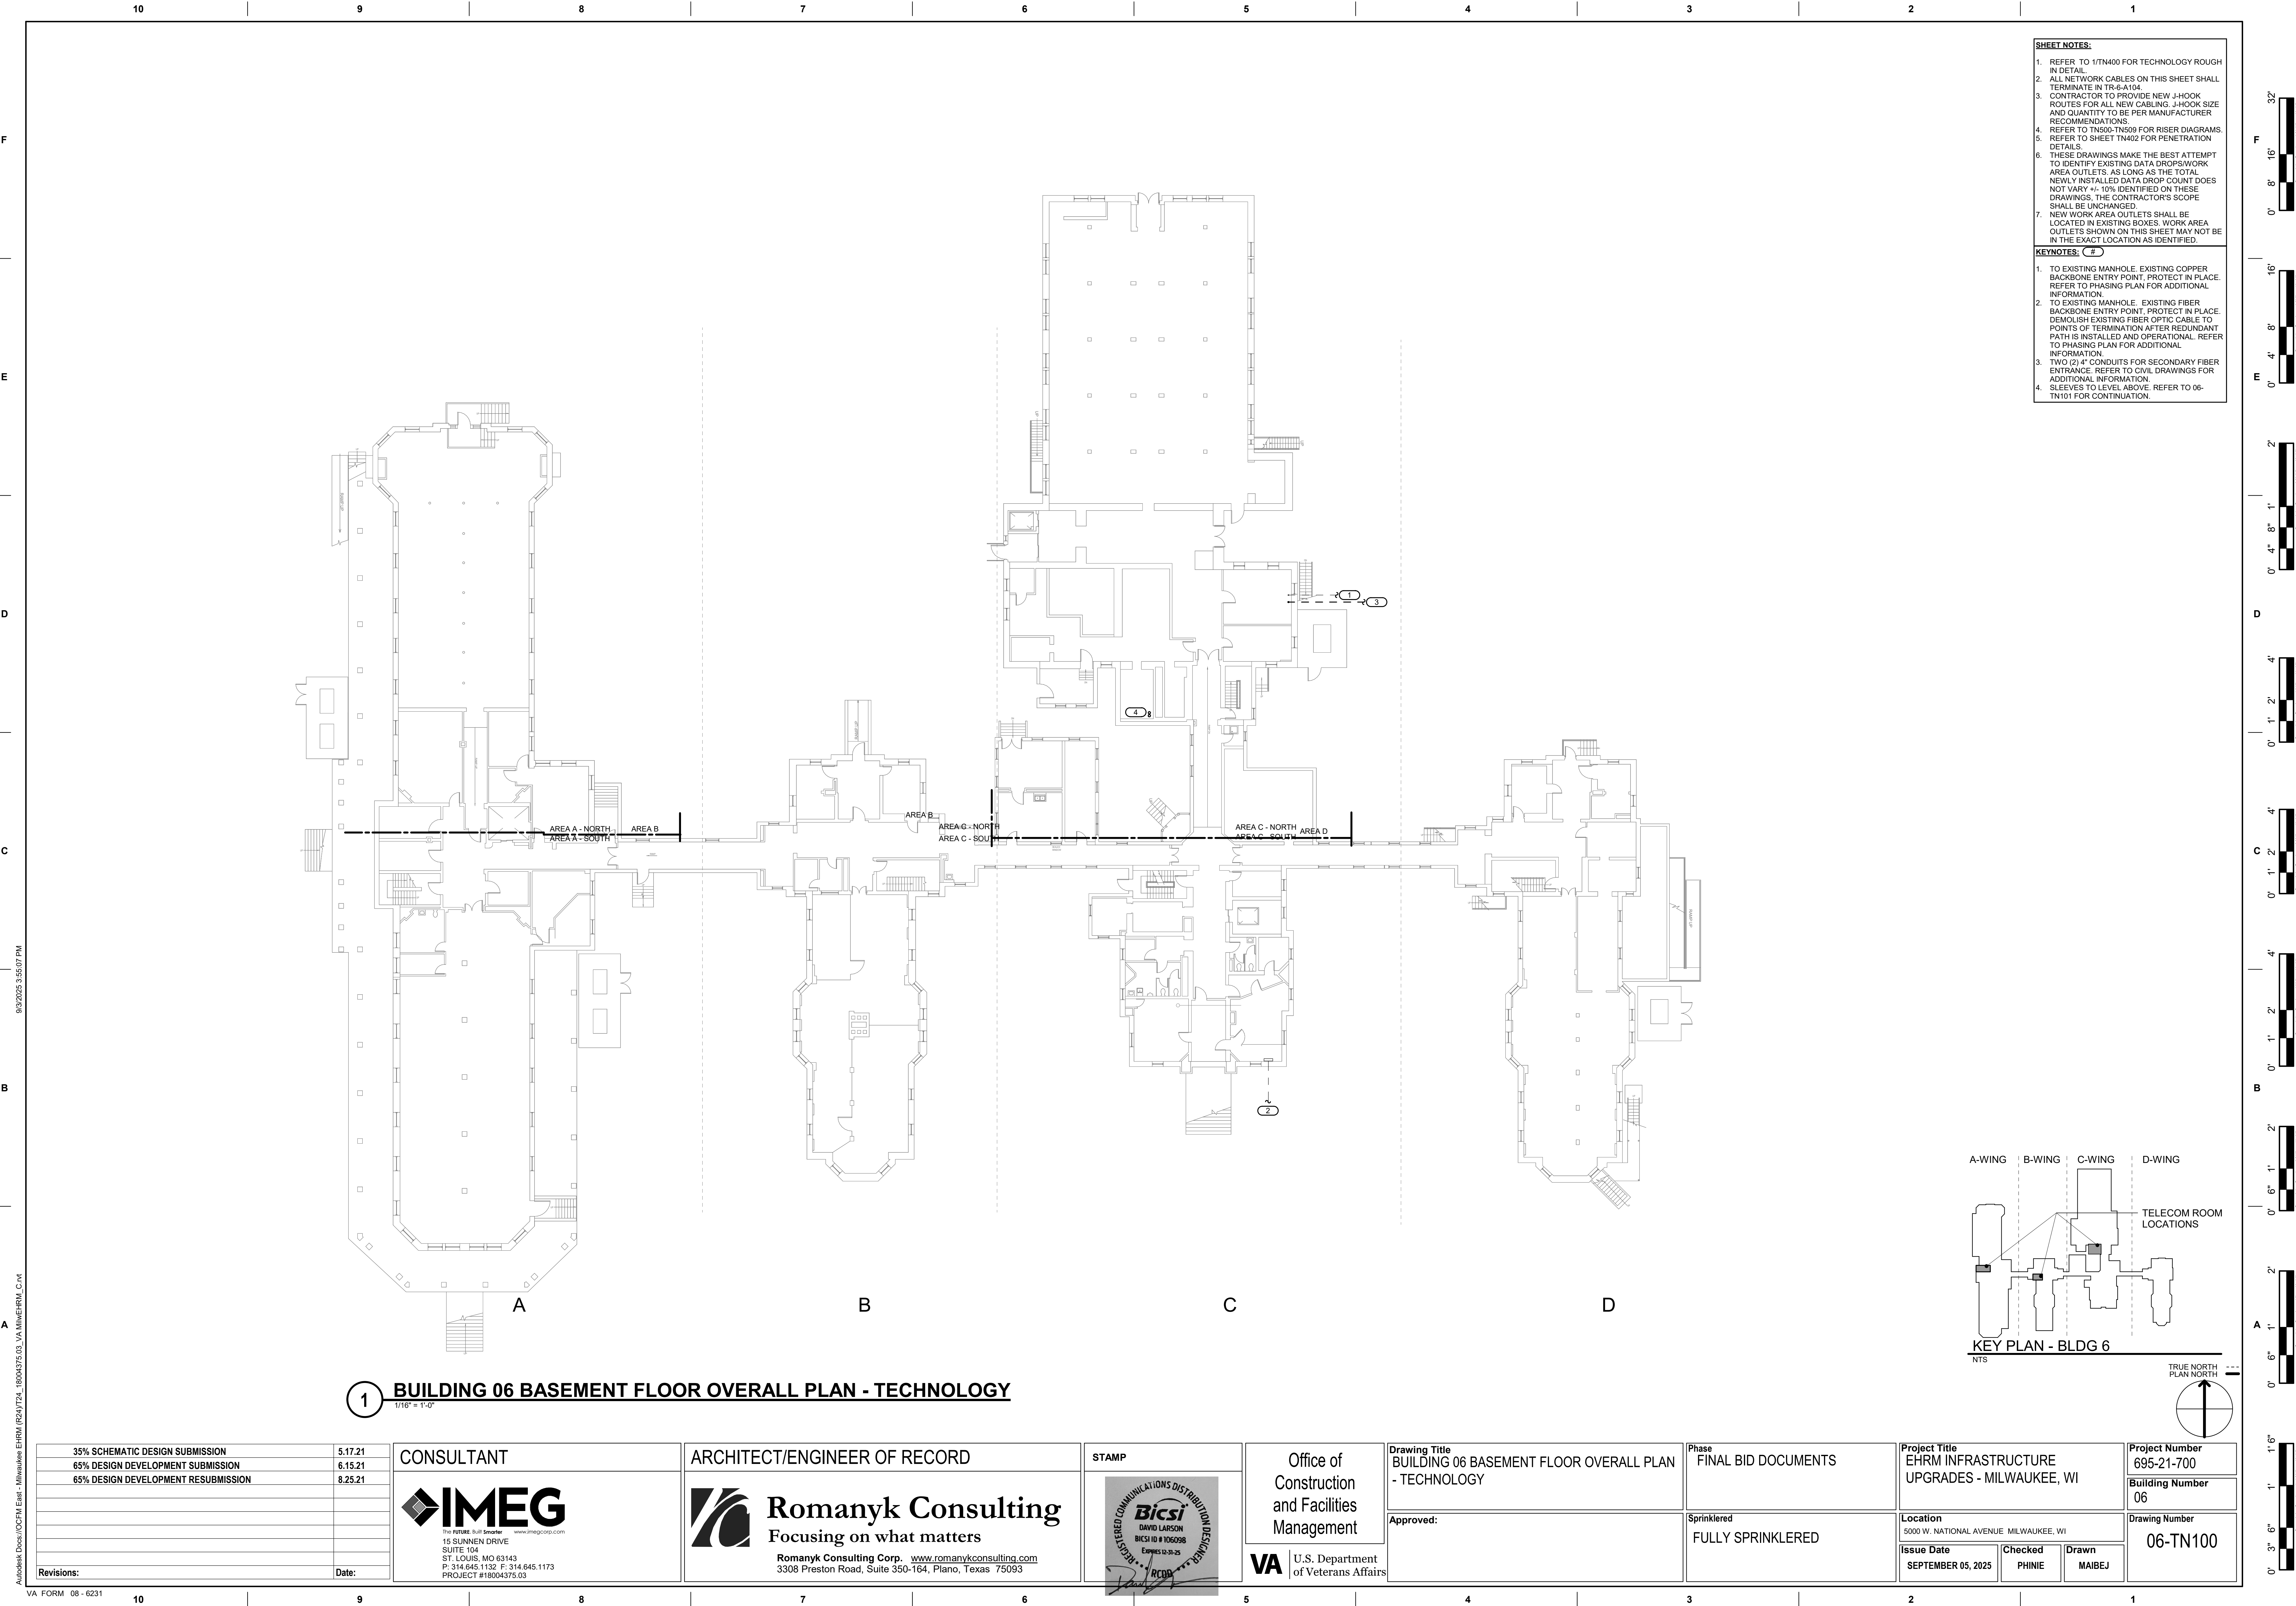

- SHEET NOTES:**
1. REFER TO 1/TN400 FOR TECHNOLOGY ROUGH IN DETAIL.
 2. ALL NETWORK CABLES ON THIS SHEET SHALL TERMINATE IN TS-6-A104.
 3. CONTRACTOR TO PROVIDE NEW J-HOOK ROUTES FOR ALL NEW CABLING. J-HOOK SIZE AND QUANTITY TO BE PER MANUFACTURER RECOMMENDATIONS.
 4. REFER TO TN500-TN509 FOR RISER DIAGRAMS.
 5. REFER TO SHEET TN402 FOR PENETRATION DETAILS.
 6. THESE DRAWINGS MAKE THE BEST ATTEMPT TO IDENTIFY EXISTING DATA DROPS/WORK AREA OUTLETS. AS LONG AS THE TOTAL NEWLY INSTALLED DATA DROP COUNT DOES NOT VARY +/- 10% IDENTIFIED ON THESE DRAWINGS, THE CONTRACTOR'S SCOPE SHALL BE UNCHANGED.
 7. NEW WORK AREA OUTLETS SHALL BE LOCATED IN EXISTING BOXES. WORK AREA OUTLETS SHOWN ON THIS SHEET MAY NOT BE IN THE EXACT LOCATION AS IDENTIFIED.
- KEYNOTES: (#)**
1. TO EXISTING MANHOLE. EXISTING COPPER BACKBONE ENTRY POINT. PROTECT IN PLACE. REFER TO PHASING PLAN FOR ADDITIONAL INFORMATION.
 2. TO EXISTING MANHOLE. EXISTING FIBER BACKBONE ENTRY POINT. PROTECT IN PLACE. DEMOLISH EXISTING FIBER OPTIC CABLE TO POINTS OF TERMINATION AFTER REDUNDANT PATH IS INSTALLED AND OPERATIONAL. REFER TO PHASING PLAN FOR ADDITIONAL INFORMATION.
 3. TWO (2) 4" CONDUITS FOR SECONDARY FIBER ENTRANCE. REFER TO CIVIL DRAWINGS FOR ADDITIONAL INFORMATION.
 4. SLEEVES TO LEVEL ABOVE. REFER TO 06-TN101 FOR CONTINUATION.

1 BUILDING 06 BASEMENT FLOOR OVERALL PLAN - TECHNOLOGY
1/16" = 1'-0"

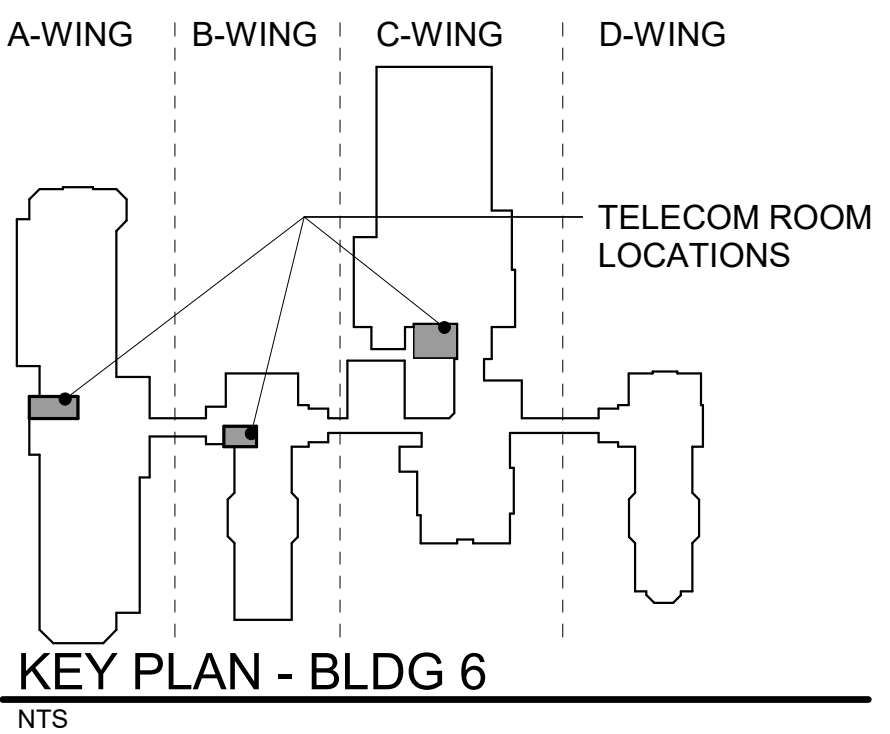

35% SCHEMATIC DESIGN SUBMISSION	5.17.21
65% DESIGN DEVELOPMENT SUBMISSION	6.15.21
65% DESIGN DEVELOPMENT RESUBMISSION	8.25.21
Revisions:	Date:

CONSULTANT

IMEG

15 SUNNEN DRIVE
SUITE 104
ST. LOUIS, MO 63143
P: 314.645.1132 F: 314.645.1173
PROJECT #18004375.03

ARCHITECT/ENGINEER OF RECORD

Romanyk Consulting
Focusing on what matters

Romanyk Consulting Corp. www.romanykconsulting.com
3308 Preston Road, Suite 350-164, Plano, Texas 75093

STAMP

Bicsi
DAVID LARSON
BICS1 ID # 106098
EXPIRES 12-31-25
REGISTERED COMMUNICATIONS DISTRIBUTION DESIGNER
RCDD

Office of
Construction
and Facilities
Management

VA U.S. Department
of Veterans Affairs

Drawing Title
BUILDING 06 BASEMENT FLOOR OVERALL PLAN
- TECHNOLOGY

Approved:

Phase
FINAL BID DOCUMENTS

Sprinklered
FULLY SPRINKLERED

Project Title
EHRM INFRASTRUCTURE
UPGRADES - MILWAUKEE, WI

Location
5000 W. NATIONAL AVENUE MILWAUKEE, WI

Issue Date
SEPTEMBER 05, 2025

Checked
PHINE

Drawn
MAIBEJ

Project Number
695-21-700

Building Number
06

Drawing Number
06-TN100

F

E


D

C


B

A

Autodesk Docs\DCFM East - Milwaukee EHRM (R24)T24_1804375\03_VA Milwaukee EHRM_C.dwg 9/23/2025 3:55:08 PM

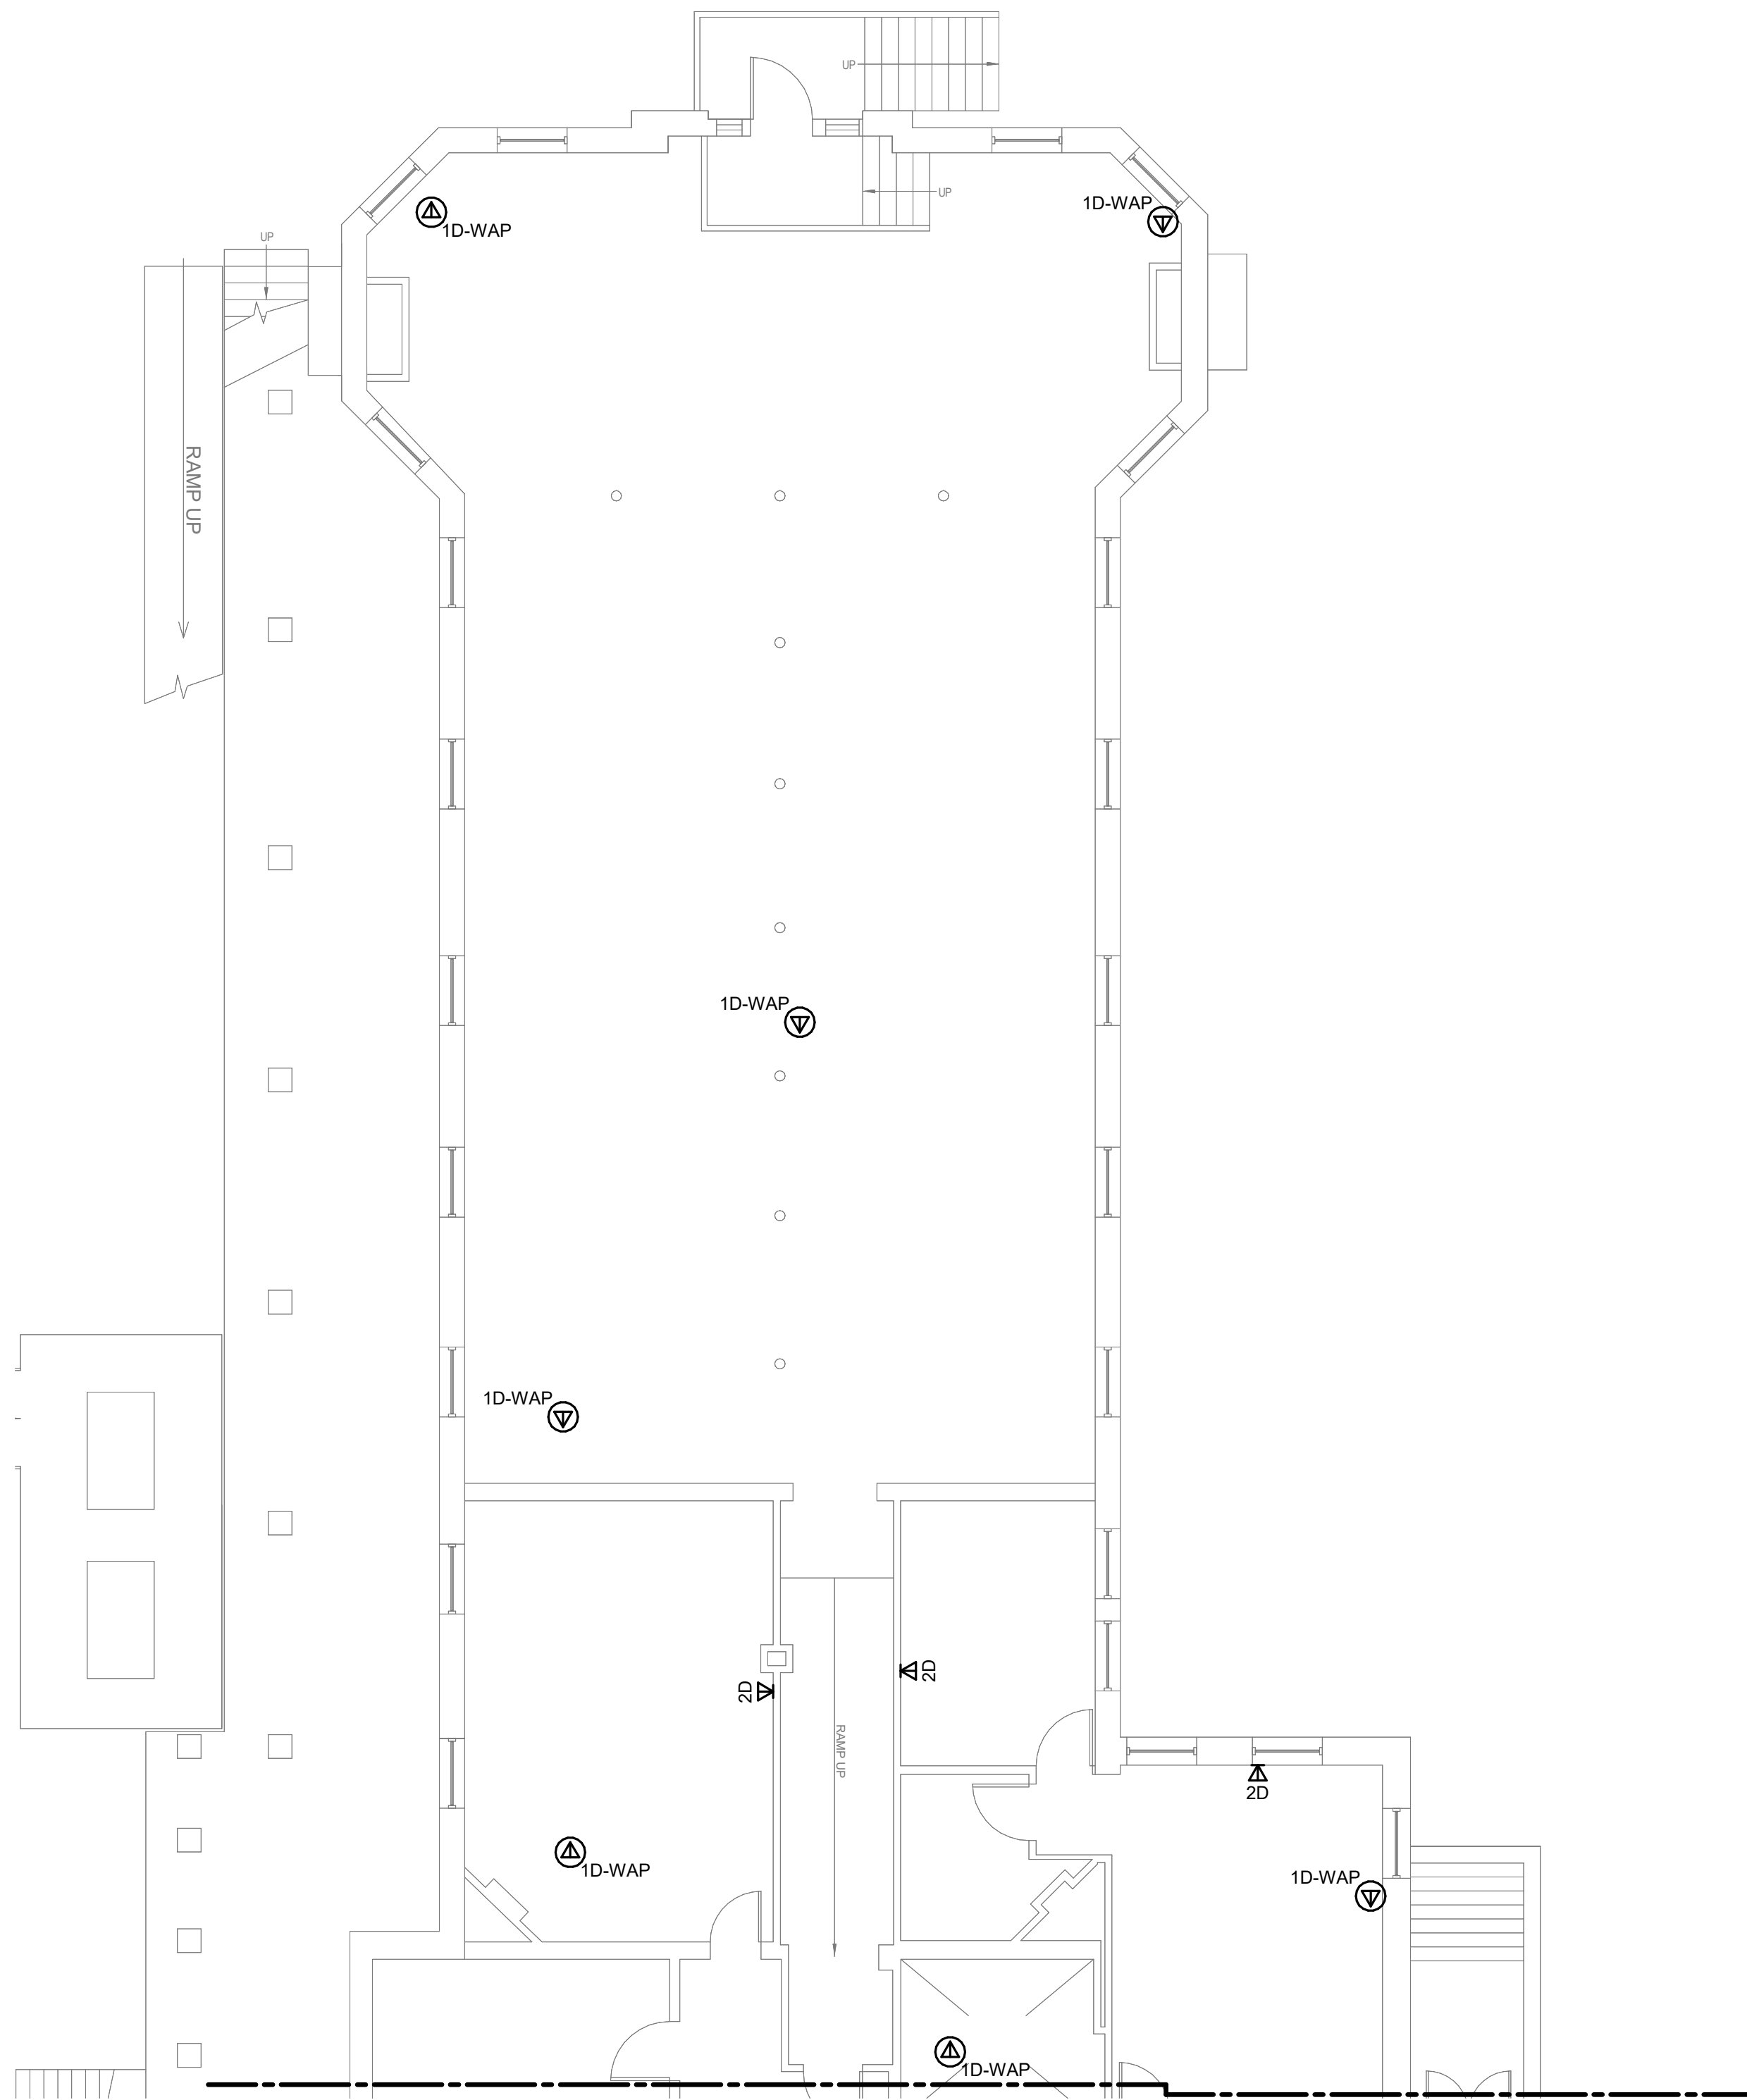


1 BUILDING 06 BASEMENT FLOOR PLAN - AREA A NORTH
1/8" = 1'-0"

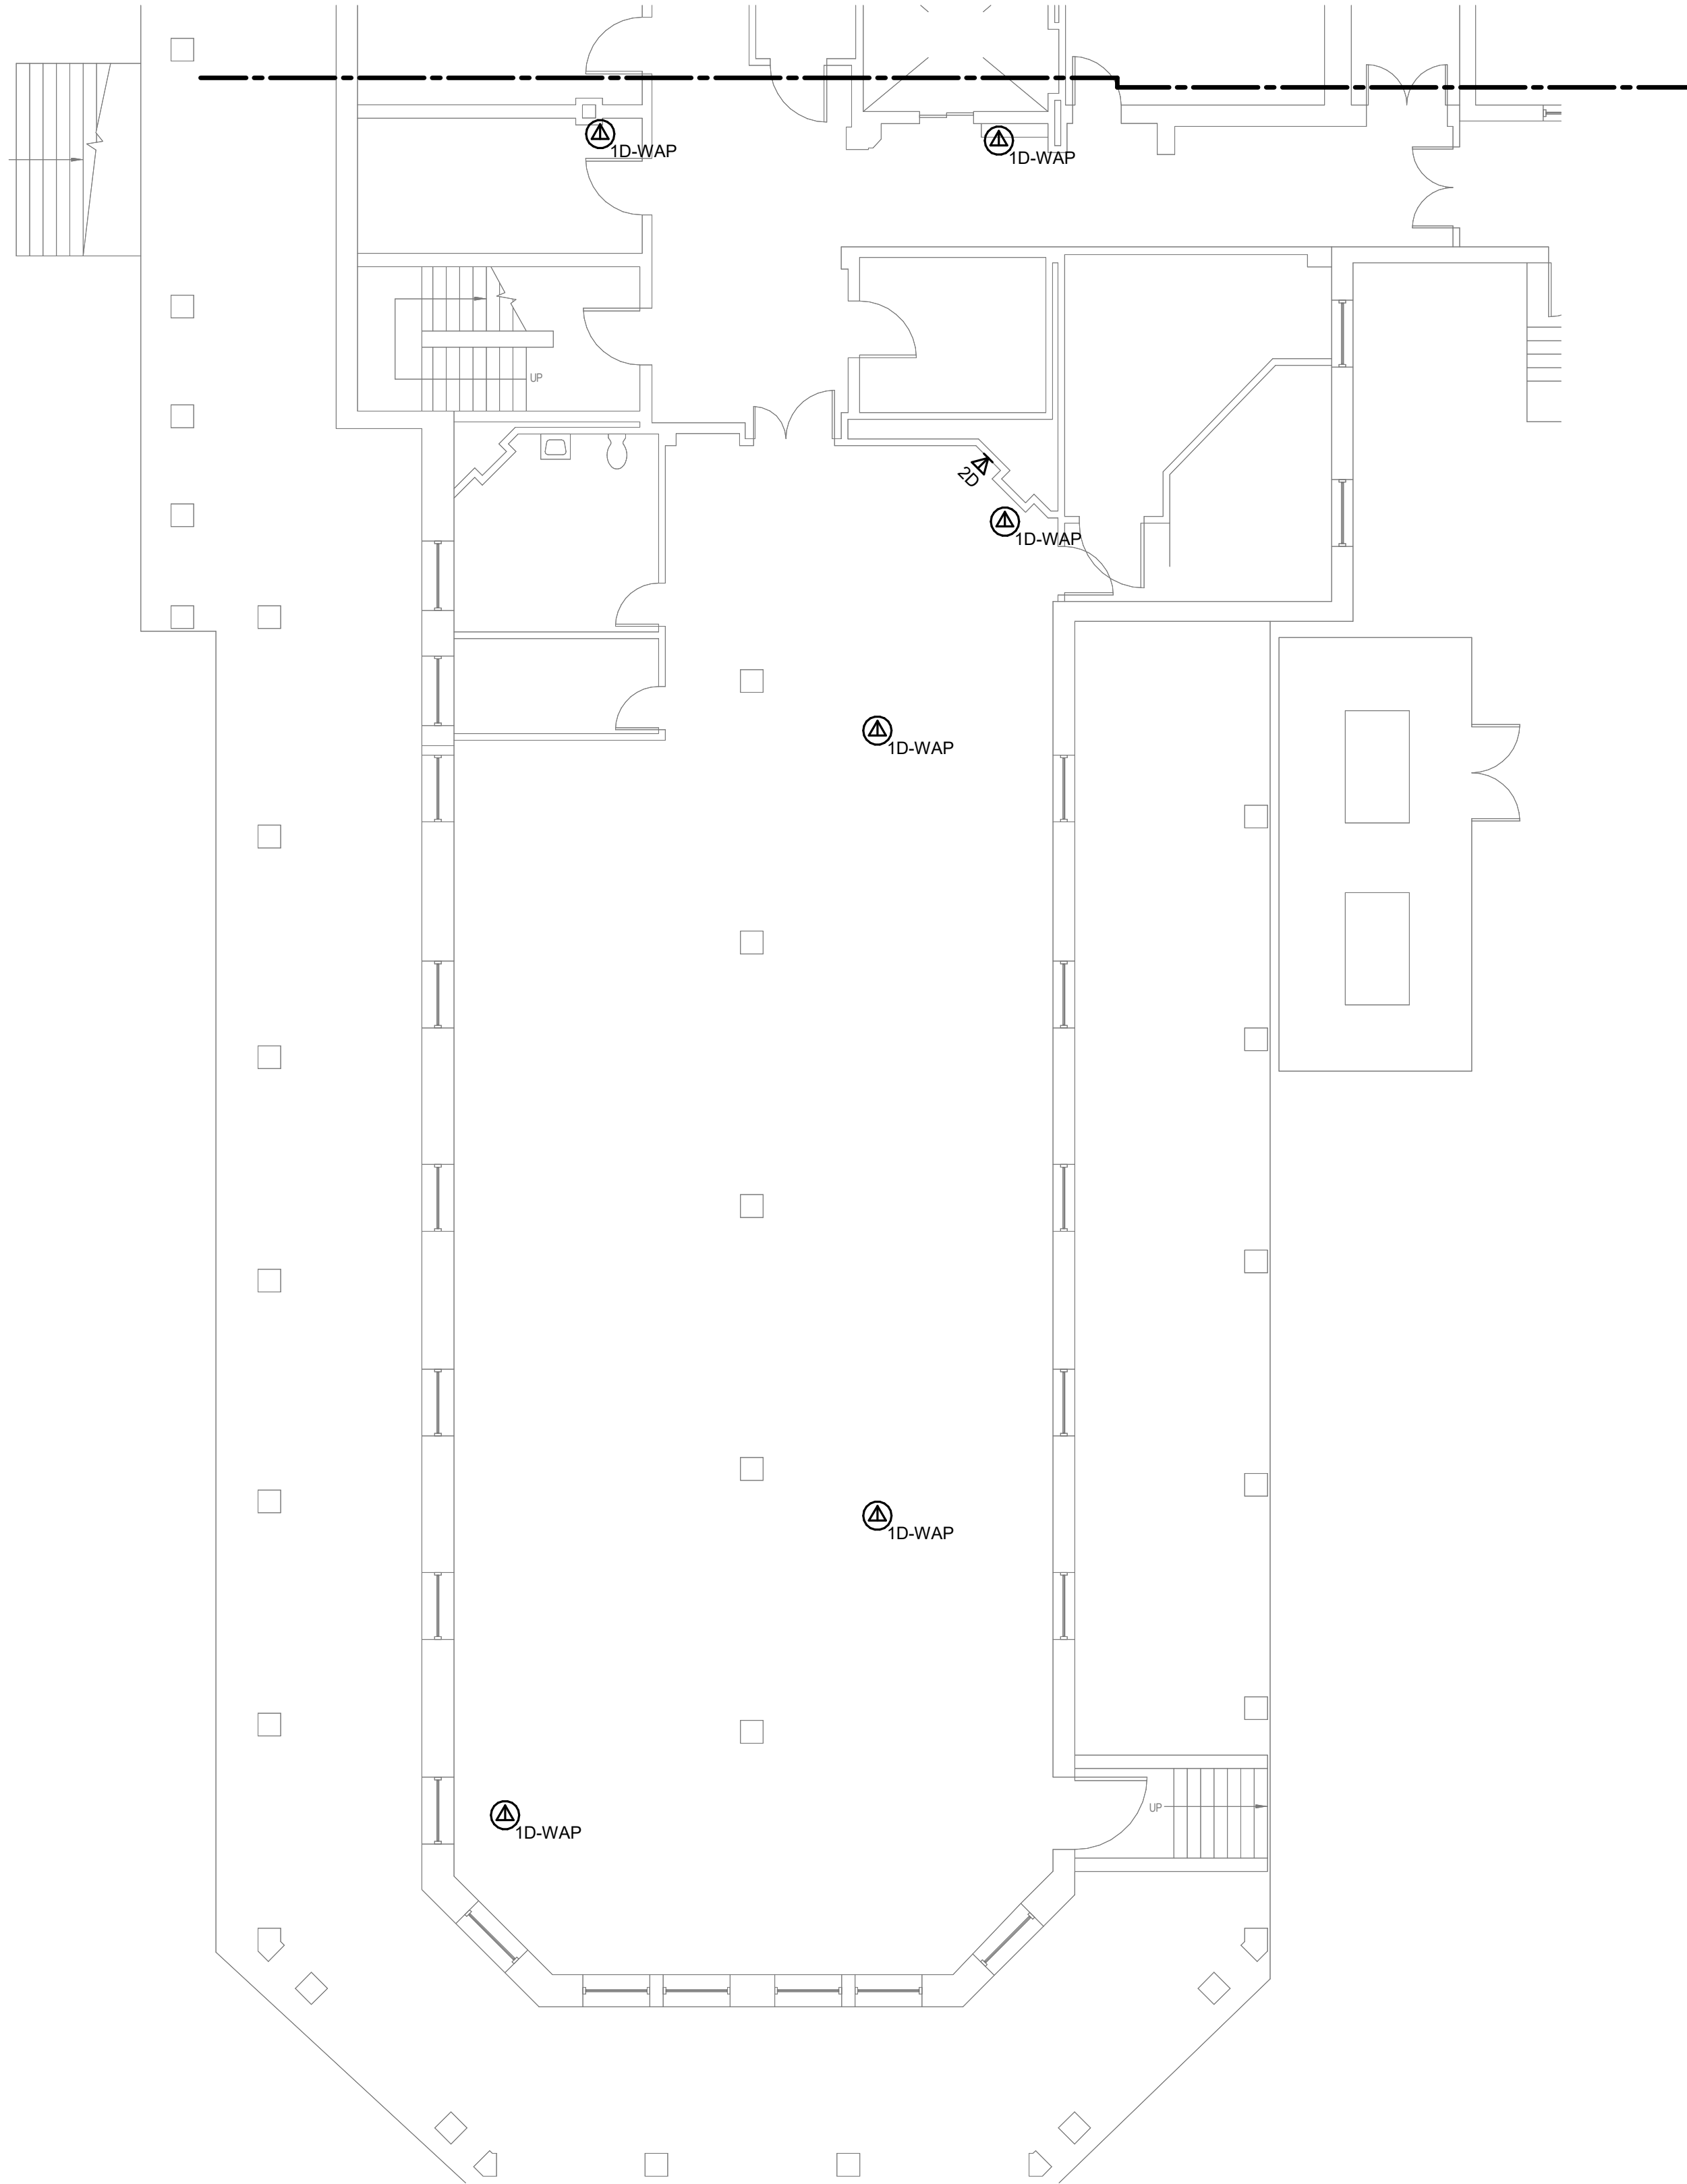

2 BUILDING 06 BASEMENT FLOOR PLAN - AREA A SOUTH
1/8" = 1'-0"

- SHEET NOTES:**
1. REFER TO 1/TN400 FOR TECHNOLOGY ROUGH IN DETAIL.
 2. ALL NETWORK CABLES ON THIS SHEET SHALL TERMINATE IN TS-6-A104.
 3. CONTRACTOR TO PROVIDE NEW J-HOOK ROUTES FOR ALL NEW CABLING. J-HOOK SIZE AND QUANTITY TO BE PER MANUFACTURER RECOMMENDATIONS.
 4. REFER TO TN500-TN509 FOR RISER DIAGRAMS.
 5. REFER TO SHEET TN402 FOR PENETRATION DETAILS.
 6. THESE DRAWINGS MAKE THE BEST ATTEMPT TO IDENTIFY EXISTING DATA DROPS/WORK AREA OUTLETS. AS LONG AS THE TOTAL NEWLY INSTALLED DATA DROP COUNT DOES NOT VARY +/- 10% IDENTIFIED ON THESE DRAWINGS, THE CONTRACTOR'S SCOPE SHALL BE UNCHANGED.
 7. NEW WORK AREA OUTLETS SHALL BE LOCATED IN EXISTING BOXES. WORK AREA OUTLETS SHOWN ON THIS SHEET MAY NOT BE IN THE EXACT LOCATION AS IDENTIFIED.
 8. CONTRACTOR TO INCLUDE AN ALLOWANCE FOR 10% ADDITIONAL 2-PORTS CAT6A INFORMATION OUTLETS IN THEIR PROPOSAL FOR THIS SHEET. FUTURE INFORMATION OUTLET LOCATIONS WILL BE DETERMINED BY THE VA AT A LATER DATE.

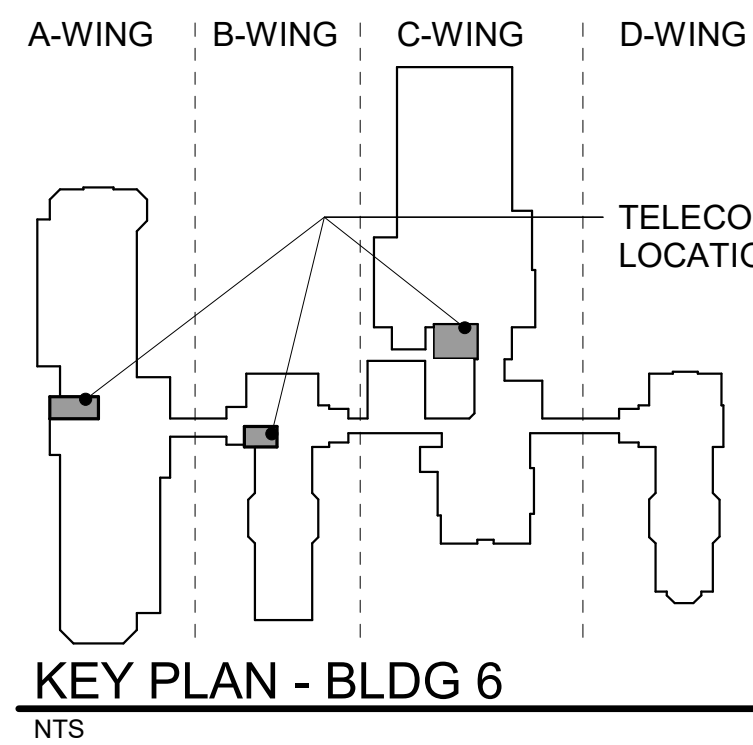

35% SCHEMATIC DESIGN SUBMISSION	5.17.21
65% DESIGN DEVELOPMENT SUBMISSION	6.15.21
65% DESIGN DEVELOPMENT RESUBMISSION	8.25.21
Revisions:	Date:

CONSULTANT



ARCHITECT/ENGINEER OF RECORD



STAMP



Office of
Construction
and Facilities
Management



U.S. Department
of Veterans Affairs

Drawing Title
BUILDING 06 BASEMENT PLAN - TECHNOLOGY -
AREA A

Approved:

Phase
FINAL BID DOCUMENTS

Sprinklered
FULLY SPRINKLERED

Project Title
EHRM INFRASTRUCTURE
UPGRADES - MILWAUKEE, WI

Location
5000 W. NATIONAL AVENUE, MILWAUKEE, WI

Issue Date
SEPTEMBER 05, 2025







Checked
PHINIE

Drawn
MAIBEJ

Project Number
695-21-700

Building Number
06

Drawing Number
06-TN100A

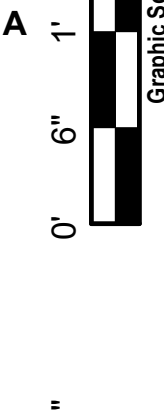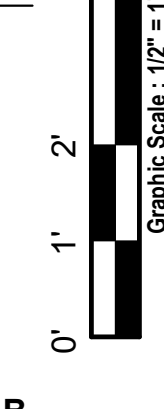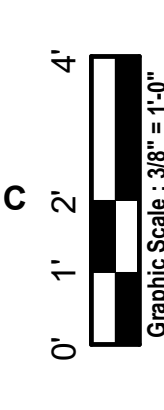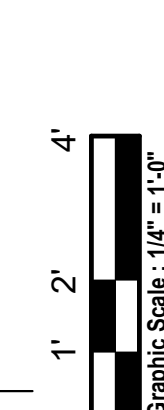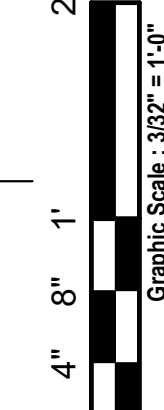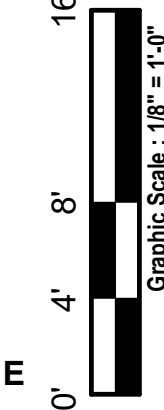

F

E

D

C


B

A


9/2/2025 3:55:09 PM

Autodesk Docs\DCFM East - Milwaukee EHRM (R24)T24_1804375\03_VA Milwaukee_C.dwt


- SHEET NOTES:**
1. REFER TO 1/TN400 FOR TECHNOLOGY ROUGH IN DETAIL.
 2. ALL NETWORK CABLES ON THIS SHEET SHALL TERMINATE IN TS-6-A104.
 3. CONTRACTOR TO PROVIDE NEW J-HOOK ROUTES FOR ALL NEW CABLING. J-HOOK SIZE AND QUANTITY TO BE PER MANUFACTURER RECOMMENDATIONS.
 4. REFER TO TN500-TN509 FOR RISER DIAGRAMS.
 5. REFER TO SHEET TN402 FOR PENETRATION DETAILS.
 6. THESE DRAWINGS MAKE THE BEST ATTEMPT TO IDENTIFY EXISTING DATA DROPS/WORK AREA OUTLETS. AS LONG AS THE TOTAL NEWLY INSTALLED DATA DROP COUNT DOES NOT VARY +/- 10% IDENTIFIED ON THESE DRAWINGS, THE CONTRACTOR'S SCOPE SHALL BE UNCHANGED.
 7. NEW WORK AREA OUTLETS SHALL BE LOCATED IN EXISTING BOXES. WORK AREA OUTLETS SHOWN ON THIS SHEET MAY NOT BE IN THE EXACT LOCATION AS IDENTIFIED.
 8. CONTRACTOR TO INCLUDE AN ALLOWANCE FOR 10% ADDITIONAL 2-PORTS CAT6A INFORMATION OUTLETS IN THEIR PROPOSAL FOR THIS SHEET. FUTURE INFORMATION OUTLET LOCATIONS WILL BE DETERMINED BY THE VA AT A LATER DATE.

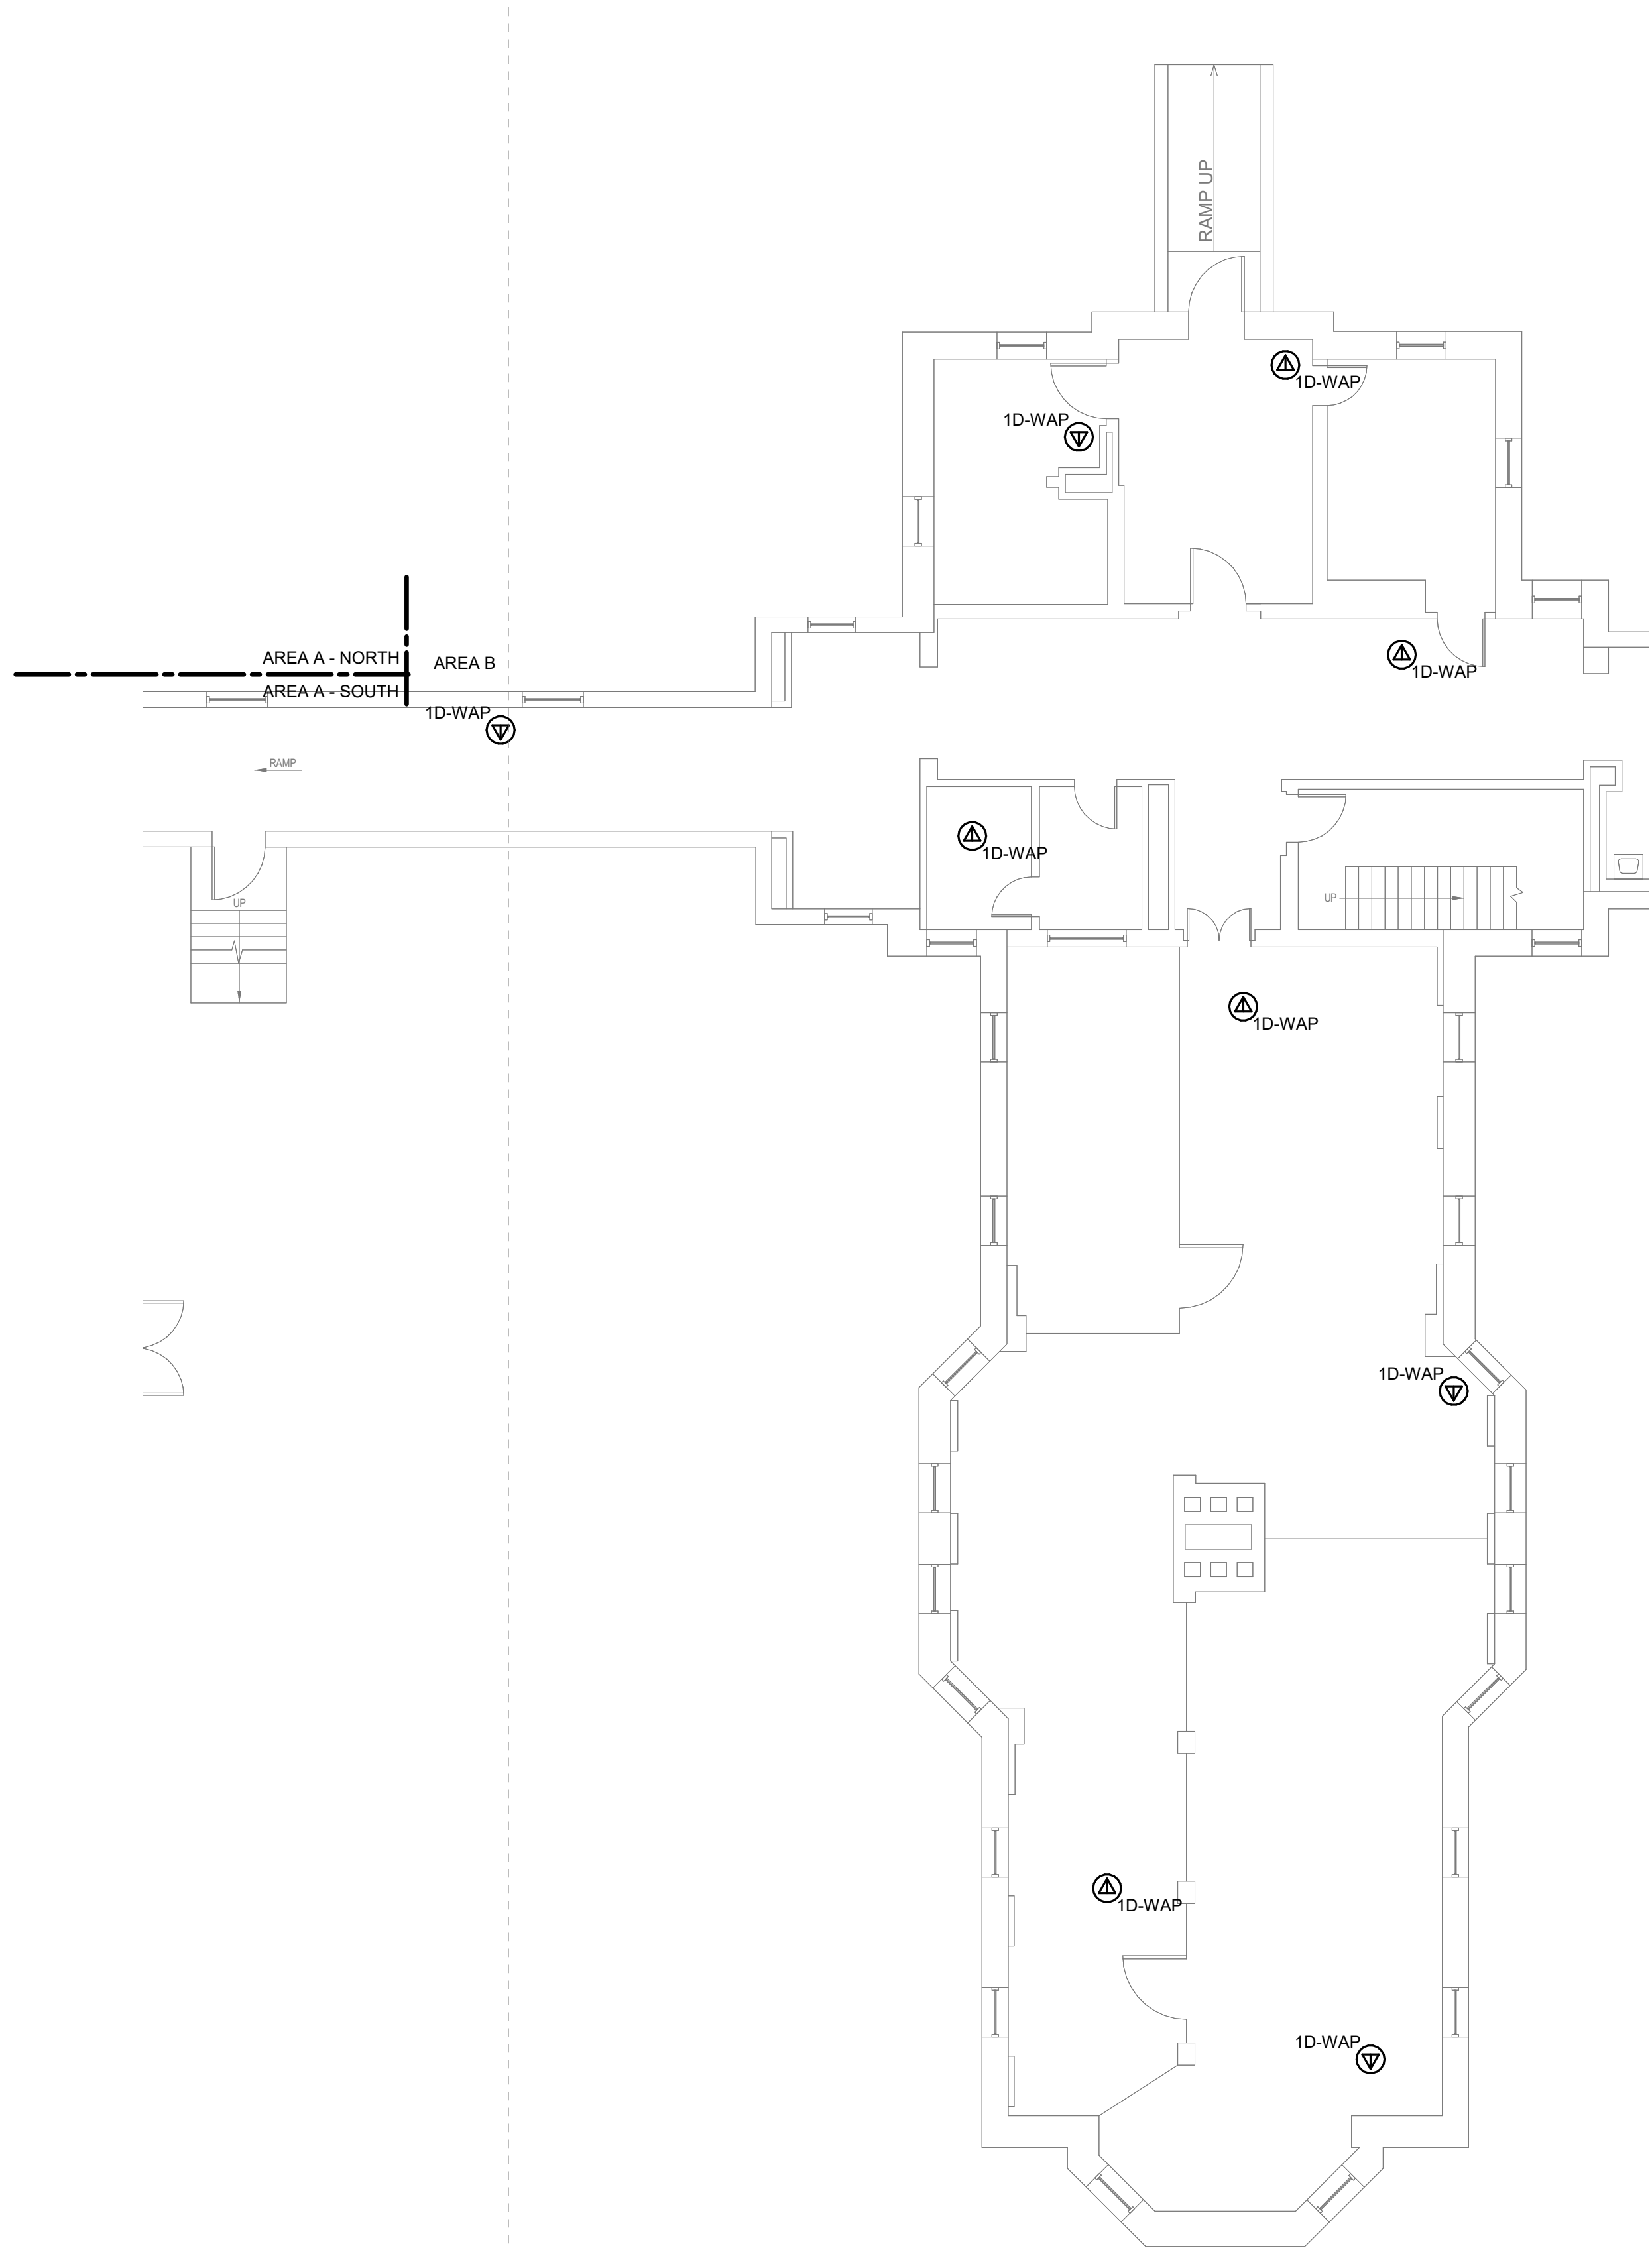

1 BUILDING 06 BASEMENT FLOOR PLAN - AREA B
1/8" = 1'-0"

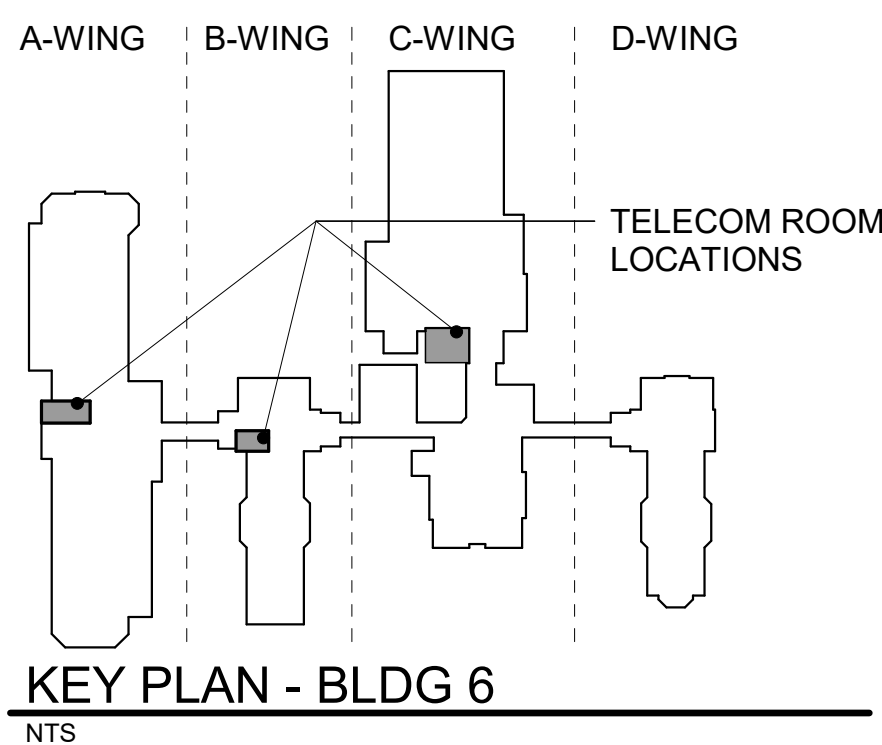

KEY PLAN - BLDG 6
NTS

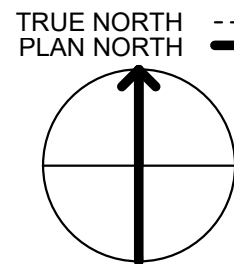

35% SCHEMATIC DESIGN SUBMISSION	5.17.21
65% DESIGN DEVELOPMENT SUBMISSION	6.15.21
65% DESIGN DEVELOPMENT RESUBMISSION	8.25.21
Revisions:	Date:

CONSULTANT

IMEG

THE FUTURE IS IT'S HERE! www.imegcorp.com
15 SUNNEN DRIVE
SUITE 104
ST. LOUIS, MO 63143
P: 314.645.1132 F: 314.645.1173
PROJECT #18004375.03

ARCHITECT/ENGINEER OF RECORD

Romanyk Consulting
Focusing on what matters

Romanyk Consulting Corp. www.romanykconsulting.com
3308 Preston Road, Suite 350-164, Plano, Texas 75093

STAMP

Bicsi
DAVID LARSON
BICS1 ID # 106098
EXPIRES 12-31-25
REGISTERED COMMUNICATIONS DISTRIBUTION DESIGNER
RCDD

Office of
Construction
and Facilities
Management

VA U.S. Department
of Veterans Affairs

Drawing Title BUILDING 06 BASEMENT PLAN - TECHNOLOGY - AREA B
Approved:

Phase FINAL BID DOCUMENTS
Sprinklered FULLY SPRINKLERED

Project Title EHRM INFRASTRUCTURE UPGRADES - MILWAUKEE, WI
Location 5000 W. NATIONAL AVENUE MILWAUKEE, WI
Issue Date SEPTEMBER 05, 2025
Checked PHINIE
Drawn MAIBEJ

Project Number 695-21-700
Building Number 06
Drawing Number 06-TN100B

F

E

D

C


B

A


9/20/2025 3:55:12 PM

Autodesk Docs\DOCFM East - Milwaukee EHRM (R24)T24_18043725.03_VA MilwEHRM_C.dwt

- SHEET NOTES:**
1. REFER TO 1/TN400 FOR TECHNOLOGY ROUGH IN DETAIL.
 2. ALL NETWORK CABLES ON THIS SHEET SHALL TERMINATE IN TS-6-A104.
 3. CONTRACTOR TO PROVIDE NEW J-HOOK ROUTES FOR ALL NEW CABLING. J-HOOK SIZE AND QUANTITY TO BE PER MANUFACTURER RECOMMENDATIONS.
 4. REFER TO TN500-TN509 FOR RISER DIAGRAMS.
 5. REFER TO SHEET TN402 FOR PENETRATION DETAILS.
 6. THESE DRAWINGS MAKE THE BEST ATTEMPT TO IDENTIFY EXISTING DATA DROPS/WORK AREA OUTLETS. AS LONG AS THE TOTAL NEWLY INSTALLED DATA DROP COUNT DOES NOT VARY +/- 10% IDENTIFIED ON THESE DRAWINGS, THE CONTRACTOR'S SCOPE SHALL BE UNCHANGED.
 7. NEW WORK AREA OUTLETS SHALL BE LOCATED IN EXISTING BOXES. WORK AREA OUTLETS SHOWN ON THIS SHEET MAY NOT BE IN THE EXACT LOCATION AS IDENTIFIED.
 8. CONTRACTOR TO INCLUDE AN ALLOWANCE FOR 10% ADDITIONAL 2-PORTS CAT6A INFORMATION OUTLETS IN THEIR PROPOSAL FOR THIS SHEET. FUTURE INFORMATION OUTLET LOCATIONS WILL BE DETERMINED BY THE VA AT A LATER DATE.

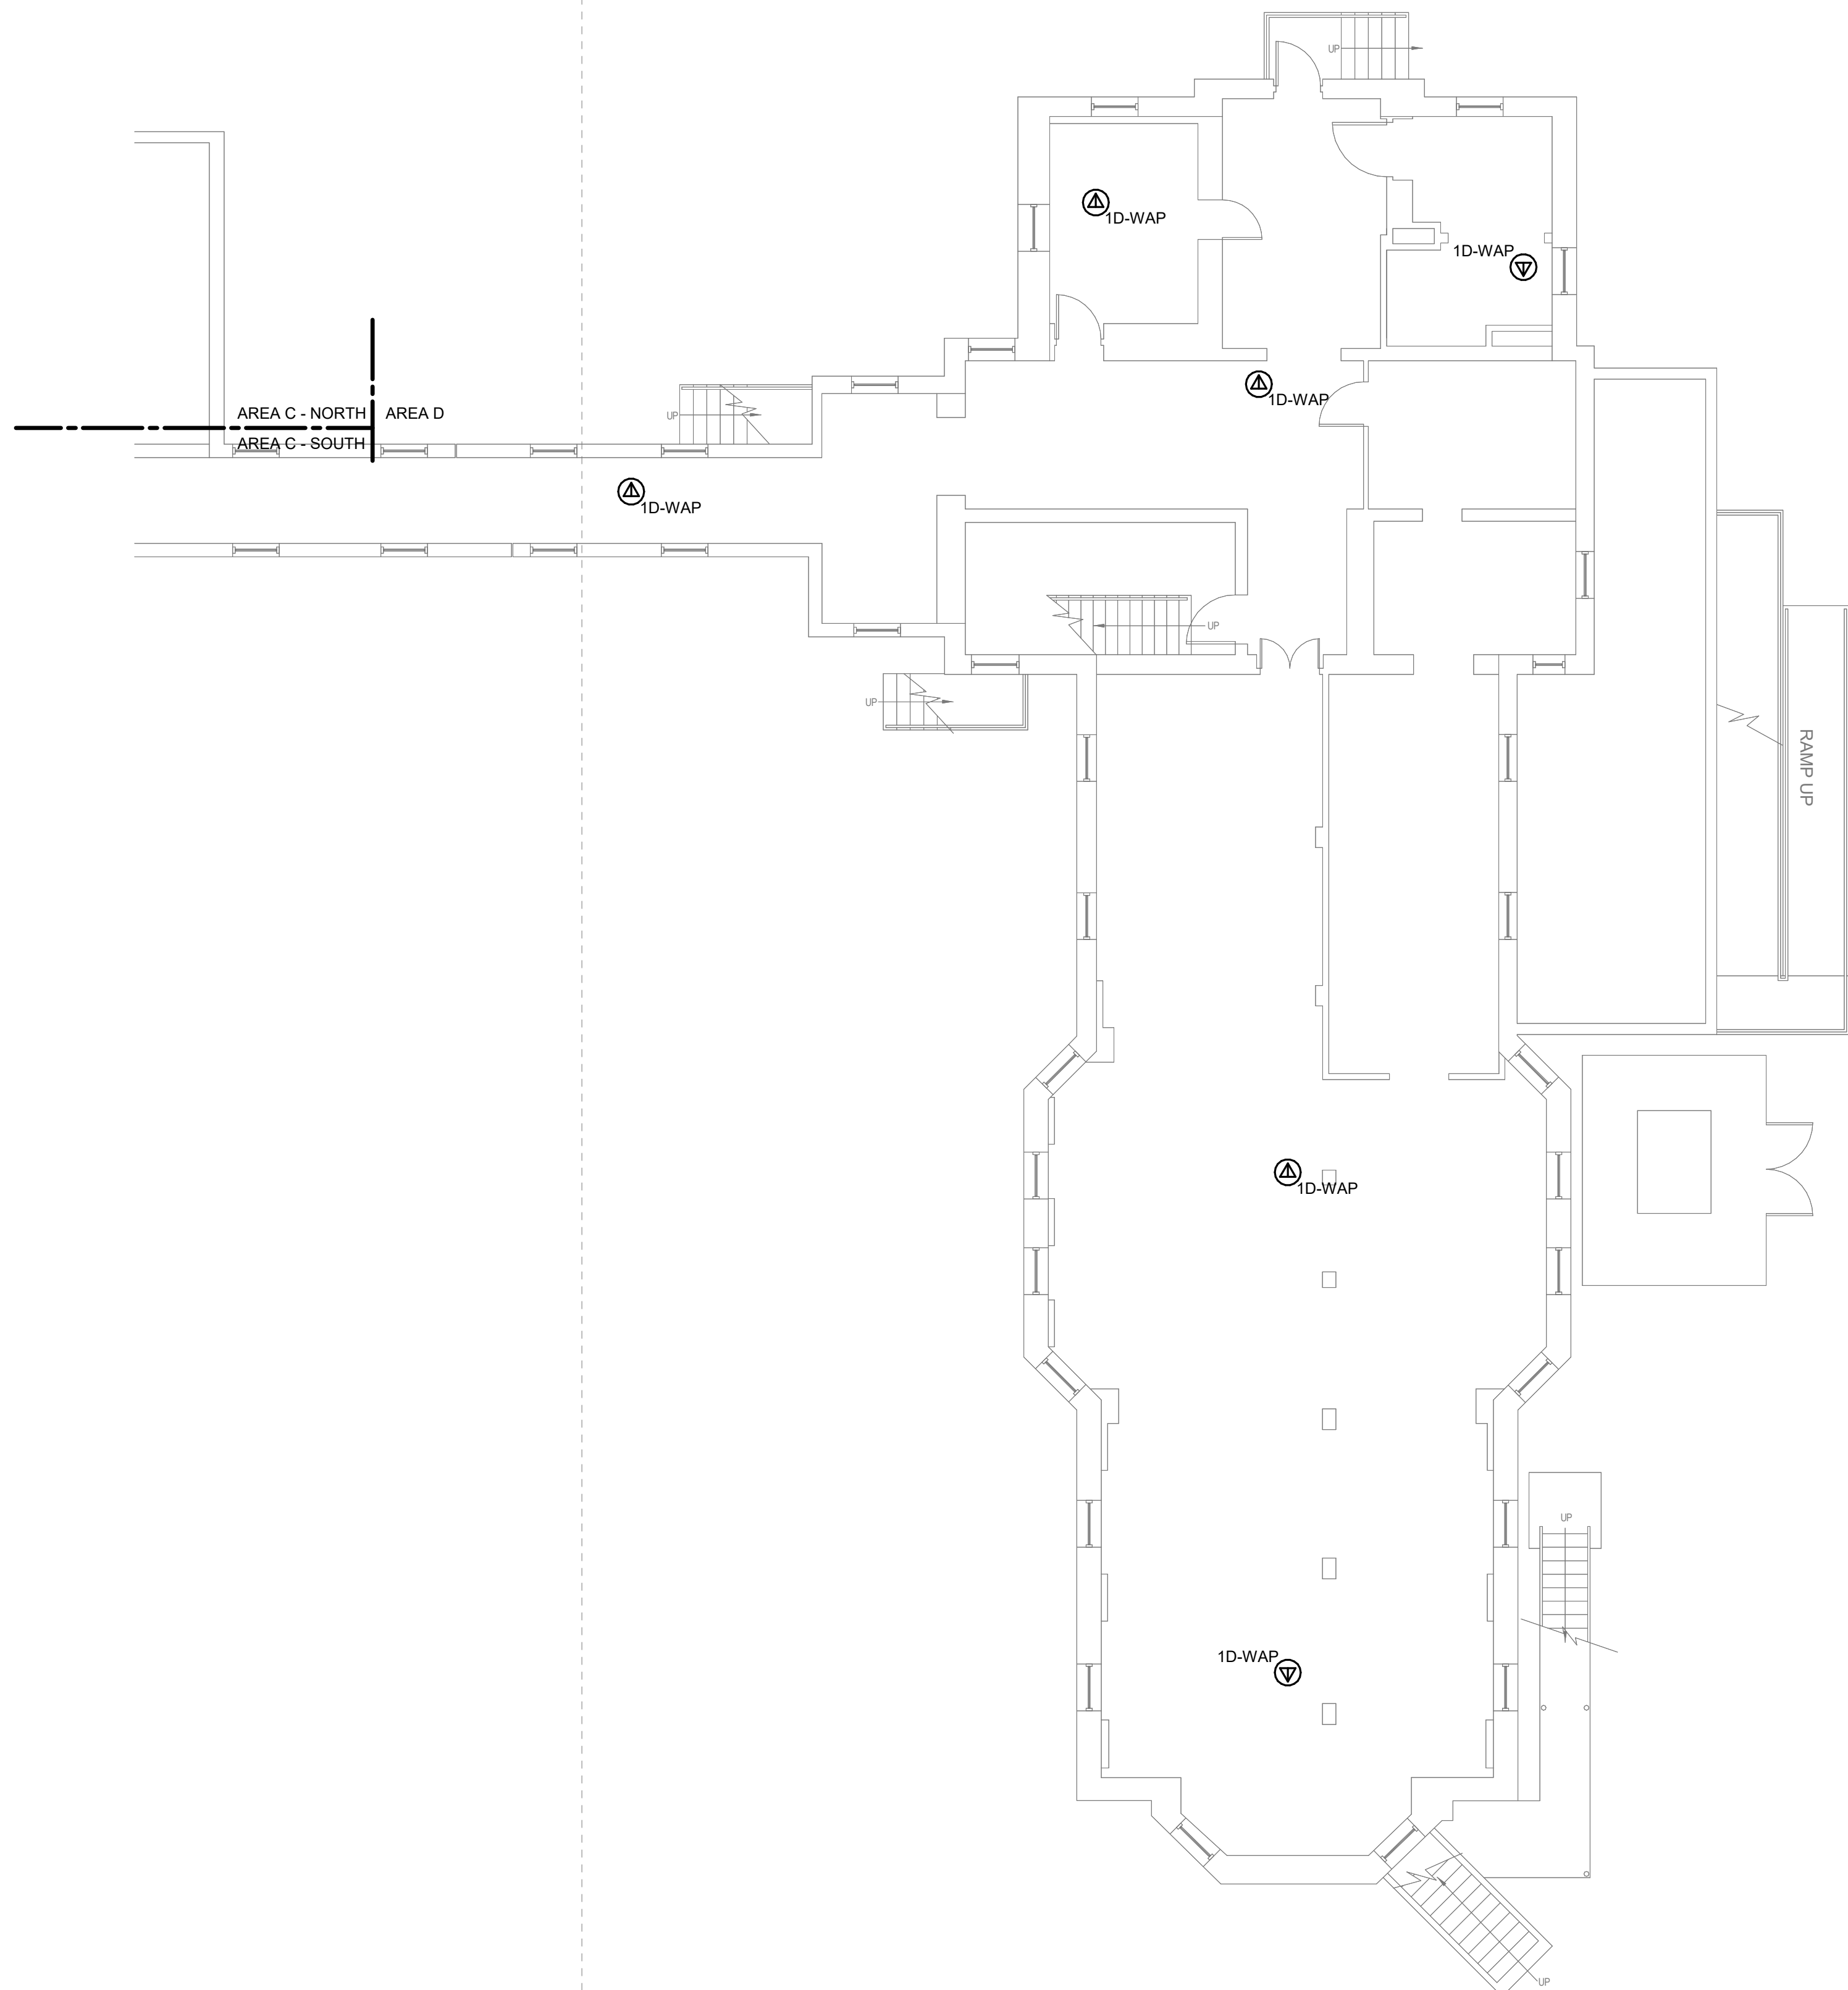

1 BUILDING 06 BASEMENT FLOOR PLAN - AREA D
1/8" = 1'-0"

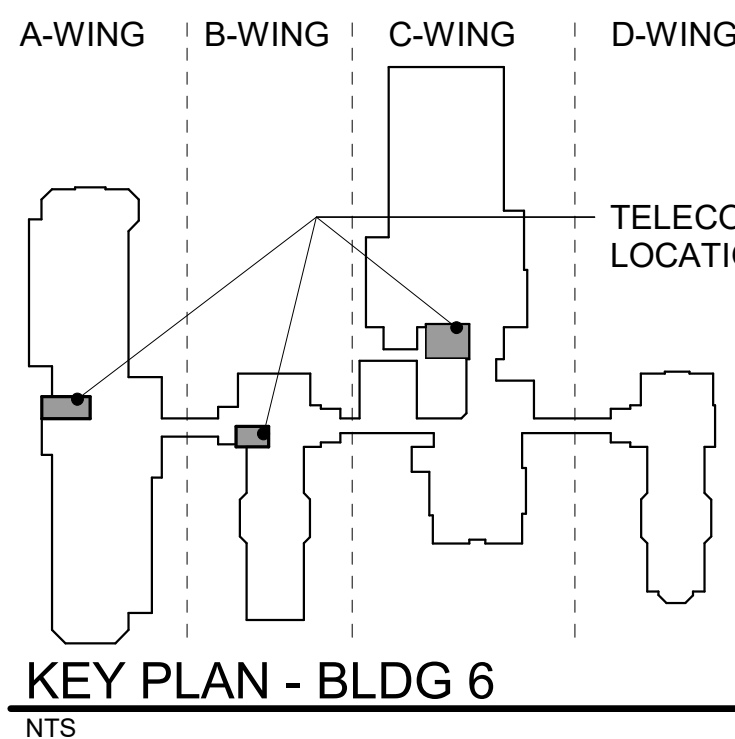

35% SCHEMATIC DESIGN SUBMISSION	5.17.21
65% DESIGN DEVELOPMENT SUBMISSION	6.15.21
65% DESIGN DEVELOPMENT RESUBMISSION	8.25.21
Revisions:	Date:


CONSULTANT



ARCHITECT/ENGINEER OF RECORD



STAMP

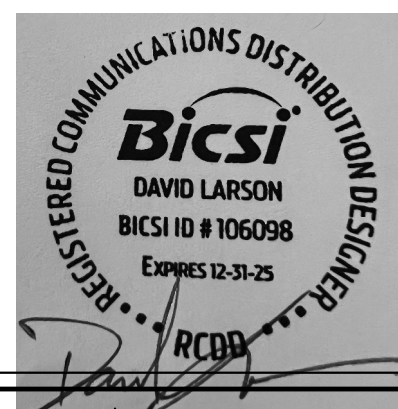

Office of
Construction
and Facilities
Management



U.S. Department
of Veterans Affairs

Drawing Title
BUILDING 06 BASEMENT PLAN - TECHNOLOGY -
AREA D

Approved:

Phase
FINAL BID DOCUMENTS

Sprinklered
FULLY SPRINKLERED

Project Title
EHRM INFRASTRUCTURE
UPGRADES - MILWAUKEE, WI

Location
5000 W. NATIONAL AVENUE, MILWAUKEE, WI

Issue Date
SEPTEMBER 05, 2025









Checked
PHINIE

Drawn
MAIBEJ

Project Number
695-21-700

Building Number
06

Drawing Number
06-TN100D

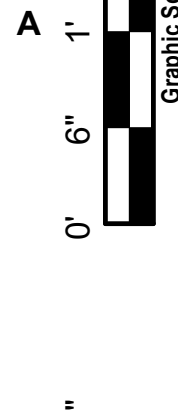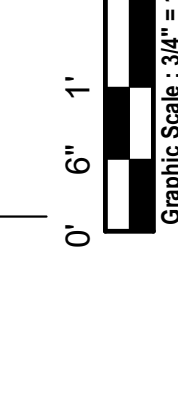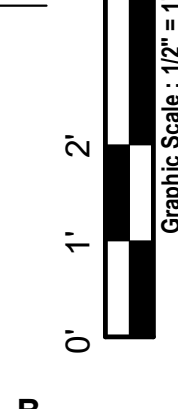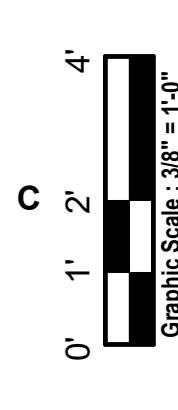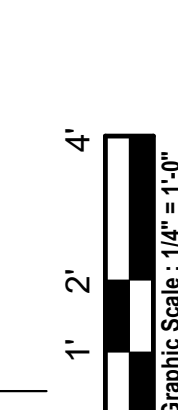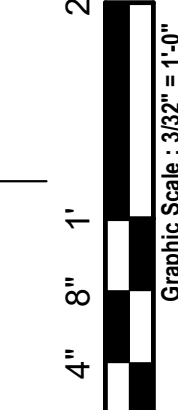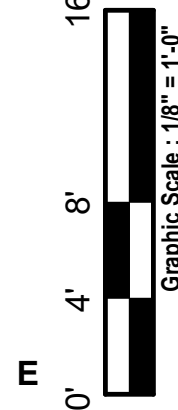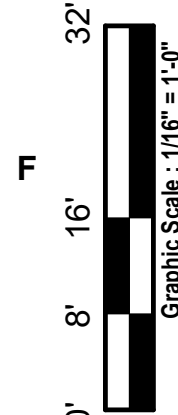

F

E

D

C

B

A

F

E

D


C

B

A

9/3/2025 3:55:13 PM


Autodesk Docs://OCFM East - Milwaukee EHRM (R24)VT24 18004375.03 VA Milwaukee C.M.

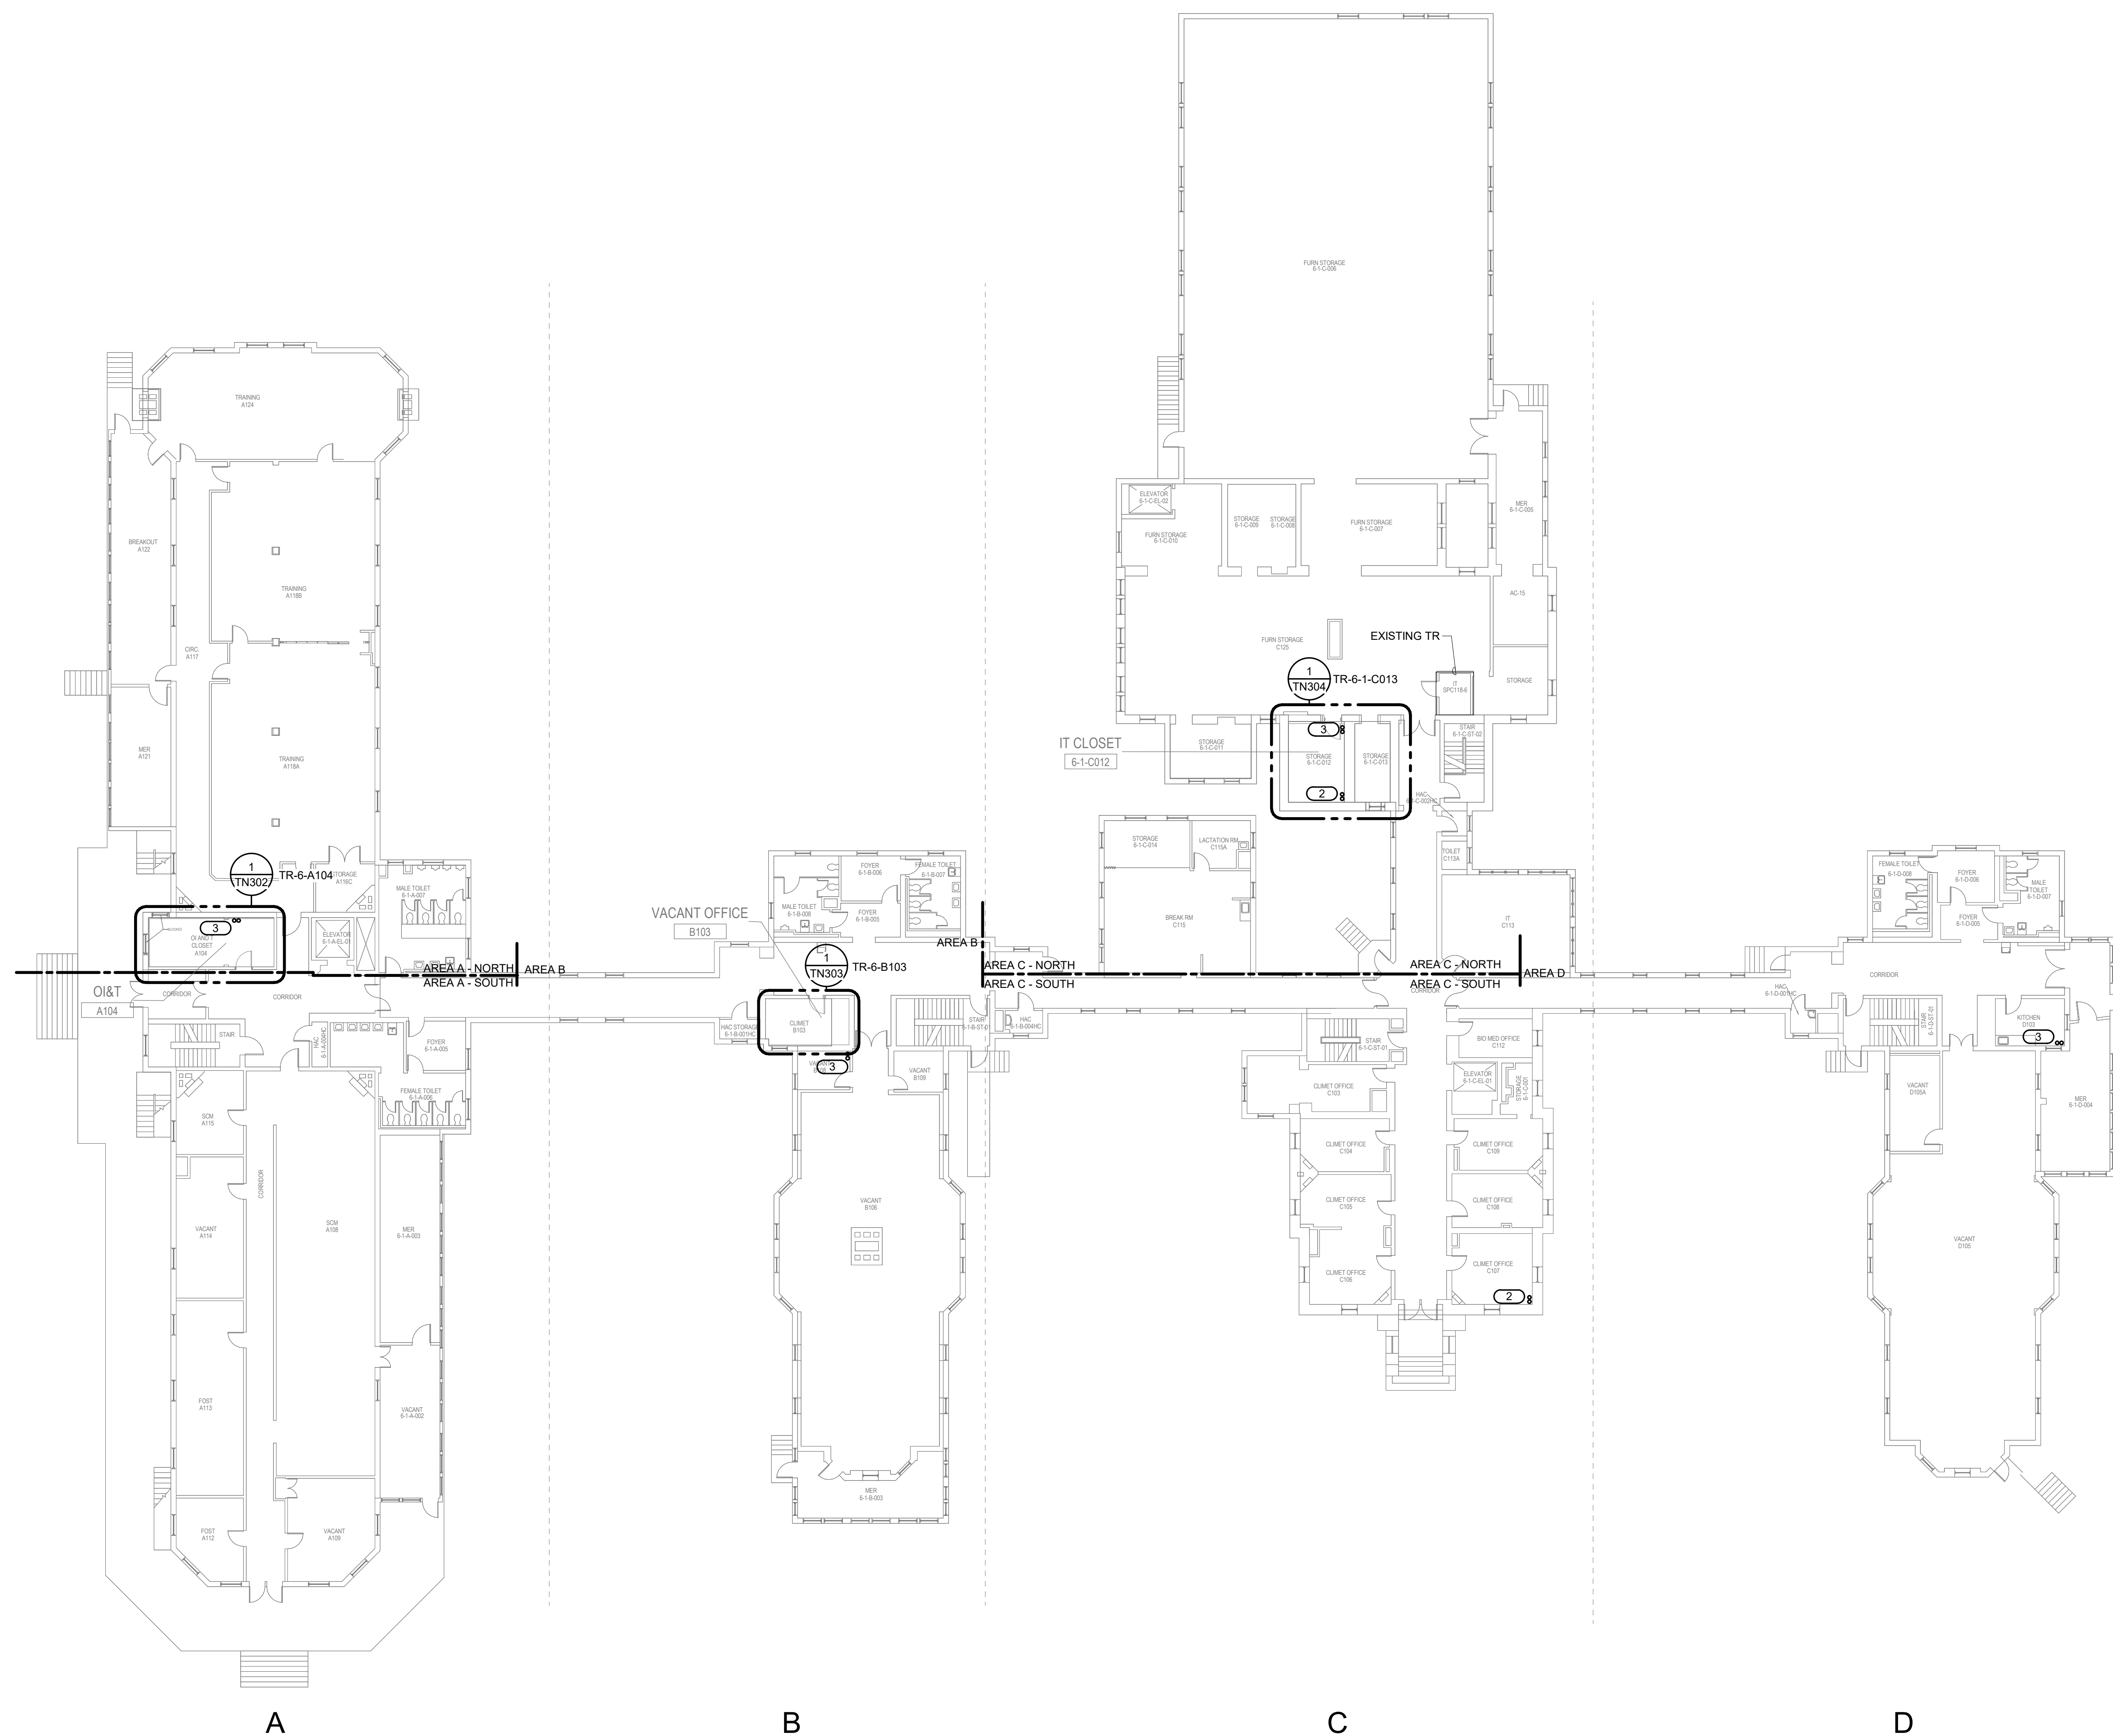




SHEET NOTES:	1. REMOVE ALL NETWORK CABLING TO POINTS OF TERMINATION IN ASSOCIATED DATA TELECOM WORK AREA. SEE SHEET T1001 FOR TELECOM ROOM LOCATIONS. 2. REFER TO CIVIL DRAWINGS AND T1003 FOR ADDITIONAL PATHWAY INFORMATION. 3. THESE DRAWINGS MAKE THE BEST ATTEMPT TO IDENTIFY EXISTING DATA DROPS/WORK AREA OUTLETS, AS LONG AS THE TOTAL NEWLY INSTALLED DATA DROP COUNT DOES NOT VARY +/- 10% IDENTIFIED ON THESE DRAWINGS, THE CONTRACTOR'S SCOPE SHALL BE MAINTAINED. 4. NEW WORK AREA OUTLETS SHALL BE LOCATED IN EXISTING BOXES. WORK AREA OUTLETS SHOWN ON THIS SHEET MAY NOT BE IN THE EXACT LOCATION AS IDENTIFIED.
--------------	---

KEYNOTES: #

1. LEG "B" BACKBONE CABLING PATH. REFER TO SITE PLAN ON SHEET T1003 FOR ADDITIONAL INFORMATION. CONDUIT SHALL BE MOUNTED TO THE EXTERIOR OF THE BUILDING AND ENTER THE BUILDING IN 1ST FLOOR CEILING SPACE.
2. TWO (2) 4" PATHWAYS TO LEVEL BELOW. REFER TO 06-TN100 FOR CONTINUATION.
3. TWO (2) 4" PATHWAYS TO LEVEL ABOVE. REFER TO 06-TN103 FOR CONTINUATION.

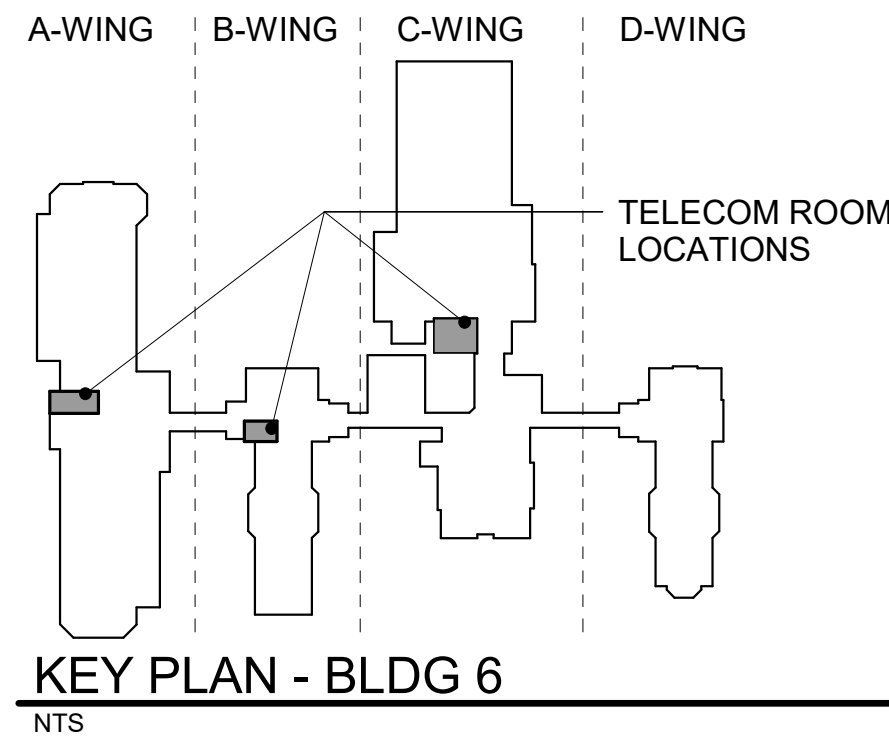



1 BUILDING 06 FIRST FLOOR OVERALL PLAN - TECHNOLOGY
1/16" = 1'-0"

  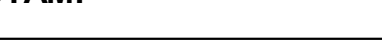
35% SCHEMATIC DESIGN SUBMISSION	5.17.21	CONSULTANT	 The FUTURE. Built Smarter. www.imegcorp.com 15 SUNNEN DRIVE SUITE 104 ST. LOUIS, MO 63143 P: 314.645.1132 F: 314.645.1173 PROJECT #18004375.03	ARCHITECT/ENGINEER OF RECORD	 Romanyk Consulting Focusing on what matters Romanyk Consulting Corp. www.romanykconsulting.com 3308 Preston Road, Suite 350-164, Plano, Texas 75093	 REGISTERED COMMUNICATIONS DISTRIBUTION OFFICIAL Bicsi DAVID LARSON BICSI ID # 106098 Expires 12-31-25 RCDO	Office of Construction and Facilities Management	VA U.S. Department of Veterans Affairs	Drawing Title BUILDING 06 FIRST FLOOR OVERALL PLAN - TECHNOLOGY	Phase FINAL BID DOCUMENTS	Project Title EHRM INFRASTRUCTURE UPGRADES - MILWAUKEE, WI	Project Number 695-21-700		
65% DESIGN DEVELOPMENT SUBMISSION	6.15.21								Building Number 06					
65% DESIGN DEVELOPMENT RESUBMISSION	8.25.21								Drawing Number 06-TN101					
Revisions:	Date:								Approved:	Sprinklered FULLY SPRINKLERED	Location 5000 W. NATIONAL AVENUE MILWAUKEE, WI	Issue Date SEPTEMBER 05, 2025	Checked PHINIE	Drawn MAIBEJ

1. REFER TO 1/7N400 FOR TECHNOLOGY ROUGH IN DETAIL.
2. ALL NETWORK CABLES ON THIS SHEET SHALL BE GENERAL IN TYPE, 19-104.
3. CONTRACTOR TO PROVIDE NEW J-HOOK ROUTES FOR ALL NEW CABLEING, J-HOOK SIZE AND QUANTITY TO BE PER MANUFACTURER RECOMMENDATION.
4. REFER TO T5000-T5009 FOR RISER DIAGRAMS.
5. REFER TO SHEET T4002 FOR PENETRATION DETAILS.

THESE DRAWINGS MAKE THE BEST ATTEMPT TO IDENTIFY EXISTING DATA DROPS/WORK AREAS. AS A RESULT, SOME NEWLY INSTALLED DATA DROP COUNTS DO NOT VARY +/- 10% IDENTIFIED ON THESE DRAWINGS. THE CONTRACTOR'S SCOPE SHALL BE CHANGED.

7. NEW WORK AREA OUTLETS SHALL BE LOCATED IN EXISTING BOXES. WORK AREA OUTLETS SHOWN ON THIS SHEET MAY NOT BE IN THE EXACT LOCATION AS IDENTIFIED.
8. CONTRACTOR TO INCLUDE AN ALLOWANCE FOR FUTURE INFORMATION OUTLETS IN THEIR PROPOSAL FOR THIS SHEET. FUTURE INFORMATION OUTLETS TO BE PROVIDED WILL BE DETERMINED BY THE VA AT A LATER DATE.

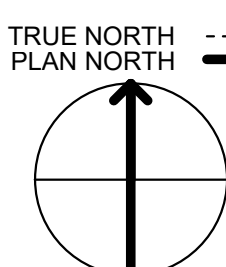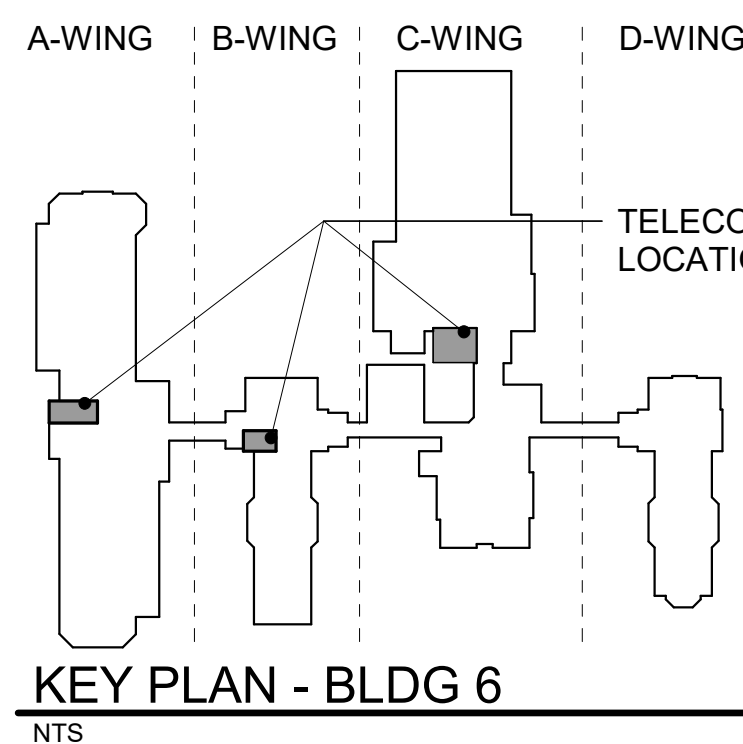

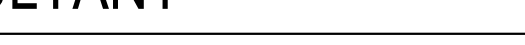35% SCHEMATIC DESIGN SUBMISSION	5.17.21	CONSULTANT	 IMEG THE FUTURE. Built Smarter. www.imegcorp.com 15 SUNNEN DRIVE SUITE 104 ST. LOUIS, MO 63143 P: 314.645.1132 F: 314.645.1173 PROJECT #18204372.03	ARCHITECT/ENGINEER OF RECORD	 Romanyk Consulting Focusing on what matters Romanyk Consulting Corp. www.romanykconsulting.com 3308 Preston Road, Suite 350-164, Plano, Texas 75093	STAMP		Office of Construction and Facilities Management	VA U.S. Department of Veterans Affairs	Drawing Title BUILDING 06 FIRST FLOOR PLAN - TECHNOLOGY - AREA A	Project Title EHRM INFRASTRUCTURE UPGRADES - MILWAUKEE, WI	Phase FINAL BID DOCUMENTS	Project Number 695-21-700
65% DESIGN DEVELOPMENT SUBMISSION	6.15.21									Building Number 06			
65% DESIGN DEVELOPMENT RESUBMISSION	8.25.21									Location 5000 W. NATIONAL AVENUE MILWAUKEE, WI	Drawing Number 06-TN101A		
										Issue Date SEPTEMBER 05, 2025	Checked PHINIE	Drawn MAIBEJ	
Revisions:	Date:												

F

E

D


C

B


A

9/2/2025 3:55:15 PM


Autodesk Docs\DCFM East - Milwaukee EHRM (R24)T24_1804375.03_VA Milwaukee_C.dwt

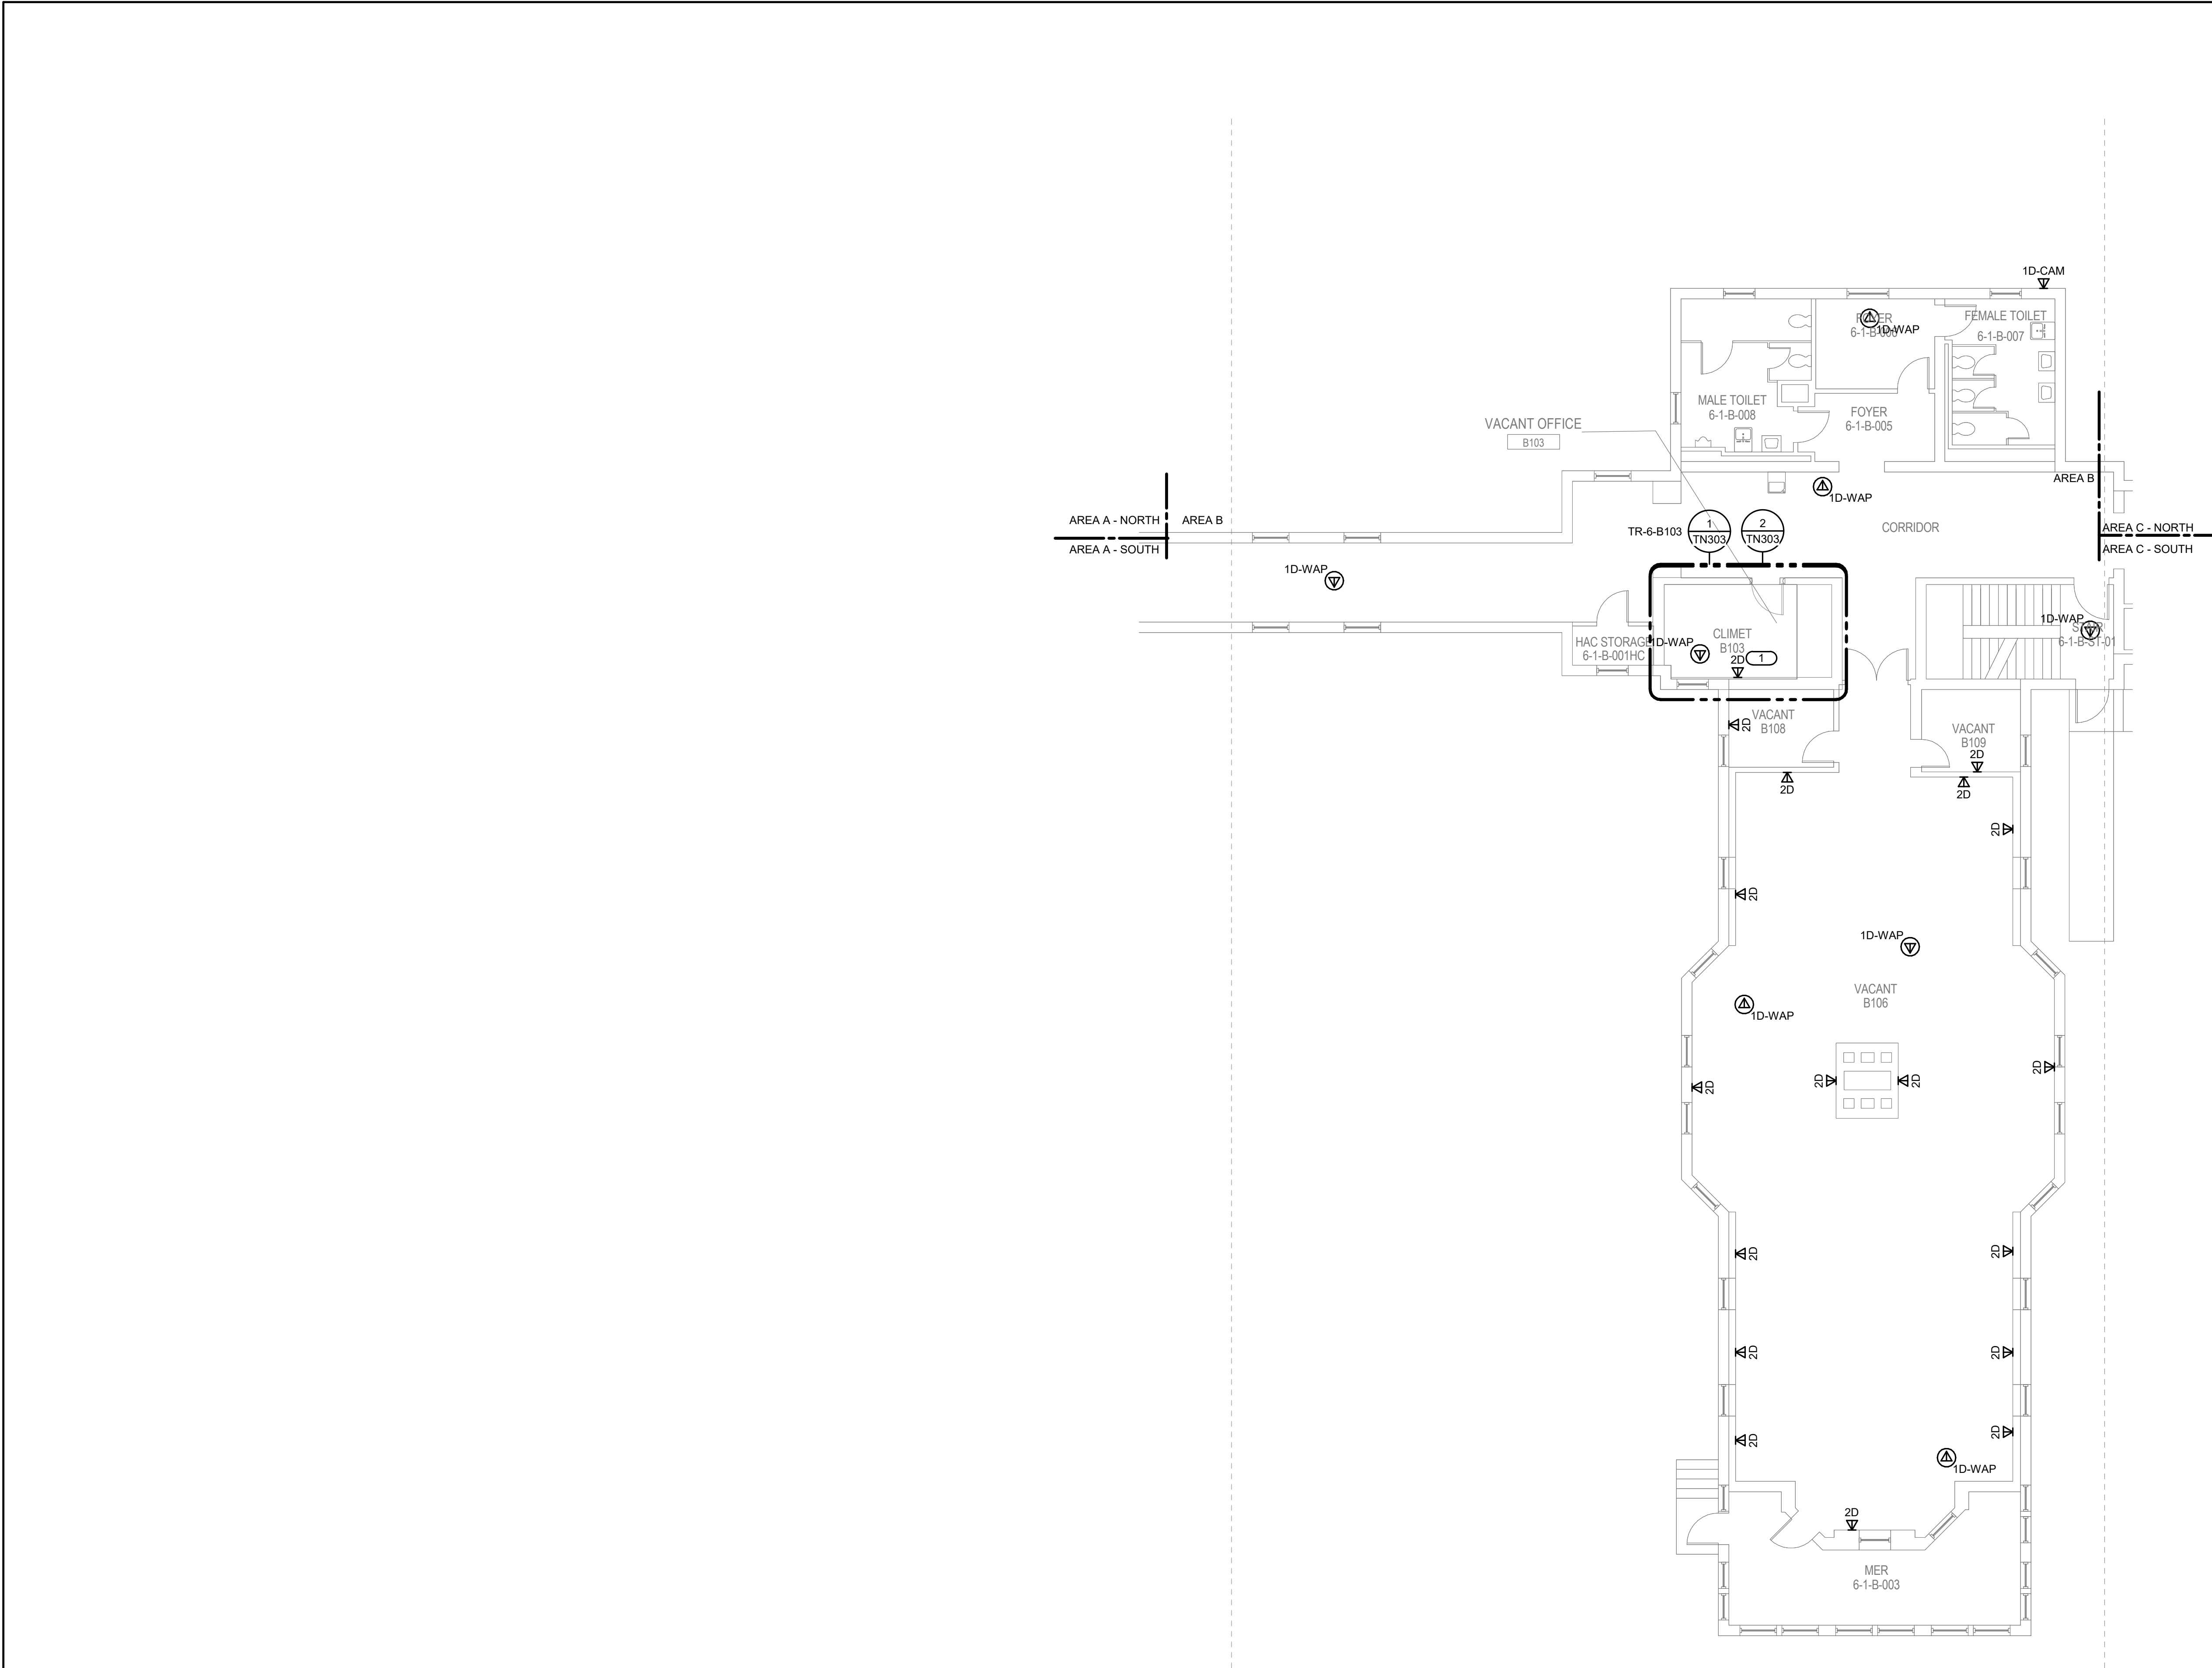

1 BUILDING 06 FIRST FLOOR PLAN - TECHNOLOGY - AREA B
1/8" = 1'-0"

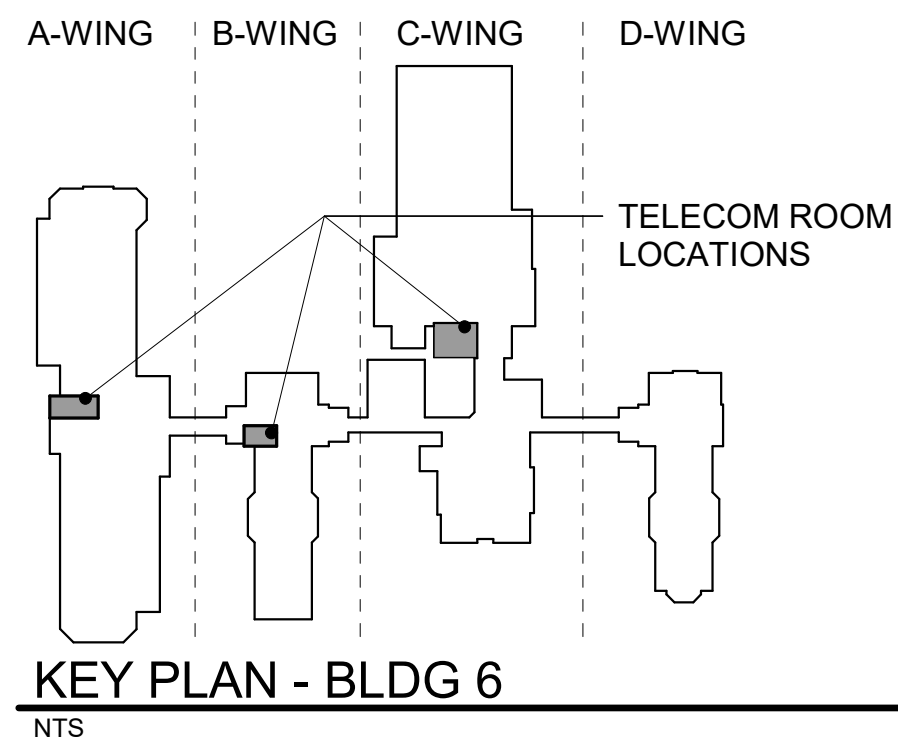

- SHEET NOTES:**
1. REFER TO 1/TN400 FOR TECHNOLOGY ROUGH IN DETAIL.
 2. ALL NETWORK CABLES ON THIS SHEET SHALL TERMINATE IN TS-6-B103.
 3. CONTRACTOR TO PROVIDE NEW J-HOOK ROUTES FOR ALL NEW CABLING. J-HOOK SIZE AND QUANTITY TO BE PER MANUFACTURER RECOMMENDATIONS.
 4. REFER TO TN500-TN509 FOR RISER DIAGRAMS.
 5. REFER TO SHEET TN402 FOR PENETRATION DETAILS.
 6. THESE DRAWINGS MAKE THE BEST ATTEMPT TO IDENTIFY EXISTING DATA DROPS/WORK AREA OUTLETS. AS LONG AS THE TOTAL NEWLY INSTALLED DATA DROP COUNT DOES NOT VARY +/- 10% IDENTIFIED ON THESE DRAWINGS, THE CONTRACTOR'S SCOPE SHALL BE UNCHANGED.
 7. NEW WORK AREA OUTLETS SHALL BE LOCATED IN EXISTING BOXES. WORK AREA OUTLETS SHOWN ON THIS SHEET MAY NOT BE IN THE EXACT LOCATION AS IDENTIFIED.
 8. CONTRACTOR TO INCLUDE AN ALLOWANCE FOR 10% ADDITIONAL 2-PORTS CAT6A INFORMATION OUTLETS IN THEIR PROPOSAL FOR THIS SHEET. FUTURE INFORMATION OUTLET LOCATIONS WILL BE DETERMINED BY THE VA AT A LATER DATE.
- KEYNOTES:**
1. JCI PACS PANEL LOCATION. GC TO COORDINATE EXACT LOCATION AND HEIGHT WITH COR TO RE-CONNECT TO SWITCHRACK TE IN SAME ROOM WITH CAT6A CABLE AS NECESSARY.

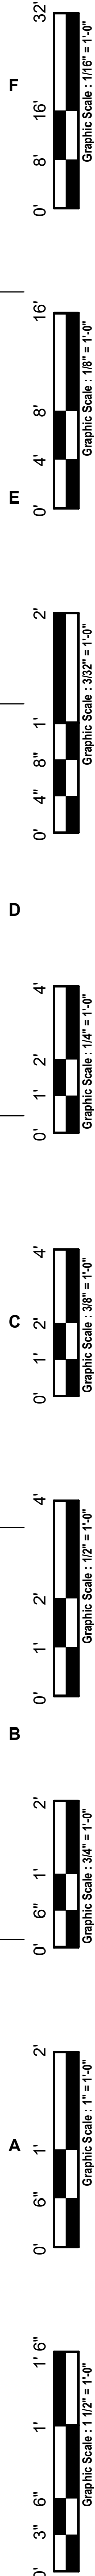

35% SCHEMATIC DESIGN SUBMISSION	5.17.21
65% DESIGN DEVELOPMENT SUBMISSION	6.15.21
65% DESIGN DEVELOPMENT RESUBMISSION	8.25.21
Revisions:	Date:

CONSULTANT

IMEG

15 SUNNEN DRIVE
SUITE 104
ST. LOUIS, MO 63143
P: 314.645.1132 F: 314.645.1173
PROJECT #18004375.03

ARCHITECT/ENGINEER OF RECORD

Romanyk Consulting
Focusing on what matters

Romanyk Consulting Corp. www.romanykconsulting.com
3308 Preston Road, Suite 350-164, Plano, Texas 75093

STAMP

Bicsi
DAVID LARSON
BICS1 ID # 106098
EXPIRES 12-31-25

Office of
Construction
and Facilities
Management

VA U.S. Department
of Veterans Affairs

Drawing Title
BUILDING 06 FIRST FLOOR PLAN - TECHNOLOGY
- AREA B

Approved:

Phase
FINAL BID DOCUMENTS

Sprinklered
FULLY SPRINKLERED

Project Title
EHRM INFRASTRUCTURE
UPGRADES - MILWAUKEE, WI

Location
5000 W. NATIONAL AVENUE MILWAUKEE, WI

Issue Date
SEPTEMBER 05, 2025

Checked
PHINIE

Drawn
MAIBEJ

Project Number
695-21-700

Building Number
06

Drawing Number
06-TN101B

F

E


D

C


B

A

9/3/2025 3:55:17 PM
Autodesk Docs\DCRM\East - Milwaukee EHRM (R24)T24_1804375.03_VA MilWEHRM_C.rvt

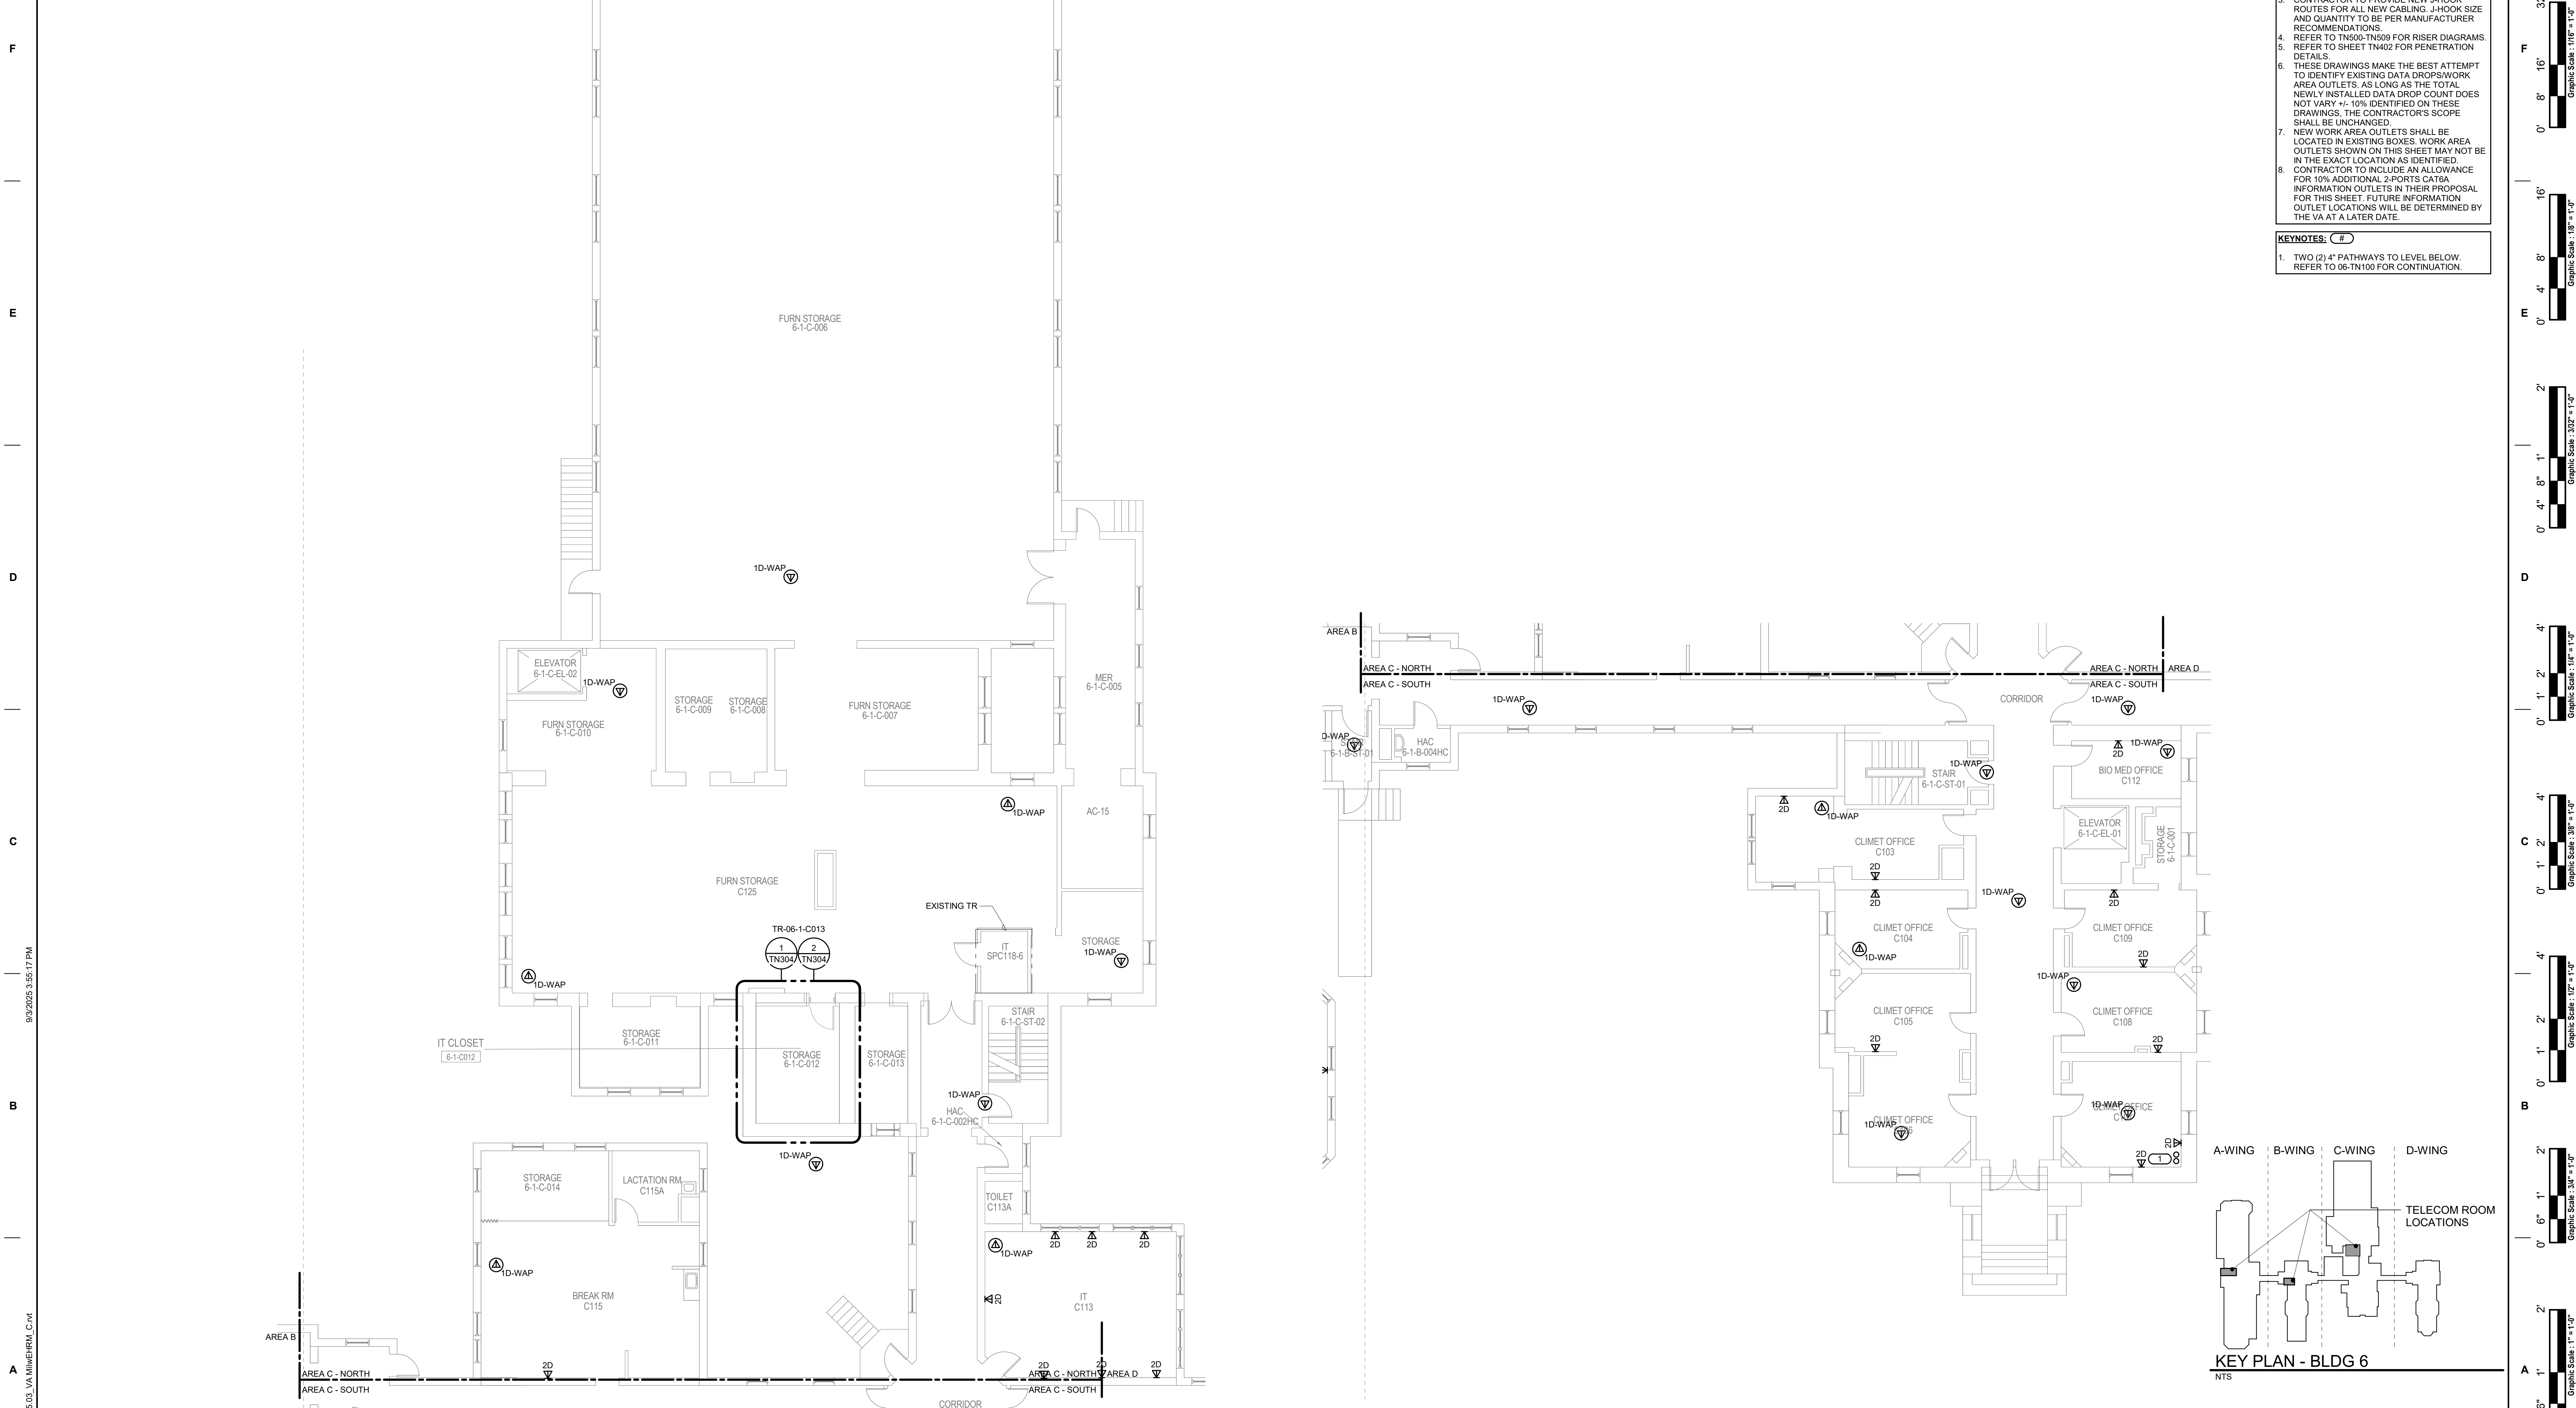


- SHEET NOTES:**
1. REFER TO 1/TN400 FOR TECHNOLOGY ROUGH IN DETAIL.
 2. ALL NETWORK CABLES ON THIS SHEET SHALL TERMINATE IN TS-6-1-C-013.
 3. CONTRACTOR TO PROVIDE NEW J-HOOK ROUTES FOR ALL NEW CABLING. J-HOOK SIZE AND QUANTITY TO BE PER MANUFACTURER RECOMMENDATIONS.
 4. REFER TO TN500-TN509 FOR RISER DIAGRAMS.
 5. REFER TO SHEET TN402 FOR PENETRATION DETAILS.
 6. THESE DRAWINGS MAKE THE BEST ATTEMPT TO IDENTIFY EXISTING DATA DROPS/WORK AREA OUTLETS. AS LONG AS THE TOTAL NEWLY INSTALLED DATA DROP COUNT DOES NOT VARY +/- 10% IDENTIFIED ON THESE DRAWINGS, THE CONTRACTOR'S SCOPE SHALL BE UNCHANGED.
 7. NEW WORK AREA OUTLETS SHALL BE LOCATED IN EXISTING BOXES. WORK AREA OUTLETS SHOWN ON THIS SHEET MAY NOT BE IN THE EXACT LOCATION AS IDENTIFIED.
 8. CONTRACTOR TO INCLUDE AN ALLOWANCE FOR 10% ADDITIONAL 2-PORTS CAT6A INFORMATION OUTLETS IN THEIR PROPOSAL FOR THIS SHEET. FUTURE INFORMATION OUTLET LOCATIONS WILL BE DETERMINED BY THE VA AT A LATER DATE.
- KEYNOTES: C #**
1. TWO (2) 4" PATHWAYS TO LEVEL BELOW. REFER TO 06-TN100 FOR CONTINUATION.

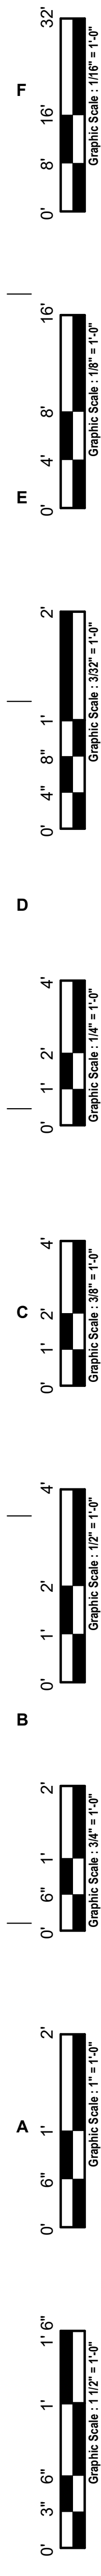

1 BUILDING 06 FIRST FLOOR PLAN - TECHNOLOGY - AREA C NORTH
1/8" = 1'-0"

2 BUILDING 06 FIRST FLOOR PLAN - TECHNOLOGY - AREA C SOUTH
1/8" = 1'-0"

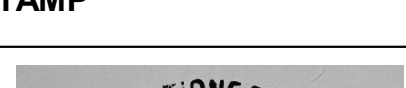35% SCHEMATIC DESIGN SUBMISSION		5.17.21	CONSULTANT		ARCHITECT/ENGINEER OF RECORD		STAMP		Office of Construction and Facilities Management		Drawing Title BUILDING 06 FIRST FLOOR PLAN - TECHNOLOGY - AREA C		Phase FINAL BID DOCUMENTS		Project Title EHRM INFRASTRUCTURE UPGRADES - MILWAUKEE, WI		Project Number 695-21-700	
65% DESIGN DEVELOPMENT SUBMISSION		6.15.21	 15 SUNNEN DRIVE SUITE 104 ST. LOUIS, MO 63143 P: 314.645.1132 F: 314.645.1173 PROJECT #18004375.03		 Romanyk Consulting Focusing on what matters Romanyk Consulting Corp. www.romanykconsulting.com 3308 Preston Road, Suite 350-164, Plano, Texas 75093		 RCDB		VA U.S. Department of Veterans Affairs		Approved:		Sprinklered FULLY SPRINKLERED		Location 5000 W. NATIONAL AVENUE MILWAUKEE, WI		Building Number 06	
65% DESIGN DEVELOPMENT RESUBMISSION		8.25.21															Drawing Number 06-TN101C	
Revisions:		Date:																

F

E

D


C

B

A

9/2/2025 3:55:19 PM

Autodesk Docs\DCFM East - Milwaukee EHRM (R24)T24_1804375.03_VA MilWEHRM_C.dwt

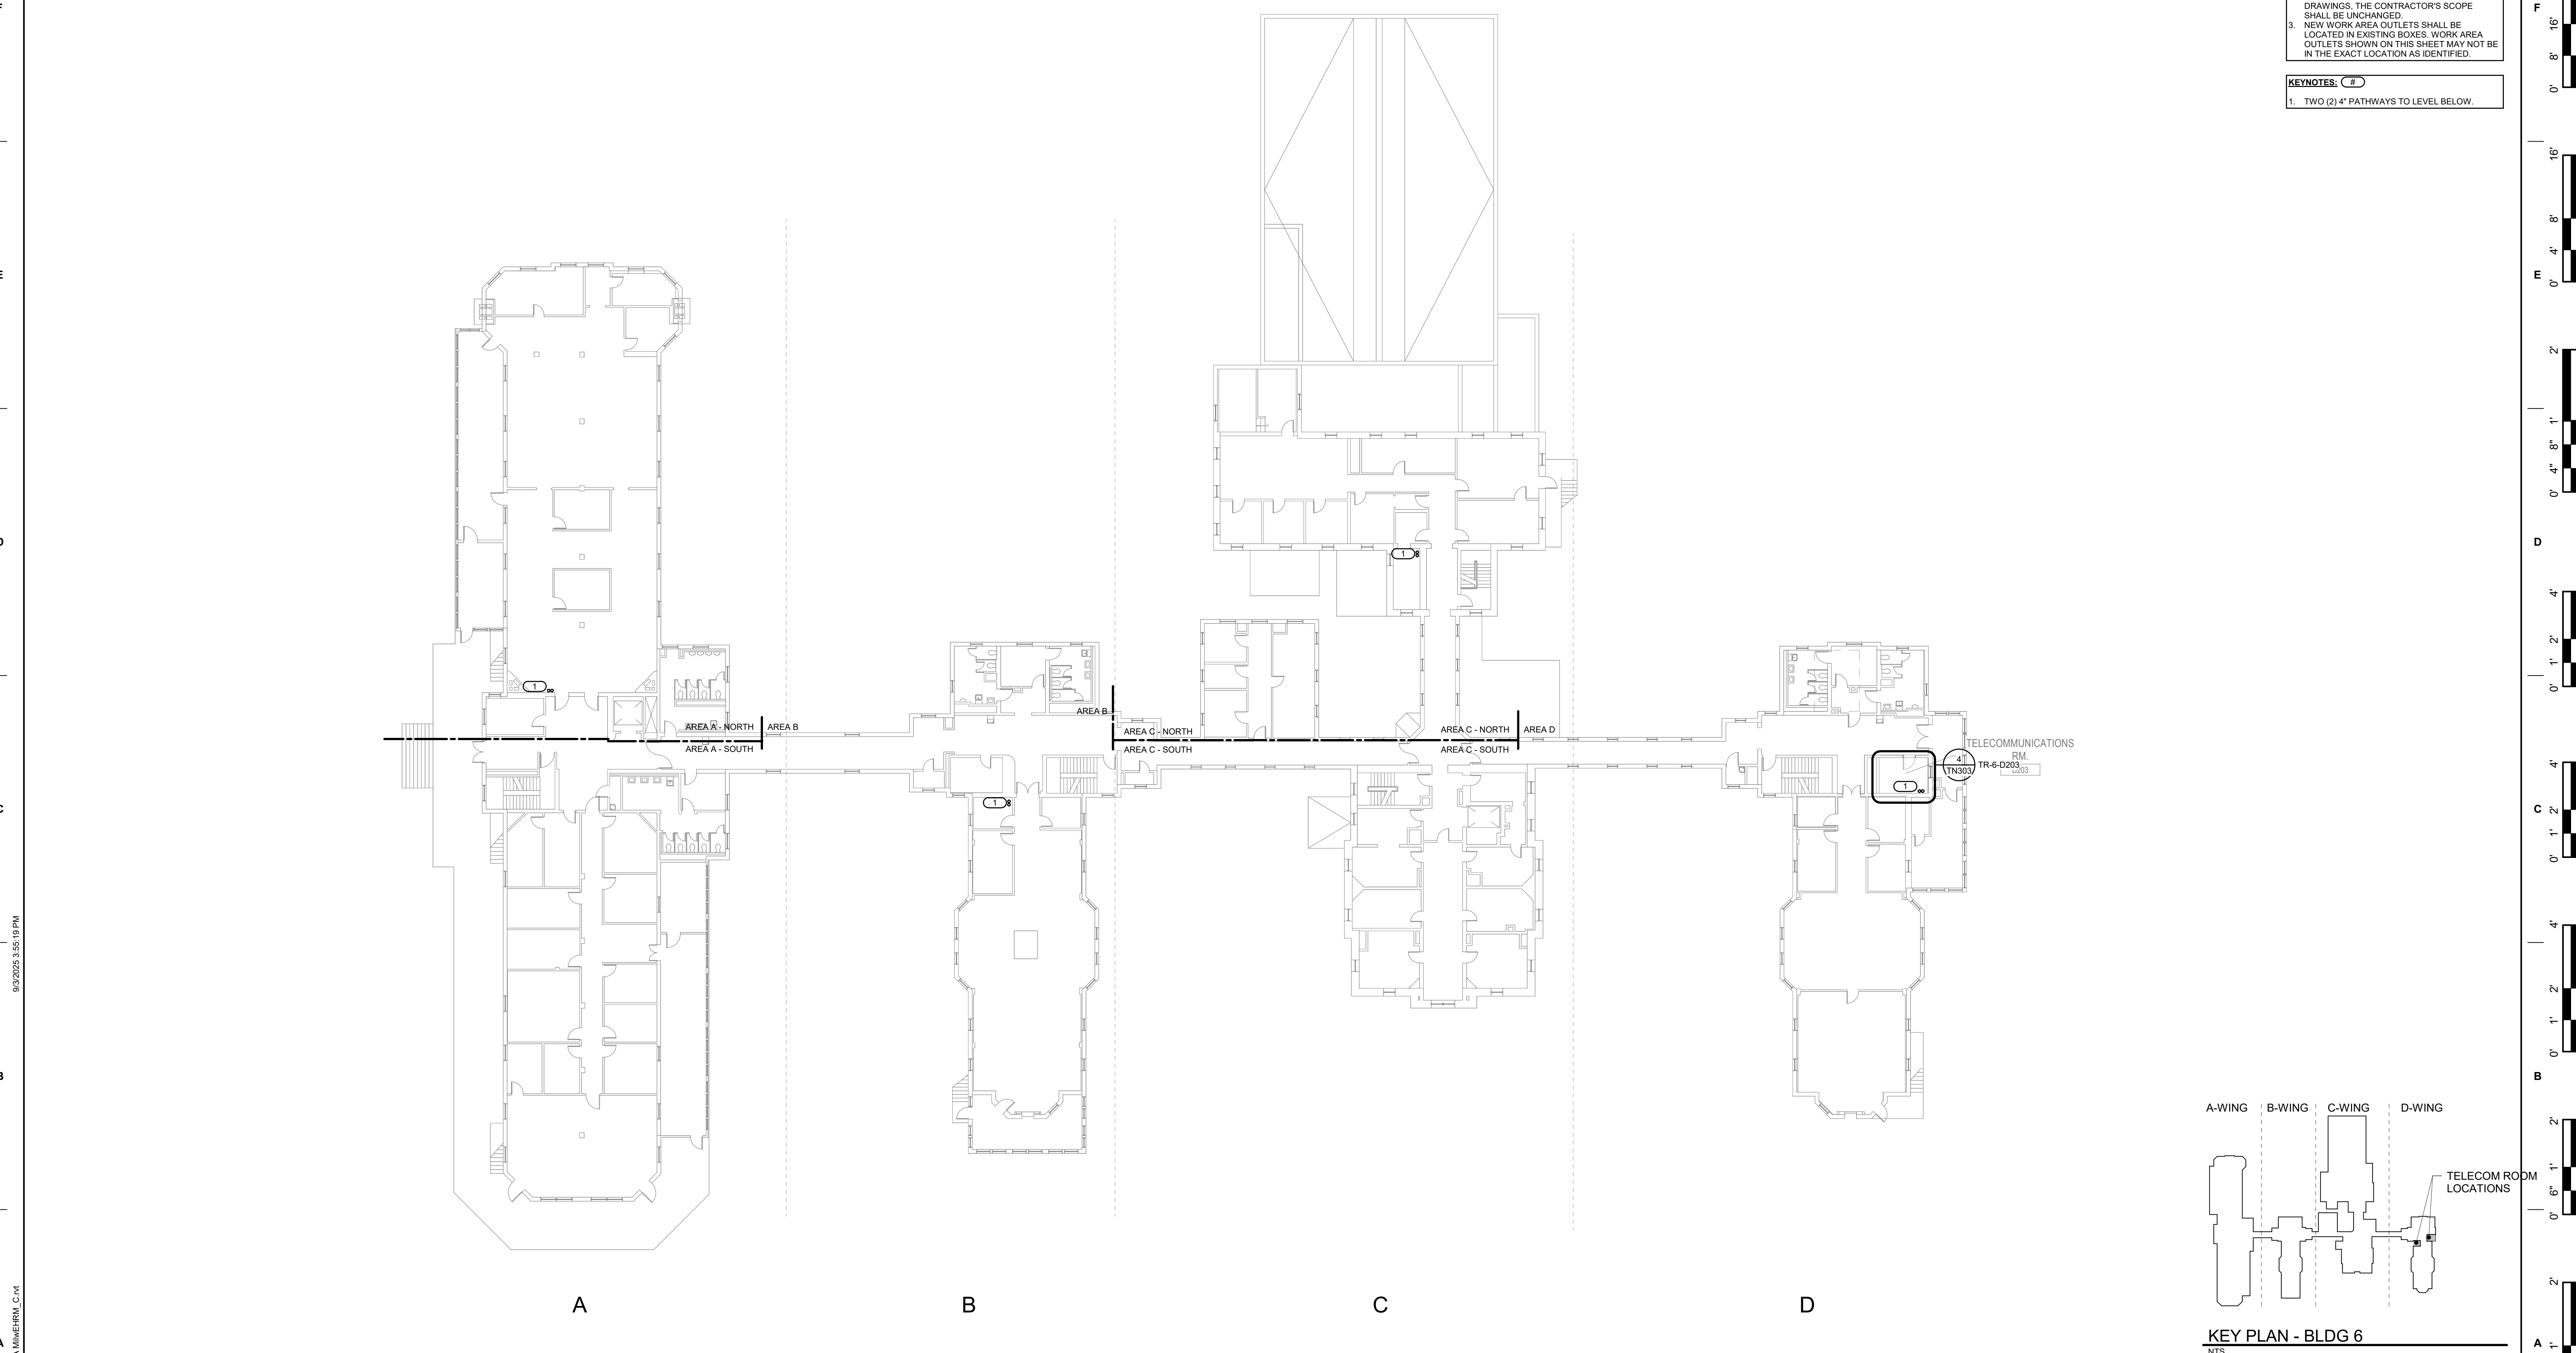


SHEET NOTES:

1. REMOVE ALL NETWORK CABLING TO POINTS OF TERMINATION IN ASSOCIATED DATA CLOSET. REFER TO FLOOR PLANS AND SHEET T1001 FOR TR ROOM LOCATIONS.
2. THESE DRAWINGS MAKE THE BEST ATTEMPT TO IDENTIFY EXISTING DATA DROPS/WORK AREA OUTLETS. AS LONG AS THE TOTAL NEWLY INSTALLED DATA DROP COUNT DOES NOT VARY +/- 10% IDENTIFIED ON THESE DRAWINGS, THE CONTRACTOR'S SCOPE SHALL BE UNCHANGED.
3. NEW WORK AREA OUTLETS SHALL BE LOCATED IN EXISTING BOXES. WORK AREA OUTLETS SHOWN ON THIS SHEET MAY NOT BE IN THE EXACT LOCATION AS IDENTIFIED.

KEYNOTES: C #

1. TWO (2) 4" PATHWAYS TO LEVEL BELOW.

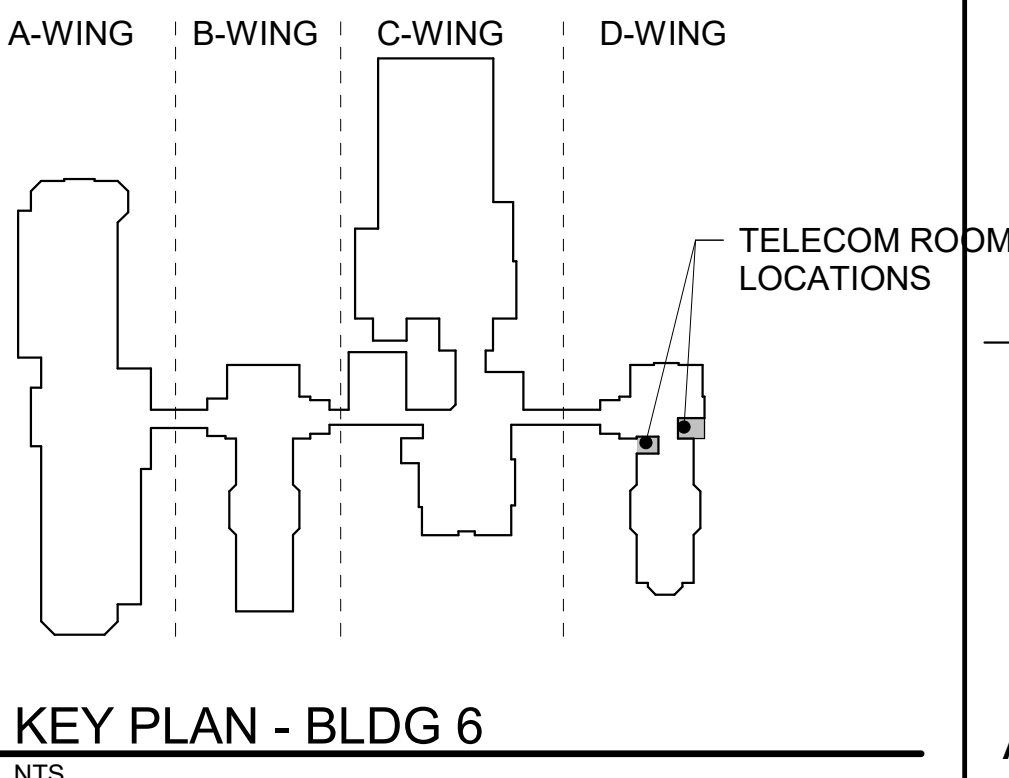

1 BUILDING 06 SECOND FLOOR OVERALL PLAN - TECHNOLOGY
1/16" = 1'-0"

35% SCHEMATIC DESIGN SUBMISSION	5.17.21
65% DESIGN DEVELOPMENT SUBMISSION	6.15.21
65% DESIGN DEVELOPMENT RESUBMISSION	8.25.21
Revisions:	Date:

CONSULTANT

IMEG

THE FUTURE IS IT SERVICES
15 SUNNEN DRIVE
SUITE 104
ST. LOUIS, MO 63143
P: 314.645.1132 F: 314.645.1173
PROJECT #18004375.03

ARCHITECT/ENGINEER OF RECORD

Romanyk Consulting
Focusing on what matters

Romanyk Consulting Corp. www.romanykconsulting.com
3308 Preston Road, Suite 350-164, Plano, Texas 75093

STAMP

Bicsi
DAVID LARSON
BICS1 ID # 106098
EXPIRES 12-31-25
REGISTERED COMMUNICATIONS DISTRIBUTION DESIGNER
RCDD

Office of
Construction
and Facilities
Management

VA U.S. Department
of Veterans Affairs

Drawing Title
**BUILDING 06 SECOND FLOOR OVERALL PLAN -
TECHNOLOGY**

Approved:

Phase
FINAL BID DOCUMENTS

Sprinklered
FULLY SPRINKLERED

Project Title
**EHRM INFRASTRUCTURE
UPGRADES - MILWAUKEE, WI**

Location
5000 W. NATIONAL AVENUE MILWAUKEE, WI

Issue Date
SEPTEMBER 05, 2025

Checked
PHINIE

Drawn
MAIBEJ

Project Number
695-21-700

Building Number
06

Drawing Number
06-TN102

F

E

D

C


B

A



9/3/2025 3:55:22 PM

Autodesk Docs\DCFM East - Milwaukee EHRM (R24)T24_1804375\03_VA MilwEHRM_C.dwt

- SHEET NOTES:**
1. REFER TO 1/TN400 FOR TECHNOLOGY ROUGH IN DETAIL.
 2. ALL NETWORK CABLES ON THIS SHEET SHALL TERMINATE IN TS-6-0203.
 3. CONTRACTOR TO PROVIDE NEW J-HOOK ROUTES FOR ALL NEW CABLING. J-HOOK SIZE AND QUANTITY TO BE PER MANUFACTURER RECOMMENDATIONS.
 4. REFER TO TN500-TN509 FOR RISER DIAGRAMS.
 5. REFER TO SHEET TN402 FOR PENETRATION DETAILS.
 6. THESE DRAWINGS MAKE THE BEST ATTEMPT TO IDENTIFY EXISTING DATA DROPS/WORK AREA OUTLETS. AS LONG AS THE TOTAL NEWLY INSTALLED DATA DROP COUNT DOES NOT VARY +/- 10% IDENTIFIED ON THESE DRAWINGS, THE CONTRACTOR'S SCOPE SHALL BE UNCHANGED.
 7. NEW WORK AREA OUTLETS SHALL BE LOCATED IN EXISTING BOXES. WORK AREA OUTLETS SHOWN ON THIS SHEET MAY NOT BE IN THE EXACT LOCATION AS IDENTIFIED.
 8. CONTRACTOR TO INCLUDE AN ALLOWANCE FOR 10% ADDITIONAL 2-PORTS CAT6A INFORMATION OUTLETS IN THEIR PROPOSAL FOR THIS SHEET. FUTURE INFORMATION OUTLET LOCATIONS WILL BE DETERMINED BY THE VA AT A LATER DATE.
- KEYNOTES:** C #
1. TWO (2) 4" PATHWAYS TO LEVEL BELOW.

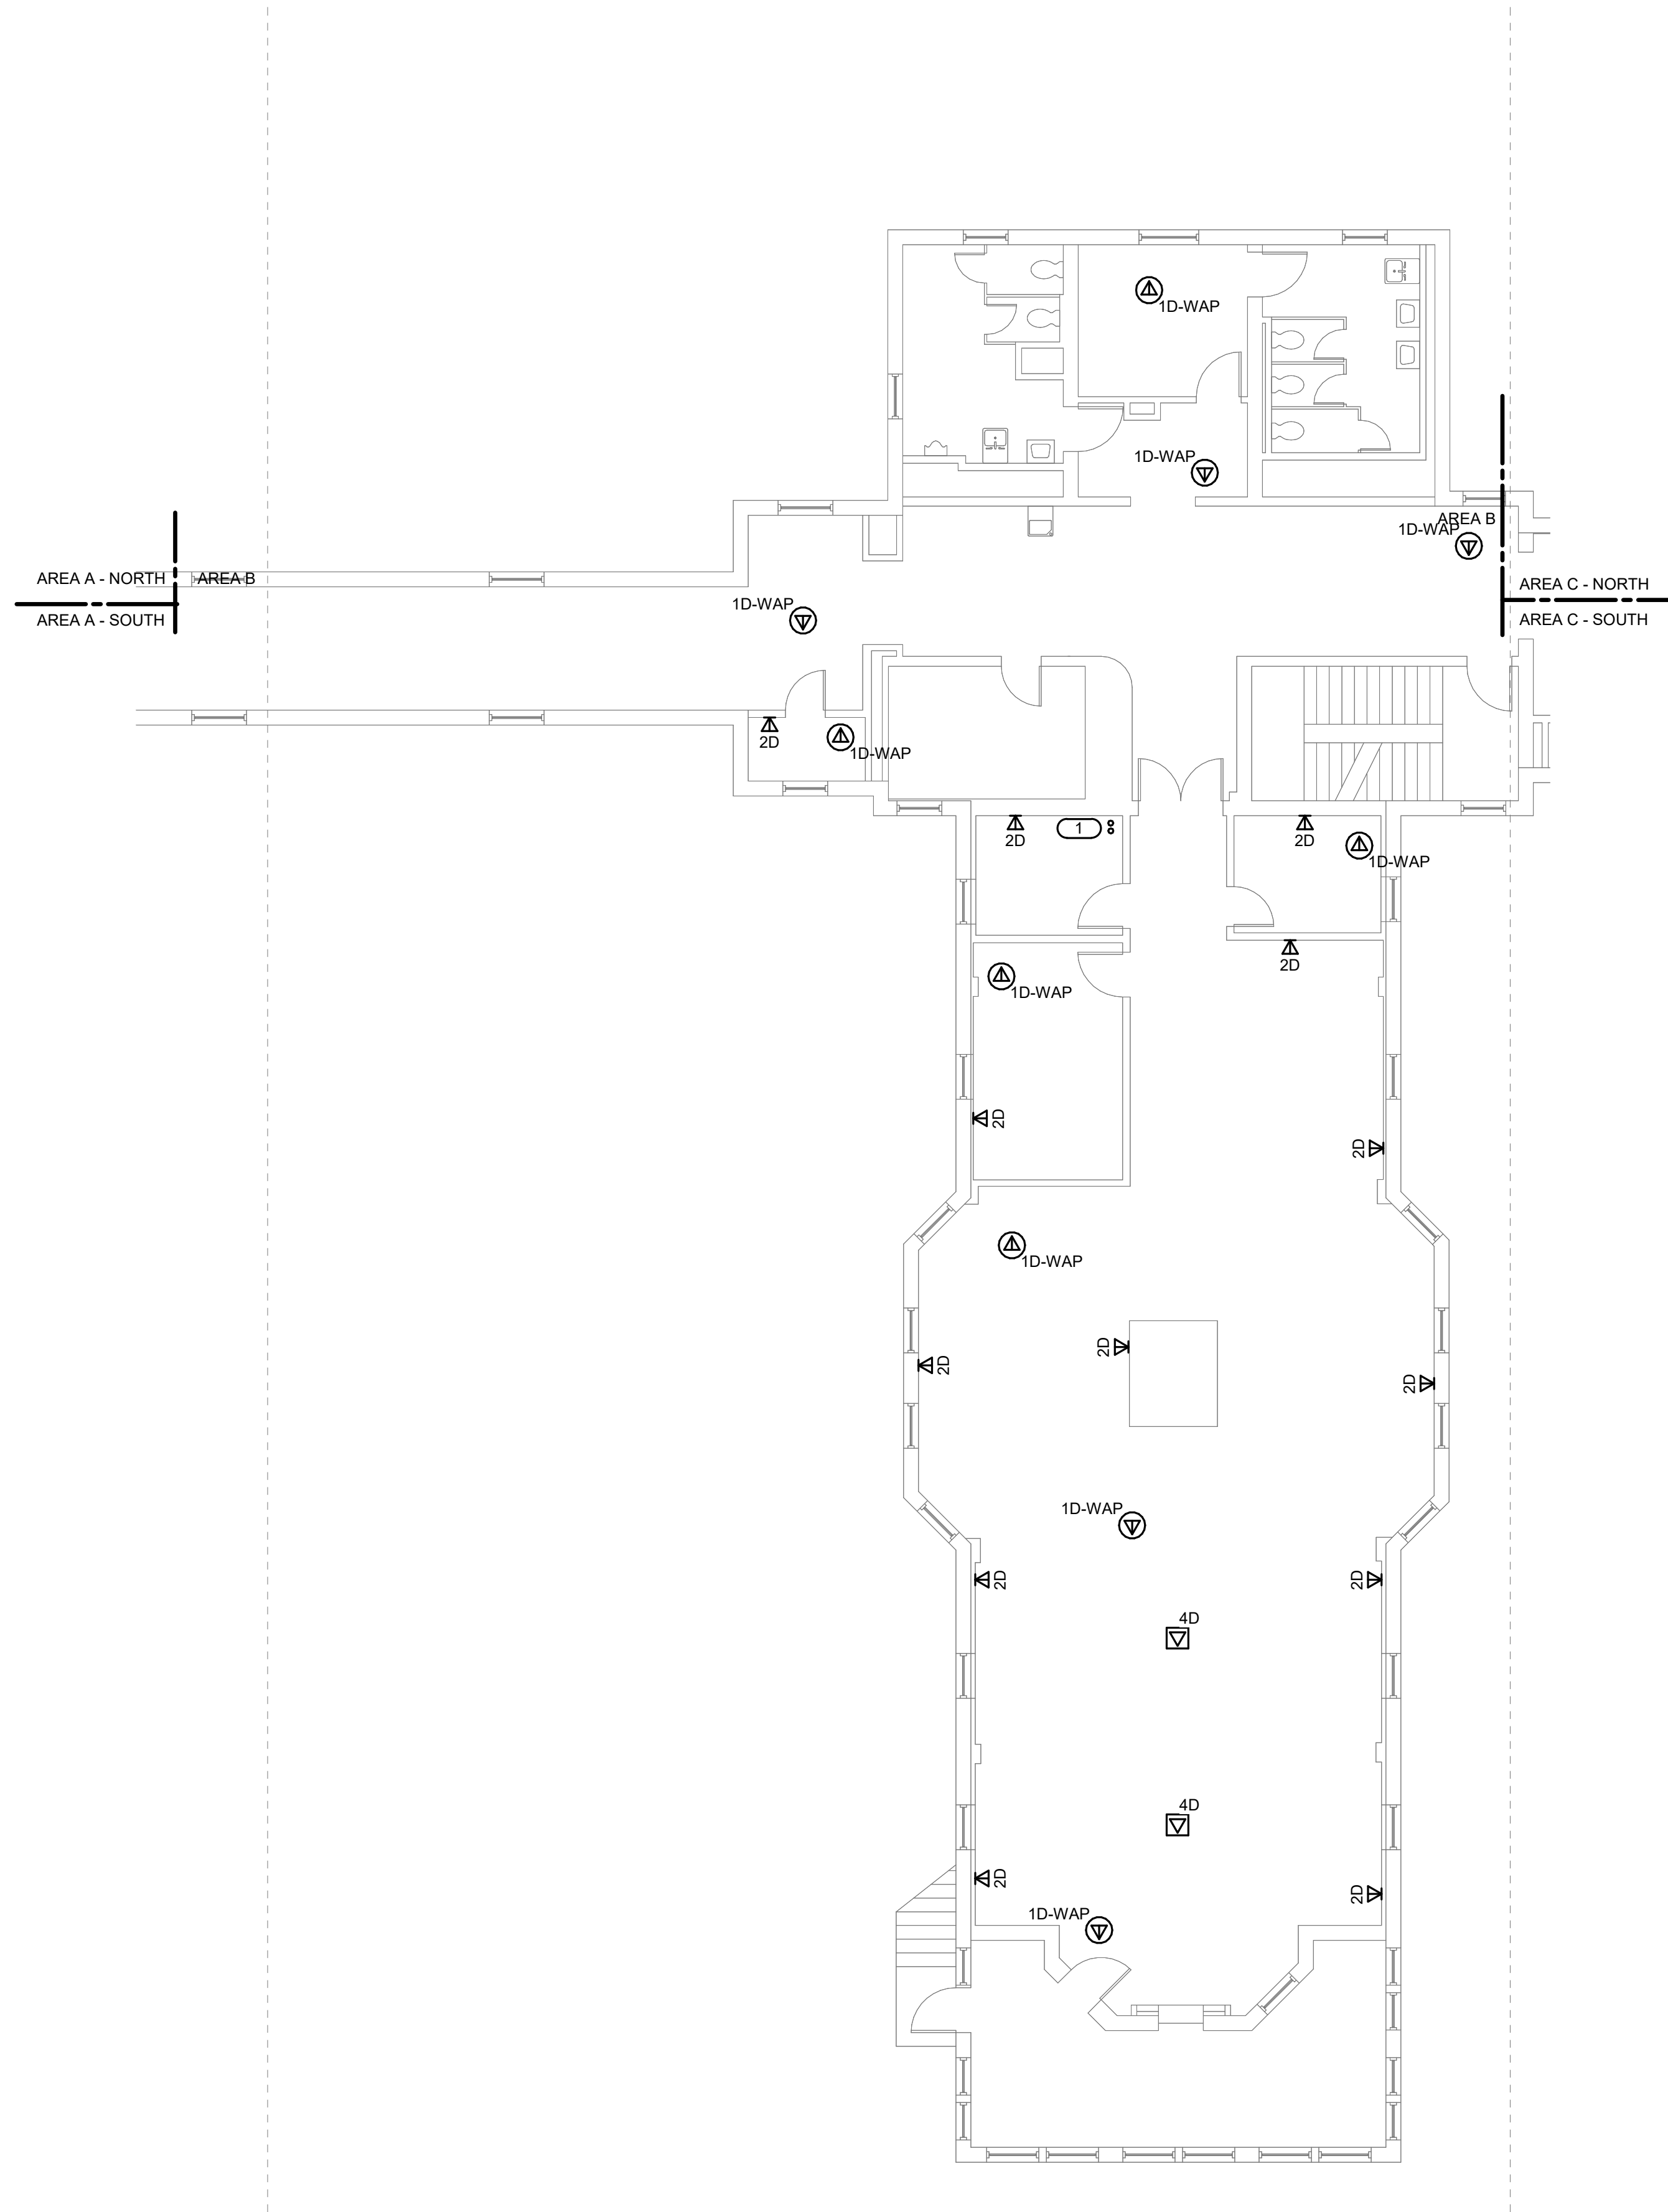

1 BUILDING 06 SECOND FLOOR PLAN - TECHNOLOGY - AREA B
1/8" = 1'-0"

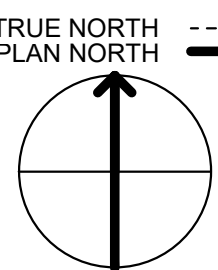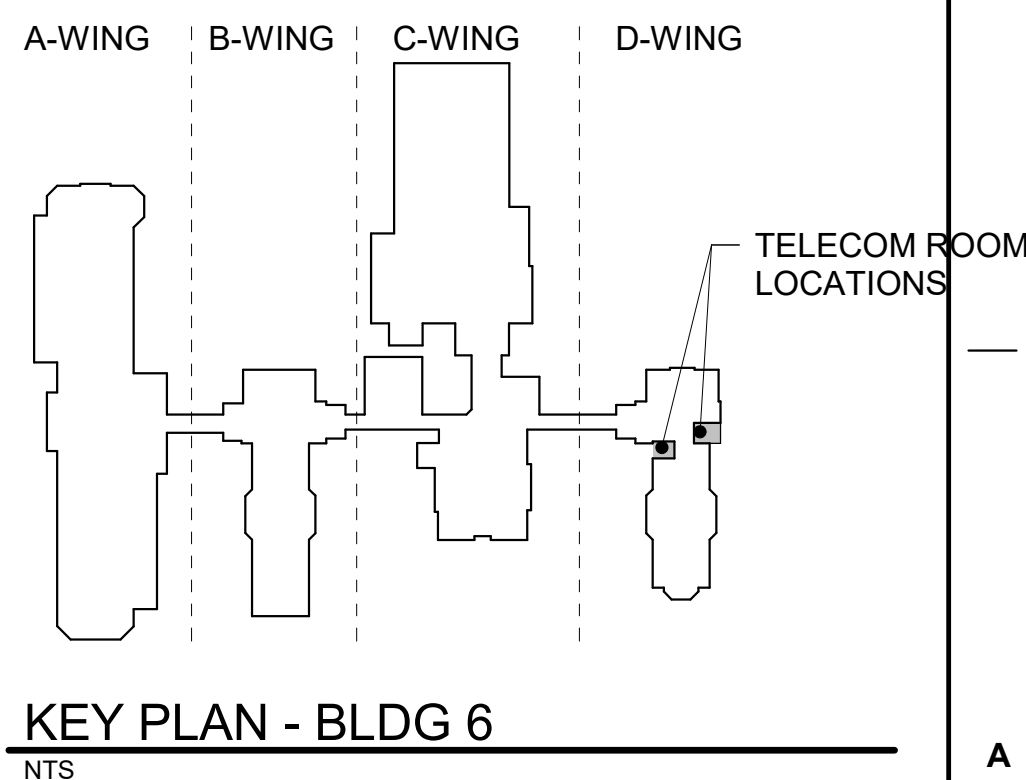

35% SCHEMATIC DESIGN SUBMISSION	5.17.21
65% DESIGN DEVELOPMENT SUBMISSION	6.15.21
65% DESIGN DEVELOPMENT RESUBMISSION	8.25.21
Revisions:	Date:

CONSULTANT

IMEG

15 SUNNEN DRIVE
SUITE 104
ST. LOUIS, MO 63143
P: 314.645.1132 F: 314.645.1173
PROJECT #18004375.03

ARCHITECT/ENGINEER OF RECORD

Romanyk Consulting
Focusing on what matters

Romanyk Consulting Corp. www.romanykconsulting.com
3308 Preston Road, Suite 350-164, Plano, Texas 75093

STAMP

Bicsi
DAVID LARSON
BICS1 ID # 106098
EXPIRES 12-31-25
REGISTERED COMMUNICATIONS DISTRIBUTION DESIGNER

Office of
Construction
and Facilities
Management

VA U.S. Department
of Veterans Affairs

Drawing Title
BUILDING 06 SECOND FLOOR PLAN -
TECHNOLOGY - AREA B

Approved:

Phase
FINAL BID DOCUMENTS

Sprinklered
FULLY SPRINKLERED

Project Title
EHRM INFRASTRUCTURE
UPGRADES - MILWAUKEE, WI

Location
5000 W. NATIONAL AVENUE MILWAUKEE, WI

Issue Date
SEPTEMBER 05, 2025

Checked
PHINIE

Drawn
MAIBEJ

Project Number
695-21-700

Building Number
06

Drawing Number
06-TN102B

F

E

D


C

B


A

9/20/2025 3:45:23 PM


Autodesk Docs\DCFM East - Milwaukee EHRM (R24)T24_1804375.03_VA MilWEHRM_C.rvt

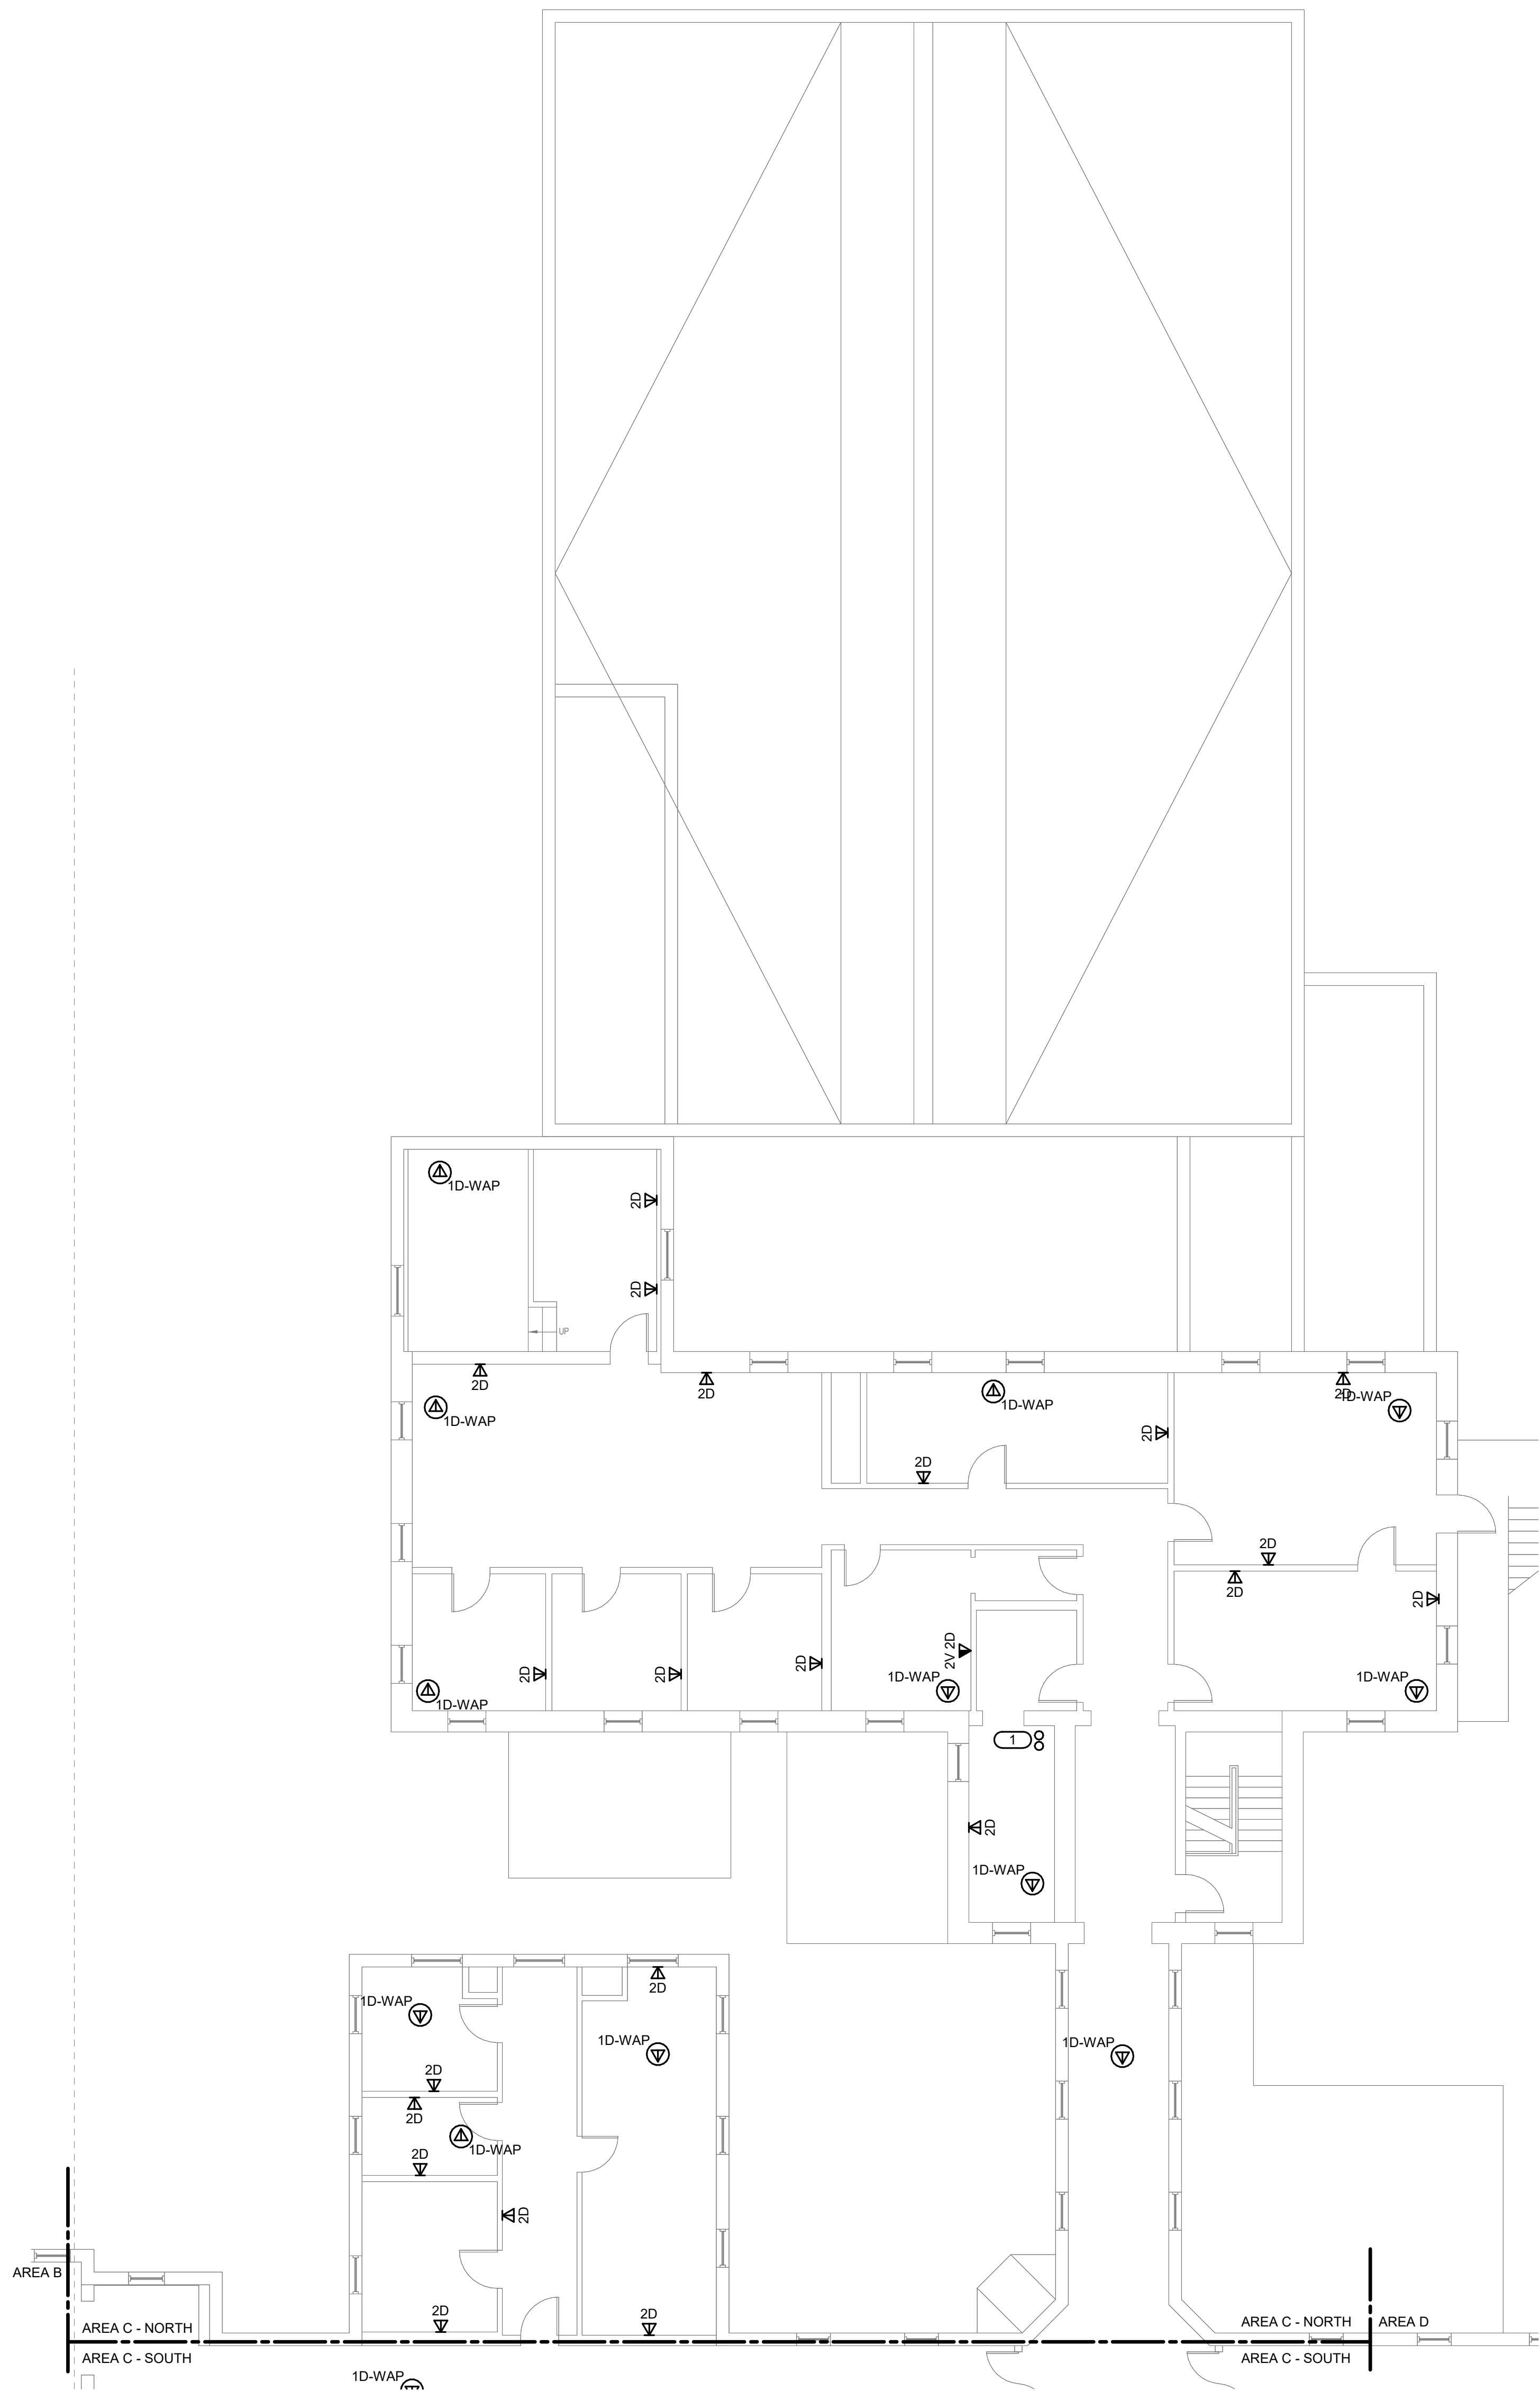

1 BUILDING 06 SECOND FLOOR PLAN - TECHNOLOGY - AREA C NORTH
1/8" = 1'-0"

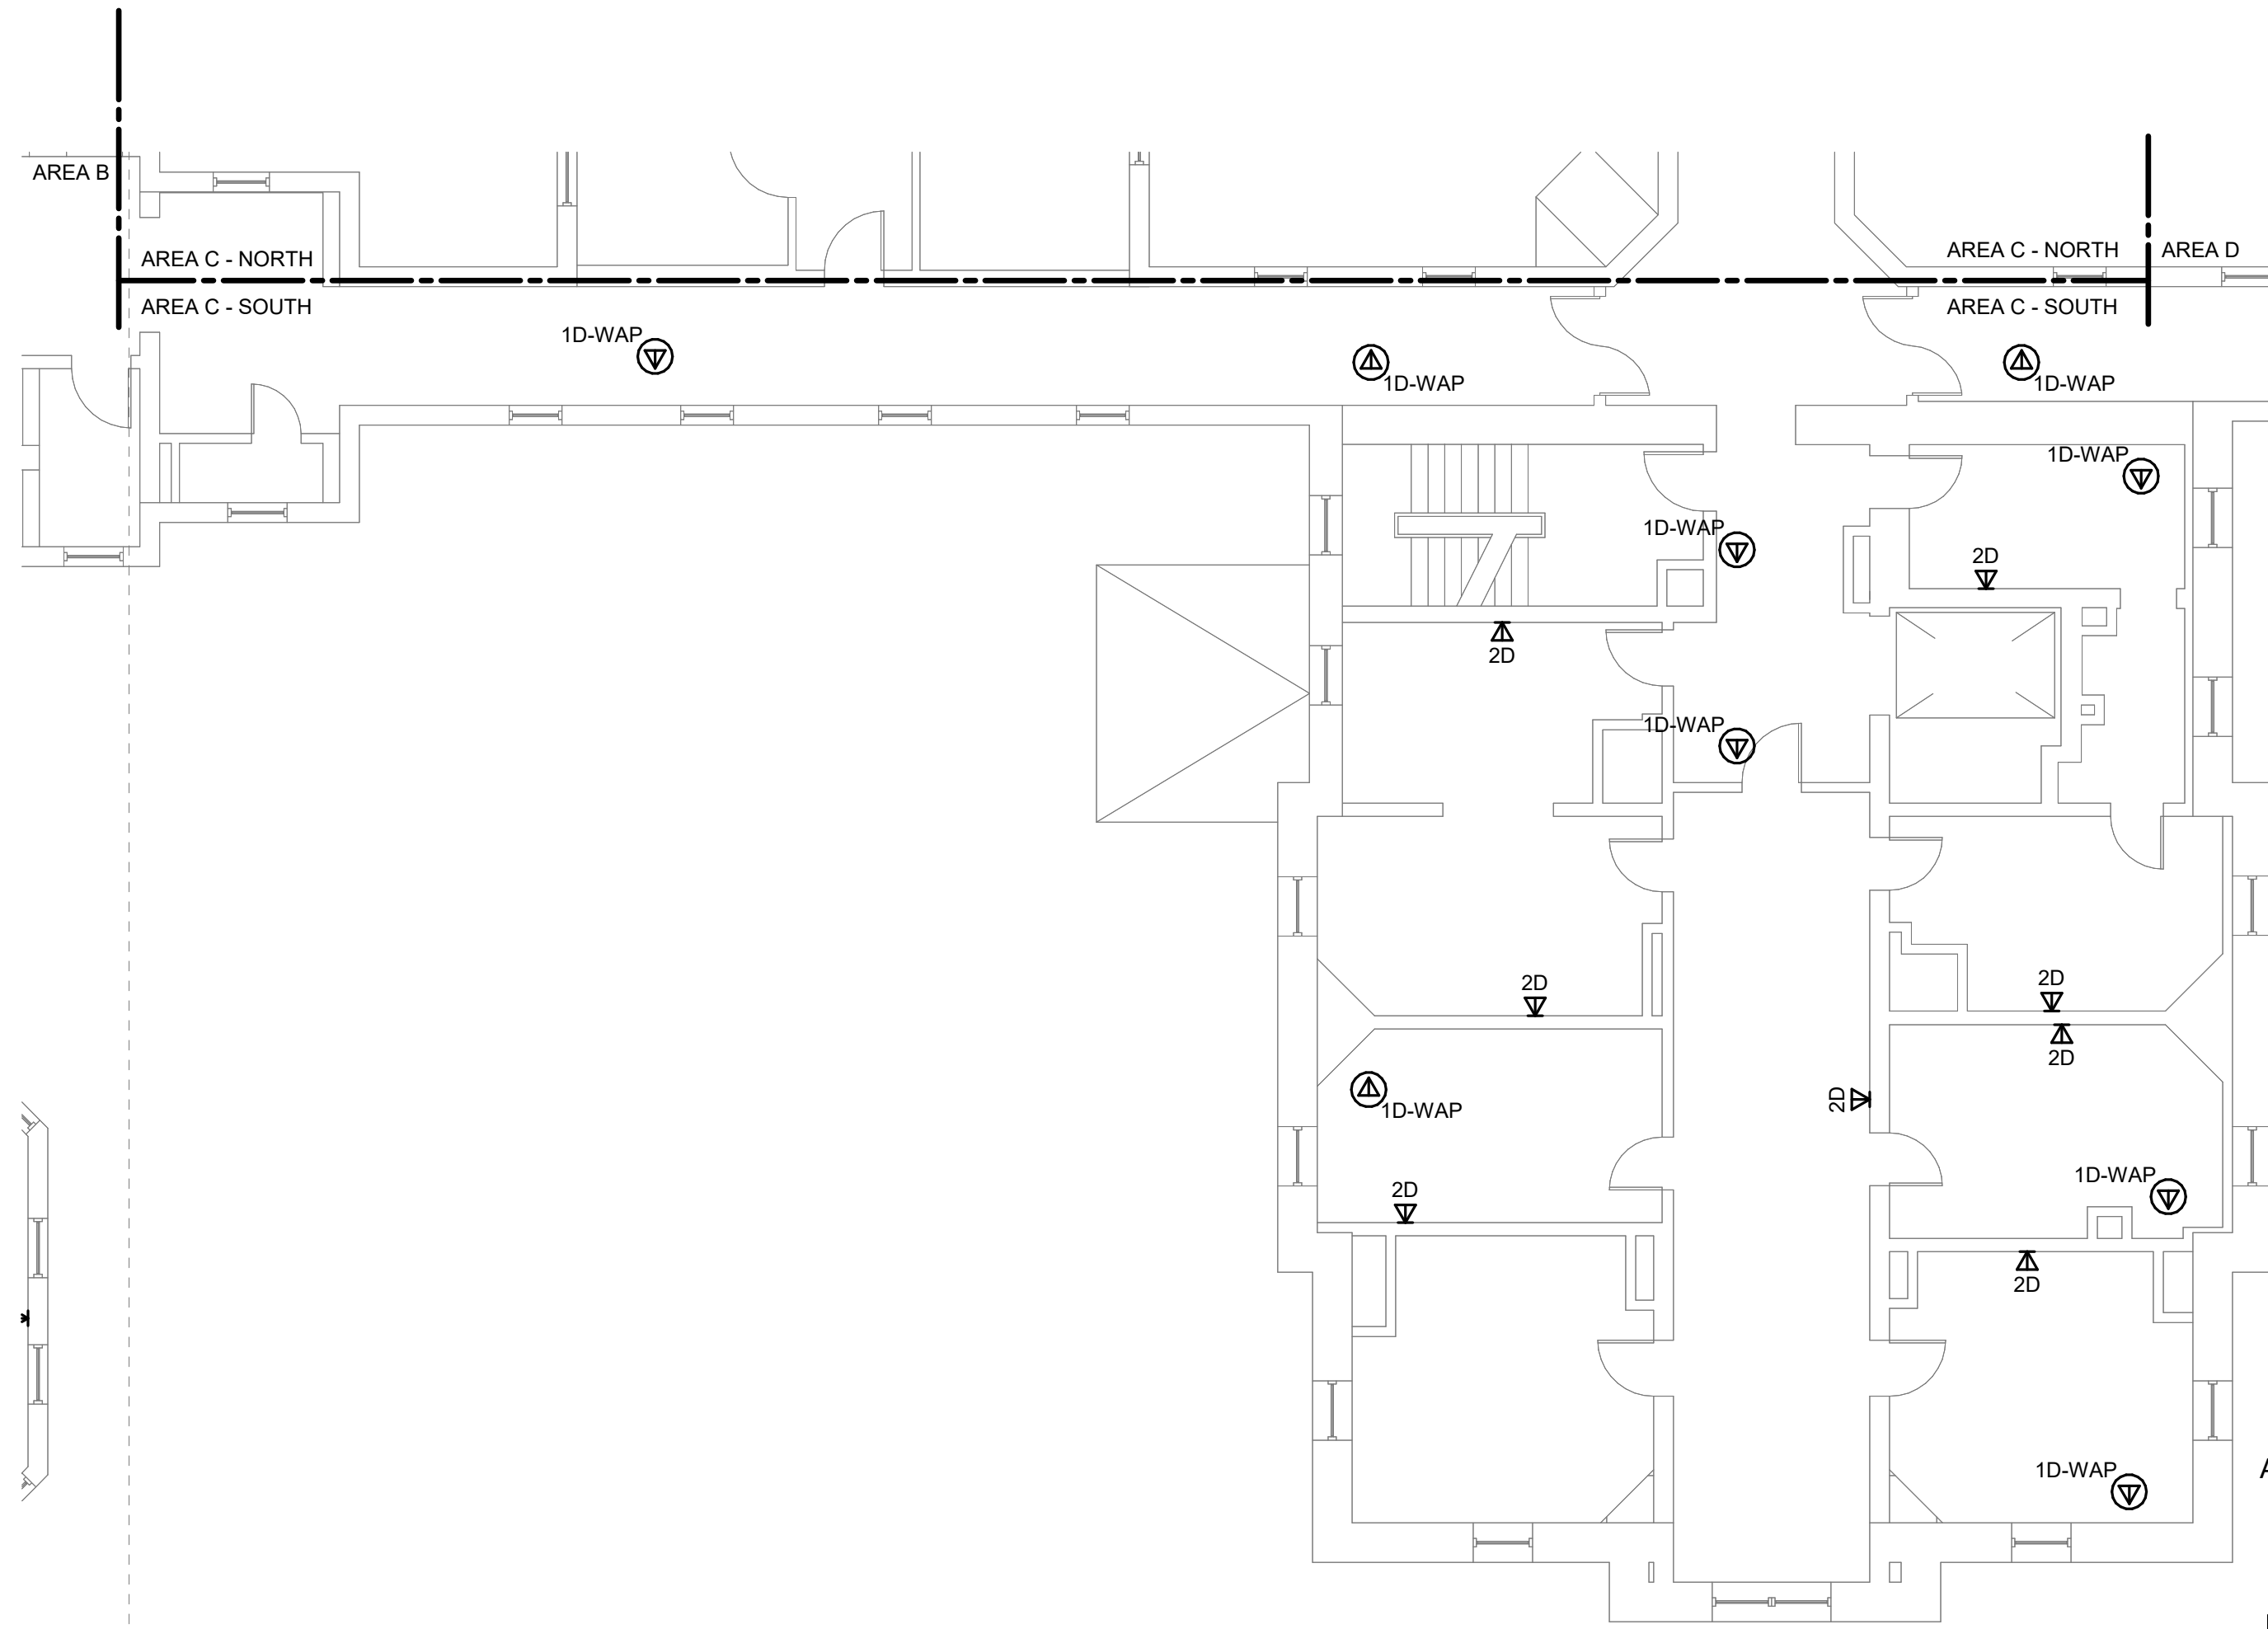


2 BUILDING 06 SECOND FLOOR PLAN - TECHNOLOGY - AREA C SOUTH
1/8" = 1'-0"

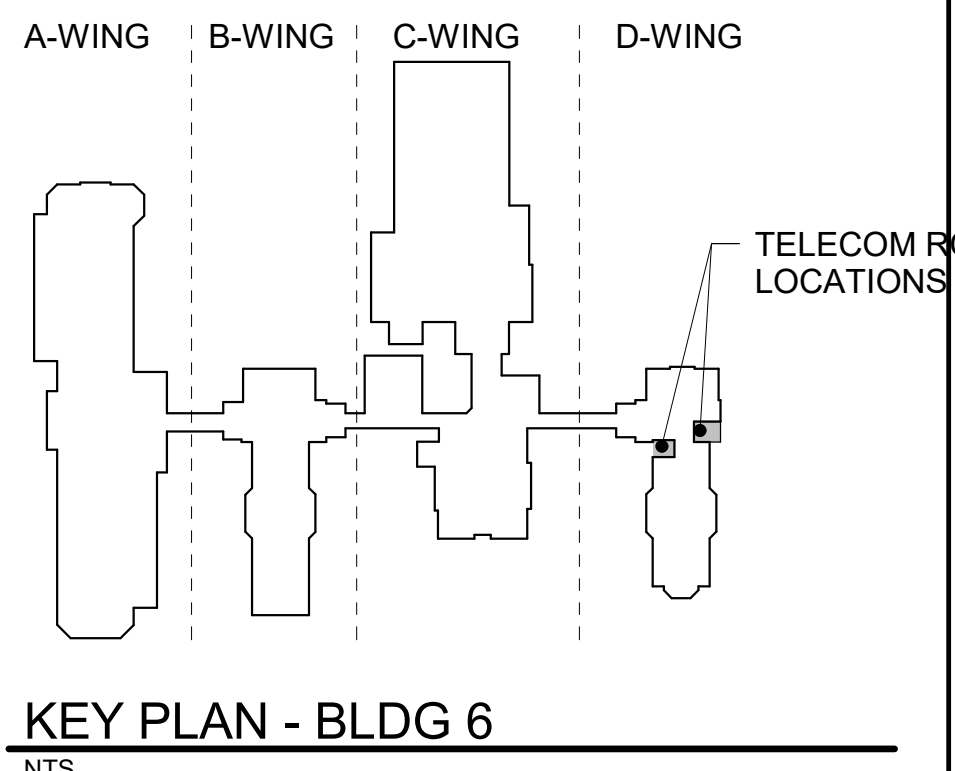


KEY PLAN - BLDG 6
NTS

- SHEET NOTES:**
1. REFER TO 1/TN400 FOR TECHNOLOGY ROUGH IN DETAIL.
 2. ALL NETWORK CABLES ON THIS SHEET SHALL TERMINATE IN TS-6-0203.
 3. CONTRACTOR TO PROVIDE NEW J-HOOK ROUTES FOR ALL NEW CABLING. J-HOOK SIZE AND QUANTITY TO BE PER MANUFACTURER RECOMMENDATIONS.
 4. REFER TO TN500-TN509 FOR RISER DIAGRAMS.
 5. REFER TO SHEET TN402 FOR PENETRATION DETAILS.
 6. THESE DRAWINGS MAKE THE BEST ATTEMPT TO IDENTIFY EXISTING DATA DROPS/WORK AREA OUTLETS. AS LONG AS THE TOTAL NEWLY INSTALLED DATA DROP COUNT DOES NOT VARY +/- 10% IDENTIFIED ON THESE DRAWINGS, THE CONTRACTOR'S SCOPE SHALL BE UNCHANGED.
 7. NEW WORK AREA OUTLETS SHALL BE LOCATED IN EXISTING BOXES. WORK AREA OUTLETS SHOWN ON THIS SHEET MAY NOT BE IN THE EXACT LOCATION AS IDENTIFIED.
 8. CONTRACTOR TO INCLUDE AN ALLOWANCE FOR 10% ADDITIONAL 2-PORTS CAT6A INFORMATION OUTLETS IN THEIR PROPOSAL FOR THIS SHEET. FUTURE INFORMATION OUTLET LOCATIONS WILL BE DETERMINED BY THE VA AT A LATER DATE.
- KEYNOTES:** C #
1. TWO (2) 4" PATHWAYS TO LEVEL BELOW.

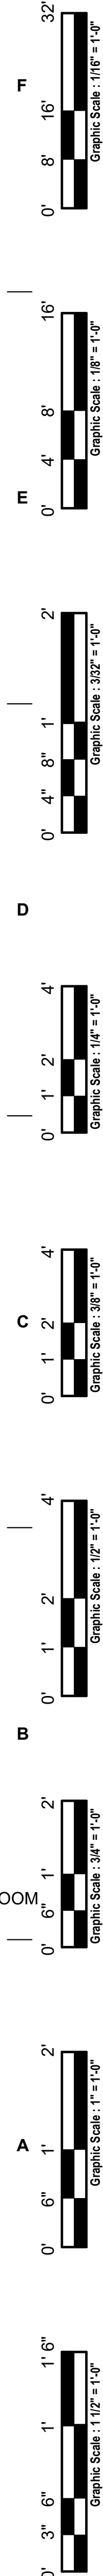

1. TWO (2) 4" PATHWAYS TO LEVEL BELOW.

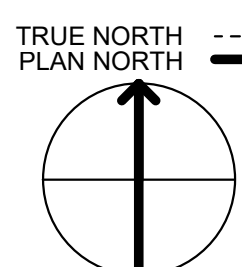

Project Number 695-21-700
Building Number 06
Drawing Number 06-TN102D

F

E

D

C

B

A

9/3/2025 3:55:25 PM


Autodesk Docs\DCFM East - Milwaukee EHRM (R24)T24_1804375.03_VA MilWEHRM_C.dwg

SHEET NOTES:


1. REMOVE ALL NETWORK CABLING TO POINTS OF TERMINATION IN ASSOCIATED DATA CLOSET. REFER TO FLOOR PLANS AND SHEET T1001 FOR TR ROOM LOCATIONS.
2. THESE DRAWINGS MAKE THE BEST ATTEMPT TO IDENTIFY EXISTING DATA DROPS/WORK AREA OUTLETS. AS LONG AS THE TOTAL NEWLY INSTALLED DATA DROP COUNT DOES NOT VARY +/- 10% IDENTIFIED ON THESE DRAWINGS, THE CONTRACTOR'S SCOPE SHALL BE UNCHANGED.
3. NEW WORK AREA OUTLETS SHALL BE LOCATED IN EXISTING BOXES. WORK AREA OUTLETS SHOWN ON THIS SHEET MAY NOT BE IN THE EXACT LOCATION AS IDENTIFIED.

KEYNOTES: C #

1. TWO (2) 4" PATHWAYS TO LEVEL BELOW. REFER TO 06-TN102 FOR CONTINUATION.

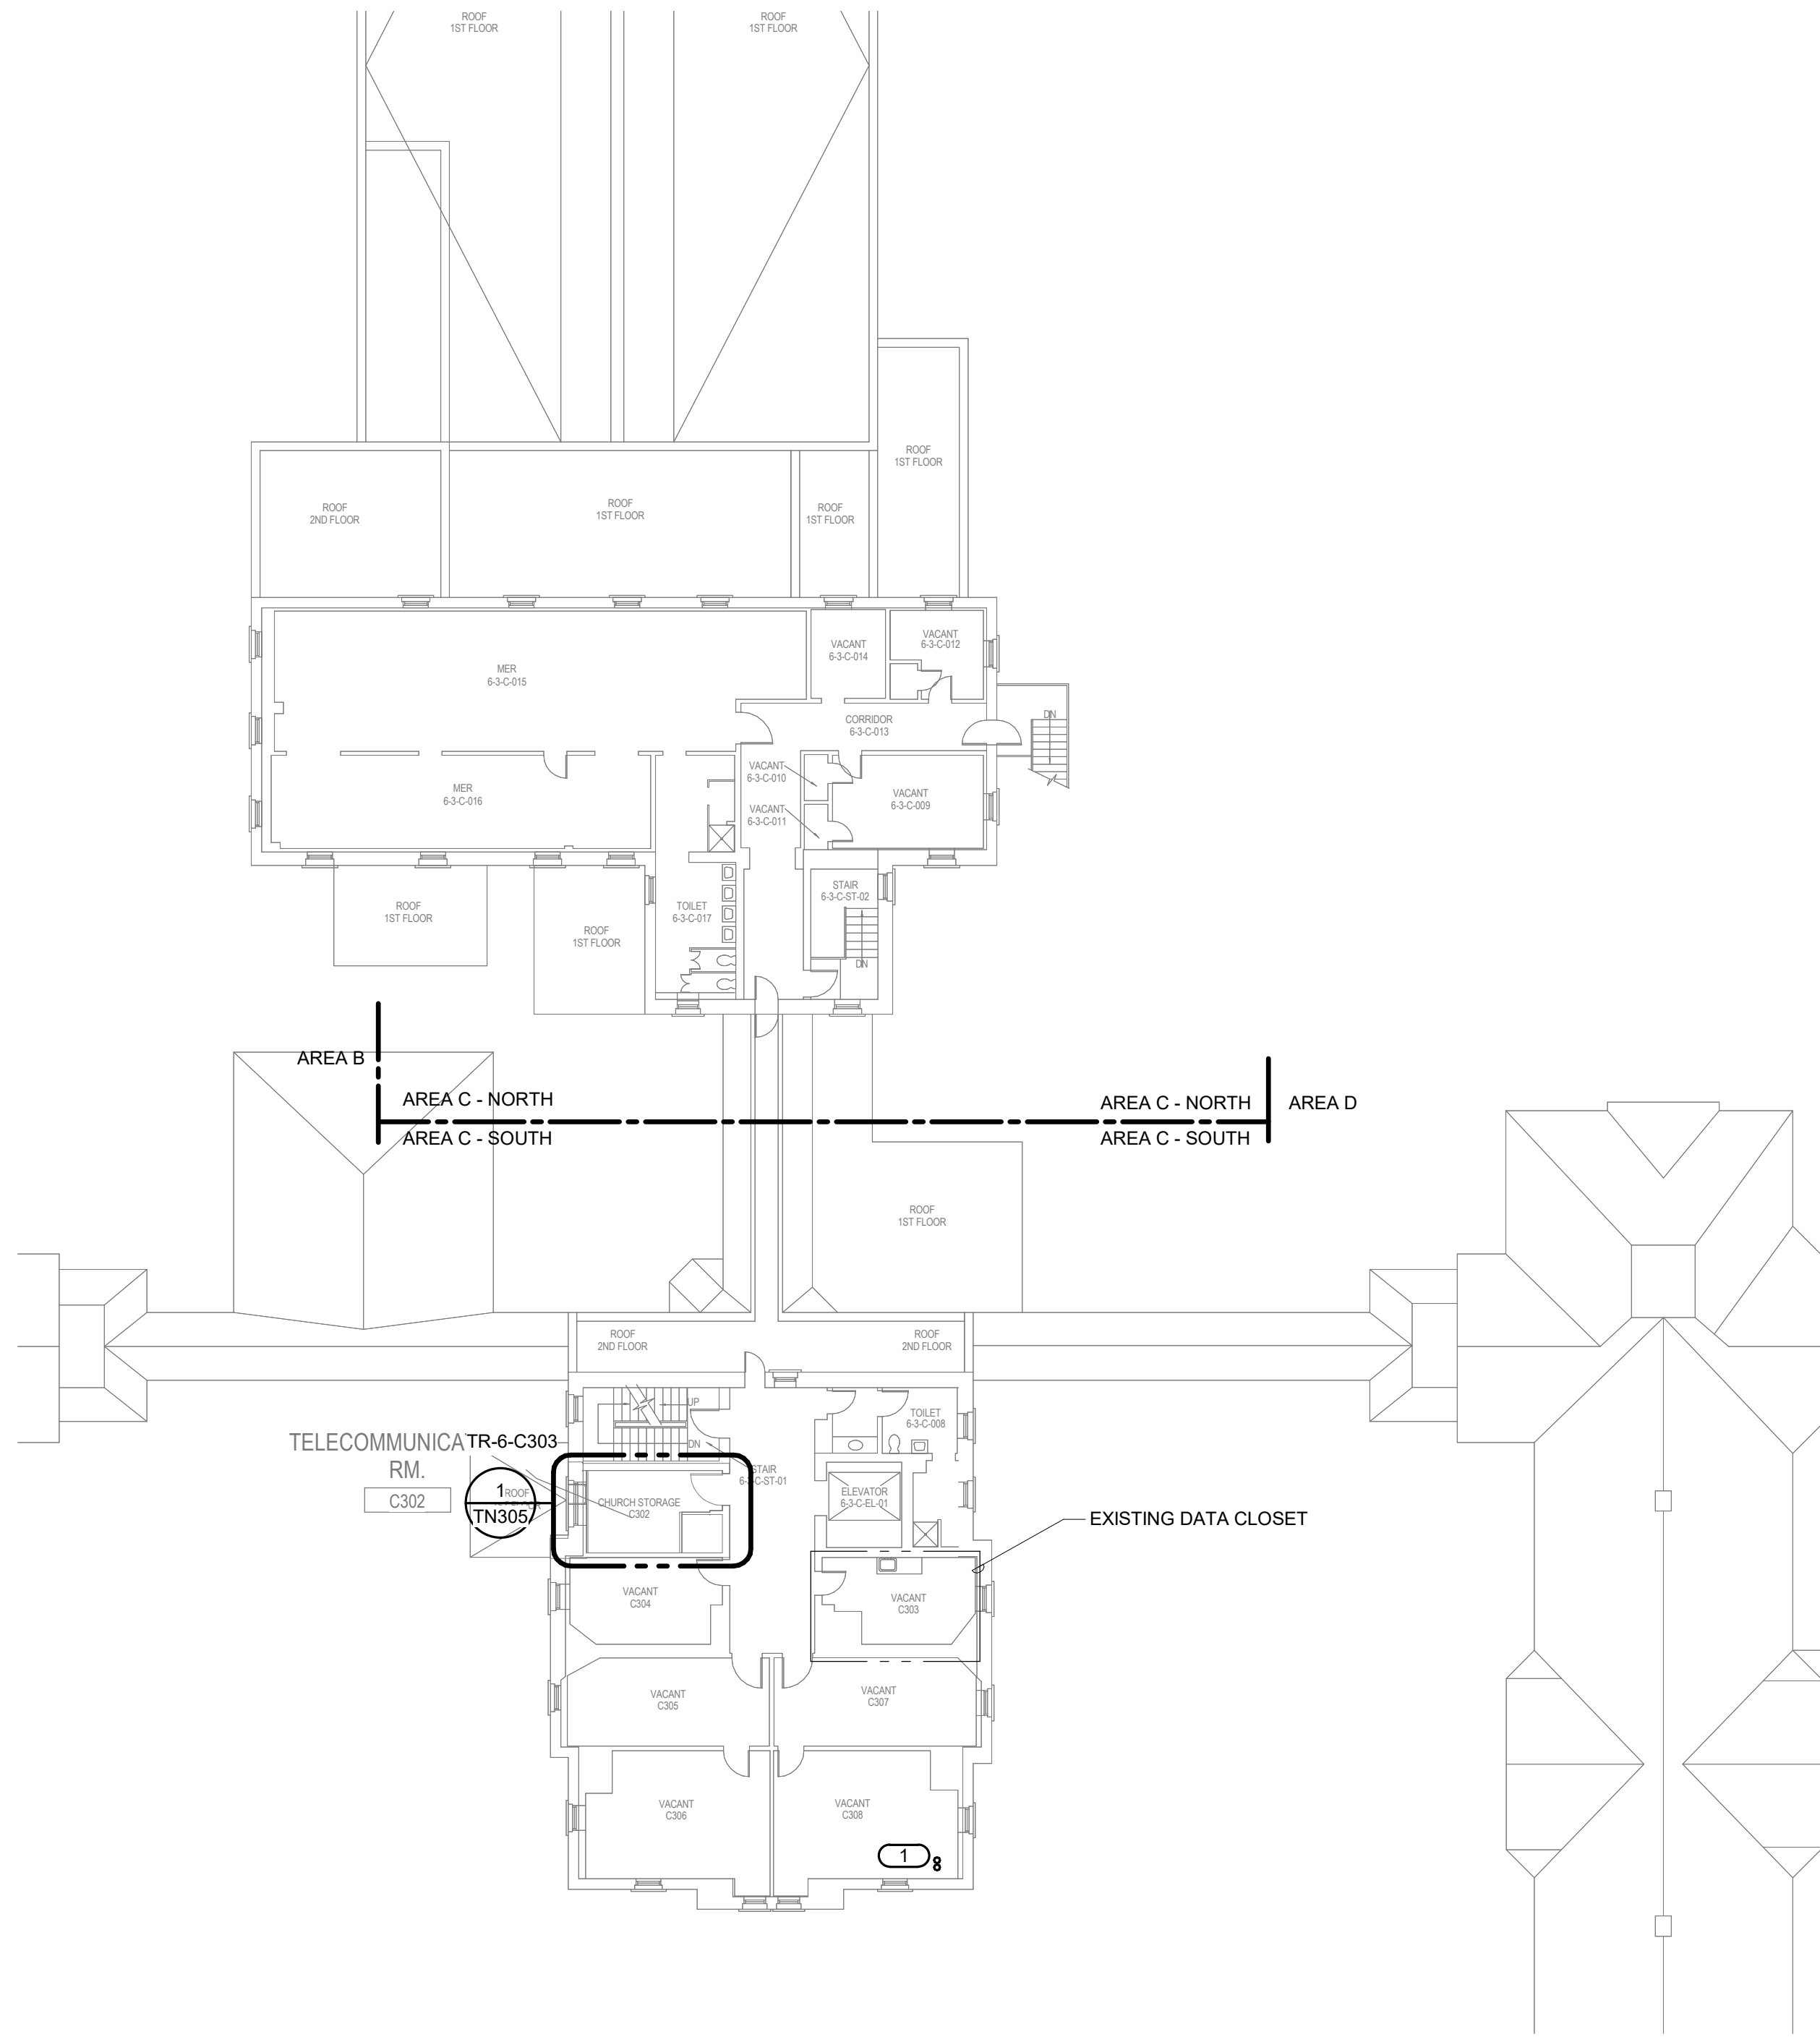

1 BUILDING 06 THIRD FLOOR OVERALL PLAN - TECHNOLOGY
1/16" = 1'-0"

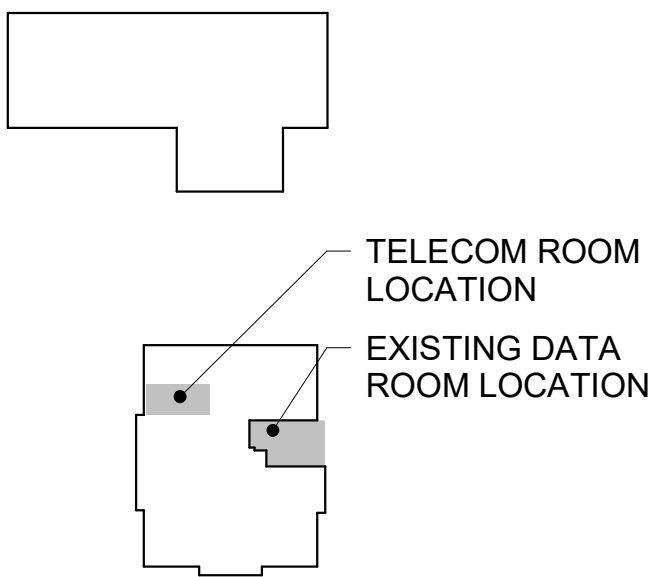

KEY PLAN - BLDG 6
NTS



35% SCHEMATIC DESIGN SUBMISSION	5.17.21
65% DESIGN DEVELOPMENT SUBMISSION	6.15.21
65% DESIGN DEVELOPMENT RESUBMISSION	8.25.21
Revisions:	Date:

CONSULTANT

IMEG

15 SUNNEN DRIVE
SUITE 104
ST. LOUIS, MO 63143
P: 314.645.1132 F: 314.645.1173
PROJECT #18004375.03

ARCHITECT/ENGINEER OF RECORD

Romanyk Consulting
Focusing on what matters

Romanyk Consulting Corp. www.romanykconsulting.com
3308 Preston Road, Suite 350-164, Plano, Texas 75093

STAMP

Bicsi
DAVID LARSON
BICS1 ID # 106098
EXPIRES 12-31-25
REGISTERED COMMUNICATIONS DISTRIBUTION DESIGNER

Office of
Construction
and Facilities
Management

VA U.S. Department
of Veterans Affairs

Drawing Title
BUILDING 06 THIRD FLOOR OVERALL PLAN -
TECHNOLOGY

Approved:

Phase
FINAL BID DOCUMENTS

Sprinklered
FULLY SPRINKLERED

Project Title
EHRM INFRASTRUCTURE
UPGRADES - MILWAUKEE, WI

Location
5000 W. NATIONAL AVENUE MILWAUKEE, WI

Issue Date
SEPTEMBER 05, 2025

Checked
PHINE

Drawn
MAIBEJ

Project Number
695-21-700

Building Number
06

Drawing Number
06-TN103

F

E

D

C


B

A


9/3/2025 3:55:26 PM

Autodesk Docs\DCFM East - Milwaukee EHRM (R24)T24_1804375\03_VA Milwaukee C.d

- SHEET NOTES:**
1. REFER TO 1/TN400 FOR TECHNOLOGY ROUGH-IN DETAIL.
 2. ALL NETWORK CABLES ON THIS SHEET SHALL TERMINATE IN TS-6-C302.
 3. CONTRACTOR TO PROVIDE NEW J-HOOK ROUTES FOR ALL NEW CABLING. J-HOOK SIZE AND QUANTITY TO BE PER MANUFACTURER RECOMMENDATIONS.
 4. REFER TO TN500-TN509 FOR RISER DIAGRAMS.
 5. REFER TO SHEET TN402 FOR PENETRATION DETAILS.
 6. THESE DRAWINGS MAKE THE BEST ATTEMPT TO IDENTIFY EXISTING DATA DROPS/WORK AREA OUTLETS. AS LONG AS THE TOTAL NEWLY INSTALLED DATA DROP COUNT DOES NOT VARY +/- 10% IDENTIFIED ON THESE DRAWINGS, THE CONTRACTOR'S SCOPE SHALL BE UNCHANGED.
 7. NEW WORK AREA OUTLETS SHALL BE LOCATED IN EXISTING BOXES. WORK AREA OUTLETS SHOWN ON THIS SHEET MAY NOT BE IN THE EXACT LOCATION AS IDENTIFIED.
 8. CONTRACTOR TO INCLUDE AN ALLOWANCE FOR 10% ADDITIONAL 2-PORTS CAT6A INFORMATION OUTLETS IN THEIR PROPOSAL FOR THIS SHEET. FUTURE INFORMATION OUTLET LOCATIONS WILL BE DETERMINED BY THE VA AT A LATER DATE.

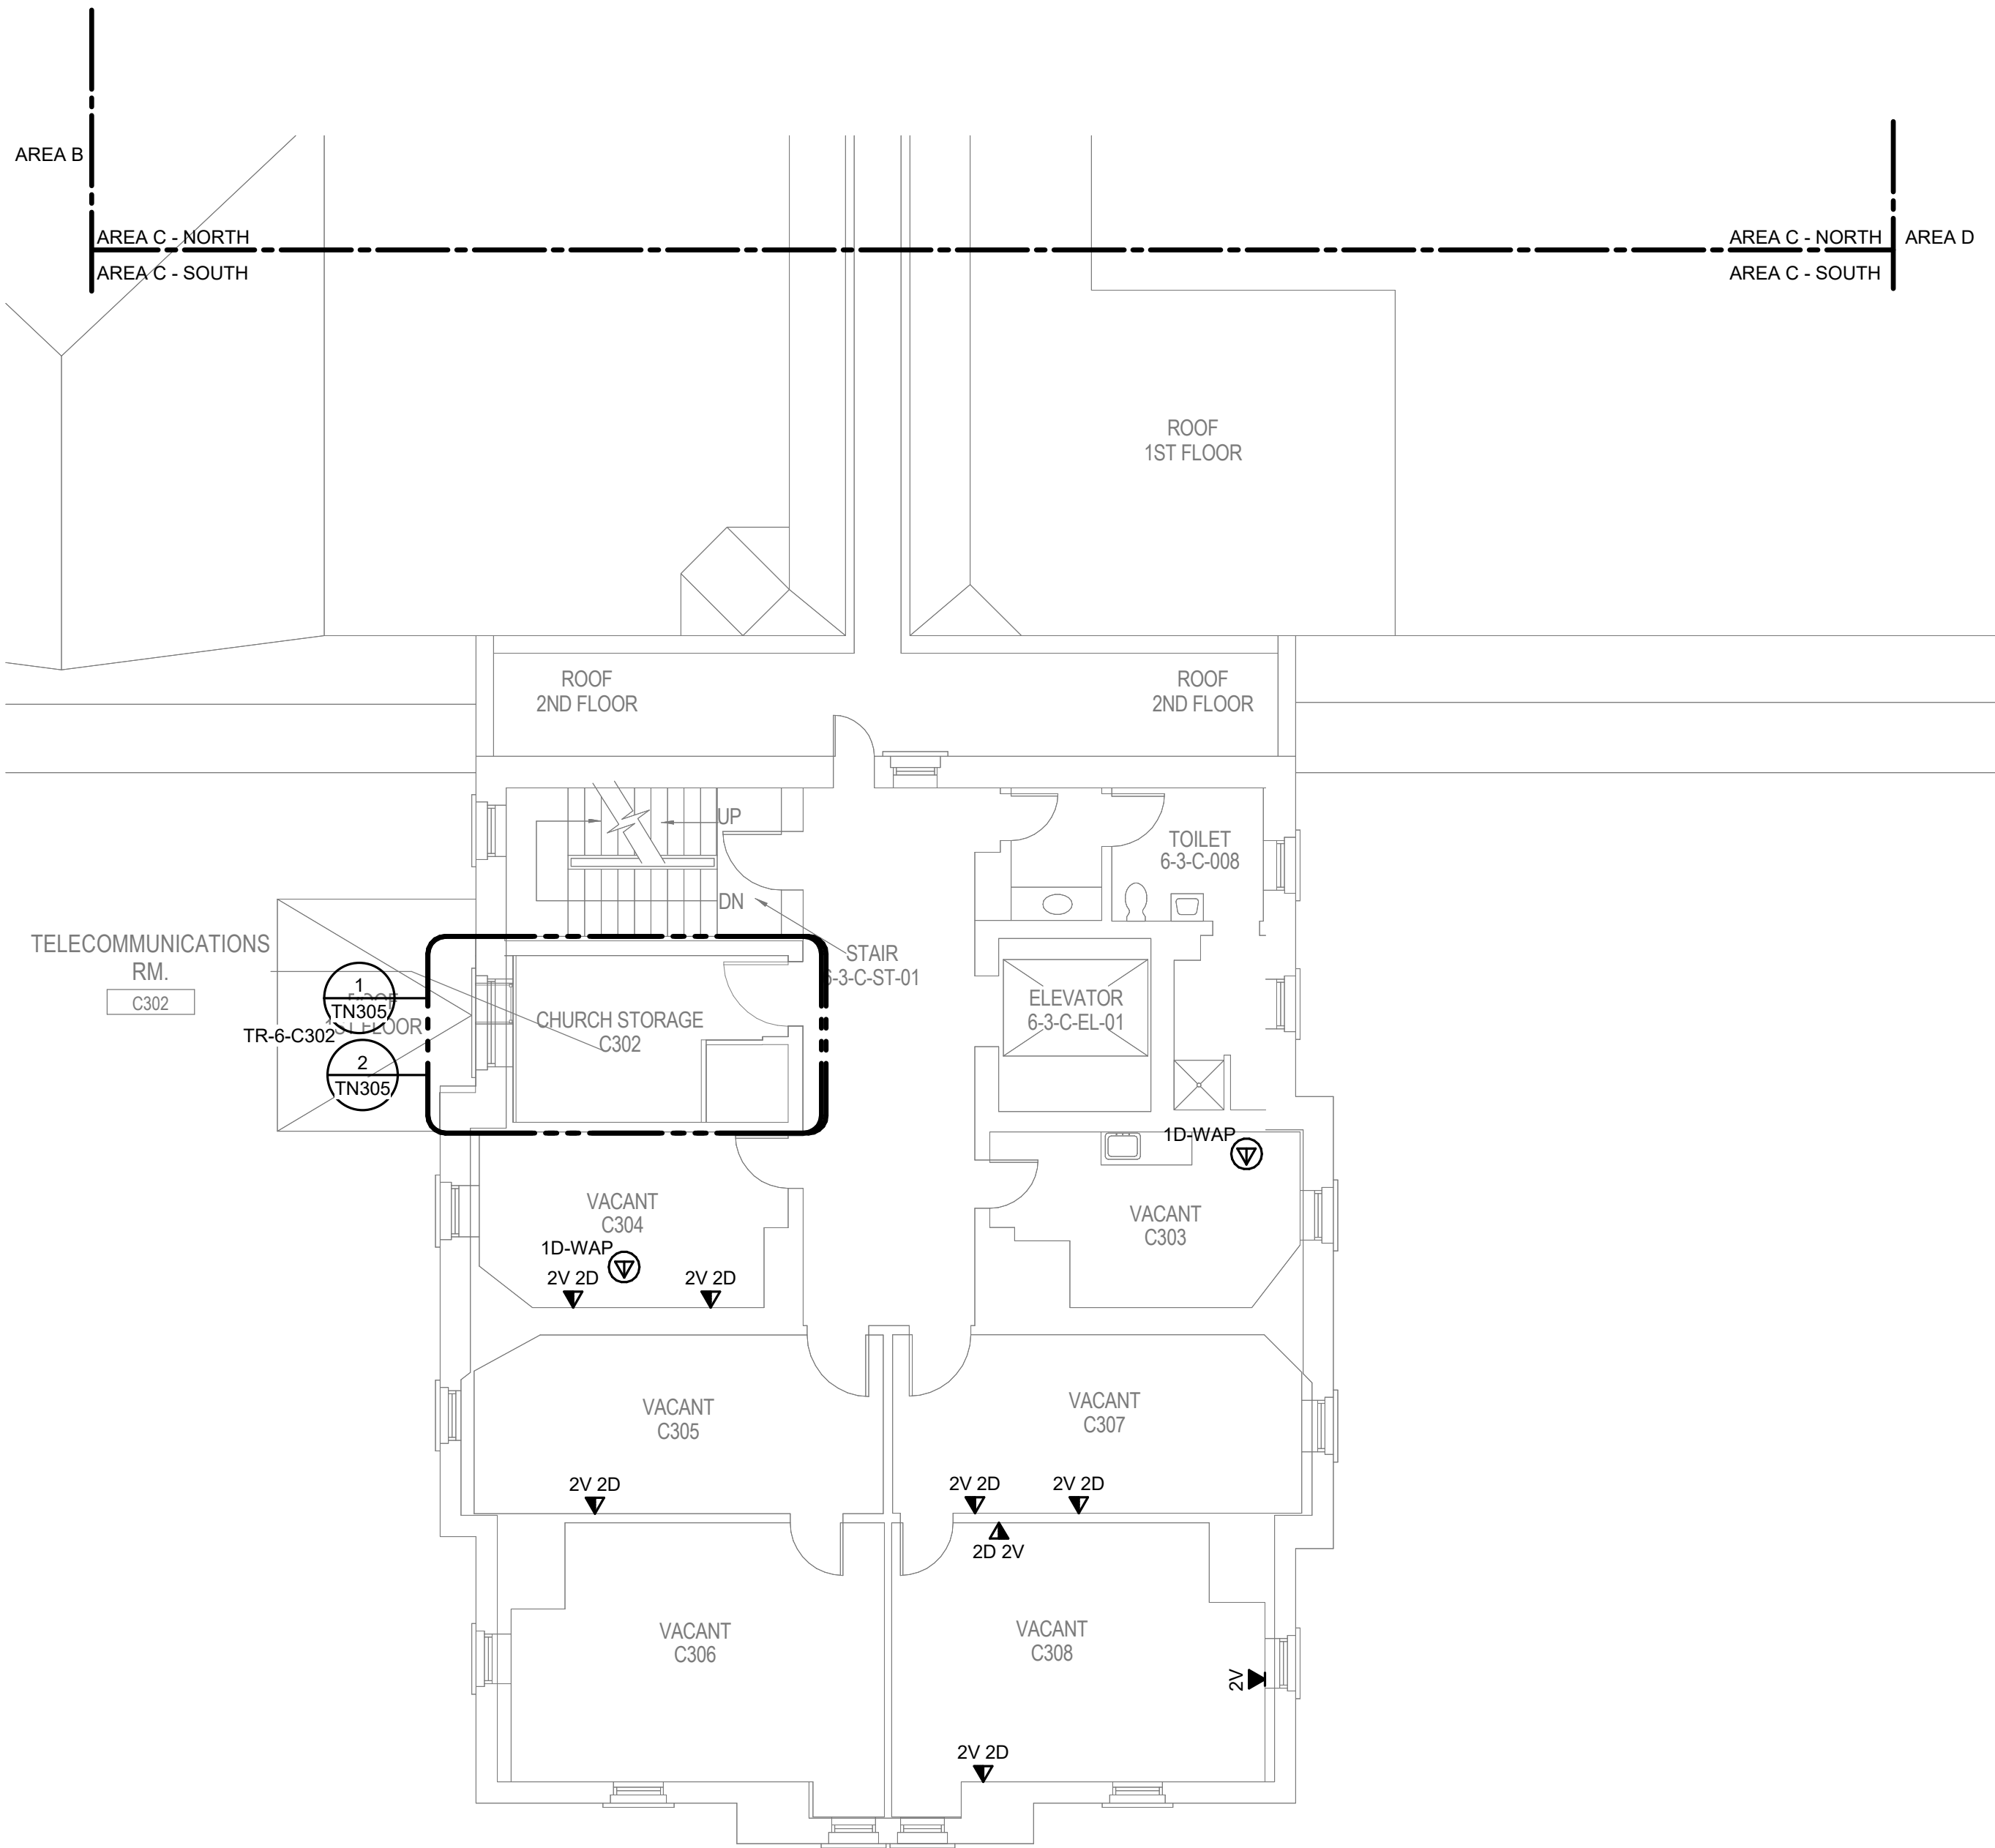

1 BUILDING 06 THIRD FLOOR PLAN - TECHNOLOGY - AREA C NORTH
1/8" = 1'-0"

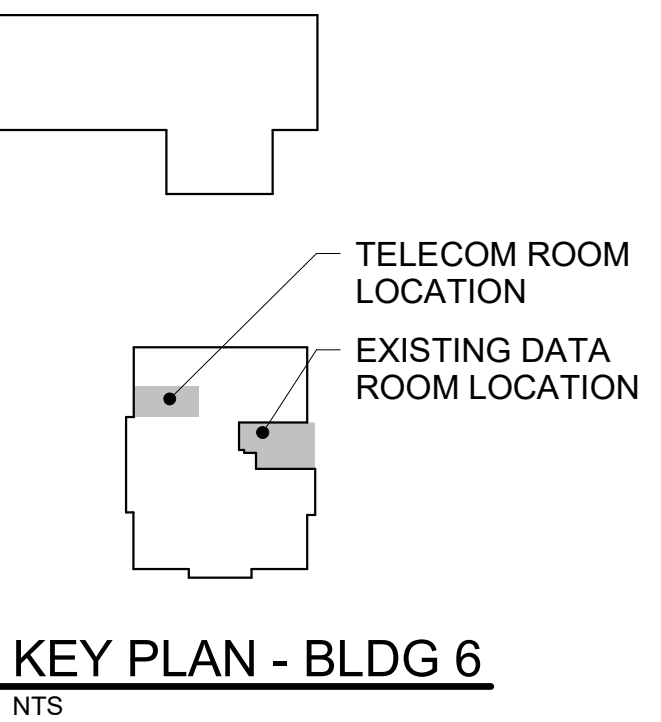

35% SCHEMATIC DESIGN SUBMISSION	5.17.21
65% DESIGN DEVELOPMENT SUBMISSION	6.15.21
65% DESIGN DEVELOPMENT RESUBMISSION	8.25.21
Revisions:	Date:

CONSULTANT

IMEG

15 SUNNEN DRIVE
SUITE 104
ST. LOUIS, MO 63143
P: 314.645.1132 F: 314.645.1173
PROJECT #18004375.03

ARCHITECT/ENGINEER OF RECORD

Romanyk Consulting
Focusing on what matters

Romanyk Consulting Corp. www.romanykconsulting.com
3308 Preston Road, Suite 350-164, Plano, Texas 75093

STAMP

Bicsi
DAVID LARSON
BICS1 ID # 106098
EXPIRES 12-31-25
REGISTERED COMMUNICATIONS DISTRIBUTION DESIGNER

Office of
Construction
and Facilities
Management

VA U.S. Department
of Veterans Affairs

Drawing Title
BUILDING 06 THIRD FLOOR PLAN -
TECHNOLOGY - AREA C

Approved:

Phase
FINAL BID DOCUMENTS

Sprinklered
FULLY SPRINKLERED

Project Title
EHRM INFRASTRUCTURE
UPGRADES - MILWAUKEE, WI

Location
5000 W. NATIONAL AVENUE MILWAUKEE, WI

Issue Date
SEPTEMBER 05, 2025

Checked
PHINE

Drawn
MAIBEJ

Project Number
695-21-700

Building Number
06

Drawing Number
06-TN103C

F

E

D

C











B

A

9/3/2025 3:55:27 PM


Autodesk Docs\DCRM East - Milwaukee EHRM (R24)T24_1804375.03_VA Milwaukee_C.dwg

- SHEET NOTES:**
1. REMOVE ALL NETWORK CABLING TO POINTS OF TERMINATION IN ASSOCIATED TRS. REFER TO FLOOR PLANS AND SHEET T1001 FOR TR ROOM LOCATIONS.
 2. REFER TO ARCHITECTURAL PHASING PLANS FOR WHEN EXISTING CABLING IS ALLOWED TO BE DEMOLISHED.
 3. EXISTING BACKBONE ENTRY POINT. PROTECT IN PLACE. DEMOLISH EXISTING FIBER OPTIC CABLE TO POINTS OF TERMINATION AFTER REDUNDANT PATH IS INSTALLED AND OPERATIONAL. REFER TO PHASING PLAN FOR ADDITIONAL INFORMATION.
 4. FOR ALL EXISTING WIRELESS ACCESS POINTS AND SURVEILLANCE CAMERAS, DEVICES SHALL REMAIN. SCOPE OF WORK INCLUDES CABLE REPLACEMENT ONLY. COORDINATE WITH COR FOR ANY DOWNTIME OF DEVICES.
 5. EXISTING LOCATIONS OF WORK AREA OUTLETS SHOWN ON THIS SHEET MAY NOT NECESSARILY BE IN THE EXACT LOCATION AS IDENTIFIED.

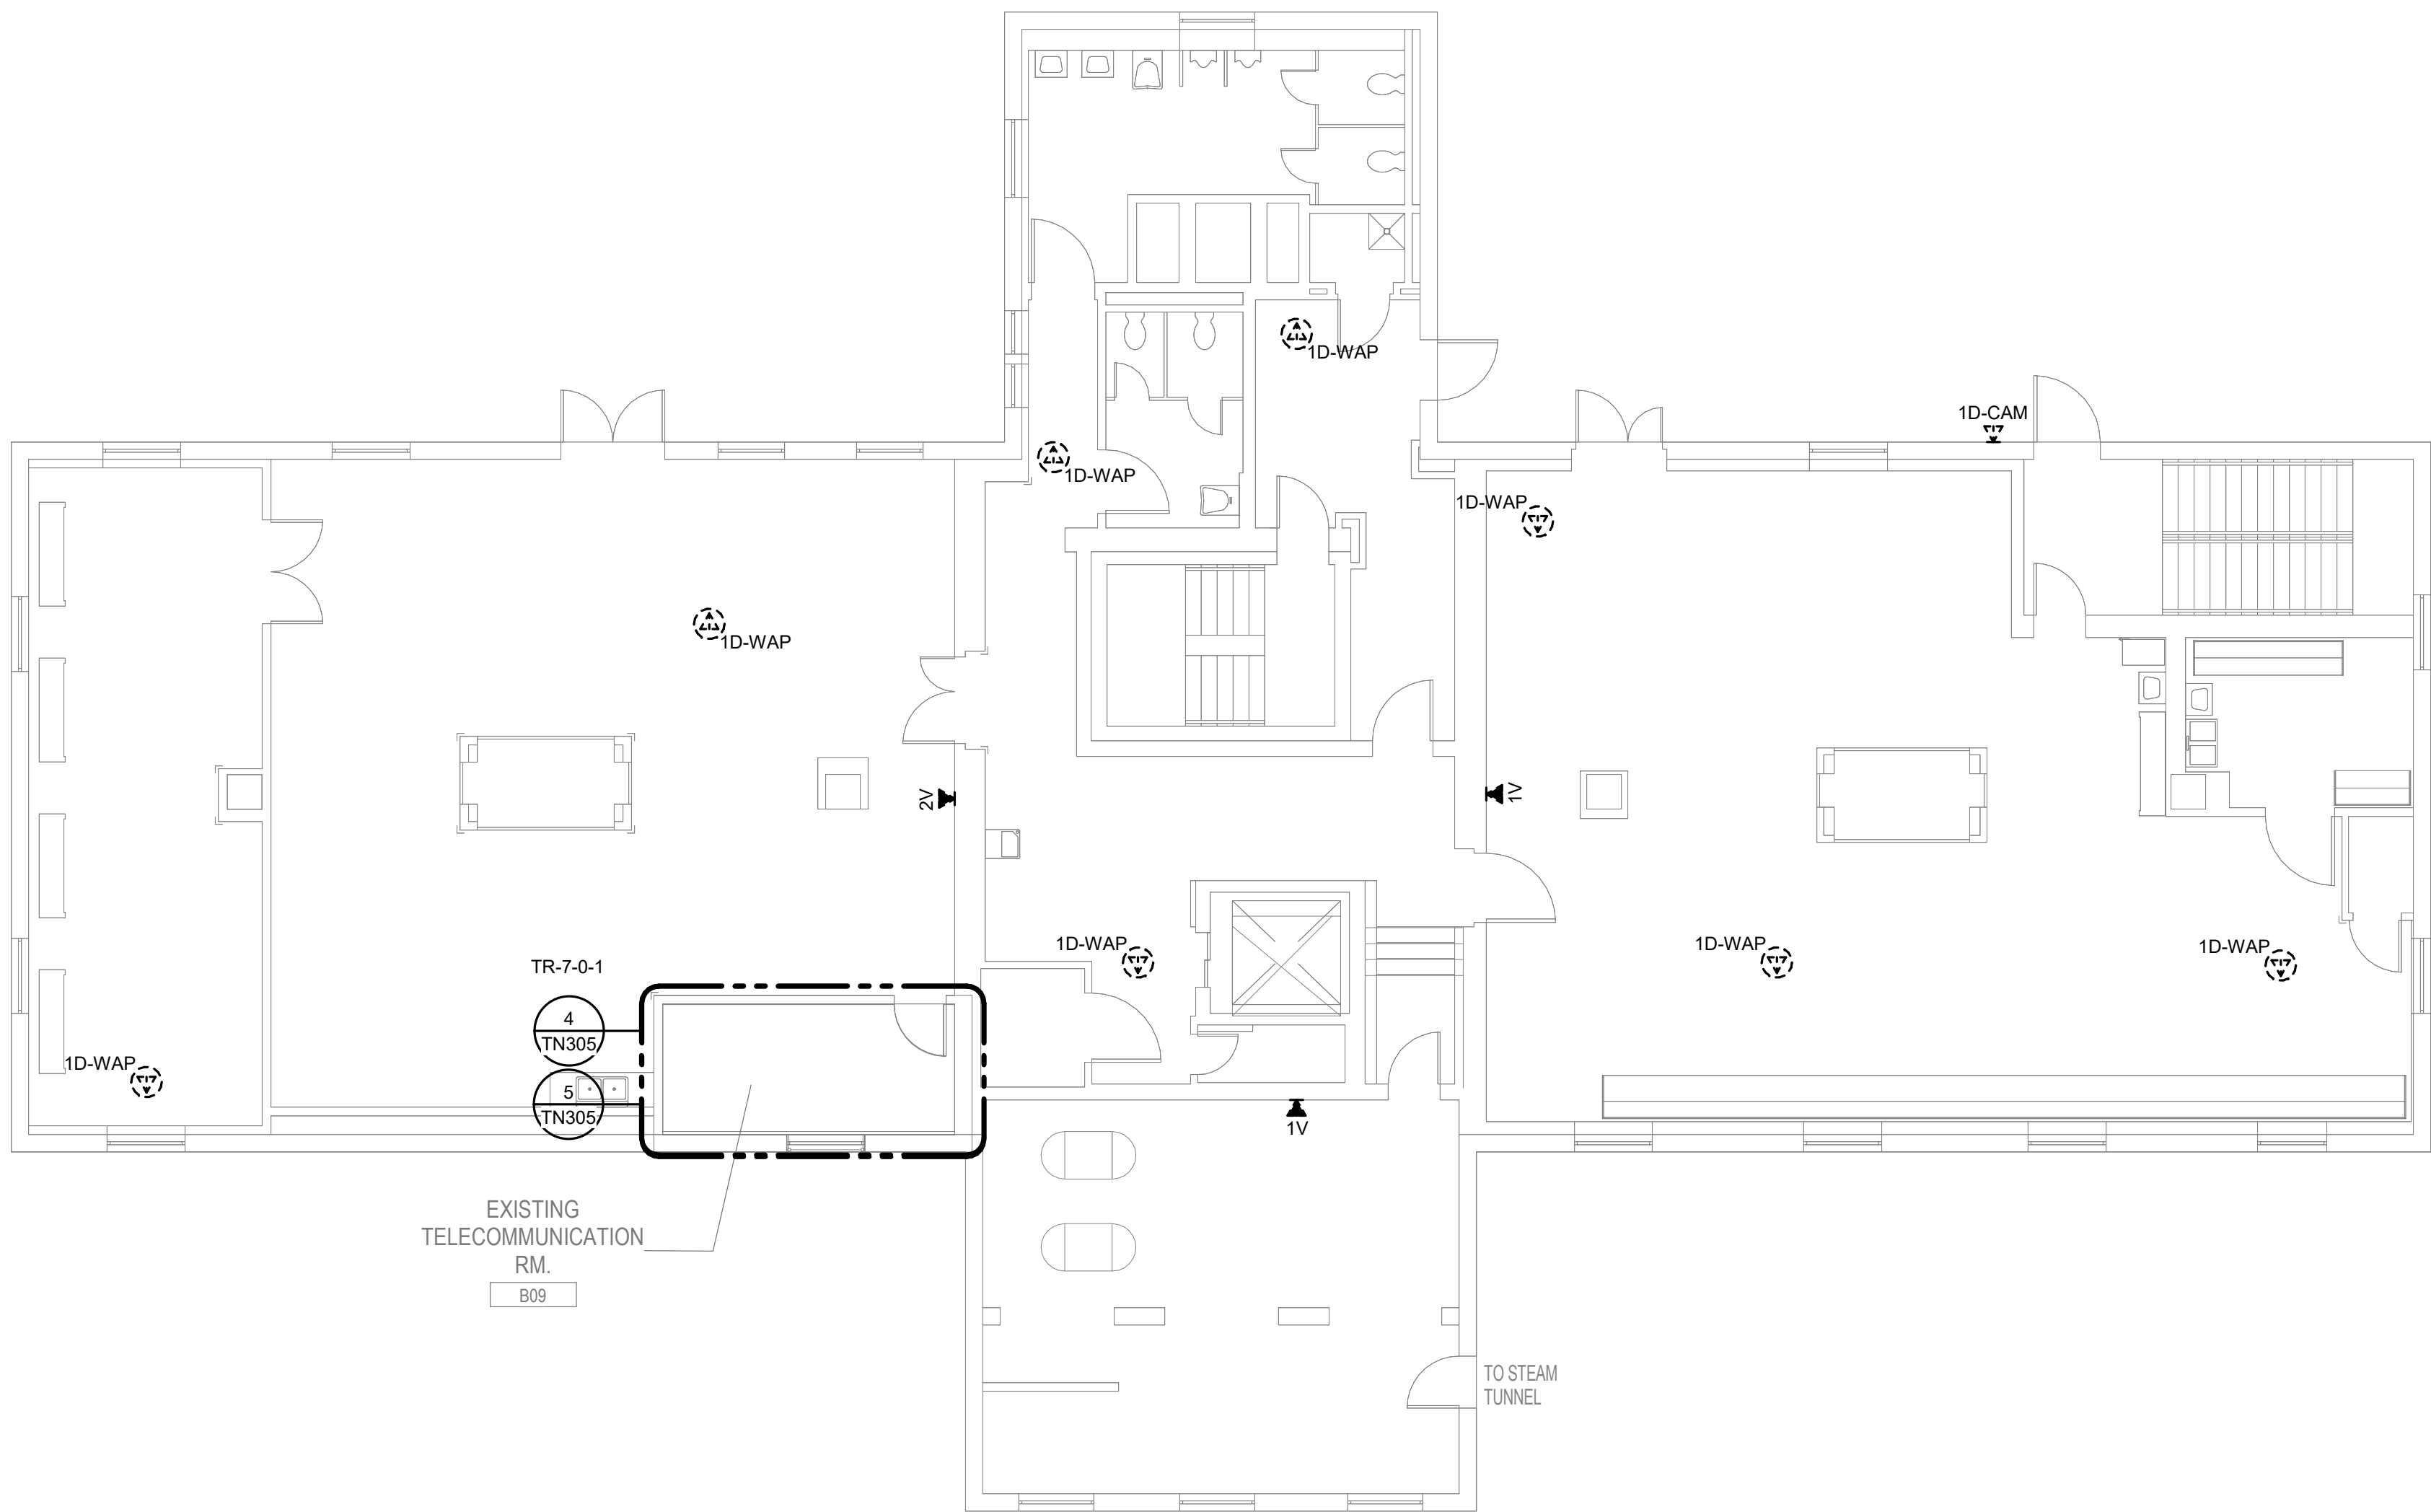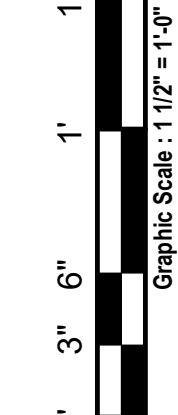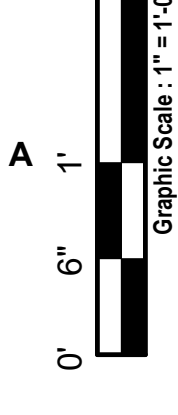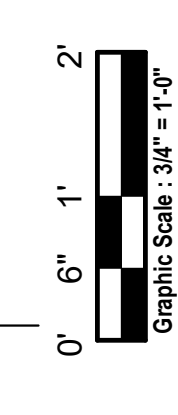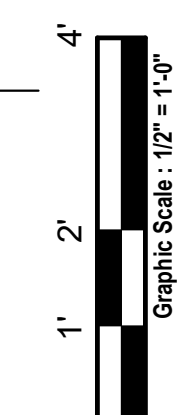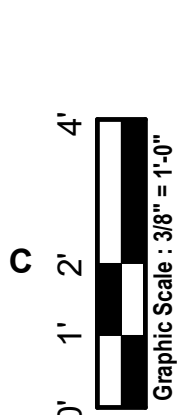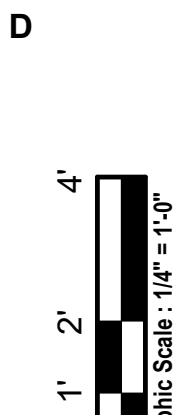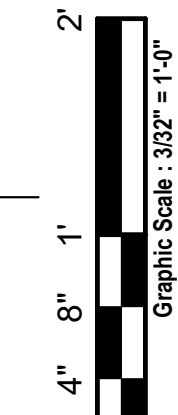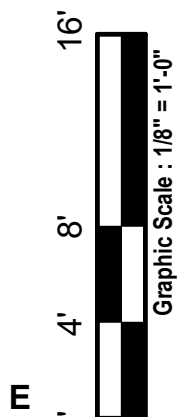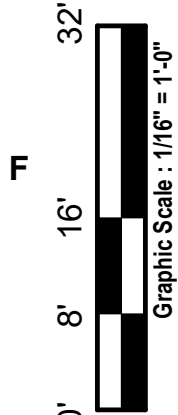

1 BUILDING 07 BASEMENT DEMOLITION PLAN - TECHNOLOGY

1/8" = 1'-0"

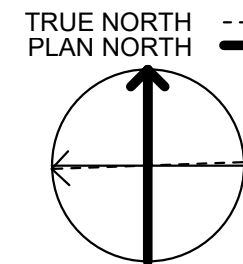

35% SCHEMATIC DESIGN SUBMISSION	5.17.21
65% DESIGN DEVELOPMENT SUBMISSION	6.15.21
65% DESIGN DEVELOPMENT RESUBMISSION	8.25.21
Revisions:	Date:

CONSULTANT

IMEG

15 SUNNEN DRIVE
SUITE 104
ST. LOUIS, MO 63143
P: 314.645.1132 F: 314.645.1173
PROJECT #18004375.03

ARCHITECT/ENGINEER OF RECORD

Romanyk Consulting
Focusing on what matters

Romanyk Consulting Corp. www.romanykconsulting.com
3308 Preston Road, Suite 350-164, Plano, Texas 75093

STAMP

Bicsi
DAVID LARSON
BICS1 ID # 106098
Expires 12-31-25
REGISTERED COMMUNICATIONS DISTRIBUTION DESIGNER

Office of
Construction
and Facilities
Management

VA U.S. Department
of Veterans Affairs

Drawing Title
BUILDING 07 BASEMENT DEMO PLAN -
TECHNOLOGY

Approved:

Phase
FINAL BID DOCUMENTS

Sprinklered
FULLY SPRINKLERED

Project Title
EHRM INFRASTRUCTURE
UPGRADES - MILWAUKEE, WI

Location
5000 W. NATIONAL AVENUE MILWAUKEE, WI

Issue Date
SEPTEMBER 05, 2025

Checked
PHINIE

Drawn
MAIBEJ

Project Number
695-21-700

Building Number
07

Drawing Number
07-TD100

F

E

D

C









B

A


9/3/2025 3:55:28 PM

Autodesk Docs\DOCFM East - Milwaukee EHRM (R24)T24_1804375\03_VA Milwaukee_C.dwt

- SHEET NOTES:**
1. REMOVE ALL NETWORK CABLING TO POINTS OF TERMINATION IN ASSOCIATED DATA CLOSET. REFER TO FLOOR PLANS AND SHEET T1001 FOR TR ROOM LOCATIONS.
 2. REFER TO ARCHITECTURAL PHASING PLANS FOR WHEN EXISTING CABLING IS ALLOWED TO BE DEMOLISHED.
 3. FOR ALL EXISTING WIRELESS ACCESS POINTS AND SURVEILLANCE CAMERAS, DEVICES SHALL REMAIN. SCOPE OF WORK INCLUDES CABLE REPLACEMENT ONLY. COORDINATE WITH COR FOR ANY DOWNTIME OF DEVICES.
 4. EXISTING LOCATIONS OF WORK AREA OUTLETS SHOWN ON THIS SHEET MAY NOT NECESSARILY BE IN THE EXACT LOCATION AS IDENTIFIED.

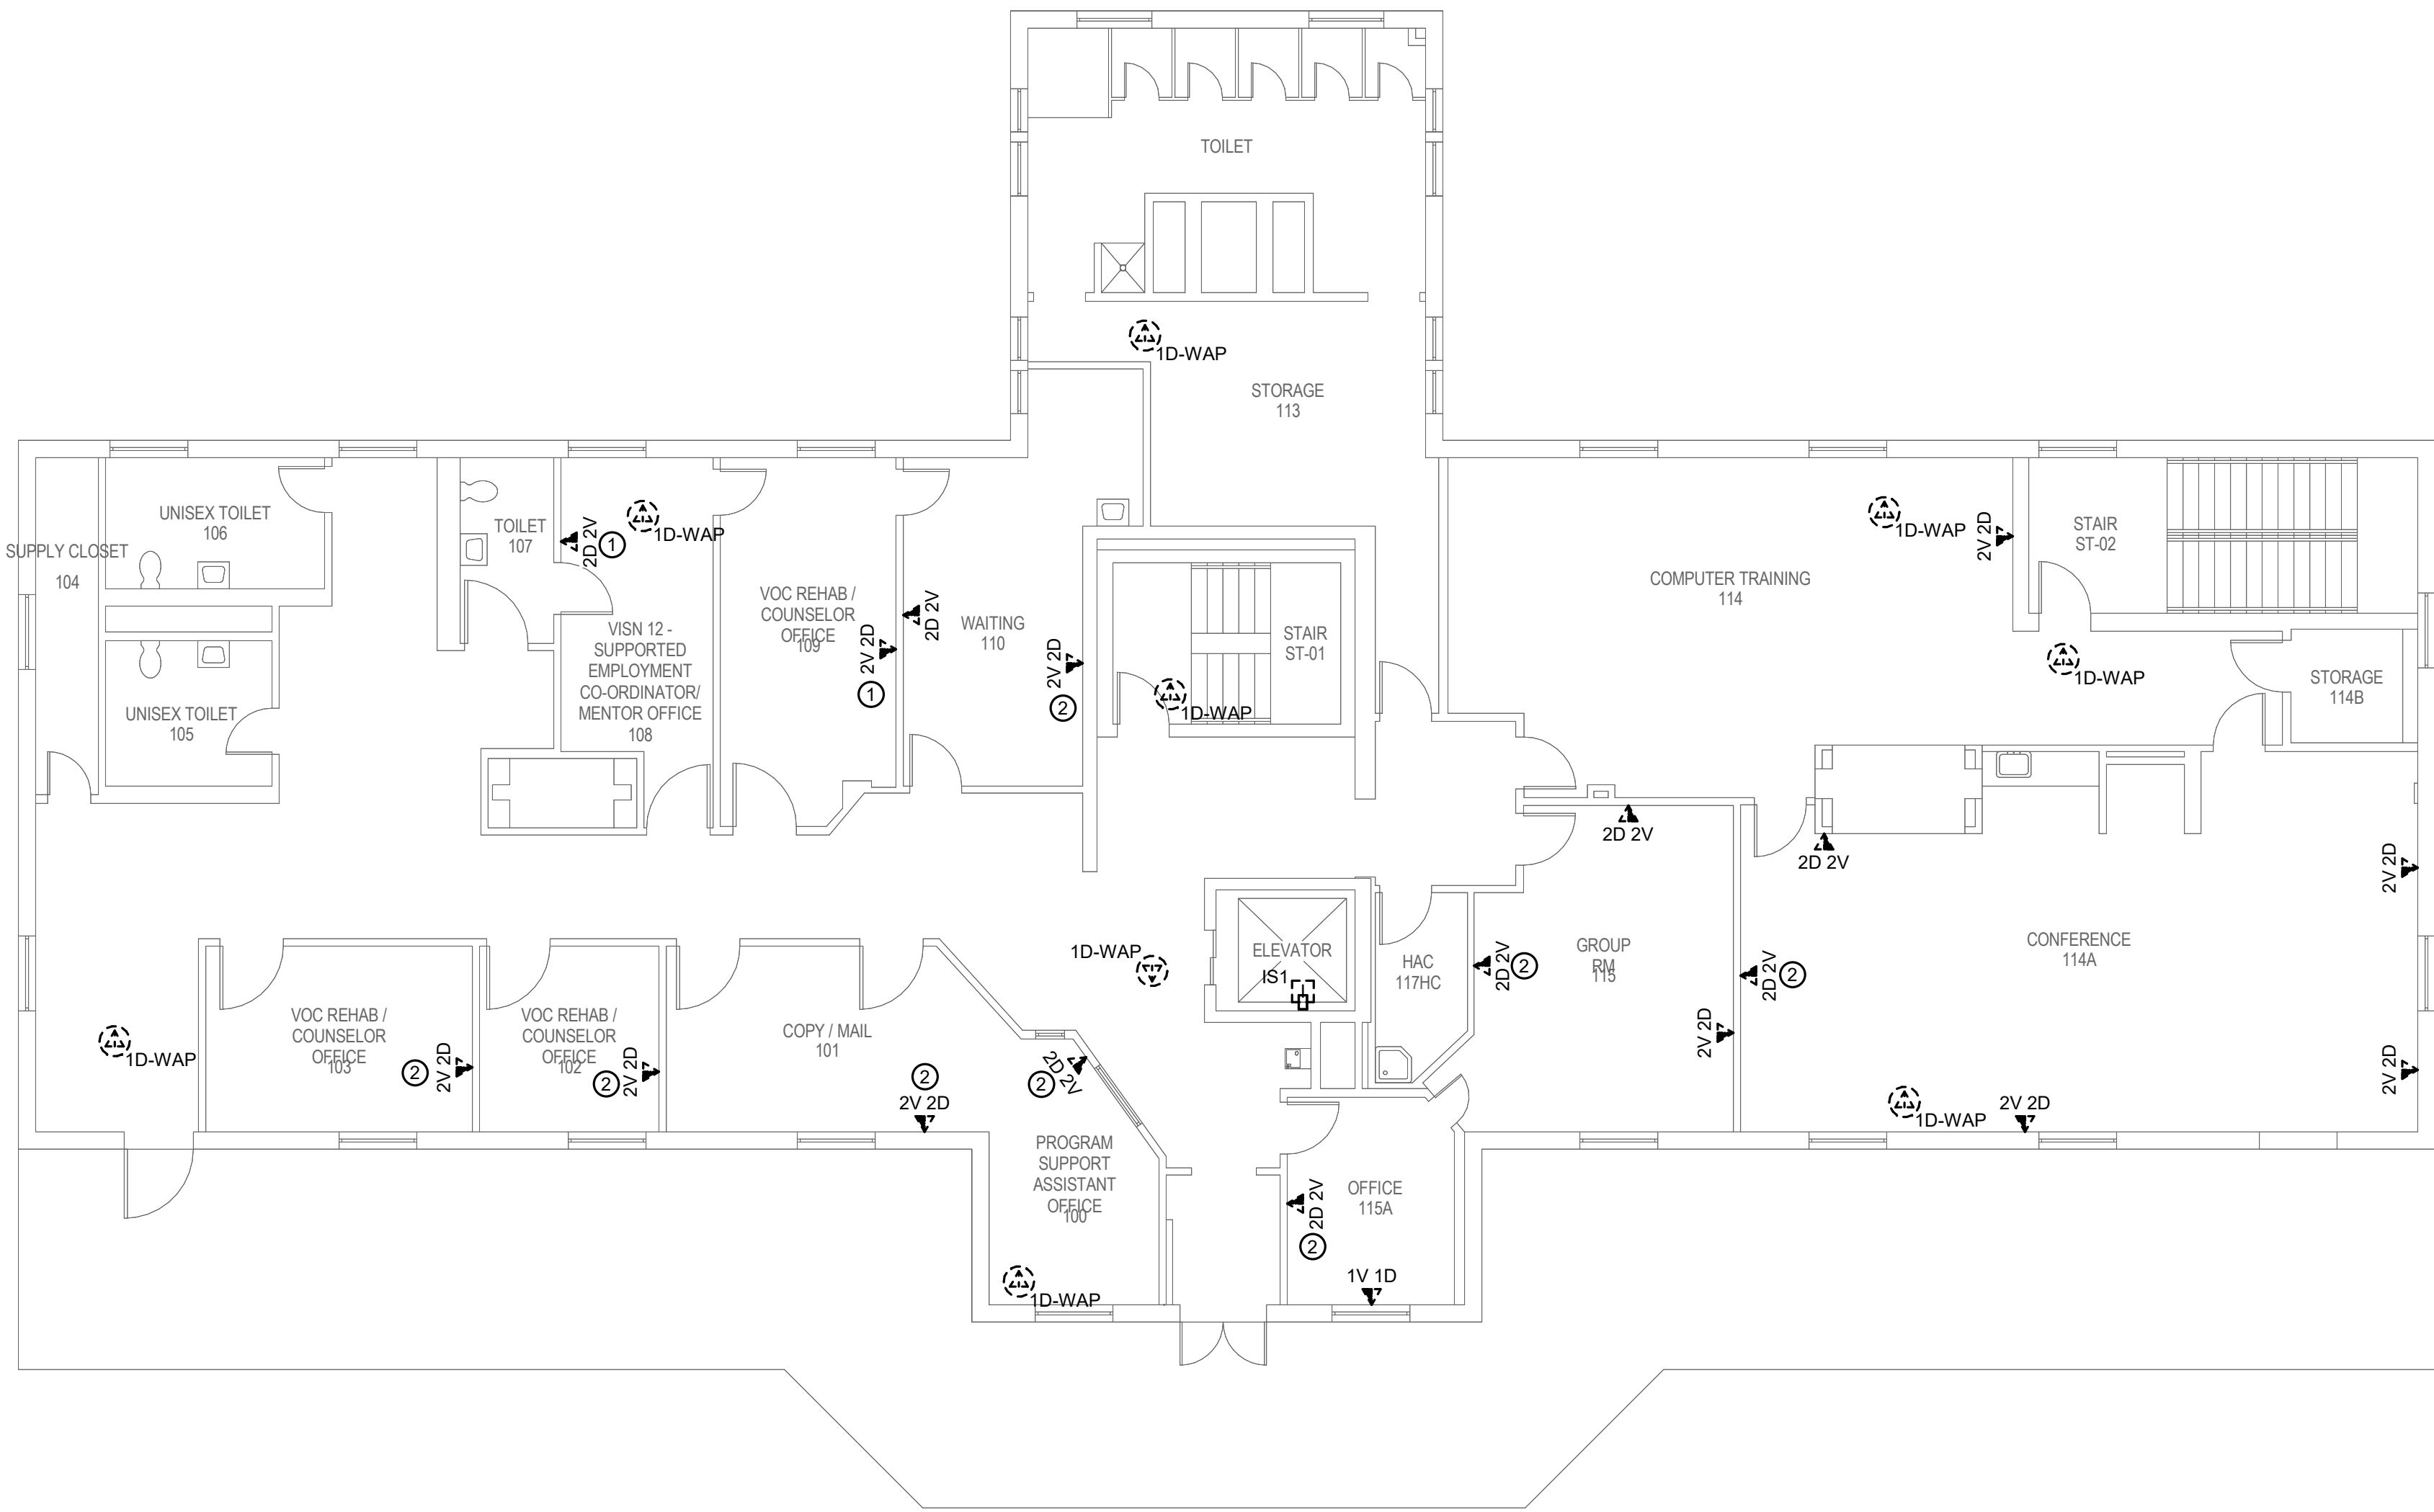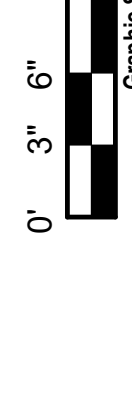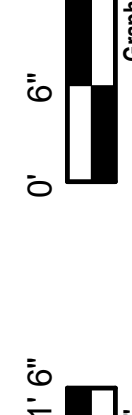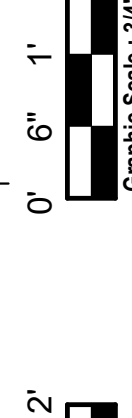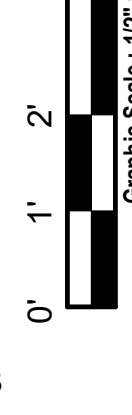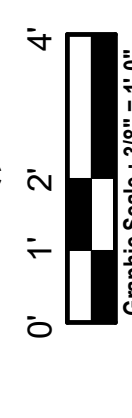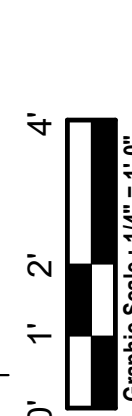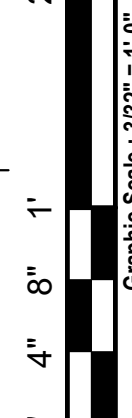

1 BUILDING 07 FIRST FLOOR DEMOLITION PLAN - TECHNOLOGY
1/8" = 1'-0"

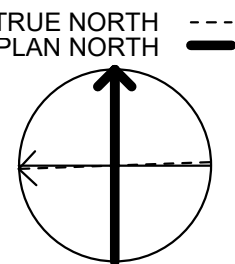

35% SCHEMATIC DESIGN SUBMISSION	5.17.21
65% DESIGN DEVELOPMENT SUBMISSION	6.15.21
65% DESIGN DEVELOPMENT RESUBMISSION	8.25.21
Revisions:	Date:

CONSULTANT

IMEG
The Future is Full of Possibilities
15 SUNNEN DRIVE
SUITE 104
ST. LOUIS, MO 63143
P: 314.645.1132 F: 314.645.1173
PROJECT #18004375.03

ARCHITECT/ENGINEER OF RECORD

Romanyk Consulting
Focusing on what matters
Romanyk Consulting Corp. www.romanykconsulting.com
3308 Preston Road, Suite 350-164, Plano, Texas 75093

STAMP

Bicsi
DAVID LARSON
BICS1 ID # 106098
Expires 12-31-25
REGISTERED COMMUNICATIONS DISTRIBUTION DESIGNER
RCDD

Office of Construction and Facilities Management

VA U.S. Department of Veterans Affairs

Drawing Title
BUILDING 07 FIRST FLOOR DEMO PLAN - TECHNOLOGY

Approved:

Phase
FINAL BID DOCUMENTS

Sprinklered
FULLY SPRINKLERED

Project Title
EHRM INFRASTRUCTURE UPGRADES - MILWAUKEE, WI

Location
5000 W. NATIONAL AVENUE MILWAUKEE, WI

Issue Date
SEPTEMBER 05, 2025

Checked
PHINIE

Drawn
MAIBEJ

Project Number
695-21-700

Building Number
07

Drawing Number
07-TD101

F

E

D

C

B

A

F

E

D

C

B

A

F

E

D

F

E

D

C


B

A


9/3/2025 3:55:30 PM

Autodesk Docs\DOCFM East - Milwaukee EHRM (R24)T24_1804375.03_VA Milwaukee_C.dwt

- SHEET NOTES:**
1. REMOVE ALL NETWORK CABLING TO POINTS OF TERMINATION IN ASSOCIATED DATA CLOSET. REFER TO FLOOR PLANS AND SHEET T1001 FOR TR ROOM LOCATIONS.
 2. REFER TO ARCHITECTURAL PHASING PLANS FOR WHEN EXISTING CABLING IS ALLOWED TO BE DEMOLISHED.
 3. FOR ALL EXISTING WIRELESS ACCESS POINTS AND SURVEILLANCE CAMERAS, DEVICES SHALL REMAIN. SCOPE OF WORK INCLUDES CABLE REPLACEMENT ONLY. COORDINATE WITH COR FOR ANY DOWNTIME OF DEVICES. EXISTING LOCATIONS OF WORK AREA, OUTLETS SHOWN ON THIS SHEET MAY NOT NECESSARILY BE IN THE EXACT LOCATION AS IDENTIFIED.
 - 4.

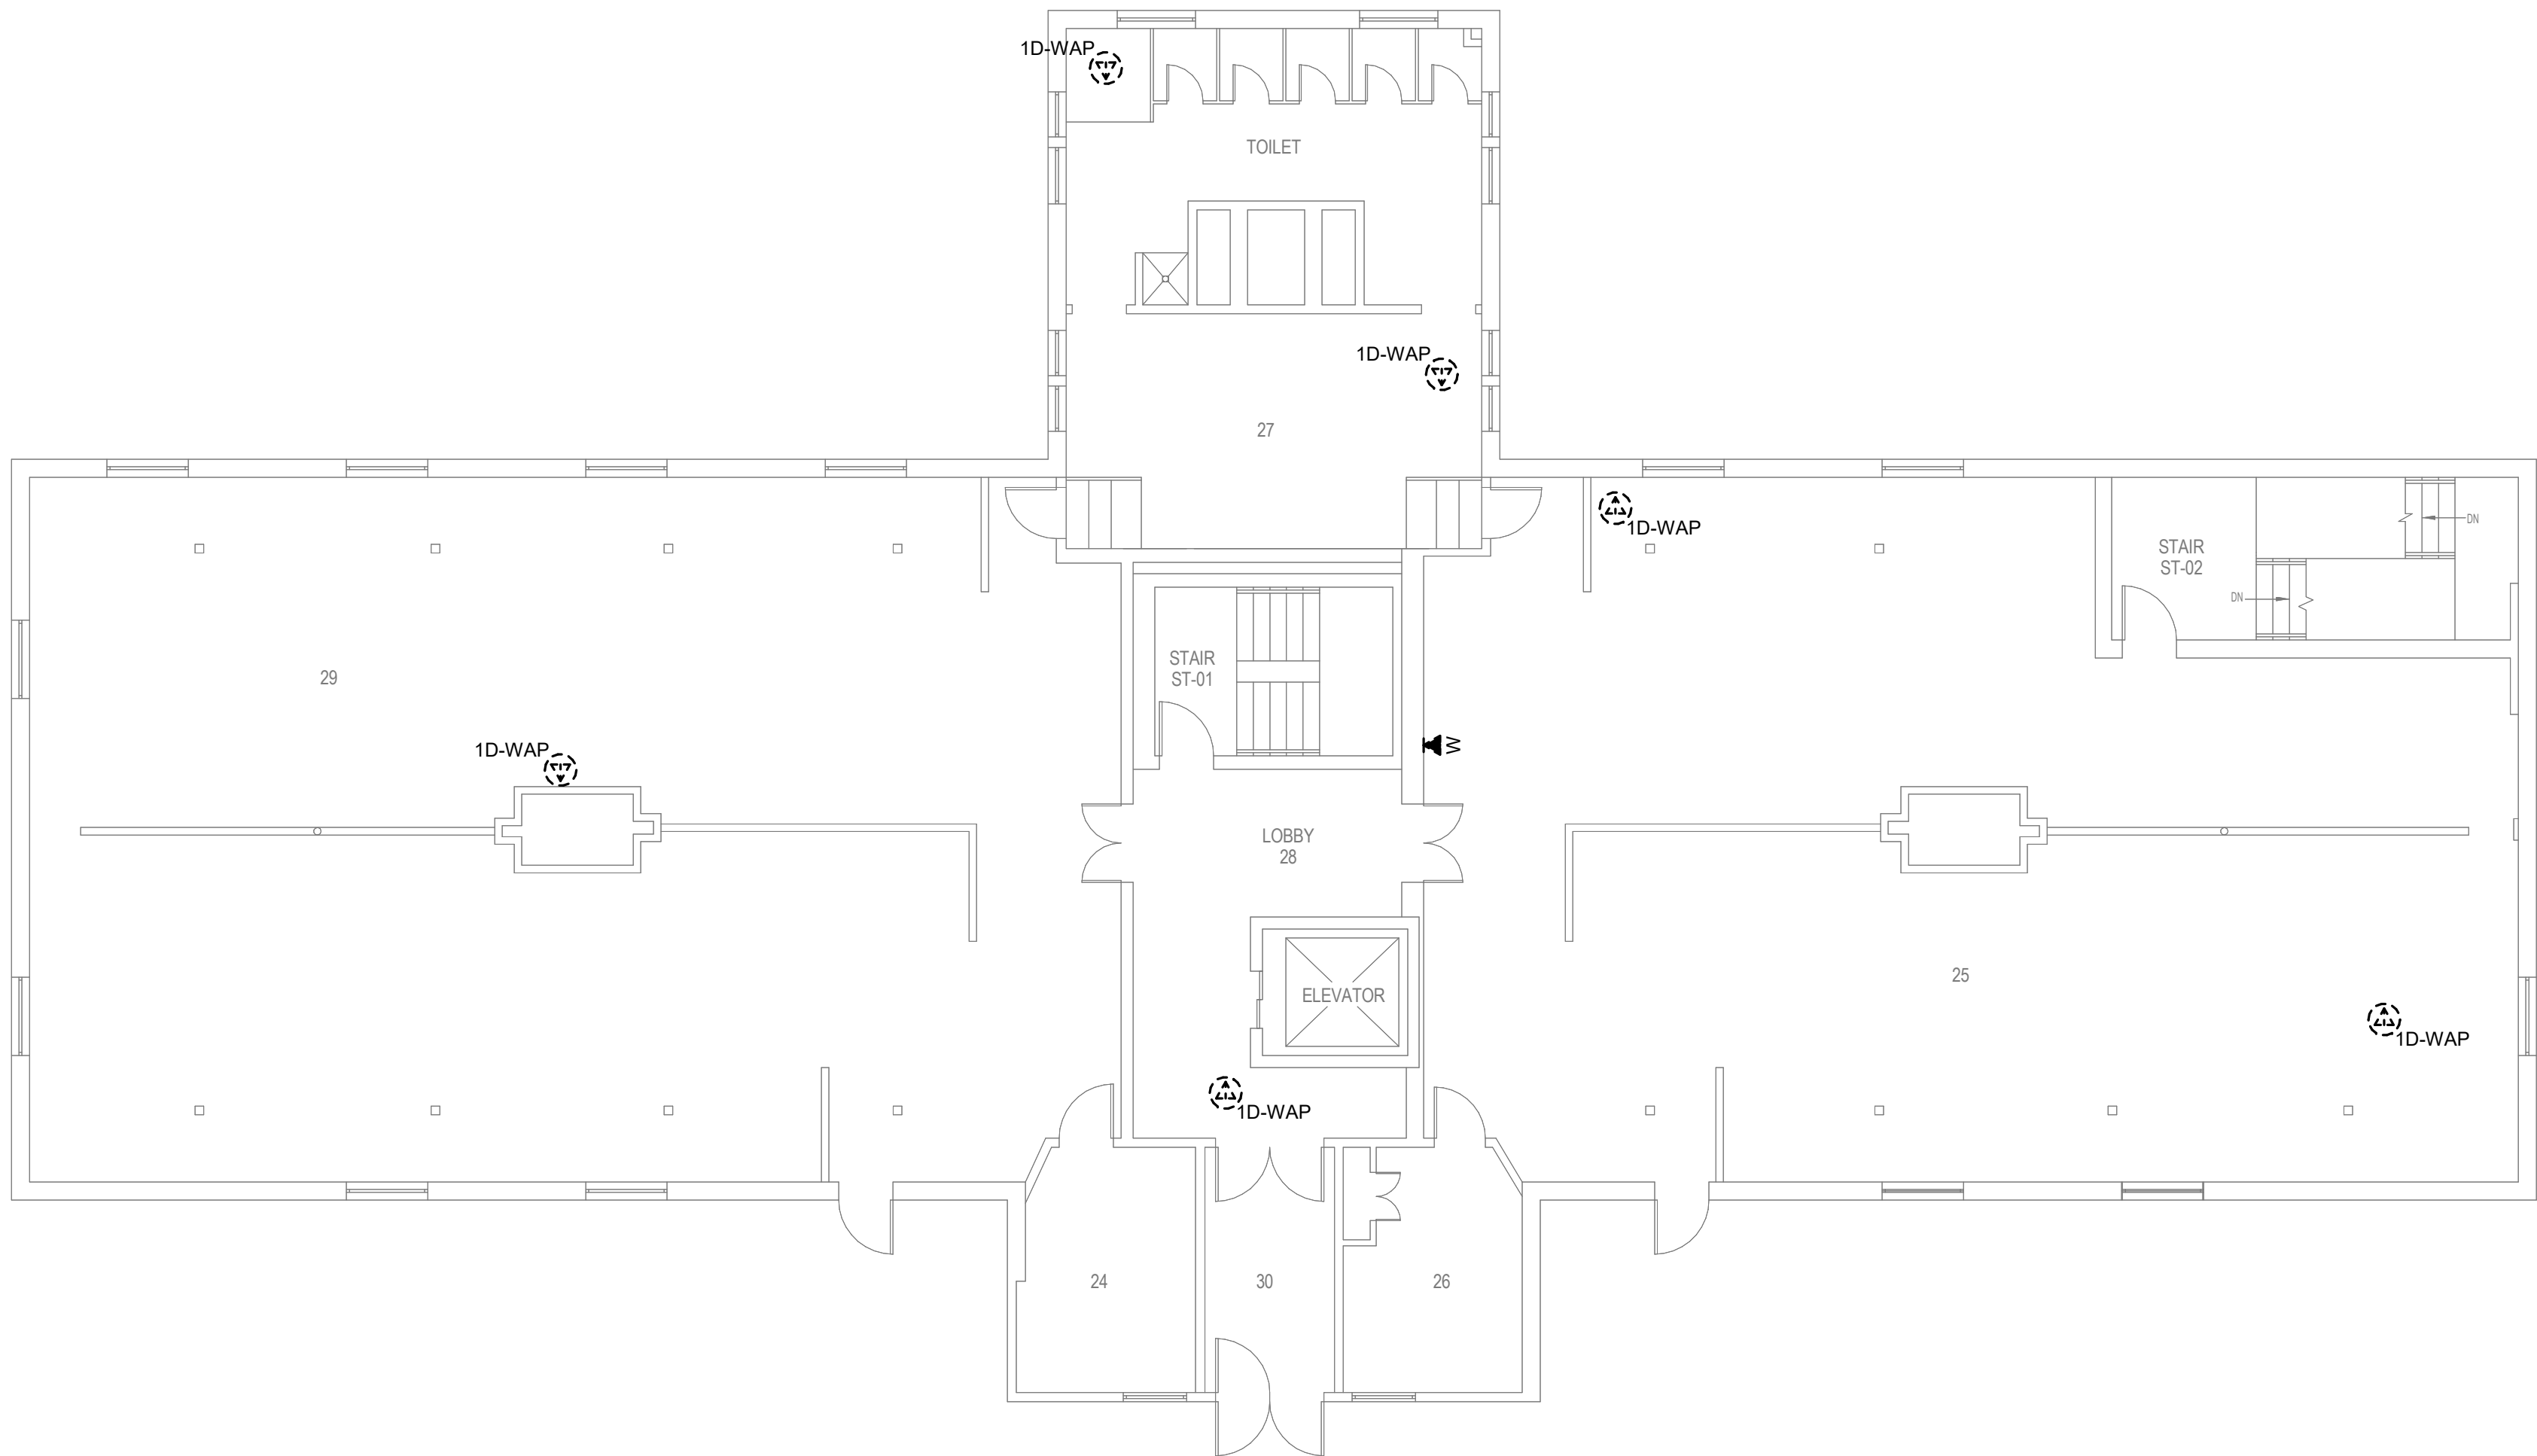

1 BUILDING 07 THIRD FLOOR DEMOLITION PLAN - TECHNOLOGY
1/8" = 1'-0"

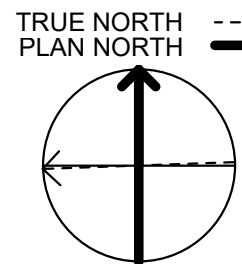

35% SCHEMATIC DESIGN SUBMISSION	5.17.21
65% DESIGN DEVELOPMENT SUBMISSION	6.15.21
65% DESIGN DEVELOPMENT RESUBMISSION	8.25.21
Revisions:	Date:

CONSULTANT

IMEG

15 SUNNEN DRIVE
SUITE 104
ST. LOUIS, MO 63143
P: 314.645.1132 F: 314.645.1173
PROJECT #18004375.03

ARCHITECT/ENGINEER OF RECORD

Romanyk Consulting
Focusing on what matters

Romanyk Consulting Corp. www.romanykconsulting.com
3308 Preston Road, Suite 350-164, Plano, Texas 75093

STAMP

Bicsi
DAVID LARSON
BICS1 ID # 106098
EXPIRES 12-31-25
REGISTERED COMMUNICATIONS DISTRIBUTION DESIGNER

Office of
Construction
and Facilities
Management

VA U.S. Department
of Veterans Affairs

Drawing Title
BUILDING 07 THIRD FLOOR DEMO PLAN -
TECHNOLOGY

Approved:

Phase
FINAL BID DOCUMENTS

Sprinklered
FULLY SPRINKLERED

Project Title
EHRM INFRASTRUCTURE
UPGRADES - MILWAUKEE, WI

Location
5000 W. NATIONAL AVENUE MILWAUKEE, WI

Issue Date
SEPTEMBER 05, 2025


Checked
PHINIE

Drawn
MAIBEJ

Project Number
695-21-700


Building Number
07

Drawing Number
07-TD103

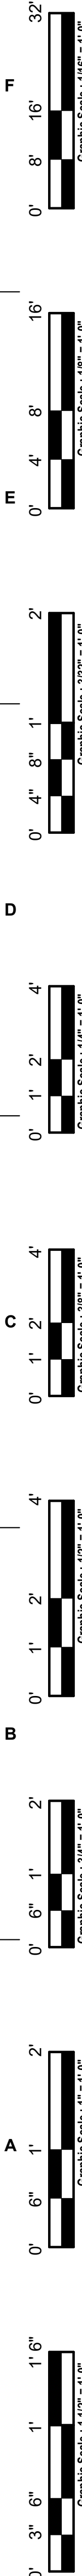

35% SCHEMATIC DESIGN SUBMISSION	5.17.21
65% DESIGN DEVELOPMENT SUBMISSION	6.15.21
65% DESIGN DEVELOPMENT RESUBMISSION	8.25.21
Revisions:	Date:

CONSULTANT

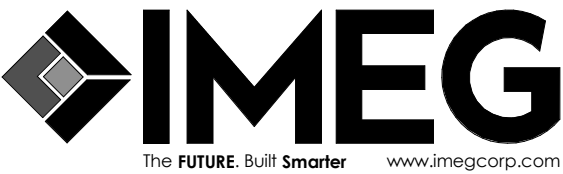

THE FUTURE IS IT'S STRONGER
15 SUNNEN DRIVE
SUITE 104
ST. LOUIS, MO 63143
P: 314.645.1132 F: 314.645.1173
PROJECT #18004375.03

ARCHITECT/ENGINEER OF RECORD



Romanyk Consulting
Focusing on what matters

Romanyk Consulting Corp. www.romanykconsulting.com
3308 Preston Road, Suite 350-164, Plano, Texas 75093

STAMP



REGISTERED COMMUNICATIONS DISTRIBUTION DESIGNER
DAVID LARSON
BICS1 ID # 106098
EXPIRES 12-31-25
RCDD

Office of Construction and Facilities Management



U.S. Department of Veterans Affairs

Drawing Title

BUILDING 07 BASEMENT PLAN - TECHNOLOGY

Approved:

Phase

FINAL BID DOCUMENTS

Sprinklered

FULLY SPRINKLERED

Project Title

EHRM INFRASTRUCTURE UPGRADES - MILWAUKEE, WI

Location

5000 W. NATIONAL AVENUE, MILWAUKEE, WI

Issue Date

SEPTEMBER 05, 2025

Checked

PHINIE

Drawn

MAIBEJ

Project Number


695-21-700

Building Number


07

Drawing Number

07-TN100

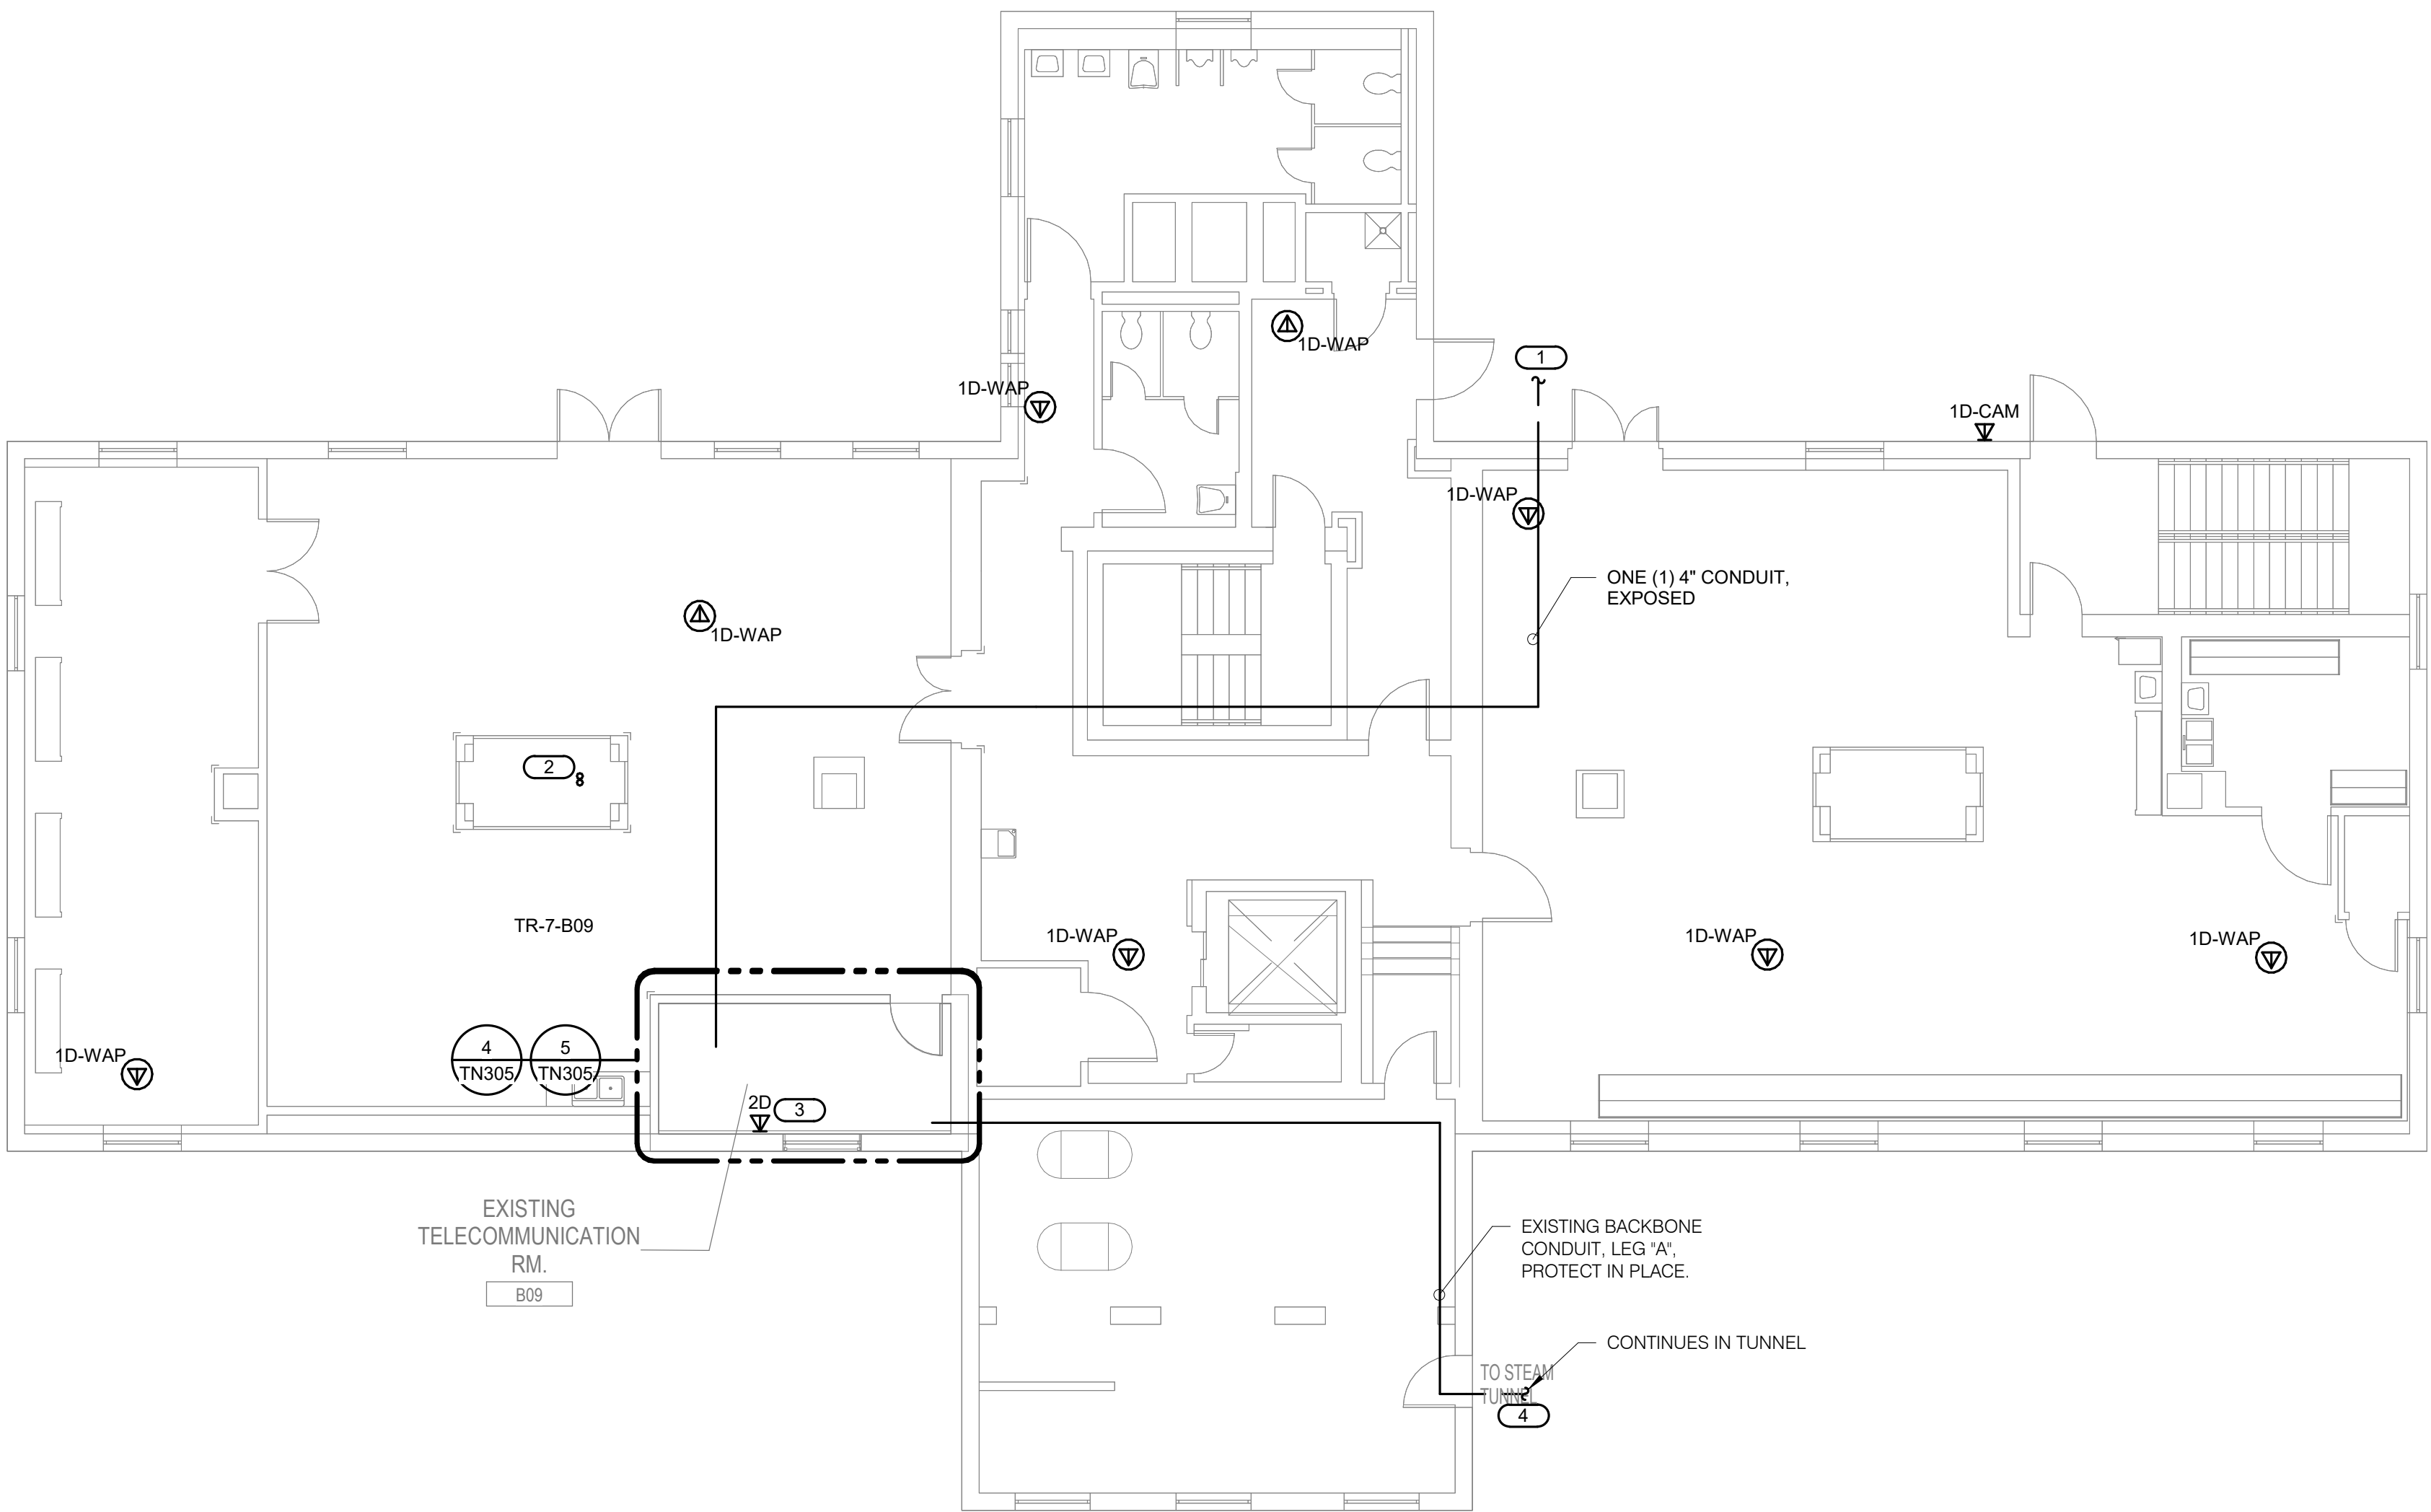


1 BUILDING 07 BASEMENT PLAN - TECHNOLOGY
1/8" = 1'-0"

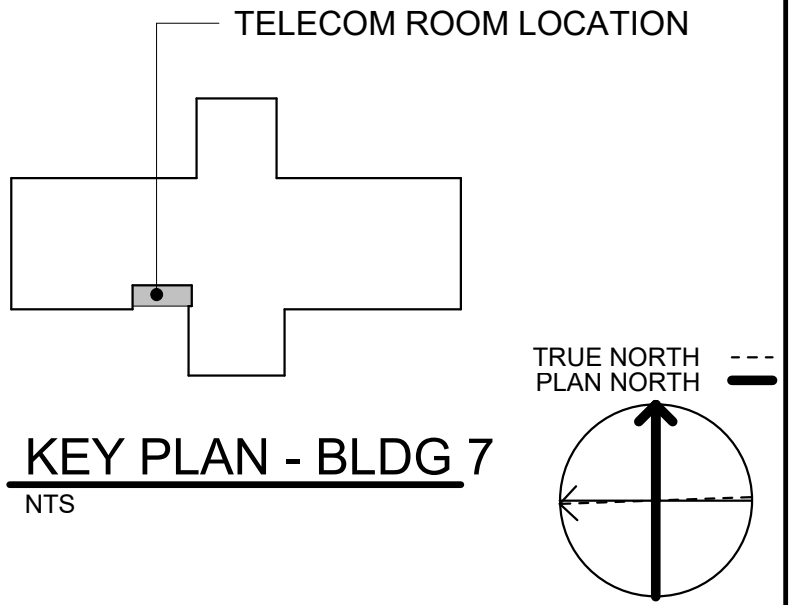

- SHEET NOTES:
- ALL NETWORK CABLES ON THIS SHEET SHALL TERMINATE IN TR-7-B09.
 - REFER TO CIVIL DRAWINGS AND T1003 FOR ADDITIONAL PATHWAY INFORMATION.
 - CONTRACTOR TO PROVIDE NEW J-HOOK ROUTES FOR ALL NEW CABLING. J-HOOK SIZE AND QUANTITY TO BE PER MANUFACTURER RECOMMENDATIONS.
 - REFER TO TN500-TN509 FOR RISER DIAGRAMS.
 - REFER TO SHEET TN402 FOR PENETRATION DETAILS.
 - THESE DRAWINGS MAKE THE BEST ATTEMPT TO IDENTIFY EXISTING DATA DROPS/WORK AREA OUTLETS. AS LONG AS THE TOTAL NEWLY INSTALLED DATA DROP COUNT DOES NOT VARY +/- 10% IDENTIFIED ON THESE DRAWINGS, THE CONTRACTOR'S SCOPE SHALL BE UNCHANGED.
 - NEW WORK AREA OUTLETS SHALL BE LOCATED IN EXISTING BOXES. WORK AREA OUTLETS SHOWN ON THIS SHEET MAY NOT BE IN THE EXACT LOCATION AS IDENTIFIED.
 - CONTRACTOR TO INCLUDE AN ALLOWANCE FOR 10% ADDITIONAL 2-PORTS CAT6A INFORMATION OUTLETS IN THEIR PROPOSAL FOR THIS SHEET. FUTURE INFORMATION OUTLET LOCATIONS WILL BE DETERMINED BY THE VA AT A LATER DATE.

- KEYNOTES: C #
- LEG "B" BACKBONE CABLING PATH. REFER TO SITE PLAN ON SHEET T1003 FOR ADDITIONAL INFORMATION.
 - TWO (2) 4" PATHWAYS TO LEVEL ABOVE.
 - JCI PACS PANEL LOCATION. GC TO COORDINATE EXACT LOCATION AND HEIGHT WITH COR TO RE-CONNECT TO SWITCH/RACK TE IN SAME ROOM WITH CAT6A CABLE AS NECESSARY.
 - EXISTING BACKBONE ENTRY POINT, PROTECT IN PLACE. DEMOLISH EXISTING FIBER OPTIC CABLE TO POINTS OF TERMINATION AFTER REDUNDANT PATH IS INSTALLED AND OPERATIONAL. REFER TO ARCHITECTURAL PHASING PLAN FOR ADDITIONAL INFORMATION. CONDUIT ENTERS ON LOWER LEVEL.

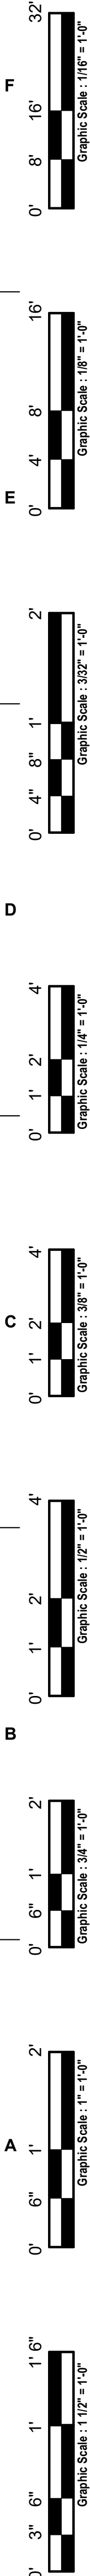

F

E

D

C

B


A

9/2/2025 3:55:31 PM


Autodesk Docs\DCFM East - Milwaukee EHRM (R24)T24_1804375\03_VA MilwEHRM_C.dwg

- SHEET NOTES:**
 - REFER TO 1/TN400 FOR TECHNOLOGY ROUGH-IN DETAIL.
 - ALL NETWORK CABLES ON THIS SHEET SHALL TERMINATE IN TIS 7-509.
 - CONTRACTOR TO PROVIDE NEW J-HOOK ROUTES FOR ALL NEW CABLING. J-HOOK SIZE AND QUANTITY TO BE PER MANUFACTURER RECOMMENDATIONS.
 - REFER TO TN500-TN509 FOR RISER DIAGRAMS.
 - REFER TO SHEET TN402 FOR PENETRATION DETAILS.
 - THESE DRAWINGS MAKE THE BEST ATTEMPT TO IDENTIFY EXISTING DATA DROPS/WORK AREA OUTLETS. AS LONG AS THE TOTAL NEWLY INSTALLED DATA DROP COUNT DOES NOT VARY +/- 10% IDENTIFIED ON THESE DRAWINGS, THE CONTRACTOR'S SCOPE SHALL BE UNCHANGED.
 - NEW WORK AREA OUTLETS SHALL BE LOCATED IN EXISTING BOXES. WORK AREA OUTLETS SHOWN ON THIS SHEET MAY NOT BE IN THE EXACT LOCATION AS IDENTIFIED.
 - CONTRACTOR TO INCLUDE AN ALLOWANCE FOR 10% ADDITIONAL 2-PORTS CAT6A INFORMATION OUTLETS IN THEIR PROPOSAL FOR THIS SHEET. FUTURE INFORMATION OUTLET LOCATIONS WILL BE DETERMINED BY THE VA AT A LATER DATE.

KEYNOTES: **C** **#**
 - TWO (2) 4" PATHWAYS TO LEVEL BELOW.

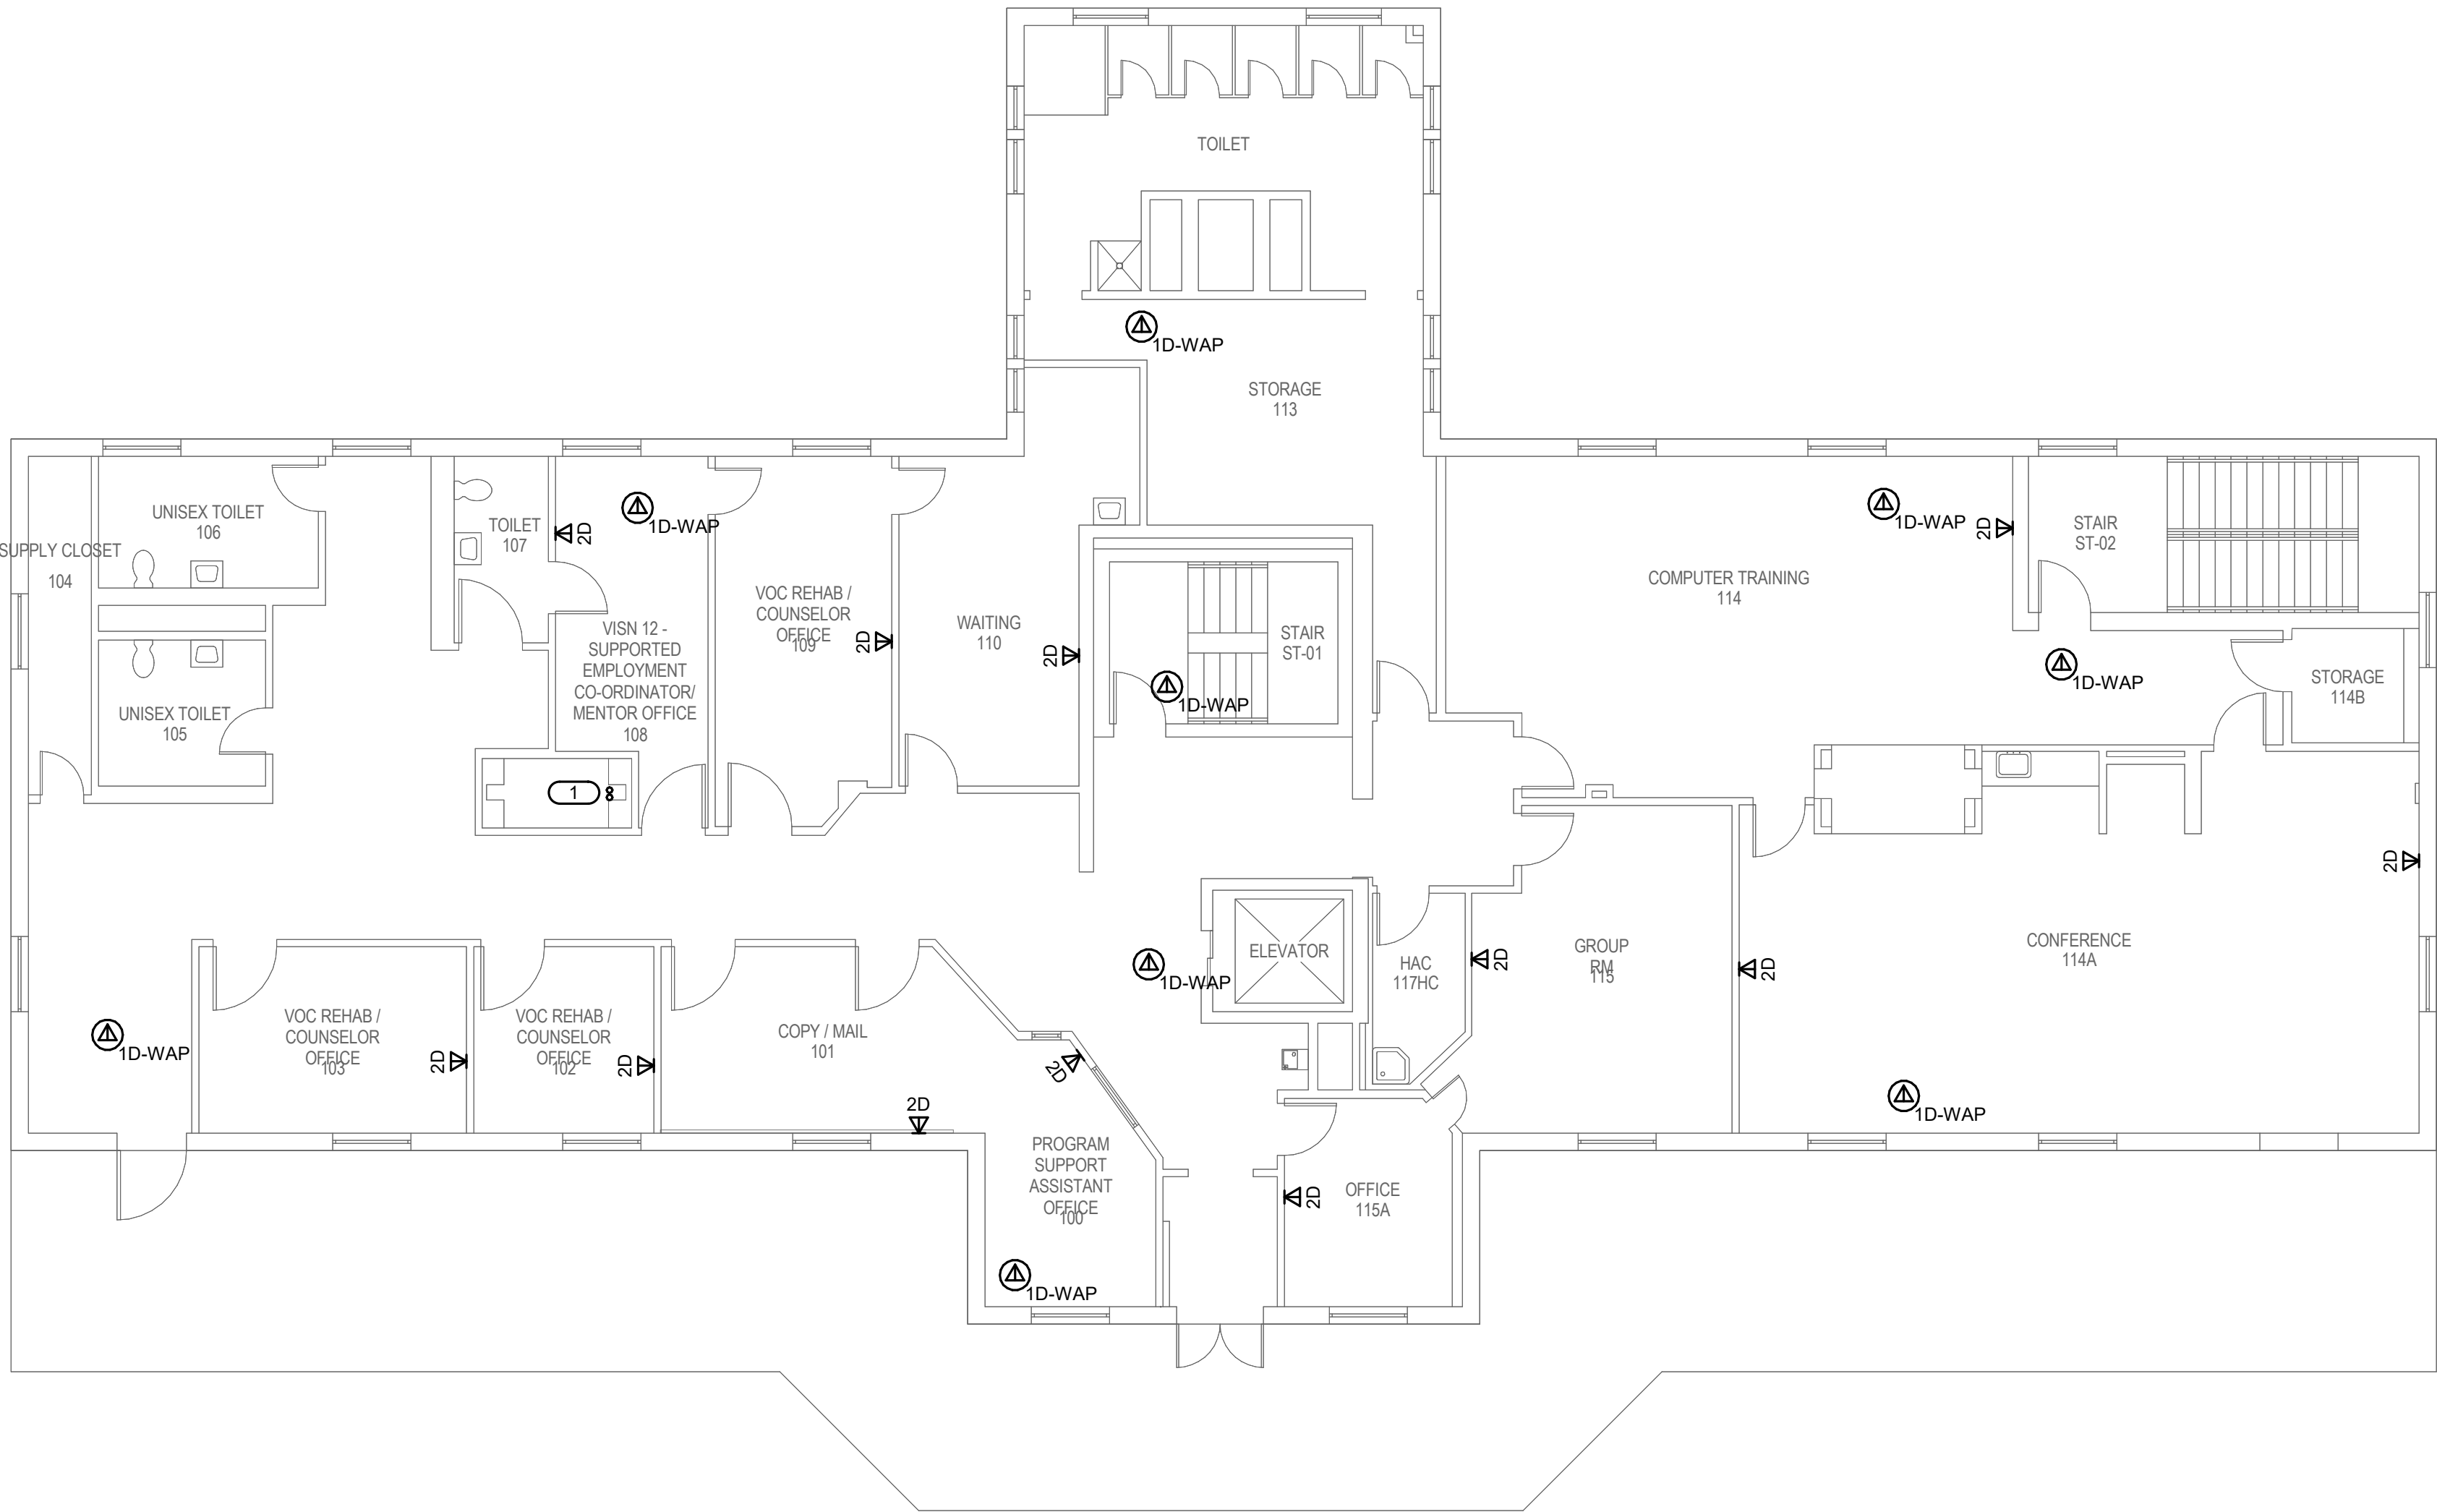

1 **BUILDING 07 FIRST FLOOR PLAN - TECHNOLOGY**
1/8" = 1'-0"

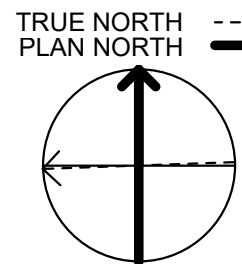

35% SCHEMATIC DESIGN SUBMISSION	5.17.21
65% DESIGN DEVELOPMENT SUBMISSION	6.15.21
65% DESIGN DEVELOPMENT RESUBMISSION	8.25.21
Revisions:	Date:

CONSULTANT



THE FUTURE IS IT'S STRONGER
www.imegcorp.com
15 SUNNEN DRIVE
SUITE 104
ST. LOUIS, MO 63143
P: 314.645.1132 F: 314.645.1173
PROJECT #18004375.03

ARCHITECT/ENGINEER OF RECORD



Romanyk Consulting
Focusing on what matters
Romanyk Consulting Corp. www.romanykconsulting.com
3308 Preston Road, Suite 350-164, Plano, Texas 75093

STAMP



Office of
Construction
and Facilities
Management

 U.S. Department
of Veterans Affairs

Drawing Title BUILDING 07 FIRST FLOOR PLAN - TECHNOLOGY
Approved:

Phase FINAL BID DOCUMENTS
Sprinklered FULLY SPRINKLERED

Project Title EHRM INFRASTRUCTURE UPGRADES - MILWAUKEE, WI
Location 5000 W. NATIONAL AVENUE, MILWAUKEE, WI
Issue Date SEPTEMBER 05, 2025
Checked PHINIE
Drawn MAIBEJ

Project Number 695-21-700
Building Number 07
Drawing Number 07-TN101

F

E

D

C


B

A


9/3/2025 3:45:32 PM

Autodesk Docs\DOCFM East - Milwaukee EHRM (R24)T24_1804375\03_VA Milwaukee C.dwt

- SHEET NOTES:**
1. REFER TO 1/TN400 FOR TECHNOLOGY ROUGH-IN DETAIL.
 2. ALL NETWORK CABLES ON THIS SHEET SHALL TERMINATE IN TRS-7-509.
 3. CONTRACTOR TO PROVIDE NEW J-HOOK ROUTES FOR ALL NEW CABLING. J-HOOK SIZE AND QUANTITY TO BE PER MANUFACTURER RECOMMENDATIONS.
 4. REFER TO TN500-TN509 FOR RISER DIAGRAMS.
 5. REFER TO SHEET TN402 FOR PENETRATION DETAILS.
 6. THESE DRAWINGS MAKE THE BEST ATTEMPT TO IDENTIFY EXISTING DATA DROPS/WORK AREA OUTLETS. AS LONG AS THE TOTAL NEWLY INSTALLED DATA DROP COUNT DOES NOT VARY +/- 10% IDENTIFIED ON THESE DRAWINGS, THE CONTRACTOR'S SCOPE SHALL BE UNCHANGED.
 7. NEW WORK AREA OUTLETS SHALL BE LOCATED IN EXISTING BOXES. WORK AREA OUTLETS SHOWN ON THIS SHEET MAY NOT BE IN THE EXACT LOCATION AS IDENTIFIED.
 8. CONTRACTOR TO INCLUDE AN ALLOWANCE FOR 10% ADDITIONAL 2-PORTS CAT6A INFORMATION OUTLETS IN THEIR PROPOSAL FOR THIS SHEET. FUTURE INFORMATION OUTLET LOCATIONS WILL BE DETERMINED BY THE VA AT A LATER DATE.
- KEYNOTES:** (#)
1. TWO (2) 4" PATHWAYS TO LEVEL BELOW.

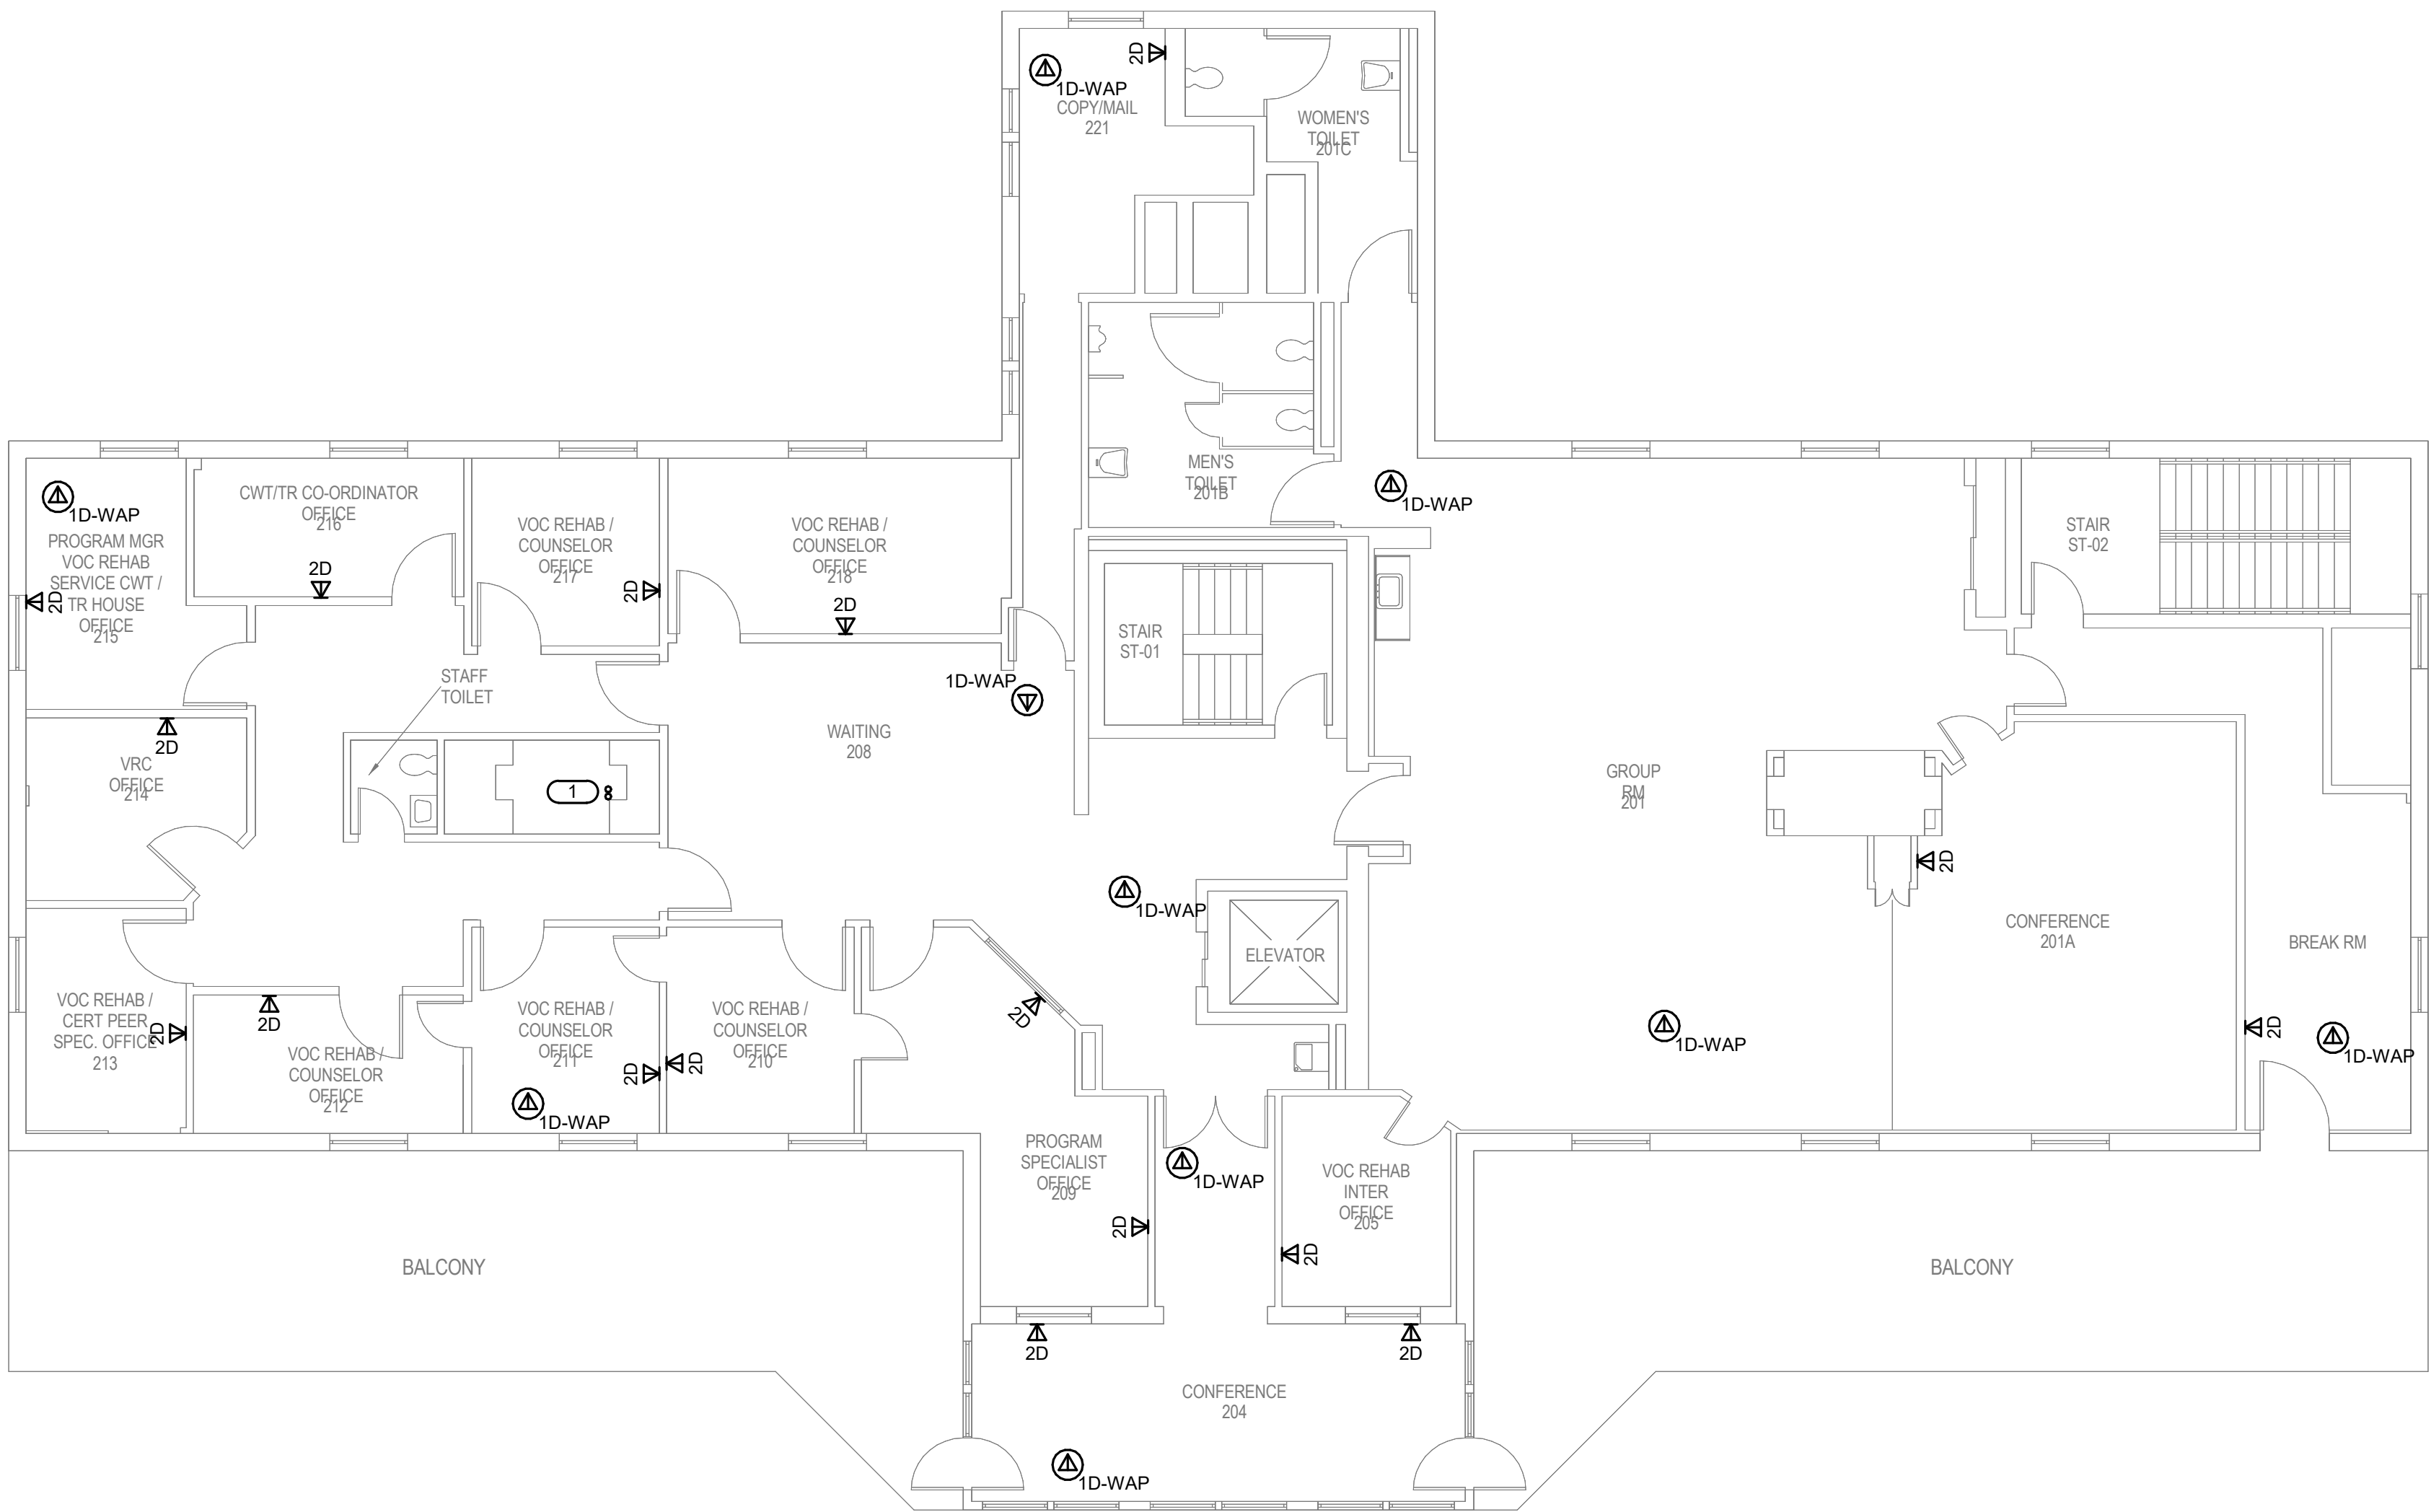

1 BUILDING 07 SECOND FLOOR PLAN - TECHNOLOGY
1/8" = 1'-0"

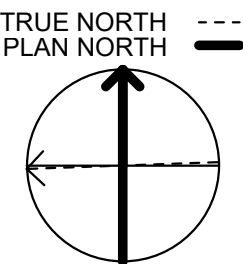

35% SCHEMATIC DESIGN SUBMISSION	5.17.21
65% DESIGN DEVELOPMENT SUBMISSION	6.15.21
65% DESIGN DEVELOPMENT RESUBMISSION	8.25.21
Revisions:	Date:

CONSULTANT

IMEG
The Future Built Smarter www.imegcorp.com
15 SUNNEN DRIVE
SUITE 104
ST. LOUIS, MO 63143
P: 314.645.1132 F: 314.645.1173
PROJECT #18004375.03

ARCHITECT/ENGINEER OF RECORD

Romanyk Consulting
Focusing on what matters
Romanyk Consulting Corp. www.romanykconsulting.com
3308 Preston Road, Suite 350-164, Plano, Texas 75093

STAMP

Bicsi
DAVID LARSON
BICS1 ID # 106098
EXPIRES 12-31-25
REGISTERED COMMUNICATIONS DISTRIBUTION DESIGNER
RCDD

Office of
Construction
and Facilities
Management

VA U.S. Department
of Veterans Affairs

Drawing Title
**BUILDING 07 SECOND FLOOR PLAN -
TECHNOLOGY**

Approved:

Phase
FINAL BID DOCUMENTS

Sprinklered
FULLY SPRINKLERED

Project Title
**EHRM INFRASTRUCTURE
UPGRADES - MILWAUKEE, WI**

Location
5000 W. NATIONAL AVENUE MILWAUKEE, WI

Issue Date
SEPTEMBER 05, 2025

Checked
PHINIE

Drawn
MAIBEJ

Project Number
695-21-700

Building Number
07

Drawing Number
07-TN102

- SHEET NOTES:
1. NO WORK SHOWN ON THIS SHEET. SHOWN FOR REFERENCE ONLY.







2. REFER TO TN500-TN509 FOR RISER DIAGRAMS.

3. REFER TO SHEET TN402 FOR PENETRATION DETAILS.

4. THESE DRAWINGS MAKE THE BEST ATTEMPT TO IDENTIFY EXISTING DATA DROPS/WORK AREA OUTLETS. AS LONG AS THE TOTAL NEWLY INSTALLED DATA DROP COUNT DOES NOT VARY +/- 10% IDENTIFIED ON THESE DRAWINGS, THE CONTRACTOR'S SCOPE SHALL BE UNCHANGED.

5. NEW WORK AREA OUTLETS SHALL BE LOCATED IN EXISTING BOXES. WORK AREA OUTLETS SHOWN ON THIS SHEET MAY NOT BE IN THE EXACT LOCATION AS IDENTIFIED.


6. CONTRACTOR TO INCLUDE AN ALLOWANCE FOR 10% ADDITIONAL 2-PORTS CAT6A INFORMATION OUTLETS IN THEIR PROPOSAL FOR THIS SHEET. FUTURE INFORMATION OUTLET LOCATIONS WILL BE DETERMINED BY THE VA AT A LATER DATE.

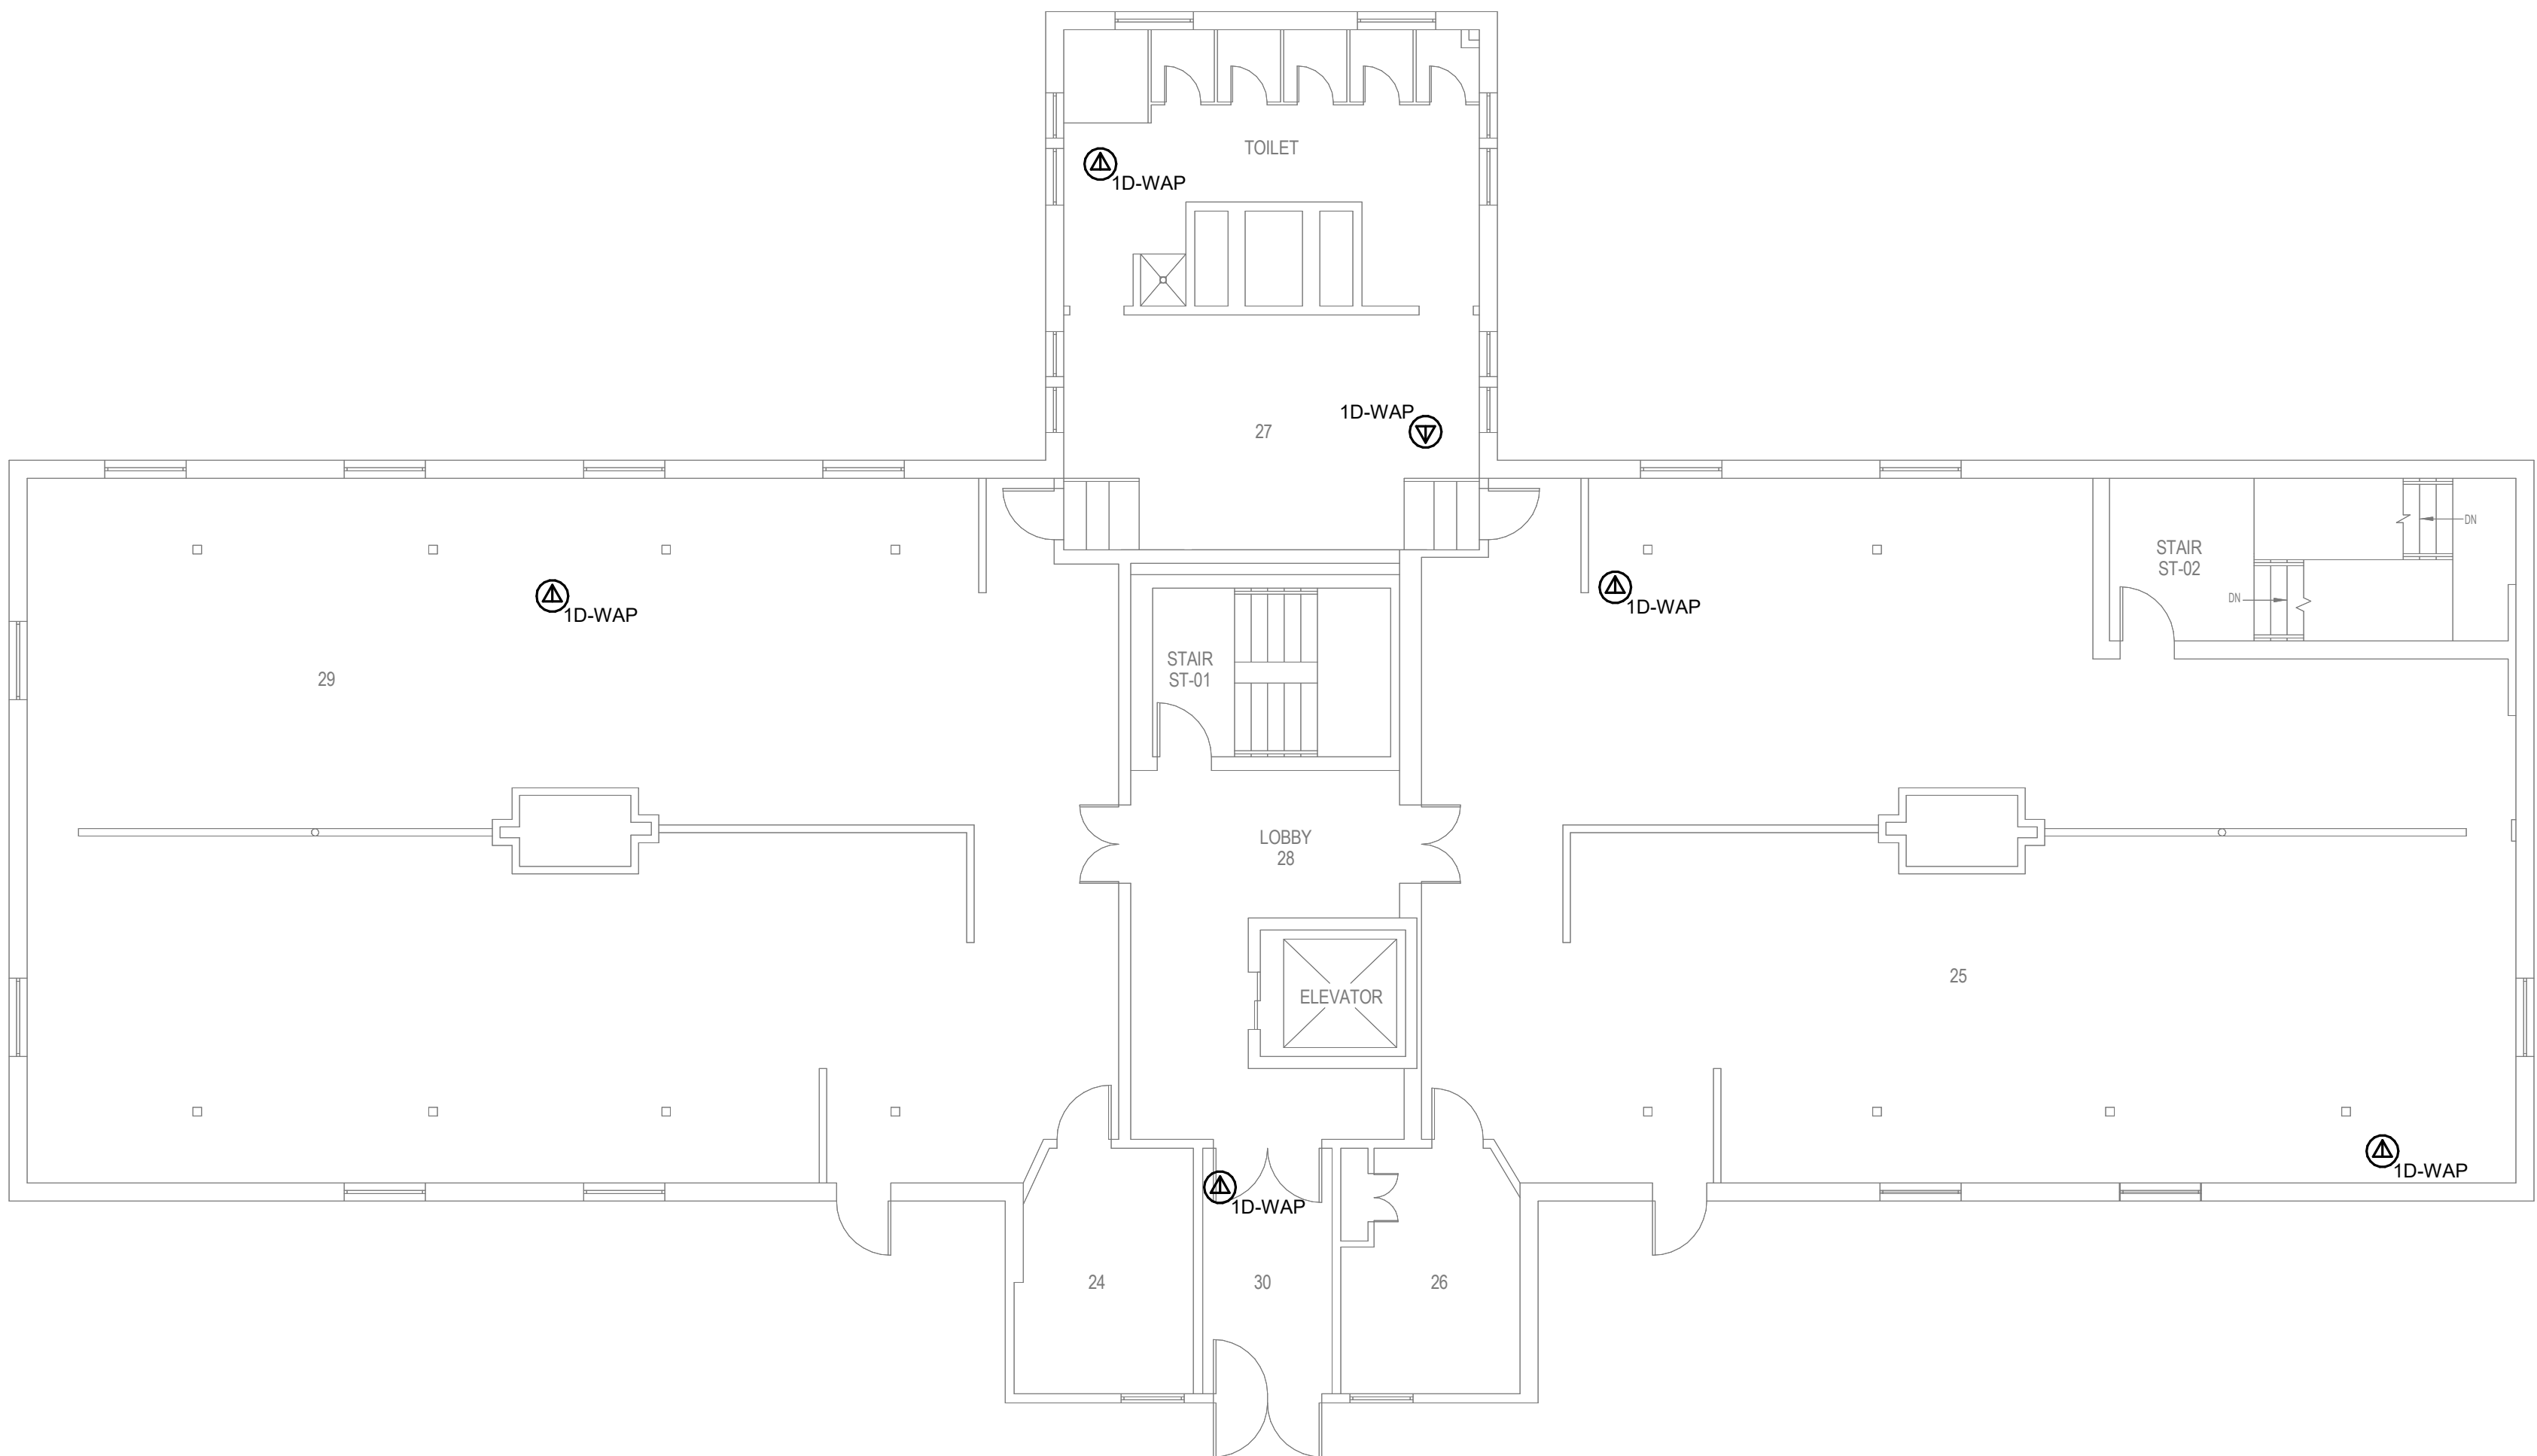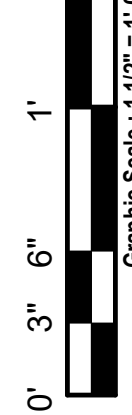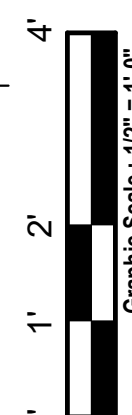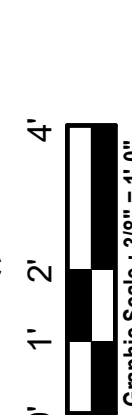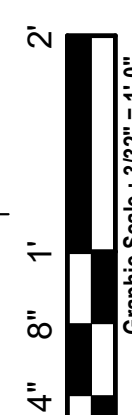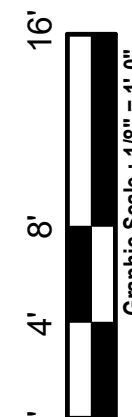

1

BUILDING 07 THIRD FLOOR PLAN - TECHNOLOGY

1/8" = 1'-0"

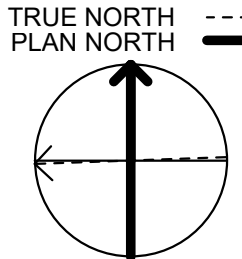

35% SCHEMATIC DESIGN SUBMISSION5.17.21 65% DESIGN DEVELOPMENT SUBMISSION6.15.21 65% DESIGN DEVELOPMENT RESUBMISSION8.25.21 Revisions: Date:	CONSULTANT IMEG The Future is Full of Possibilitieswww.imegcorp.com 15 SUNNEN DRIVE SUITE 104 ST. LOUIS, MO 63143 P: 314.645.1132 F: 314.645.1173 PROJECT #18004375.03	ARCHITECT/ENGINEER OF RECORD Romanyk Consulting Focusing on what matters Romanyk Consulting Corp. www.romanykconsulting.com 3308 Preston Road, Suite 350-164, Plano, Texas 75093	STAMP Bicsi DAVID LARSON BICS1 ID # 106098 Expires 12-31-25 RCED	Office of Construction and Facilities Management VAU.S. Department of Veterans Affairs	Drawing Title BUILDING 07 THIRD FLOOR PLAN - TECHNOLOGY Approved:	Phase FINAL BID DOCUMENTS Sprinklered FULLY SPRINKLERED	Project Title EHRM INFRASTRUCTURE UPGRADES - MILWAUKEE, WI Location 5000 W. NATIONAL AVENUE MILWAUKEE, WI Issue Date SEPTEMBER 05, 2025 Checked PHINIE Drawn MAIBEJ	Project Number 695-21-700 Building Number 07 Drawing Number 07-TN103

F

E

D

C


B

A


9/3/2025 3:55:34 PM

Autodesk Docs\DCFM East - Milwaukee EHRM (R24)T24_1804375.03_VA Milwaukee_C.dwt

- SHEET NOTES:**
1. REMOVE ALL NETWORK CABLING TO POINTS OF TERMINATION IN ASSOCIATED TELECOM ROOMS. REFER TO FLOOR PLANS AND SHEET T1001 FOR TR ROOM LOCATIONS.
 2. REFER TO ARCHITECTURAL PHASING PLANS FOR WHEN EXISTING CABLING IS ALLOWED TO BE DEMOLISHED.
 3. EXISTING BACKBONE ENTRY POINT. PROTECT IN PLACE. DEMOLISH EXISTING FIBER OPTIC CABLE TO POINTS OF TERMINATION AFTER REDUNDANT PATH IS INSTALLED AND OPERATIONAL. REFER TO PHASING PLAN FOR ADDITIONAL INFORMATION.
 4. FOR ALL EXISTING WIRELESS ACCESS POINTS AND SURVEILLANCE CAMERAS, DEVICES SHALL REMAIN. SCOPE OF WORK INCLUDES CABLE REPLACEMENT ONLY. COORDINATE WITH COR FOR ANY DOWNTIME OF DEVICES.
 5. EXISTING LOCATIONS OF WORK AREA OUTLETS SHOWN ON THIS SHEET MAY NOT NECESSARILY BE IN THE EXACT LOCATION AS IDENTIFIED.

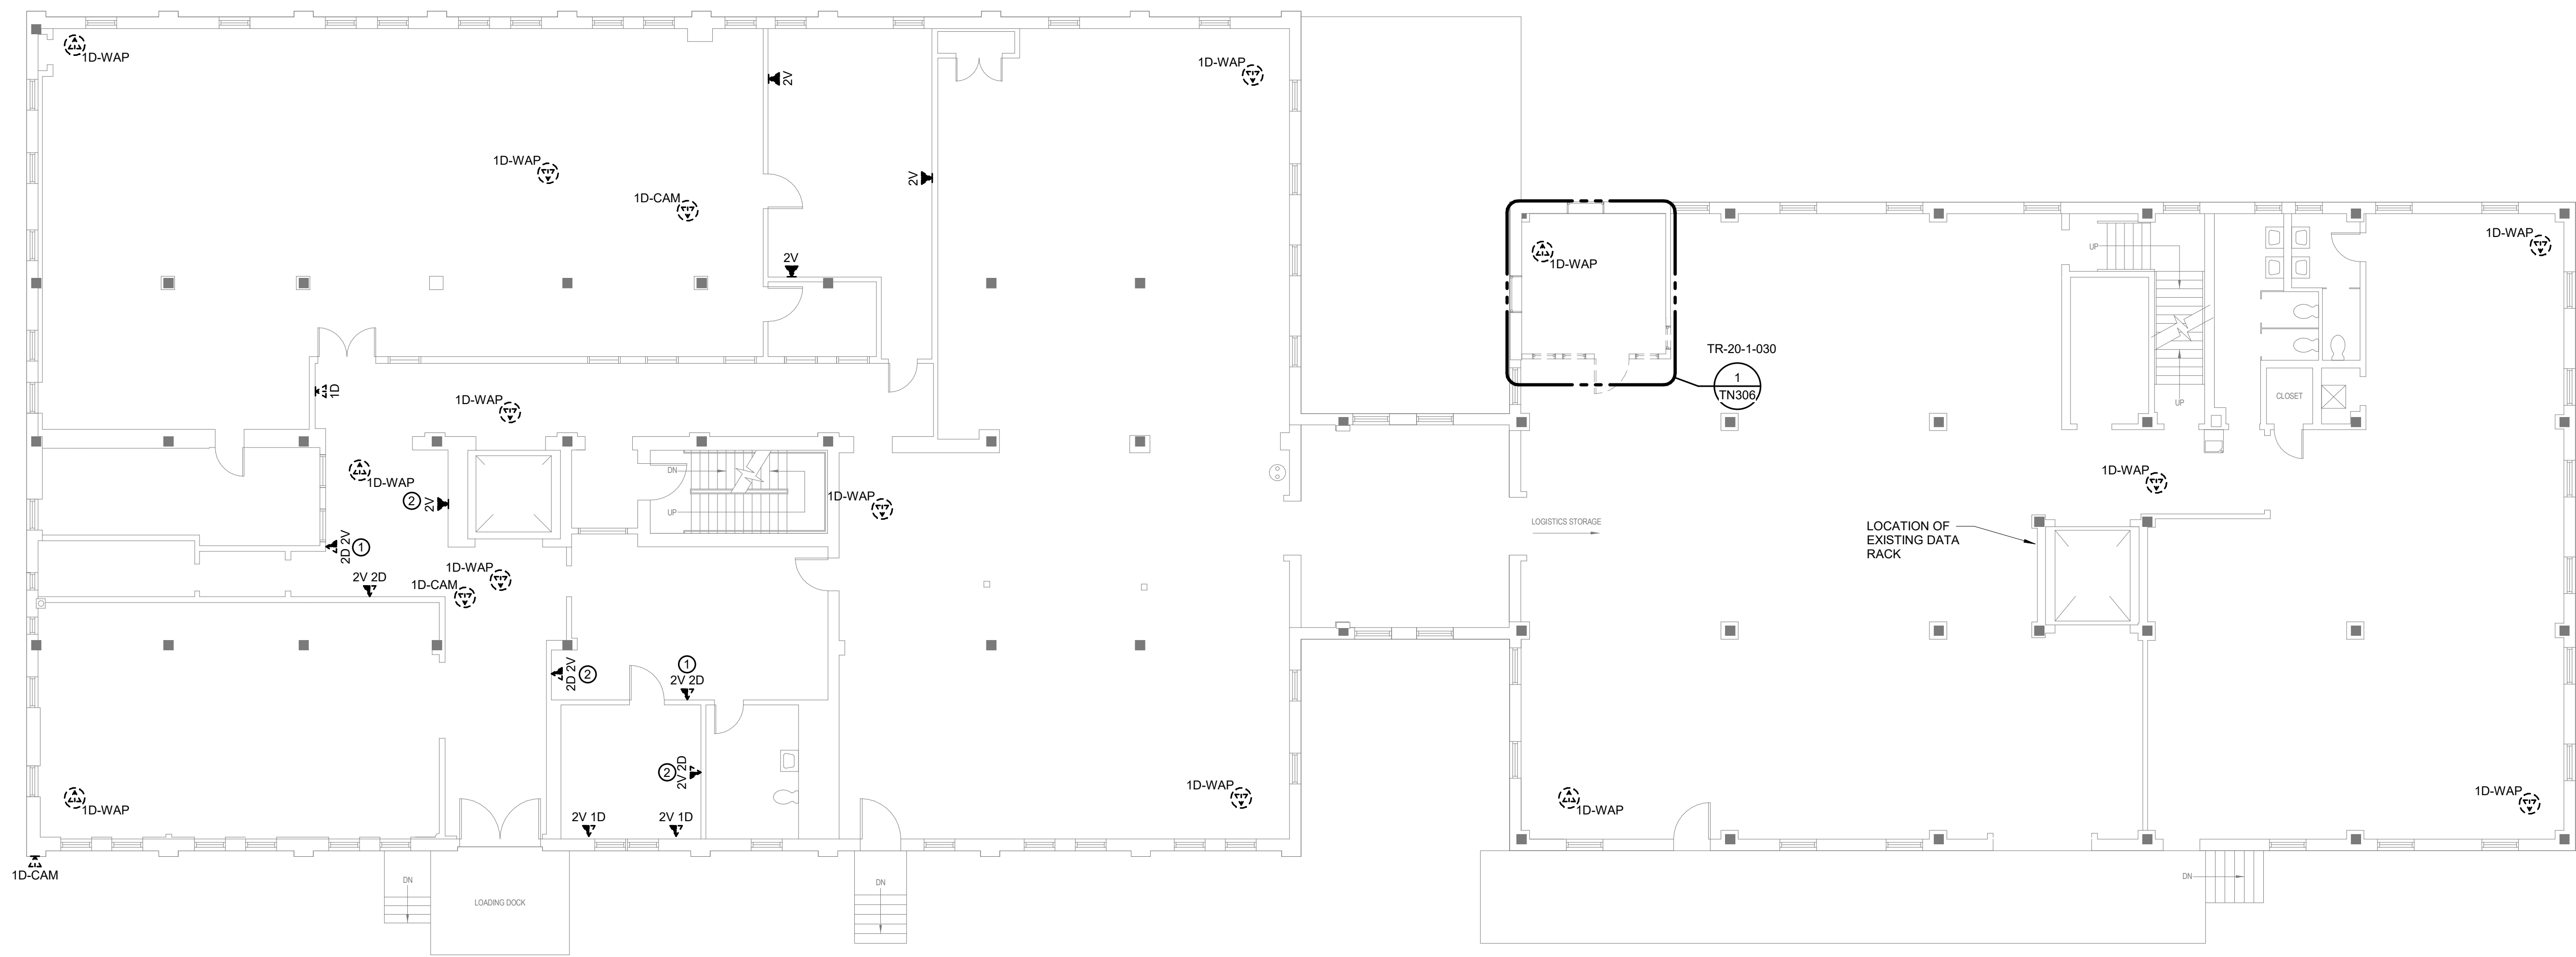

1 BUILDING 20 FIRST FLOOR DEMOLITION PLAN - TECHNOLOGY
1/8" = 1'-0"

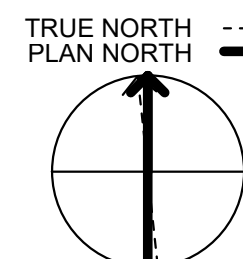

35% SCHEMATIC DESIGN SUBMISSION	5.17.21
65% DESIGN DEVELOPMENT SUBMISSION	6.15.21
65% DESIGN DEVELOPMENT RESUBMISSION	8.25.21
Revisions:	Date:

CONSULTANT

IMEG

15 SUNNEN DRIVE
SUITE 104
ST. LOUIS, MO 63143
P: 314.645.1132 F: 314.645.1173
PROJECT #18004375.03

ARCHITECT/ENGINEER OF RECORD

Romanyk Consulting
Focusing on what matters

Romanyk Consulting Corp. www.romanykconsulting.com
3308 Preston Road, Suite 350-164, Plano, Texas 75093

STAMP

Bicsi
DAVID LARSON
BICS1 ID # 106098
EXPIRES 12-31-25
REGISTERED COMMUNICATIONS DISTRIBUTION DESIGNER

Office of
Construction
and Facilities
Management

VA U.S. Department
of Veterans Affairs

Drawing Title
**BUILDING 20 FIRST FLOOR DEMO PLAN -
TECHNOLOGY**

Approved:

Phase
FINAL BID DOCUMENTS

Sprinklered

Project Title
**EHRM INFRASTRUCTURE
UPGRADES - MILWAUKEE, WI**

Location
5000 W. NATIONAL AVENUE, MILWAUKEE, WI

Issue Date
SEPTEMBER 05, 2025

Checked
PHINIE

Drawn
MAIBEJ

Project Number
695-21-700

Building Number
20

Drawing Number
20-TD101

F

E

D

C

B

A

F

E

D

C

B

A

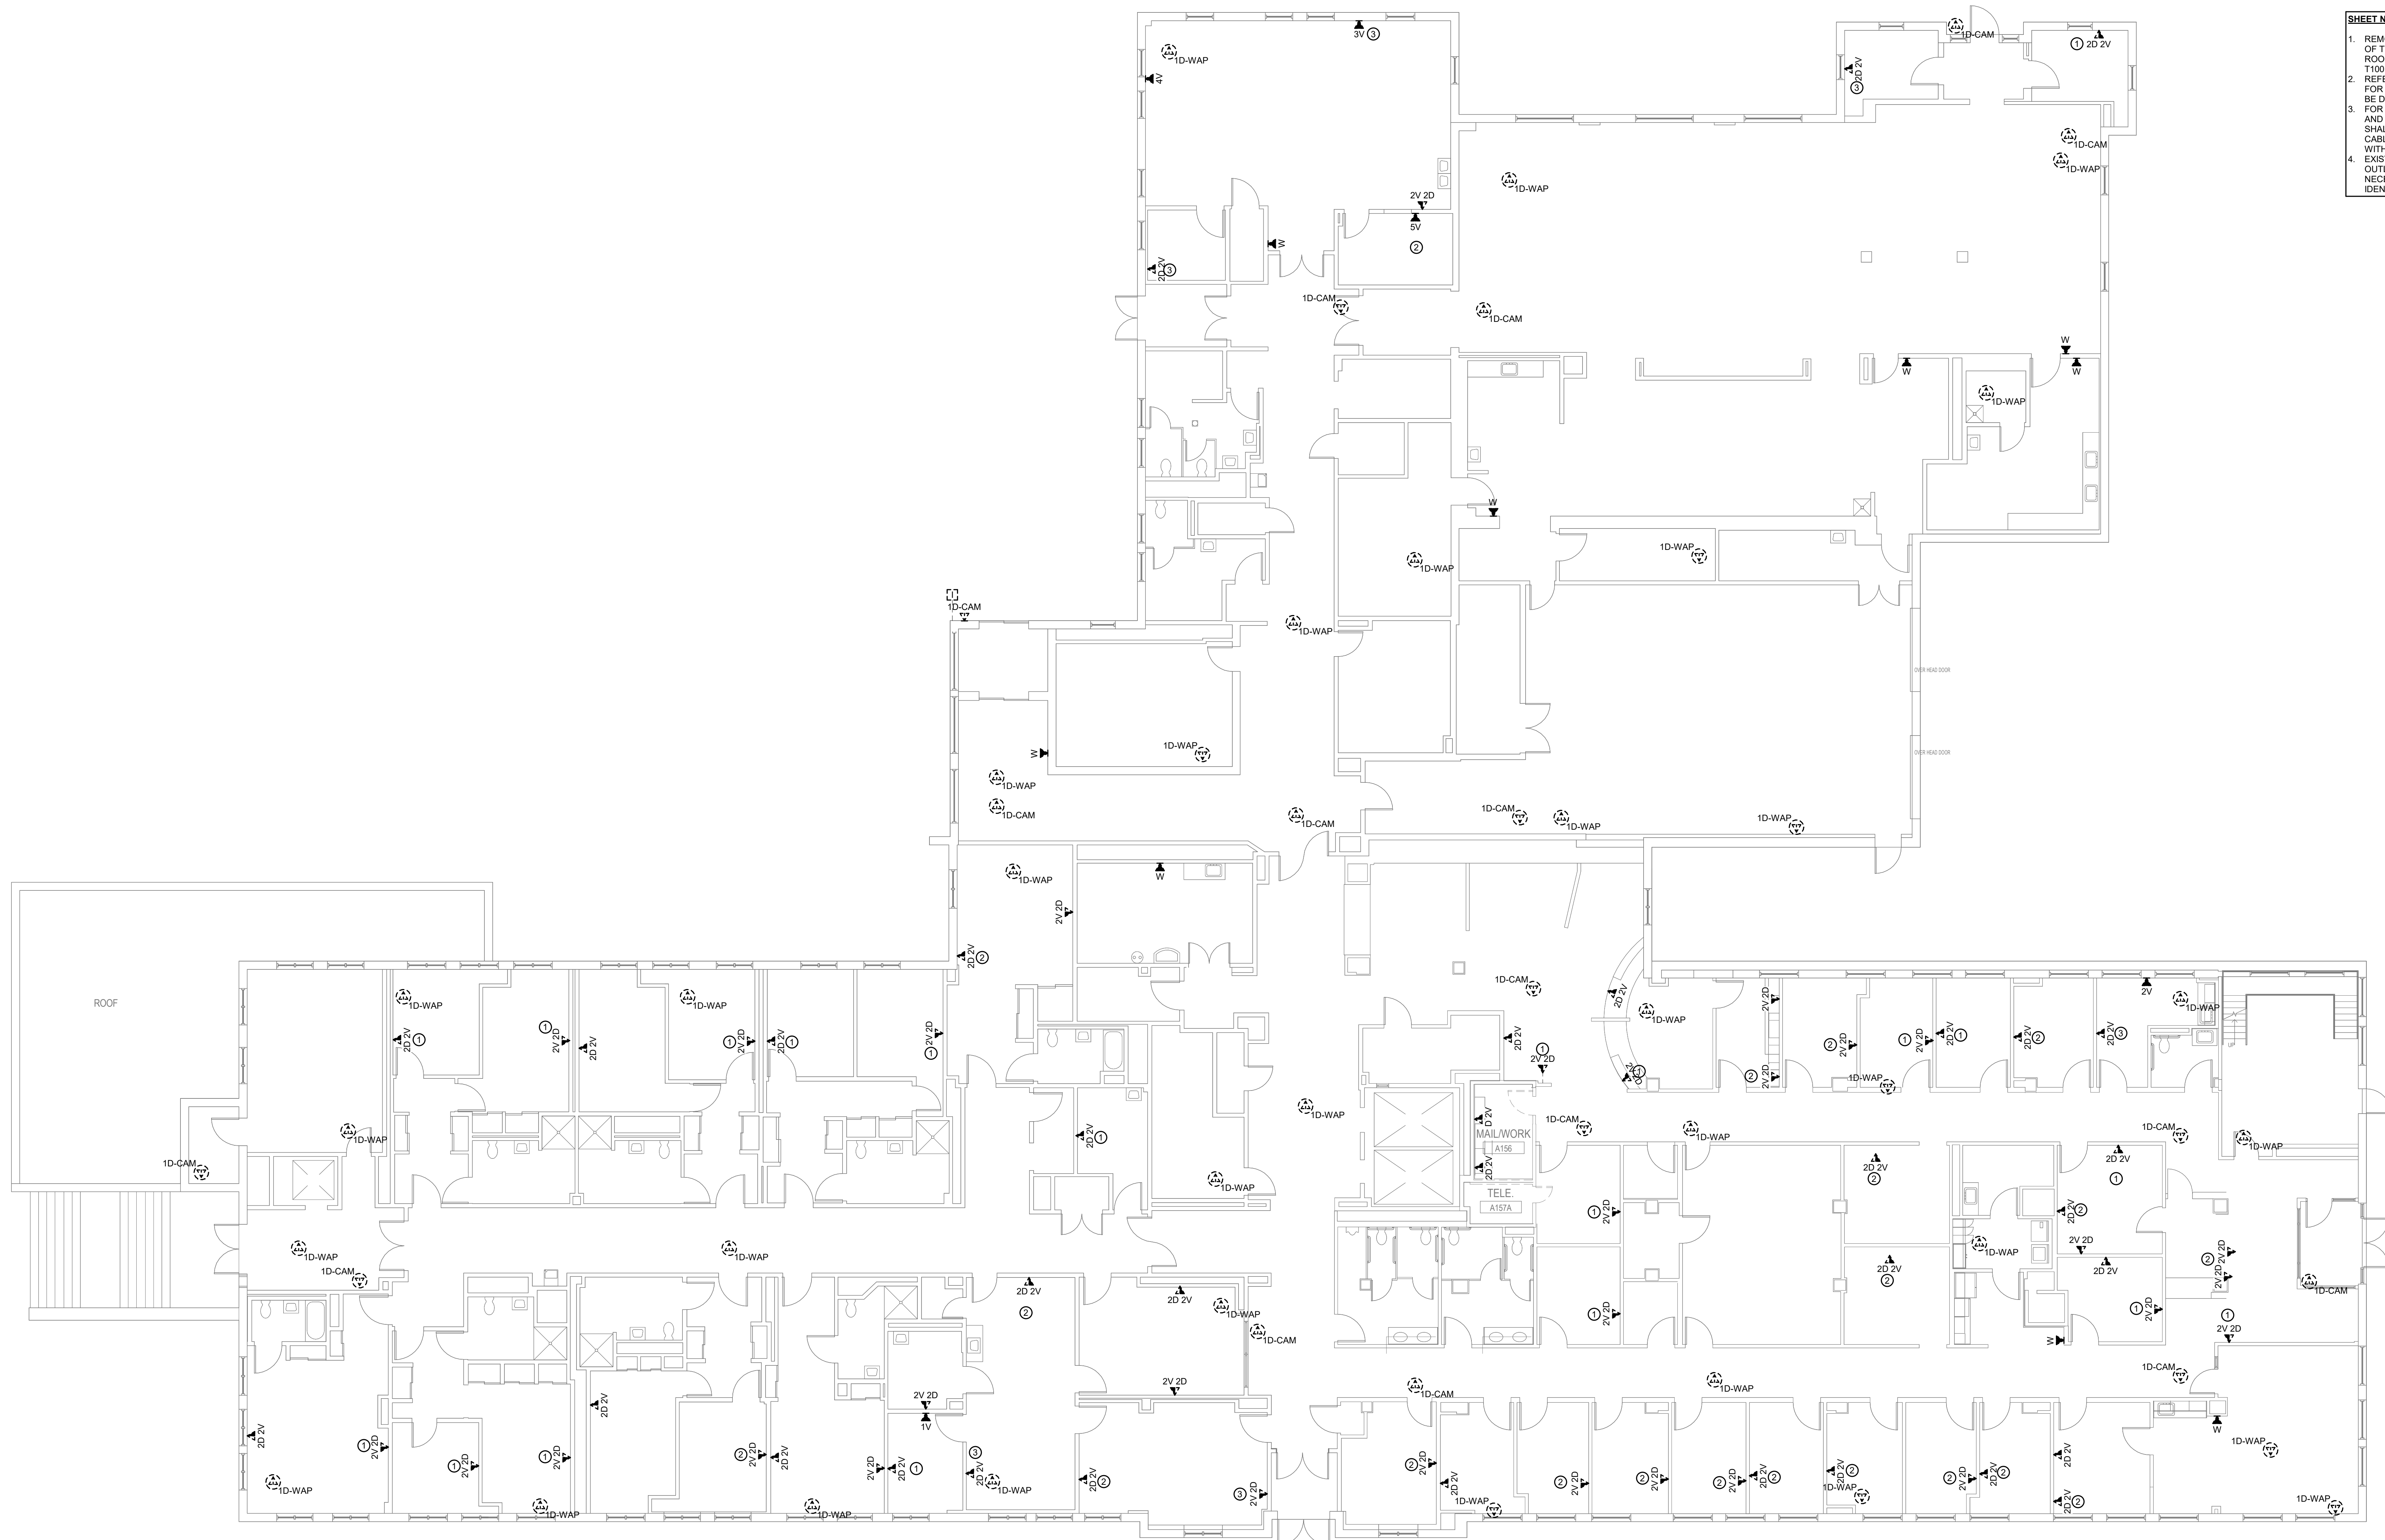

- SHEET NOTES:**
1. REMOVE ALL NETWORK CABLING TO POINTS OF TERMINATION IN ASSOCIATED TELECOM ROOMS. REFER TO FLOOR PLANS AND SHEET T1001 FOR TR ROOM LOCATIONS.
 2. REFER TO ARCHITECTURAL PHASING PLANS FOR WHEN EXISTING CABLING IS ALLOWED TO BE DEMOLISHED.
 3. FOR ALL EXISTING WIRELESS ACCESS POINTS AND SURVEILLANCE CAMERAS, DEVICES SHALL REMAIN. SCOPE OF WORK INCLUDES CABLE REPLACEMENT ONLY. COORDINATE WITH COR FOR ANY DOWNTIME OF DEVICES.
 4. EXISTING LOCATIONS OF WORK AREA, OUTLETS SHOWN ON THIS SHEET MAY NOT NECESSARILY BE IN THE EXACT LOCATION AS IDENTIFIED.

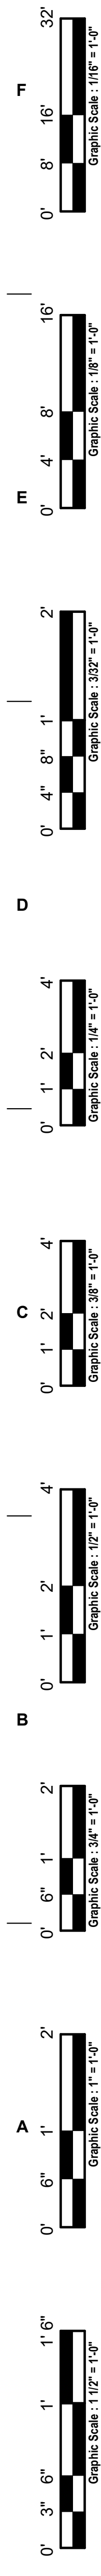

1 BUILDING 43 FIRST FLOOR DEMOLITION PLAN - TECHNOLOGY
1/8" = 1'-0"

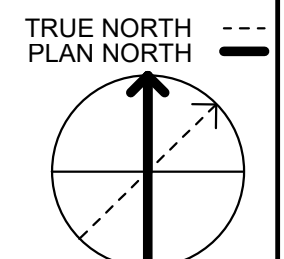

35% SCHEMATIC DESIGN SUBMISSION	5.17.21
65% DESIGN DEVELOPMENT SUBMISSION	6.15.21
65% DESIGN DEVELOPMENT RESUBMISSION	8.25.21
Revisions:	Date:

CONSULTANT

IMEG

15 SUNNEN DRIVE
SUITE 104
ST. LOUIS, MO 63143
P: 314.645.1132 F: 314.645.1173
PROJECT #1804375.03

ARCHITECT/ENGINEER OF RECORD

Romanyk Consulting
Focusing on what matters

Romanyk Consulting Corp. www.romanykconsulting.com
3308 Preston Road, Suite 350-164, Plano, Texas 75093

STAMP

Bicsi
DAVID LARSON
BICS1 ID # 106098
EXPIRES 12-31-25

Office of
Construction
and Facilities
Management

VA U.S. Department
of Veterans Affairs

Drawing Title
**BUILDING 43 FIRST FLOOR DEMO PLAN -
TECHNOLOGY**

Approved:

Phase
FINAL BID DOCUMENTS

Sprinklered
FULLY SPRINKLERED

Project Title
**EHRM INFRASTRUCTURE
UPGRADES - MILWAUKEE, WI**

Location
5000 W. NATIONAL AVENUE MILWAUKEE, WI

Issue Date
SEPTEMBER 05, 2025


Checked
PHINIE

Drawn
MAIBEJ

Project Number
695-21-700

Building Number
43

Drawing Number
43-TD101

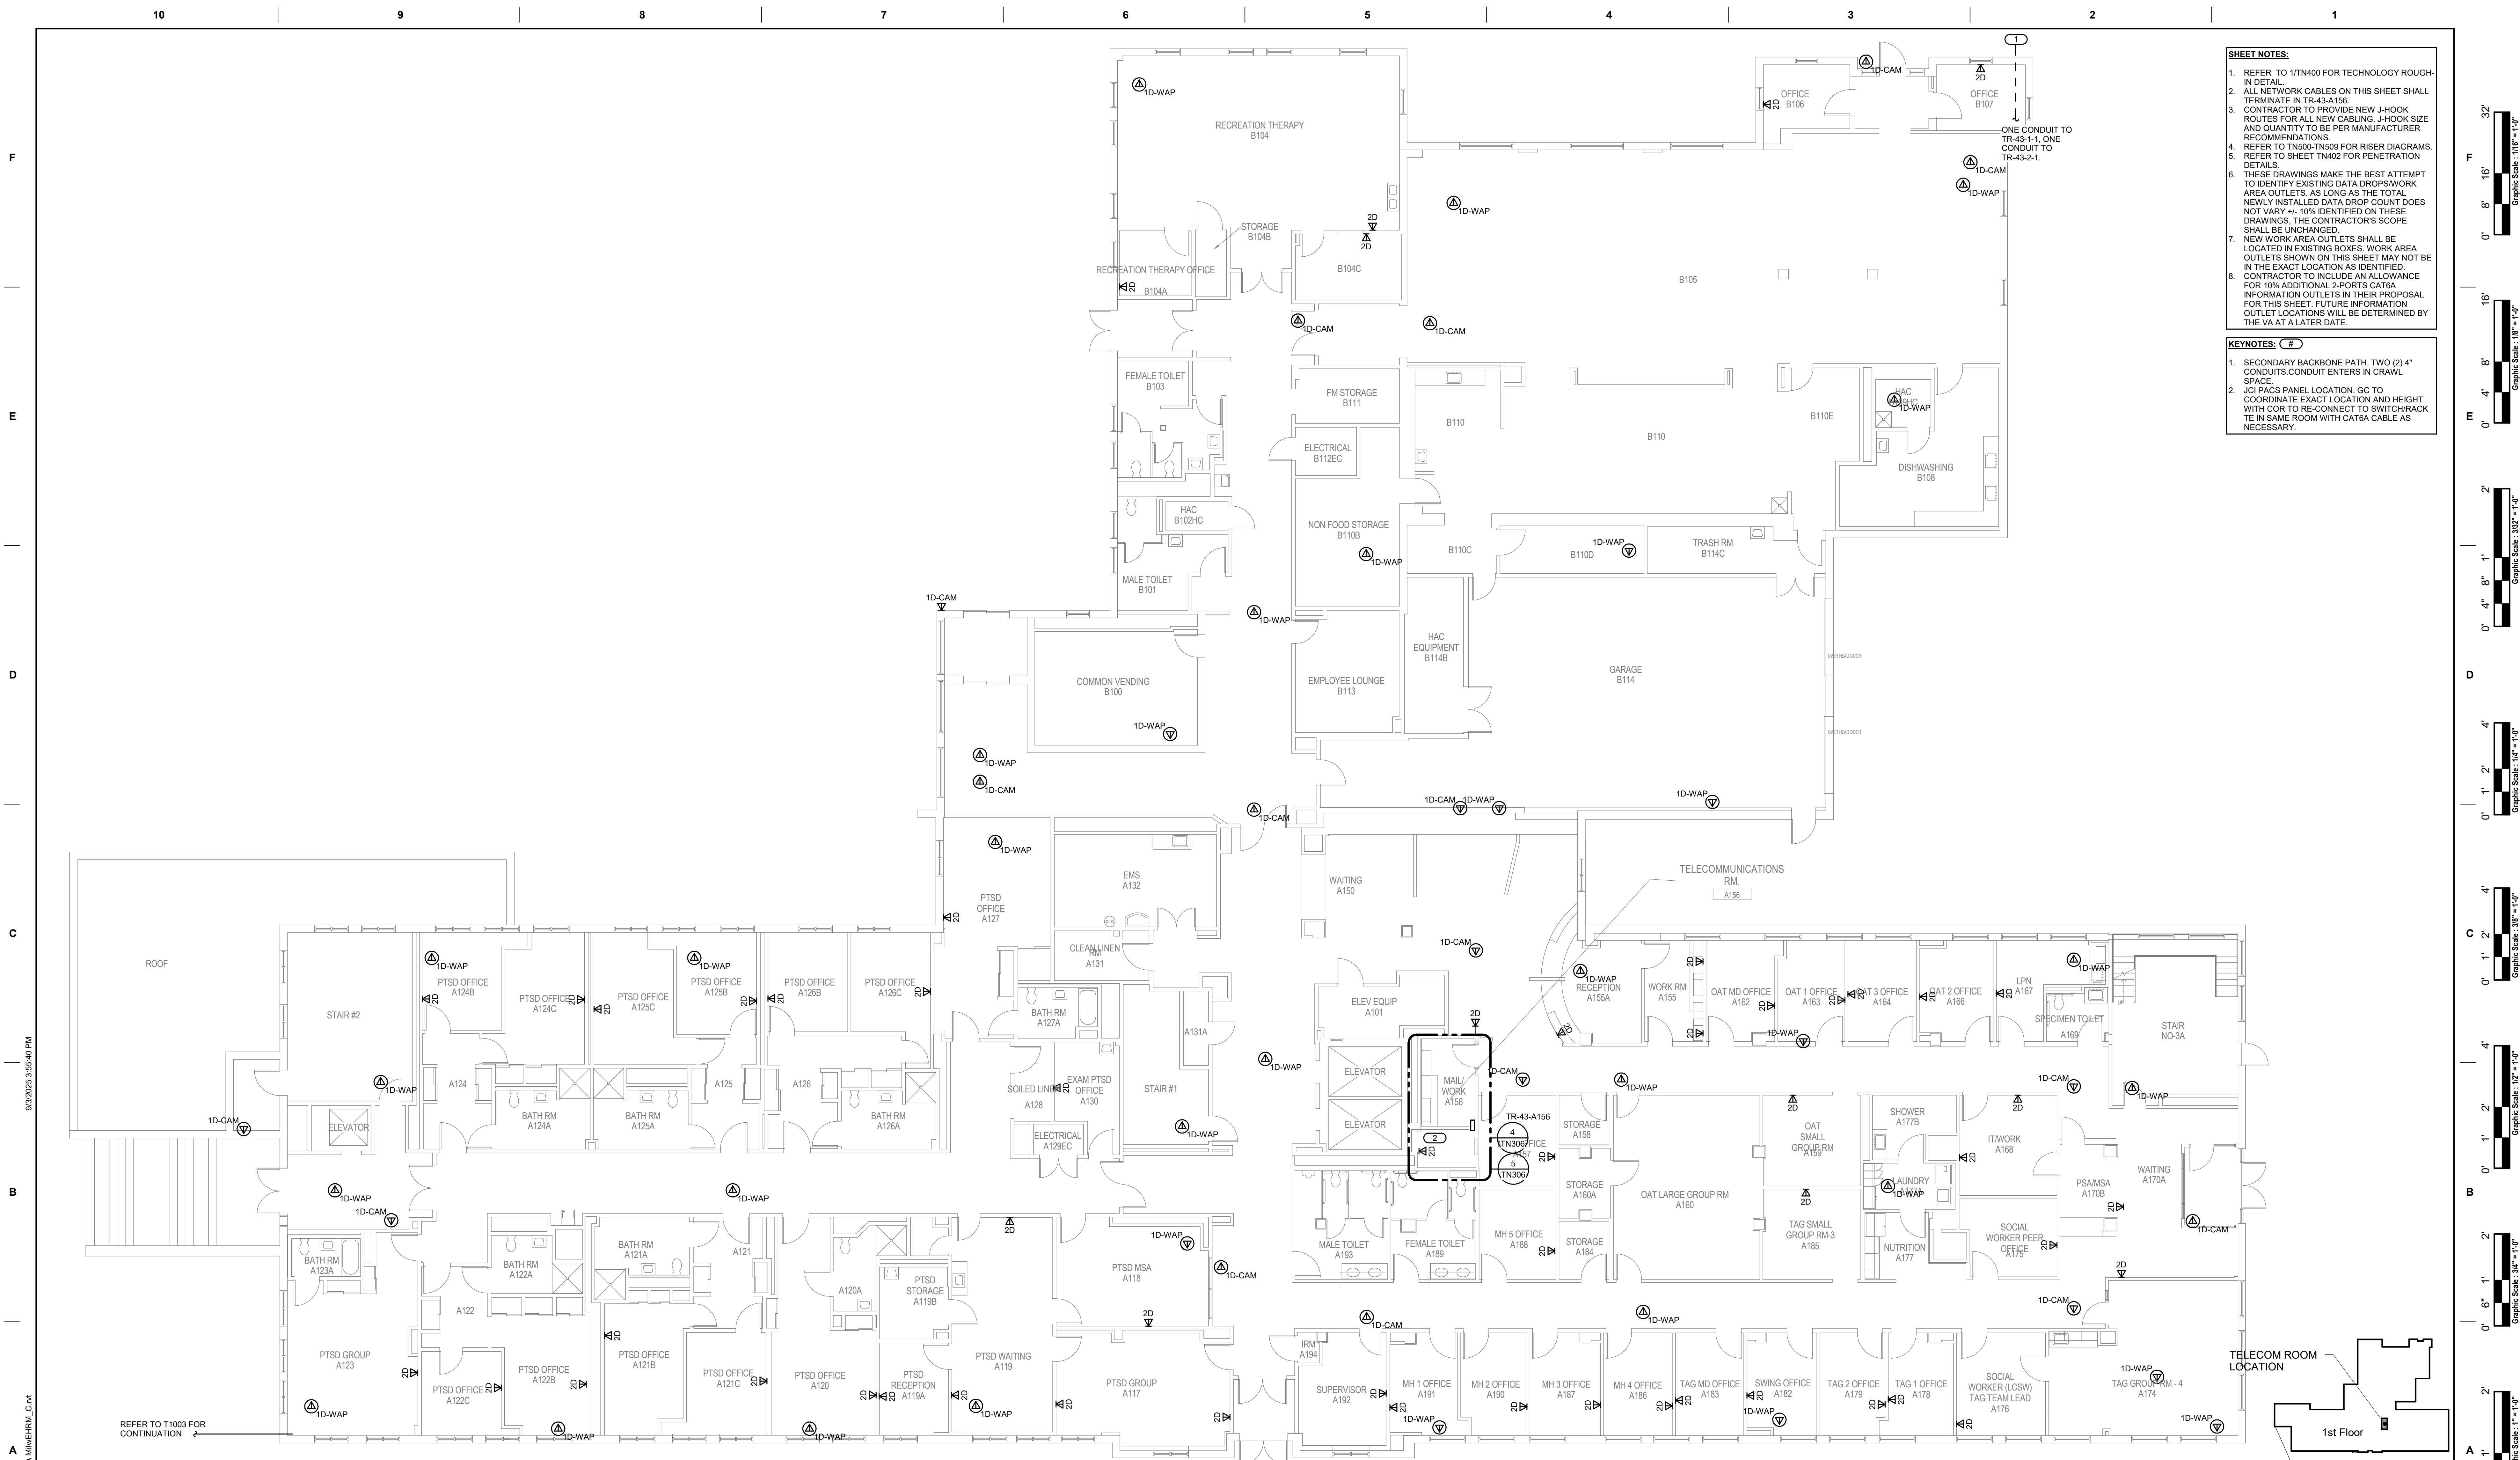

1 BUILDING 43 FIRST FLOOR PLAN - TECHNOLOGY

35% SCHEMATIC DESIGN SUBMISSION	5.17.21
65% DESIGN DEVELOPMENT SUBMISSION	6.15.21
65% DESIGN DEVELOPMENT RESUBMISSION	8.25.21
Revisions:	Date:

CONSULTANT

**IMEG**

The FUTURE. Built *Smaller*. www.imegcorp.com

15 SUNNEN DRIVE
SUITE 104
ST. LOUIS, MO 63143
P: 314.645.1132 F: 314.645.1173
PROJECT #18004375.03

ARCHITECT/ENGINEER OF RECORD	
	Romanyk Consulting Focusing on what matters Romanyk Consulting Corp. www.romanykconsulting.com 3308 Preston Road, Suite 350-164, Plano, Texas 75093

STAMP

Bicsi
 DAVID LARSON
 BICSI ID # 106098
 EXPIRES 12-31-25
 REGISTERED COMMUNICATIONS DISTRIBUTION DESIGNER
 RCDD

Office of
Construction
and Facilities
Management

VA | U.S. Department
of Veterans Affairs

Drawing Title BUILDING 43 FIRST FLOOR PLAN - TECHNOLOGY
Approved:

Phase FINAL BID DOCUMENTS
Sprinklered FULLY SPRINKLERED

Project Title EHRM INFRASTRUCTURE UPGRADES - MILWAUKEE, WI			Project Number 695-21-700	
			Building Number 43	
Location 5000 W. NATIONAL AVENUE MILWAUKEE, WI			Drawing Number 43-TN101	
Issue Date SEPTEMBER 05, 2025	Checked PHINIE	Drawn MAIBEJ		

F

E

D


C

B









A

9/2/2025 3:55:41 PM

Autodesk Docs (DCC) File - Milwaukee EHRM (R24)T24_1804375.03_VA MilWHERM_C.rvt

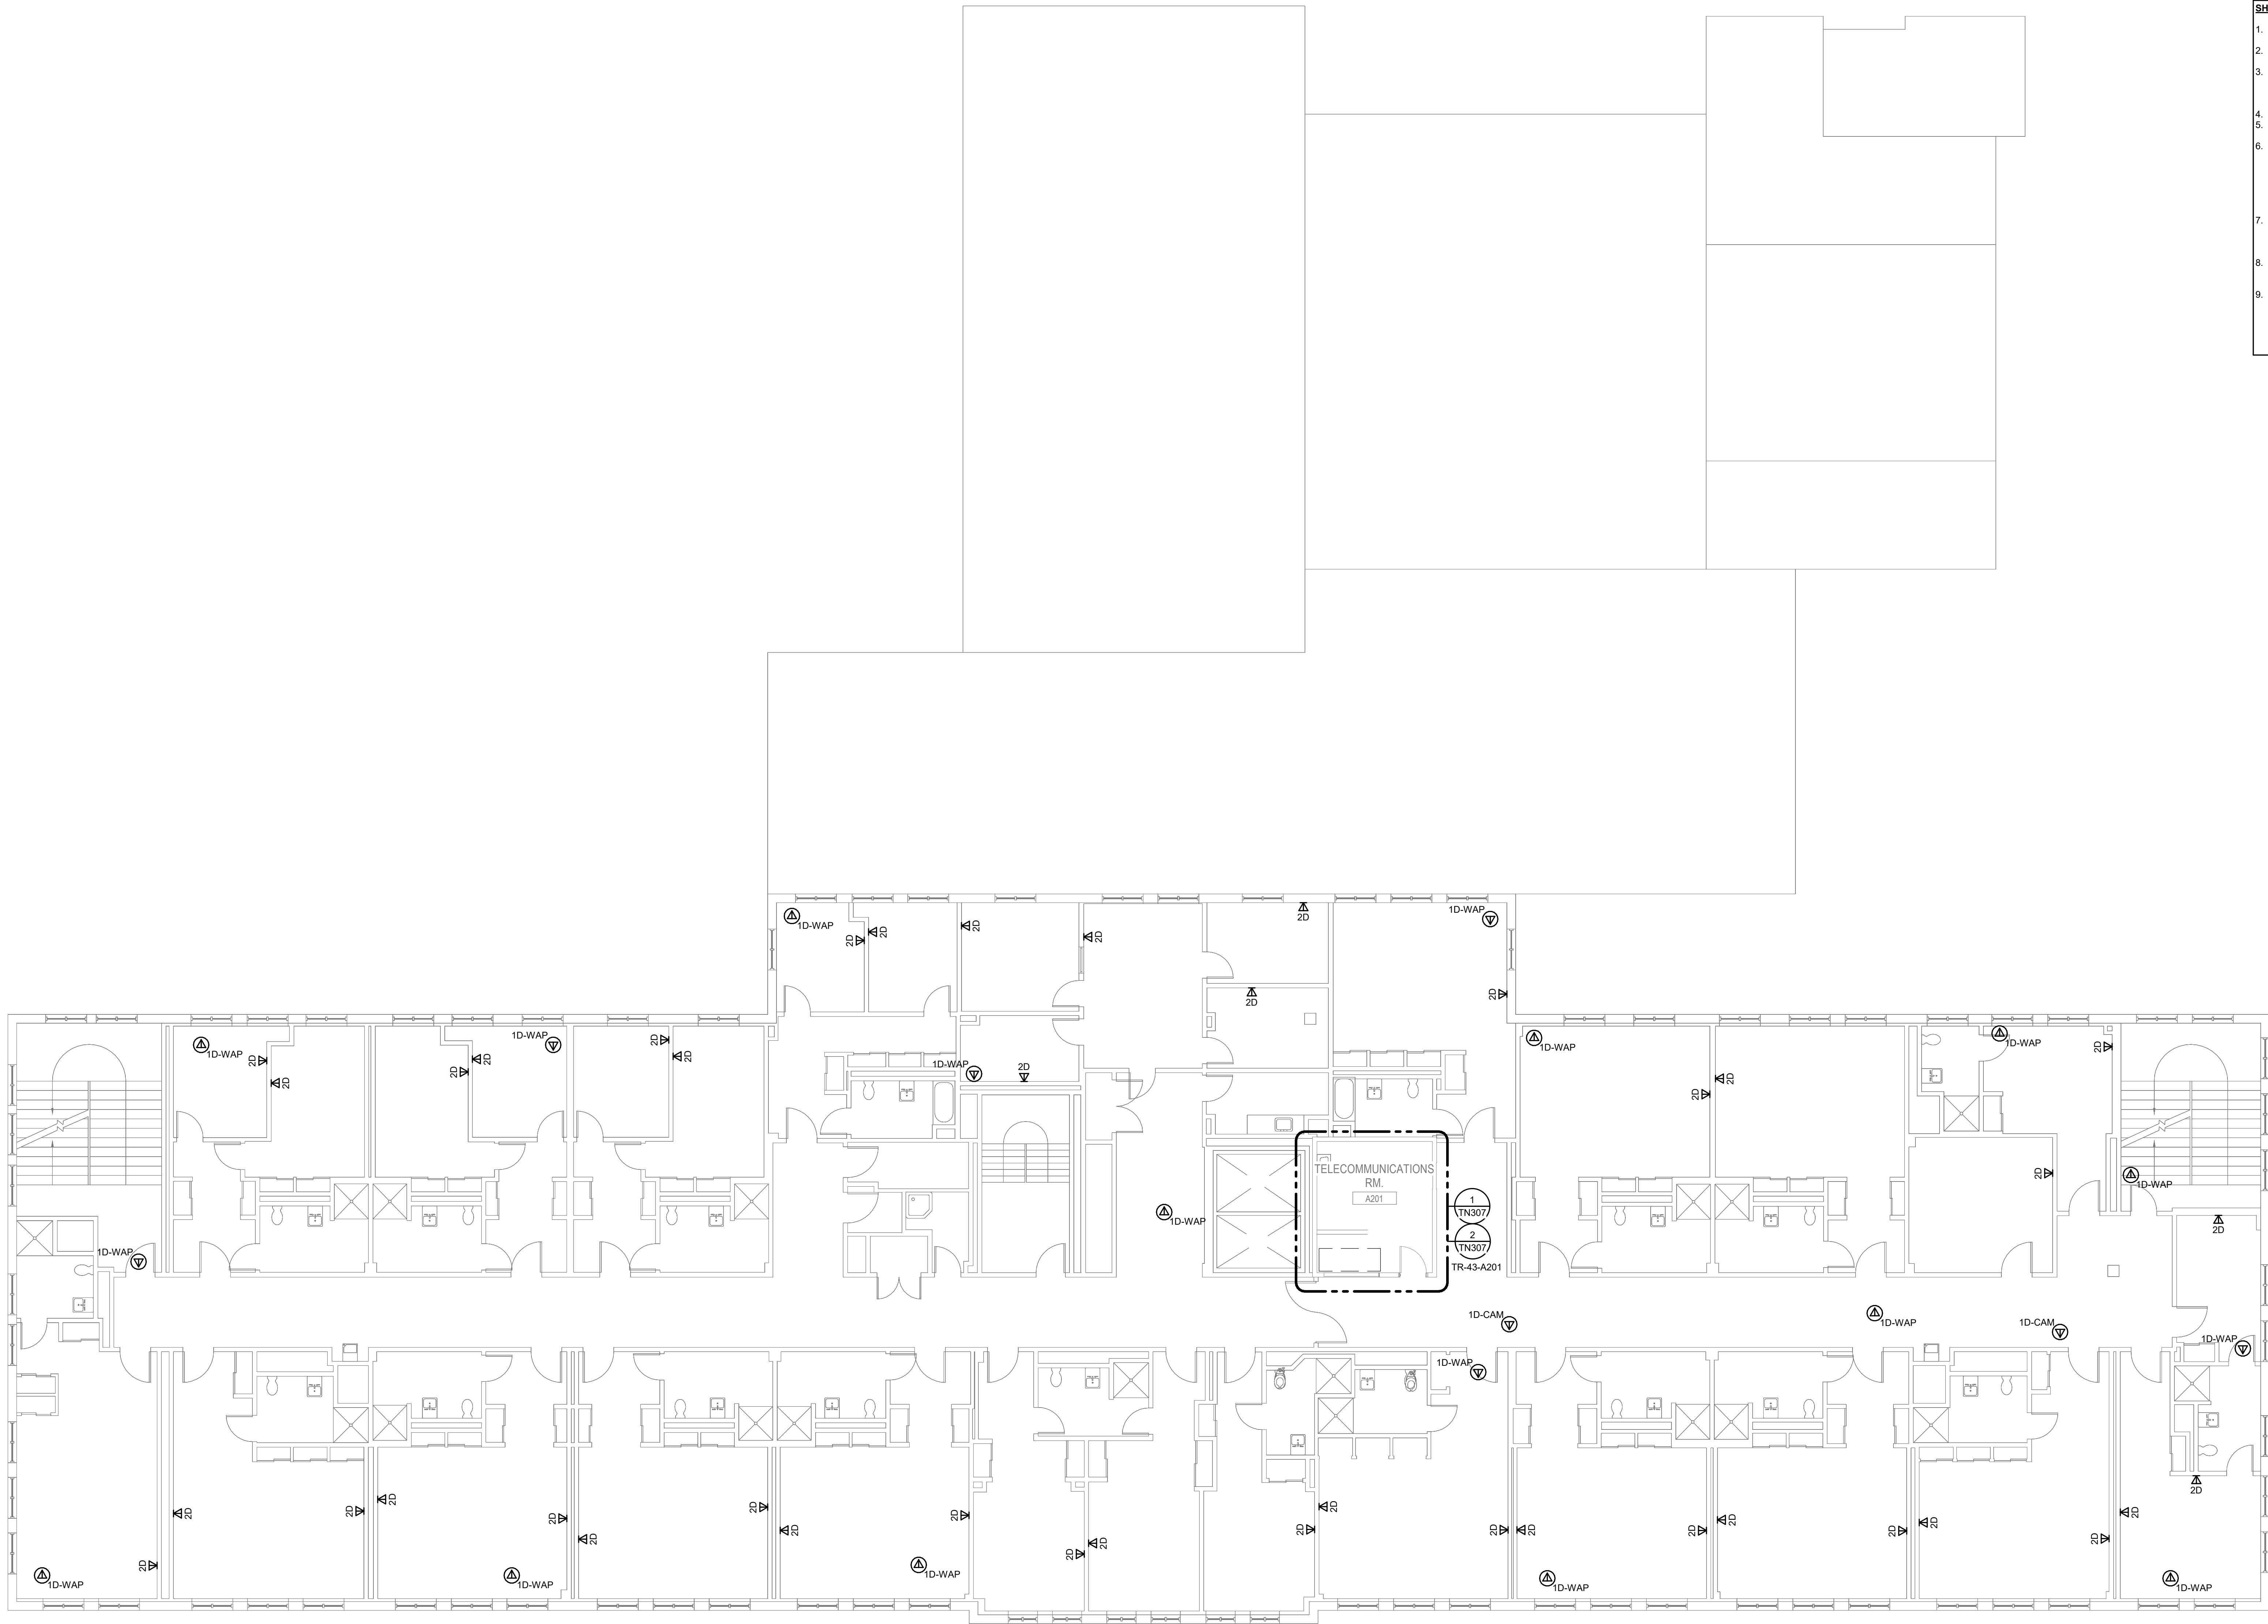

- SHEET NOTES:**
1. REFER TO 1/TN400 FOR TECHNOLOGY ROUGH-IN DETAIL.
 2. ALL NETWORK CABLES ON THIS SHEET SHALL TERMINATE IN TR-43-A201.
 3. CONTRACTOR TO PROVIDE NEW J-HOOK ROUTES FOR ALL NEW CABLING. J-HOOK SIZE AND QUANTITY TO BE PER MANUFACTURER RECOMMENDATIONS.
 4. REFER TO TN500-TN509 FOR RISER DIAGRAMS.
 5. REFER TO SHEET TN402 FOR PENETRATION DETAILS.
 6. THESE DRAWINGS MAKE THE BEST ATTEMPT TO IDENTIFY EXISTING DATA DROPS/WORK AREA OUTLETS. AS LONG AS THE TOTAL NEWLY INSTALLED DATA DROP COUNT DOES NOT VARY +/- 10% IDENTIFIED ON THESE DRAWINGS, THE CONTRACTOR'S SCOPE SHALL BE UNCHANGED.
 7. NEW WORK AREA OUTLETS SHALL BE LOCATED IN EXISTING BOXES. WORK AREA OUTLETS SHOWN ON THIS SHEET MAY NOT BE IN THE EXACT LOCATION AS IDENTIFIED.
 8. WORK AREA OUTLETS SHOWN ON THIS SHEET MAY NOT NECESSARILY BE IN THE EXACT LOCATION AS IDENTIFIED.
 9. CONTRACTOR TO INCLUDE AN ALLOWANCE FOR 10% ADDITIONAL 2-PORTS CAT6A INFORMATION OUTLETS IN THEIR PROPOSAL FOR THIS SHEET. FUTURE INFORMATION OUTLET LOCATIONS WILL BE DETERMINED BY THE VA AT A LATER DATE.

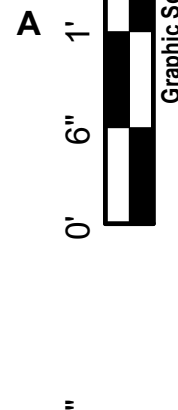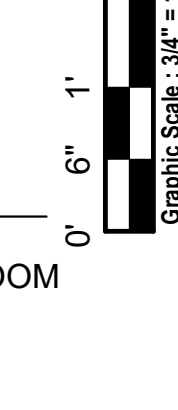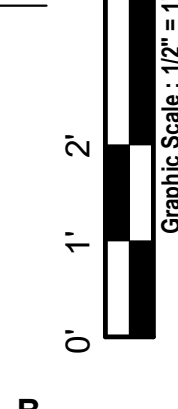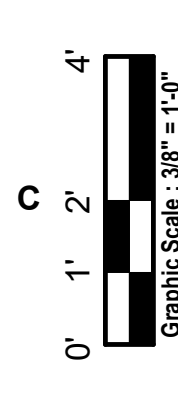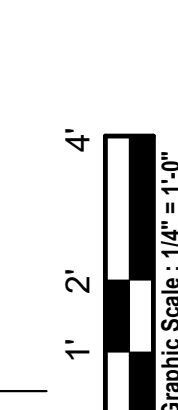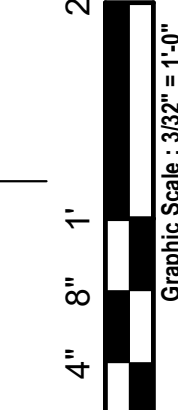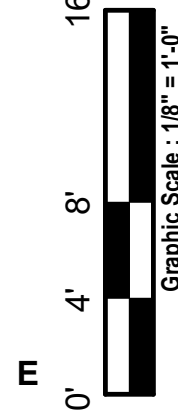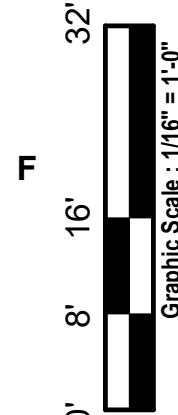

1 BUILDING 43 SECOND FLOOR PLAN - TECHNOLOGY
1/8" = 1'-0"

35% SCHEMATIC DESIGN SUBMISSION	5.17.21
65% DESIGN DEVELOPMENT SUBMISSION	6.15.21
65% DESIGN DEVELOPMENT RESUBMISSION	8.25.21
Revisions:	Date:

CONSULTANT

IMEG

15 SUNNEN DRIVE
SUITE 104
ST. LOUIS, MO 63143
P: 314.645.1132 F: 314.645.1173
PROJECT #18004375.03

ARCHITECT/ENGINEER OF RECORD

Romanyk Consulting
Focusing on what matters

Romanyk Consulting Corp. www.romanykconsulting.com
3308 Preston Road, Suite 350-164, Plano, Texas 75093

STAMP

Bicsi
DAVID LARSON
BICS1 ID # 106098
EXPIRES 12-31-25

Office of
Construction
and Facilities
Management

VA U.S. Department
of Veterans Affairs

Drawing Title
**BUILDING 43 SECOND FLOOR PLAN -
TECHNOLOGY**

Approved:

Phase
FINAL BID DOCUMENTS

Sprinklered
FULLY SPRINKLERED

Project Title
**EHRM INFRASTRUCTURE
UPGRADES - MILWAUKEE, WI**

Location
5000 W. NATIONAL AVENUE MILWAUKEE, WI

Issue Date
SEPTEMBER 05, 2025

Checked
PHINIE

Drawn
MAIBEJ

Project Number
695-21-700


Building Number
43

Drawing Number
43-TN102










TELECOM ROOM
LOCATION

LEVEL 02

KEY PLAN - BLDG 43
NTS

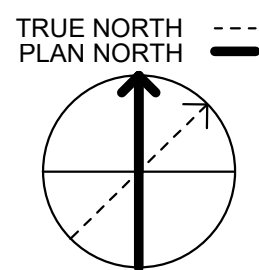

- SHEET NOTES:**
1. REFER TO 1/TN400 FOR TECHNOLOGY ROUGH-IN DETAIL.
 2. ALL NETWORK CABLES ON THIS SHEET SHALL TERMINATE IN TR-43-A201.
 3. CONTRACTOR TO PROVIDE NEW J-HOOK ROUTES FOR ALL NEW CABLING. J-HOOK SIZE AND QUANTITY TO BE PER MANUFACTURER RECOMMENDATIONS.
 4. REFER TO TN500-TN509 FOR RISER DIAGRAMS.
 5. REFER TO SHEET TN402 FOR PENETRATION DETAILS.
 6. THESE DRAWINGS MAKE THE BEST ATTEMPT TO IDENTIFY EXISTING DATA DROPS/WORK AREA OUTLETS. AS LONG AS THE TOTAL NEWLY INSTALLED DATA DROP COUNT DOES NOT VARY +/- 10% IDENTIFIED ON THESE DRAWINGS, THE CONTRACTOR'S SCOPE SHALL BE UNCHANGED.
 7. NEW WORK AREA OUTLETS SHALL BE LOCATED IN EXISTING BOXES. WORK AREA OUTLETS SHOWN ON THIS SHEET MAY NOT BE IN THE EXACT LOCATION AS IDENTIFIED.
 8. CONTRACTOR TO INCLUDE AN ALLOWANCE FOR 10% ADDITIONAL 2-PORTS CAT6A INFORMATION OUTLETS IN THEIR PROPOSAL FOR THIS SHEET. FUTURE INFORMATION OUTLET LOCATIONS WILL BE DETERMINED BY THE VA AT A LATER DATE.

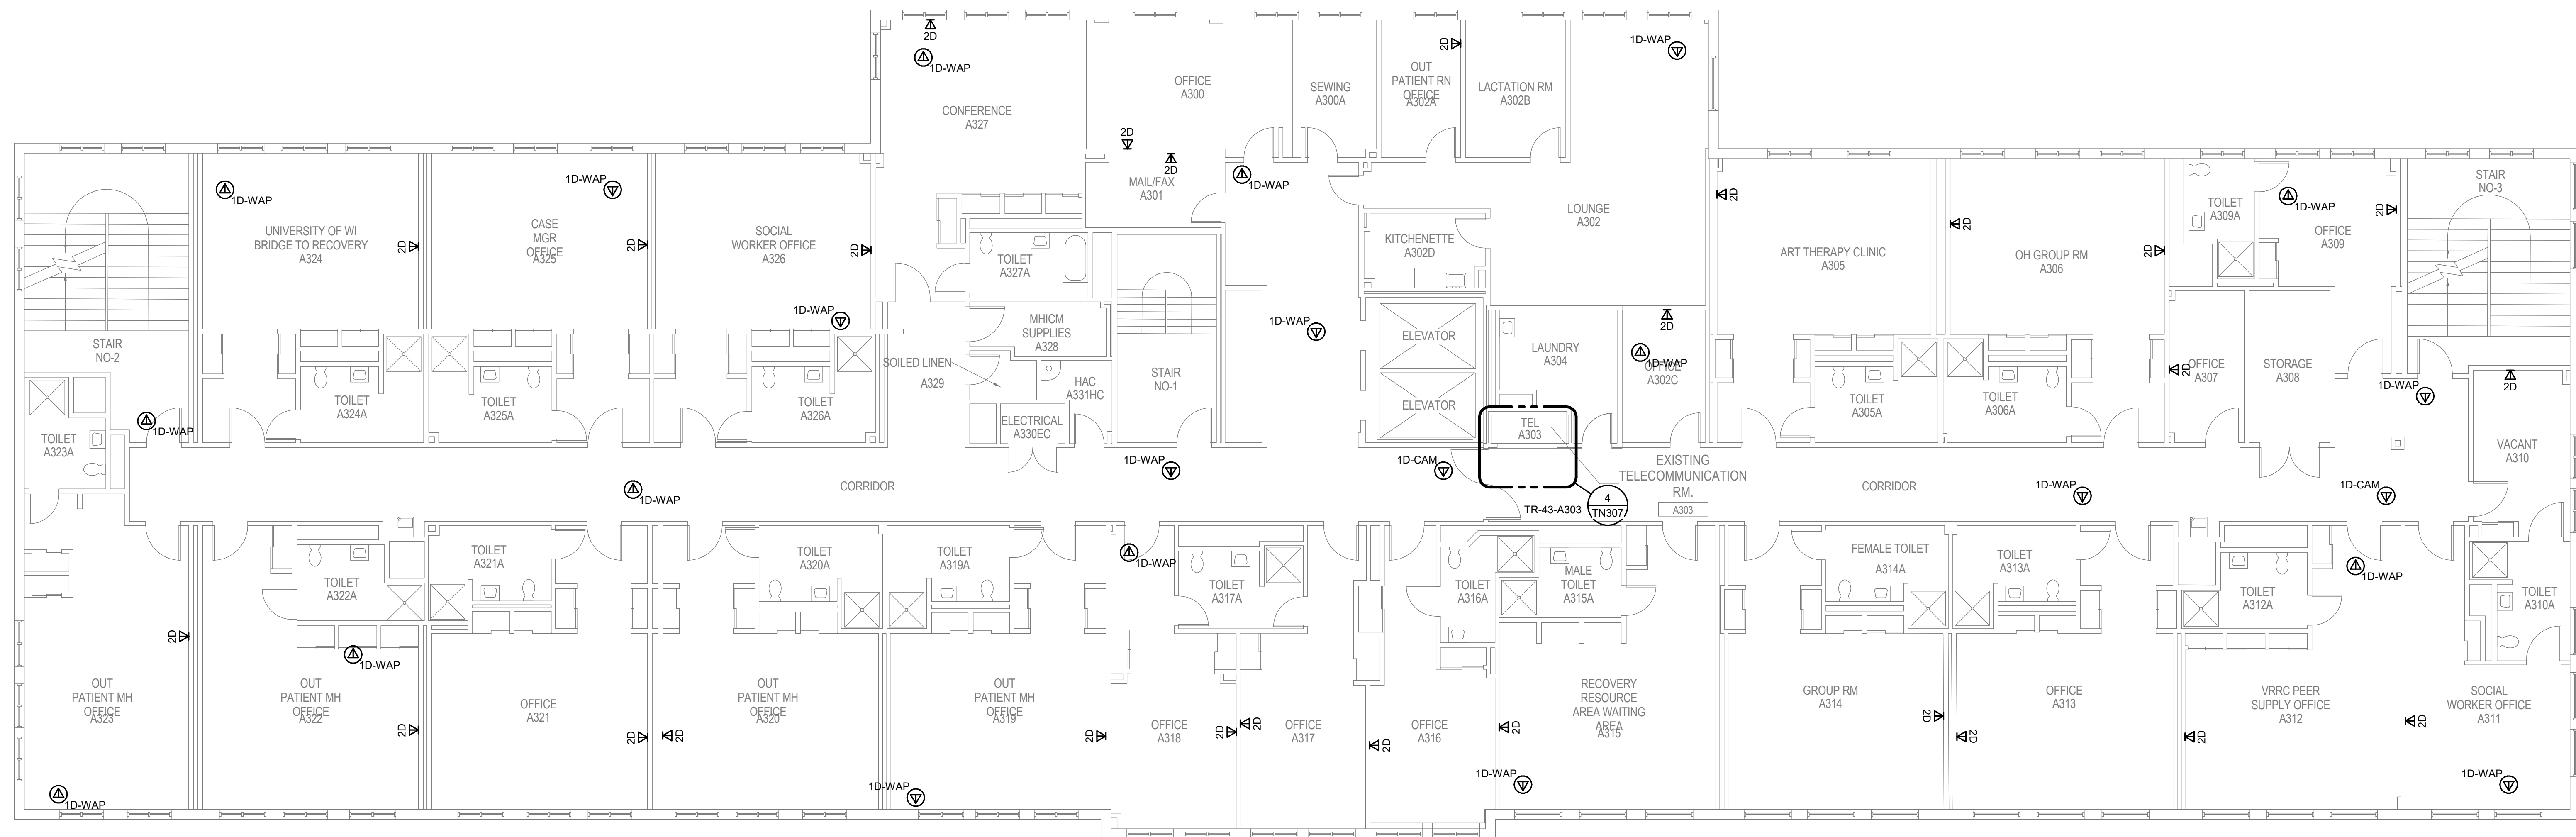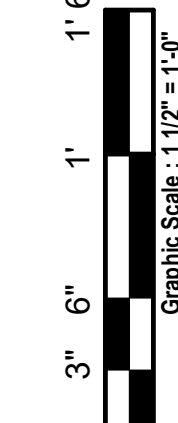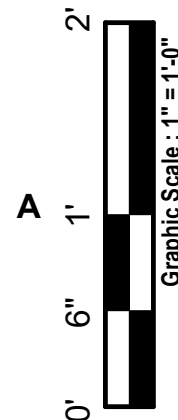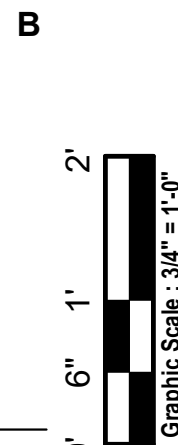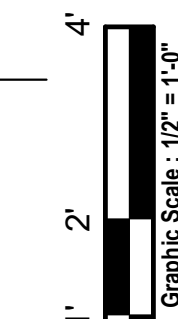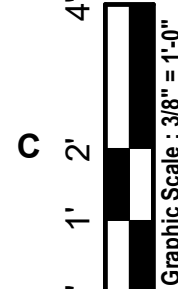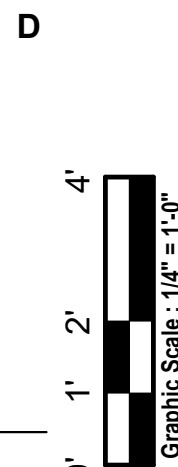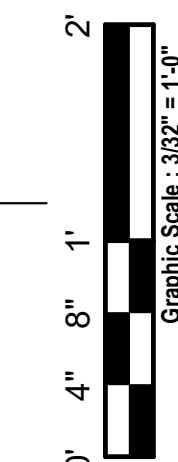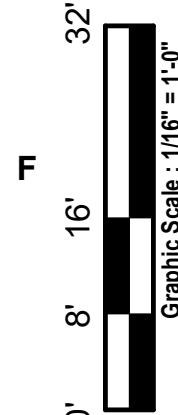


F
E
D
C
B
A

9/3/2025 3:55:44 PM
Autodesk Docs\DCFM East - Milwaukee EHRM (R24)T24_1804375\03_VA MilWEHRM_C.dwg

10 9 8 7 6 5 4 3 2 1



- SHEET NOTES:**
1. REMOVE ALL NETWORK CABLING TO POINTS OF TERMINATION IN ASSOCIATED TELECOM ROOMS. REFER TO FLOOR PLANS AND SHEET T1001 FOR TR ROOM LOCATIONS.
 2. REFER TO ARCHITECTURAL PHASING PLANS FOR WHEN EXISTING CABLING IS ALLOWED TO BE DEMOLISHED.
 3. FOR ALL EXISTING WIRELESS ACCESS POINTS AND SURVEILLANCE CAMERAS, DEVICES SHALL REMAIN. SCOPE OF WORK INCLUDES CABLE REPLACEMENT ONLY. COORDINATE WITH COR FOR ANY DOWNTIME OF DEVICES. EXISTING LOCATIONS OF WORK AREA OUTLETS SHOWN ON THIS SHEET MAY NOT NECESSARILY BE IN THE EXACT LOCATION AS IDENTIFIED.

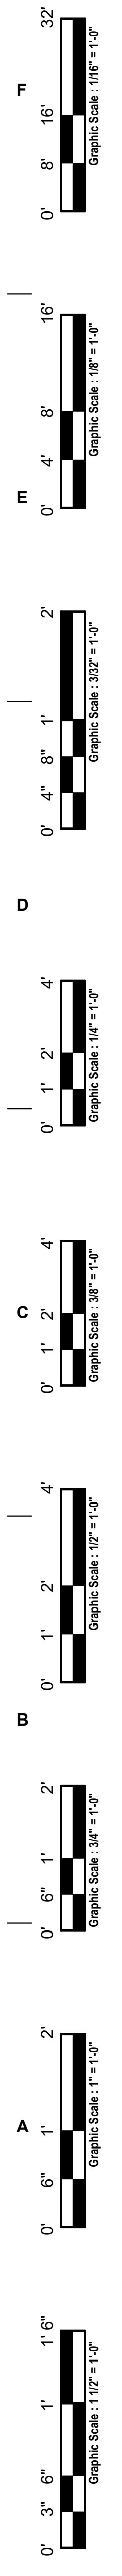

1 BUILDING 70 BASEMENT DEMOLITION PLAN - TECHNOLOGY
1" = 20'-0"

35% SCHEMATIC DESIGN SUBMISSION	5.17.21
65% DESIGN DEVELOPMENT SUBMISSION	6.15.21
65% DESIGN DEVELOPMENT RESUBMISSION	8.25.21
Revisions:	Date:

CONSULTANT

IMEG

15 SUNNEN DRIVE
SUITE 104
ST. LOUIS, MO 63143
P: 314.645.1132 F: 314.645.1173
PROJECT #18004375.03

ARCHITECT/ENGINEER OF RECORD

Romanyk Consulting
Focusing on what matters

Romanyk Consulting Corp. www.romanykconsulting.com
3308 Preston Road, Suite 350-164, Plano, Texas 75093

STAMP

Bicsi
DAVID LARSON
BICS1 ID # 106098
Expires 12-31-25

Office of
Construction
and Facilities
Management

VA U.S. Department
of Veterans Affairs

Drawing Title
BUILDING 70 BASEMENT DEMOLITION PLAN -
TECHNOLOGY

Approved:

Phase
FINAL BID DOCUMENTS

Sprinklered
FULLY SPRINKLERED

Project Title
EHRM INFRASTRUCTURE
UPGRADES - MILWAUKEE, WI

Location
5000 W. NATIONAL AVENUE MILWAUKEE, WI

Issue Date
SEPTEMBER 05, 2025


Checked
PHINIE

Drawn
MAIBEJ

Project Number
695-21-700

Building Number
70

Drawing Number
70-TD100

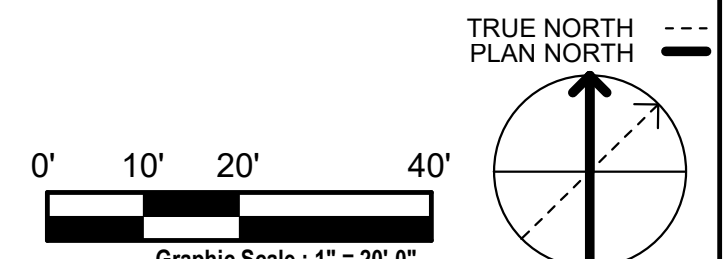

10 9 8 7 6 5 4 3 2 1

F

E

D

C

B

A


9/3/2025 3:55:46 PM

Autodesk Docs\DCFM East - Milwaukee EHRM (R24)T24_1804375.03_VA Milwaukee_C.dwg

- SHEET NOTES:**
1. REMOVE ALL NETWORK CABLING TO POINTS OF TERMINATION IN ASSOCIATED TELECOM ROOMS. REFER TO FLOOR PLANS AND SHEET T1001 FOR TR ROOM LOCATIONS.
 2. REFER TO ARCHITECTURAL PHASING PLANS FOR WHEN EXISTING CABLING IS ALLOWED TO BE DEMOLISHED.
 3. FOR ALL EXISTING WIRELESS ACCESS POINTS AND SURVEILLANCE CAMERAS, DEVICES SHALL REMAIN. SCOPE OF WORK INCLUDES CABLE REPLACEMENT ONLY. COORDINATE WITH COR FOR ANY DOWNTIME OF DEVICES. EXISTING LOCATIONS OF WORK AREA OUTLETS SHOWN ON THIS SHEET MAY NOT NECESSARILY BE IN THE EXACT LOCATION AS IDENTIFIED.



1 BUILDING 70 BASEMENT DEMOLITION PLAN - TECHNOLOGY - AREA A
1/8" = 1'-0"

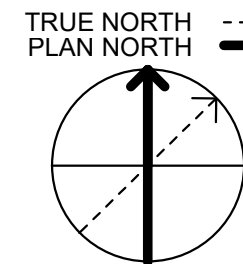

35% SCHEMATIC DESIGN SUBMISSION	5.17.21
65% DESIGN DEVELOPMENT SUBMISSION	6.15.21
65% DESIGN DEVELOPMENT RESUBMISSION	8.25.21
Revisions:	Date:

CONSULTANT

IMEG

THE FUTURE IS NOW
15 SUNNEN DRIVE
SUITE 104
ST. LOUIS, MO 63143
P: 314.645.1132 F: 314.645.1173
PROJECT #18004375.03

ARCHITECT/ENGINEER OF RECORD

Romanyk Consulting
Focusing on what matters

Romanyk Consulting Corp. www.romanykconsulting.com
3308 Preston Road, Suite 350-164, Plano, Texas 75093

STAMP

Bicsi
DAVID LARSON
BICS1 ID # 106098
EXPIRES 12-31-25
REGISTERED COMMUNICATIONS DISTRIBUTION DESIGNER

Office of
Construction
and Facilities
Management

VA U.S. Department
of Veterans Affairs

Drawing Title
BUILDING 70 BASEMENT DEMO PLAN -
TECHNOLOGY - AREA A

Approved:

Phase
FINAL BID DOCUMENTS

Sprinklered
FULLY SPRINKLERED

Project Title
EHRM INFRASTRUCTURE
UPGRADES - MILWAUKEE, WI

Location
5000 W. NATIONAL AVENUE, MILWAUKEE, WI

Issue Date
SEPTEMBER 05, 2025


Checked
PHINIE

Drawn
MAIBEJ


Project Number
695-21-700

Building Number
70

Drawing Number
70-TD100A

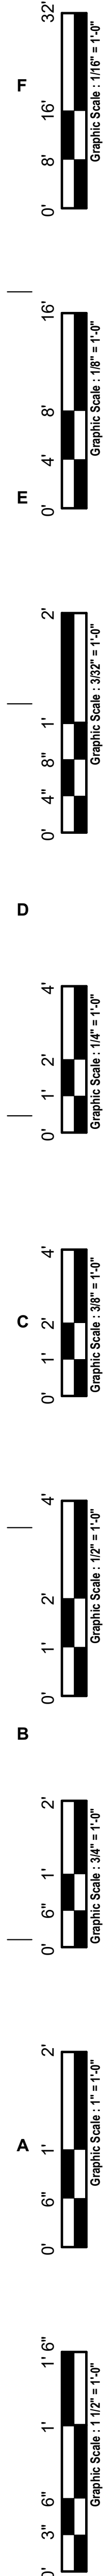

1. REMOVE ALL NETWORK CABLING TO POINTS OF TERMINATION IN ASSOCIATED TELECOM ROOMS. REFER TO FLOOR PLANS AND SHEET T1001 FOR TR ROOM LOCATIONS.
2. REFER TO ARCHITECTURAL PHASING PLANS FOR WHEN EXISTING CABLING IS ALLOWED TO BE DEMOLISHED.
3. FOR ALL EXISTING WIRELESS ACCESS POINTS AND SURVEILLANCE CAMERAS, DEVICES SHALL REMAIN. SCOPE OF WORK INCLUDES CABLE REPLACEMENT ONLY. COORDINATE WITH COR FOR ANY DOWNTIME OF DEVICES.
4. EXISTING LOCATIONS OF WORK AREA OUTLETS SHOWN ON THIS SHEET MAY NOT NECESSARILY BE IN THE EXACT LOCATION AS IDENTIFIED.

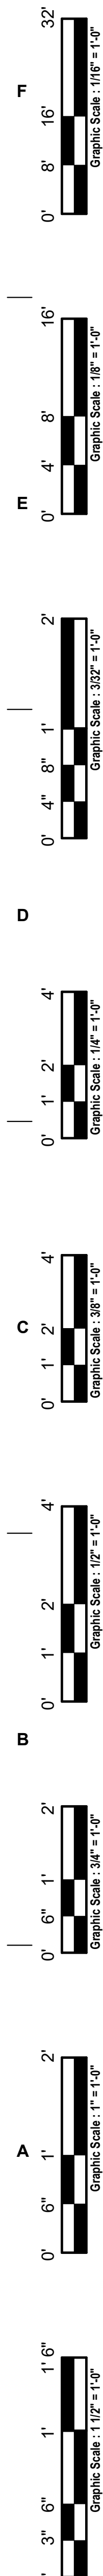

35% SCHEMATIC DESIGN SUBMISSION	5.17.21
65% DESIGN DEVELOPMENT SUBMISSION	6.15.21
65% DESIGN DEVELOPMENT RESUBMISSION	8.25.21
Revisions:	Date:



IMEG
The FUTURE. Built Smarter www.imegcorp.com
15 SUNNEN DRIVE
SUITE 104
ST. LOUIS, MO 63143
P: 314.645.1132 F: 314.645.1173
PROJECT #18004375.03

 **Romanyk Consulting**
Focusing on what matters

Romanyk Consulting Corp. www.romanykconsulting.com
3308 Preston Road, Suite 350-164, Plano, Texas 75093

REGISTERED COMMUNICATIONS DISTRIBUTION DESIGNER

Bicsi

DAVID LARSON

BICSI ID # 106098

EXPIRES 12-31-25

RCDD

VA | U.S. Department
of Veterans Affairs

Approved:

Sprinklered
FULLY SPRINKLERED

Location	5000 W. NATIONAL AVENUE MILWAUKEE, WI
-----------------	---------------------------------------

Drawing Number
70-TD100C-N

F

E

D


C

B









A

9/3/2025 3:55:48 PM


Autodesk Docs\DOCFM East - Milwaukee EHRM (R24)T24_1804375\03_VA Milwaukee C.d

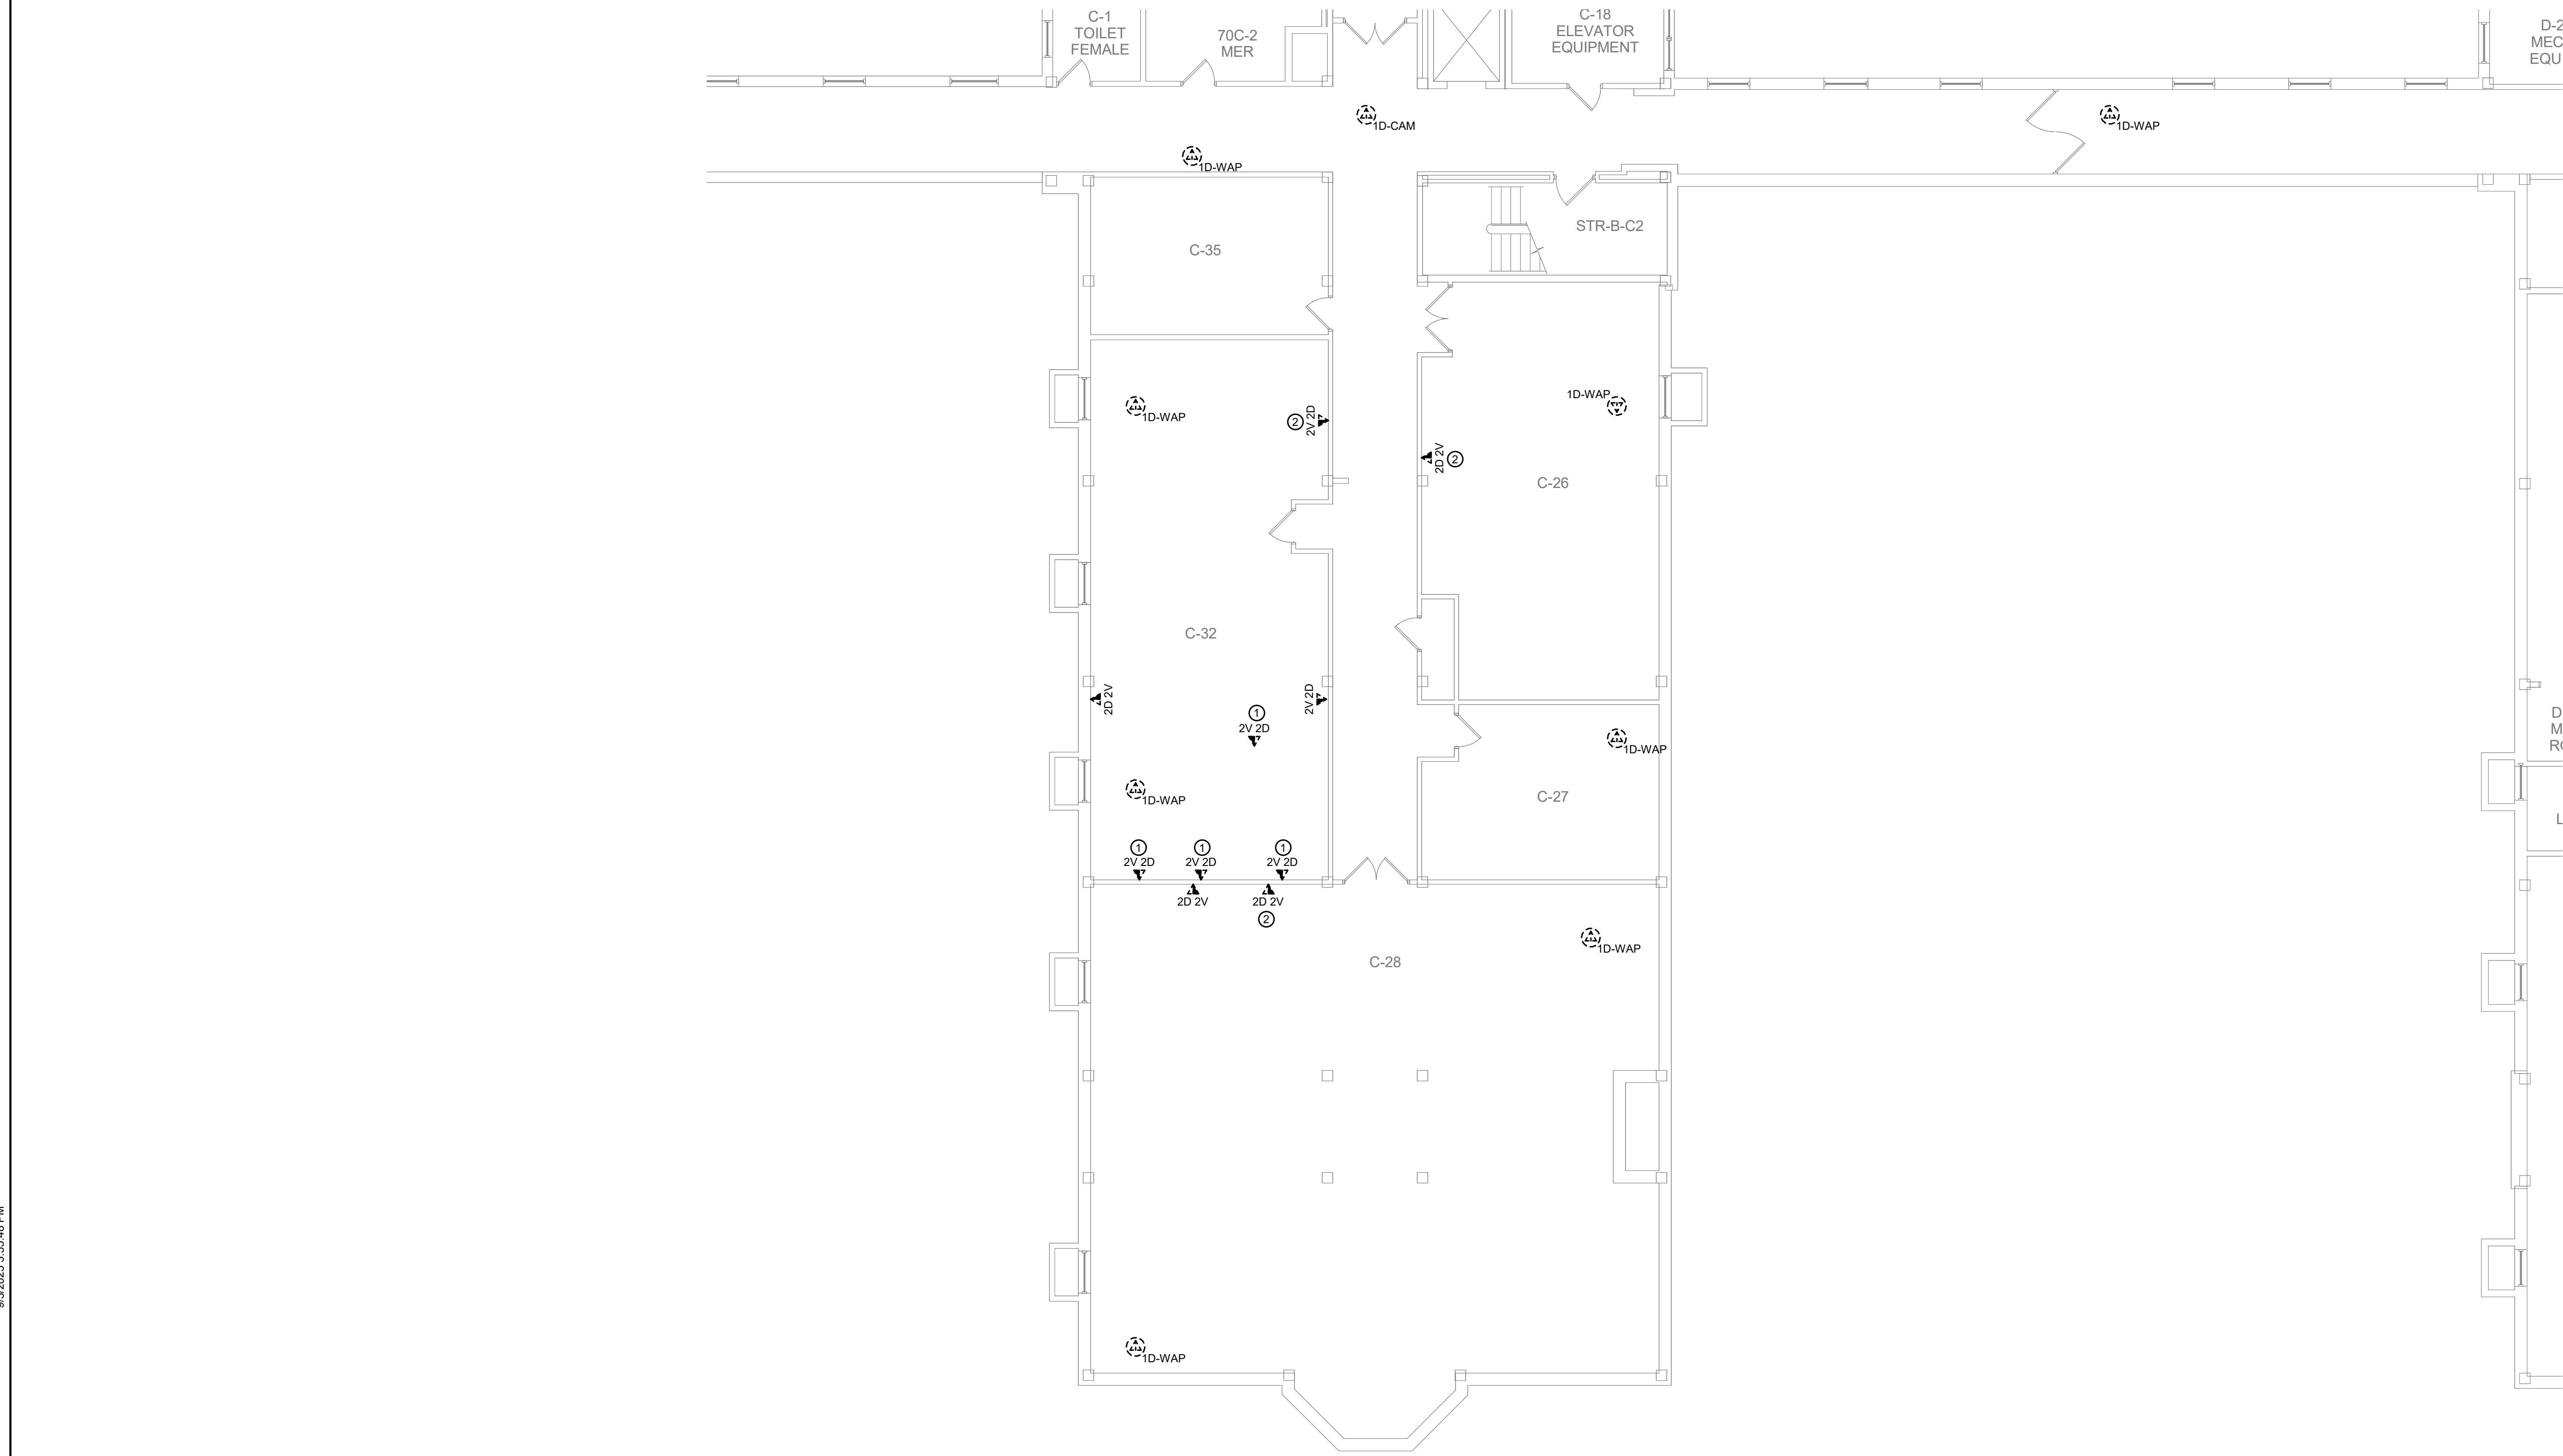

- SHEET NOTES:**
1. REMOVE ALL NETWORK CABLING TO POINTS OF TERMINATION IN ASSOCIATED TELECOM ROOMS. REFER TO FLOOR PLANS AND SHEET T1001 FOR TR ROOM LOCATIONS.
 2. REFER TO ARCHITECTURAL PHASING PLANS FOR WHEN EXISTING CABLING IS ALLOWED TO BE DEMOLISHED.
 3. FOR ALL EXISTING WIRELESS ACCESS POINTS AND SURVEILLANCE CAMERAS, DEVICES SHALL REMAIN. SCOPE OF WORK INCLUDES CABLE REPLACEMENT ONLY. COORDINATE WITH COR FOR ANY DOWNTIME OF DEVICES.
 4. EXISTING LOCATIONS OF WORK AREA, OUTLETS SHOWN ON THIS SHEET MAY NOT NECESSARILY BE IN THE EXACT LOCATION AS IDENTIFIED.

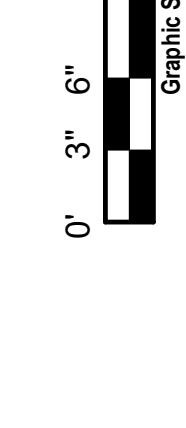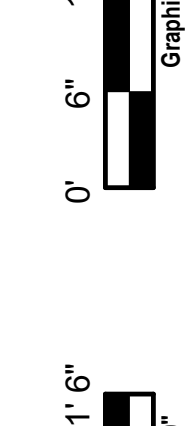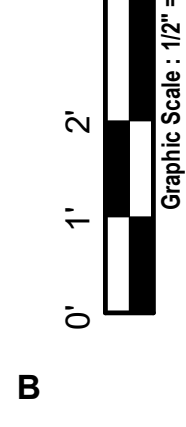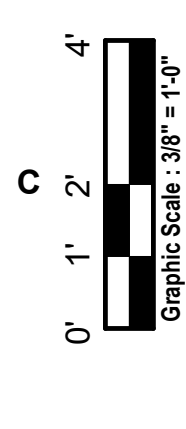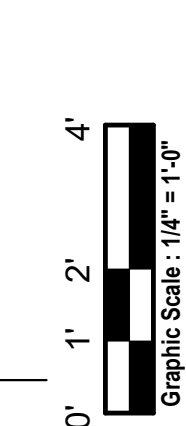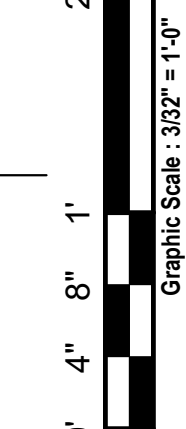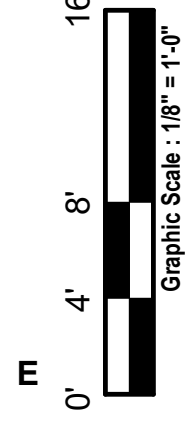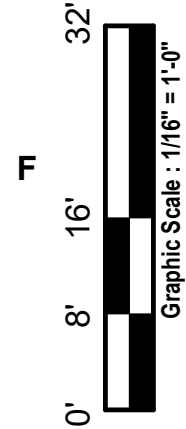

1 BUILDING 70 BASEMENT DEMOLITION PLAN - TECHNOLOGY - AREA C SOUTH
1/8" = 1'-0"

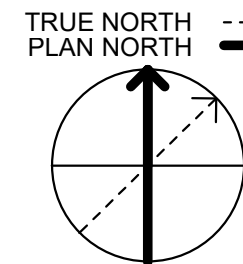

35% SCHEMATIC DESIGN SUBMISSION	5.17.21
65% DESIGN DEVELOPMENT SUBMISSION	6.15.21
65% DESIGN DEVELOPMENT RESUBMISSION	8.25.21
Revisions:	Date:

CONSULTANT

IMEG

15 SUNNEN DRIVE
SUITE 104
ST. LOUIS, MO 63143
P: 314.645.1132 F: 314.645.1173
PROJECT #18004375.03

ARCHITECT/ENGINEER OF RECORD

Romanyk Consulting
Focusing on what matters

Romanyk Consulting Corp. www.romanykconsulting.com
3308 Preston Road, Suite 350-164, Plano, Texas 75093

STAMP

Bicsi
DAVID LARSON
BICS1 ID # 106098
EXPIRES 12-31-25
REGISTERED COMMUNICATIONS DISTRIBUTION DESIGNER

Office of
Construction
and Facilities
Management

VA U.S. Department
of Veterans Affairs

Drawing Title
BUILDING 70 BASEMENT DEMO PLAN -
TECHNOLOGY - AREA C SOUTH

Approved:

Phase
FINAL BID DOCUMENTS

Sprinklered
FULLY SPRINKLERED

Project Title
EHRM INFRASTRUCTURE
UPGRADES - MILWAUKEE, WI

Location
5000 W. NATIONAL AVENUE MILWAUKEE, WI

Issue Date
SEPTEMBER 05, 2025

Checked
PHINIE

Drawn
MAIBEJ

Project Number
695-21-700

Building Number
70

Drawing Number
70-TD100C-S

F

E

D


C

B

A


9/2/2025 3:55:49 PM



Autodesk Docs\DCFM East - Milwaukee EHRM (R24)T24_1804375.03_VA MilWEHRM_C.rvt

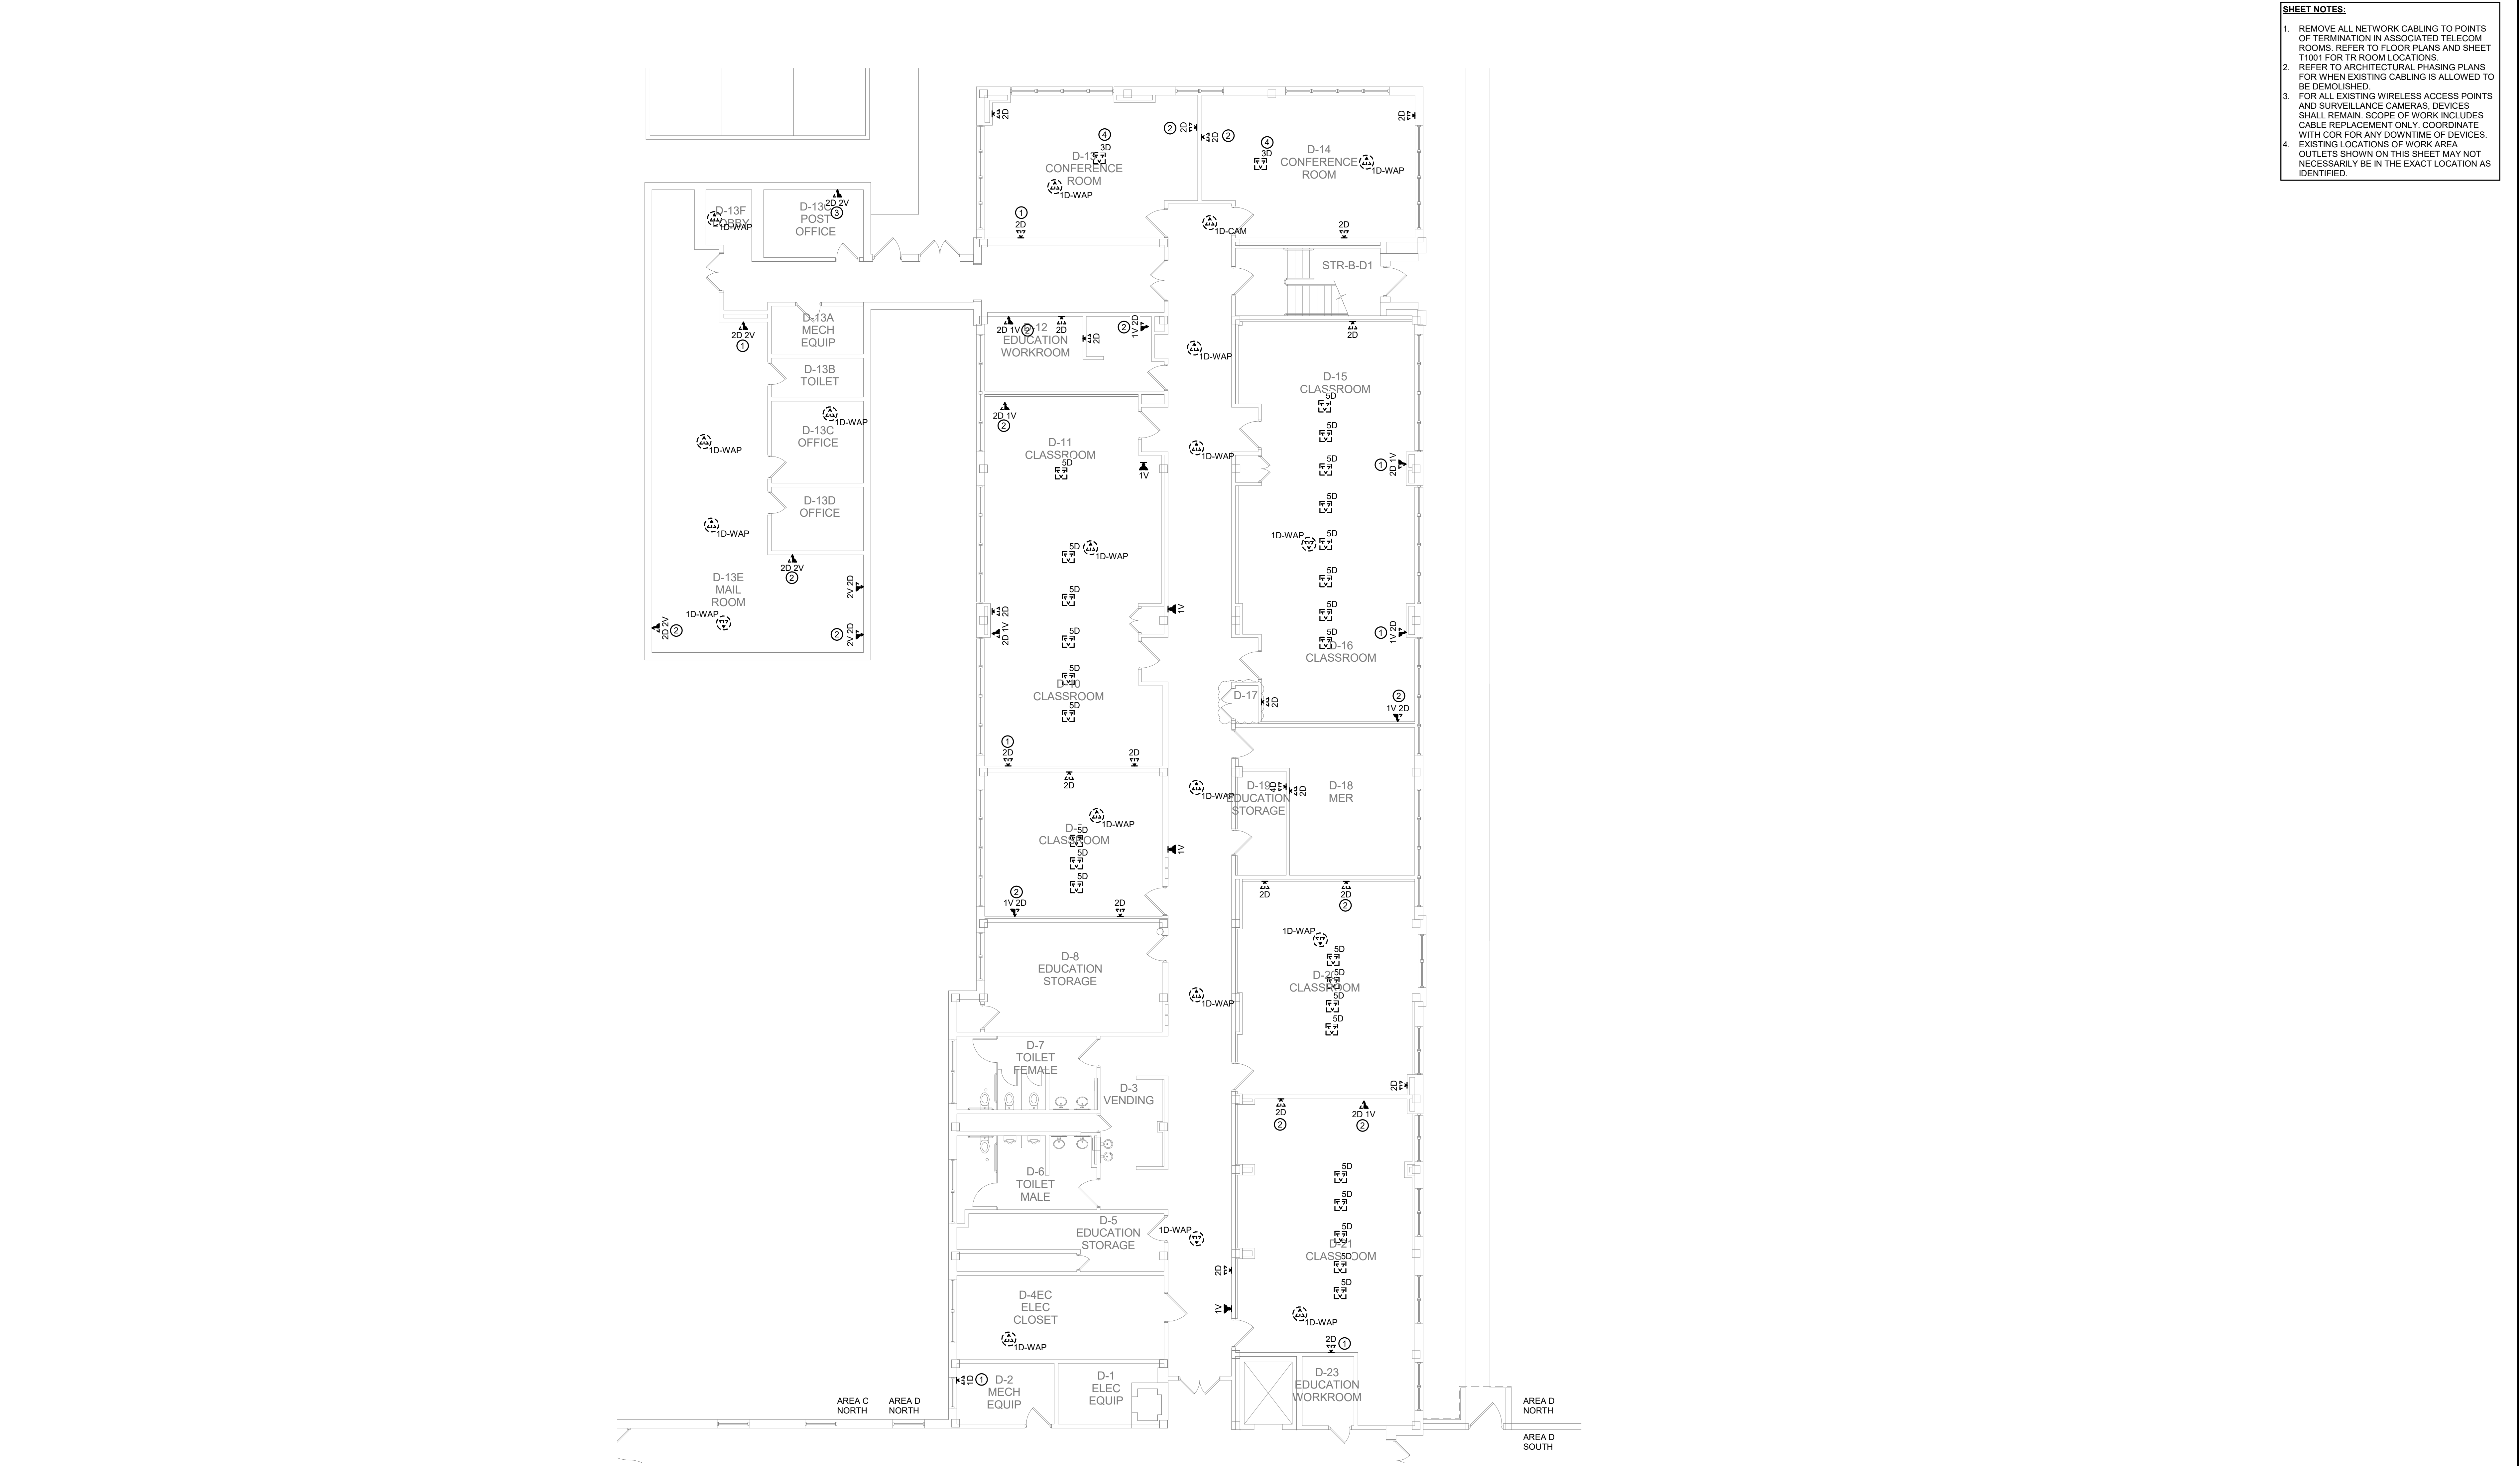


- SHEET NOTES:**
1. REMOVE ALL NETWORK CABLING TO POINTS OF TERMINATION IN ASSOCIATED TELECOM ROOMS. REFER TO FLOOR PLANS AND SHEET T1001 FOR TR ROOM LOCATIONS.
 2. REFER TO ARCHITECTURAL PHASING PLANS FOR WHEN EXISTING CABLING IS ALLOWED TO BE DEMOLISHED.
 3. FOR ALL EXISTING WIRELESS ACCESS POINTS AND SURVEILLANCE CAMERAS, DEVICES SHALL REMAIN. SCOPE OF WORK INCLUDES CABLE REPLACEMENT ONLY. COORDINATE WITH COR FOR ANY DOWNTIME OF DEVICES.
 4. EXISTING LOCATIONS OF WORK AREA, OUTLETS SHOWN ON THIS SHEET MAY NOT NECESSARILY BE IN THE EXACT LOCATION AS IDENTIFIED.

1 BUILDING 70 BASEMENT DEMOLITION PLAN - TECHNOLOGY - AREA D NORTH
1/8" = 1'-0"

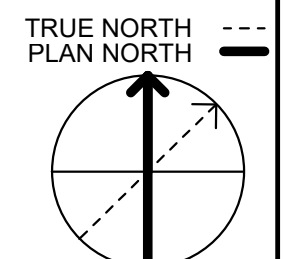

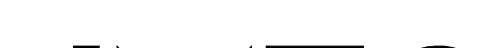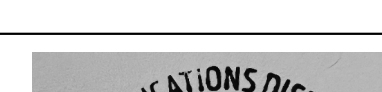35% SCHEMATIC DESIGN SUBMISSION		5.17.21	CONSULTANT	 the future, built Smarter www.imegcorp.com 15 SUNNEN DRIVE SUITE 104 ST. LOUIS, MO 63143 P: 314.645.1132 F: 314.645.1173 PROJECT #18004375.03	ARCHITECT/ENGINEER OF RECORD	 Romanyk Consulting Focusing on what matters Romanyk Consulting Corp. www.romanykconsulting.com 3308 Preston Road, Suite 350-164, Plano, Texas 75093	STAMP 	Office of Construction and Facilities Management VA U.S. Department of Veterans Affairs	Drawing Title BUILDING 70 BASEMENT DEMO PLAN - TECHNOLOGY - AREA D NORTH	Phase FINAL BID DOCUMENTS	Project Title EHRM INFRASTRUCTURE UPGRADES - MILWAUKEE, WI	Project Number 695-21-700	
65% DESIGN DEVELOPMENT SUBMISSION		6.15.21											Building Number 70
65% DESIGN DEVELOPMENT RESUBMISSION		8.25.21											
Revisions:		Date:							Approved:	Sprinklered FULLY SPRINKLERED	Location 5000 W. NATIONAL AVENUE MILWAUKEE, WI	Drawing Number 70-TD100D-N	
											Issue Date SEPTEMBER 05, 2025	Checked PHINIE	Drawn MAIBEJ

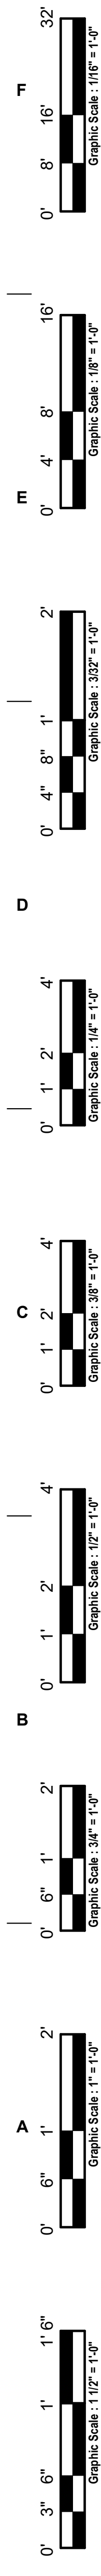

F

E

D

C


B

A


9/2/2025 3:55:51 PM

Autodesk Docs\DCFM East - Milwaukee EHRM (R24)T24_1804375.03_VA Milwaukee_C.dwt

- SHEET NOTES:**
1. REMOVE ALL NETWORK CABLING TO POINTS OF TERMINATION IN ASSOCIATED TELECOM ROOMS. REFER TO FLOOR PLANS AND SHEET T1001 FOR TR ROOM LOCATIONS.
 2. REFER TO ARCHITECTURAL PHASING PLANS FOR WHEN EXISTING CABLING IS ALLOWED TO BE DEMOLISHED.
 3. FOR ALL EXISTING WIRELESS ACCESS POINTS AND SURVEILLANCE CAMERAS, DEVICES SHALL REMAIN. SCOPE OF WORK INCLUDES CABLE REPLACEMENT ONLY. COORDINATE WITH COR FOR ANY DOWNTIME OF DEVICES.
 4. EXISTING LOCATIONS OF WORK AREA, OUTLETS SHOWN ON THIS SHEET MAY NOT NECESSARILY BE IN THE EXACT LOCATION AS IDENTIFIED.

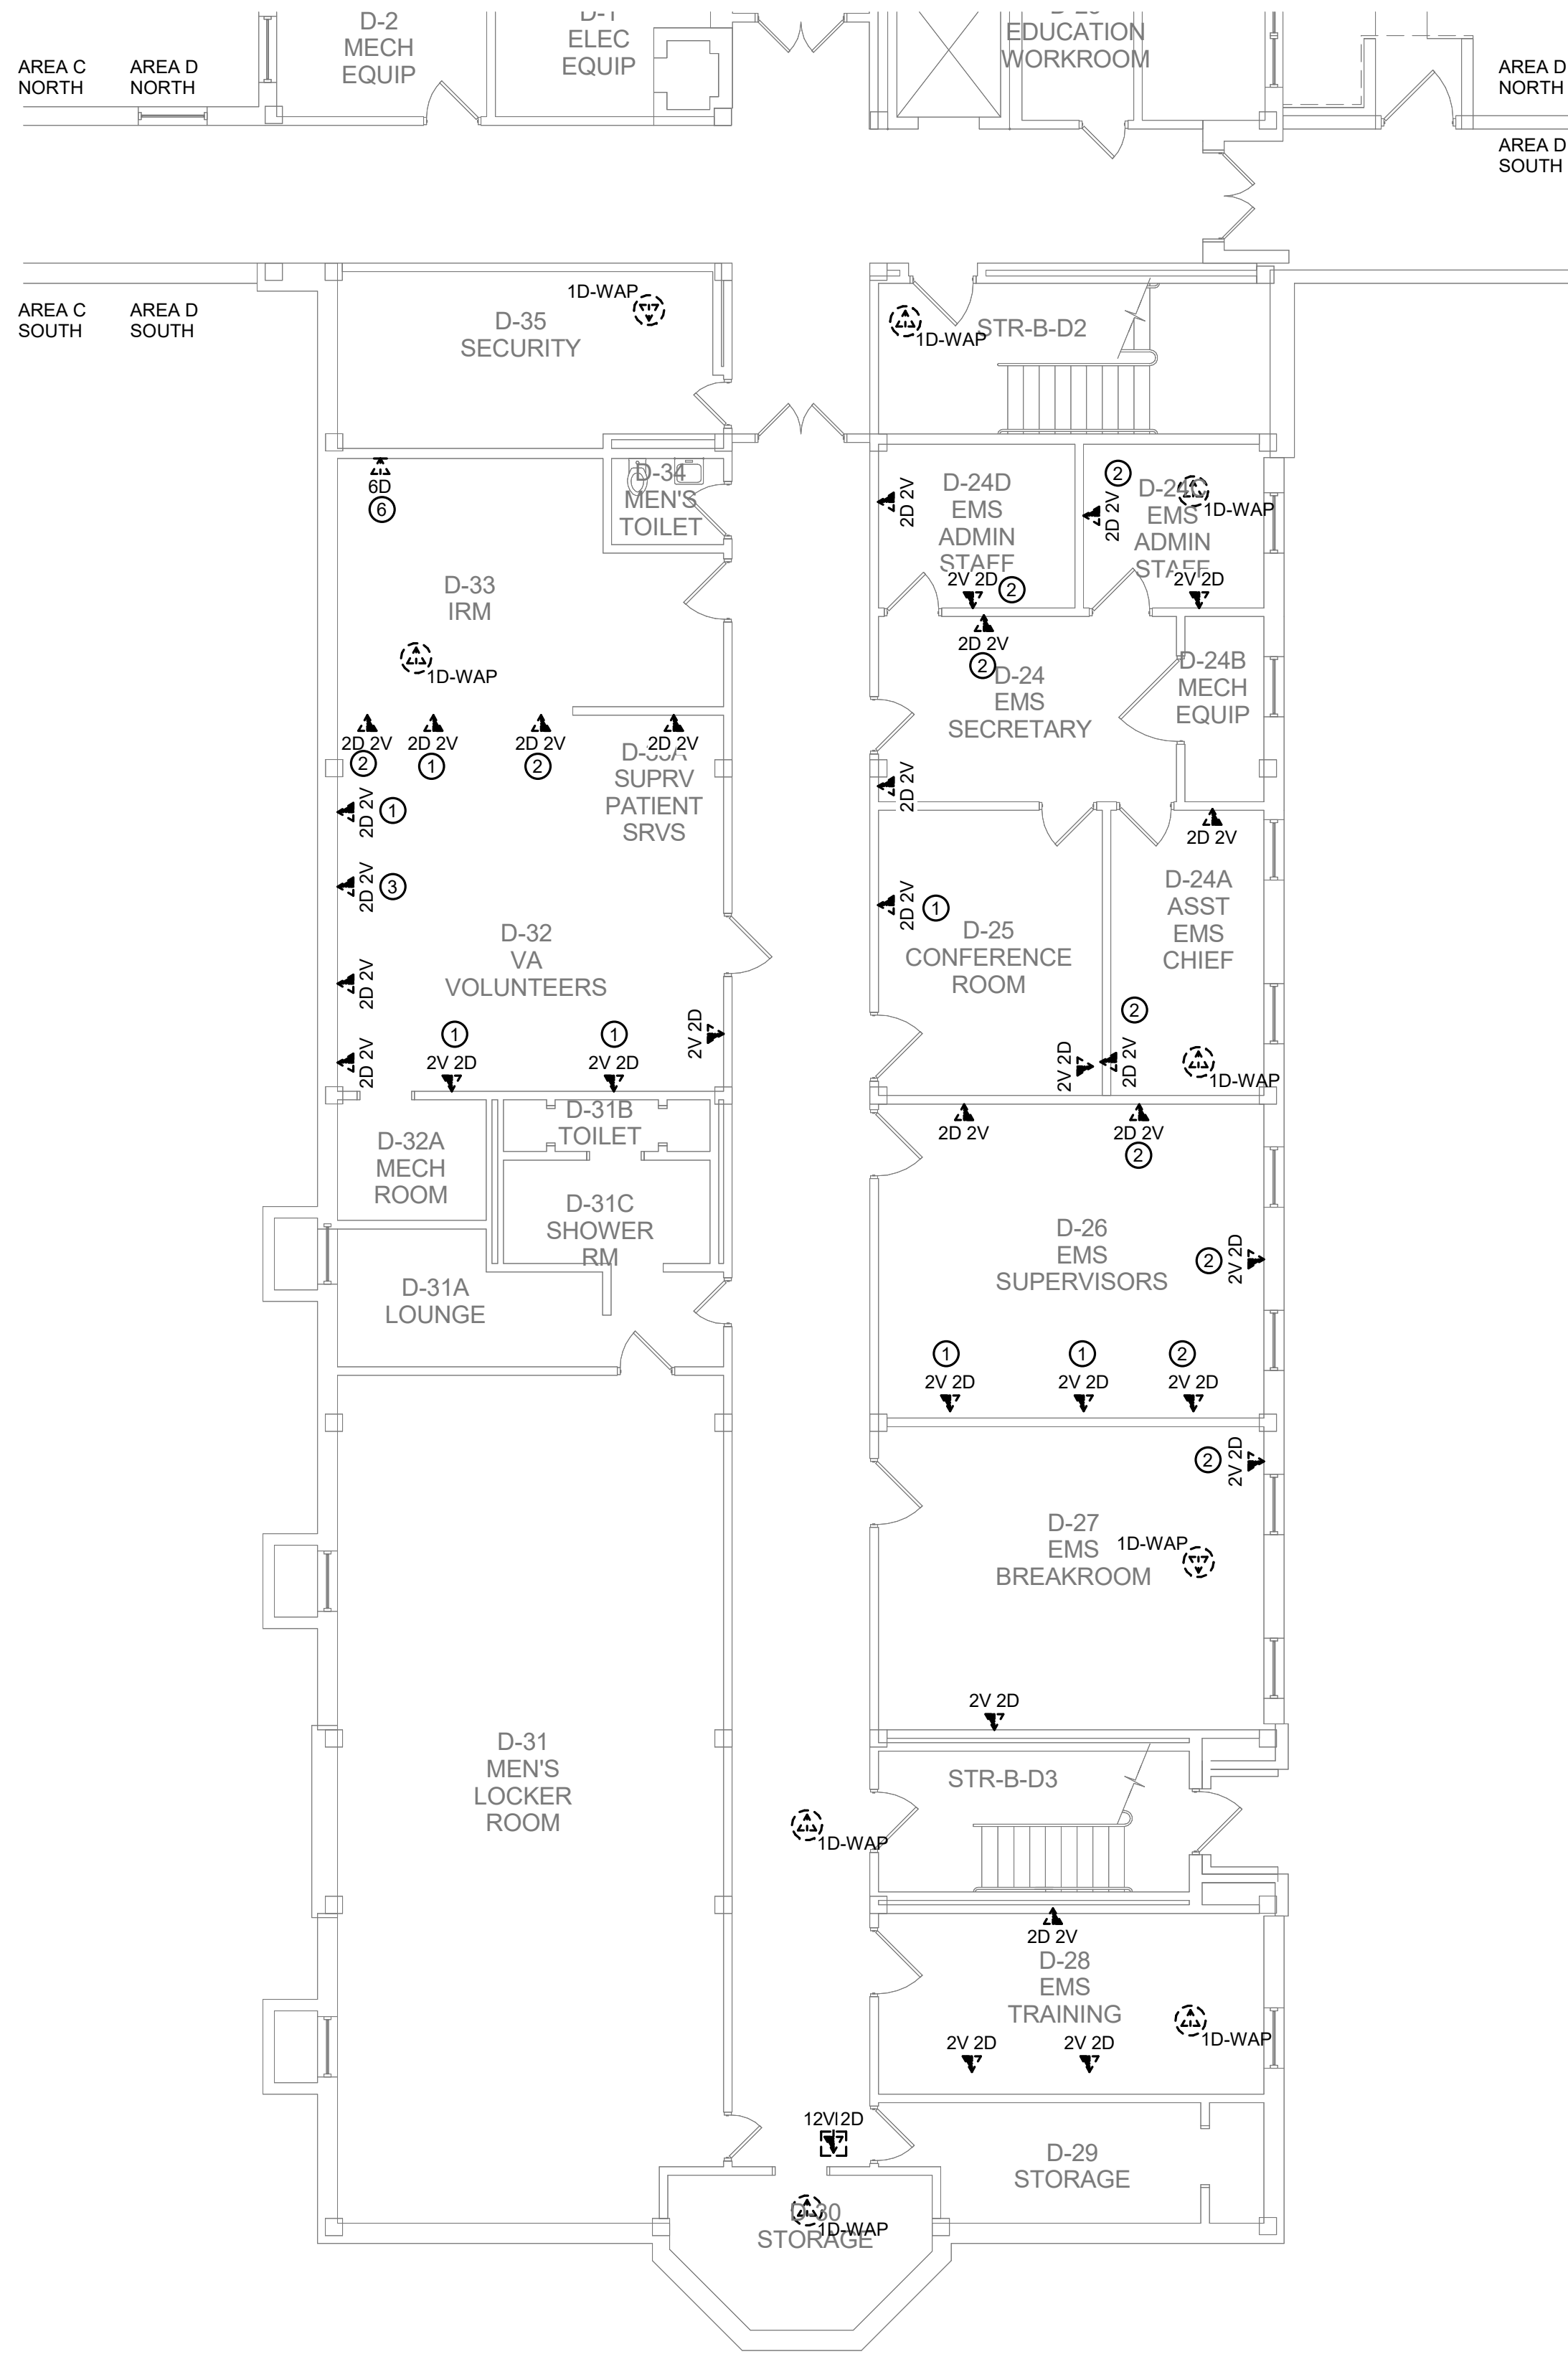

1 BUILDING 70 BASEMENT DEMOLITION PLAN - TECHNOLOGY - AREA D SOUTH
1/8" = 1'-0"

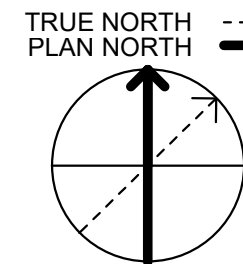

35% SCHEMATIC DESIGN SUBMISSION	5.17.21
65% DESIGN DEVELOPMENT SUBMISSION	6.15.21
65% DESIGN DEVELOPMENT RESUBMISSION	8.25.21
Revisions:	Date:

CONSULTANT

IMEG

THE FUTURE IS IN THE HANDS OF THE IMEG CORPORATION
15 SUNNEN DRIVE
SUITE 104
ST. LOUIS, MO 63143
P: 314.645.1132 F: 314.645.1173
PROJECT #18004375.03

ARCHITECT/ENGINEER OF RECORD

Romanyk Consulting
Focusing on what matters

Romanyk Consulting Corp. www.romanykconsulting.com
3308 Preston Road, Suite 350-164, Plano, Texas 75093

STAMP

Bicsi
DAVID LARSON
BICS1 ID # 106098
EXPIRES 12-31-25
REGISTERED COMMUNICATIONS DISTRIBUTION DESIGNER

Office of
Construction
and Facilities
Management

VA U.S. Department
of Veterans Affairs

Drawing Title
BUILDING 70 BASEMENT DEMO PLAN -
TECHNOLOGY - AREA D SOUTH

Approved:

Phase
FINAL BID DOCUMENTS

Sprinklered
FULLY SPRINKLERED

Project Title
EHRM INFRASTRUCTURE
UPGRADES - MILWAUKEE, WI

Location
5000 W. NATIONAL AVENUE, MILWAUKEE, WI

Issue Date
SEPTEMBER 05, 2025

Checked
PHINIE

Drawn
MAIBEJ

Project Number
695-21-700

Building Number
70

Drawing Number
70-TD100D-S

F

E

D


C

B


A

9/3/2025 3:55:52 PM


Autodesk Docs\DCFM East - Milwaukee EHRM (R24)T24_1804375.03_VA MilWEHRM_C.dwt

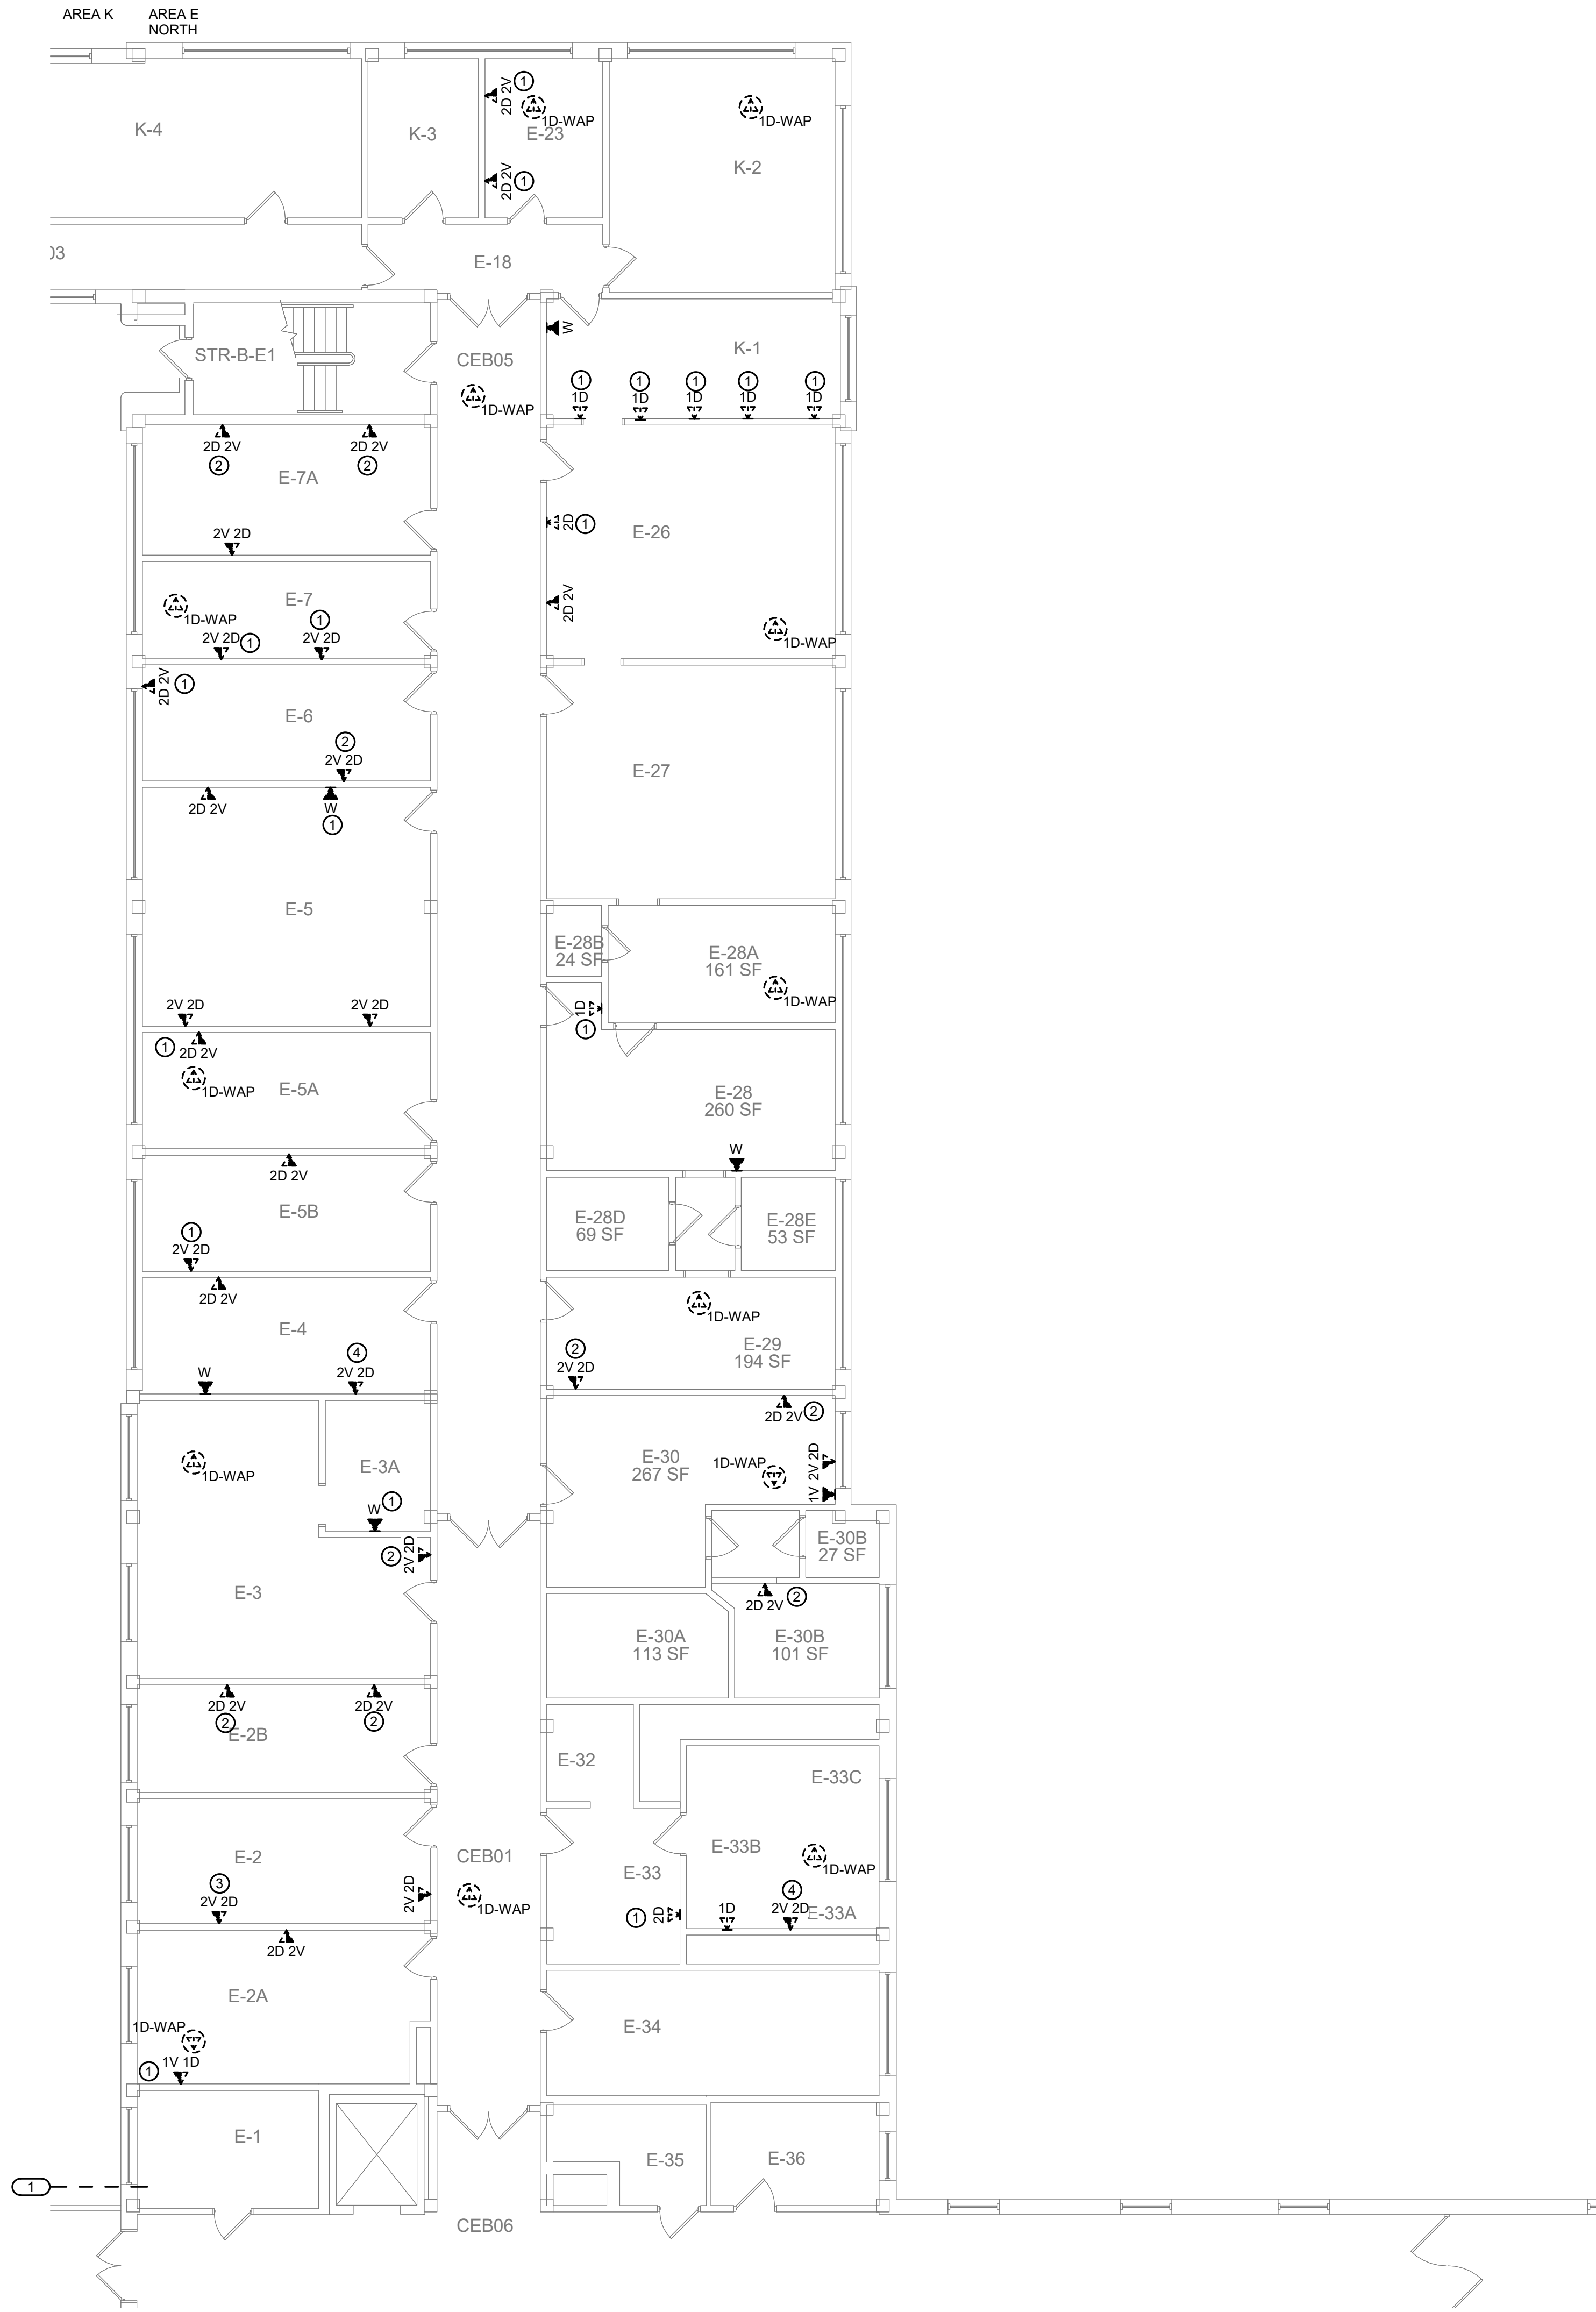

- SHEET NOTES:**
1. REMOVE ALL NETWORK CABLING TO POINTS OF TERMINATION IN ASSOCIATED TELECOM ROOMS. REFER TO FLOOR PLANS AND SHEET T1001 FOR TR ROOM LOCATIONS.
 2. REFER TO ARCHITECTURAL PHASING PLANS FOR WHEN EXISTING CABLING IS ALLOWED TO BE DEMOLISHED.
 3. FOR ALL EXISTING WIRELESS ACCESS POINTS AND SURVEILLANCE CAMERAS, DEVICES SHALL REMAIN. SCOPE OF WORK INCLUDES CABLE REPLACEMENT ONLY. COORDINATE WITH COR FOR ANY DOWNTIME OF DEVICES.
 4. EXISTING LOCATIONS OF WORK AREA, OUTLETS SHOWN ON THIS SHEET MAY NOT NECESSARILY BE IN THE EXACT LOCATION AS IDENTIFIED.
- KEYNOTES:** (#)
1. EXISTING BACKBONE CABLING PATH, LEG "A" TO BUILDING 123. PROTECT IN PLACE.

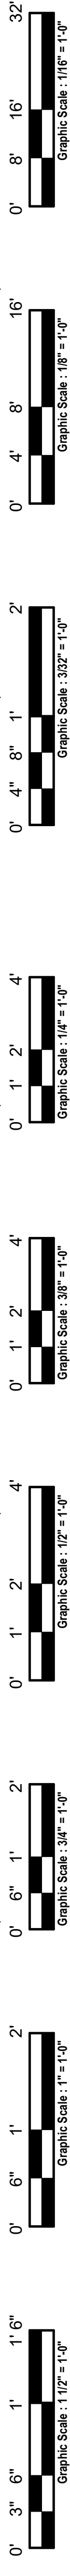

1 BUILDING 70 BASEMENT DEMOLITION PLAN - TECHNOLOGY - AREA E NORTH
1/8" = 1'-0"

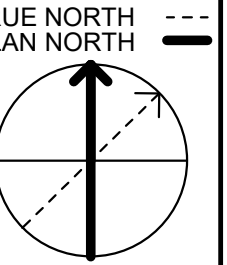

35% SCHEMATIC DESIGN SUBMISSION	5.17.21
65% DESIGN DEVELOPMENT SUBMISSION	6.15.21
65% DESIGN DEVELOPMENT RESUBMISSION	8.25.21
Revisions:	Date:

CONSULTANT

IMEG
15 SUNNEN DRIVE
SUITE 104
ST. LOUIS, MO 63143
P: 314.645.1132 F: 314.645.1173
PROJECT #18004375.03

ARCHITECT/ENGINEER OF RECORD

Romanyk Consulting
Focusing on what matters

Romanyk Consulting Corp. www.romanykconsulting.com
3308 Preston Road, Suite 350-164, Plano, Texas 75093

STAMP

Bicsi
DAVID LARSON
BICS1 ID # 106098
Expires 12-31-25

Office of
Construction
and Facilities
Management

VA U.S. Department
of Veterans Affairs

Drawing Title
BUILDING 70 BASEMENT DEMO PLAN -
TECHNOLOGY - AREA E NORTH

Approved:

Phase
FINAL BID DOCUMENTS

Sprinklered
FULLY SPRINKLERED

Project Title
EHRM INFRASTRUCTURE
UPGRADES - MILWAUKEE, WI

Location
5000 W. NATIONAL AVENUE, MILWAUKEE, WI

Issue Date
SEPTEMBER 05, 2025

Checked
PHINIE

Drawn
MAIBEJ

Project Number
695-21-700

Building Number
70

Drawing Number
70-TD100E-N

F

E

D

C


B

A

9/3/2025 3:55:54 PM

Autodesk Docs\OCF\East - Milwaukee EHRM (R24)T24_1804375\03_VA MilwEHRM_C.dwt

- SHEET NOTES:**
1. REMOVE ALL NETWORK CABLING TO POINTS OF TERMINATION IN ASSOCIATED TELECOM ROOMS. REFER TO FLOOR PLANS AND SHEET T1001 FOR TR ROOM LOCATIONS.
 2. REFER TO ARCHITECTURAL PHASING PLANS FOR WHEN EXISTING CABLING IS ALLOWED TO BE DEMOLISHED.
 3. FOR ALL EXISTING WIRELESS ACCESS POINTS AND SURVEILLANCE CAMERAS, DEVICES SHALL REMAIN. SCOPE OF WORK INCLUDES CABLE REPLACEMENT ONLY. COORDINATE WITH COR FOR ANY DOWNTIME OF DEVICES. EXISTING LOCATIONS OF WORK AREA, OUTLETS SHOWN ON THIS SHEET MAY NOT NECESSARILY BE IN THE EXACT LOCATION AS IDENTIFIED.

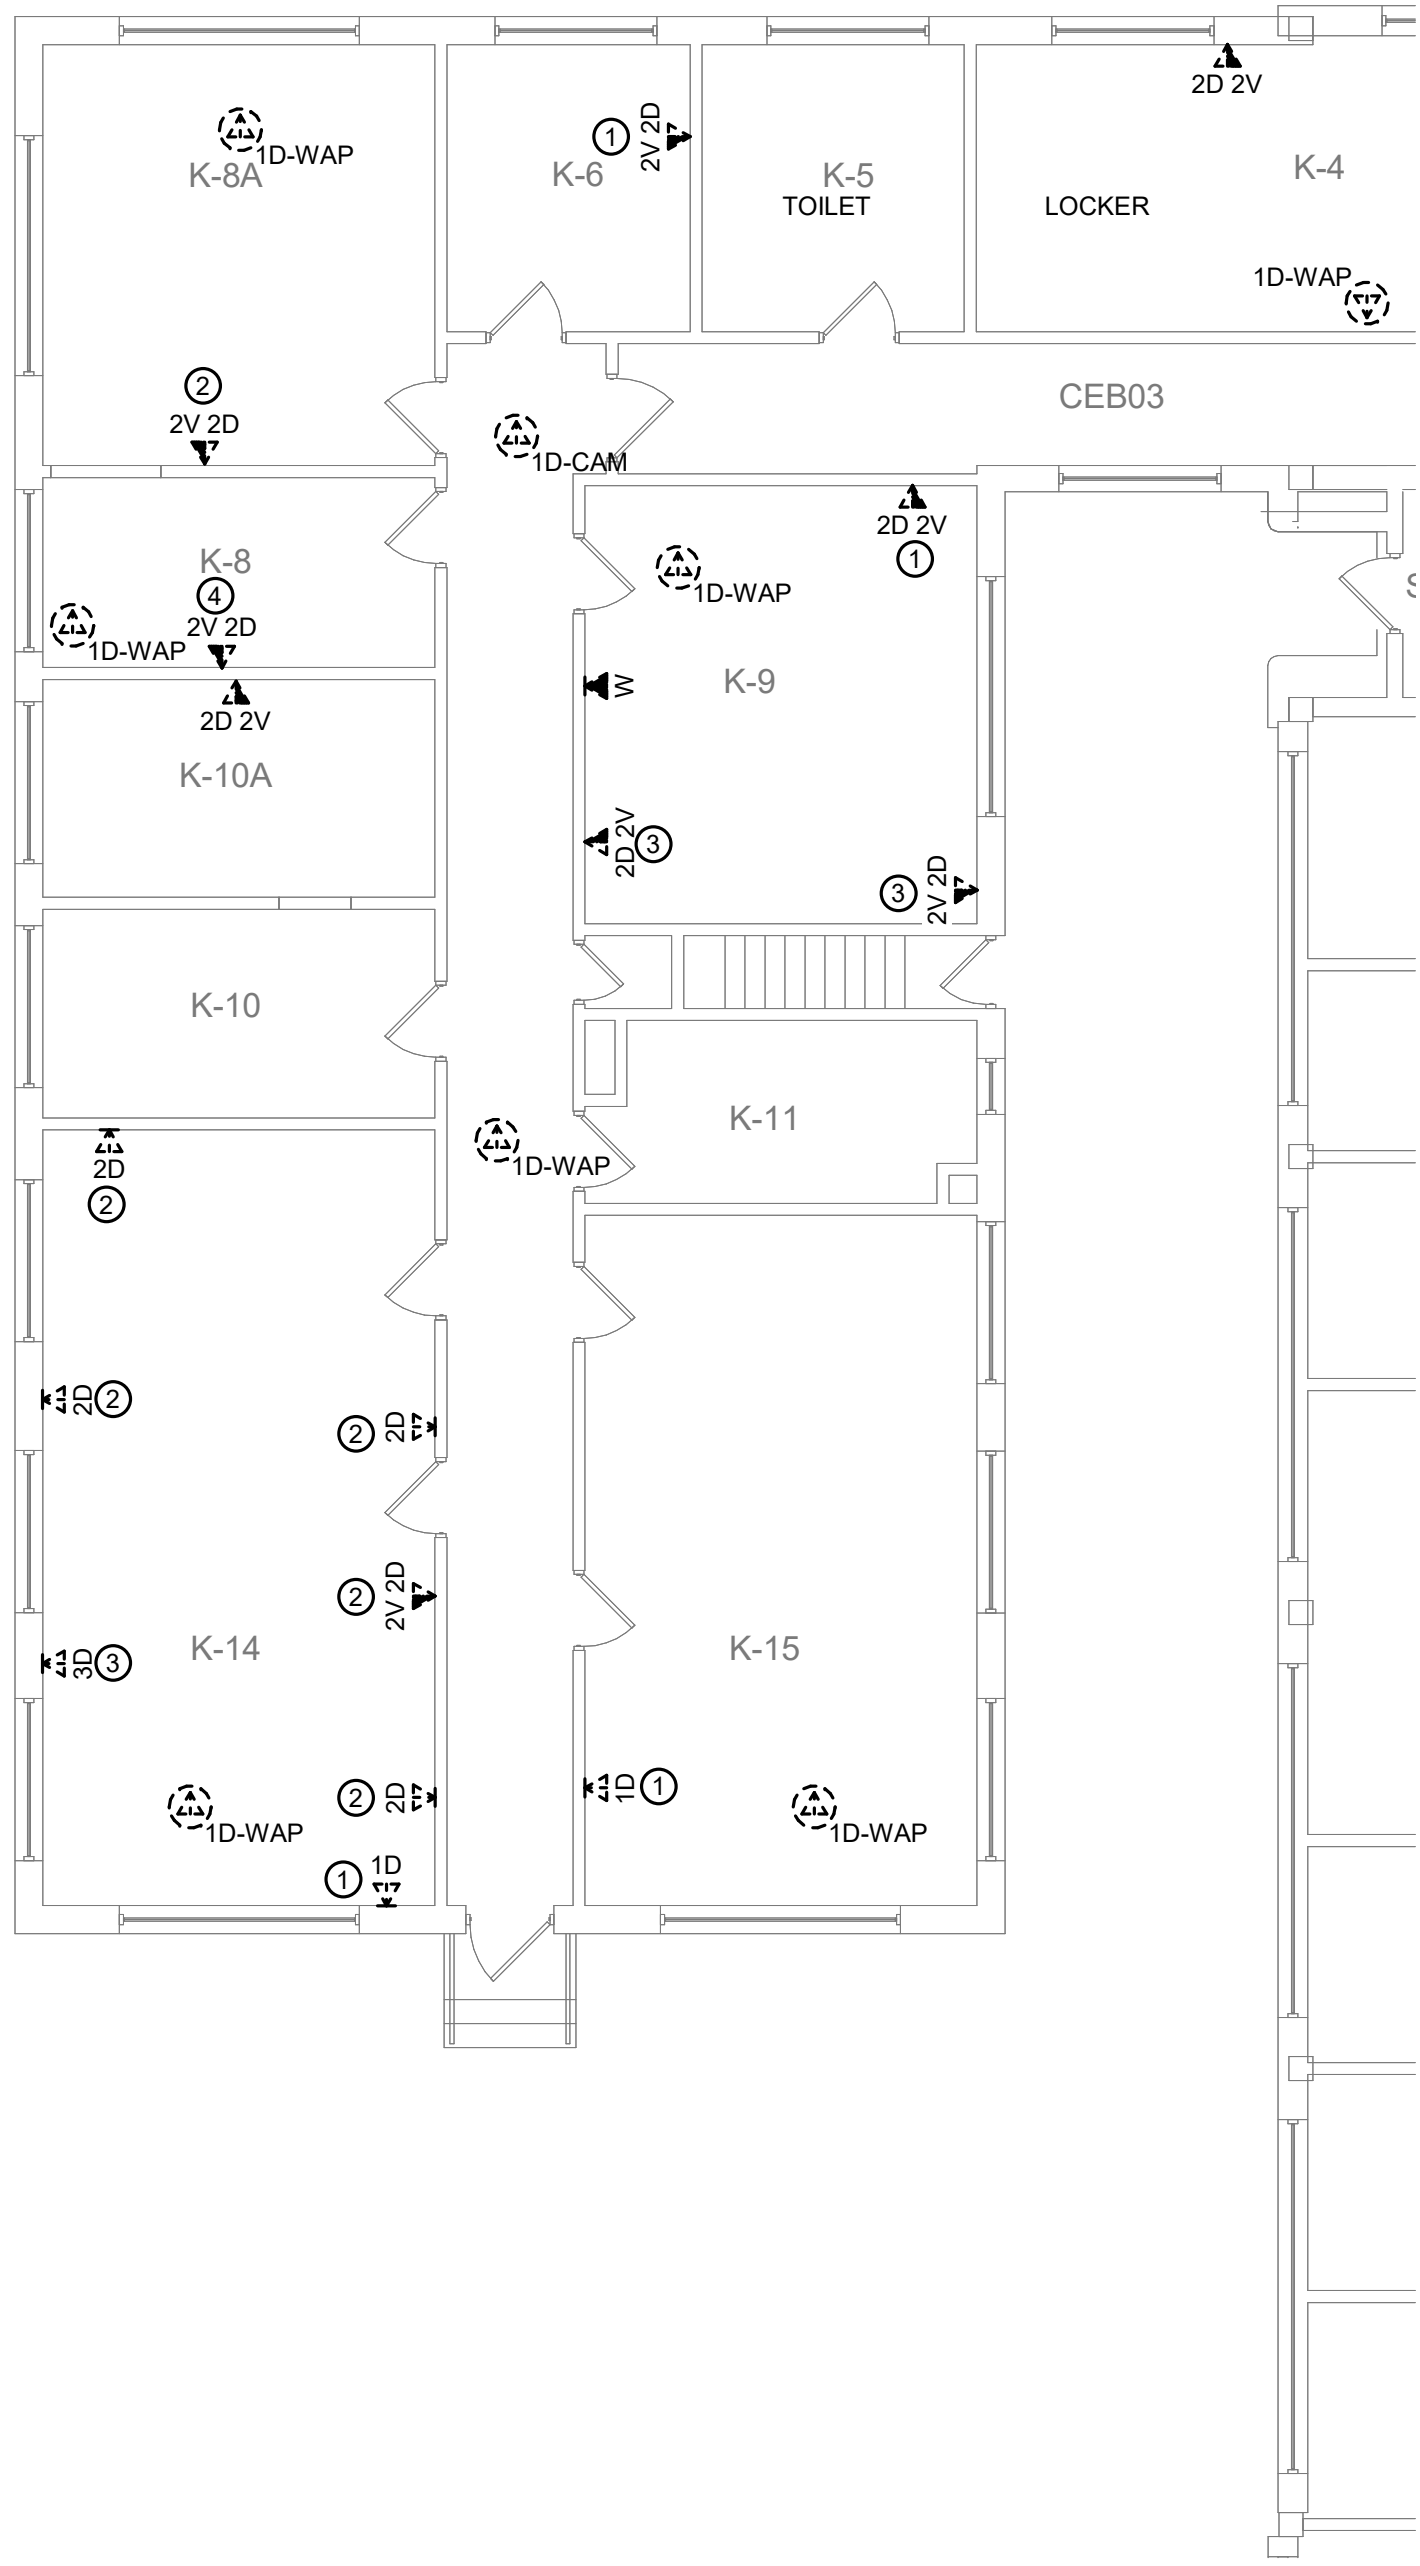

1 BUILDING 70 BASEMENT DEMOLITION PLAN - TECHNOLOGY - AREA K
1/8" = 1'-0"

35% SCHEMATIC DESIGN SUBMISSION	5.17.21
65% DESIGN DEVELOPMENT SUBMISSION	6.15.21
65% DESIGN DEVELOPMENT RESUBMISSION	8.25.21
Revisions:	Date:

CONSULTANT

IMEG
The Future is Full of Solutions www.imegcorp.com
15 SUNNEN DRIVE
SUITE 104
ST. LOUIS, MO 63143
P: 314.645.1132 F: 314.645.1173
PROJECT #18004375.03

ARCHITECT/ENGINEER OF RECORD

Romanyk Consulting
Focusing on what matters
Romanyk Consulting Corp. www.romanykconsulting.com
3308 Preston Road, Suite 350-164, Plano, Texas 75093

STAMP

Bicsi
DAVID LARSON
BICS1 ID # 106098
EXPIRES 12-31-25
REGISTERED COMMUNICATIONS DISTRIBUTION DESIGNER
RCDD

Office of
Construction
and Facilities
Management

VA U.S. Department
of Veterans Affairs

Drawing Title
BUILDING 70 BASEMENT DEMO PLAN -
TECHNOLOGY - AREA K

Approved:

Phase
FINAL BID DOCUMENTS

Sprinklered
FULLY SPRINKLERED

Project Title
EHRM INFRASTRUCTURE
UPGRADES - MILWAUKEE, WI

Location
5000 W. NATIONAL AVENUE, MILWAUKEE, WI

Issue Date
SEPTEMBER 05, 2025



Checked
PHINIE

Drawn
MAIBEJ

Project Number
695-21-700

Building Number
70

Drawing Number
70-TD100K

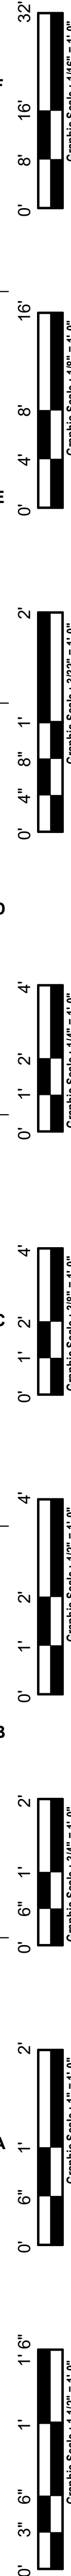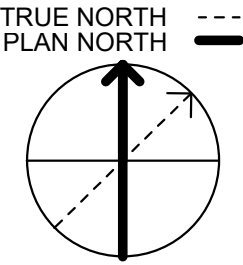

9/3/2025 3:55:55 PM
A
B
C
D
E
F
Autodesk Docs\DCFM East - Milwaukee EHRM (R24)T24_1804375.03_VA Milwaukee_C.dwg

F



E

D

C

B


A

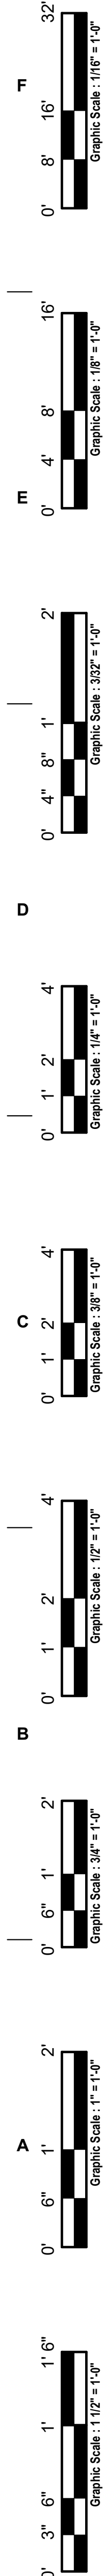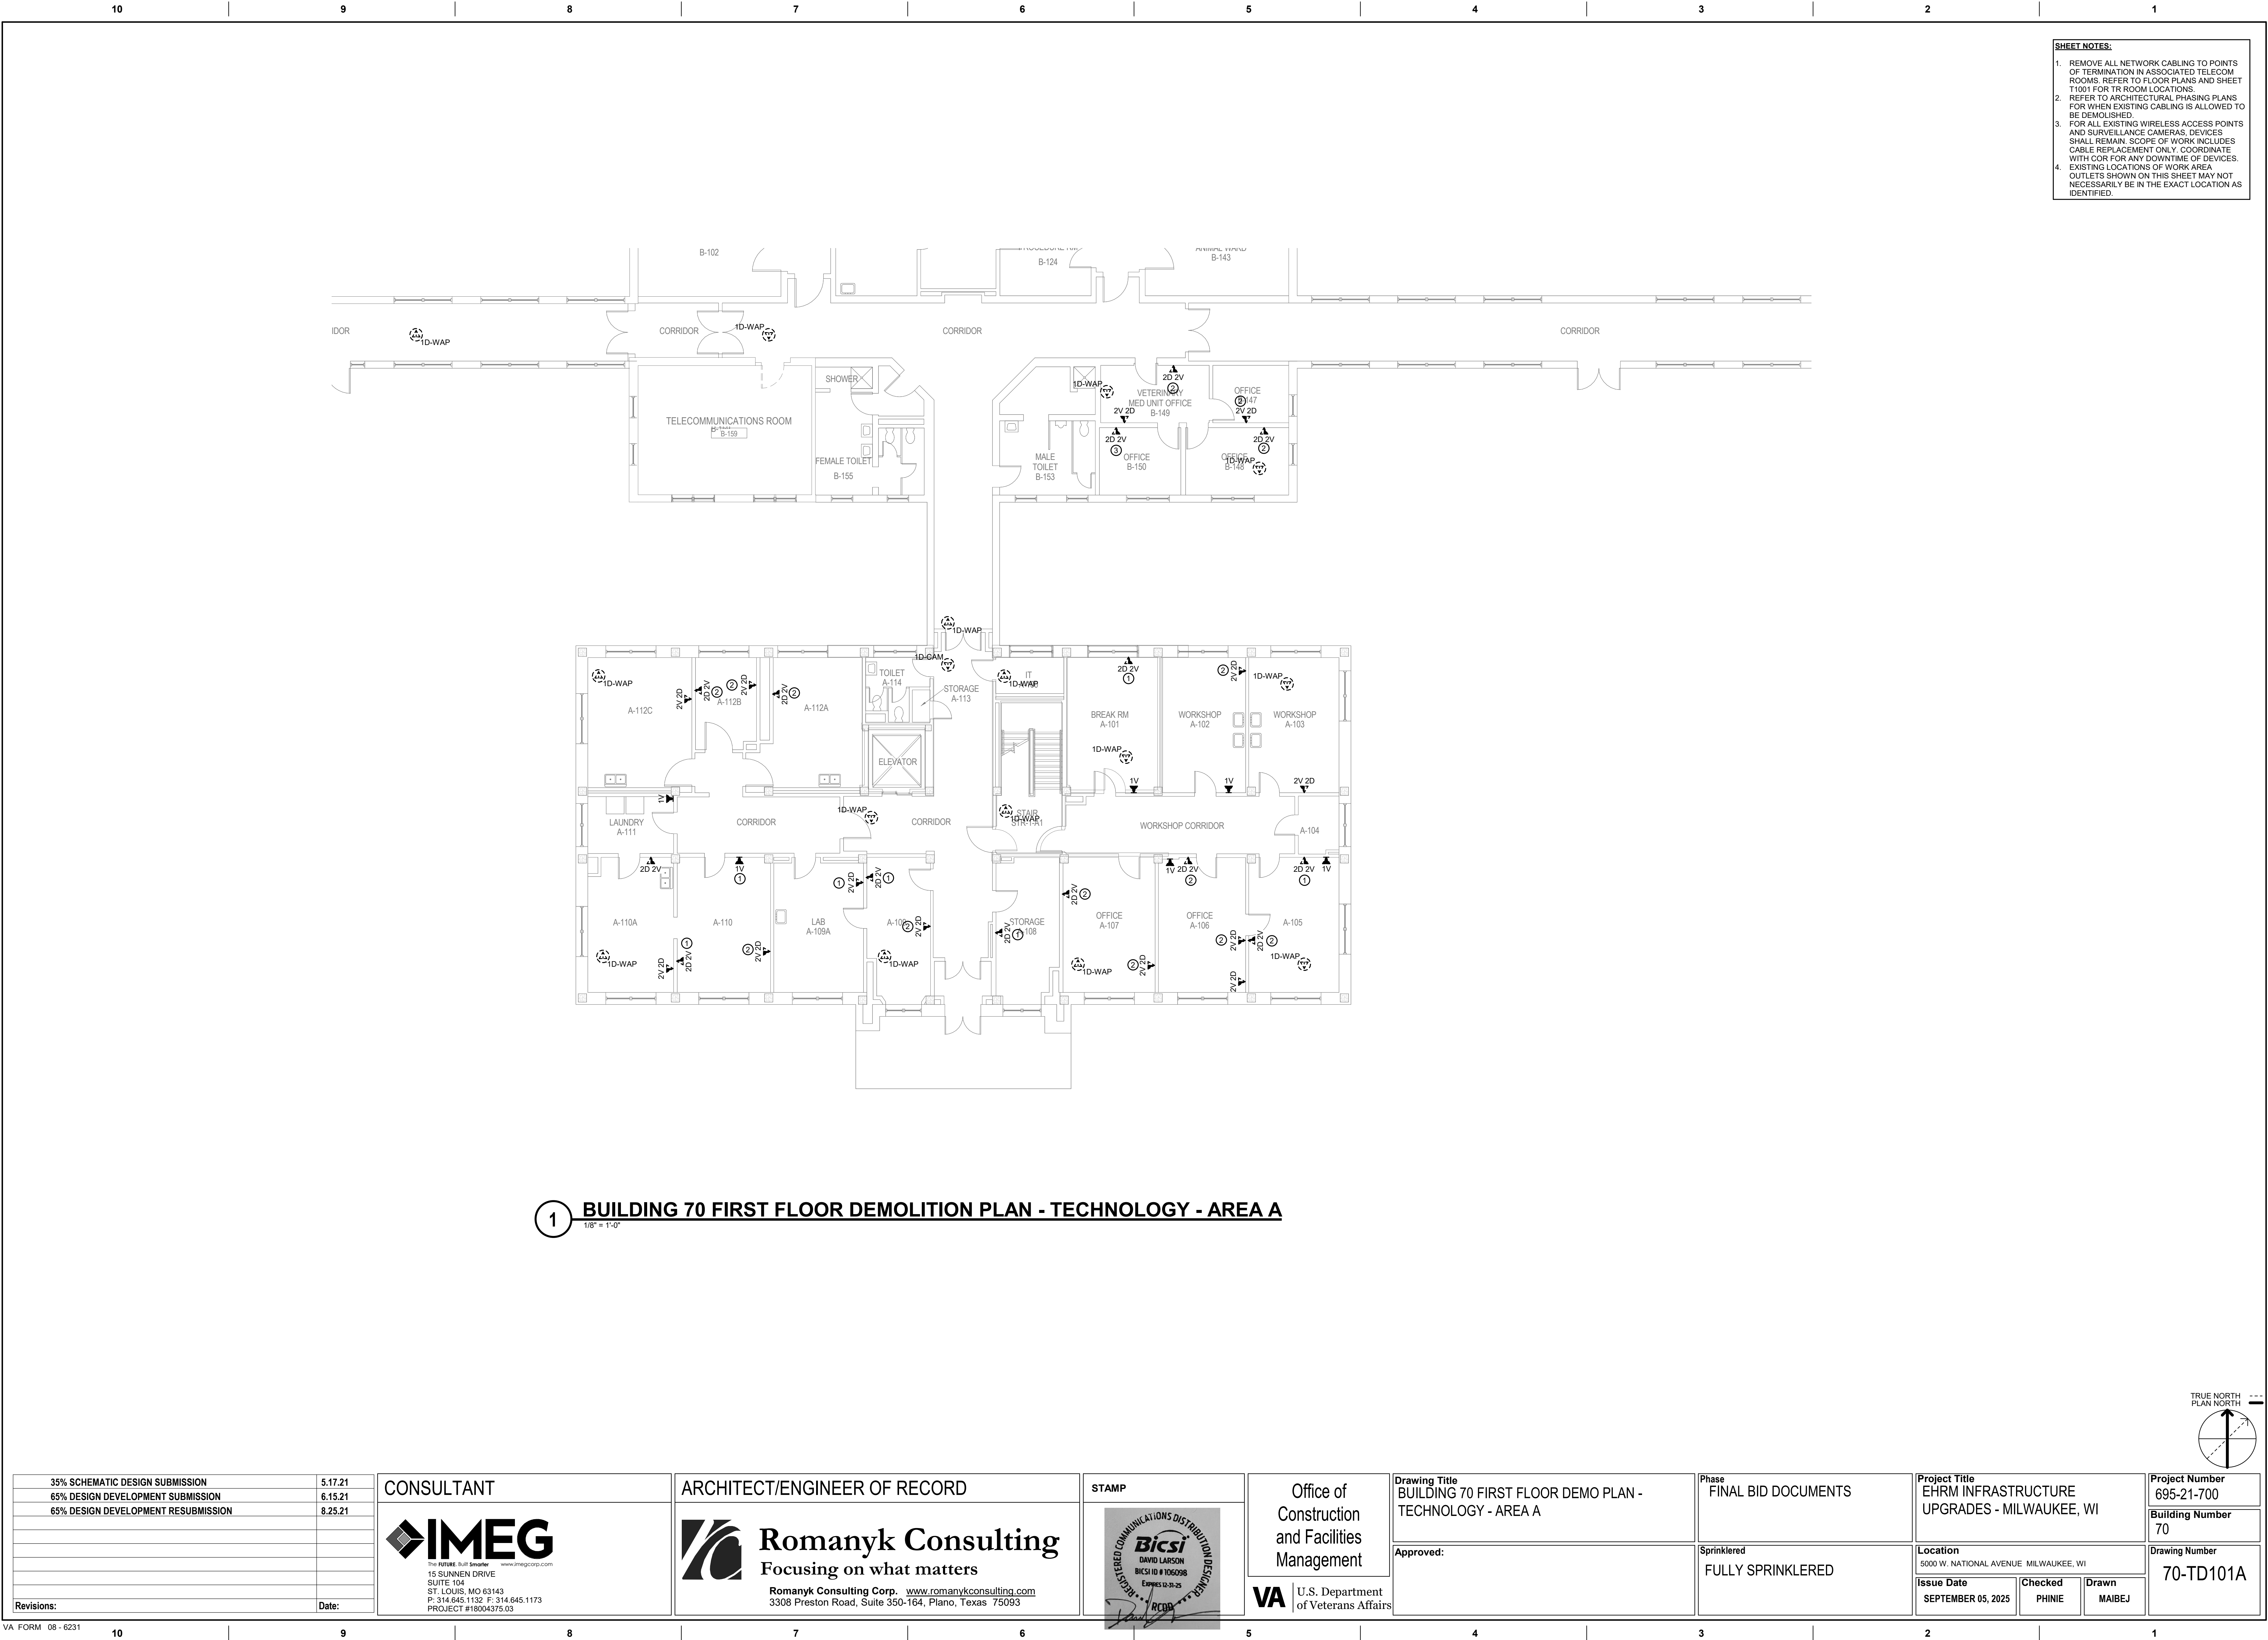

9/3/2025 3:55:57 PM
A B C D E F
Autodesk Docs\DCFM East - Milwaukee EHRM (R24)T24_1804375.03_VA Milwaukee C.d



- SHEET NOTES:**
1. REMOVE ALL NETWORK CABLING TO POINTS OF TERMINATION IN ASSOCIATED TELECOM ROOMS. REFER TO FLOOR PLANS AND SHEET T1001 FOR TR ROOM LOCATIONS.
 2. REFER TO ARCHITECTURAL PHASING PLANS FOR WHEN EXISTING CABLING IS ALLOWED TO BE DEMOLISHED.
 3. FOR ALL EXISTING WIRELESS ACCESS POINTS AND SURVEILLANCE CAMERAS, DEVICES SHALL REMAIN. SCOPE OF WORK INCLUDES CABLE REPLACEMENT ONLY. COORDINATE WITH COR FOR ANY DOWNTIME OF DEVICES.
 4. EXISTING LOCATIONS OF WORK AREA OUTLETS SHOWN ON THIS SHEET MAY NOT NECESSARILY BE IN THE EXACT LOCATION AS IDENTIFIED.

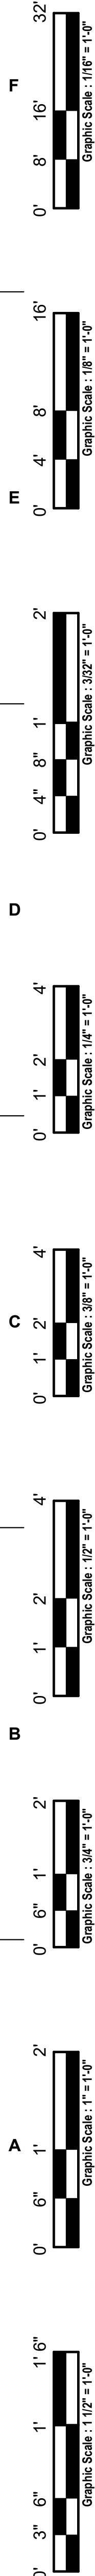

1 BUILDING 70 FIRST FLOOR DEMOLITION PLAN - TECHNOLOGY - AREA B
1/8" = 1'-0"

35% SCHEMATIC DESIGN SUBMISSION	5.17.21
65% DESIGN DEVELOPMENT SUBMISSION	6.15.21
65% DESIGN DEVELOPMENT RESUBMISSION	8.25.21
Revisions:	Date:

CONSULTANT

IMEG
15 SUNNEN DRIVE
SUITE 104
ST. LOUIS, MO 63143
P: 314.645.1132 F: 314.645.1173
PROJECT #18004375.03

ARCHITECT/ENGINEER OF RECORD

Romanyk Consulting
Focusing on what matters
Romanyk Consulting Corp. www.romanykconsulting.com
3308 Preston Road, Suite 350-164, Plano, Texas 75093

STAMP

Bicsi
DAVID LARSON
BICS1 ID # 106098
EXPIRES 12-31-25
REGISTERED COMMUNICATIONS DISTRIBUTION DESIGNER

Office of
Construction
and Facilities
Management

VA U.S. Department
of Veterans Affairs

Drawing Title
BUILDING 70 FIRST FLOOR DEMO PLAN -
TECHNOLOGY - AREA B

Approved:

Phase
FINAL BID DOCUMENTS

Sprinklered
FULLY SPRINKLERED

Project Title
EHRM INFRASTRUCTURE
UPGRADES - MILWAUKEE, WI

Location
5000 W. NATIONAL AVENUE MILWAUKEE, WI

Issue Date
SEPTEMBER 05, 2025

Checked
PHINIE

Drawn
MAIBEJ

Project Number
695-21-700

Building Number
70

Drawing Number
70-TD101B

F

E

D

C


B

A



9/2/2025 3:55:59 PM

Autodesk Docs\DCFM East - Milwaukee EHRM (R24)T24_1804375.03_VA Milwaukee C-04

- SHEET NOTES:**
1. REMOVE ALL NETWORK CABLING TO POINTS OF TERMINATION IN ASSOCIATED TELECOM ROOMS. REFER TO FLOOR PLANS AND SHEET T1001 FOR TR ROOM LOCATIONS.
 2. REFER TO ARCHITECTURAL PHASING PLANS FOR WHEN EXISTING CABLING IS ALLOWED TO BE DEMOLISHED.
 3. FOR ALL EXISTING WIRELESS ACCESS POINTS AND SURVEILLANCE CAMERAS, DEVICES SHALL REMAIN. SCOPE OF WORK INCLUDES CABLE REPLACEMENT ONLY. COORDINATE WITH COR FOR ANY DOWNTIME OF DEVICES.
 4. EXISTING LOCATIONS OF WORK AREA, OUTLETS SHOWN ON THIS SHEET MAY NOT NECESSARILY BE IN THE EXACT LOCATION AS IDENTIFIED.

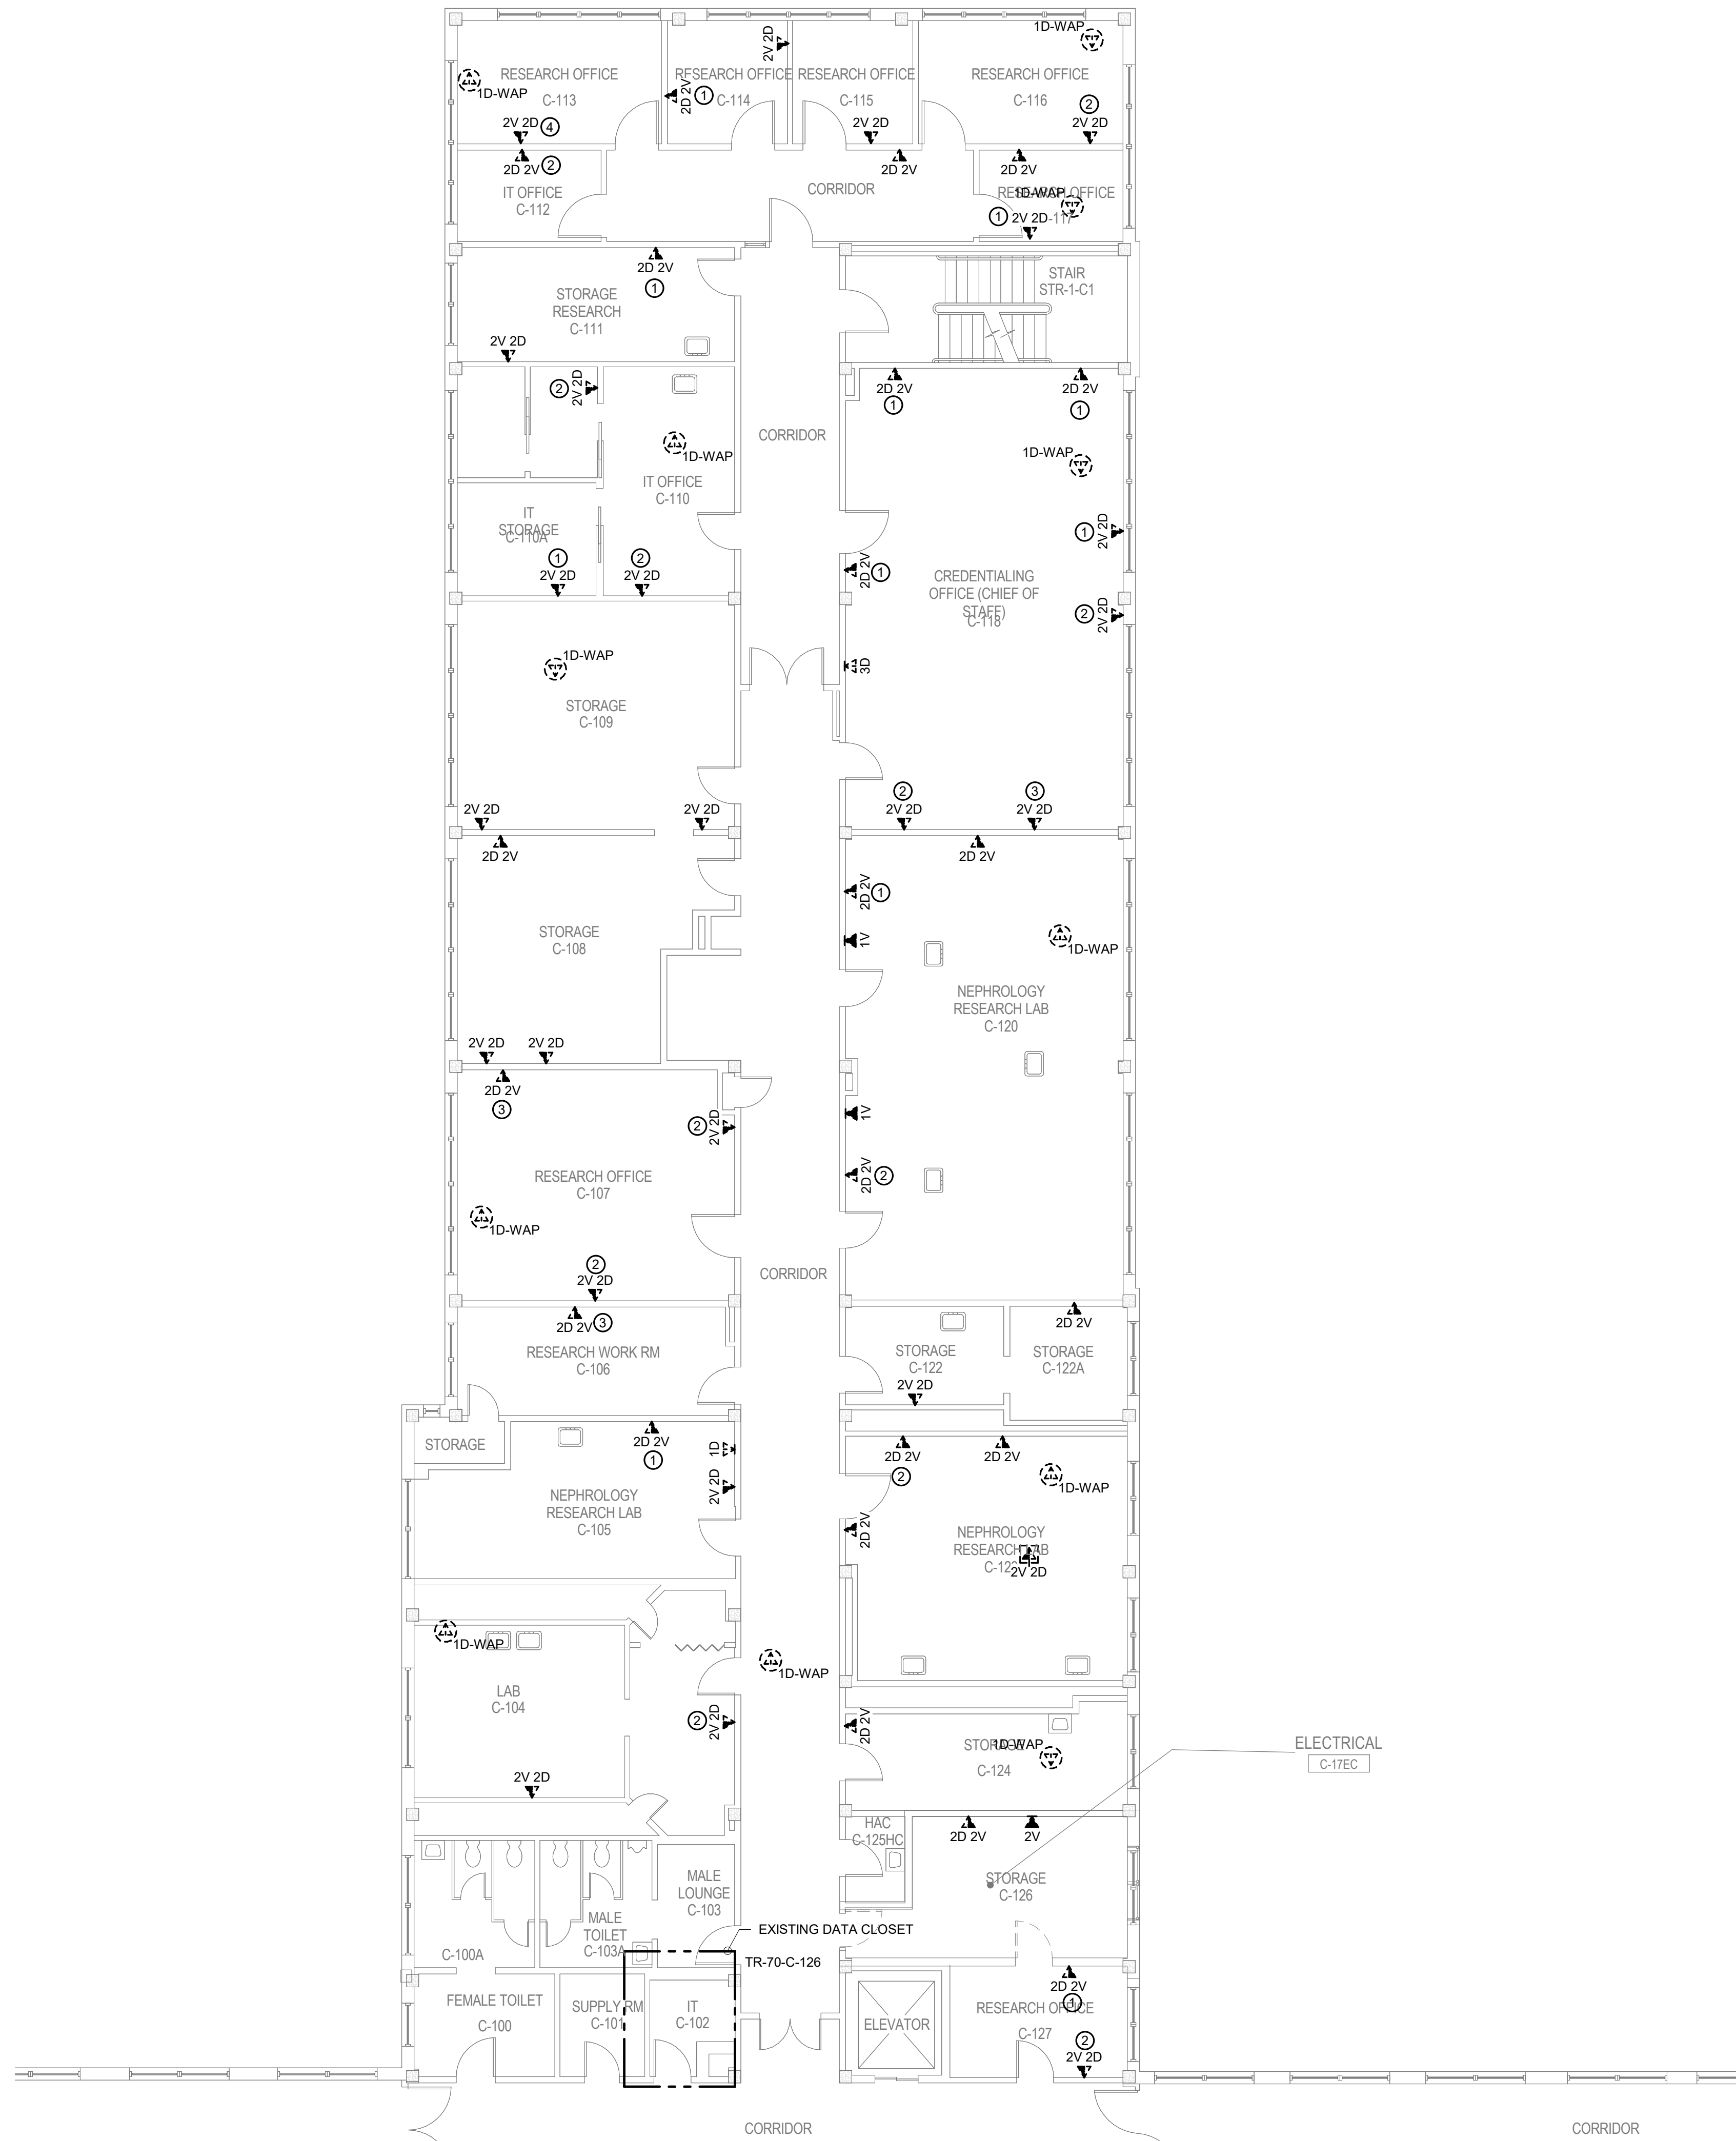

1 BUILDING 70 FIRST FLOOR DEMOLITION PLAN - TECHNOLOGY - AREA C NORTH
1/8" = 1'-0"

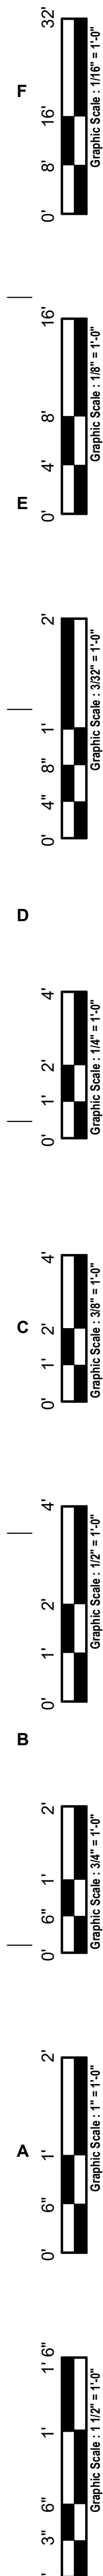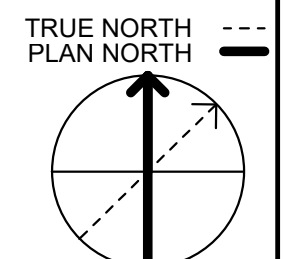

35% SCHEMATIC DESIGN SUBMISSION	5.17.21
65% DESIGN DEVELOPMENT SUBMISSION	6.15.21
65% DESIGN DEVELOPMENT RESUBMISSION	8.25.21
Revisions:	Date:

CONSULTANT

IMEG
The Future is Now
15 SUNNEN DRIVE
SUITE 104
ST. LOUIS, MO 63143
P: 314.645.1132 F: 314.645.1173
PROJECT #18004375.03

ARCHITECT/ENGINEER OF RECORD

Romanyk Consulting
Focusing on what matters
Romanyk Consulting Corp. www.romanykconsulting.com
3308 Preston Road, Suite 350-164, Plano, Texas 75093

STAMP

Bicsi
DAVID LARSON
BICS1 ID # 106098
Expires 12-31-25
RCB

Office of
Construction
and Facilities
Management
VA U.S. Department
of Veterans Affairs

Drawing Title
**BUILDING 70 FIRST FLOOR DEMO PLAN -
TECHNOLOGY - AREA C NORTH**

Approved:

Phase
FINAL BID DOCUMENTS

Sprinklered
FULLY SPRINKLERED

Project Title
**EHRM INFRASTRUCTURE
UPGRADES - MILWAUKEE, WI**

Location
5000 W. NATIONAL AVENUE, MILWAUKEE, WI

Issue Date
SEPTEMBER 05, 2025

Checked
PHINIE

Drawn
MAIBEJ

Project Number
695-21-700

Building Number
70

Drawing Number
70-TD101C-N

F

E


D

C

B


A

9/3/2025 3:55:59 PM
Autodesk Docs\DCFM East - Milwaukee EHRM (R24)T24_1804375.03_VA MilWEHRM_C.rvt

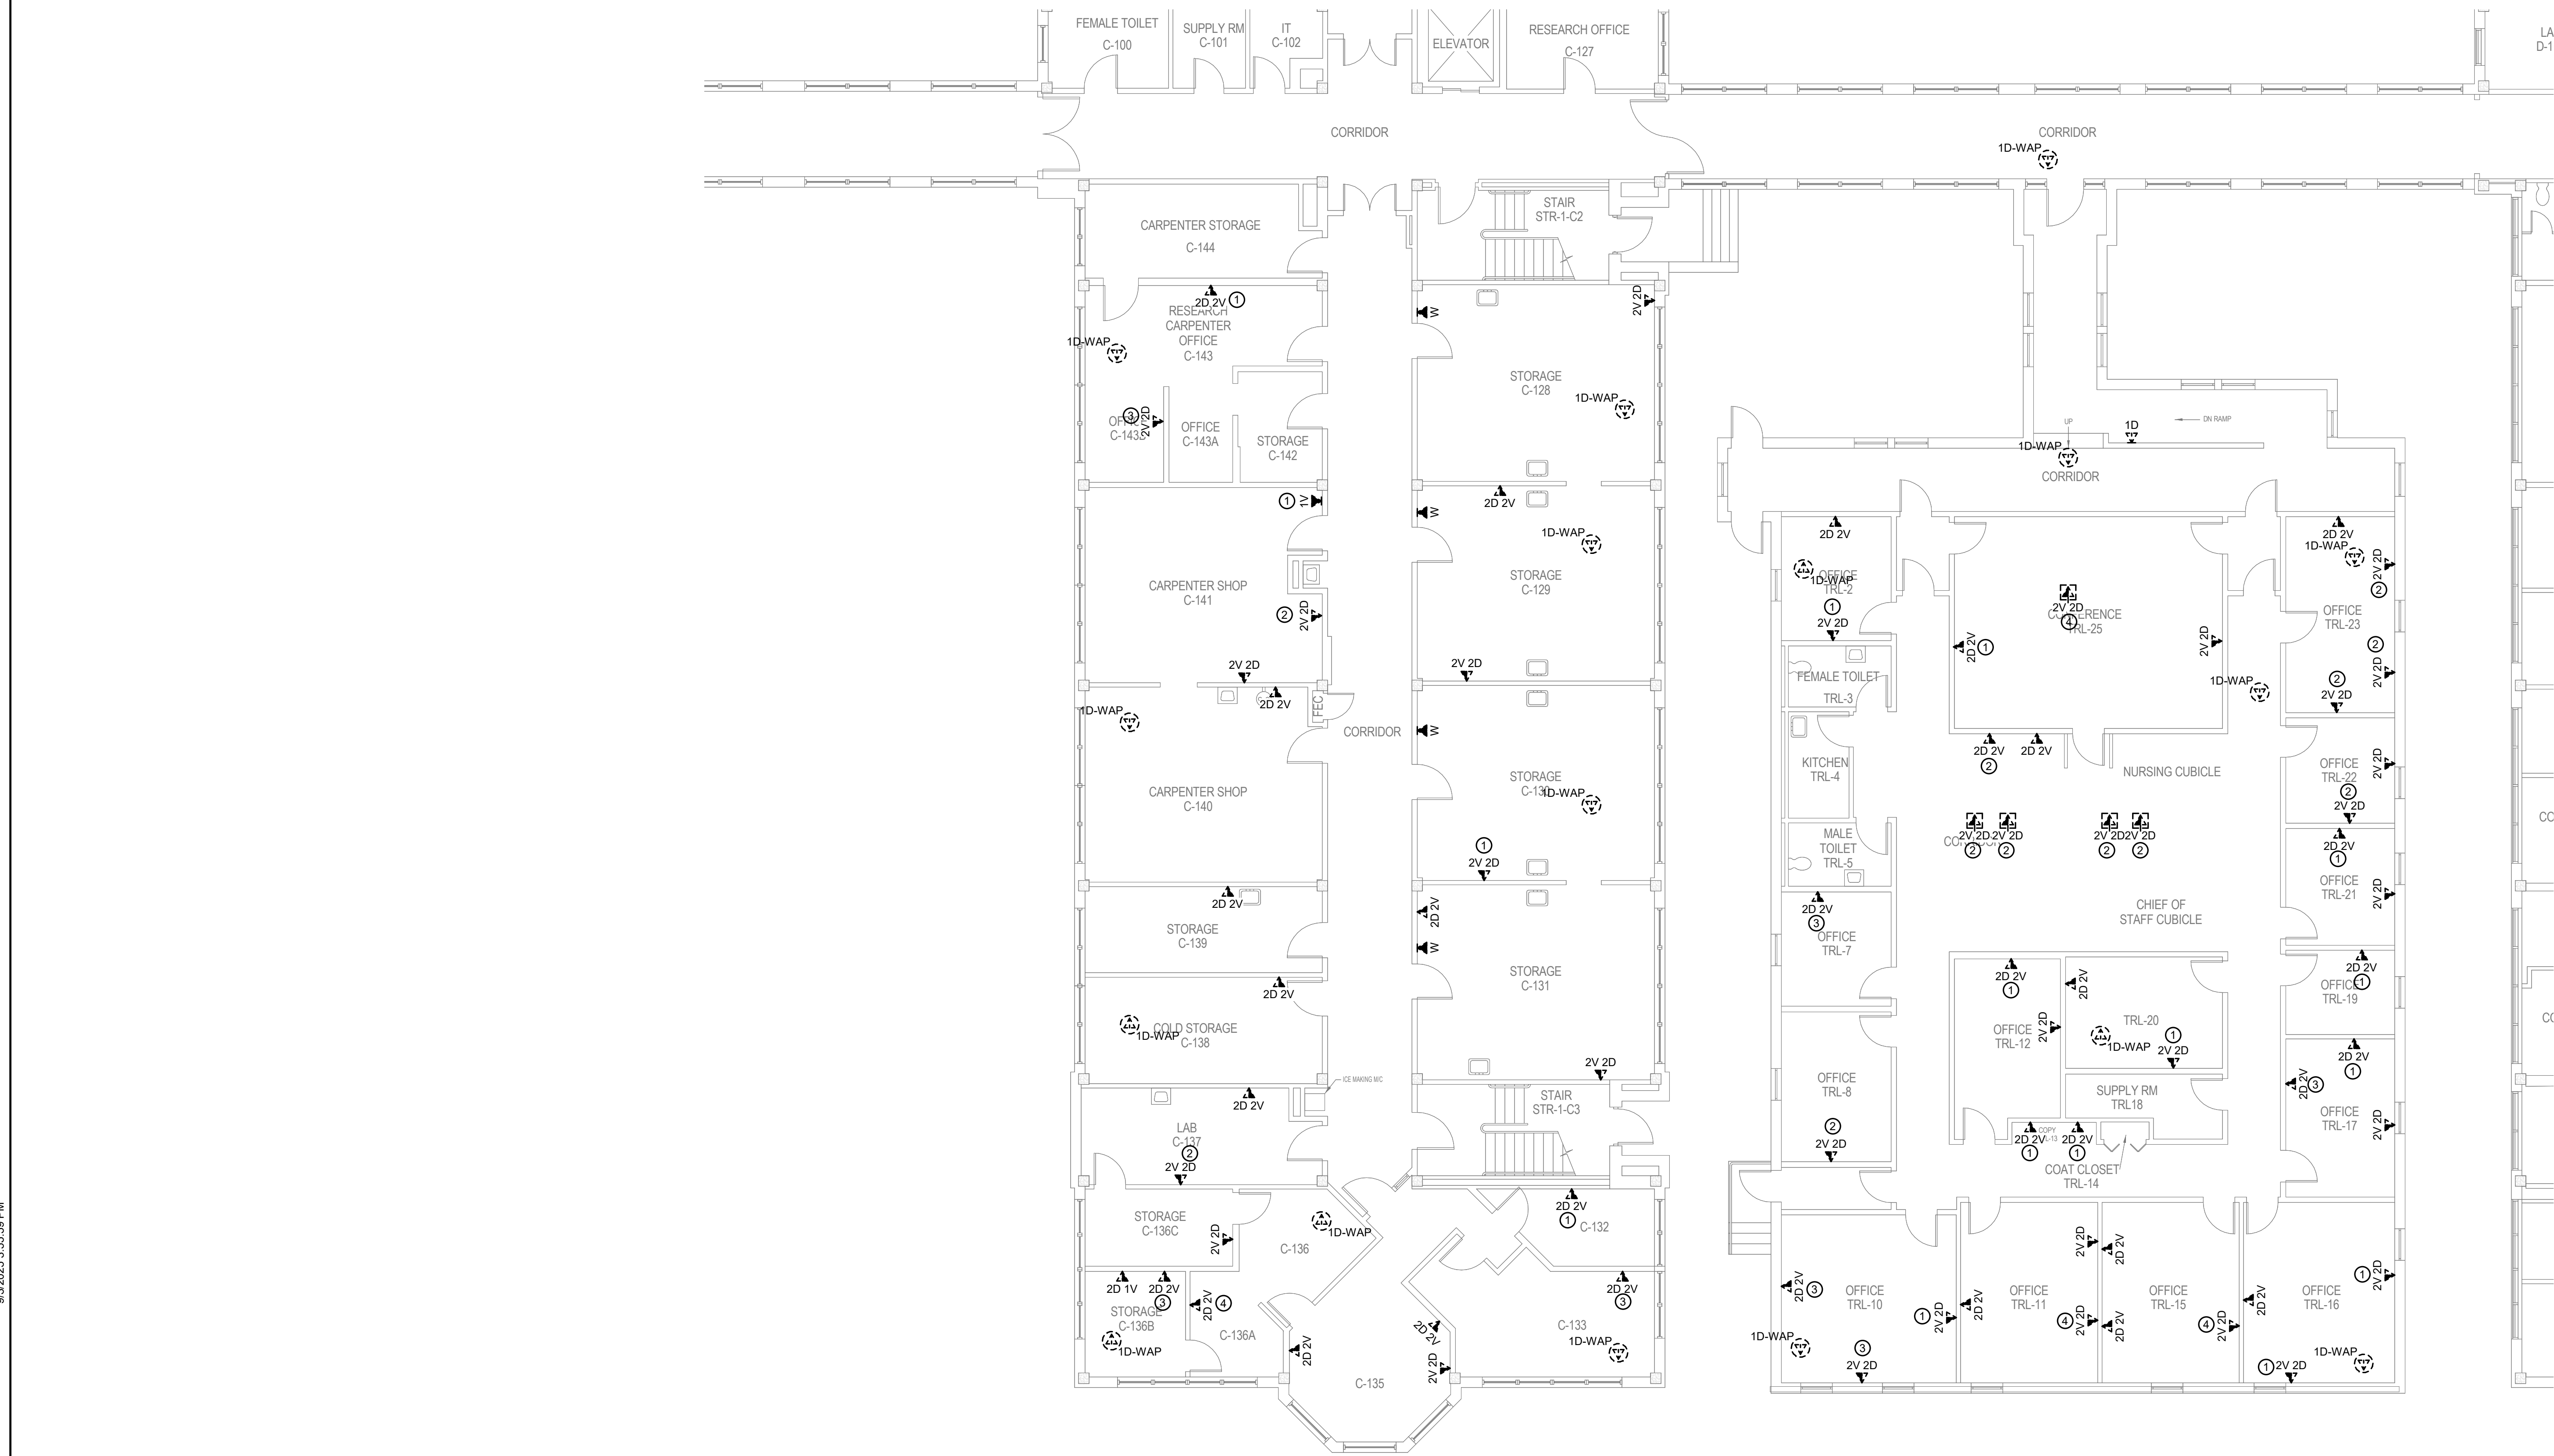

- SHEET NOTES:**
1. REMOVE ALL NETWORK CABLING TO POINTS OF TERMINATION IN ASSOCIATED TELECOM ROOMS. REFER TO FLOOR PLANS AND SHEET T1001 FOR TR ROOM LOCATIONS.
 2. REFER TO ARCHITECTURAL PHASING PLANS FOR WHEN EXISTING CABLING IS ALLOWED TO BE DEMOLISHED.
 3. FOR ALL EXISTING WIRELESS ACCESS POINTS AND SURVEILLANCE CAMERAS, DEVICES SHALL REMAIN. SCOPE OF WORK INCLUDES CABLE REPLACEMENT ONLY. COORDINATE WITH COR FOR ANY DOWNTIME OF DEVICES.
 4. EXISTING LOCATIONS OF WORK AREA, OUTLETS SHOWN ON THIS SHEET MAY NOT NECESSARILY BE IN THE EXACT LOCATION AS IDENTIFIED.

1 BUILDING 70 FIRST FLOOR DEMOLITION PLAN - TECHNOLOGY - AREA C SOUTH
1/8" = 1'-0"

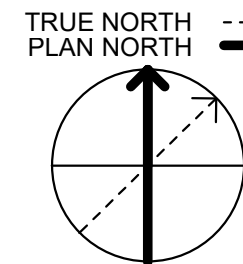

35% SCHEMATIC DESIGN SUBMISSION	5.17.21
65% DESIGN DEVELOPMENT SUBMISSION	6.15.21
65% DESIGN DEVELOPMENT RESUBMISSION	8.25.21
Revisions:	Date:

CONSULTANT

IMEG

15 SUNNEN DRIVE
SUITE 104
ST. LOUIS, MO 63143
P: 314.645.1132 F: 314.645.1173
PROJECT #18004375.03

ARCHITECT/ENGINEER OF RECORD

Romanyk Consulting
Focusing on what matters

Romanyk Consulting Corp. www.romanykconsulting.com
3308 Preston Road, Suite 350-164, Plano, Texas 75093

STAMP

Bicsi
DAVID LARSON
BICS1 ID # 106098
EXPIRES 12-31-25

Office of
Construction
and Facilities
Management

VA U.S. Department
of Veterans Affairs

Drawing Title
**BUILDING 70 FIRST FLOOR DEMO PLAN -
TECHNOLOGY - AREA C SOUTH**

Approved:

Phase
FINAL BID DOCUMENTS

Sprinklered
FULLY SPRINKLERED

Project Title
**EHRM INFRASTRUCTURE
UPGRADES - MILWAUKEE, WI**

Location
5000 W. NATIONAL AVENUE, MILWAUKEE, WI

Issue Date
SEPTEMBER 05, 2025

Checked
PHINIE


Drawn
MAIBEJ

Project Number
695-21-700

Building Number
70

Drawing Number
70-TD101C-S

1. REMOVE ALL NETWORK CABLING TO POINTS OF TERMINATION IN ASSOCIATED TELECOM ROOMS. REFER TO FLOOR PLANS AND SHEET T1001 FOR TR ROOM LOCATIONS.
2. REFER TO ARCHITECTURAL PHASING PLANS FOR WHEN EXISTING CABLING IS ALLOWED TO BE DEMOLISHED.
3. FOR ALL EXISTING WIRELESS ACCESS POINTS AND SURVEILLANCE CAMERAS, DEVICES SHALL REMAIN. SCOPE OF WORK INCLUDES CABLE REPLACEMENT ONLY. COORDINATE WITH COR FOR ANY DOWNTIME OF DEVICES.
4. EXISTING LOCATIONS OF WORK AREA OUTLETS SHOWN ON THIS SHEET MAY NOT NECESSARILY BE IN THE EXACT LOCATION AS IDENTIFIED.

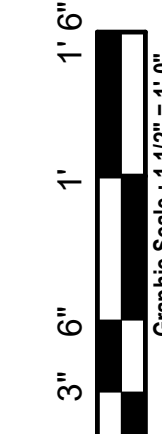**F**

F

E

D

C


B

A


9/20/2025 3:56:04 PM

Autodesk Docs\DCFM East - Milwaukee EHRM (R24)T24_1804375.03_VA Milwaukee_C.dwt

- SHEET NOTES:**
1. REMOVE ALL NETWORK CABLING TO POINTS OF TERMINATION IN ASSOCIATED TELECOM ROOMS. REFER TO FLOOR PLANS AND SHEET T1001 FOR TR ROOM LOCATIONS.
 2. REFER TO ARCHITECTURAL PHASING PLANS FOR WHEN EXISTING CABLING IS ALLOWED TO BE DEMOLISHED.
 3. FOR ALL EXISTING WIRELESS ACCESS POINTS AND SURVEILLANCE CAMERAS, DEVICES SHALL REMAIN. SCOPE OF WORK INCLUDES CABLE REPLACEMENT ONLY. COORDINATE WITH COR FOR ANY DOWNTIME OF DEVICES.
 4. EXISTING LOCATIONS OF WORK AREA, OUTLETS SHOWN ON THIS SHEET MAY NOT NECESSARILY BE IN THE EXACT LOCATION AS IDENTIFIED.

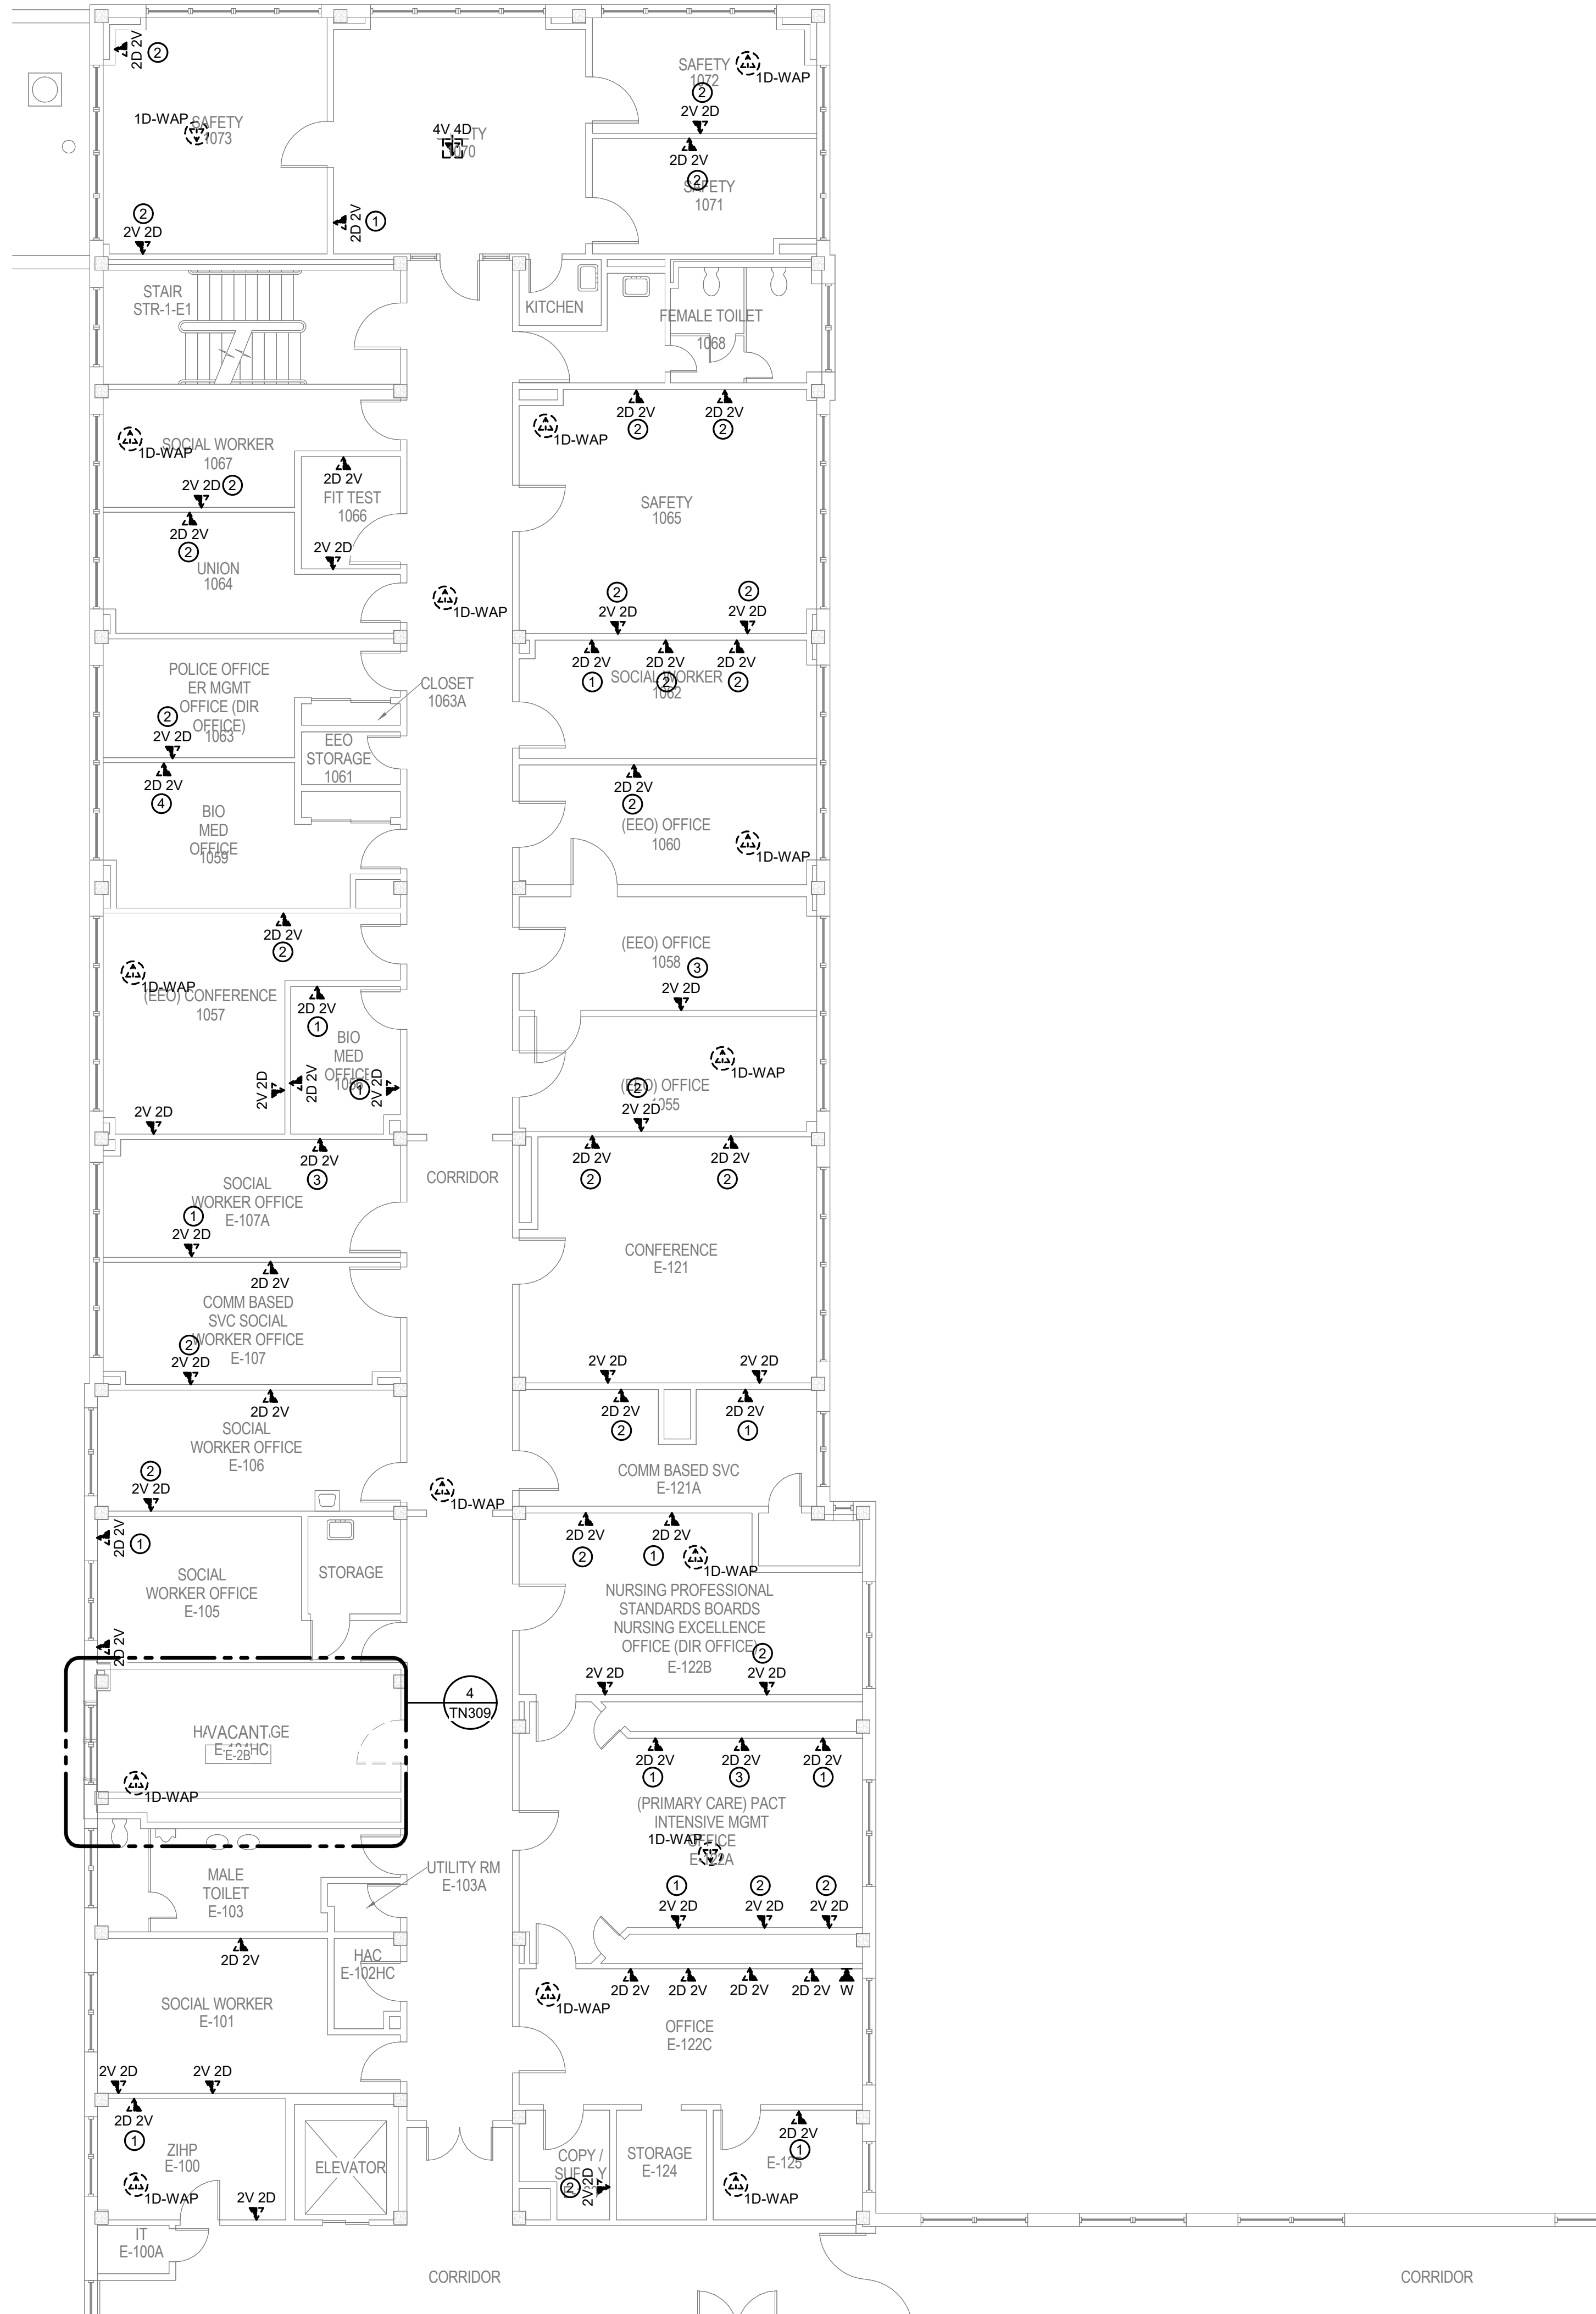

1 BUILDING 70 FIRST FLOOR DEMOLITION PLAN - TECHNOLOGY - AREA E NORTH
1/8" = 1'-0"

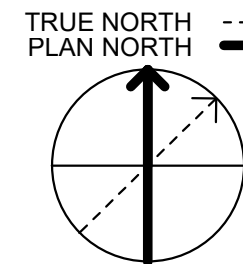

35% SCHEMATIC DESIGN SUBMISSION	5.17.21
65% DESIGN DEVELOPMENT SUBMISSION	6.15.21
65% DESIGN DEVELOPMENT RESUBMISSION	8.25.21
Revisions:	Date:

CONSULTANT

IMEG
15 SUNNEN DRIVE
SUITE 104
ST. LOUIS, MO 63143
P: 314.645.1132 F: 314.645.1173
PROJECT #18004375.03

ARCHITECT/ENGINEER OF RECORD

Romanyk Consulting
Focusing on what matters
Romanyk Consulting Corp. www.romanykconsulting.com
3308 Preston Road, Suite 350-164, Plano, Texas 75093

STAMP

Bicsi
DAVID LARSON
BICS1 ID # 106098
Expires 12-31-25
RCDD

Office of
Construction
and Facilities
Management
VA U.S. Department
of Veterans Affairs

Drawing Title
BUILDING 70 FIRST FLOOR DEMO PLAN -
TECHNOLOGY - AREA E NORTH

Approved:

Phase
FINAL BID DOCUMENTS

Sprinklered
FULLY SPRINKLERED

Project Title
EHRM INFRASTRUCTURE
UPGRADES - MILWAUKEE, WI

Location
5000 W. NATIONAL AVENUE, MILWAUKEE, WI

Issue Date
SEPTEMBER 05, 2025

Checked
PHINIE

Drawn
MAIBEJ

Project Number
695-21-700

Building Number
70

Drawing Number
70-TD101E-N

F

E

D

C


B

A


9/3/2025 3:56:06 PM

Autodesk Docs\DCRM East - Milwaukee EHRM (R24)T24_1804375.03_VA Milwaukee C.d

- SHEET NOTES:**
1. REMOVE ALL NETWORK CABLING TO POINTS OF TERMINATION IN ASSOCIATED TELECOM ROOMS. REFER TO FLOOR PLANS AND SHEET T1001 FOR TR ROOM LOCATIONS.
 2. REFER TO ARCHITECTURAL PHASING PLANS FOR WHEN EXISTING CABLING IS ALLOWED TO BE DEMOLISHED.
 3. FOR ALL EXISTING WIRELESS ACCESS POINTS AND SURVEILLANCE CAMERAS, DEVICES SHALL REMAIN. SCOPE OF WORK INCLUDES CABLE REPLACEMENT ONLY. COORDINATE WITH COR FOR ANY DOWNTIME OF DEVICES.
 4. EXISTING LOCATIONS OF WORK AREA, OUTLETS SHOWN ON THIS SHEET MAY NOT NECESSARILY BE IN THE EXACT LOCATION AS IDENTIFIED.

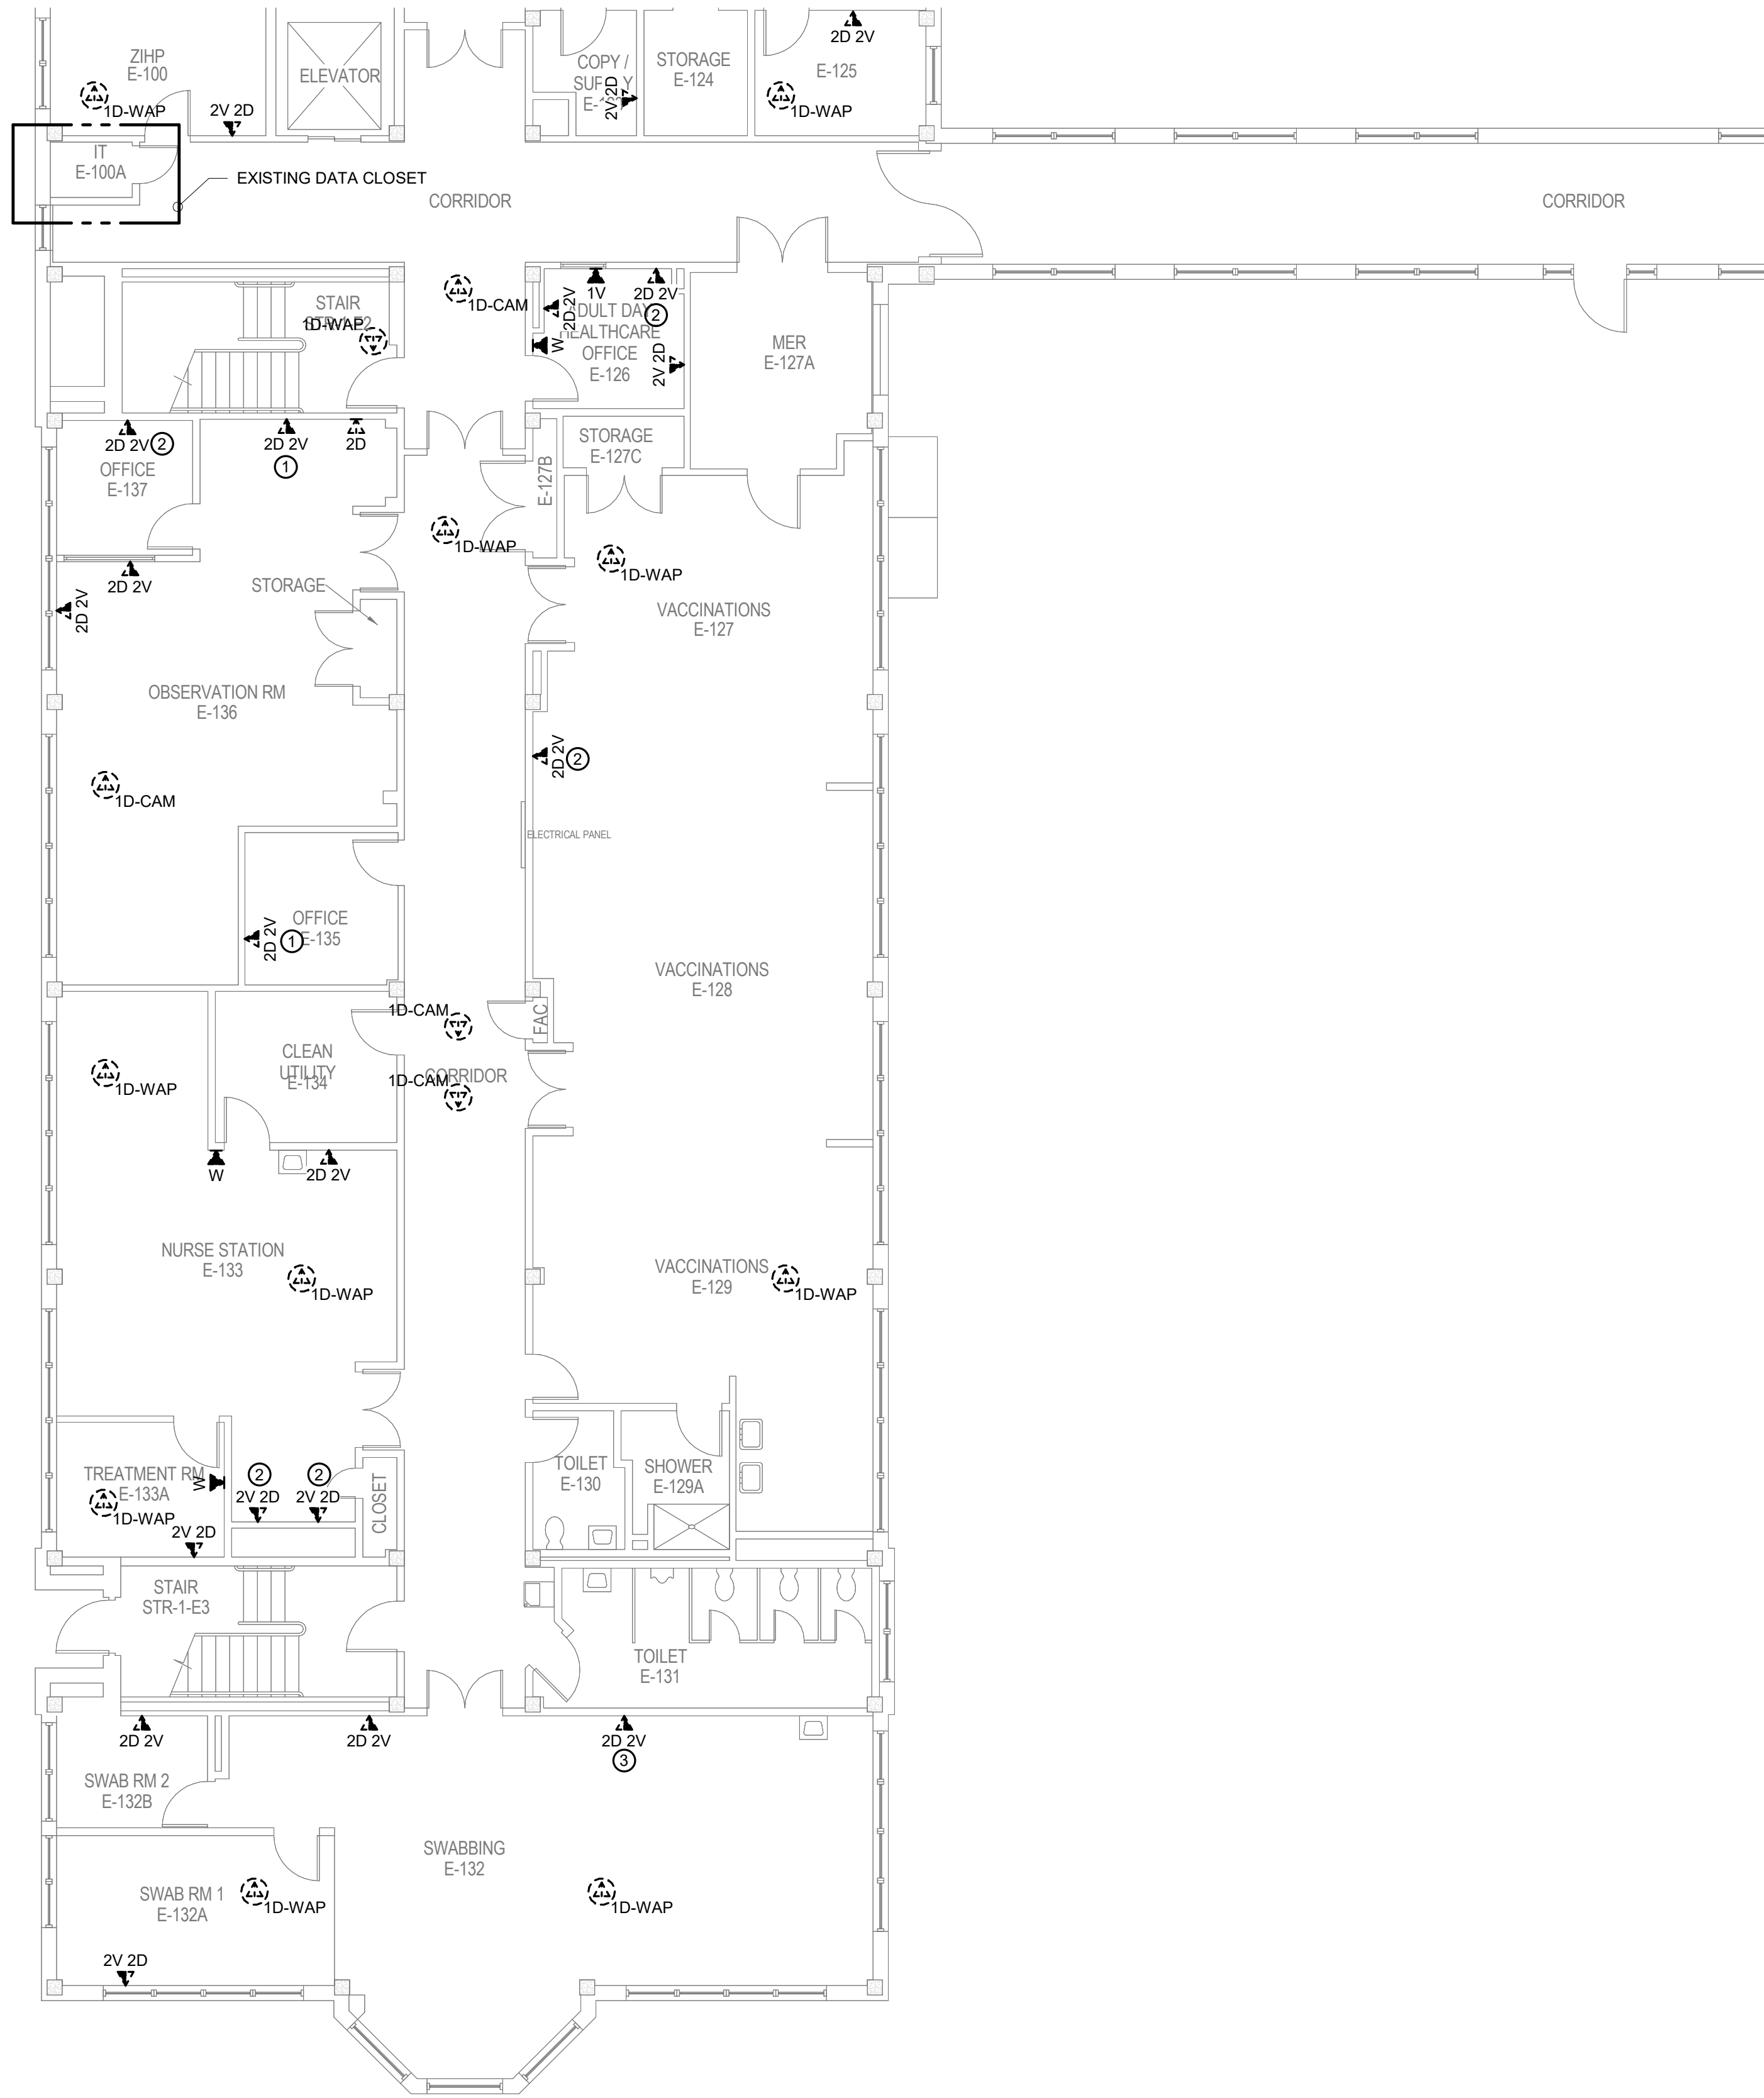

1 BUILDING 70 FIRST FLOOR DEMOLITION PLAN - TECHNOLOGY - AREA E SOUTH
1/8" = 1'-0"

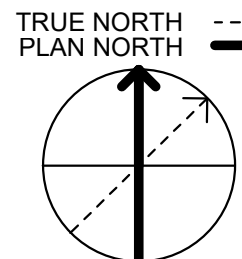

35% SCHEMATIC DESIGN SUBMISSION	5.17.21
65% DESIGN DEVELOPMENT SUBMISSION	6.15.21
65% DESIGN DEVELOPMENT RESUBMISSION	8.25.21
Revisions:	Date:

CONSULTANT

IMEG
15 SUNNEN DRIVE
SUITE 104
ST. LOUIS, MO 63143
P: 314.645.1132 F: 314.645.1173
PROJECT #18004375.03

ARCHITECT/ENGINEER OF RECORD

Romanyk Consulting
Focusing on what matters
Romanyk Consulting Corp. www.romanykconsulting.com
3308 Preston Road, Suite 350-164, Plano, Texas 75093

STAMP

Bicsi
DAVID LARSON
BICS1 ID # 106098
EXPIRES 12-31-25
REGISTERED COMMUNICATIONS DISTRIBUTION DESIGNER

Office of
Construction
and Facilities
Management

VA U.S. Department
of Veterans Affairs

Drawing Title
BUILDING 70 FIRST FLOOR DEMO PLAN -
TECHNOLOGY - AREA E SOUTH

Approved:

Phase
FINAL BID DOCUMENTS

Sprinklered
FULLY SPRINKLERED

Project Title
EHRM INFRASTRUCTURE
UPGRADES - MILWAUKEE, WI

Location
5000 W. NATIONAL AVENUE, MILWAUKEE, WI

Issue Date
SEPTEMBER 05, 2025

Checked
PHINIE

Drawn
MAIBEJ

Project Number
695-21-700


Building Number
70

Drawing Number
70-TD101E-S

- SHEET NOTES:
1. REMOVE ALL NETWORK CABLING TO POINTS OF TERMINATION IN ASSOCIATED TELECOM ROOMS. REFER TO FLOOR PLANS AND SHEET T1001 FOR TR ROOM LOCATIONS.

2. REFER TO ARCHITECTURAL PHASING PLANS FOR WHEN EXISTING CABLING IS ALLOWED TO BE DEMOLISHED.


3. FOR ALL EXISTING WIRELESS ACCESS POINTS AND SURVEILLANCE CAMERAS, DEVICES SHALL REMAIN. SCOPE OF WORK INCLUDES CABLE REPLACEMENT ONLY. COORDINATE WITH COR FOR ANY DOWNTIME OF DEVICES. EXISTING LOCATIONS OF WORK AREA, OUTLETS SHOWN ON THIS SHEET MAY NOT NECESSARILY BE IN THE EXACT LOCATION AS IDENTIFIED.

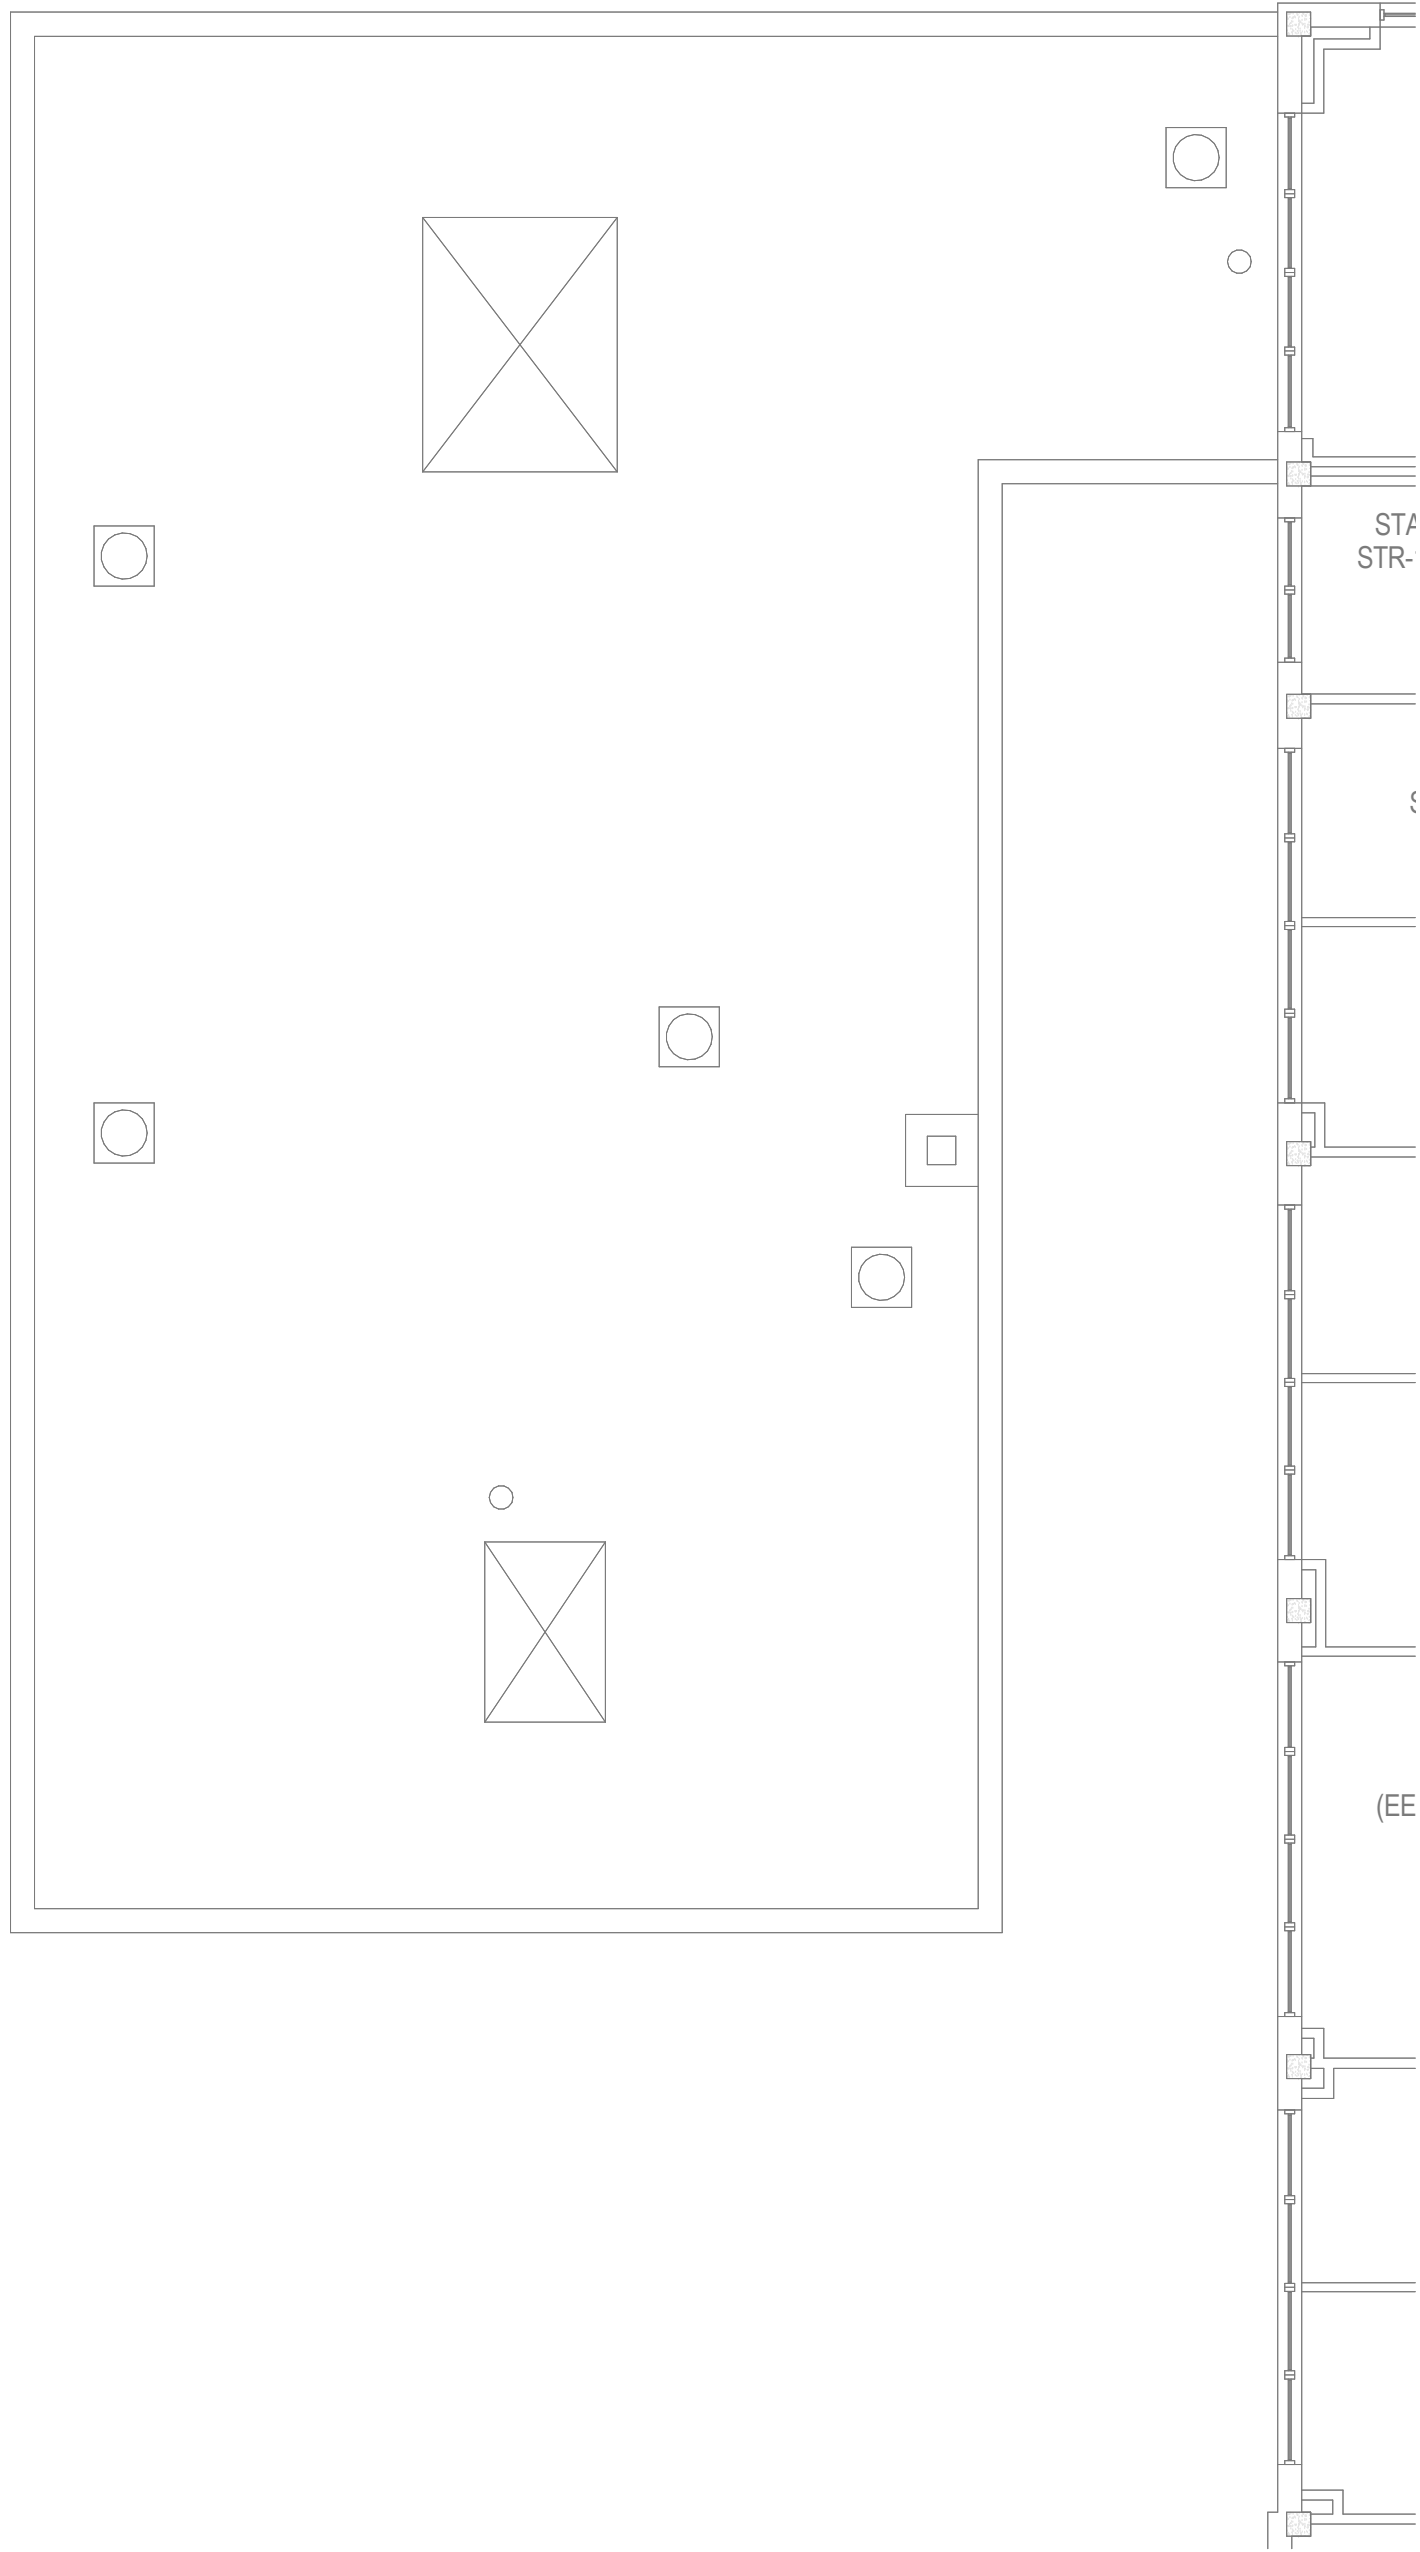

1

BUILDING 70 FIRST FLOOR DEMOLITION PLAN - TECHNOLOGY - AREA K

1/8" = 1'-0"

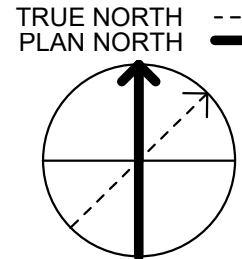

35% SCHEMATIC DESIGN SUBMISSION	5.17.21
65% DESIGN DEVELOPMENT SUBMISSION	6.15.21
65% DESIGN DEVELOPMENT RESUBMISSION	8.25.21
Revisions:	Date:

CONSULTANT



The IMEG Group of Companieswww.imegcorp.com

15 SUNNEN DRIVE

SUITE 104

ST. LOUIS, MO 63143

P: 314.645.1132 F: 314.645.1173

PROJECT #18004375.03

ARCHITECT/ENGINEER OF RECORD



Romanyk Consulting

Focusing on what matters

Romanyk Consulting Corp. www.romanykconsulting.com

3308 Preston Road, Suite 350-164, Plano, Texas 75093

STAMP



Office of
Construction
and Facilities
Management

 U.S. Department
of Veterans Affairs

Drawing Title
BUILDING 70 FIRST FLOOR DEMO PLAN -
TECHNOLOGY - AREA K

Approved:

Phase
FINAL BID DOCUMENTS

Sprinklered
FULLY SPRINKLERED

Project Title
EHRM INFRASTRUCTURE
UPGRADES - MILWAUKEE, WI

Location
5000 W. NATIONAL AVENUE, MILWAUKEE, WI

Issue Date
SEPTEMBER 05, 2025

Checked
PHINIE

Drawn
MAIBEJ

Project Number
695-21-700

Building Number
70

Drawing Number
70-TD101K

F

E

D

C


B

A


9/3/2025 3:56:08 PM

Autodesk Docs\DCFM East - Milwaukee EHRM (R24)T24_1804375.03_VA MilWEHRM_C.dwg

- SHEET NOTES:**
1. REMOVE ALL NETWORK CABLING TO POINTS OF TERMINATION IN ASSOCIATED TELECOM ROOMS. REFER TO FLOOR PLANS AND SHEET T1001 FOR TR ROOM LOCATIONS.
 2. REFER TO ARCHITECTURAL PHASING PLANS FOR WHEN EXISTING CABLING IS ALLOWED TO BE DEMOLISHED.
 3. FOR ALL EXISTING WIRELESS ACCESS POINTS AND SURVEILLANCE CAMERAS, DEVICES SHALL REMAIN. SCOPE OF WORK INCLUDES CABLE REPLACEMENT ONLY. COORDINATE WITH COR FOR ANY DOWNTIME OF DEVICES.
 4. EXISTING LOCATIONS OF WORK AREA, OUTLETS SHOWN ON THIS SHEET MAY NOT NECESSARILY BE IN THE EXACT LOCATION AS IDENTIFIED.

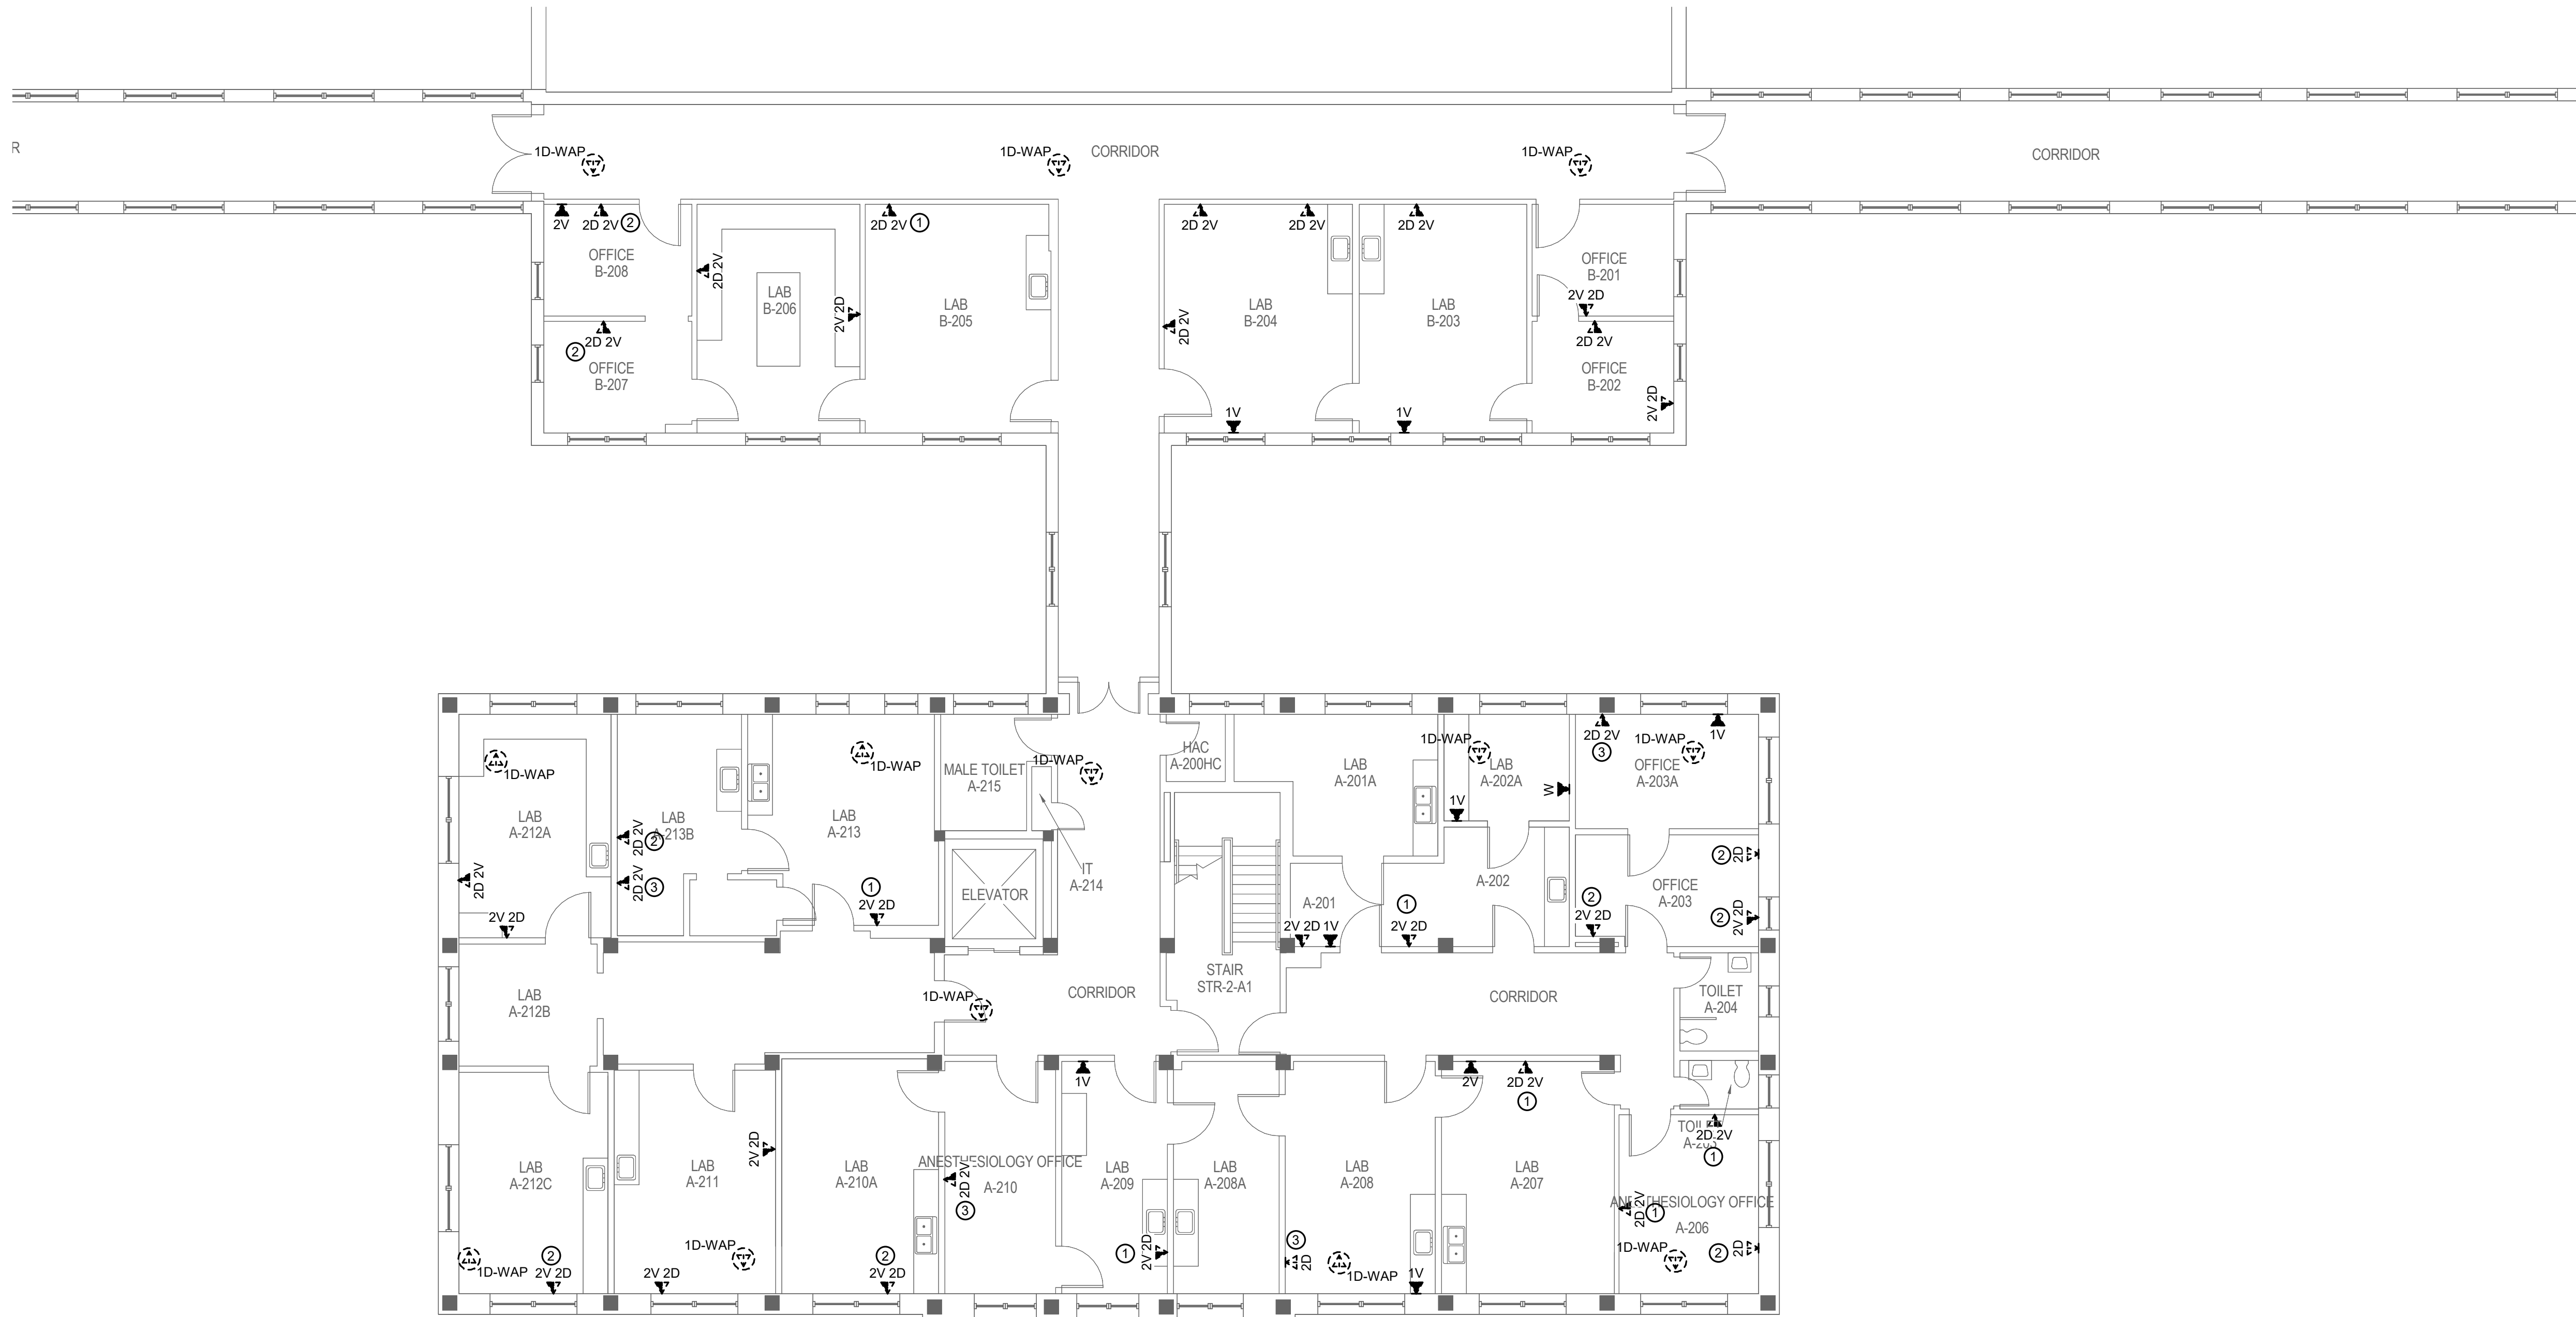

1 BUILDING 70 SECOND FLOOR DEMOLITION PLAN - TECHNOLOGY - AREA A
1/8" = 1'-0"

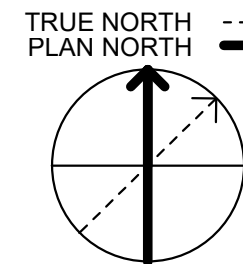

35% SCHEMATIC DESIGN SUBMISSION	5.17.21
65% DESIGN DEVELOPMENT SUBMISSION	6.15.21
65% DESIGN DEVELOPMENT RESUBMISSION	8.25.21
Revisions:	Date:

CONSULTANT

IMEG
15 SUNNEN DRIVE
SUITE 104
ST. LOUIS, MO 63143
P: 314.645.1132 F: 314.645.1173
PROJECT #18004375.03

ARCHITECT/ENGINEER OF RECORD

Romanyk Consulting
Focusing on what matters
Romanyk Consulting Corp. www.romanykconsulting.com
3308 Preston Road, Suite 350-164, Plano, Texas 75093

STAMP

Bicsi
DAVID LARSON
BICS1 ID # 106098
EXPIRES 12-31-25
REGISTERED COMMUNICATIONS DISTRIBUTION DESIGNER

Office of
Construction
and Facilities
Management

VA U.S. Department
of Veterans Affairs

Drawing Title
BUILDING 70 SECOND FLOOR DEMO PLAN -
TECHNOLOGY - AREA A

Approved:

Phase
FINAL BID DOCUMENTS

Sprinklered
FULLY SPRINKLERED

Project Title
EHRM INFRASTRUCTURE
UPGRADES - MILWAUKEE, WI

Location
5000 W. NATIONAL AVENUE, MILWAUKEE, WI

Issue Date
SEPTEMBER 05, 2025

Checked
PHINIE

Drawn
MAIBEJ

Project Number
695-21-700

Building Number
70

Drawing Number
70-TD102A



F

E

D

C


B

A


9/3/2025 3:56:09 PM

Autodesk Docs\DCFM East - Milwaukee EHRM (R24)T24_1804375\03_VA MilwEHRM_C.dwg

GENERAL NOTES:
1. NO WORK SHOWN ON THIS SHEET. SHEET SHOWN FOR REFERENCE ONLY.

 

1 ② **BUILDING 70 SECOND FLOOR DEMOLITION PLAN - TECHNOLOGY - AREA B**
1/8" = 1'-0"

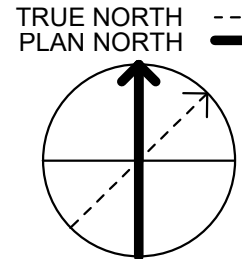

35% SCHEMATIC DESIGN SUBMISSION	5.17.21
65% DESIGN DEVELOPMENT SUBMISSION	6.15.21
65% DESIGN DEVELOPMENT RESUBMISSION	8.25.21
Revisions:	Date:

CONSULTANT



The IMEG Group of Companies
15 SUNNEN DRIVE
SUITE 104
ST. LOUIS, MO 63143
P: 314.645.1132 F: 314.645.1173
PROJECT #18004375.03

ARCHITECT/ENGINEER OF RECORD



Romanyk Consulting
Focusing on what matters
Romanyk Consulting Corp. www.romanykconsulting.com
3308 Preston Road, Suite 350-164, Plano, Texas 75093

STAMP



Office of
Construction
and Facilities
Management

 U.S. Department
of Veterans Affairs

Drawing Title
BUILDING 70 SECOND FLOOR DEMO PLAN -
TECHNOLOGY - AREA B

Approved:

Phase
FINAL BID DOCUMENTS

Sprinklered
FULLY SPRINKLERED

Project Title
EHRM INFRASTRUCTURE
UPGRADES - MILWAUKEE, WI

Location
5000 W. NATIONAL AVENUE MILWAUKEE, WI

Issue Date
SEPTEMBER 05, 2025


Checked
PHINIE

Drawn
MAIBEJ

Project Number
695-21-700

Building Number
70

Drawing Number
70-TD102B

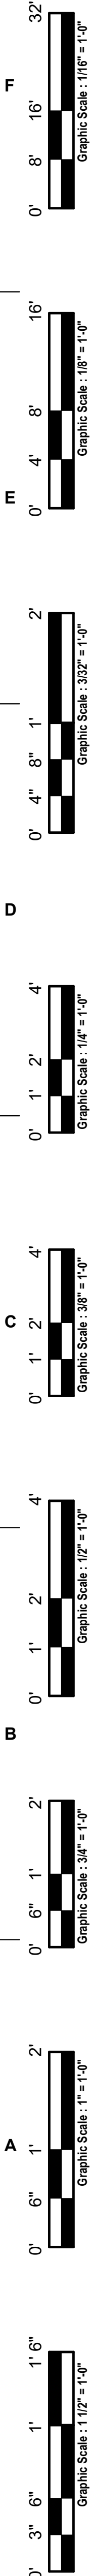

F

E

D

C











B

A


9/3/2025 3:46:10 PM

Autodesk Docs\DCFM East - Milwaukee EHRM (R24)T24_1804375.03_VA MilWEHRM_C.rvt

- SHEET NOTES:**
1. REMOVE ALL NETWORK CABLING TO POINTS OF TERMINATION IN ASSOCIATED TELECOM ROOMS. REFER TO FLOOR PLANS AND SHEET T1001 FOR TR ROOM LOCATIONS.
 2. REFER TO ARCHITECTURAL PHASING PLANS FOR WHEN EXISTING CABLING IS ALLOWED TO BE DEMOLISHED.
 3. FOR ALL EXISTING WIRELESS ACCESS POINTS AND SURVEILLANCE CAMERAS, DEVICES SHALL REMAIN. SCOPE OF WORK INCLUDES CABLE REPLACEMENT ONLY. COORDINATE WITH COR FOR ANY DOWNTIME OF DEVICES.
 4. EXISTING LOCATIONS OF WORK AREA, OUTLETS SHOWN ON THIS SHEET MAY NOT NECESSARILY BE IN THE EXACT LOCATION AS IDENTIFIED.

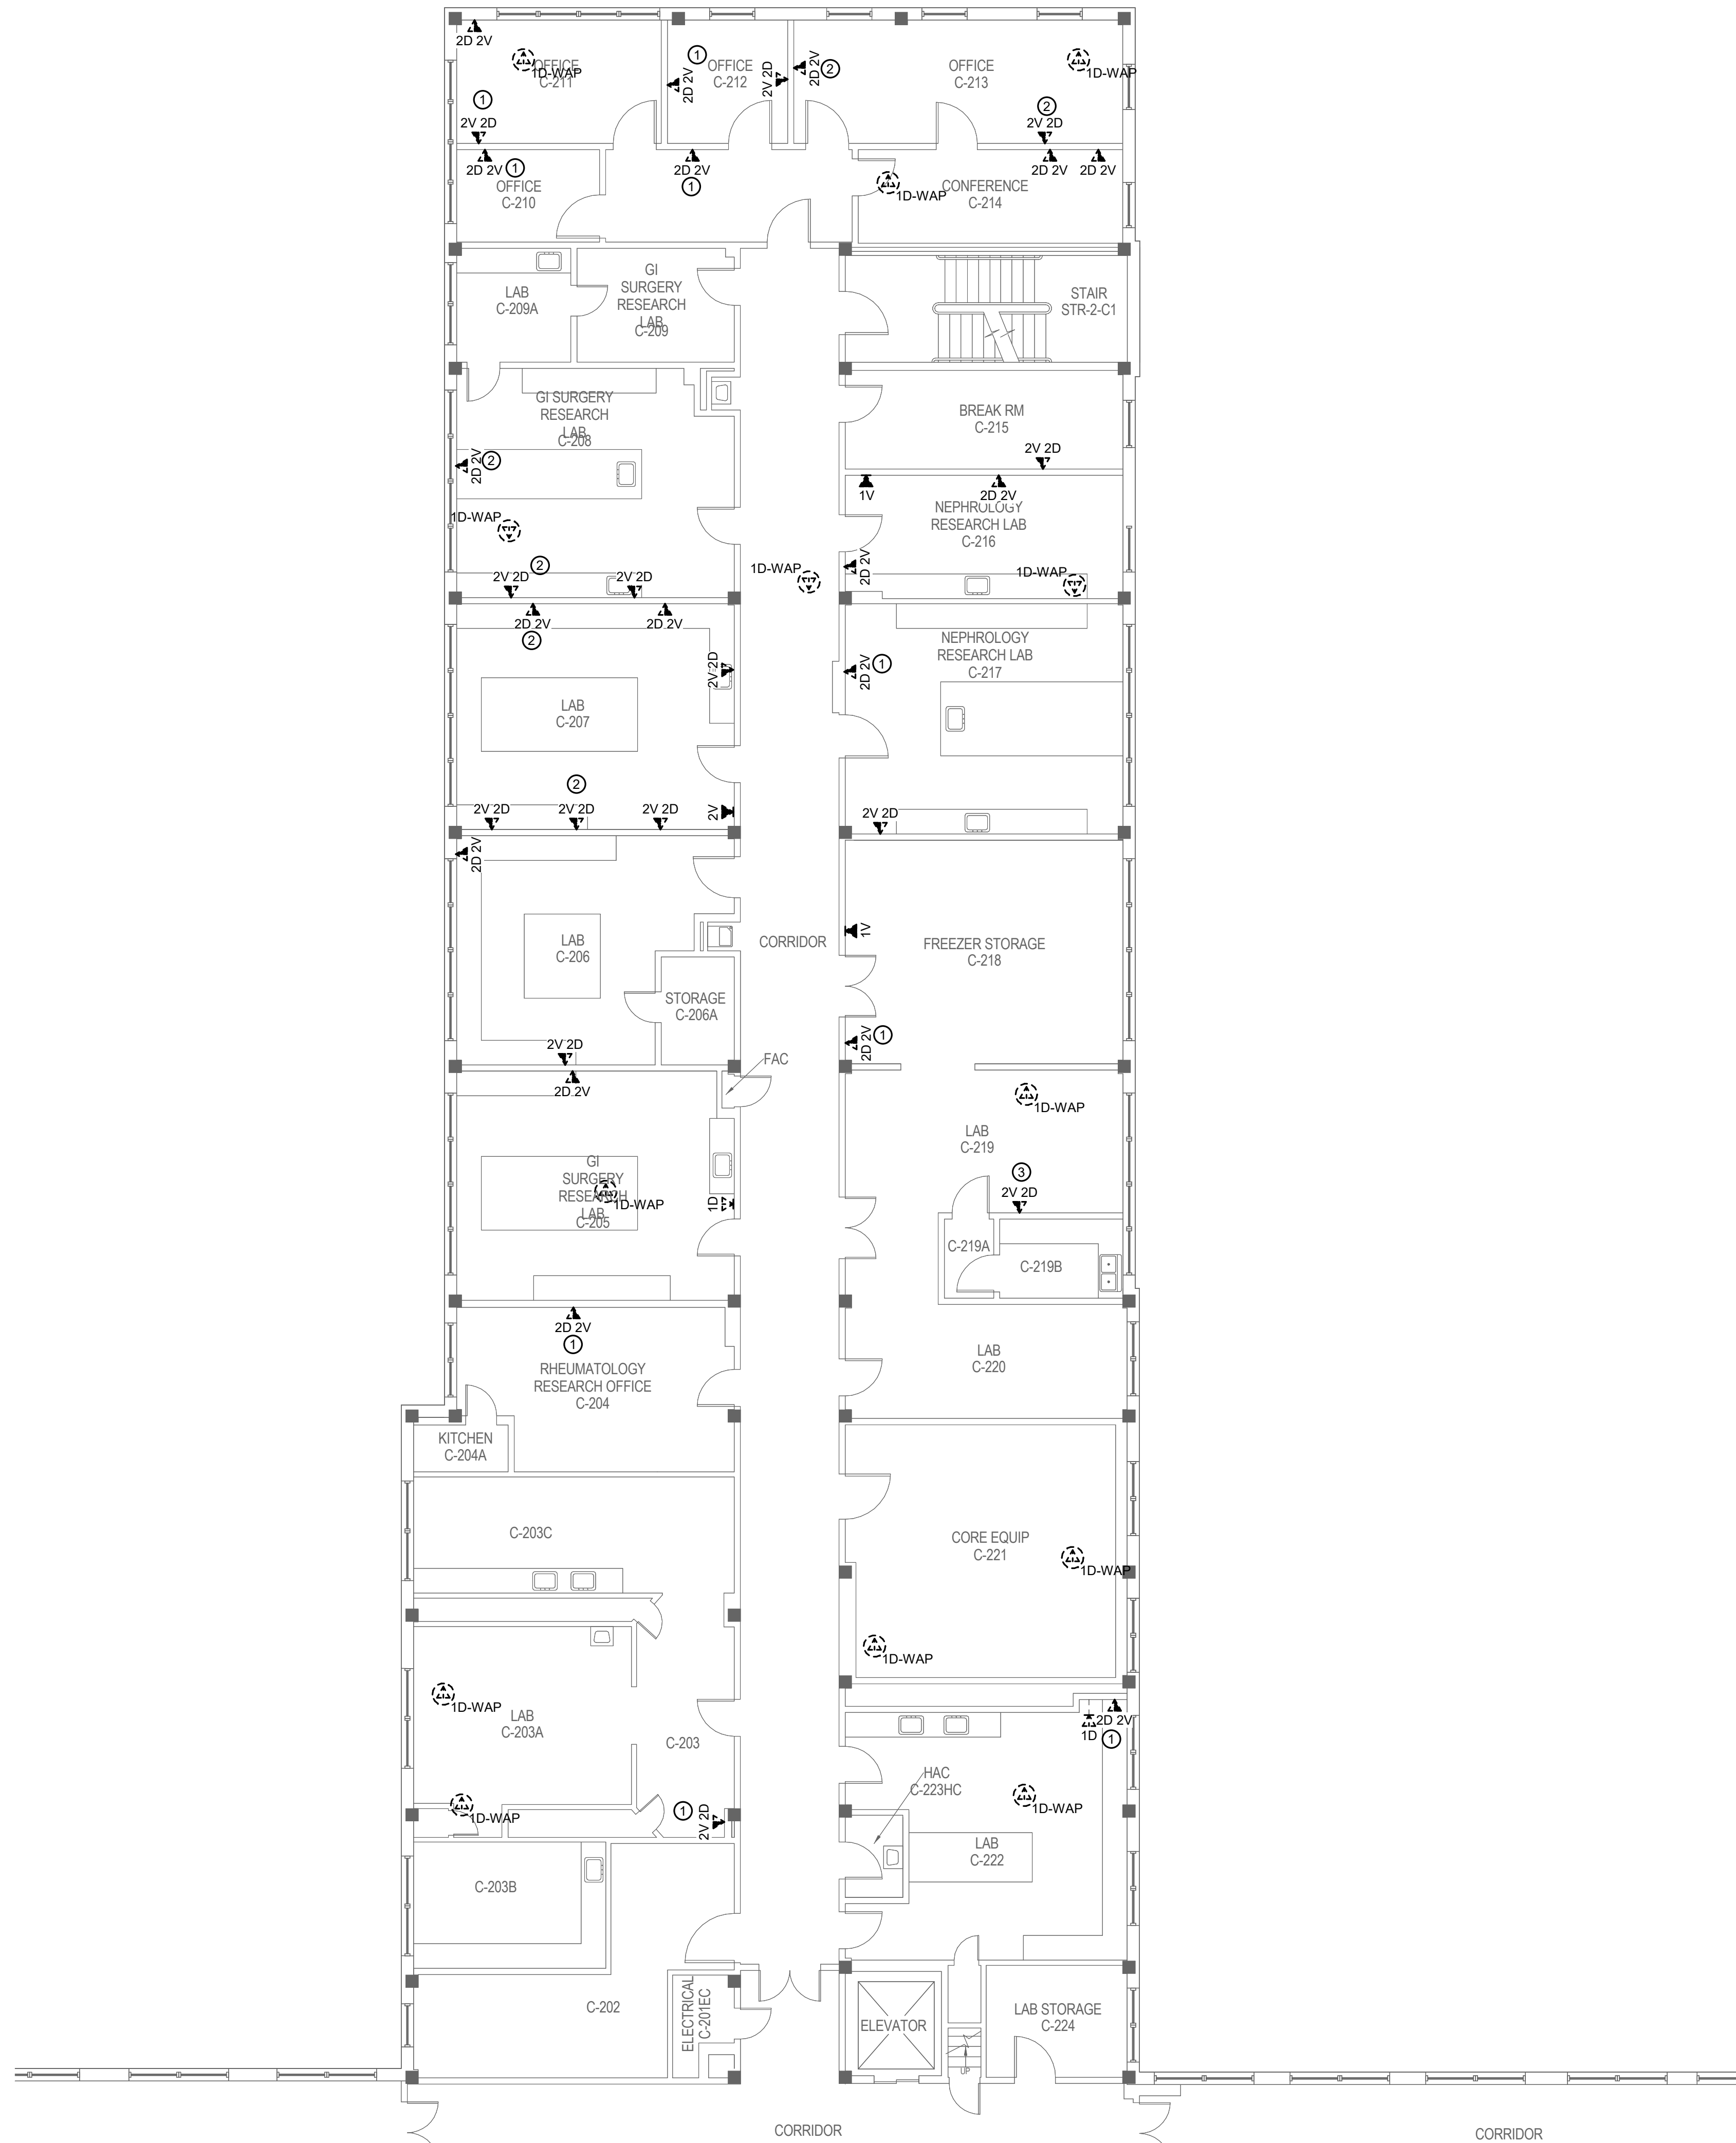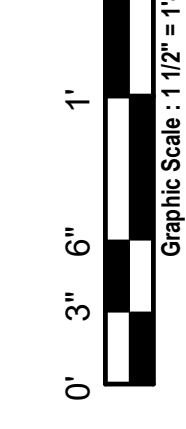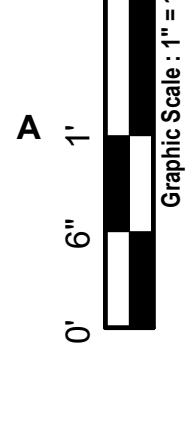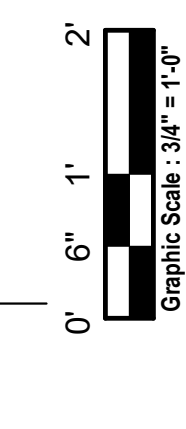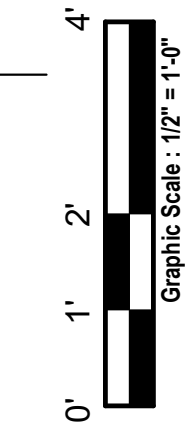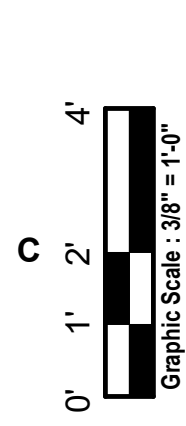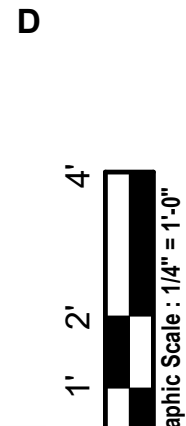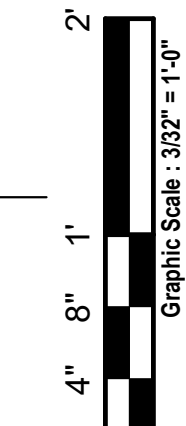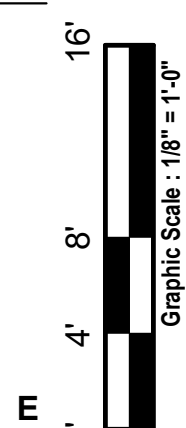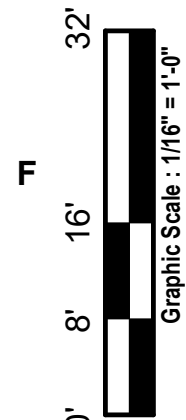

1 BUILDING 70 SECOND FLOOR DEMOLITION PLAN - TECHNOLOGY - AREA C NORTH
1/8" = 1'-0"

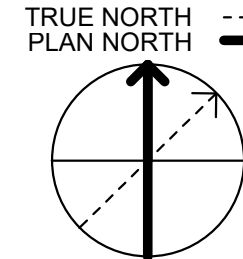

35% SCHEMATIC DESIGN SUBMISSION	5.17.21
65% DESIGN DEVELOPMENT SUBMISSION	6.15.21
65% DESIGN DEVELOPMENT RESUBMISSION	8.25.21
Revisions:	Date:

CONSULTANT

IMEG

15 SUNNEN DRIVE
SUITE 104
ST. LOUIS, MO 63143
P: 314.645.1132 F: 314.645.1173
PROJECT #18004375.03

ARCHITECT/ENGINEER OF RECORD

Romanyk Consulting
Focusing on what matters

Romanyk Consulting Corp. www.romanykconsulting.com
3308 Preston Road, Suite 350-164, Plano, Texas 75093

STAMP

Bicsi
DAVID LARSON
BICS1 ID # 106098
Expires 12-31-25

Office of
Construction
and Facilities
Management

VA U.S. Department
of Veterans Affairs

Drawing Title
BUILDING 70 SECOND FLOOR DEMO PLAN -
TECHNOLOGY - AREA C NORTH

Approved:

Phase
FINAL BID DOCUMENTS

Sprinklered
FULLY SPRINKLERED

Project Title
EHRM INFRASTRUCTURE
UPGRADES - MILWAUKEE, WI

Location
5000 W. NATIONAL AVENUE, MILWAUKEE, WI

Issue Date
SEPTEMBER 05, 2025

Checked
PHINIE

Drawn
MAIBEJ

Project Number
695-21-700

Building Number
70

Drawing Number
70-TD102C-N

1. REMOVE ALL NETWORK CABLING TO POINTS OF TERMINATION IN ASSOCIATED TELECOM ROOMS. REFER TO FLOOR PLANS AND SHEET T1001 FOR TR ROOM LOCATIONS.
2. REFER TO ARCHITECTURAL PHASING PLANS FOR WHEN EXISTING CABLING IS ALLOWED TO BE DEMOLISHED.
3. FOR ALL EXISTING WIRELESS ACCESS POINTS AND SURVEILLANCE CAMERAS, DEVICES SHALL REMAIN. SCOPE OF WORK INCLUDES CABLE REPLACEMENT ONLY. COORDINATE WITH COR FOR ANY DOWNTIME OF DEVICES.
4. EXISTING LOCATIONS OF WORK AREA OUTLETS SHOWN ON THIS SHEET MAY NOT NECESSARILY BE IN THE EXACT LOCATION AS IDENTIFIED.


$$1/8" = 1'-0"$$

Project Number 695-21-700
Building Number 70
Drawing Number 70-TD102C-S

F

E

D


C

B


A

9/2/2025 3:56:13 PM
Autodesk Docs\DCFM East - Milwaukee EHRM (R24)T24_1804375.03_VA MilWHERM_C.dwg

- SHEET NOTES:**
1. REMOVE ALL NETWORK CABLING TO POINTS OF TERMINATION IN ASSOCIATED TELECOM ROOMS. REFER TO FLOOR PLANS AND SHEET T1001 FOR TR ROOM LOCATIONS.
 2. REFER TO ARCHITECTURAL PHASING PLANS FOR WHEN EXISTING CABLING IS ALLOWED TO BE DEMOLISHED.
 3. FOR ALL EXISTING WIRELESS ACCESS POINTS AND SURVEILLANCE CAMERAS, DEVICES SHALL REMAIN. SCOPE OF WORK INCLUDES CABLE REPLACEMENT ONLY. COORDINATE WITH COR FOR ANY DOWNTIME OF DEVICES.
 4. EXISTING LOCATIONS OF WORK AREA, OUTLETS SHOWN ON THIS SHEET MAY NOT NECESSARILY BE IN THE EXACT LOCATION AS IDENTIFIED.

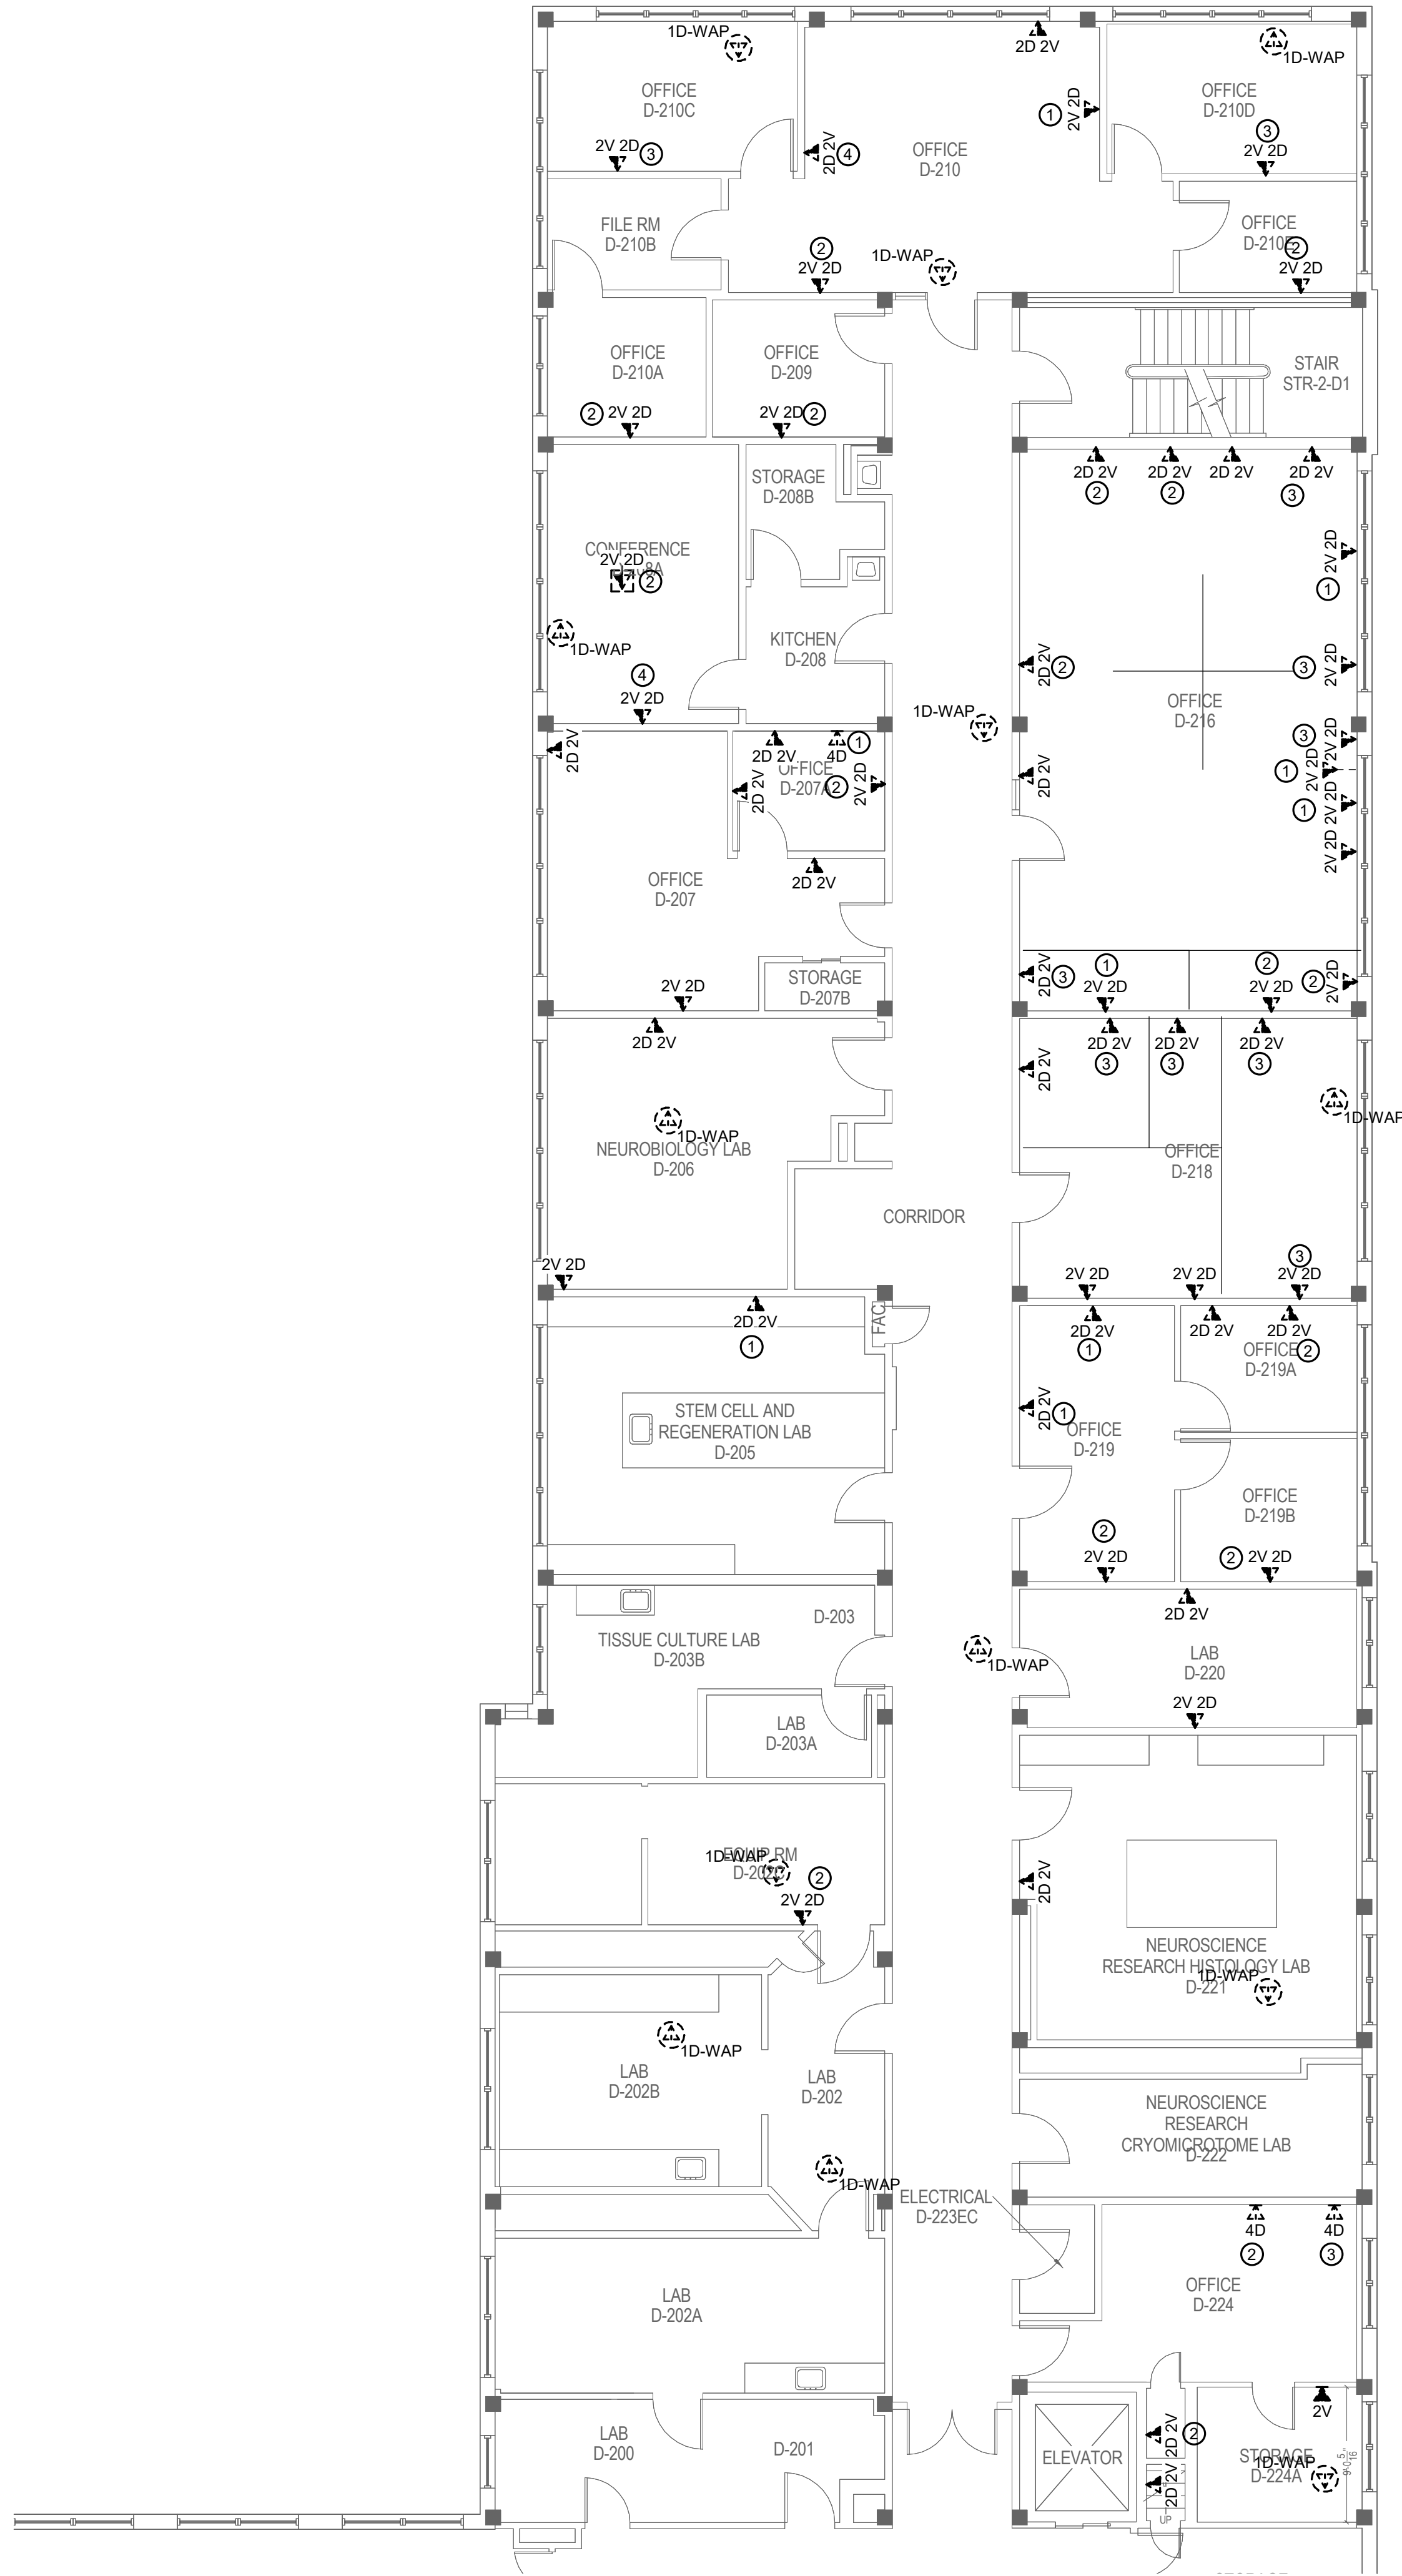

1 BUILDING 70 SECOND FLOOR DEMOLITION PLAN - TECHNOLOGY - AREA D NORTH
1/8" = 1'-0"

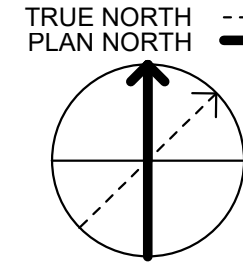

35% SCHEMATIC DESIGN SUBMISSION	5.17.21
65% DESIGN DEVELOPMENT SUBMISSION	6.15.21
65% DESIGN DEVELOPMENT RESUBMISSION	8.25.21
Revisions:	Date:

CONSULTANT

IMEG
The Future Built Smarter www.imegcorp.com
15 SUNNEN DRIVE
SUITE 104
ST. LOUIS, MO 63143
P: 314.645.1132 F: 314.645.1173
PROJECT #18004375.03

ARCHITECT/ENGINEER OF RECORD

Romanyk Consulting
Focusing on what matters
Romanyk Consulting Corp. www.romanykconsulting.com
3308 Preston Road, Suite 350-164, Plano, Texas 75093

STAMP

Bicsi
DAVID LARSON
BICS1 ID # 106098
Expires 12-31-25
REGISTERED COMMUNICATIONS DISTRIBUTION DESIGNER
RCDD

Office of
Construction
and Facilities
Management

VA U.S. Department
of Veterans Affairs

Drawing Title
BUILDING 70 SECOND FLOOR DEMO PLAN -
TECHNOLOGY - AREA D NORTH

Approved:

Phase
FINAL BID DOCUMENTS

Sprinklered
FULLY SPRINKLERED

Project Title
EHRM INFRASTRUCTURE
UPGRADES - MILWAUKEE, WI

Location
5000 W. NATIONAL AVENUE, MILWAUKEE, WI

Issue Date
SEPTEMBER 05, 2025

Checked
PHINIE

Drawn
MAIBEJ

Project Number
695-21-700

Building Number
70

Drawing Number
70-TD102D-N

F

E

D

C


B

A


9/3/2025 3:45:16 PM

Autodesk Docs\DCFM East - Milwaukee EHRM (R24)T24_1804375.03_VA MilWEHRM_C.dwt

- SHEET NOTES:**
1. REMOVE ALL NETWORK CABLING TO POINTS OF TERMINATION IN ASSOCIATED TELECOM ROOMS. REFER TO FLOOR PLANS AND SHEET T1001 FOR TR ROOM LOCATIONS.
 2. REFER TO ARCHITECTURAL PHASING PLANS FOR WHEN EXISTING CABLING IS ALLOWED TO BE DEMOLISHED.
 3. FOR ALL EXISTING WIRELESS ACCESS POINTS AND SURVEILLANCE CAMERAS, DEVICES SHALL REMAIN. SCOPE OF WORK INCLUDES CABLE REPLACEMENT ONLY. COORDINATE WITH COR FOR ANY DOWNTIME OF DEVICES.
 4. EXISTING LOCATIONS OF WORK AREA, OUTLETS SHOWN ON THIS SHEET MAY NOT NECESSARILY BE IN THE EXACT LOCATION AS IDENTIFIED.

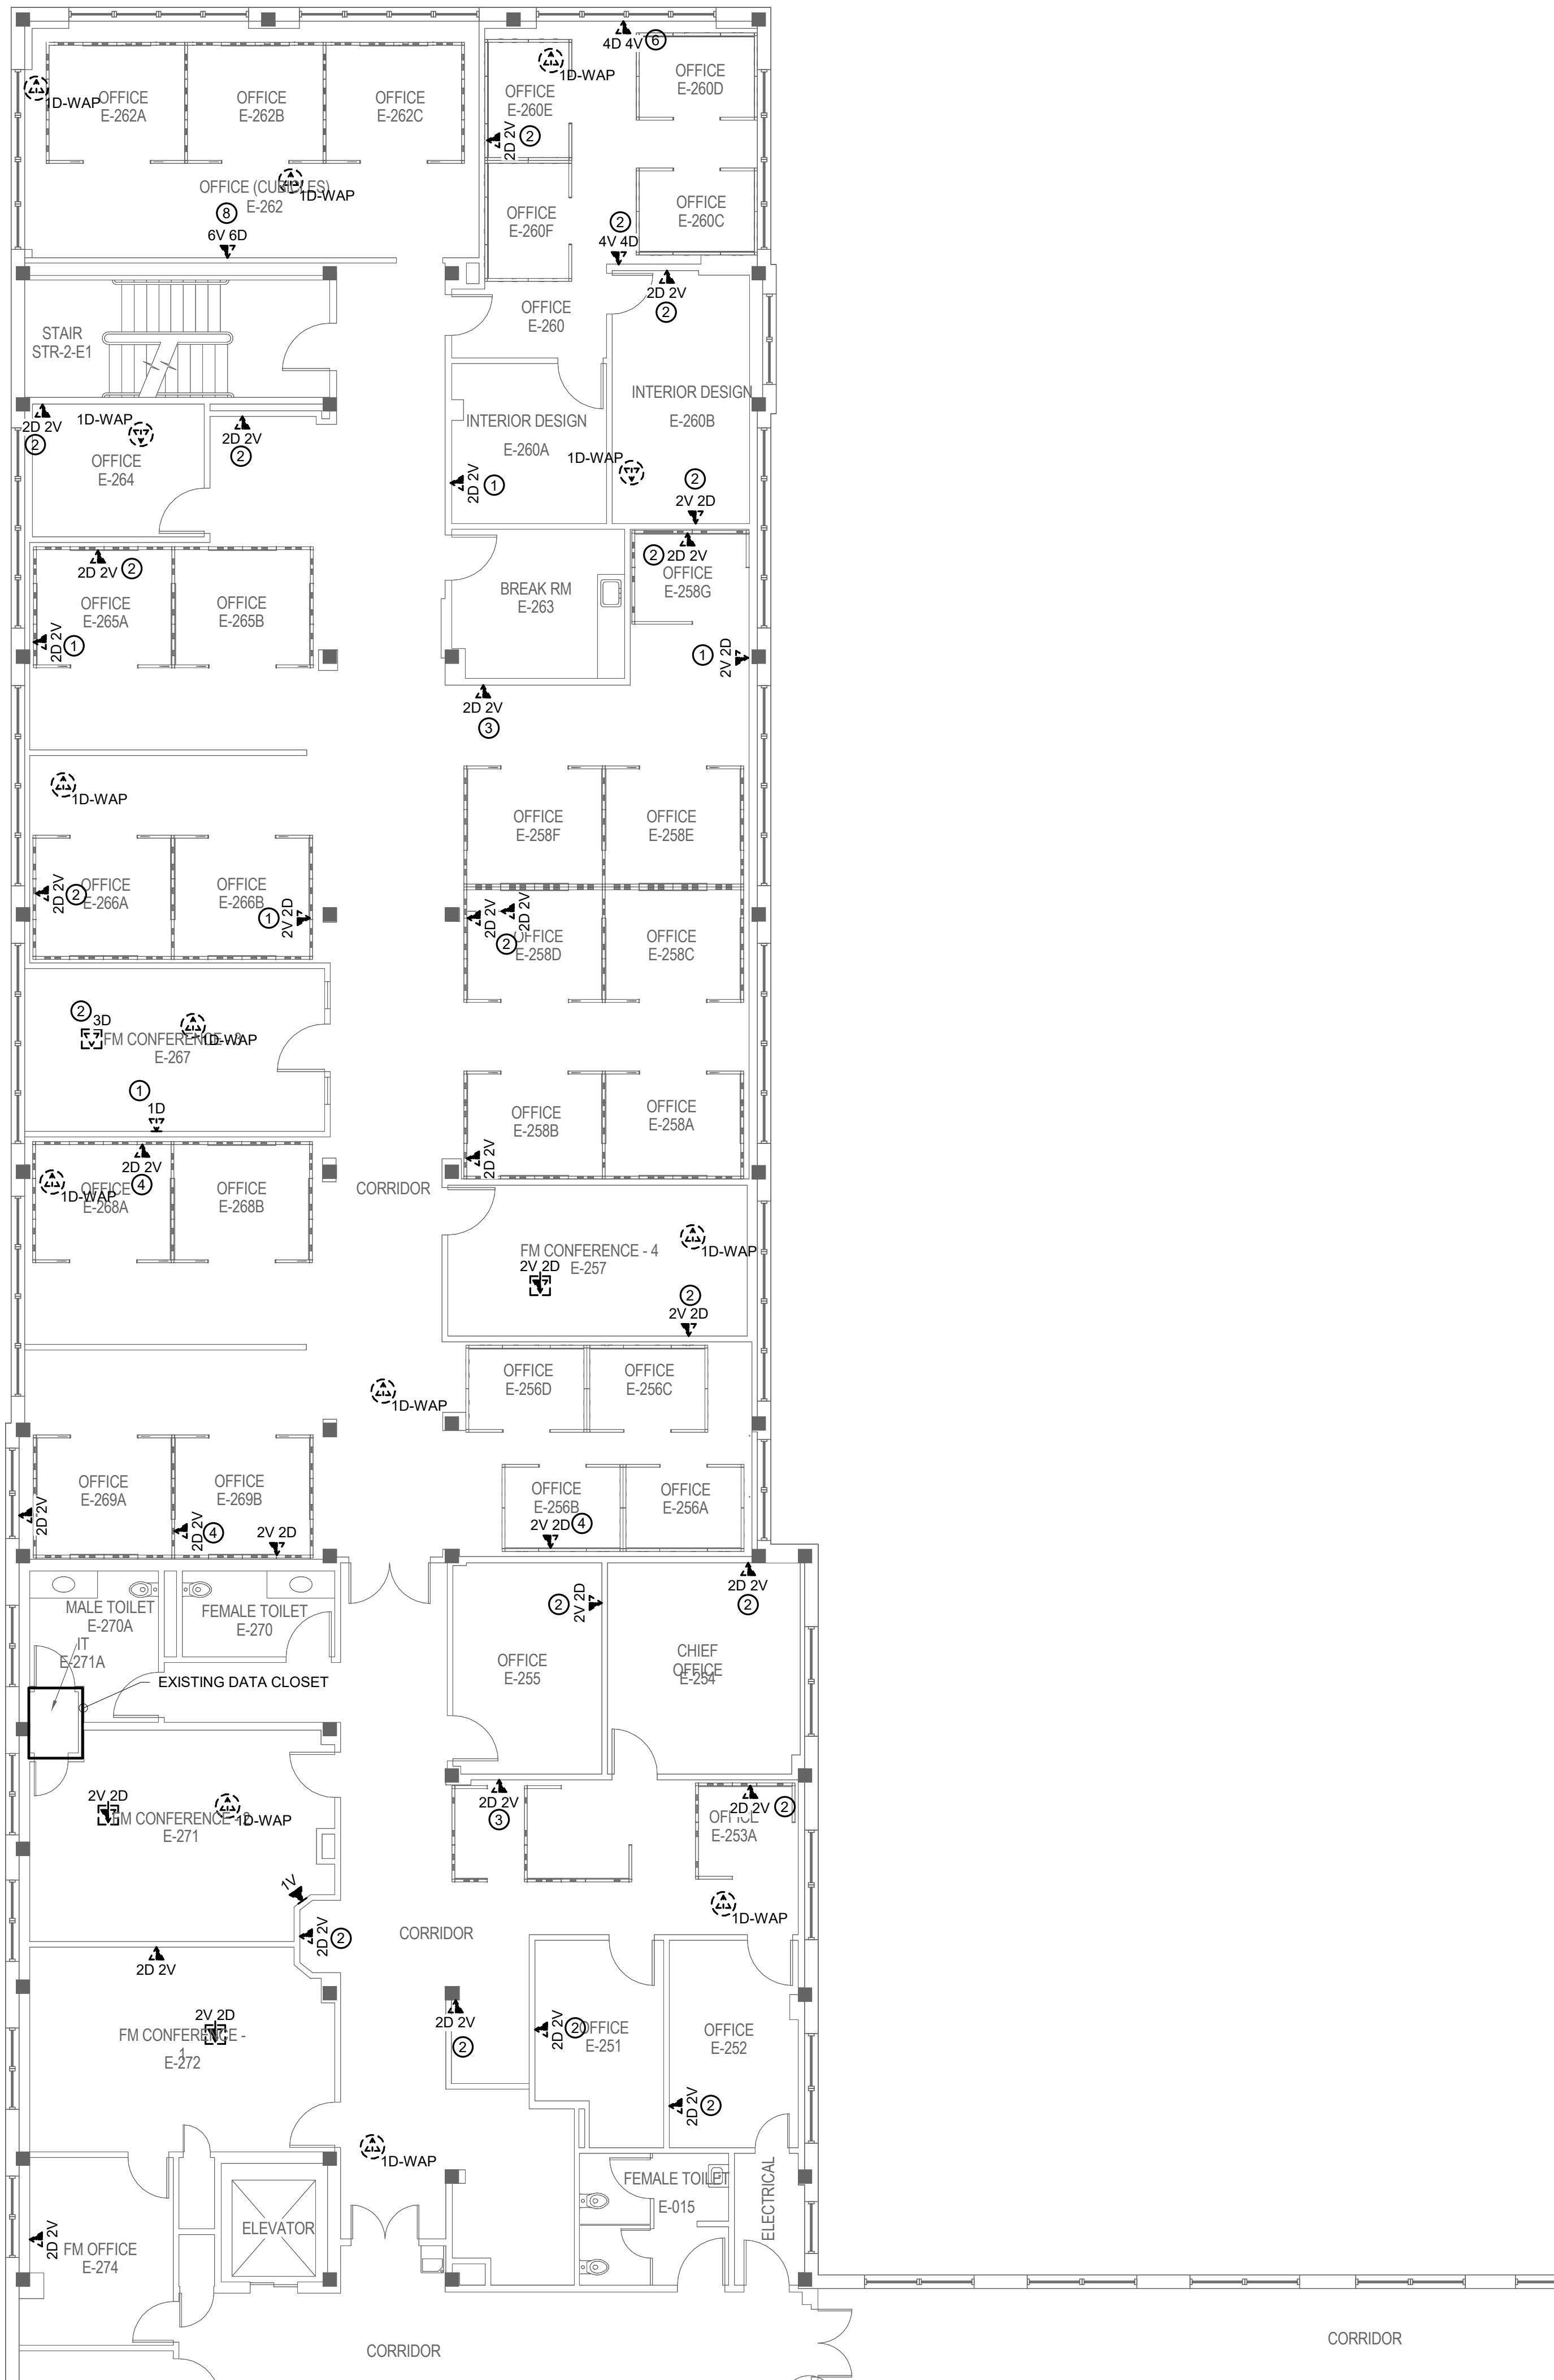

1 BUILDING 70 SECOND FLOOR DEMOLITION PLAN - TECHNOLOGY - AREA E NORTH
1/8" = 1'-0"

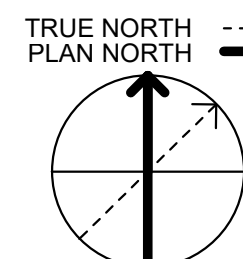

35% SCHEMATIC DESIGN SUBMISSION	5.17.21
65% DESIGN DEVELOPMENT SUBMISSION	6.15.21
65% DESIGN DEVELOPMENT RESUBMISSION	8.25.21
Revisions:	Date:

CONSULTANT

IMEG
15 SUNNEN DRIVE
SUITE 104
ST. LOUIS, MO 63143
P: 314.645.1132 F: 314.645.1173
PROJECT #18004375.03

ARCHITECT/ENGINEER OF RECORD

Romanyk Consulting
Focusing on what matters
Romanyk Consulting Corp. www.romanykconsulting.com
3308 Preston Road, Suite 350-164, Plano, Texas 75093

STAMP

Bicsi
DAVID LARSON
BICS1 ID # 106098
Expires 12-31-25

Office of
Construction
and Facilities
Management

VA U.S. Department
of Veterans Affairs

Drawing Title
BUILDING 70 SECOND FLOOR DEMO PLAN -
TECHNOLOGY - AREA E NORTH

Approved:

Phase
FINAL BID DOCUMENTS

Sprinklered
FULLY SPRINKLERED

Project Title
EHRM INFRASTRUCTURE
UPGRADES - MILWAUKEE, WI

Location
5000 W. NATIONAL AVENUE, MILWAUKEE, WI

Issue Date
SEPTEMBER 05, 2025

Checked
PHINIE

Drawn
MAIBEJ

Project Number
695-21-700

Building Number
70

Drawing Number
70-TD102E-N

F

E

D

C

B


A

9/3/2025 3:56:17 PM

Autodesk Docs://OCFM East - Milwaukee EHRM (R24)T24_18004375.03_VA MilwEHRM_C.Mt

SHEET NOTES:

1. REMOVE ALL NETWORK CABLING TO POINTS OF TERMINATION IN ASSOCIATED TELECOM ROOMS. REFER TO FLOOR PLANS AND SHEET T1001 FOR TR ROOM LOCATIONS.
2. REFER TO ARCHITECTURAL PHASING PLANS FOR WHEN EXISTING CABLING IS ALLOWED TO BE DEMOLISHED.
3. FOR ALL EXISTING WIRELESS ACCESS POINTS AND SURVEILLANCE CAMERAS, DEVICES SHALL REMAIN. SCOPE OF WORK INCLUDES CABLE REPLACEMENT ONLY. COORDINATE WITH COR FOR ANY DOWNTIME OF DEVICES.
4. EXISTING LOCATIONS OF WORK AREA OUTLETS SHOWN ON THIS SHEET MAY NOT NECESSARILY BE IN THE EXACT LOCATION AS IDENTIFIED.

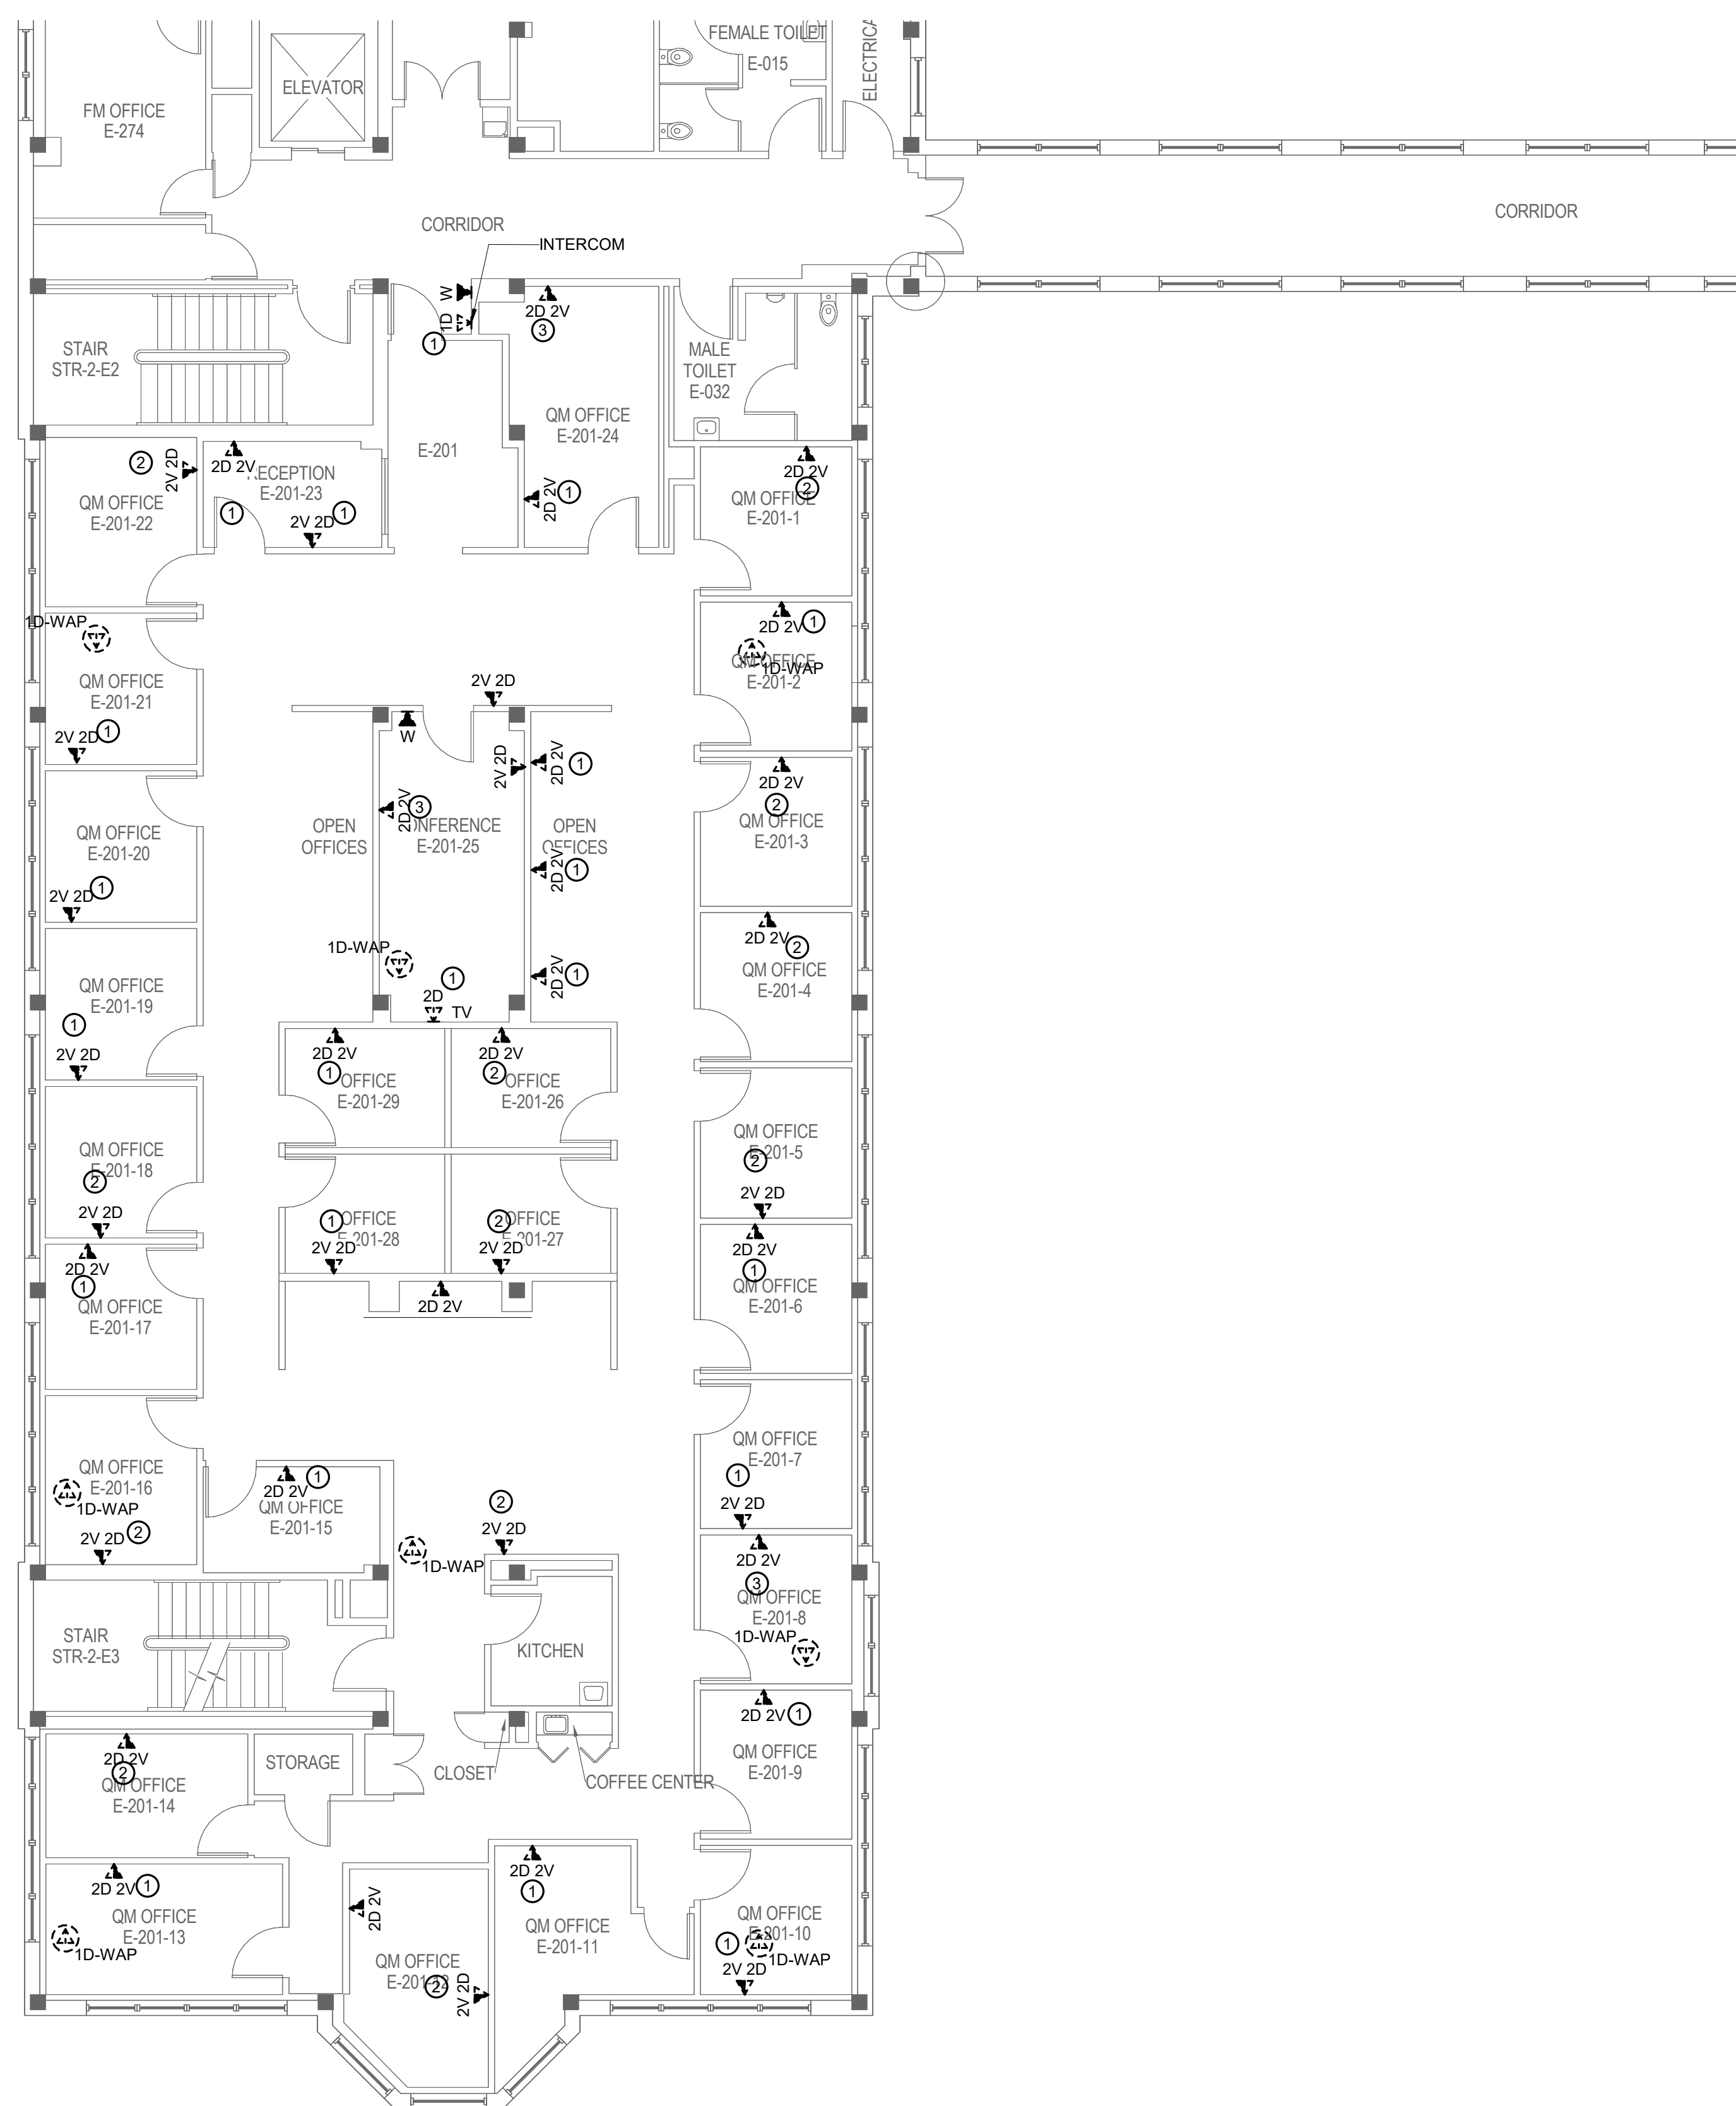

1 BUILDING 70 SECOND FLOOR DEMOLITION PLAN - TECHNOLOGY - AREA E SOUTH
1/8" = 1'-0"

35% SCHEMATIC DESIGN SUBMISSION	5.17.21
65% DESIGN DEVELOPMENT SUBMISSION	6.15.21
65% DESIGN DEVELOPMENT RESUBMISSION	8.25.21
Revisions:	Date:

CONSULTANT

 **IMEG**

The future is *here* www.imegcorp.com

15 SUNN DRIVE
SUITE 104
ST. LOUIS, MO 63143
P: 314.645.1132 F: 314.645.1173
PROJECT #18004375.03

ARCHITECT/ENGINEER OF RECORD

 **Romanyk Consulting**
Focusing on what matters

Romanyk Consulting Corp. www.romanykconsulting.com
3308 Preston Road, Suite 350-164, Plano, Texas 75093

Office of
Construction
and Facilities
Management

VA | U.S. Department
of Veterans Affairs

Drawing Title
BUILDING 70 SECOND FLOOR DEMO PLAN -
TECHNOLOGY - AREA E SOUTH

Approved:

Phase
FINAL BID DOCUMENTS

Sprinklered
FULLY SPRINKLERED

Project Title EHRM INFRASTRUCTURE UPGRADES - MILWAUKEE, WI			Project Number 695-21-700	
			Building Number 70	
Location 5000 W. NATIONAL AVENUE MILWAUKEE, WI			Drawing Number 70-TD102E-S	
Issue Date SEPTEMBER 05, 2025	Checked PHINIE	Drawn MAIBEJ		

F

E

D

C


B

A


9/3/2025 3:56:18 PM

Autodesk Docs\DCFM East - Milwaukee EHRM (R24)T24_1804375.03_VA Milwaukee_C.dwt

- SHEET NOTES:**
1. REMOVE ALL NETWORK CABLING TO POINTS OF TERMINATION IN ASSOCIATED TELECOM ROOMS. REFER TO FLOOR PLANS AND SHEET T1001 FOR TR ROOM LOCATIONS.
 2. REFER TO ARCHITECTURAL PHASING PLANS FOR WHEN EXISTING CABLING IS ALLOWED TO BE DEMOLISHED.
 3. FOR ALL EXISTING WIRELESS ACCESS POINTS AND SURVEILLANCE CAMERAS, DEVICES SHALL REMAIN. SCOPE OF WORK INCLUDES CABLE REPLACEMENT ONLY. COORDINATE WITH COR FOR ANY DOWNTIME OF DEVICES. EXISTING LOCATIONS OF WORK AREA OUTLETS SHOWN ON THIS SHEET MAY NOT NECESSARILY BE IN THE EXACT LOCATION AS IDENTIFIED.
 - 4.

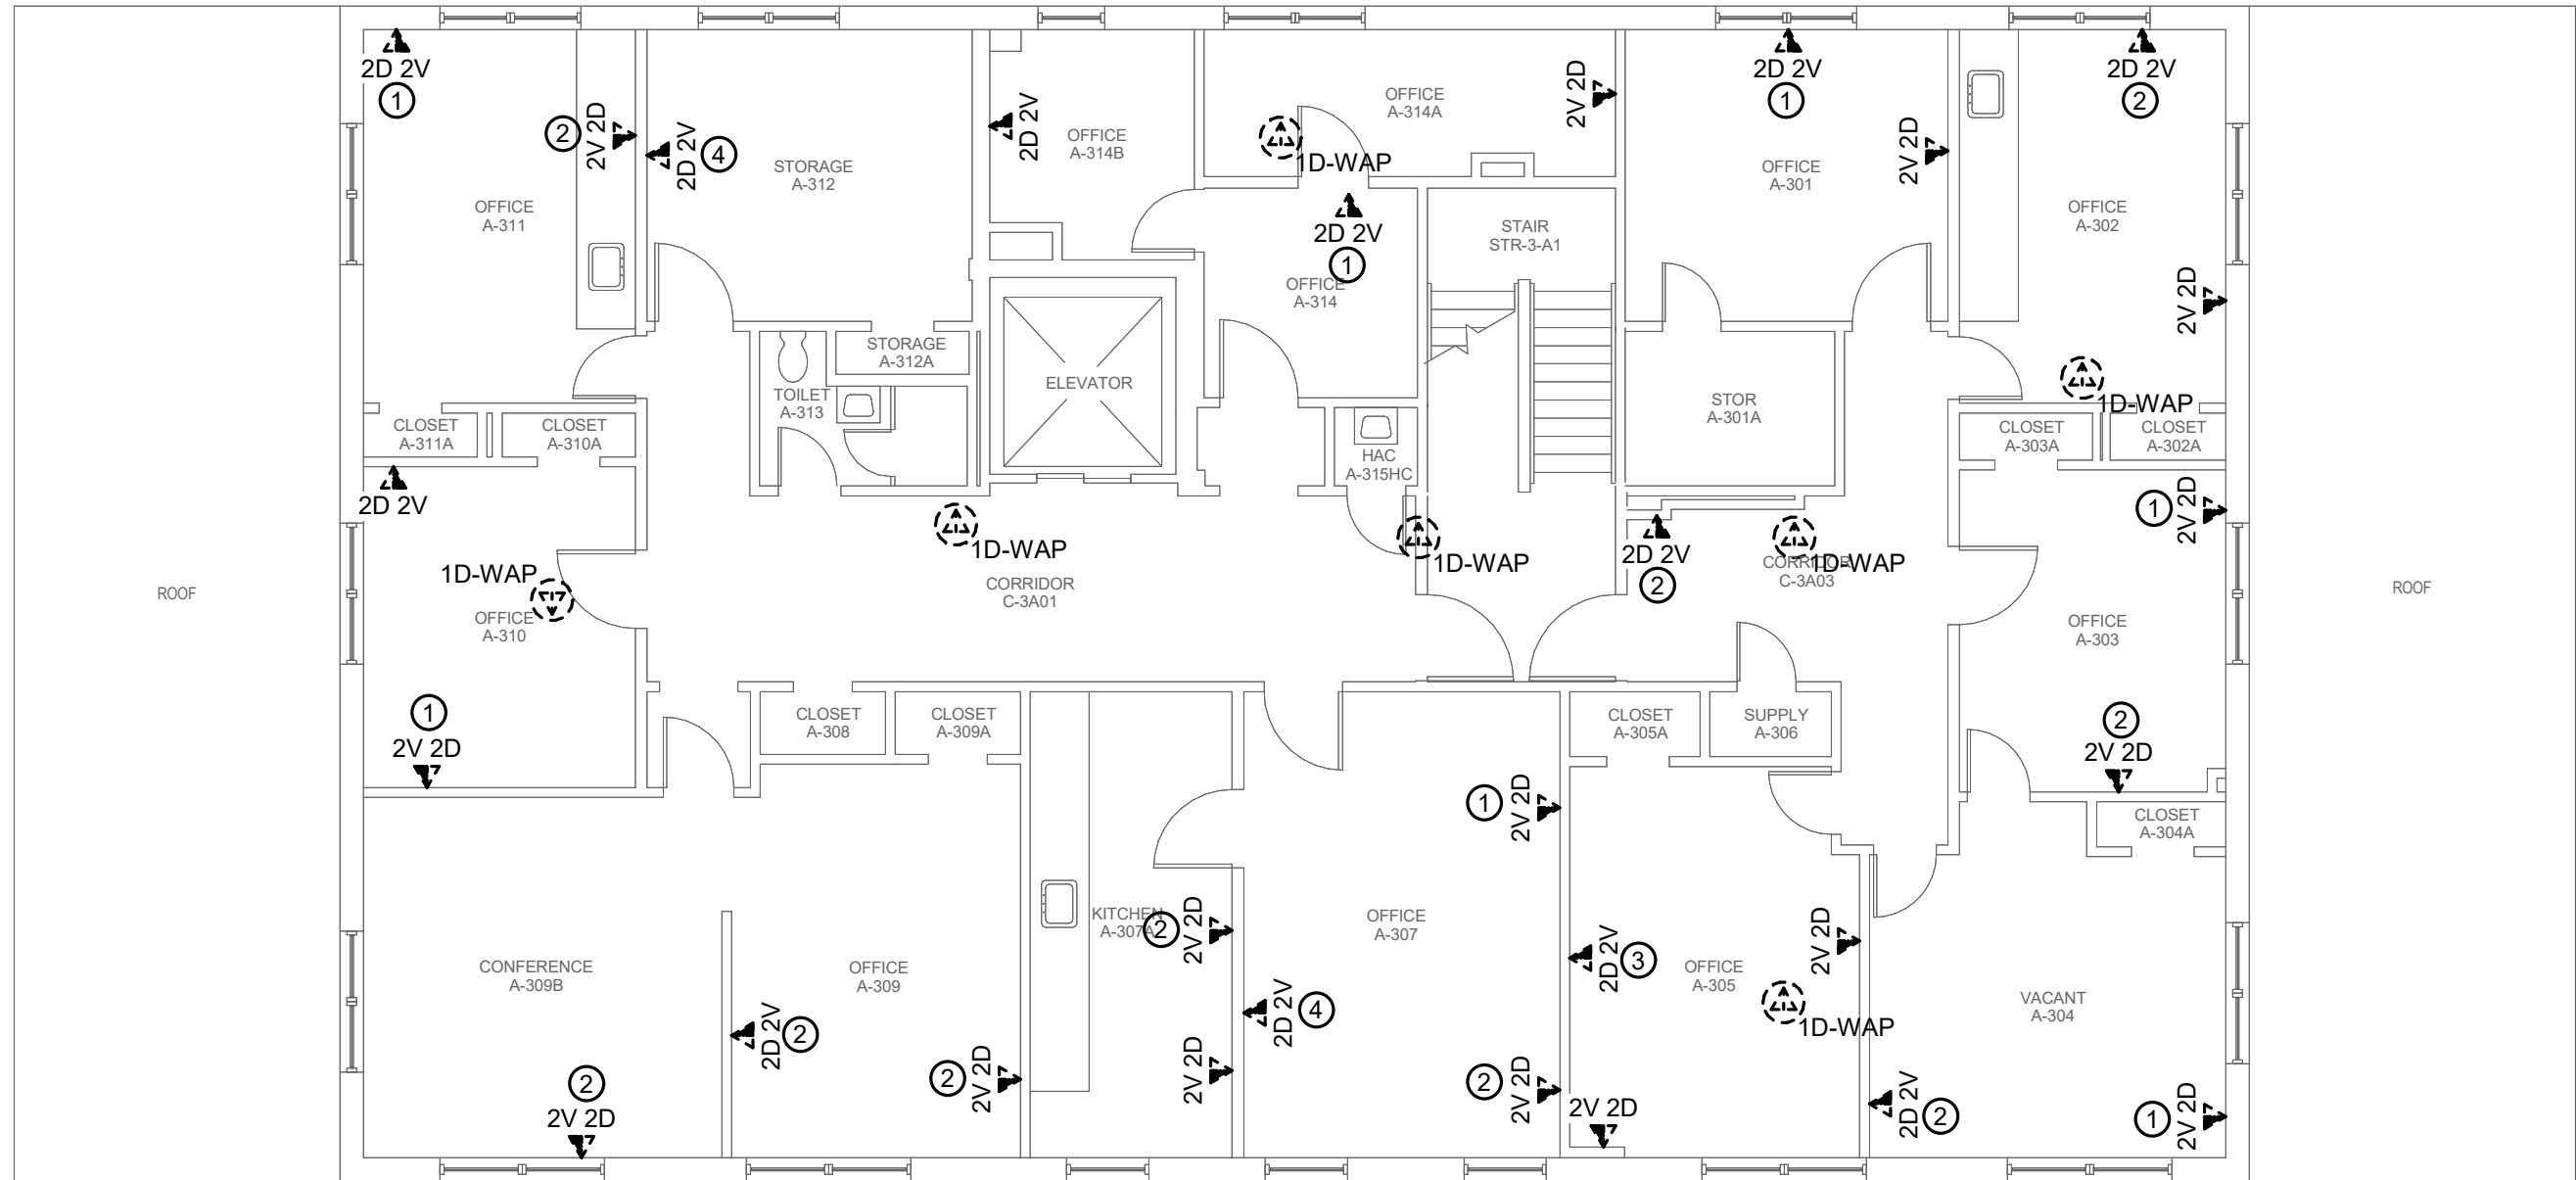

1 **BUILDING 70 THIRD FLOOR DEMOLITION PLAN - TECHNOLOGY**
1/8" = 1'-0"

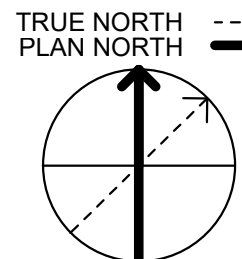

35% SCHEMATIC DESIGN SUBMISSION	5.17.21
65% DESIGN DEVELOPMENT SUBMISSION	6.15.21
65% DESIGN DEVELOPMENT RESUBMISSION	8.25.21
Revisions:	Date:

CONSULTANT

IMEG
15 SUNNEN DRIVE
SUITE 104
ST. LOUIS, MO 63143
P: 314.645.1132 F: 314.645.1173
PROJECT #18004375.03

ARCHITECT/ENGINEER OF RECORD

Romanyk Consulting
Focusing on what matters
Romanyk Consulting Corp. www.romanykconsulting.com
3308 Preston Road, Suite 350-164, Plano, Texas 75093

STAMP

Bicsi
DAVID LARSON
BICS1 ID # 106098
EXPIRES 12-31-25
REGISTERED COMMUNICATIONS DISTRIBUTION DESIGNER

Office of
Construction
and Facilities
Management
VA U.S. Department
of Veterans Affairs

Drawing Title
BUILDING 70 THIRD FLOOR DEMO PLAN -
TECHNOLOGY
Approved:

Phase
FINAL BID DOCUMENTS
Sprinklered
FULLY SPRINKLERED

Project Title
EHRM INFRASTRUCTURE
UPGRADES - MILWAUKEE, WI
Location
5000 W. NATIONAL AVENUE MILWAUKEE, WI
Issue Date
SEPTEMBER 05, 2025
Checked
PHINIE
Drawn
MAIBEJ

Project Number
695-21-700
Building Number
70
Drawing Number
70-TD103

F
E
D
C
B
A

9/2/2025 3:45:19 PM
Autodesk Docs\DCFM East - Milwaukee EHRM (R24)T24_1804375\03_VA MilWEHRM_C.dwt

10

9

8

7

6

5

4

3

2

1



- SHEET NOTES:**
1. REFER TO INDIVIDUAL AREA BUILDING DEMO FLOOR PLANS FOR ADDITIONAL INFORMATION.
 2. THESE DRAWINGS MAKE THE BEST ATTEMPT TO IDENTIFY EXISTING DATA DROPS/WORK AREA OUTLETS. AS LONG AS THE TOTAL NEWLY INSTALLED DATA DROP COUNT DOES NOT VARY +/- 10% IDENTIFIED ON THESE DRAWINGS, THE CONTRACTOR'S SCOPE SHALL BE UNCHANGED.
 3. NEW WORK AREA OUTLETS SHALL BE LOCATED IN EXISTING BOXES. WORK AREA OUTLETS SHOWN ON THIS SHEET MAY NOT BE IN THE EXACT LOCATION AS IDENTIFIED.
- KEYNOTES:** (#)
1. EXISTING MANHOLE. EXISTING PATHWAY TO BUILDING 123 TO REMAIN. PROTECT IN PLACE.
 2. TWO (2) 4" PATHWAYS TO ABOVE.

1 BUILDING 70 BASEMENT OVERALL PLAN - TECHNOLOGY
1" = 20'-0"

35% SCHEMATIC DESIGN SUBMISSION	5.17.21
65% DESIGN DEVELOPMENT SUBMISSION	6.15.21
65% DESIGN DEVELOPMENT RESUBMISSION	8.25.21
Revisions:	Date:


CONSULTANT



ARCHITECT/ENGINEER OF RECORD



STAMP

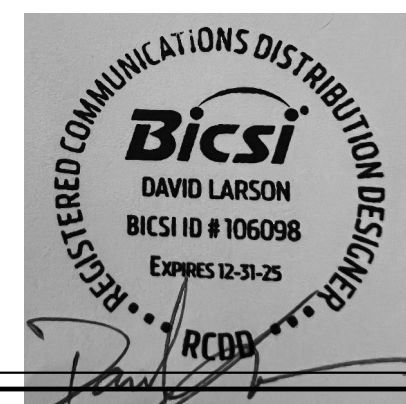

Office of
Construction
and Facilities
Management

VA

U.S. Department
of Veterans Affairs

Drawing Title
BUILDING 70 BASEMENT OVERALL PLAN -
TECHNOLOGY

Approved:

Phase
FINAL BID DOCUMENTS

Sprinklered
FULLY SPRINKLERED

Project Title
EHRM INFRASTRUCTURE
UPGRADES - MILWAUKEE, WI

Location
5000 W. NATIONAL AVENUE, MILWAUKEE, WI

Issue Date
SEPTEMBER 05, 2025



Checked
PHINIE

Drawn
MAIBEJ

Project Number
695-21-700
Building Number
70

Drawing Number
70-TN100

0' 10' 20' 40'
Graphic Scale: 1" = 20'-0"

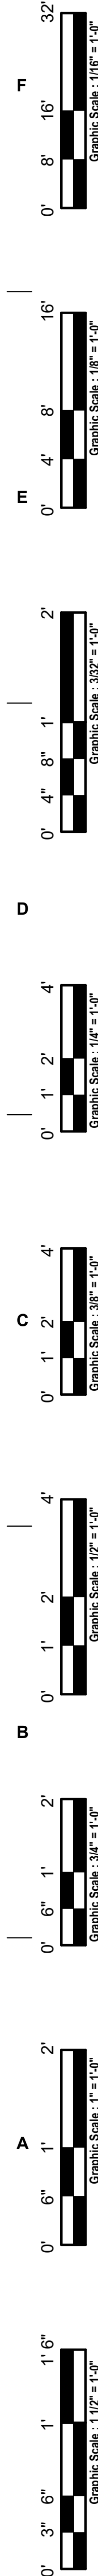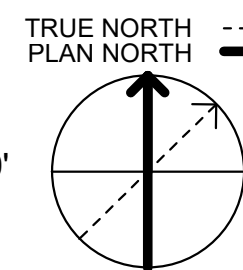

F

E

D


C

B

A

9/3/2025 3:56:20 PM

Autodesk Docs://OCFM East - Milwaukee EHRM (R24)T24_18004375.03_VA MilwEHRM_C.Mt

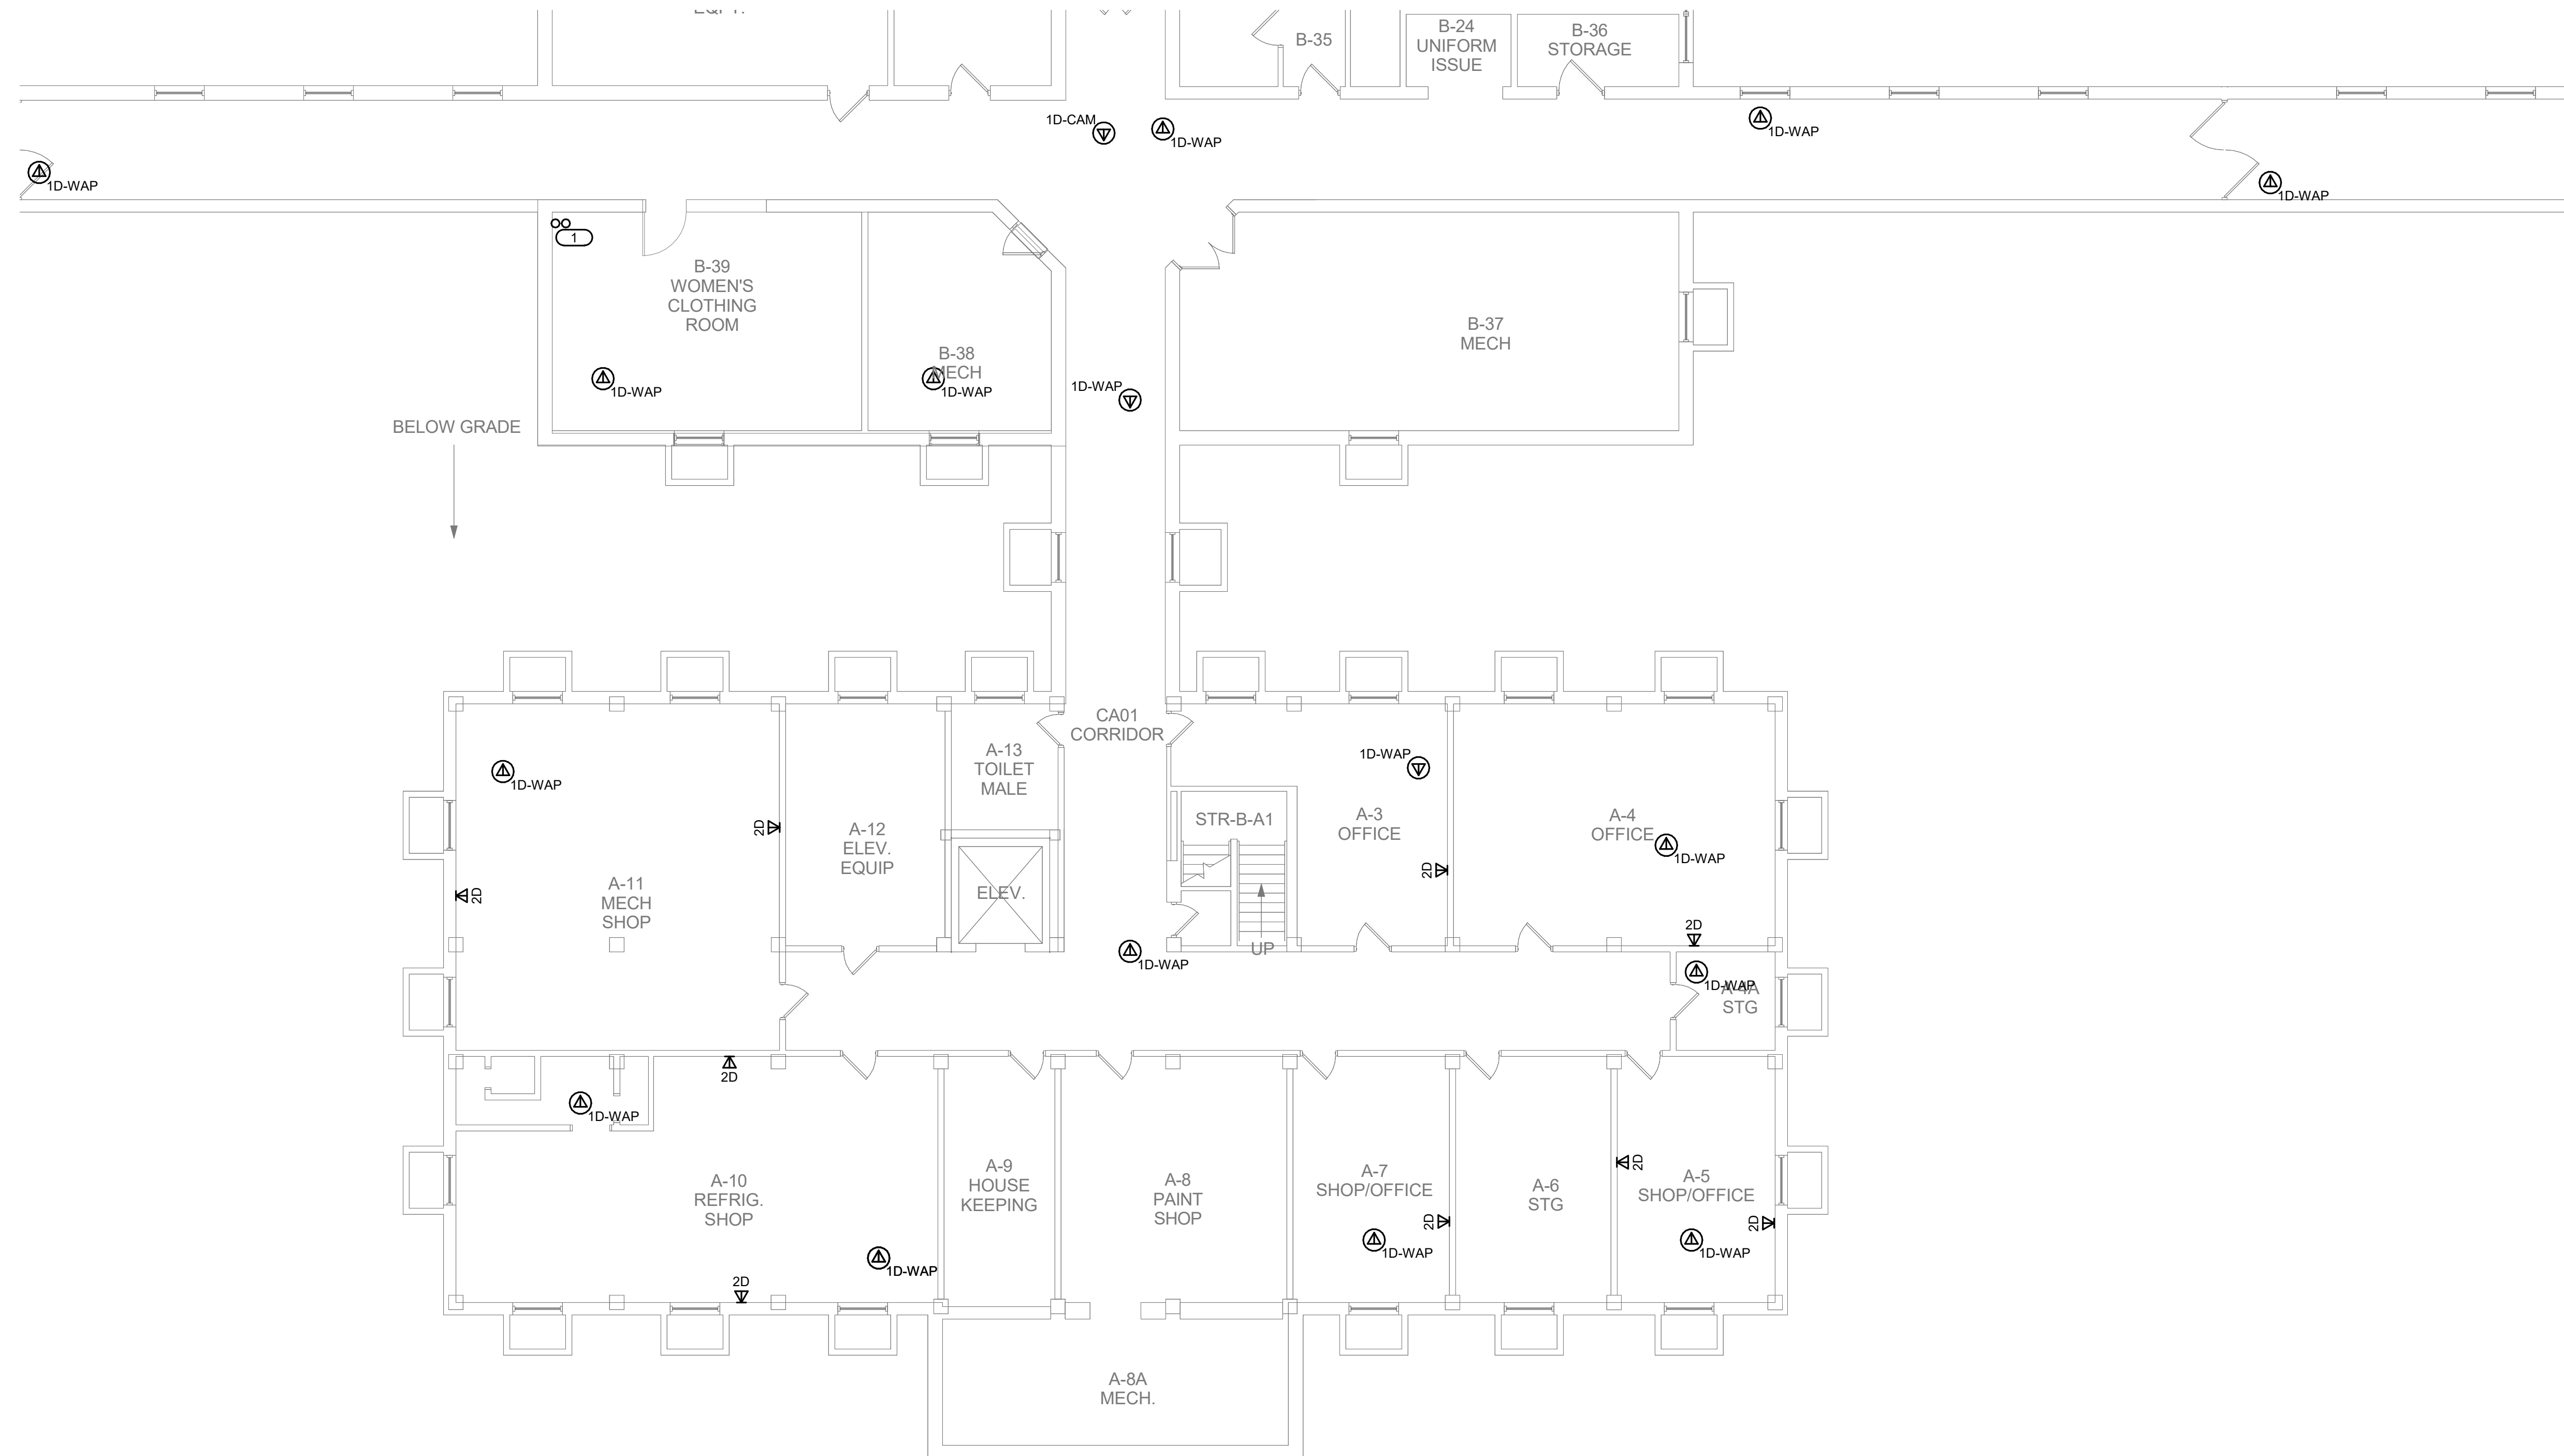

1 BUILDING 70 BASEMENT PLAN - TECHNOLOGY - AREA A
1/8" = 1'-0"

$$1/8'' = 1'-0''$$

35% SCHEMATIC DESIGN SUBMISSION	5.17.21
65% DESIGN DEVELOPMENT SUBMISSION	6.15.21
65% DESIGN DEVELOPMENT RESUBMISSION	8.25.21
Revisions:	Date:

CONSULTANT




ARCHITECT/ENGINEER OF RECORD



Romanyk Consulting

Focusing on what matters

STAMP

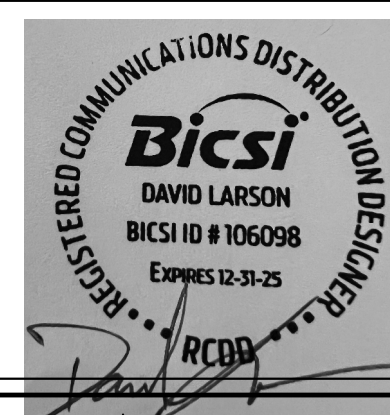

Office of
Construction
and Facilities
Management

VAU.S. Department
of Veterans Affairs

Drawing Title	BUILDING 70 BASEMENT PLAN - TECHNOLOGY AREA A
----------------------	--

Approved:

Phase	FINAL BID DOCUMENTS
-------	---------------------

Sprinklered
FULLY SPRINKLERED

Project Title	EHRM INFRASTRUCTURE UPGRADES - MILWAUKEE, WI
---------------	---

Location	5000 W. NATIONAL AVENUE MILWAUKEE, WI
-----------------	---------------------------------------

Issue Date
SEPTEMBER 05, 2025

Checked
PHINIE

Drawn
MAIBEJ

Project Number	695-21-700
Building Number	


Drawing Number
70-TN100A


GENERAL NOTES:

1. REFER TO T17N400 FOR TECHNOLOGY ROUGH IN DETAIL.
2. ALL NETWORK CABLES ON THIS SHEET SHALL TERMINATE IN TR-70-8-159.
3. CONTRACTOR TO PROVIDE NEW J-HOOK ROUTES FOR ALL NEW CABLEING, J-HOOK SIZE AND QUANTITY TO BE PER MANUFACTURER RECOMMENDATIONS.
4. REFER TO T15N400 FOR FLOOR FORM DIA GRAMS.
5. REFER TO SHEET T1402 FOR PENETRATION DETAILS.
6. THESE DRAWINGS MAKE THE BEST ATTEMPT TO IDENTIFY EXISTING DATA DROPS/WORK AREA OUTLETS, AS LONG AS THEY TO THE NEWLY LAYED CABLEING. IF THE DATA DOES NOT VARY +/- 10% IDENTIFIED ON THESE DRAWINGS, THE CONTRACTOR'S SCOPE SHALL BE UNCHANGED.
7. NEW WORK AREA OUTLETS SHALL BE LOCATED IN EXISTING BOXES. WORK AREA OUTLETS SHOWN ON THIS SHEET MAY NOT BE IN THE EXACT LOCATION AS IDENTIFIED.

KEYNOTES: #

1. (2) 4" PATHWAYS FROM LEVEL ABOVE.

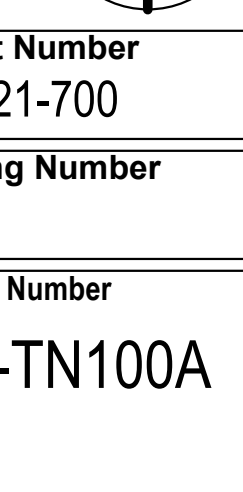

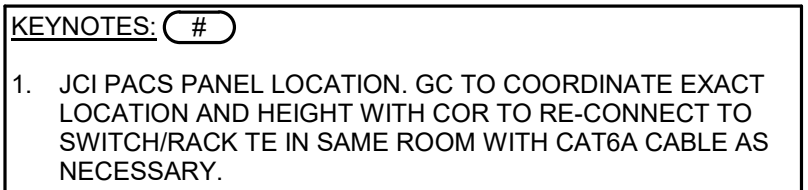

35% SCHEMATIC DESIGN SUBMISSION	5.17.21	CONSULTANT	 IMEG The Future, Built Smarter www.imegcorp.com 15 SUNNEN DRIVE SUITE 100 ST. LOUIS, MO 63143 P: 314.645.1132 F: 314.645.1173 PROJECT #18004375.03	ARCHITECT/ENGINEER OF RECORD	 Romanyk Consulting Focusing on what matters Romanyk Consulting Corp. www.romanykconsulting.com 3308 Preston Road, Suite 350-164, Plano, Texas 75093	 STAMP BICSI DAVID LARSON BICSI ID # 186098 Expires 12-31-23 RC08	Office of Construction and Facilities Management VA U.S. Department of Veterans Affairs	Drawing Title BUILDING 70 BASEMENT PLAN - TECHNOLOGY - AREA B	Project Title EHRM INFRASTRUCTURE UPGRADES - MILWAUKEE, WI	Project Number 695-21-700
65% DESIGN DEVELOPMENT SUBMISSION	6.15.21							Phase FINAL BID DOCUMENTS	Location 5000 W. NATIONAL AVENUE MILWAUKEE, WI	Building Number 70
65% DESIGN DEVELOPMENT RESUBMISSION	8.25.21							Approved:	Sprinklered FULLY SPRINKLERED	Drawing Number 70-TN100B
									Issue Date SEPTEMBER 05, 2025	Checked PHINIE
									Drawn MAIBEJ	
Revisions:	Date:									

F

E


D

C

B


A

9/3/2025 3:56:22 PM
Autodesk Docs\DCFM East - Milwaukee EHRM (R24)T24_1804375.03_VA Milwaukee_C.dwg

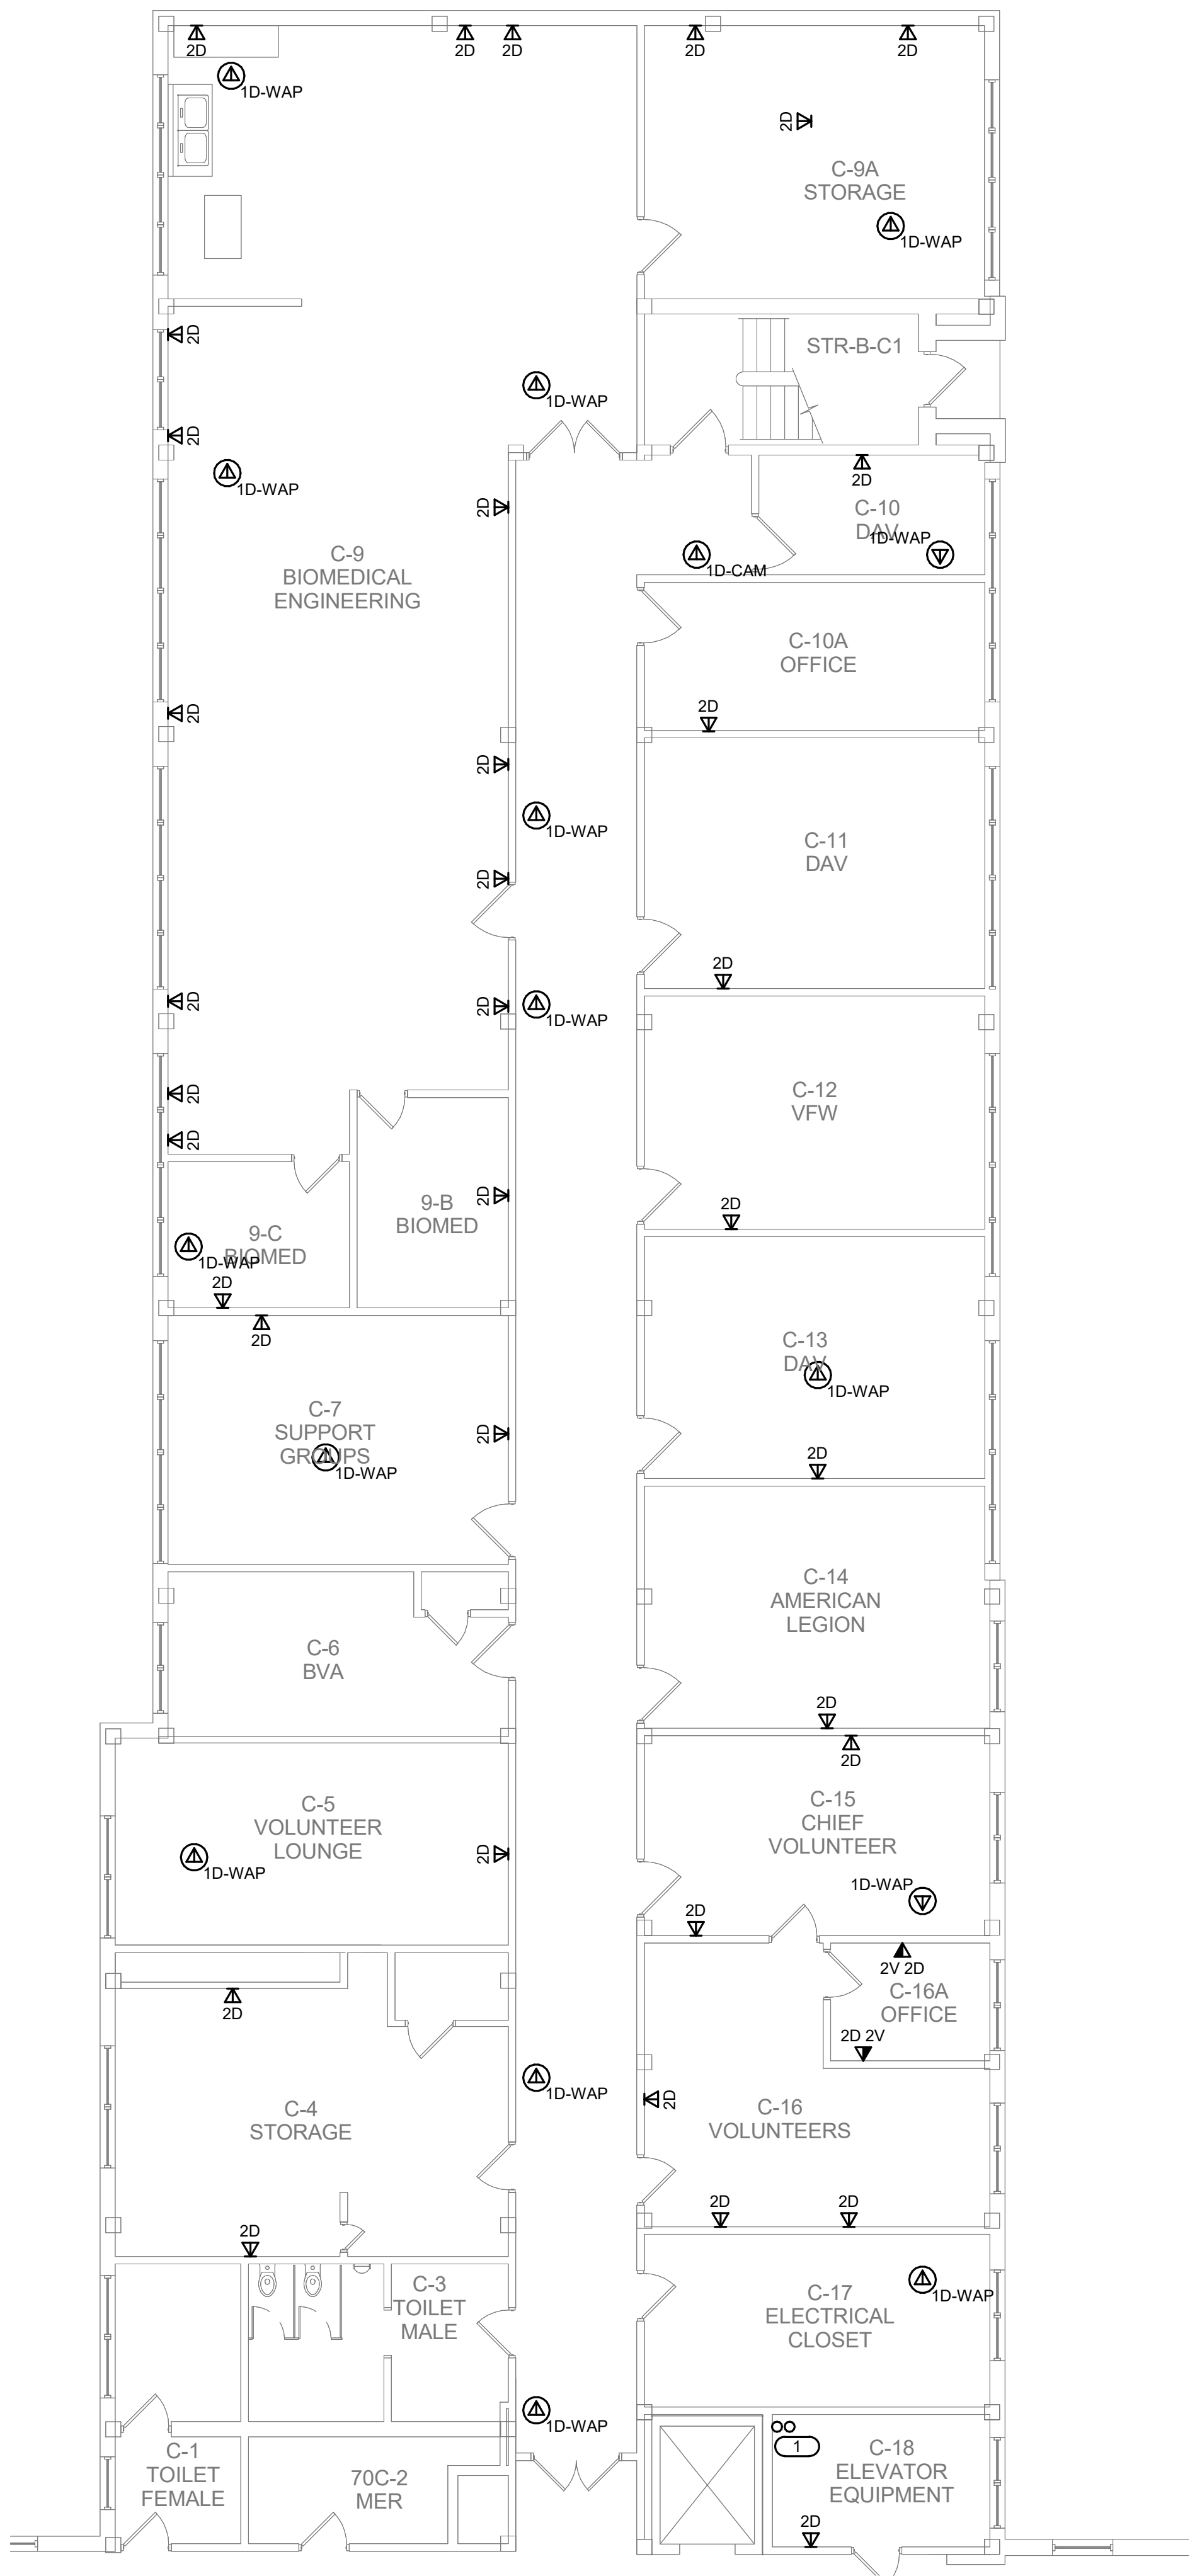

- GENERAL NOTES:**
1. REFER TO 1/TN400 FOR TECHNOLOGY ROUGH IN DETAIL.
 2. ALL NETWORK CABLES ON THIS SHEET SHALL TERMINATE IN TR-70-C-126.
 3. CONTRACTOR TO PROVIDE NEW J-HOOK ROUTES FOR ALL NEW CABLING. J-HOOK SIZE AND QUANTITY TO BE PER MANUFACTURER RECOMMENDATIONS.
 4. REFER TO TN500-TN509 FOR RISER DIAGRAMS.
 5. REFER TO SHEET TN402 FOR PENETRATION DETAILS.
 6. THESE DRAWINGS MAKE THE BEST ATTEMPT TO IDENTIFY EXISTING DATA DROPS/WORK AREA OUTLETS. AS LONG AS THE TOTAL NEWLY INSTALLED DATA DROP COUNT DOES NOT VARY +/- 10% IDENTIFIED ON THESE DRAWINGS, THE CONTRACTOR'S SCOPE SHALL BE UNCHANGED.
 7. NEW WORK AREA OUTLETS SHALL BE LOCATED IN EXISTING BOXES. WORK AREA OUTLETS SHOWN ON THIS SHEET MAY NOT BE IN THE EXACT LOCATION AS IDENTIFIED.
 8. CONTRACTOR TO INCLUDE AN ALLOWANCE FOR 10% ADDITIONAL 2-PORTS CAT6A INFORMATION OUTLETS IN THEIR PROPOSAL FOR THIS SHEET. FUTURE INFORMATION OUTLET LOCATIONS WILL BE DETERMINED BY THE VA AT A LATER DATE.
- KEYNOTES:** (#)
1. (2) 4" PATHWAYS FROM LEVEL ABOVE.

1 BUILDING 70 BASEMENT PLAN - TECHNOLOGY - AREA C NORTH
1/8" = 1'-0"

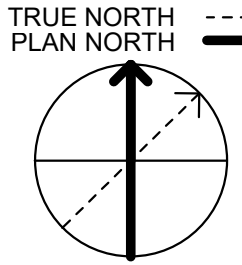

35% SCHEMATIC DESIGN SUBMISSION	5.17.21
65% DESIGN DEVELOPMENT SUBMISSION	6.15.21
65% DESIGN DEVELOPMENT RESUBMISSION	8.25.21
Revisions:	Date:

CONSULTANT

IMEG
The Future is Full of Possibilities
15 SUNNEN DRIVE
SUITE 104
ST. LOUIS, MO 63143
P: 314.645.1132 F: 314.645.1173
PROJECT #18004375.03

ARCHITECT/ENGINEER OF RECORD

Romanyk Consulting
Focusing on what matters
Romanyk Consulting Corp. www.romanykconsulting.com
3308 Preston Road, Suite 350-164, Plano, Texas 75093

STAMP

Bicsi
DAVID LARSON
BICS1 ID # 106098
Expires 12-31-25
REGISTERED COMMUNICATIONS DISTRIBUTION DESIGNER

Office of
Construction
and Facilities
Management

VA U.S. Department
of Veterans Affairs

Drawing Title
BUILDING 70 BASEMENT PLAN - TECHNOLOGY -
AREA C NORTH

Approved:

Phase
FINAL BID DOCUMENTS

Sprinklered
FULLY SPRINKLERED

Project Title
EHRM INFRASTRUCTURE
UPGRADES - MILWAUKEE, WI

Location
5000 W. NATIONAL AVENUE, MILWAUKEE, WI

Issue Date
SEPTEMBER 05, 2025

Checked
PHINIE

Drawn
MAIBEJ

Project Number
695-21-700

Building Number
70

Drawing Number
70-TN100C-N

F

E

D


C

B

A


9/3/2025 3:56:23 PM

Autodesk Docs\DCFM East - Milwaukee EHRM (R24)T24_1804375.03_VA Milwaukee_C.dwt

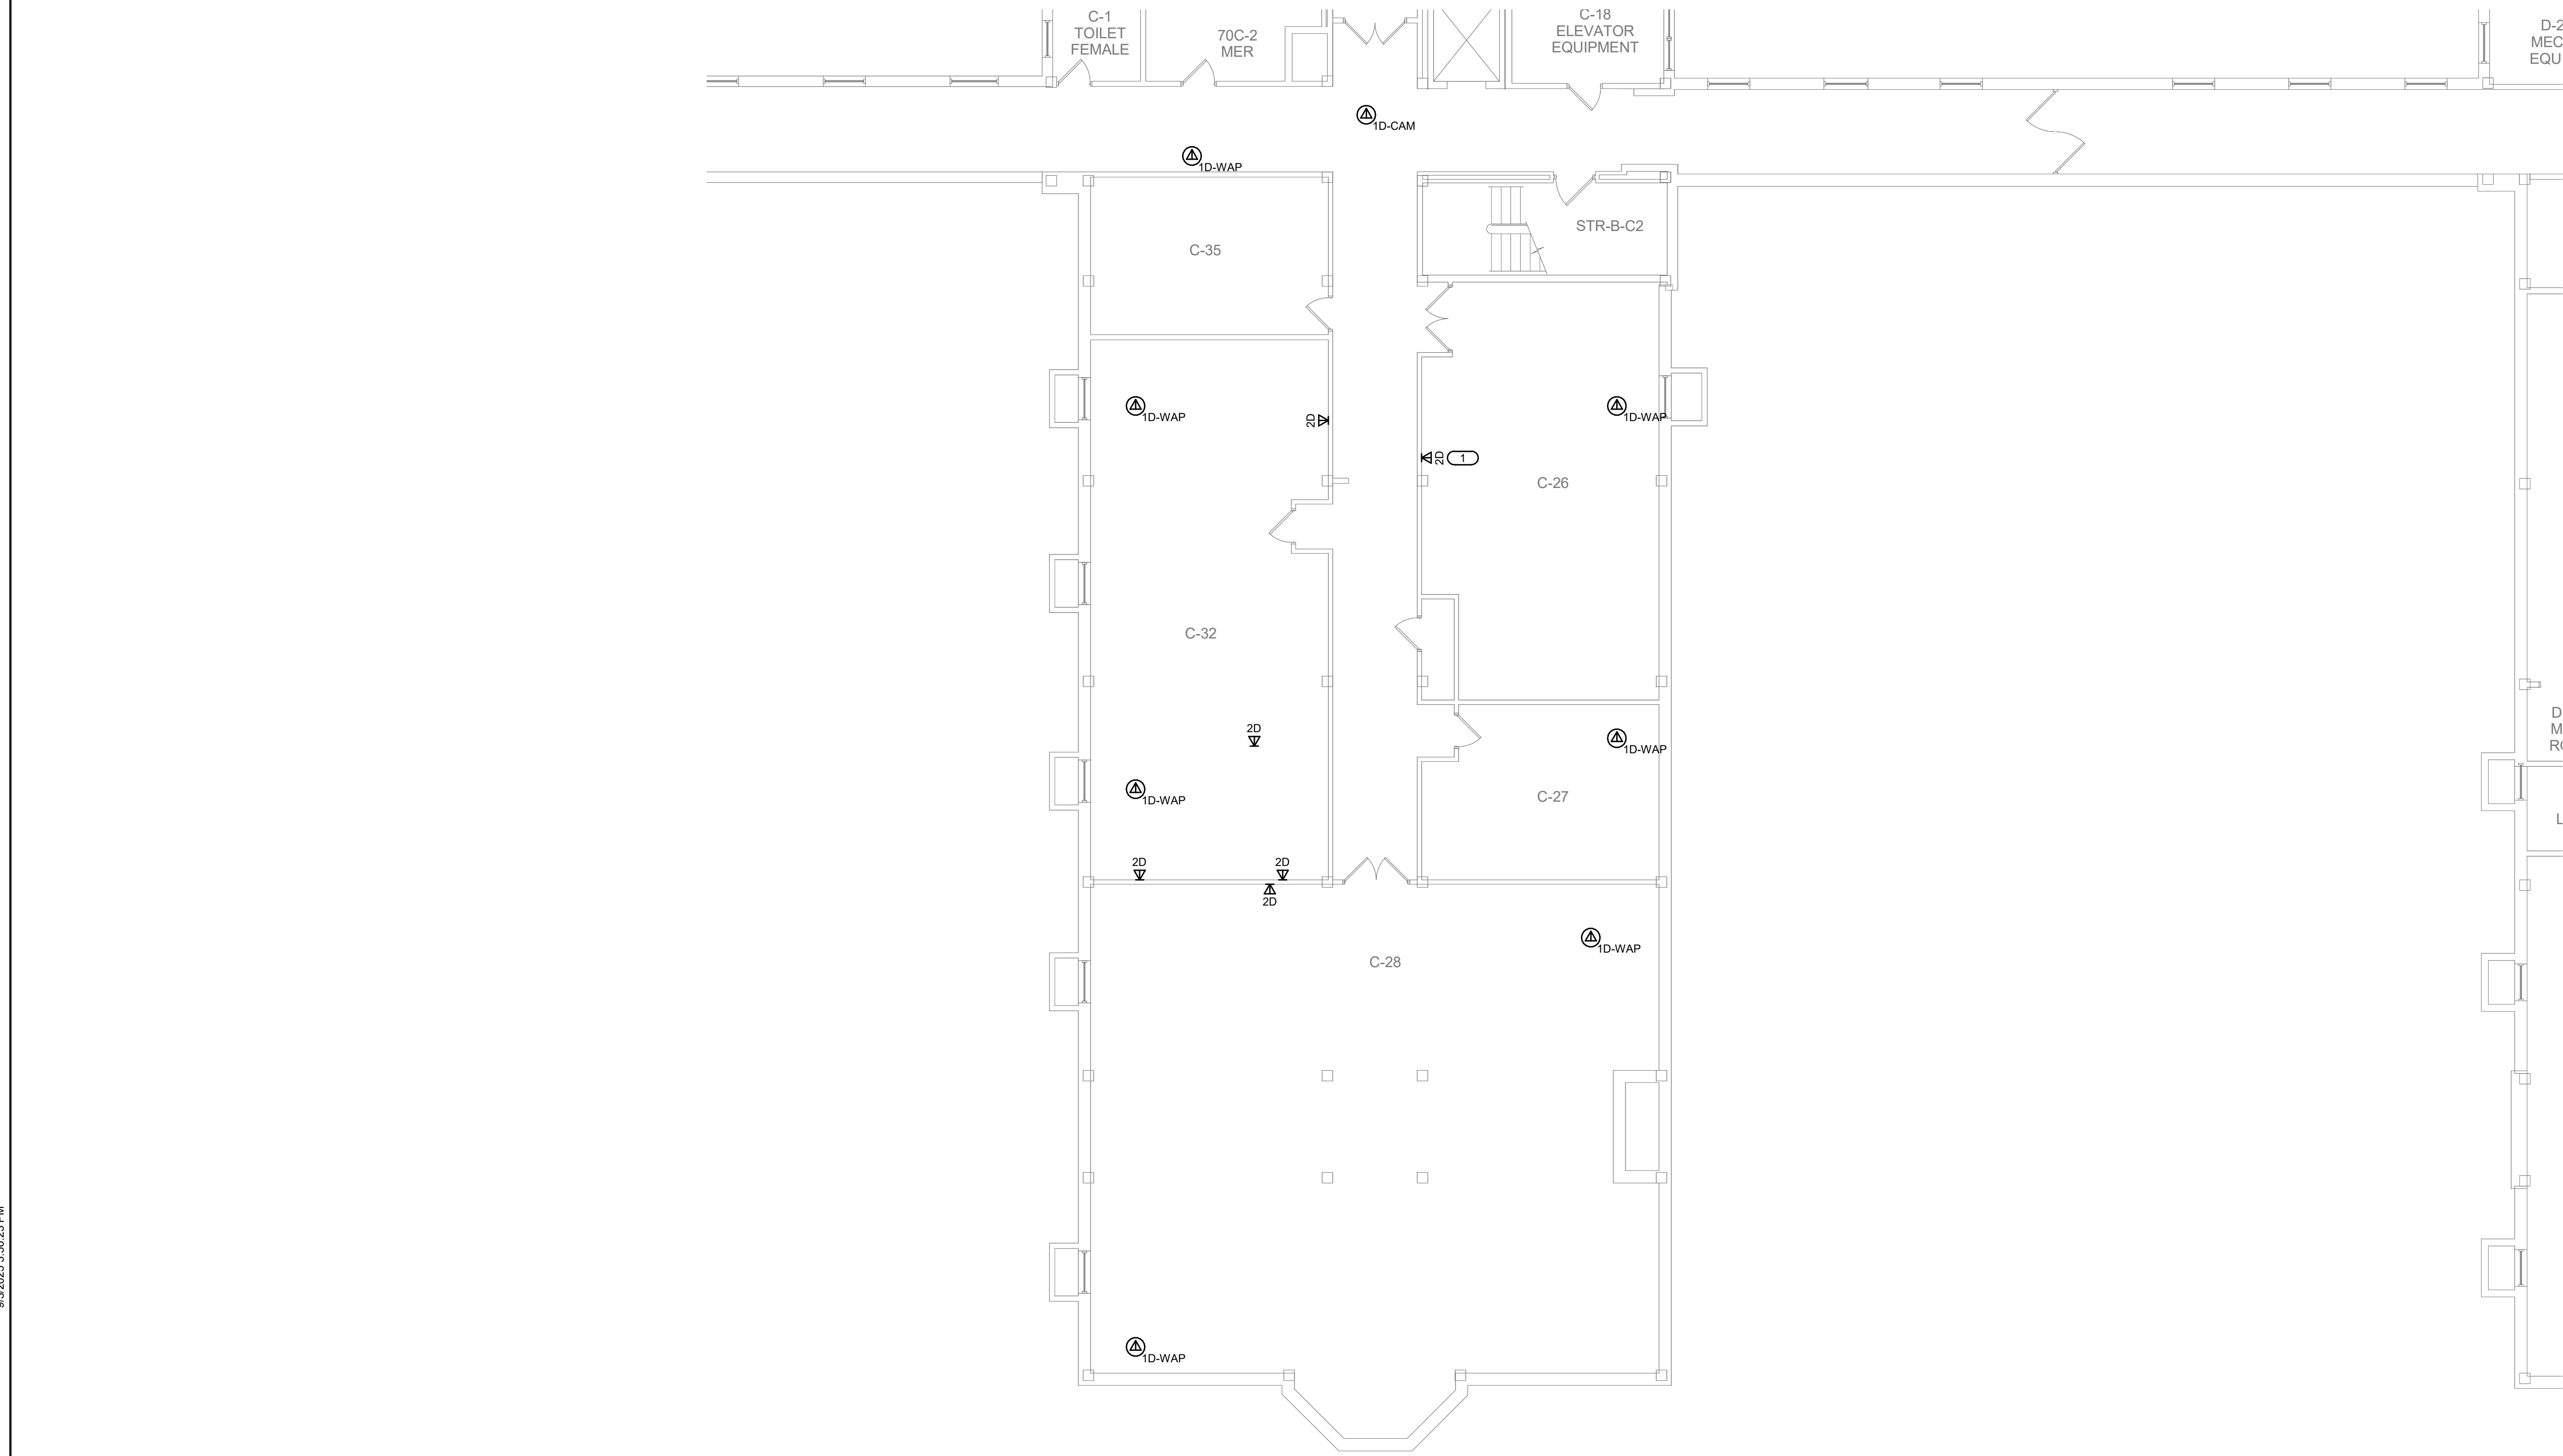

- GENERAL NOTES:**
 - REFER TO 1/TN400 FOR TECHNOLOGY ROUGH IN DETAIL.
 - ALL NETWORK CABLES ON THIS SHEET SHALL TERMINATE IN TR-70-D-125.
 - CONTRACTOR TO PROVIDE NEW J-HOOK ROUTES FOR ALL NEW CABLING. J-HOOK SIZE AND QUANTITY TO BE PER MANUFACTURER RECOMMENDATIONS.
 - REFER TO TN500-TN509 FOR RISER DIAGRAMS.
 - REFER TO SHEET TN402 FOR PENETRATION DETAILS.
 - THESE DRAWINGS MAKE THE BEST ATTEMPT TO IDENTIFY EXISTING DATA DROPS/WORK AREA OUTLETS. AS LONG AS THE TOTAL NEWLY INSTALLED DATA DROP COUNT DOES NOT VARY +/- 10% IDENTIFIED ON THESE DRAWINGS, THE CONTRACTOR'S SCOPE SHALL BE UNCHANGED.
 - NEW WORK AREA OUTLETS SHALL BE LOCATED IN EXISTING BOXES. WORK AREA OUTLETS SHOWN ON THIS SHEET MAY NOT BE IN THE EXACT LOCATION AS IDENTIFIED.
 - CONTRACTOR TO INCLUDE AN ALLOWANCE FOR 10% ADDITIONAL 2-PORTS CAT6A INFORMATION OUTLETS IN THEIR PROPOSAL FOR THIS SHEET. FUTURE INFORMATION OUTLET LOCATIONS WILL BE DETERMINED BY THE VA AT A LATER DATE.
- KEYNOTES:**
 - JCI PACS PANEL LOCATION. GC TO COORDINATE EXACT LOCATION AND HEIGHT WITH COR TO RE-CONNECT TO SWITCHRACK TE IN SAME ROOM WITH CAT6A CABLE AS NECESSARY.

1 BUILDING 70 BASEMENT PLAN - TECHNOLOGY - AREA C SOUTH
1/8" = 1'-0"

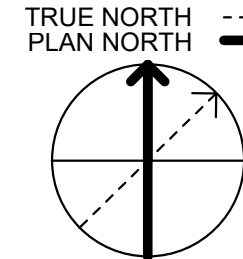

35% SCHEMATIC DESIGN SUBMISSION	5.17.21
65% DESIGN DEVELOPMENT SUBMISSION	6.15.21
65% DESIGN DEVELOPMENT RESUBMISSION	8.25.21
Revisions:	Date:

CONSULTANT



THE FUTURE IS IT'S HERE
www.imegcorp.com
15 SUNNEN DRIVE
SUITE 104
ST. LOUIS, MO 63143
P: 314.645.1132 F: 314.645.1173
PROJECT #18004375.03

ARCHITECT/ENGINEER OF RECORD



Romanyk Consulting
Focusing on what matters
Romanyk Consulting Corp. www.romanykconsulting.com
3308 Preston Road, Suite 350-164, Plano, Texas 75093

STAMP



Office of Construction and Facilities Management

 U.S. Department of Veterans Affairs

Drawing Title
BUILDING 70 BASEMENT PLAN - TECHNOLOGY - AREA C SOUTH

Approved:

Phase
FINAL BID DOCUMENTS

Sprinklered
FULLY SPRINKLERED

Project Title
EHRM INFRASTRUCTURE UPGRADES - MILWAUKEE, WI

Location
5000 W. NATIONAL AVENUE, MILWAUKEE, WI

Issue Date
SEPTEMBER 05, 2025


Checked
PHINIE

Drawn
MAIBEJ

Project Number
695-21-700

Building Number
70

Drawing Number
70-TN100C-S

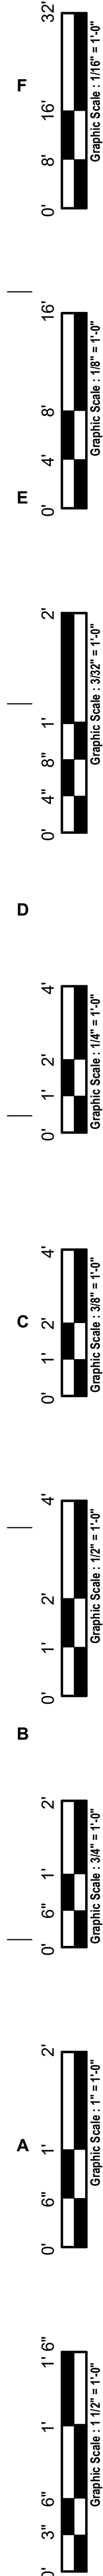

F

E

D


C

B









A

9/2/2025 3:56:24 PM


Autodesk Docs\DCFM East - Milwaukee EHRM (R24)T24_1804375.03_VA MilwEHRM_C.dwt

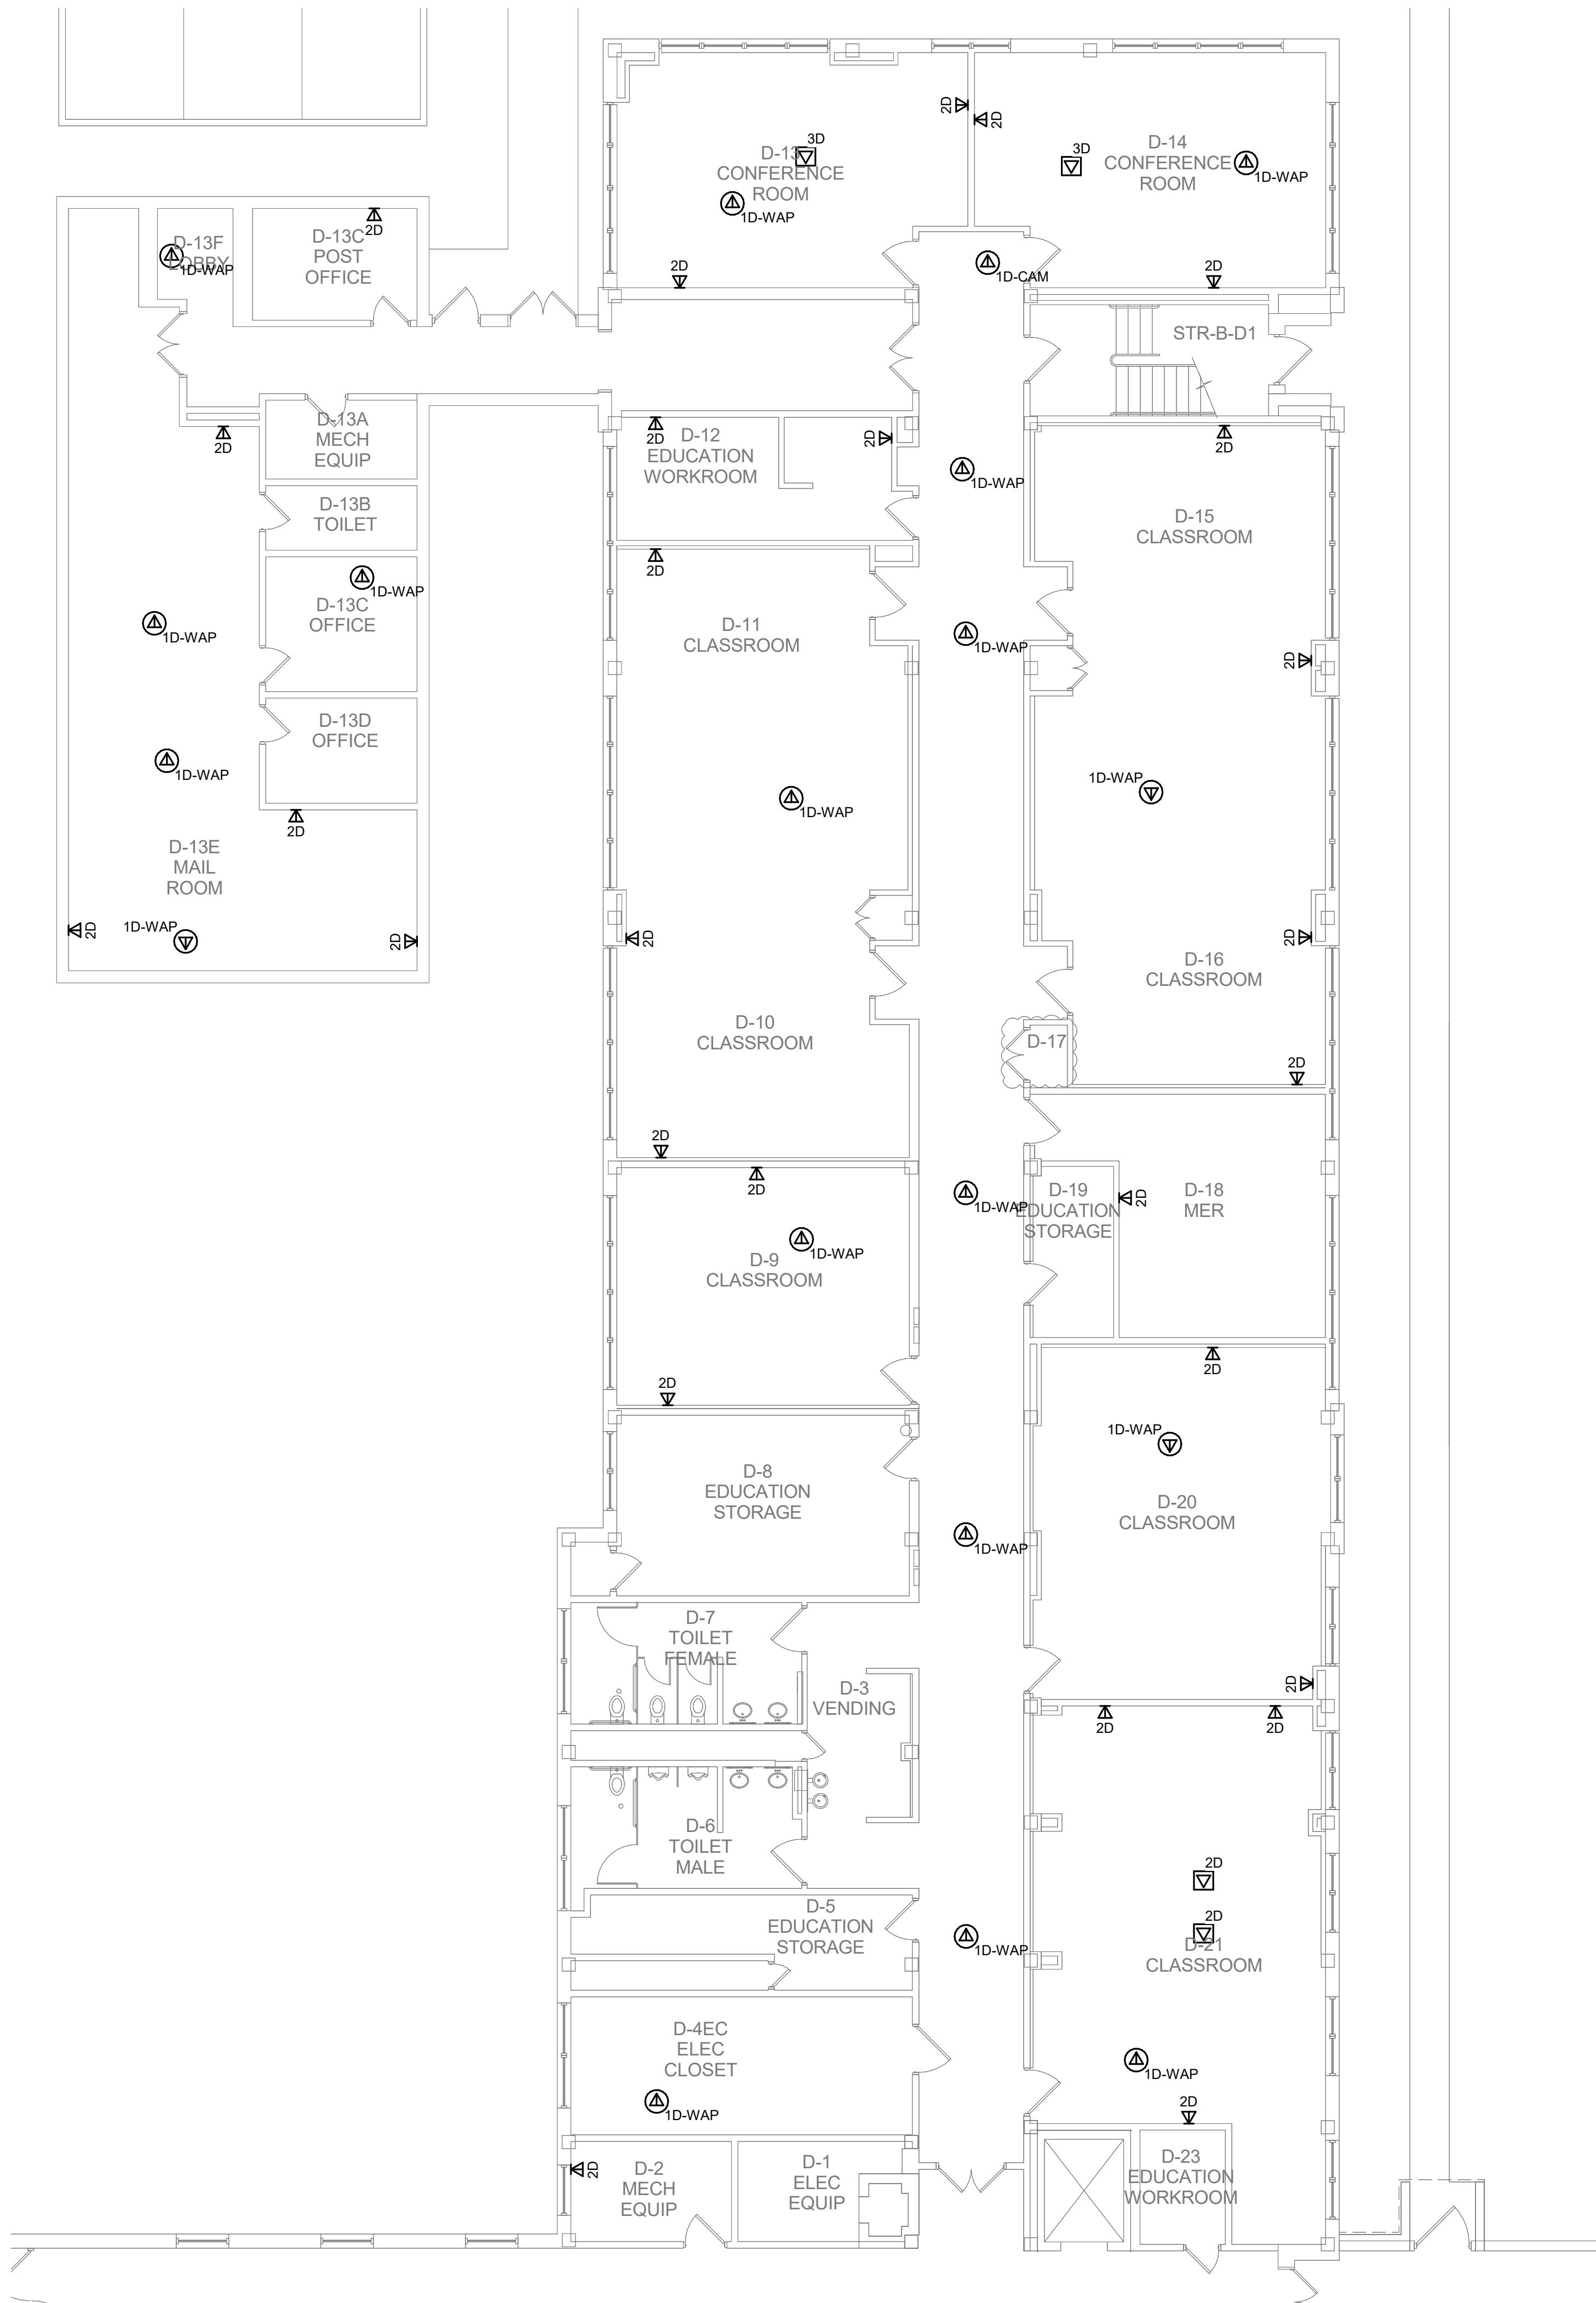

- GENERAL NOTES:**
1. REFER TO 1/TN400 FOR TECHNOLOGY ROUGH IN DETAIL.
 2. ALL NETWORK CABLES ON THIS SHEET SHALL TERMINATE IN TR-70-D-125.
 3. CONTRACTOR TO PROVIDE NEW J-HOOK ROUTES FOR ALL NEW CABLING. J-HOOK SIZE AND QUANTITY TO BE PER MANUFACTURER RECOMMENDATIONS.
 4. REFER TO TN500-TN509 FOR RISER DIAGRAMS.
 5. REFER TO SHEET TN402 FOR PENETRATION DETAILS.
 6. THESE DRAWINGS MAKE THE BEST ATTEMPT TO IDENTIFY EXISTING DATA DROPS/WORK AREA OUTLETS. AS LONG AS THE TOTAL NEWLY INSTALLED DATA DROP COUNT DOES NOT VARY +/- 10% IDENTIFIED ON THESE DRAWINGS, THE CONTRACTOR'S SCOPE SHALL BE UNCHANGED.
 7. NEW WORK AREA OUTLETS SHALL BE LOCATED IN EXISTING BOXES. WORK AREA OUTLETS SHOWN ON THIS SHEET MAY NOT BE IN THE EXACT LOCATION AS IDENTIFIED.
 8. CONTRACTOR TO INCLUDE AN ALLOWANCE FOR 10% ADDITIONAL 2-PORTS CAT6A INFORMATION OUTLETS IN THEIR PROPOSAL FOR THIS SHEET. FUTURE INFORMATION OUTLET LOCATIONS WILL BE DETERMINED BY THE VA AT A LATER DATE.

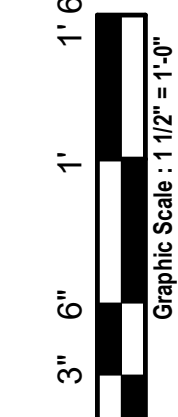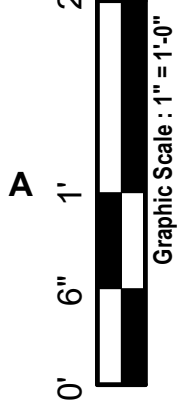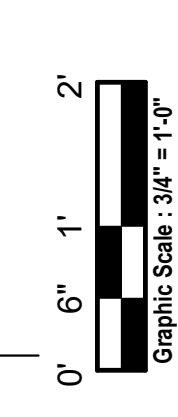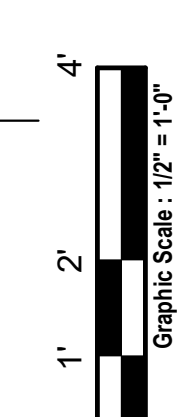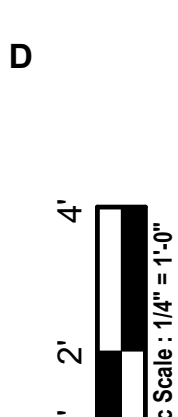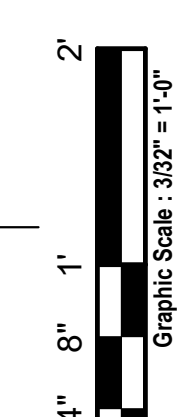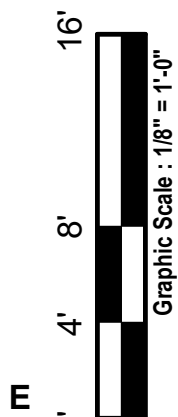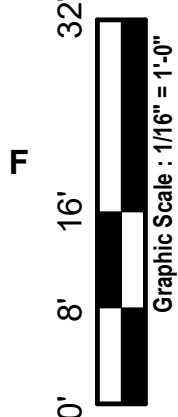

1 BUILDING 70 BASEMENT PLAN - TECHNOLOGY - AREA D NORTH
1/8" = 1'-0"

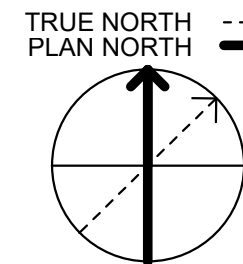

35% SCHEMATIC DESIGN SUBMISSION	5.17.21
65% DESIGN DEVELOPMENT SUBMISSION	6.15.21
65% DESIGN DEVELOPMENT RESUBMISSION	8.25.21
Revisions:	Date:

CONSULTANT

IMEG
The Future is IT Solutions www.imegcorp.com
15 SUNNEN DRIVE
SUITE 104
ST. LOUIS, MO 63143
P: 314.645.1132 F: 314.645.1173
PROJECT #18004375.03

ARCHITECT/ENGINEER OF RECORD

Romanyk Consulting
Focusing on what matters
Romanyk Consulting Corp. www.romanykconsulting.com
3308 Preston Road, Suite 350-164, Plano, Texas 75093

STAMP

Bicsi
DAVID LARSON
BICS1 ID # 106098
Expires 12-31-25
RCBD

Office of
Construction
and Facilities
Management

VA U.S. Department
of Veterans Affairs

Drawing Title BUILDING 70 BASEMENT PLAN - TECHNOLOGY - AREA D NORTH
Approved:

Phase FINAL BID DOCUMENTS
Sprinklered FULLY SPRINKLERED

Project Title EHRM INFRASTRUCTURE UPGRADES - MILWAUKEE, WI
Location 5000 W. NATIONAL AVENUE MILWAUKEE, WI
Issue Date SEPTEMBER 05, 2025
Checked PHINIE
Drawn MAIBEJ

Project Number 695-21-700
Building Number 70
Drawing Number 70-TN100D-N

F

E

D

C

B

A

9/3/2025 3:56:25 PM

Autodesk Docs\DCFM East - Milwaukee EHRM (R24)T24_1804375.03_VA MilwEHRM_C.dwt

- GENERAL NOTES
1.

REFER TO 1/TN400 FOR TECHNOLOGY ROUGH IN DETAIL.
2.

ALL NETWORK CABLES ON THIS SHEET SHALL TERMINATE IN TR-70-E-104.
3.

CONTRACTOR TO PROVIDE NEW J-HOOK ROUTES FOR ALL NEW CABLING. J-HOOK SIZE AND QUANTITY TO BE PER MANUFACTURER RECOMMENDATIONS.
4.

REFER TO TN500-TN509 FOR RISER DIAGRAMS.
5.


REFER TO SHEET TN402 FOR PENETRATION DETAILS.
6.

THESE DRAWINGS MAKE THE BEST ATTEMPT TO IDENTIFY EXISTING DATA DROPS/WORK AREA OUTLETS. AS LONG AS THE TOTAL NEWLY INSTALLED DATA DROP COUNT DOES NOT VARY +/- 10% IDENTIFIED ON THESE DRAWINGS, THE CONTRACTOR'S SCOPE SHALL BE UNCHANGED.
7.

NEW WORK AREA OUTLETS SHALL BE LOCATED IN EXISTING BOXES. WORK AREA OUTLETS SHOWN ON THIS SHEET MAY NOT BE IN THE EXACT LOCATION AS IDENTIFIED.
8.

CONTRACTOR TO INCLUDE AN ALLOWANCE FOR 10% ADDITIONAL 2-PORTS CAT6A INFORMATION OUTLETS IN THEIR PROPOSAL FOR THIS SHEET. FUTURE INFORMATION OUTLET LOCATIONS WILL BE DETERMINED BY THE VA AT A LATER DATE.
- KEYNOTES: (#)
1.

(2) 4" PATHWAYS FROM LEVEL ABOVE.

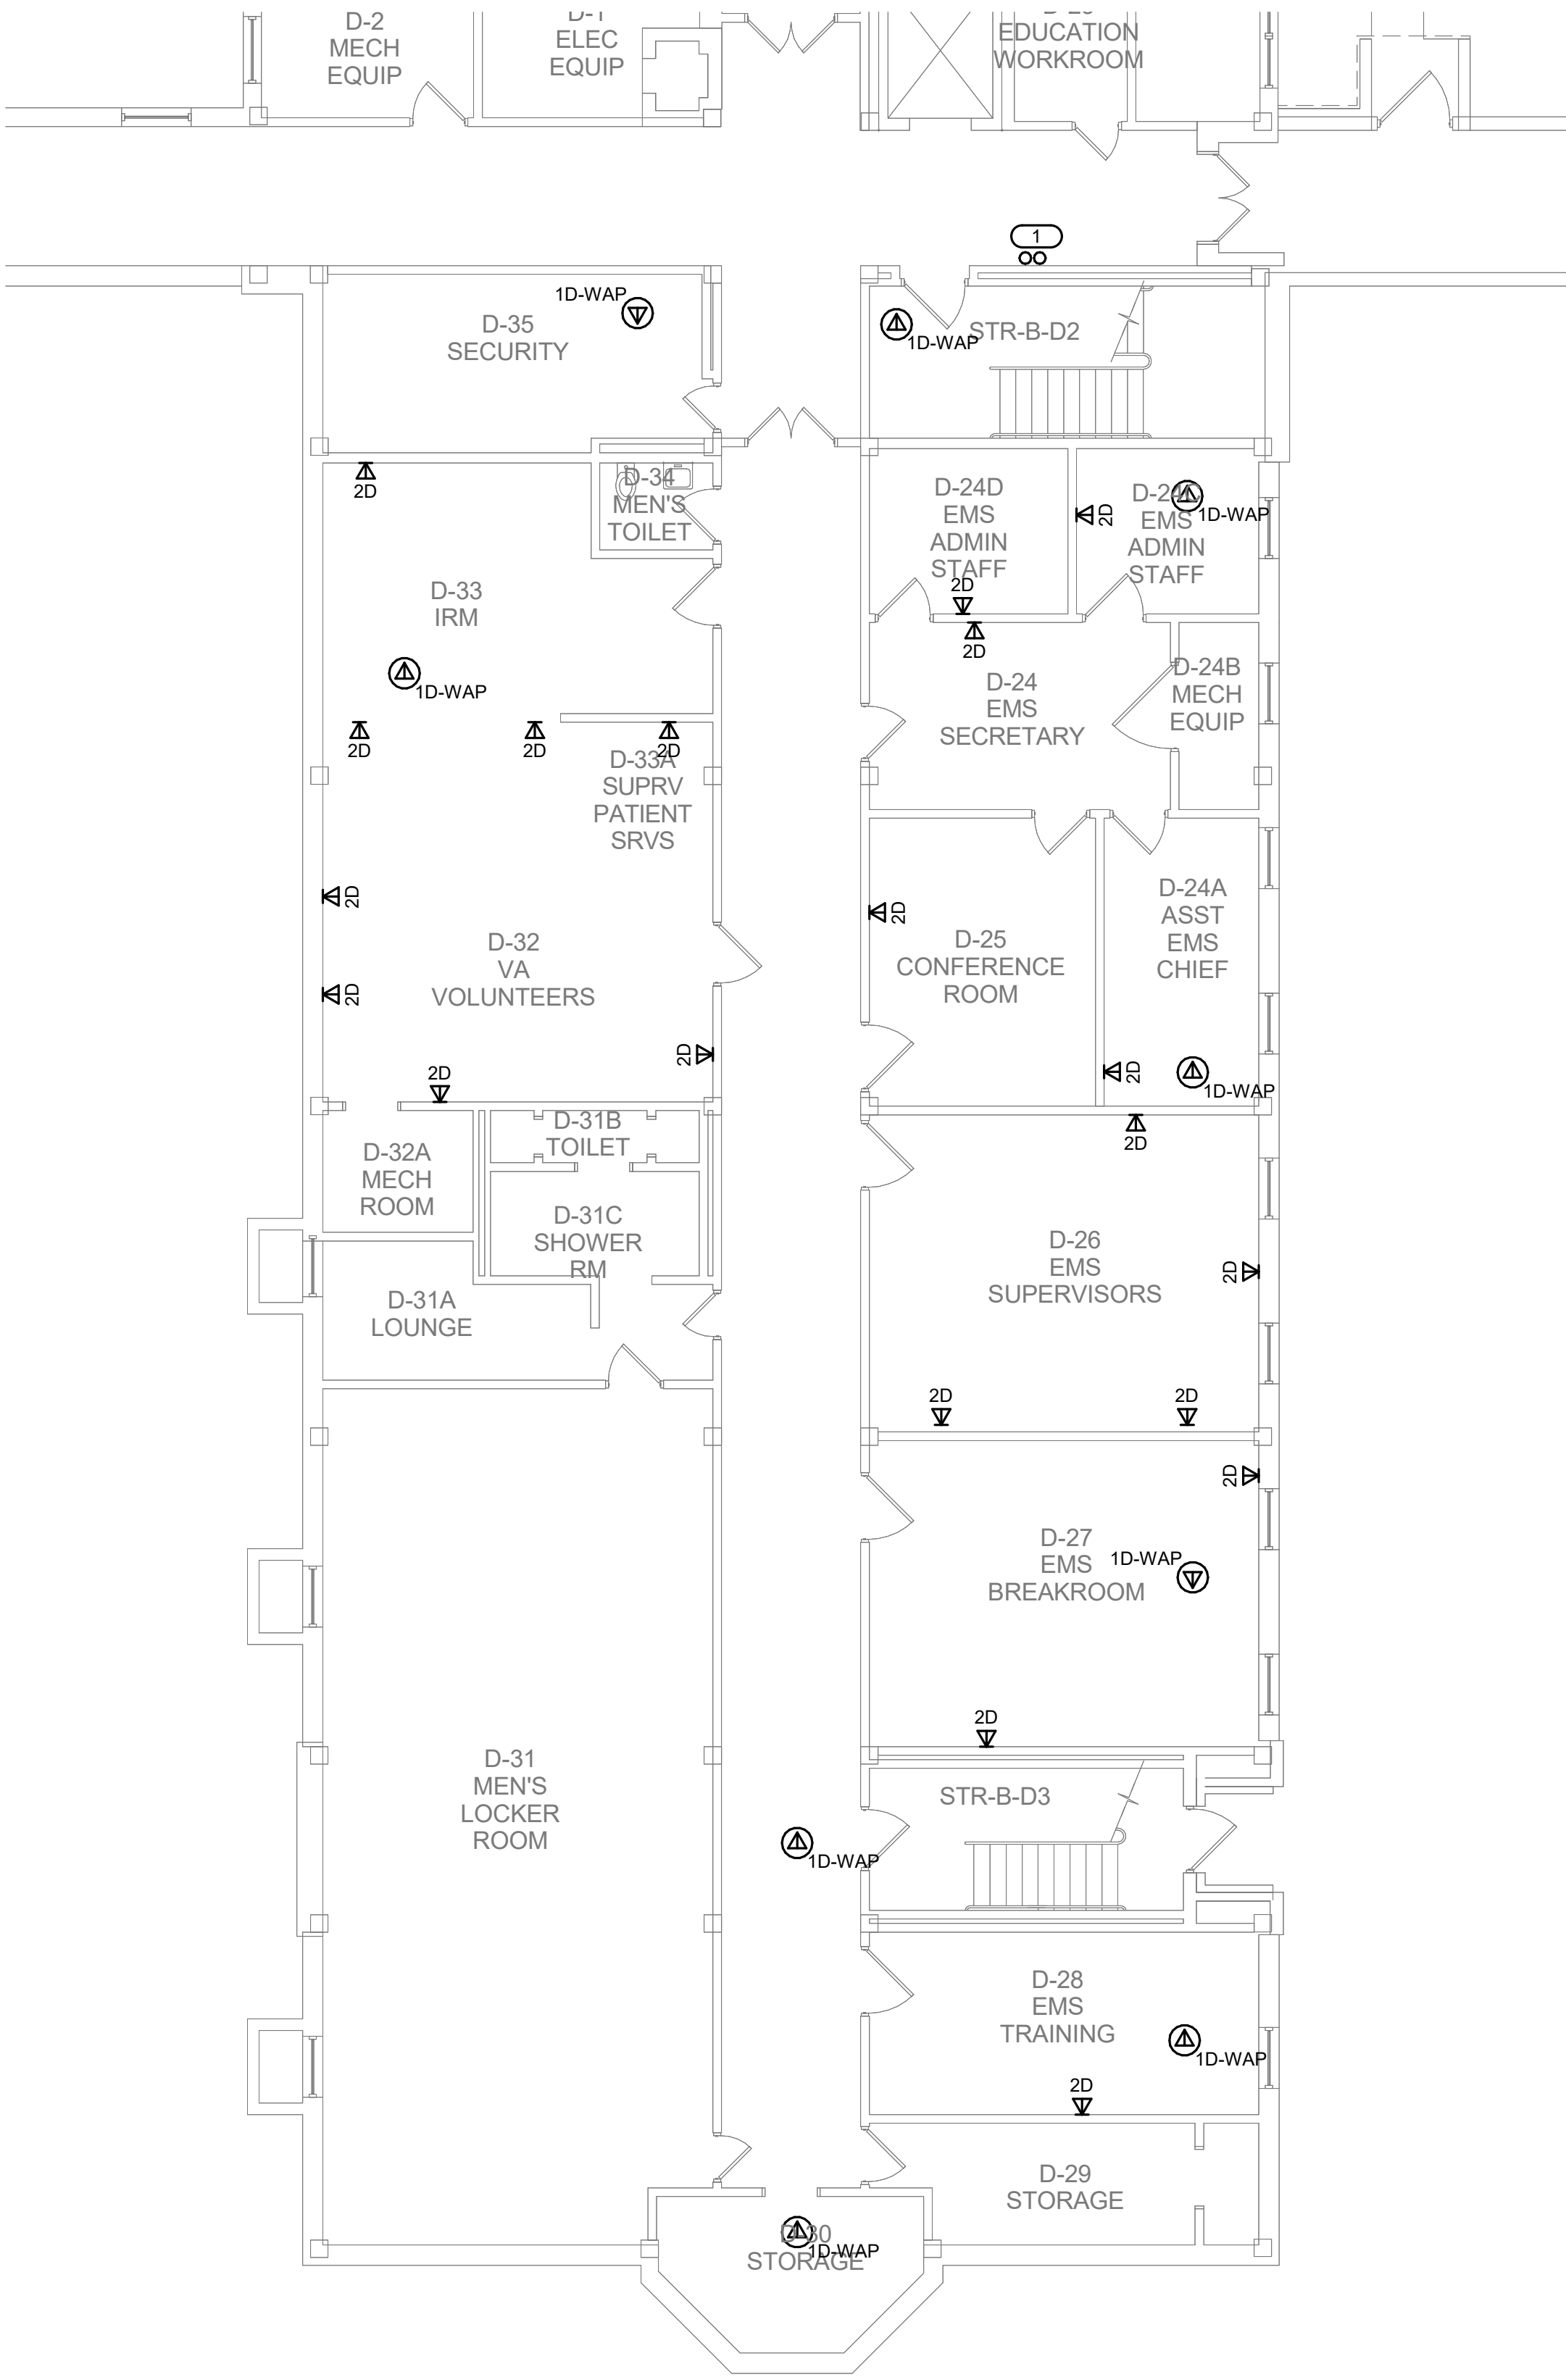

1 BUILDING 70 BASEMENT PLAN - TECHNOLOGY - AREA D SOUTH
1/8" = 1'-0"

35% SCHEMATIC DESIGN SUBMISSION	5.17.21
65% DESIGN DEVELOPMENT SUBMISSION	6.15.21
65% DESIGN DEVELOPMENT RESUBMISSION	8.25.21
Revisions:	Date:

CONSULTANT



THE FUTURE IS IT'S HERE
15 SUNNEN DRIVE
SUITE 104
ST. LOUIS, MO 63143
P: 314.645.1132 F: 314.645.1173
PROJECT #18004375.03

ARCHITECT/ENGINEER OF RECORD



Romanyk Consulting
Focusing on what matters
Romanyk Consulting Corp. www.romanykconsulting.com
3308 Preston Road, Suite 350-164, Plano, Texas 75093

STAMP



Office of
Construction
and Facilities
Management



 U.S. Department
of Veterans Affairs

Drawing Title BUILDING 70 BASEMENT PLAN - TECHNOLOGY - AREA D SOUTH
Approved:

Phase FINAL BID DOCUMENTS
Sprinklered FULLY SPRINKLERED

Project Title EHRM INFRASTRUCTURE UPGRADES - MILWAUKEE, WI
Location 5000 W. NATIONAL AVENUE, MILWAUKEE, WI
Issue Date SEPTEMBER 05, 2025
Checked PHINIE
Drawn MAIBEJ

Project Number 695-21-700
Building Number 70
Drawing Number 70-TN100D-S

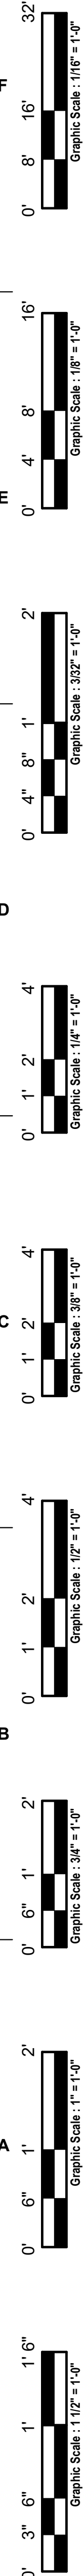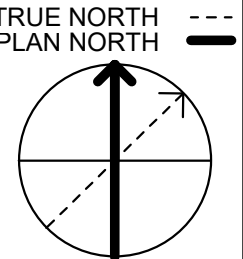

F

E

D


C

B

A


9/2/2025 3:45:26 PM

Autodesk Docs\DCFM East - Milwaukee EHRM (R24)T24_1804375.03_VA MilvEHRM_C.dwt

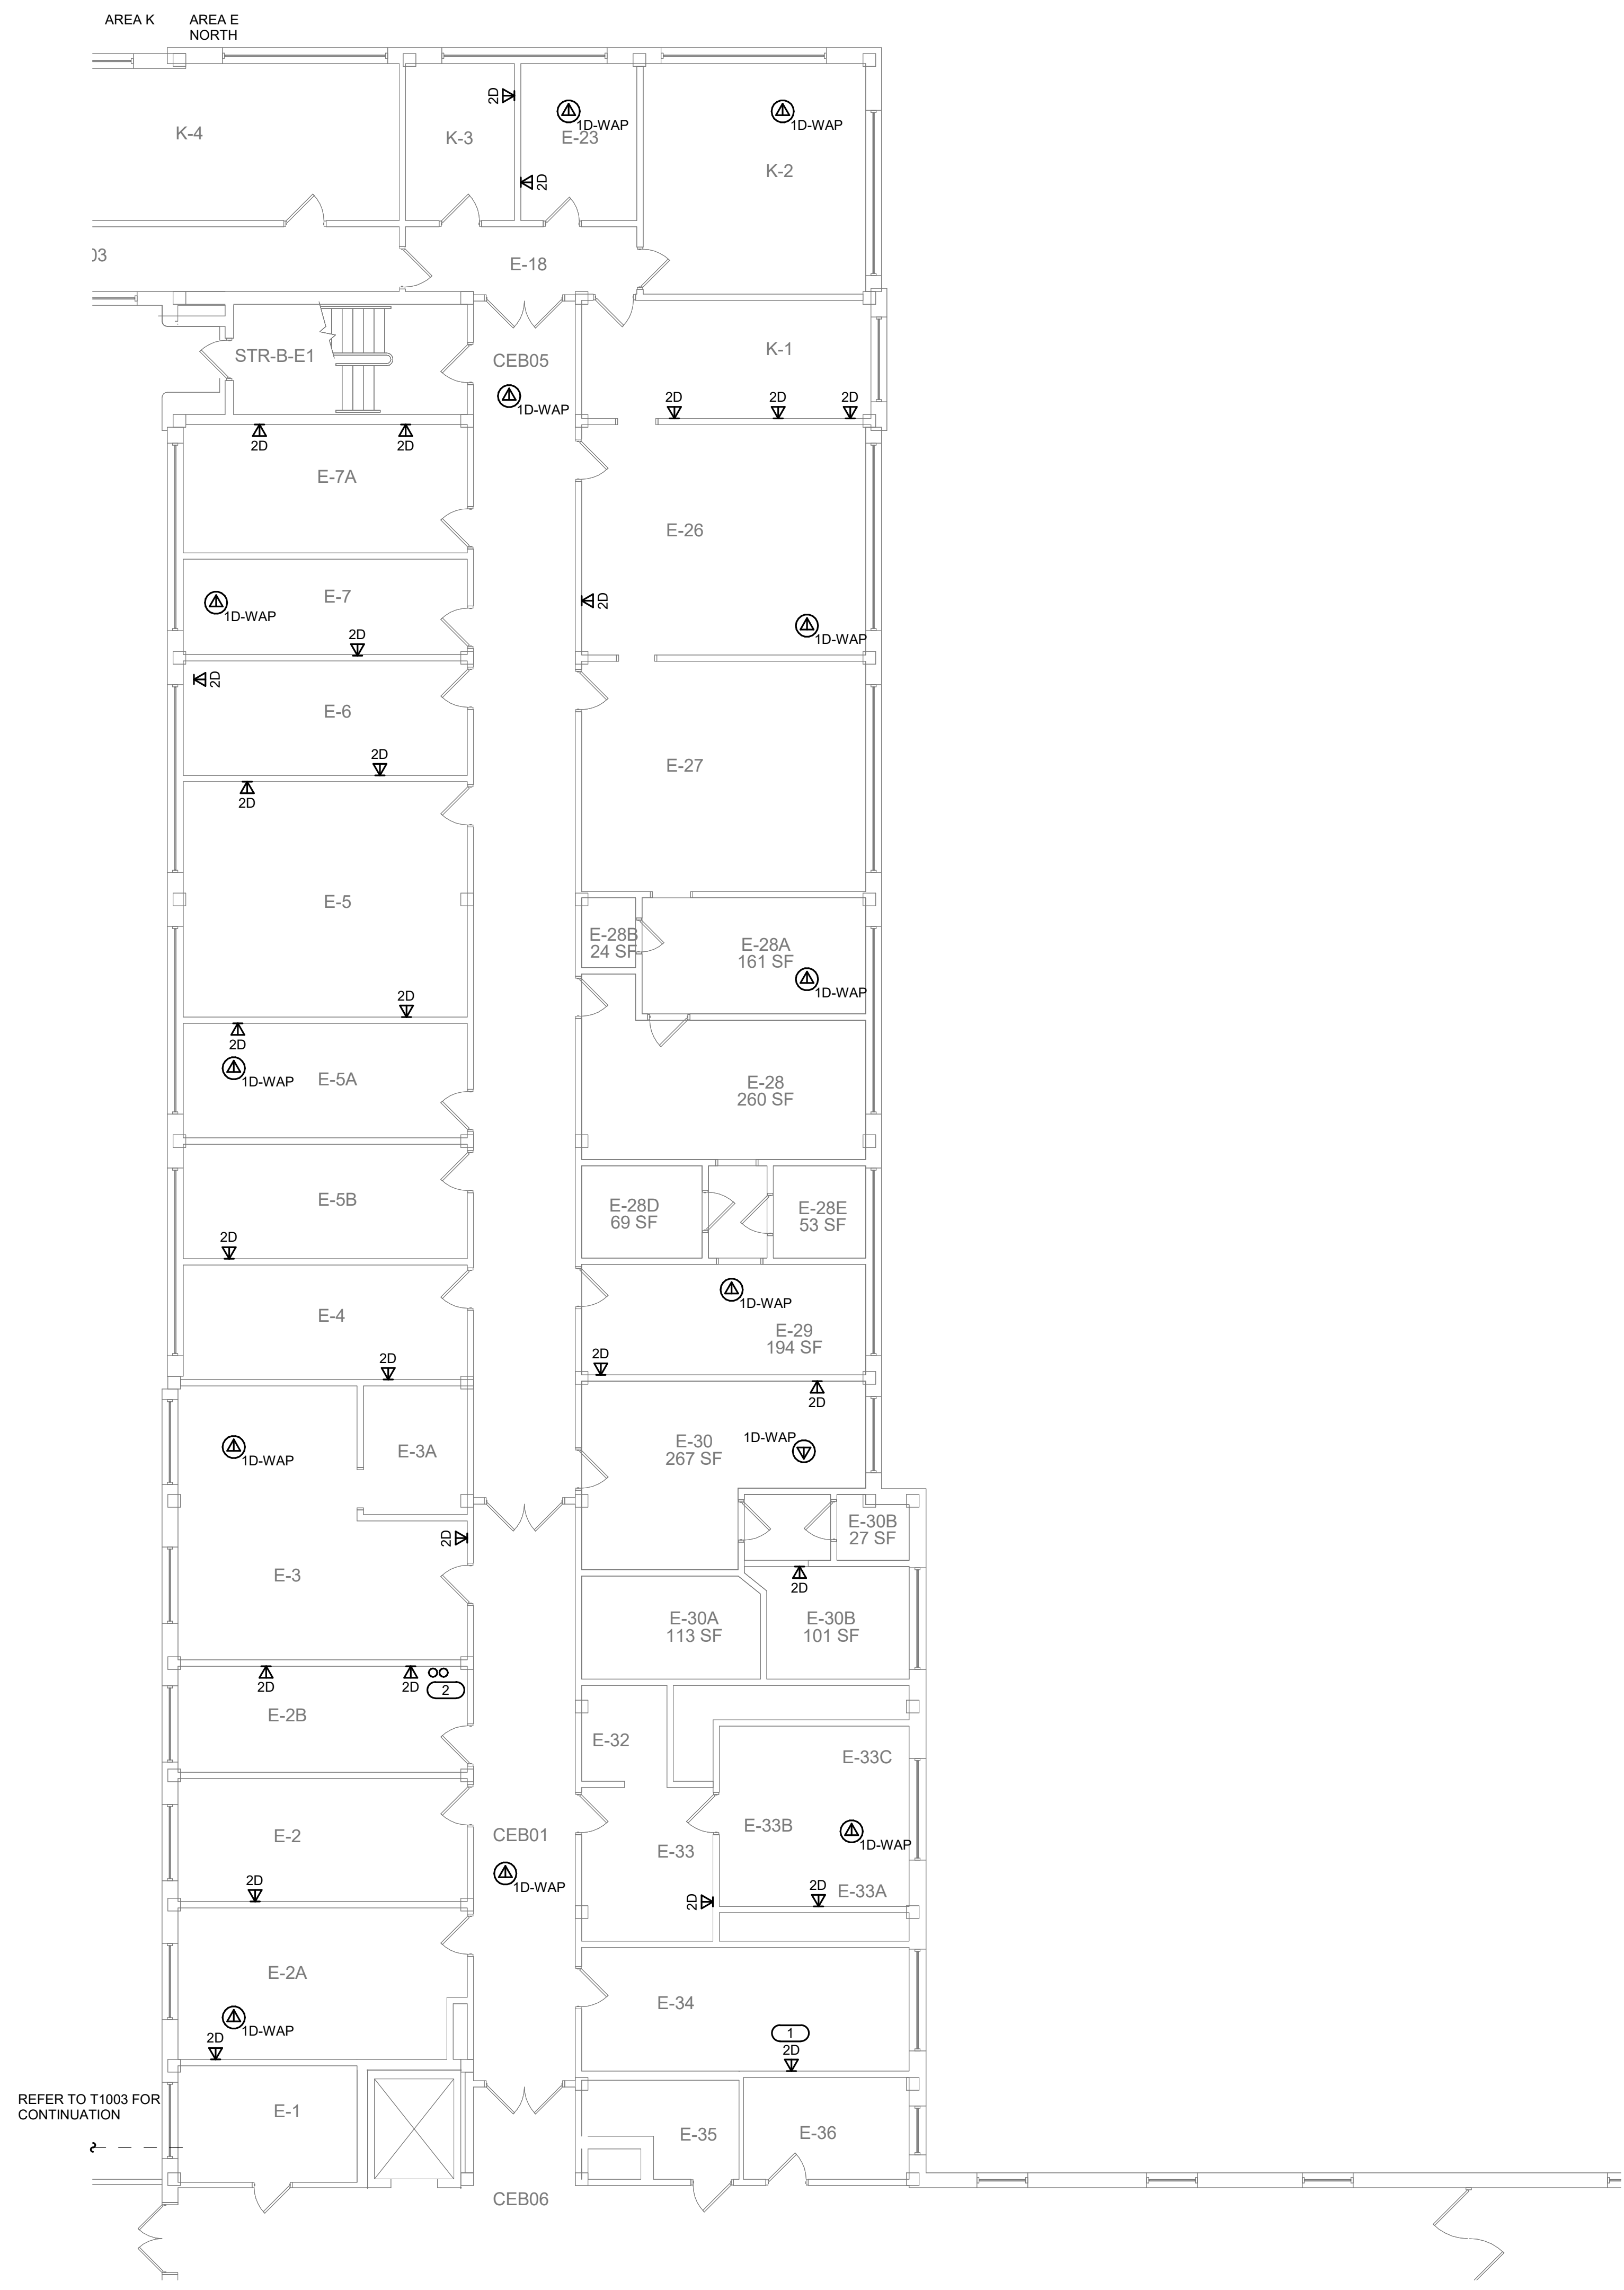


- GENERAL NOTES:**
1. REFER TO 1/TN400 FOR TECHNOLOGY ROUGH IN DETAIL.
 2. ALL NETWORK CABLES ON THIS SHEET SHALL TERMINATE IN TR70-B-159.
 3. CONTRACTOR TO PROVIDE NEW J-HOOK ROUTES FOR ALL NEW CABLING. J-HOOK SIZE AND QUANTITY TO BE PER MANUFACTURER RECOMMENDATIONS.
 4. REFER TO TN500-TN509 FOR RISER DIAGRAMS.
 5. REFER TO SHEET TN402 FOR PENETRATION DETAILS.
 6. THESE DRAWINGS MAKE THE BEST ATTEMPT TO IDENTIFY EXISTING DATA DROPS/WORK AREA OUTLETS. AS LONG AS THE TOTAL NEWLY INSTALLED DATA DROP COUNT DOES NOT VARY +/- 10% IDENTIFIED ON THESE DRAWINGS, THE CONTRACTOR'S SCOPE SHALL BE UNCHANGED.
 7. NEW WORK AREA OUTLETS SHALL BE LOCATED IN EXISTING BOXES. WORK AREA OUTLETS SHOWN ON THIS SHEET MAY NOT BE IN THE EXACT LOCATION AS IDENTIFIED.
 8. CONTRACTOR TO INCLUDE AN ALLOWANCE FOR 10% ADDITIONAL 2-PORTS CAT6A INFORMATION OUTLETS IN THEIR PROPOSAL FOR THIS SHEET. FUTURE INFORMATION OUTLET LOCATIONS WILL BE DETERMINED BY THE VA AT A LATER DATE.

- KEYNOTES:** (#)
1. JCI PACS PANEL LOCATION. GC TO COORDINATE EXACT LOCATION AND HEIGHT WITH COR TO RE-CONNECT TO SWITCH/RACK TE IN SAME ROOM WITH CAT6A CABLE AS NECESSARY.
 2. (2) 4" PATHWAYS FROM LEVEL ABOVE.

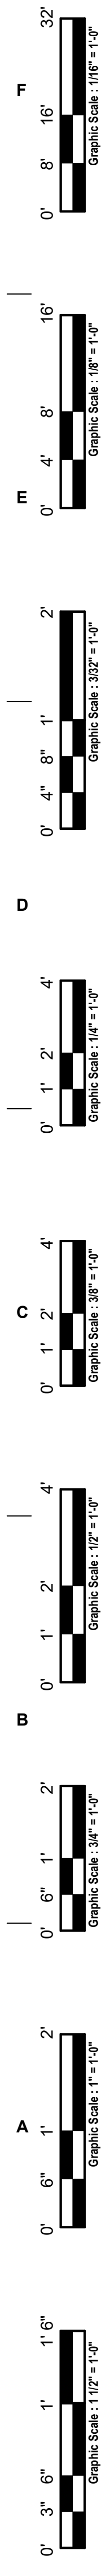

1 BUILDING 70 BASEMENT PLAN - TECHNOLOGY - AREA E NORTH
1/8" = 1'-0"

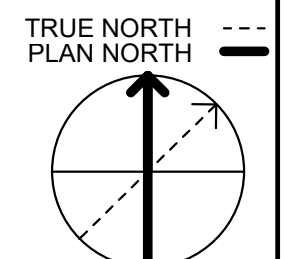

35% SCHEMATIC DESIGN SUBMISSION	5.17.21
65% DESIGN DEVELOPMENT SUBMISSION	6.15.21
65% DESIGN DEVELOPMENT RESUBMISSION	8.25.21
Revisions:	Date:

CONSULTANT

IMEG
15 SUNNEN DRIVE
SUITE 104
ST. LOUIS, MO 63143
P: 314.645.1132 F: 314.645.1173
PROJECT #18004375.03

ARCHITECT/ENGINEER OF RECORD

Romanyk Consulting
Focusing on what matters

Romanyk Consulting Corp. www.romanykconsulting.com
3308 Preston Road, Suite 350-164, Plano, Texas 75093

STAMP

Bicsi
DAVID LARSON
BICS1 ID # 106098
EXPIRES 12-31-25

Office of
Construction
and Facilities
Management

VA U.S. Department
of Veterans Affairs

Drawing Title
BUILDING 70 BASEMENT PLAN - TECHNOLOGY -
AREA E NORTH

Approved:

Phase
FINAL BID DOCUMENTS

Sprinklered
FULLY SPRINKLERED

Project Title
EHRM INFRASTRUCTURE
UPGRADES - MILWAUKEE, WI

Location
5000 W. NATIONAL AVENUE MILWAUKEE, WI

Issue Date
SEPTEMBER 05, 2025

Checked
PHINIE

Drawn
MAIBEJ

Project Number
695-21-700

Building Number
70

Drawing Number
70-TN100E-N

F

E

D

C


B

A


9/3/2025 3:56:27 PM

Autodesk Docs\DCFM East - Milwaukee EHRM (R24)T24_1804375.03_VA Milwaukee_C.dwg

- GENERAL NOTES:
1. REFER TO 1/TN400 FOR TECHNOLOGY ROUGH IN DETAIL.
 2. ALL NETWORK CABLES ON THIS SHEET SHALL TERMINATE IN TR-70-B-159.
 3. CONTRACTOR TO PROVIDE NEW J-HOOK ROUTES FOR ALL NEW CABLING. J-HOOK SIZE AND QUANTITY TO BE PER MANUFACTURER RECOMMENDATIONS.
 4. REFER TO TN500-TN509 FOR RISER DIAGRAMS.
 5. REFER TO SHEET TN402 FOR PENETRATION DETAILS.
 6. THESE DRAWINGS MAKE THE BEST ATTEMPT TO IDENTIFY EXISTING DATA DROPS/WORK AREA OUTLETS. AS LONG AS THE TOTAL NEWLY INSTALLED DATA DROP COUNT DOES NOT VARY +/- 10% IDENTIFIED ON THESE DRAWINGS, THE CONTRACTOR'S SCOPE SHALL BE UNCHANGED.
 7. NEW WORK AREA OUTLETS SHALL BE LOCATED IN EXISTING BOXES. WORK AREA OUTLETS SHOWN ON THIS SHEET MAY NOT BE IN THE EXACT LOCATION AS IDENTIFIED.
 8. CONTRACTOR TO INCLUDE AN ALLOWANCE FOR 10% ADDITIONAL 2-PORTS DATA INFORMATION OUTLETS IN THEIR PROPOSAL FOR THIS SHEET. FUTURE INFORMATION OUTLET LOCATIONS WILL BE DETERMINED BY THE VA AT A LATER DATE.

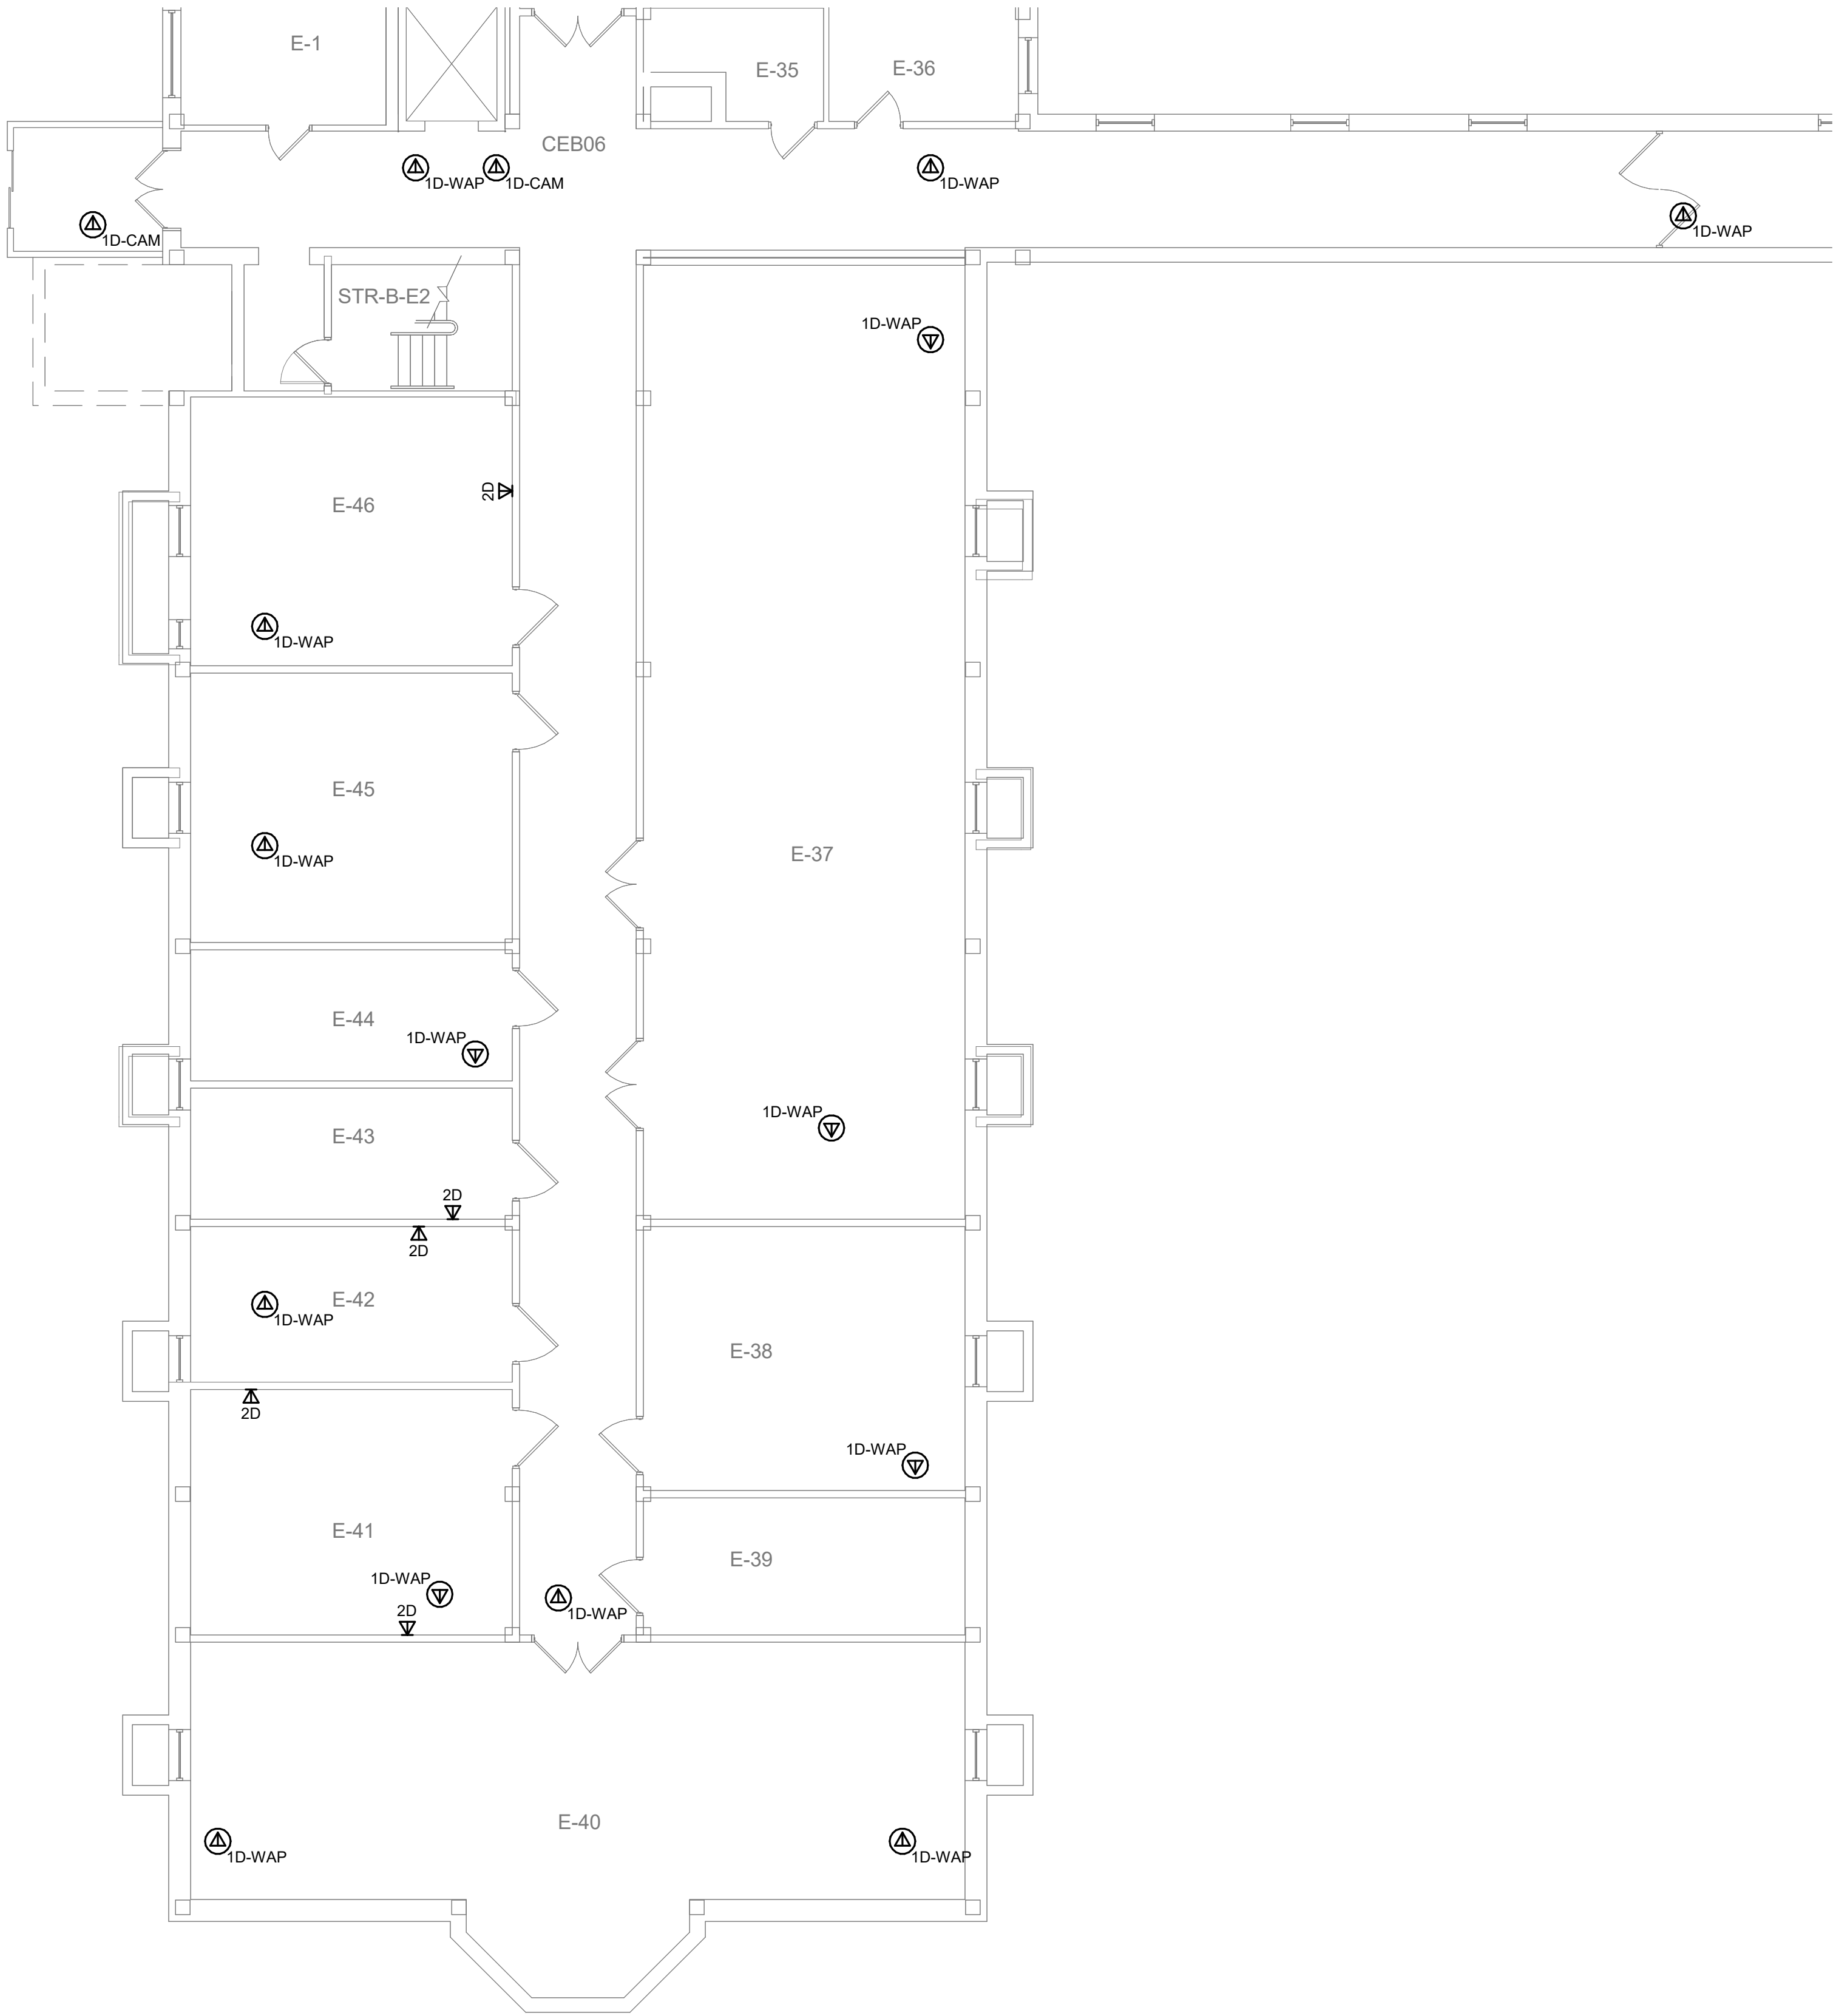

1 BUILDING 70 BASEMENT PLAN - TECHNOLOGY - AREA E SOUTH
1/8" = 1'-0"

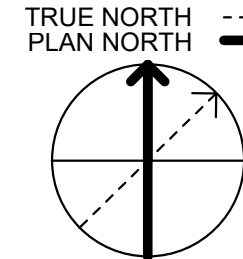

35% SCHEMATIC DESIGN SUBMISSION	5.17.21
65% DESIGN DEVELOPMENT SUBMISSION	6.15.21
65% DESIGN DEVELOPMENT RESUBMISSION	8.25.21
Revisions:	Date:

CONSULTANT

IMEG

15 SUNNEN DRIVE
SUITE 104
ST. LOUIS, MO 63143
P: 314.645.1132 F: 314.645.1173
PROJECT #18004375.03

ARCHITECT/ENGINEER OF RECORD

Romanyk Consulting
Focusing on what matters

Romanyk Consulting Corp. www.romanykconsulting.com
3308 Preston Road, Suite 350-164, Plano, Texas 75093

STAMP

Bicsi
DAVID LARSON
BICS1 ID # 106098
EXPIRES 12-31-25

Office of
Construction
and Facilities
Management

VA U.S. Department
of Veterans Affairs

Drawing Title
BUILDING 70 BASEMENT PLAN - TECHNOLOGY -
AREA E SOUTH

Approved:

Phase
FINAL BID DOCUMENTS

Sprinklered
FULLY SPRINKLERED

Project Title
EHRM INFRASTRUCTURE
UPGRADES - MILWAUKEE, WI

Location
5000 W. NATIONAL AVENUE, MILWAUKEE, WI

Issue Date
SEPTEMBER 05, 2025

Checked
PHINIE

Drawn
MAIBEJ

Project Number
695-21-700

Building Number
70

Drawing Number
70-TN100E-S

F

E

D

C

B

A

9/3/2025 3:56:28 PM

Autodesk Docs\DCFM East - Milwaukee EHRM (R24)T24_1804375\03_VA Milwaukee_C.dwt

- GENERAL NOTES
1. REFER TO 1/TN400 FOR TECHNOLOGY ROUGH IN DETAIL.

2. ALL NETWORK CABLES ON THIS SHEET SHALL TERMINATE IN TR-70-E-104.

3. CONTRACTOR TO PROVIDE NEW J-HOOK ROUTES FOR ALL NEW CABLING. J-HOOK SIZE AND QUANTITY TO BE PER MANUFACTURER RECOMMENDATIONS.

4. REFER TO TN500-TN509 FOR RISER DIAGRAMS.

5. REFER TO SHEET TN402 FOR PENETRATION DETAILS.

6. THESE DRAWINGS MAKE THE BEST ATTEMPT TO IDENTIFY EXISTING DATA DROPS/WORK AREA OUTLETS. AS LONG AS THE TOTAL NEWLY INSTALLED DATA DROP COUNT DOES NOT VARY +/- 10% IDENTIFIED ON THESE DRAWINGS, THE CONTRACTOR'S SCOPE SHALL BE UNCHANGED.

7. NEW WORK AREA OUTLETS SHALL BE LOCATED IN EXISTING BOXES. WORK AREA OUTLETS SHOWN ON THIS SHEET MAY NOT BE IN THE EXACT LOCATION AS IDENTIFIED.

8. CONTRACTOR TO INCLUDE AN ALLOWANCE FOR 10% ADDITIONAL 2-PORTS CAT6A INFORMATION OUTLETS IN THEIR PROPOSAL FOR THIS SHEET. FUTURE INFORMATION OUTLET LOCATIONS WILL BE DETERMINED BY THE VA AT A LATER DATE.



1

BUILDING 70 BASEMENT PLAN - TECHNOLOGY - AREA K

1/8" = 1'-0"

35% SCHEMATIC DESIGN SUBMISSION	5.17.21
65% DESIGN DEVELOPMENT SUBMISSION	6.15.21
65% DESIGN DEVELOPMENT RESUBMISSION	8.25.21
Revisions:	Date:

CONSULTANT



IMEG

The Future is Full of Possibilities

www.imegcorp.com

15 SUNNEN DRIVE

SUITE 104

ST. LOUIS, MO 63143

P: 314.645.1132 F: 314.645.1173

PROJECT #18004375.03

ARCHITECT/ENGINEER OF RECORD



Romanyk Consulting

Focusing on what matters

Romanyk Consulting Corp.

www.romanykconsulting.com

3308 Preston Road, Suite 350-164, Plano, Texas 75093

STAMP



Office of
Construction
and Facilities
Management

VA

U.S. Department
of Veterans Affairs

Drawing Title

BUILDING 70 BASEMENT PLAN - TECHNOLOGY - AREA K

Approved:

Phase

FINAL BID DOCUMENTS

Sprinklered

FULLY SPRINKLERED

Project Title

EHRM INFRASTRUCTURE UPGRADES - MILWAUKEE, WI

Location

5000 W. NATIONAL AVENUE, MILWAUKEE, WI

Issue Date

SEPTEMBER 05, 2025

Checked

PHINIE

Drawn

MAIBEJ

Project Number

695-21-700

Building Number

70

Drawing Number

70-TN100K

