



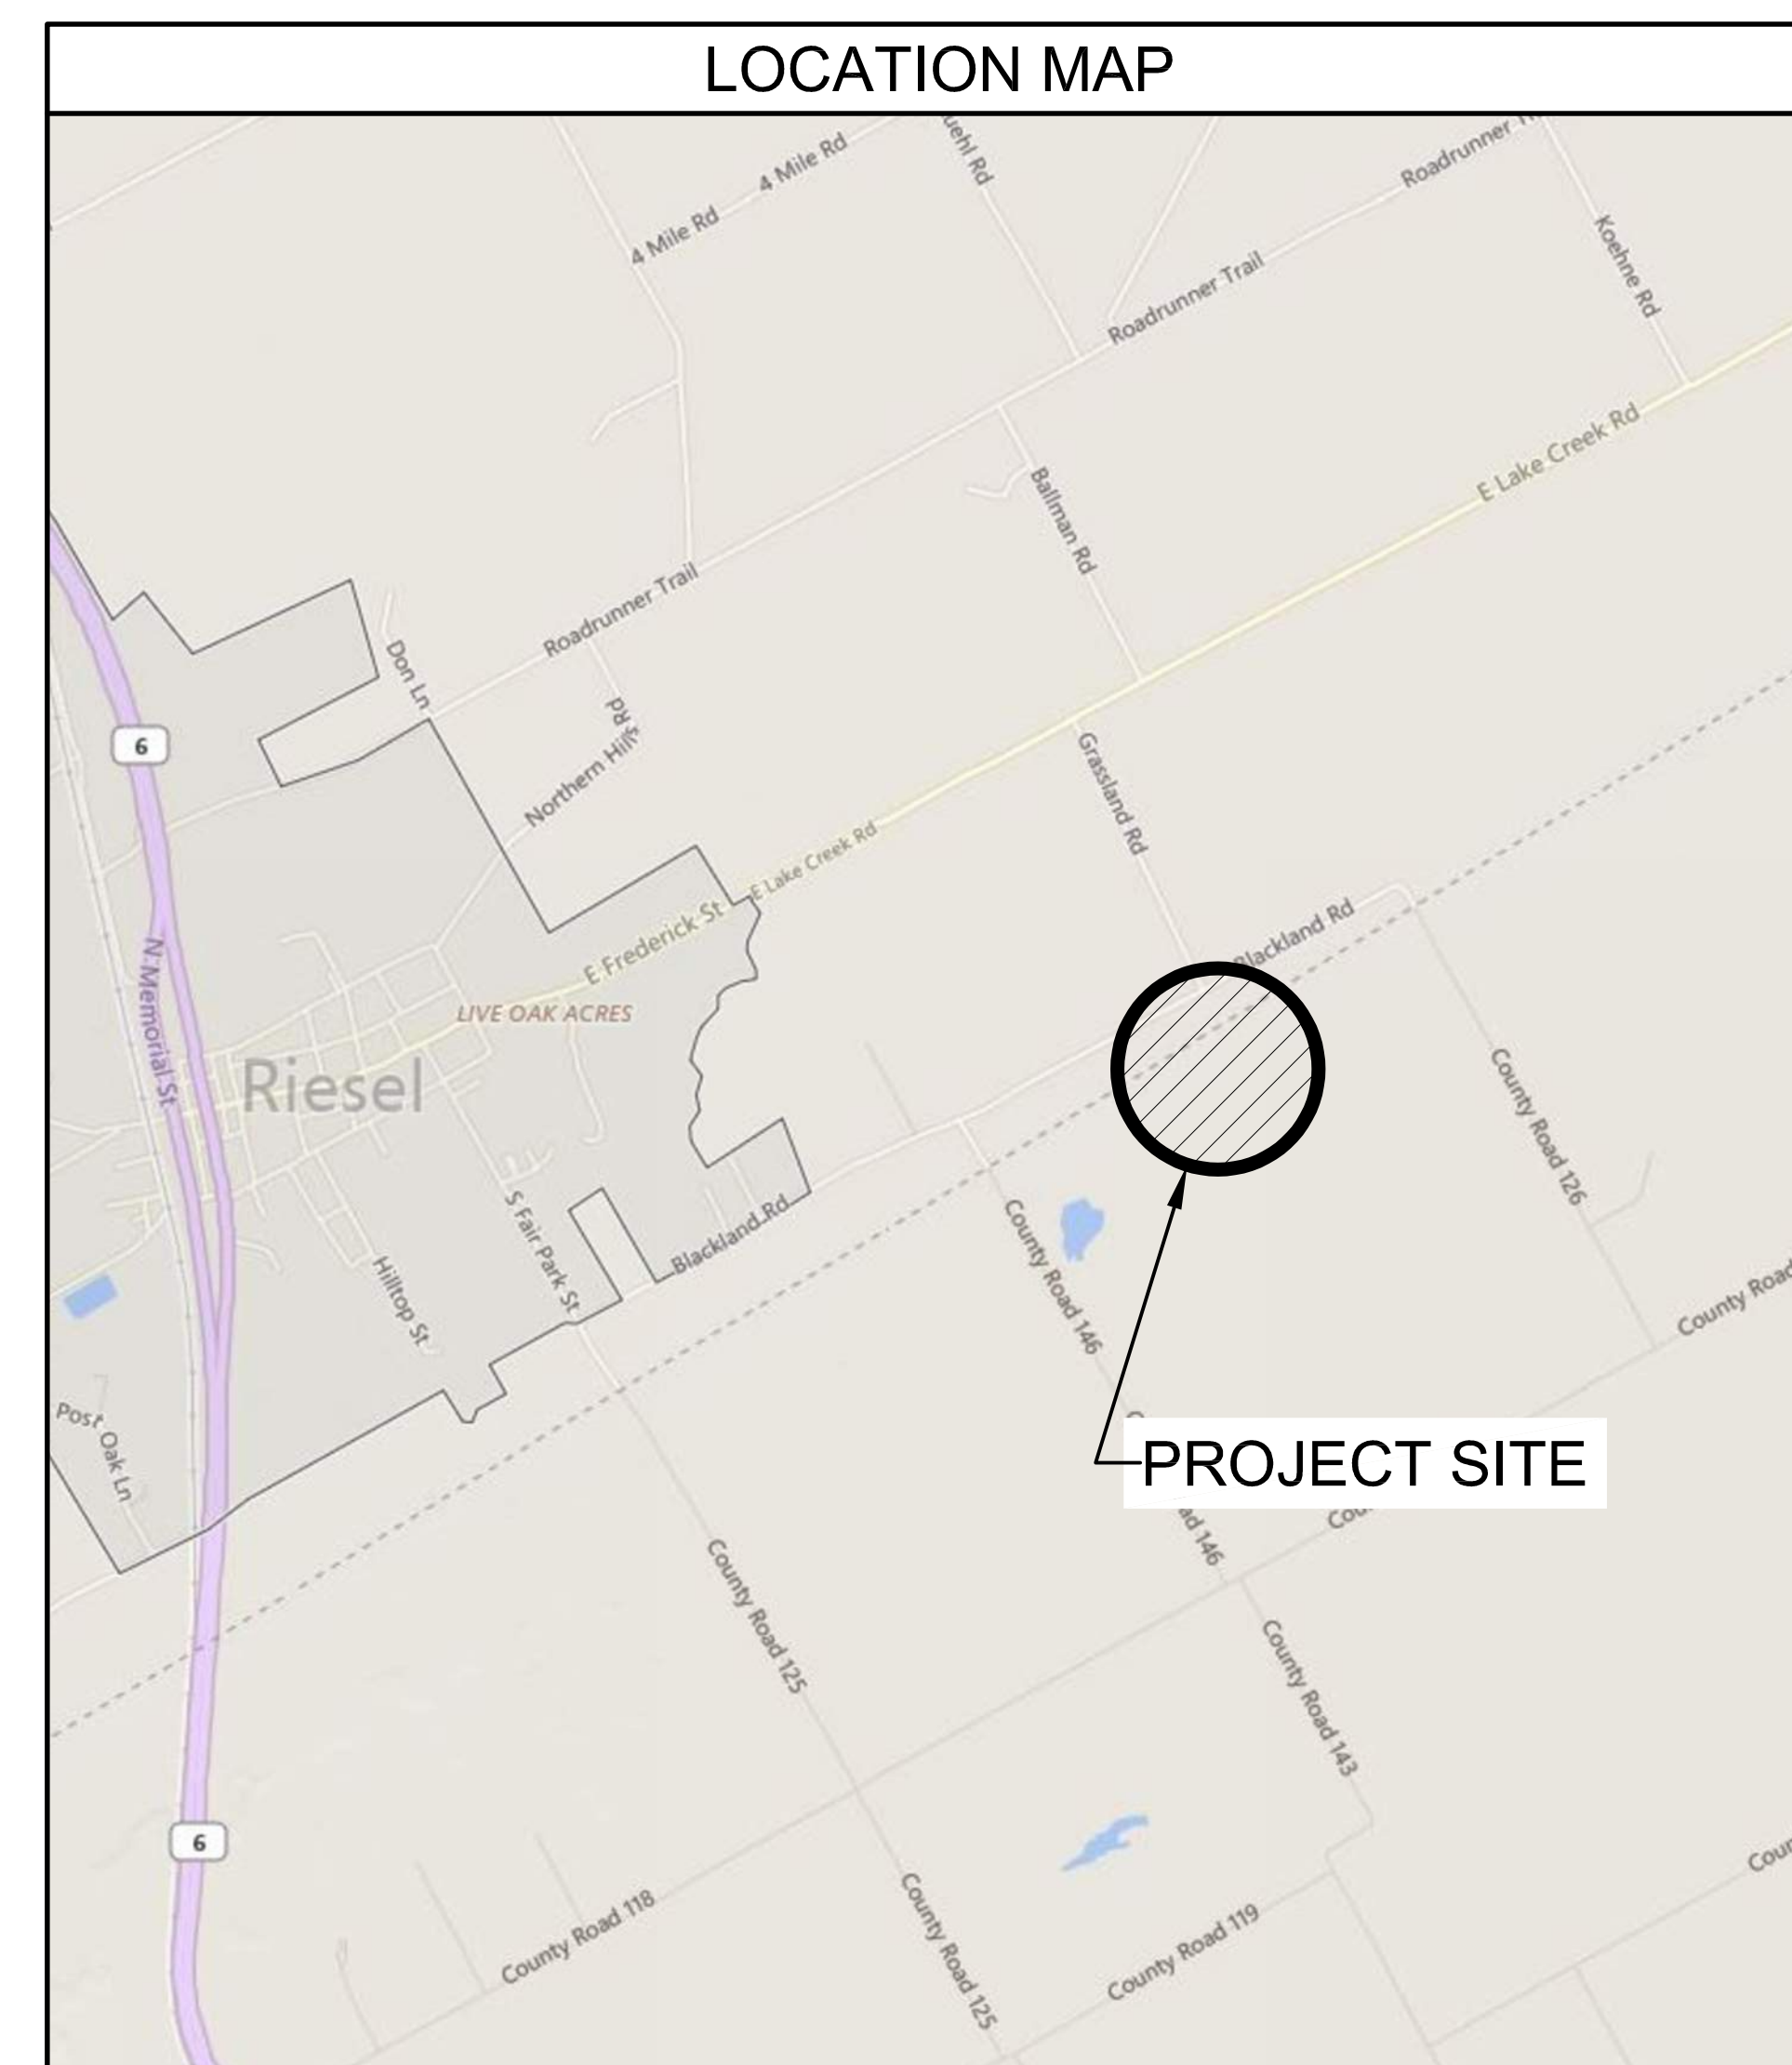

UNITED STATES DEPARTMENT OF AGRICULTURE
AGRICULTURAL RESEARCH SERVICE
RUNOFF STATIONS PROJECT
GRASSLAND, SOIL AND WATER RESEARCH LABORATORY (GSWRL)
1702 BLACKLAND ROAD, RIESEL, TEXAS 76682

ISSUED FOR BID

DECEMBER 22, 2023

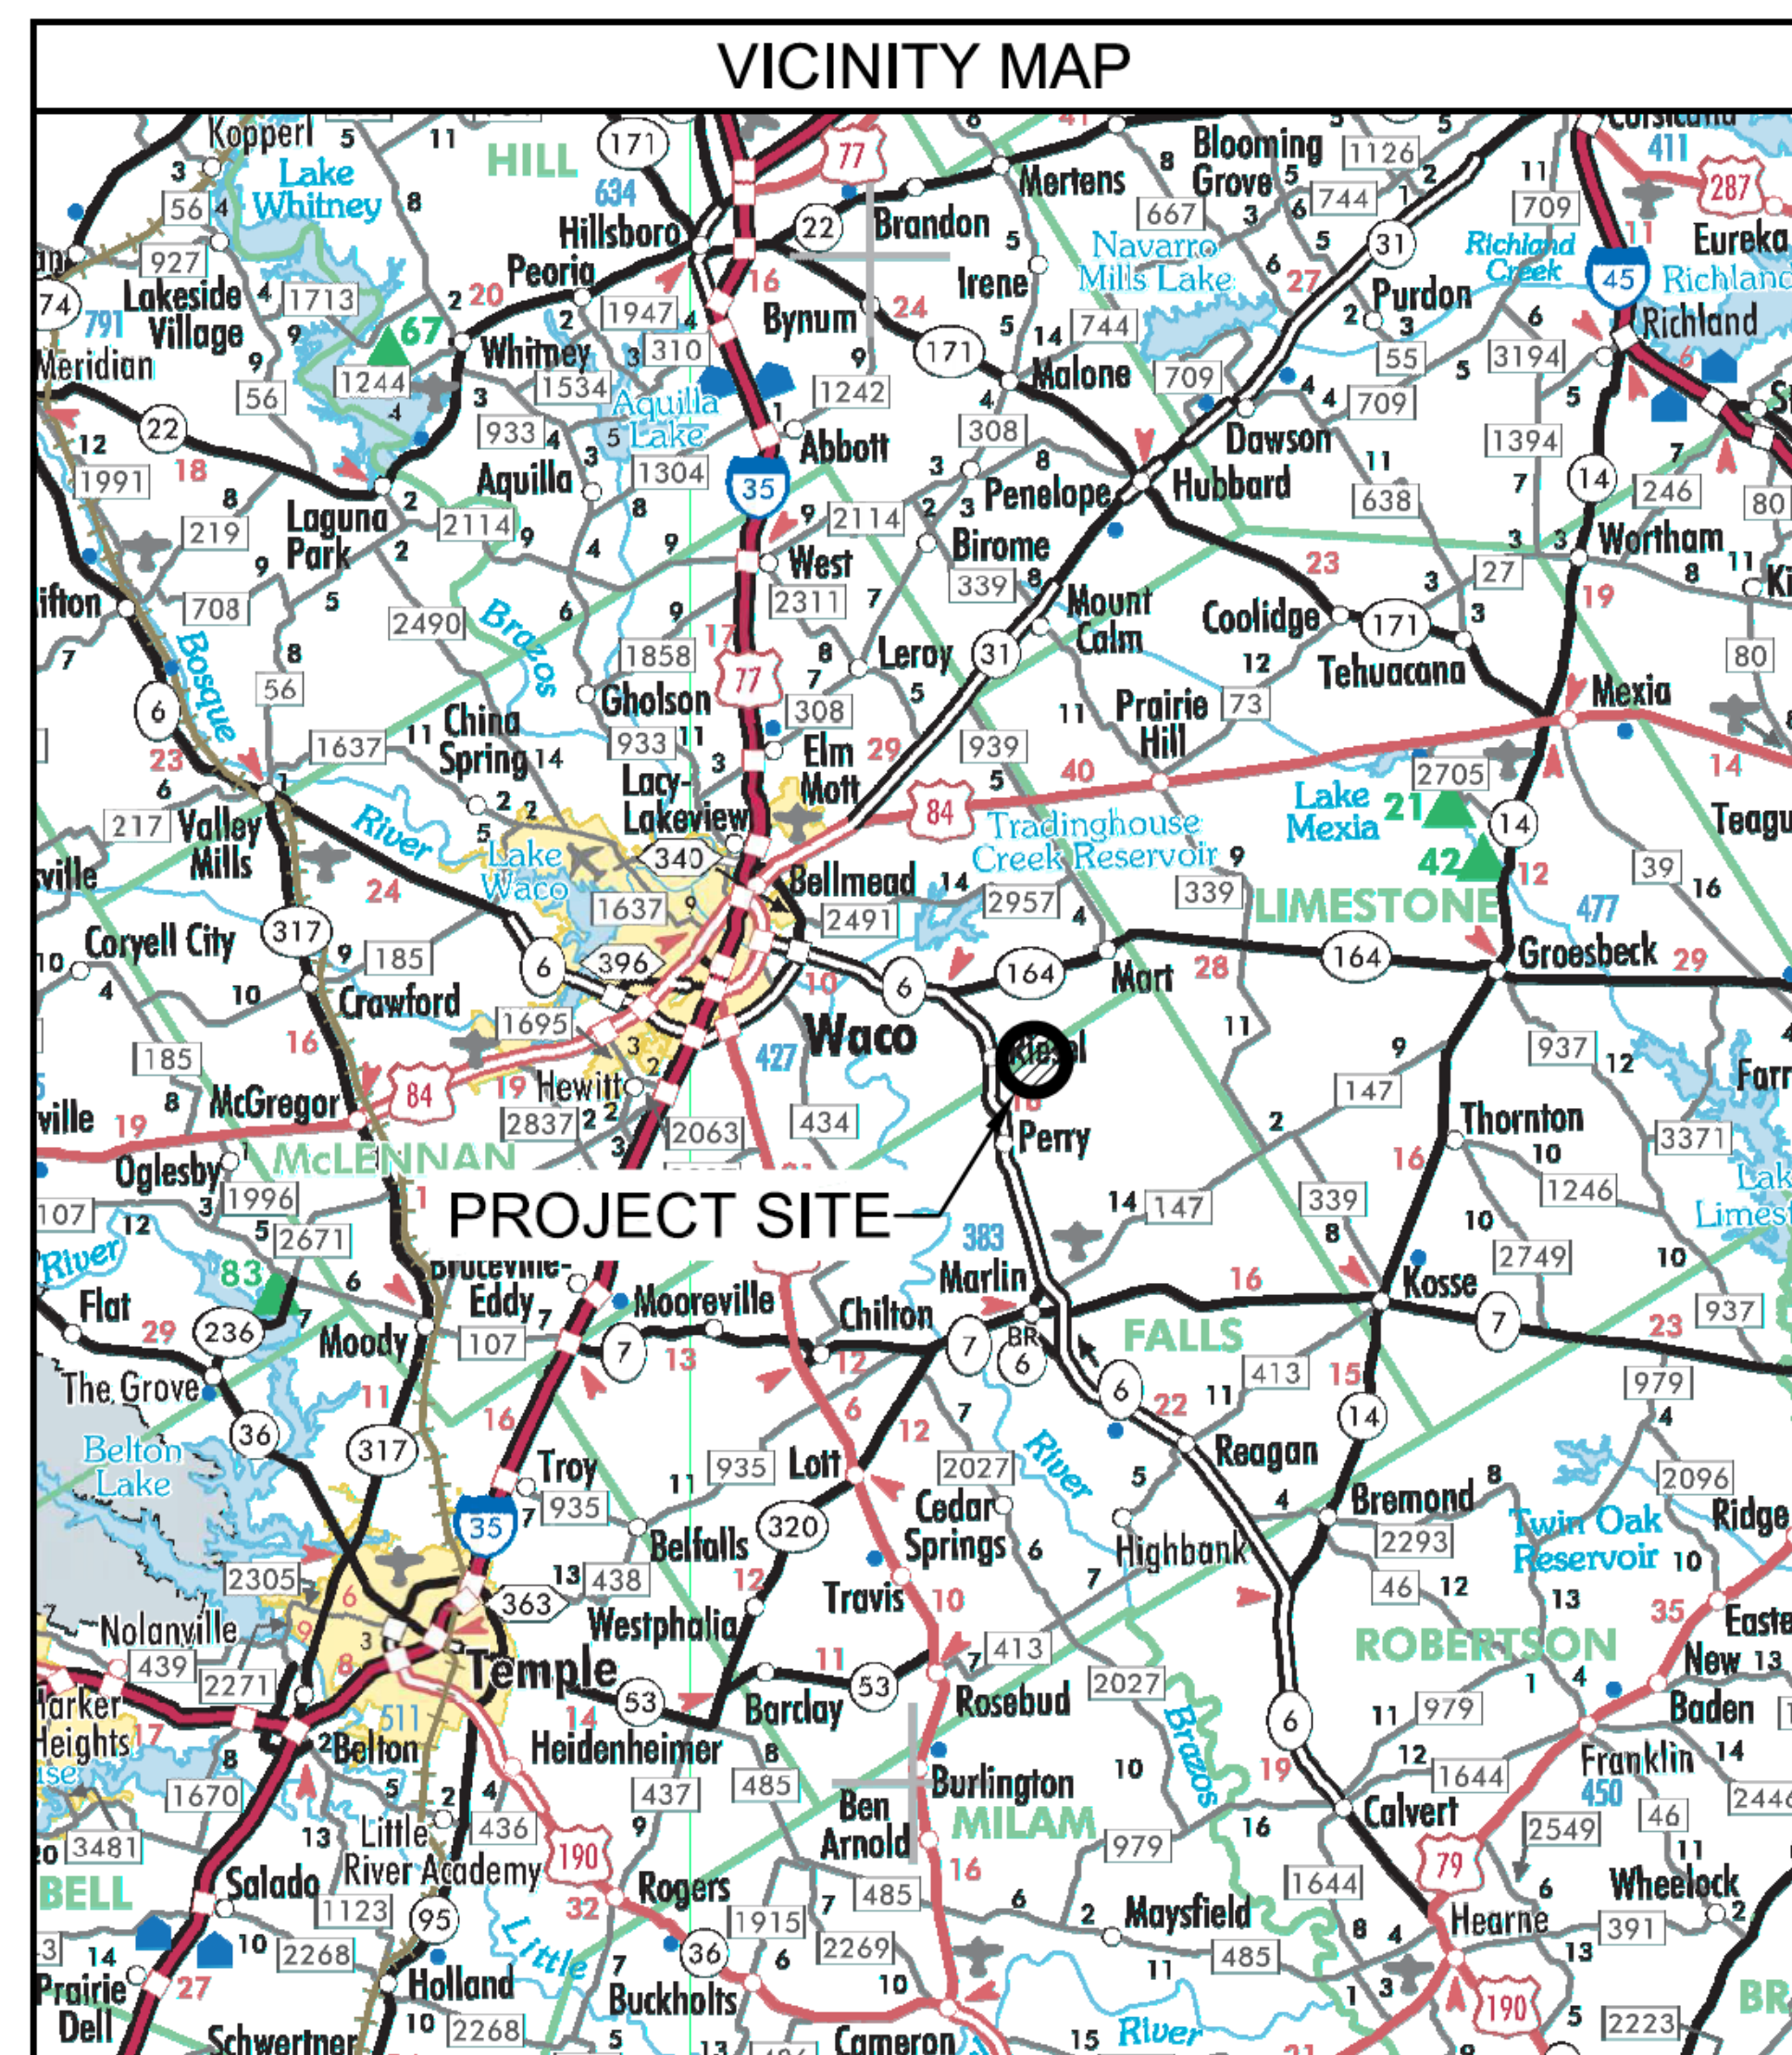

USDA ARS Notes:
These drawing sheets are associated with drawing
sheet sets broken out for bid components including
the Base, Option-1, and Option-2. Refer also to the
SOW document.

stv STV Architects, Inc. 205 West Walsh Drive Douglassville, Pennsylvania tel: 610-385-6000 fax: 610-385-6501 www.stvinc.com		A 12/22/23 R. NEFF ISSUED FOR BID		NO. DATE BY DESCRIPTION	
A-E FIRM USDA		USDA		REVISIONS	
PROJECT MANAGER R. NEFF		EPM N. GRIKEN		Agricultural Research Service	
DESIGNER W. HARCHER		LM D. SMITH		RUNOFF STATION - GRASSLAND, SOIL AND WATER RESEARCH LABORATORY (GSWRL)	
CHECKED BY R. DARLINGTON		SAFETY & HEALTH P. JOVANOVIH		COVER SHEET	
DRAWN BY W. HARCHER		REAL PROPERTY L. WURZBERGER		SOLICITATION NO. FACILITIES MODERNIZATION BRANCH (FMB) FACILITIES DIVISION (FD) RIESEL G-001	
				DATE	
				1702 BLACKLAND ROAD, RIESEL, TEXAS 76682	
				DWG NO.	

DRAWING INDEX

GENERAL			
	G-001	COVER SHEET	
	G-002	DRAWING INDEX	
	G-003	ABBREVIATIONS AND GENERAL SYMBOLS	

STRUCTURAL		
	S-001	GENERAL STRUCTURAL NOTES AND LEGEND
	S-003	RUNOFF STATIONS LOCATION PLAN
	SD4-102	RUNOFF STATION W1 DEMOLITION PLAN
	SD4-109	RUNOFF STATION Y2 DEMOLITION PLAN
	S4-101	RUNOFF STATION P1 THRU P4 REPAIRS
	S4-102	RUNOFF STATION W1 REPAIRS
	S4-103	RUNOFF STATION W6 REPAIRS
	S4-104	RUNOFF STATION W10 REPAIRS
	S4-105	RUNOFF STATION W12 REPAIRS
	S4-106	RUNOFF STATION W13 REPAIRS
	S4-107	RUNOFF STATION SW12 REPAIRS
	S4-108	RUNOFF STATION SW17 REPAIRS
	S4-109	RUNOFF STATION Y2 REPAIRS
	S4-110	RUNOFF STATION Y6 REPAIRS
	S4-111	RUNOFF STATION Y8 REPAIRS
	S4-112	RUNOFF STATION Y10 REPAIRS
	S4-113	RUNOFF STATION Y13 REPAIRS
	S4-114	RUNOFF STATION Y14 REPAIRS

stv STV Architects, Inc. 205 West Walsh Drive Douglassville, Pennsylvania tel: 610-385-6500 fax: 610-385-6501 www.stvinc.com						
		A	12/22/23	R. NEFF	ISSUED FOR BID	
		NO.	DATE	BY	DESCRIPTION	
		REVISIONS				
A-E FIRM	USDA	USDA	ars Agricultural Research Service			
	PROJECT MANAGER		EFM	RUNOFF STATION - GRASSLAND, SOIL AND WATER RESEARCH LABORATORY (GSWRL) 1702 BLACKLAND ROAD, RIESEL, TEXAS 76862		
	R. NEFF		N. GIRKEN			
DESIGNER	LM	DRAWING INDEX				
W. HARCHER	D. SMITH					
CHECKED BY	SAFETY & HEALTH					
R. DARLINGTON	P. JOVANOVICH	SOLICITATION NO.	FACILITIES MODERNIZATION BRANCH (FMB)		RIESEL G-002 DWG NO.	
DRAWN BY	REAL PROPERTY	DATE	FACILITIES DIVISION (FD)			
W. HARCHER	L. WURZBERGER		9001 SUNNYSIDE AVENUE SEL TOVILLE, MO 30105			

GENERAL SYMBOLS



PROJECT NORTH ARROW



PROJECT NORTH ARROW
(FOR SITE WORK)



DETAIL BUBBLE



ELEVATION SYMBOL



MULTIPLE INTERIOR ELEVATION SYMBOL



SECTION SYMBOL

ROOM NAME


101

ROOM IDENTIFIER, NAME AND NUMBER

— NEW CONSTRUCTION

— EXISTING CONSTRUCTION TO REMAIN

- - - - - EXISTING CONSTRUCTION TO BE REMOVED

 

SHEET KEYNOTE



DATUM ELEVATION



REVISION TAG

VIEW TITLE



PLAN TITLE OR TYPICAL DETAIL

1/8"=1'-0"





**SECTION/DETAIL/
ELEVATION/OR
ENLARGED PLAN**

1/8"=1'-0"



SECTION NUMBER OR DETAIL, ELEVATION OR ENLARGED PLAN LETTER

VIEW TITLE

X-XXX
X-XXX
X-XXX

SHEET ON WHICH SECTION, DETAIL, ELEVATION OR ENLARGED PLAN IS REFERENCED


— LIST ADDITIONAL SHEETS AS ILLUSTRATED

MATERIAL SYMBOLS

 EARTH	 CONCRETE
 GRAVEL	 INSULATION (BLANKET, BATT)
 CONCRETE MASONRY UNIT	 RIGID INSULATION
 EXTERIOR FINISH MASONRY UNIT	 STEEL IN SECTION
 PLYWOOD	 COMPOSITE METAL PANEL
 GYPSUM WALLBOARD	 WOOD BLOCKING

							
STV Architects, Inc. 200 West Main Drive Douglasville, Pennsylvania Tel: (610)384-2001 Fax: (610)384-2001 www.stvinc.com							
		A 12/22/23 R. NEFF ISSUED FOR BID					
		NO. DATE BY DESCRIPTION					
				REVISIONS			
		U S D A					
				RUNOFF STATION - GRASSLAND, SOIL AND WATER RESEARCH LABORATORY (GSWR) 1702 BLACKLAND ROAD, RIESEL, TEXAS 76682			
				ABBREVIATIONS AND GENERAL SYMBOLS			
A-E FIRM USDA							
PROJECT MANAGER N. NEFF		EFM N.GIRKEN					
DESIGNER V. HARCHER		JM D. SMITH					
CHECKED BY D. DARLINGTON		SAFETY & HEALTH P. JOVANOVICH		SUBMITTANCE NO.			
DRAWN BY V. HARCHER		REAL PROPERTY L. WURZBERGER		DATE		FACILITIES MODERNIZATION BRANCH (FMB) FACILITIES DIVISION (FD) 5601 SUNNYSIDE AVENUE BELTSHVILLE, MD 20705	
						RIESEL G-003	
						DWG NO.	

1. FOR GENERAL STRUCTURAL NOTES, LEGEND, AND STRUCTURAL TECHNICAL TERMS SEE DRAWING S-001.

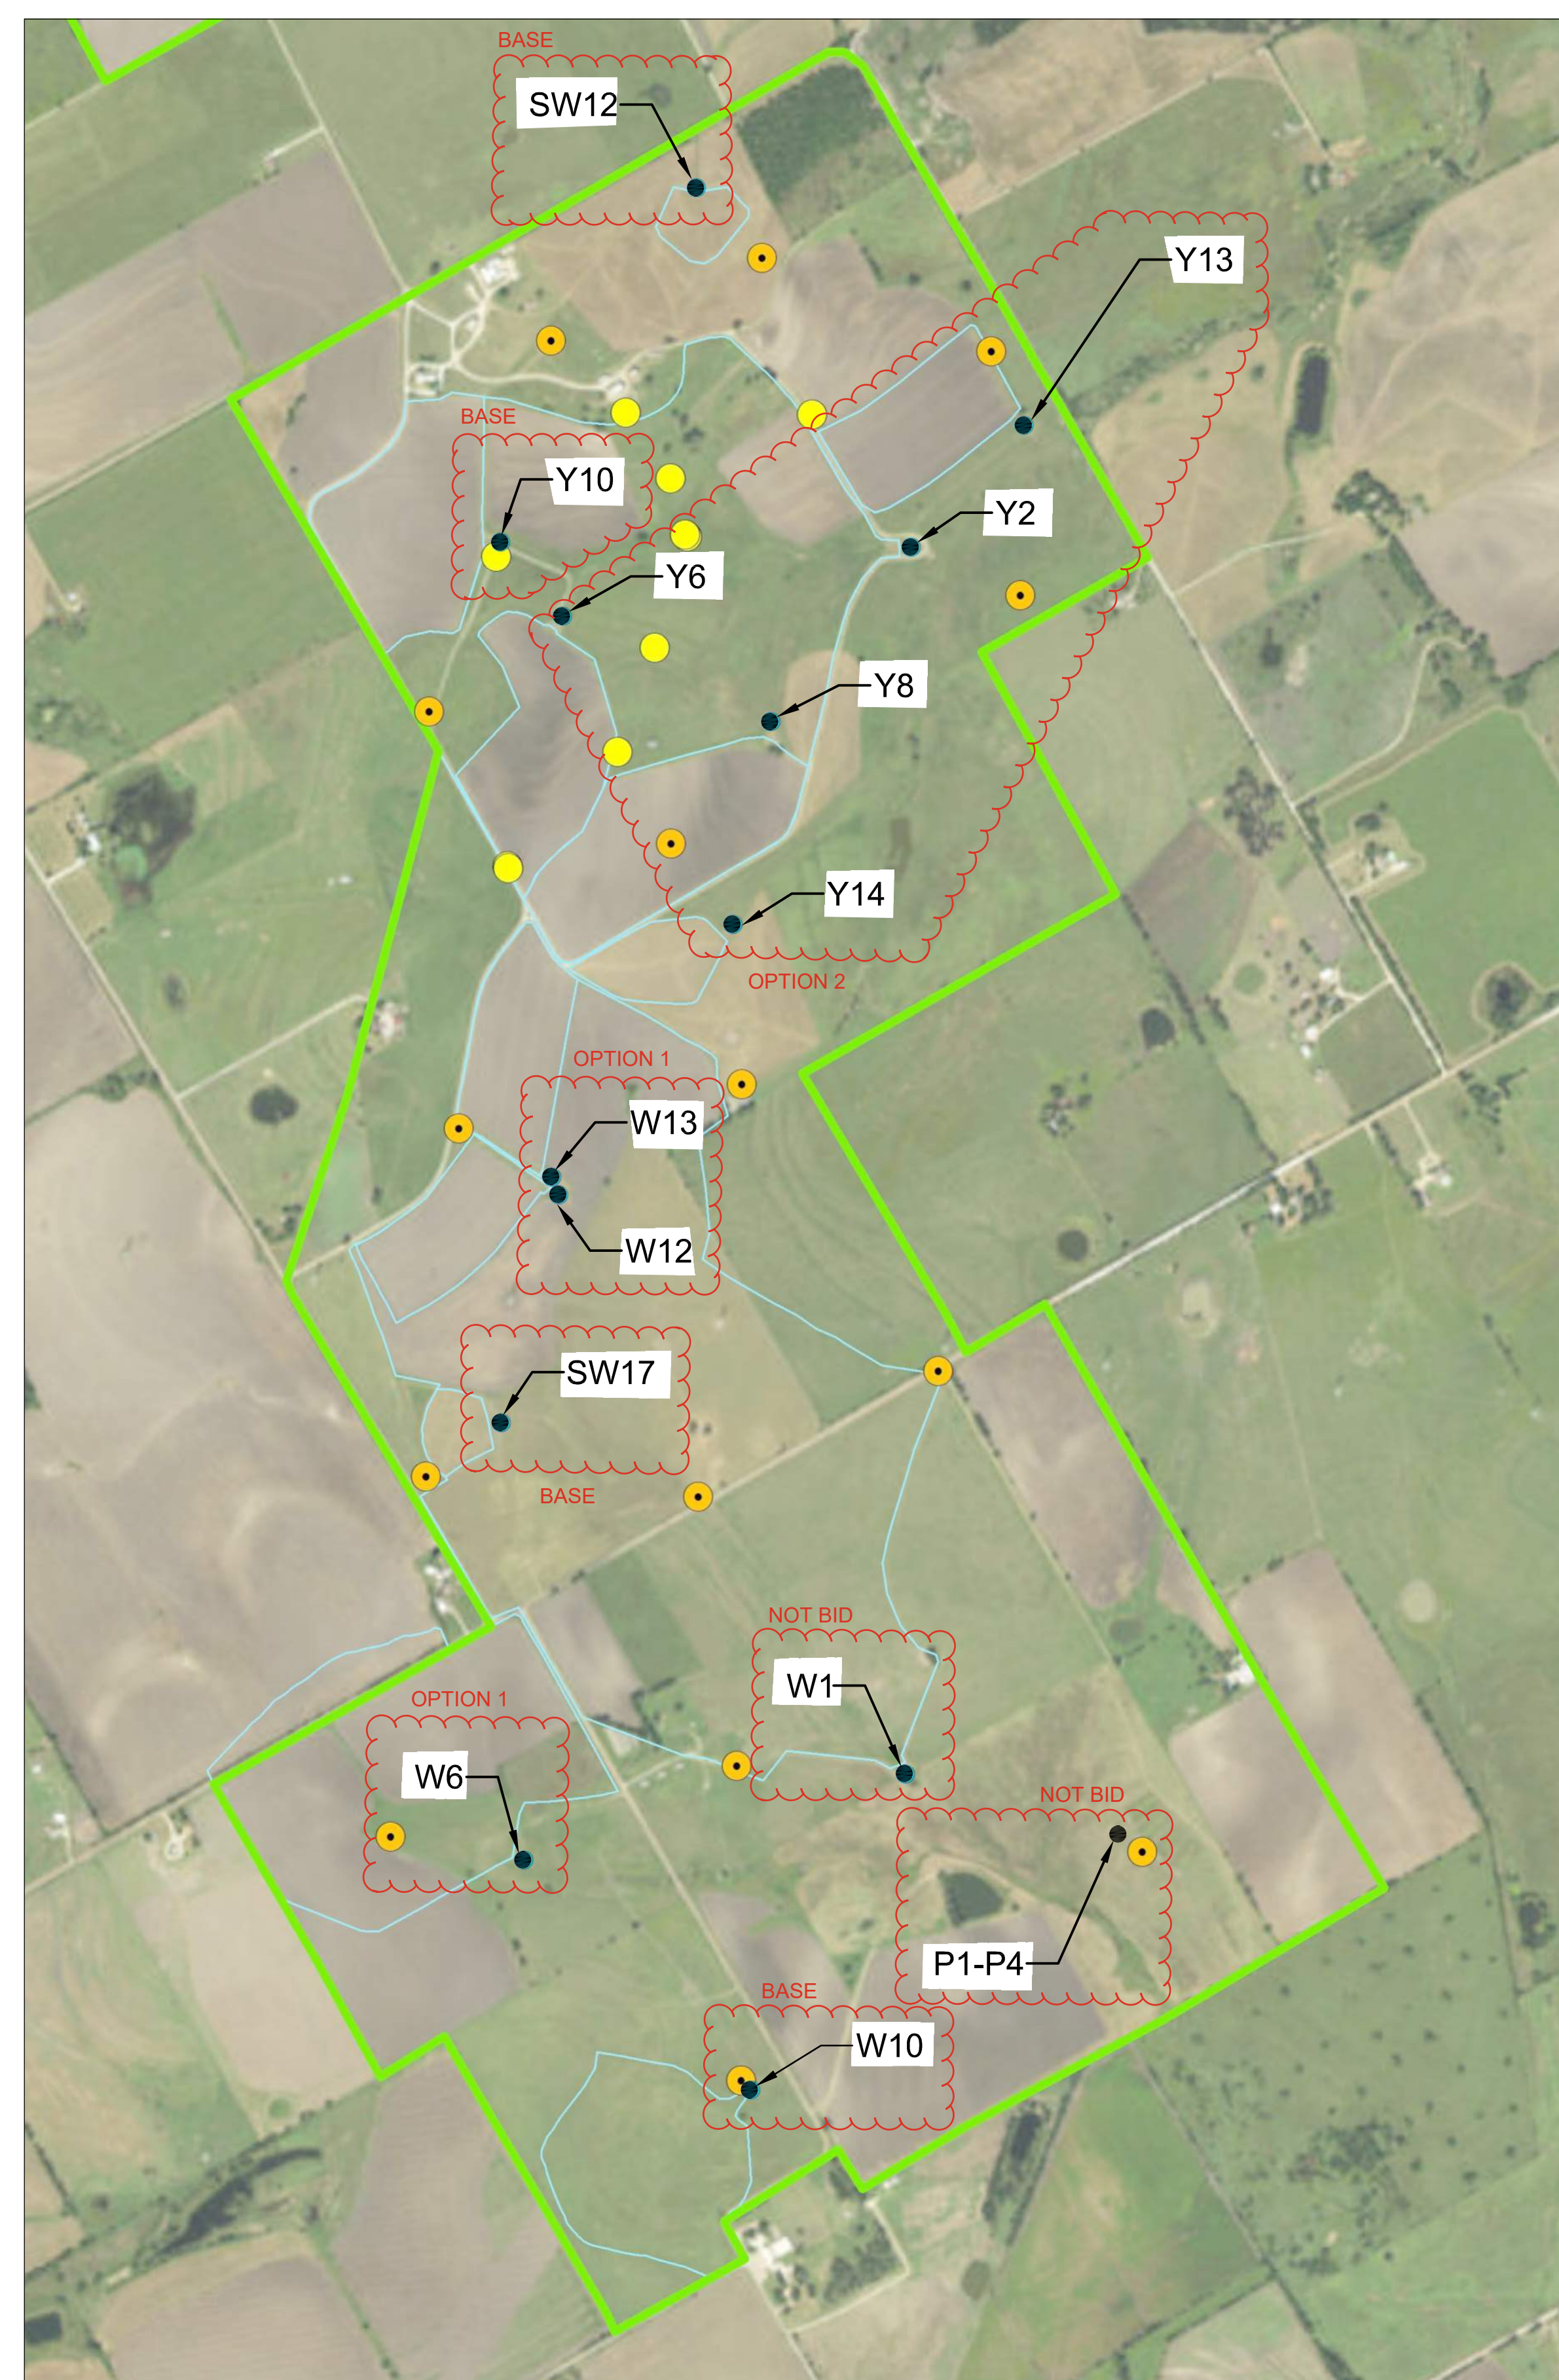

RUNOFF STATIONS LOCATION PLAN

SCALE: 1"=700'

							
STV Incorporated 205 West Walnut Drive Douglasville, Pennsylvania tel: 610-385-6200 fax: 610-385-5501 www.stvnc.com		A	12/22/23	R. NEFF	ISSUED FOR BID		
		NO.	DATE	BY	DESCRIPTION		
					REVISIONS		
		U S D A			Agricultural Research Service		
					RUNOFF STATION - GRASSLAND, SOIL AND WATER RESEARCH LABORATORY (GSWRL)		
					1702 BACKLICK ROAD, REESEL, TEXAS 79662		
A-E FIRM	USDA			RUNOFF STATIONS LOCATION PLAN			
PROJECT MANAGER	EPM	SOLICITATION NO.		FACILITIES MODERNIZATION BRANCH (FMB)		REESEL	
R. NEFF	M. GIRKEN			FACILITIES DIVISION (FD)		S-003	
DESIGNER	LM			4601 GUNNERSBY AVENUE			
S. CHAMBERS	D. SMITH			BELT SYSTEM, MD 20705			
CHECKED BY	SAFETY & HEALTH						
M. HIGH	P. JOVANOVICH	DATE					
DRAWN BY	REAL PROPERTY						
W. HELLER	L. WURZBERGER						