





United States Department of Agriculture
Forest Service

MONTANA
CASCADE COUNTY
(R01) NORTHERN REGION
HELENA-LEWIS AND CLARK NATIONAL FOREST
LEWIS AND CLARK INTERPRETIVE CENTER

LEWIS AND CLARK INTERPRETIVE CENTER
WINDOW REPAIRS

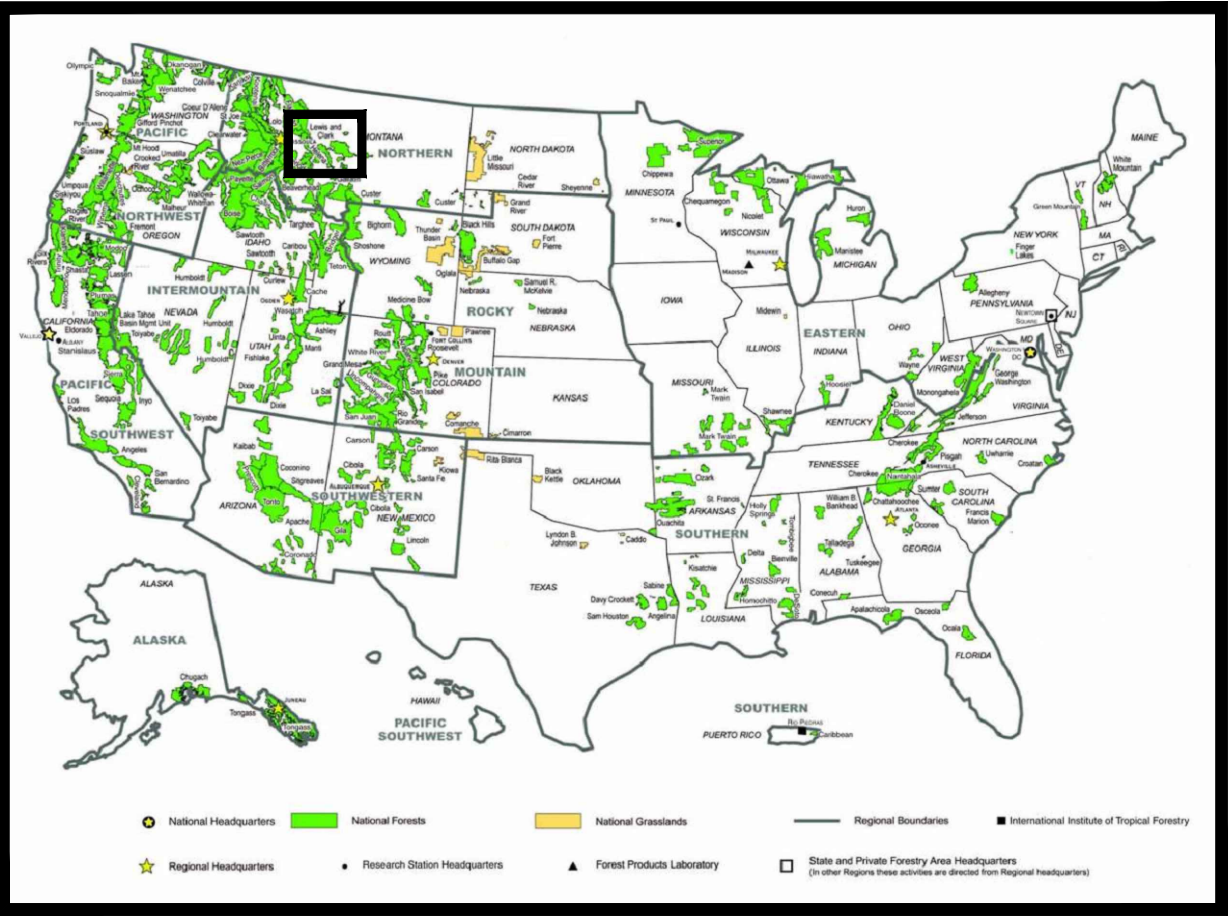

FOREST LOCATION MAP

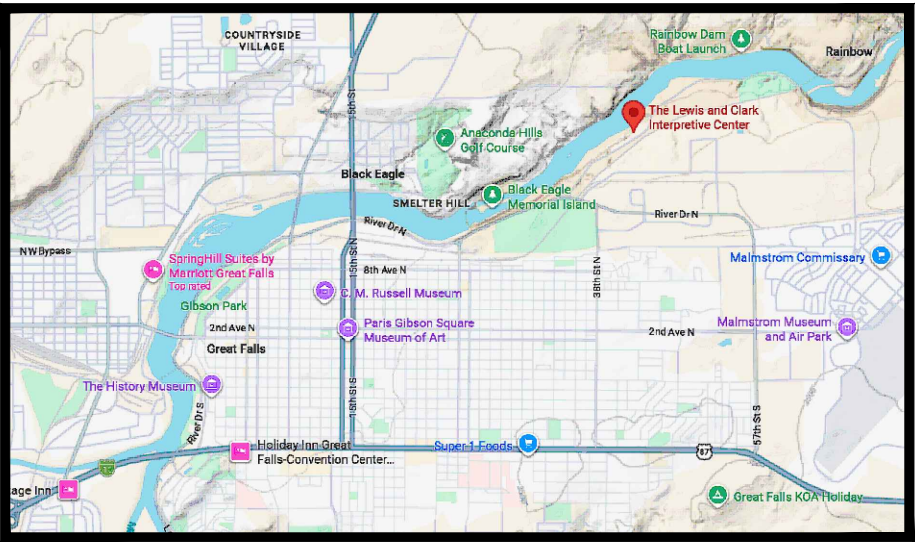

PROJECT LOCATION MAP

SITE:
LEWIS AND CLARK INTERPRETIVE CENTER
4201 GIANT SPRINGS ROAD
GREAT FALLS, MT 59405

INDEX OF SHEETS

SHEET	SHEET TITLE	DATE
01	COVERSHEET	00/00/00
2	SCHEDULE OF ITEMS	02/24/26
3	PLAN VIEW	02/24/26
4	ELEVATIONS NORTH & EAST	02/24/26
5	ELEVATIONS SOUTH & WEST	02/24/26
6	DIMENSIONS: A	02/24/26
7	DIMENSIONS: B	02/24/26
8	DIMENSIONS: C	02/24/26
9	DIMENSIONS: D & E	02/24/26
10	DIMENSIONS: F	02/24/26

RECOMMENDED BY:

FOREST ENGINEER

LCIC DIRECTOR

APPROVED:

FOREST SUPERVISOR

3/18/26 13:00 NZUCKER C:\USERS\NZUCKER\BUDGET\HLF 7000 ENGINEERING\HLF 7000 BUILDINGS AND OTHER STRUCTURES\PROJECTS\08_LCIC & GF\2026 WINDOWS\DRAWINGS\LCIC WINDOWS.DWG


SCHEDULE OF ITEMS				
Pay Item	Item Description	Method of Measure	Estimated Quantity	Pay Unit
080100	Window Cleaning: Interior & Exterior	SF	3785	LS
080110	Window Weatherstripping	LF	1680	LS
080153	Window Caulk: Exterior Edges	LF	485	LS
088155	Window Replacement	EA	11	EA

GENERAL NOTES	
080100 WINDOW CLEANING: INTERIOR & EXTERIOR 1. WASH INTERIOR AND EXTERIOR GLASS AND FRAMES OF EACH WINDOW ASSEMBLY IDENTIFIED IN THIS CONTRACT 2. WINDOW WASHING SHALL BE COMPLETED AFTER ALL OTHER WORK IS COMPLETE. 080110 WINDOW WEATHERSTRIPPING 3. REMOVE AND REPLACE ALL EXISTING WEATHERSTRIPPING WITH NEW VINYL WEATHERSTRIPPING. 4. NEW SYSTEM SHALL BE WATER TIGHT. 080153 WINDOW CAULK: EXTERIOR EDGES 5. REMOVE ALL CAULKING AROUND EXTERIOR WINDOW FRAMES AND REPLACE WITH NEW CAULK AND WATER TIGHT SYSTEM. 088155 WINDOW REPLACEMENT 6. CONTRACTOR SHALL VISIT SITE PRIOR TO BIDDING OR ORDERING WINDOWS TO VERIFY EXISTING WINDOW SPECIFICATIONS FOR IN-KIND REPLACEMENT. 7. CONTRACTOR SHALL SUBMIT PROPOSED WINDOWS PRIOR TO ORDERING. 8. NEW WINDOWS SHALL BE TEMPERED GLASS. GENERAL NOTES: 9. DIMENSIONS ARE FOR ESTIMATING PURPOSES ONLY. CONTRACTOR SHALL VERIFY ALL DIMENSIONS PRIOR TO BIDDING OR ORDERING MATERIALS. 10. FINAL PRODUCT SHALL RESULT IN A WATER TIGHT WINDOW ASSEMBLY. 11. ANY DISASSEMBLY AND/OR REASSEMBLY OF WINDOW FRAMING OR OTHER SYSTEM COMPONENTS IS INCIDENTAL TO THE WORK.	



1 EXISTING CONDITIONS

SCALE: NTS

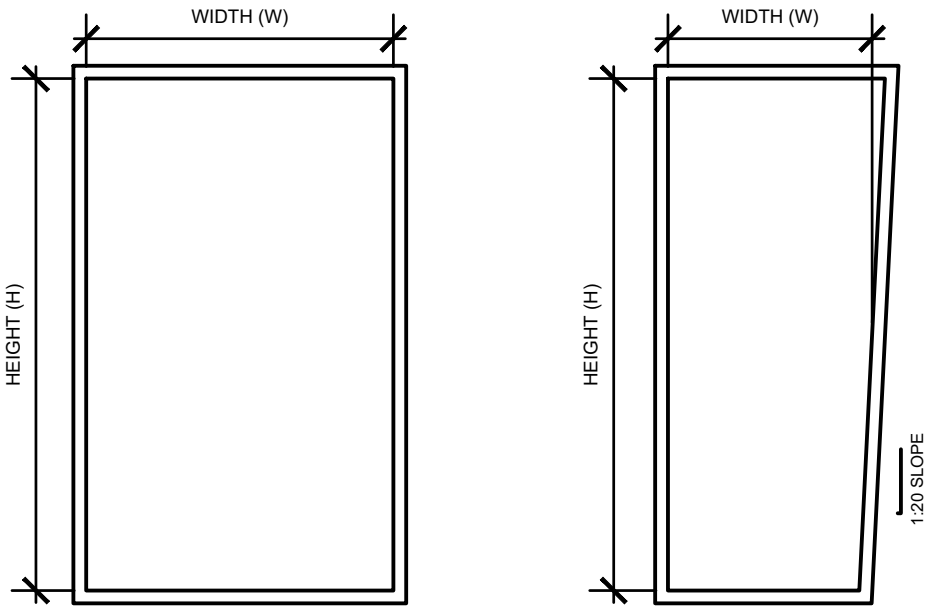

2 WINDOW SCHEDULE DIMENSIONS

SCALE: NTS

WINDOW DIMENSIONS REPRESENT GLASS AREA AND DO NOT INCLUDE FRAMES.

FOR WINDOWS WITH SLOPED EDGES, THE WIDTH WAS MEASURED FROM THE CENTER, REPRESENTING AN AVERAGE WIDTH.



United States Department of Agriculture
Forest Service

(R01)
NORTHERN REGION

STAMPS, LOGOS, AND SEALS

		
NO.	REVISION / ISSUE	DATE

PROJECT NAME

LCIC
WINDOW
REPAIRS

HELENA-LEWIS AND
CLARK NATIONAL
FOREST



LEWIS & CLARK INTERPRETIVE
CENTER (LCIC)

DRAWING TITLE

SCHEDULE OF ITEMS

DATE 02/04/2026	ARCHIVE NO.
DESIGNER R. STOVALL	DRAWING SHEET NO. 02
DRAWN R. STOVALL	
CHECKED J. GANNON	SHEET 02 OF 10
PROJECT NO.	

3/2/26 16:30 DEWOODS C:\USERS\DEWOODS\BOX1\R01_HLF 7000 ENGINEERING\HLF 7300 BUILDINGS AND OTHER STRUCTURES\PROJECTS\06_LCIC & GF\2026 WINDOWS\DRAWINGS\LCIC\WINDOWS - COPY.DWG;

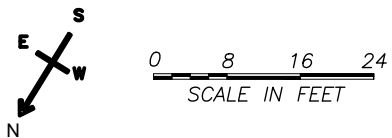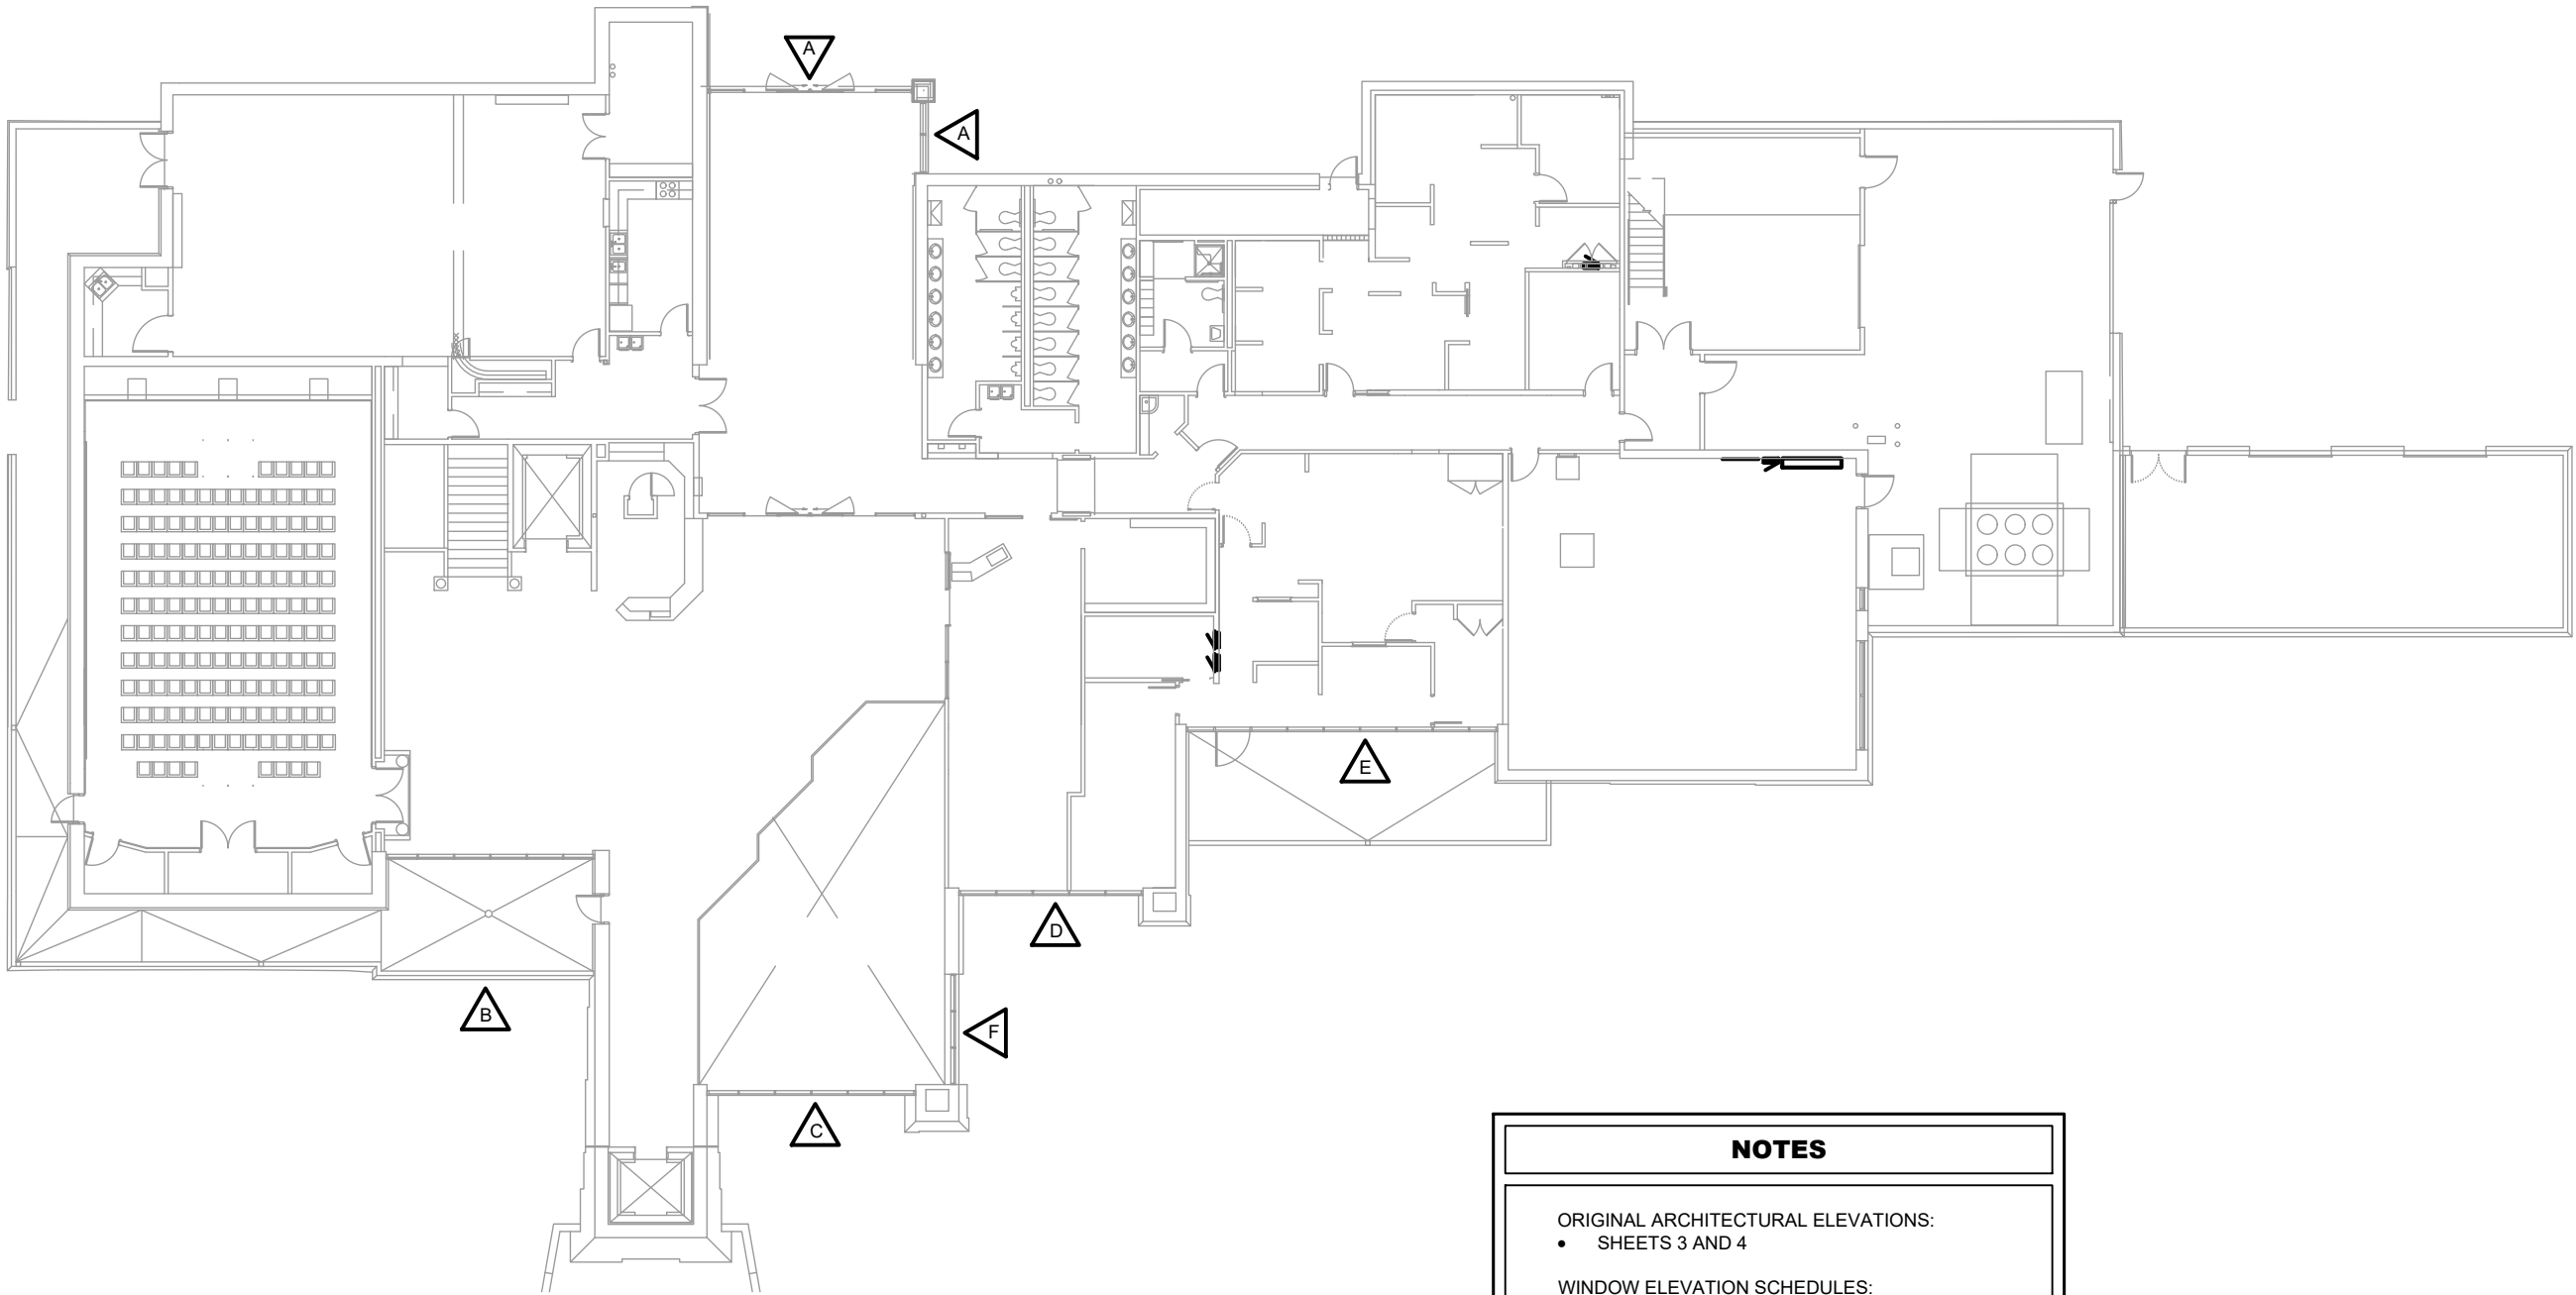

NOTES

ORIGINAL ARCHITECTURAL ELEVATIONS:
• SHEETS 3 AND 4

WINDOW ELEVATION SCHEDULES:
• A - SEE SHEET 6
• B - SEE SHEET 7
• C - SEE SHEET 8
• D - SEE SHEET 9
• E - SEE SHEET 9
• F - SEE SHEET 10



United States Department of Agriculture
Forest Service

(R01)

NORTHERN REGION

STAMPS, LOGOS, AND SEALS

NO.	REVISION / ISSUE	DATE

PROJECT NAME

**LCIC
WINDOW
REPAIRS**

**HELENA-LEWIS AND
CLARK NATIONAL
FOREST**



**LEWIS & CLARK INTERPRETIVE
CENTER (LCIC)**

DRAWING TITLE

PLAN VIEW

DATE 02/04/2026	ARCHIVE NO.
DESIGNER R. STOVALL	DRAWING SHEET NO.
DRAWN R. STOVALL	03
CHECKED J. GANNON	
PROJECT NO.	SHEET 03 OF 10

3/2/26 16:30 DEWOODS C:\USERS\DEWOODS\BOX\R01_HLF 7000 ENGINEERING\HLF 7300 BUILDINGS AND OTHER STRUCTURES\PROJECTS\06_LCIC & GF\2026 WINDOWS\DRAWINGS\LCIC\WINDOWS - COPY.DWG;

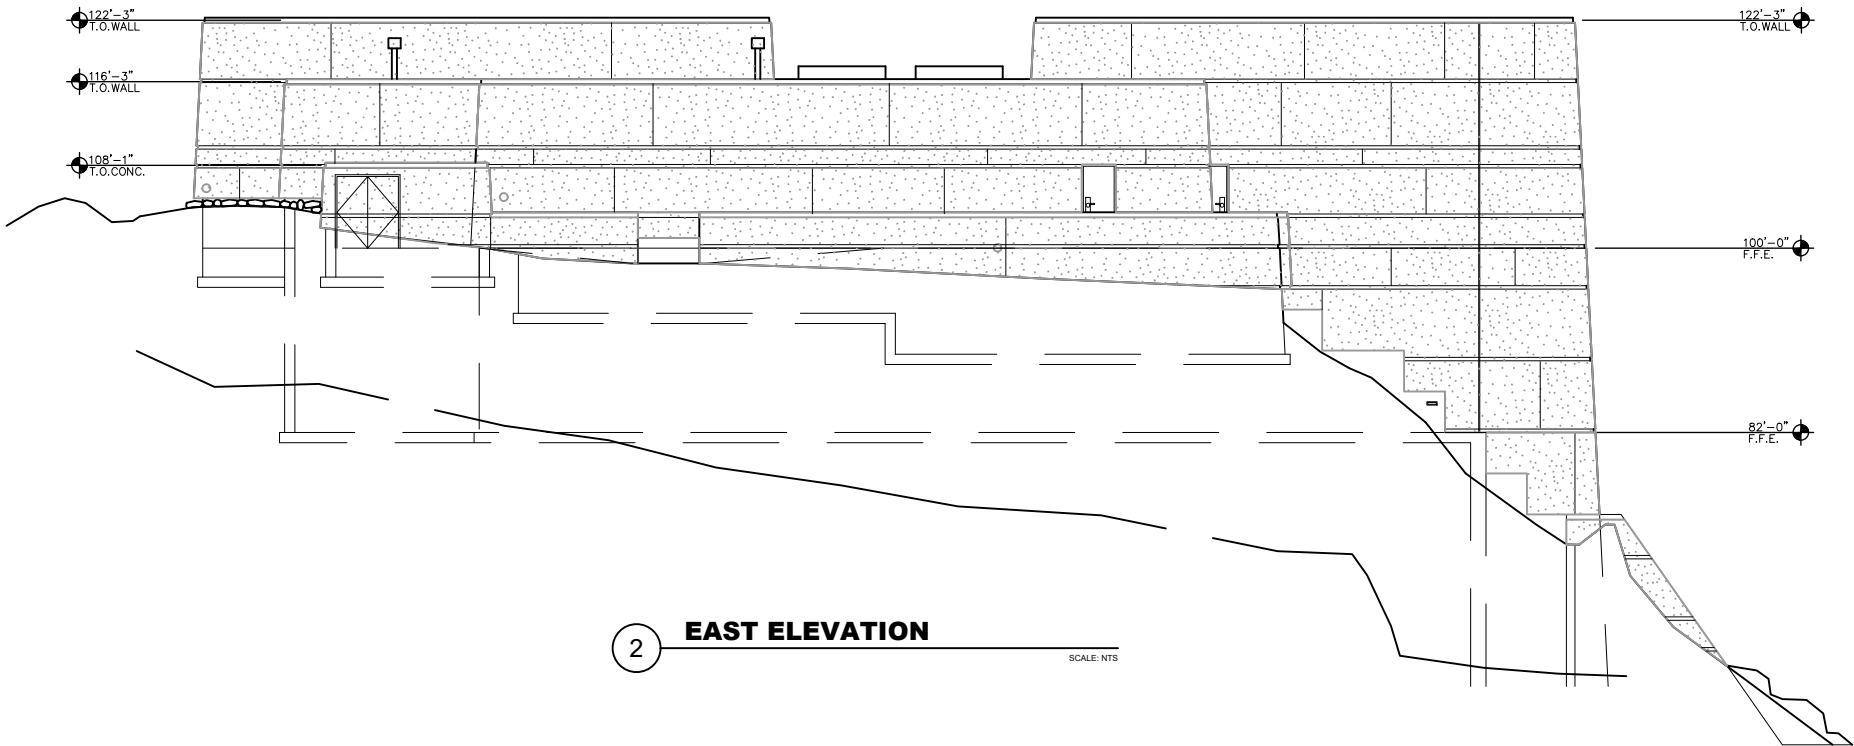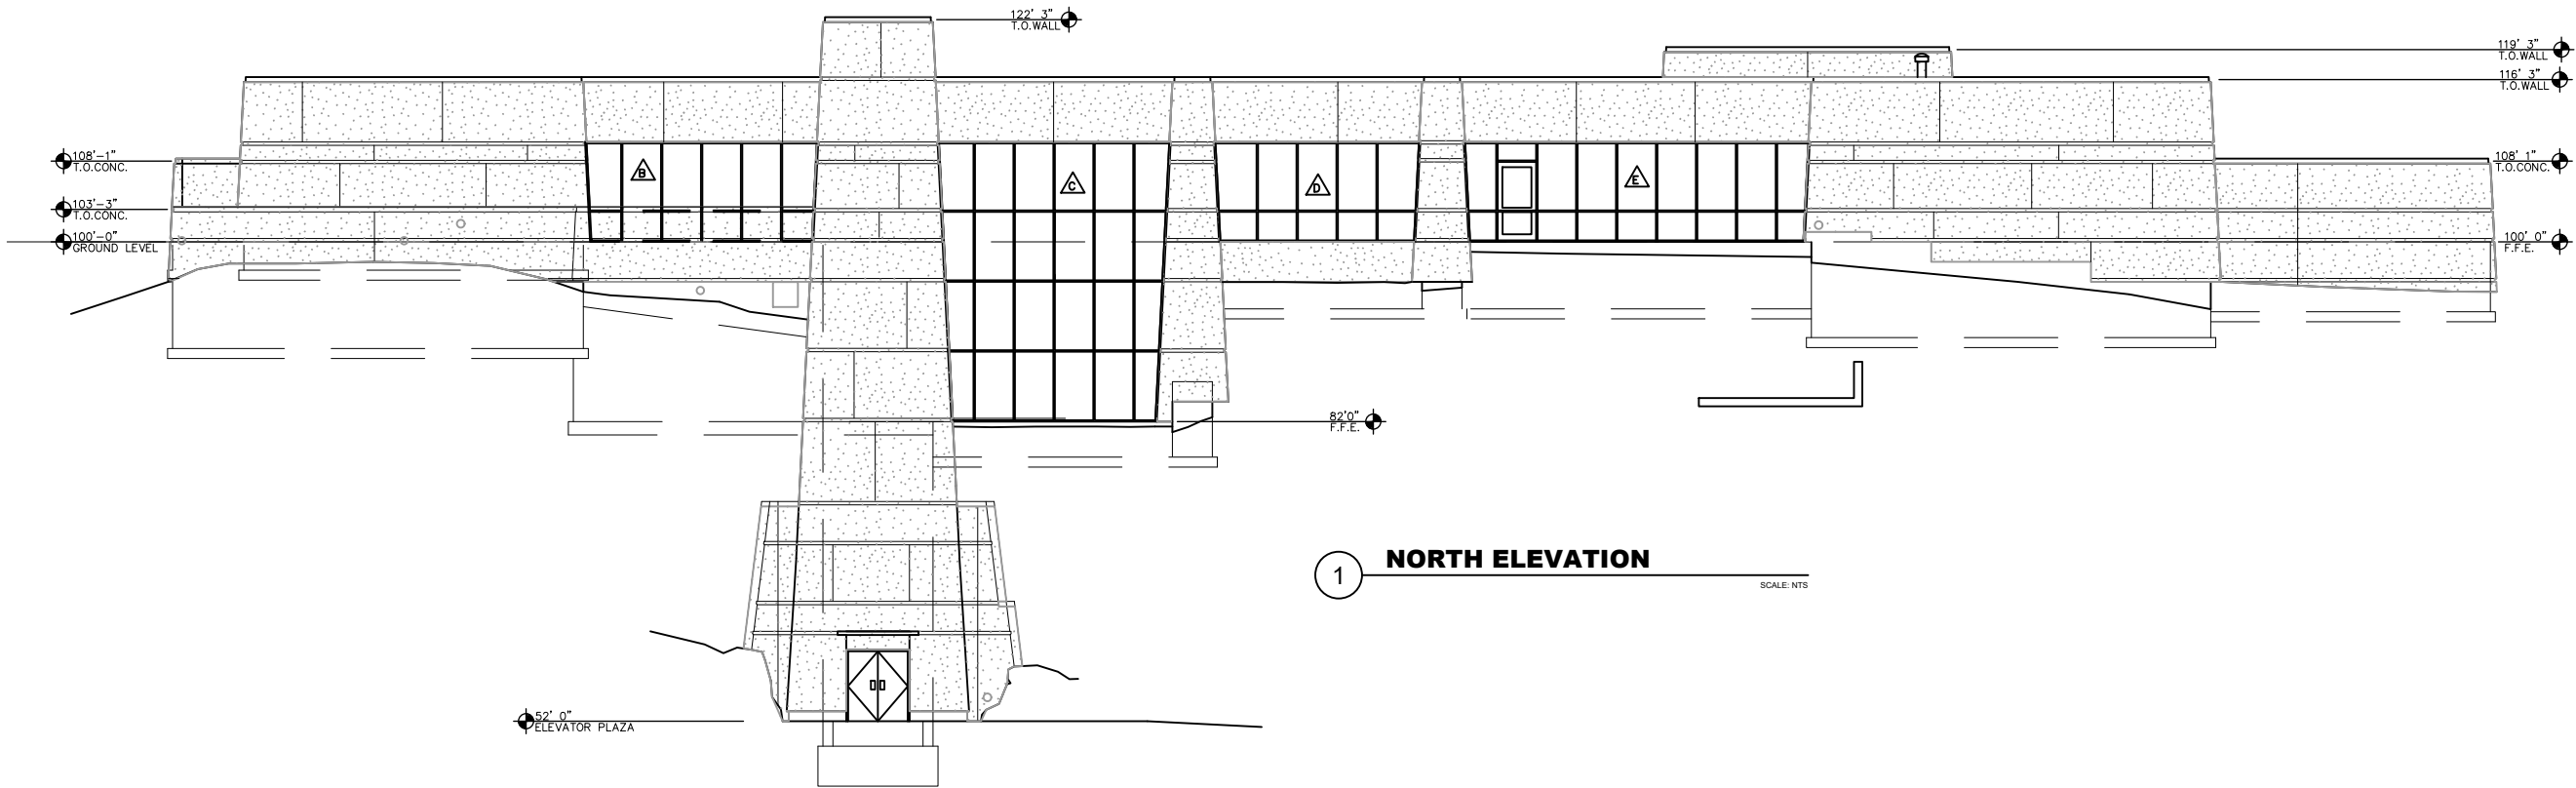

United States Department of Agriculture
Forest Service

(R01)
NORTHERN REGION

STAMPS, LOGOS, AND SEALS

△		
△		
△		
△		
NO.	REVISION / ISSUE	DATE

PROJECT NAME

LCIC
WINDOW
REPAIRS

HELENA-LEWIS AND
CLARK NATIONAL
FOREST



LEWIS & CLARK INTERPRETIVE
CENTER (LCIC)

DRAWING TITLE

ELEVATIONS
NORTH & EAST

DATE 02/04/2026	ARCHIVE NO.
DESIGNER R. STOVALL	DRAWING SHEET NO.
DRAWN R. STOVALL	04
CHECKED J. GANNON	
PROJECT NO.	SHEET 04 OF 10

3/2/26 16:30 DEWOODS C:\USERS\DEWOODS\BOX\R01_HLF 7000 ENGINEERING\HLF 7300 BUILDINGS AND OTHER STRUCTURES\PROJECTS\06_LCIC & GF 2026 WINDOWS\DRAWINGS\LCIC\WINDOWS - COPY.DWG;

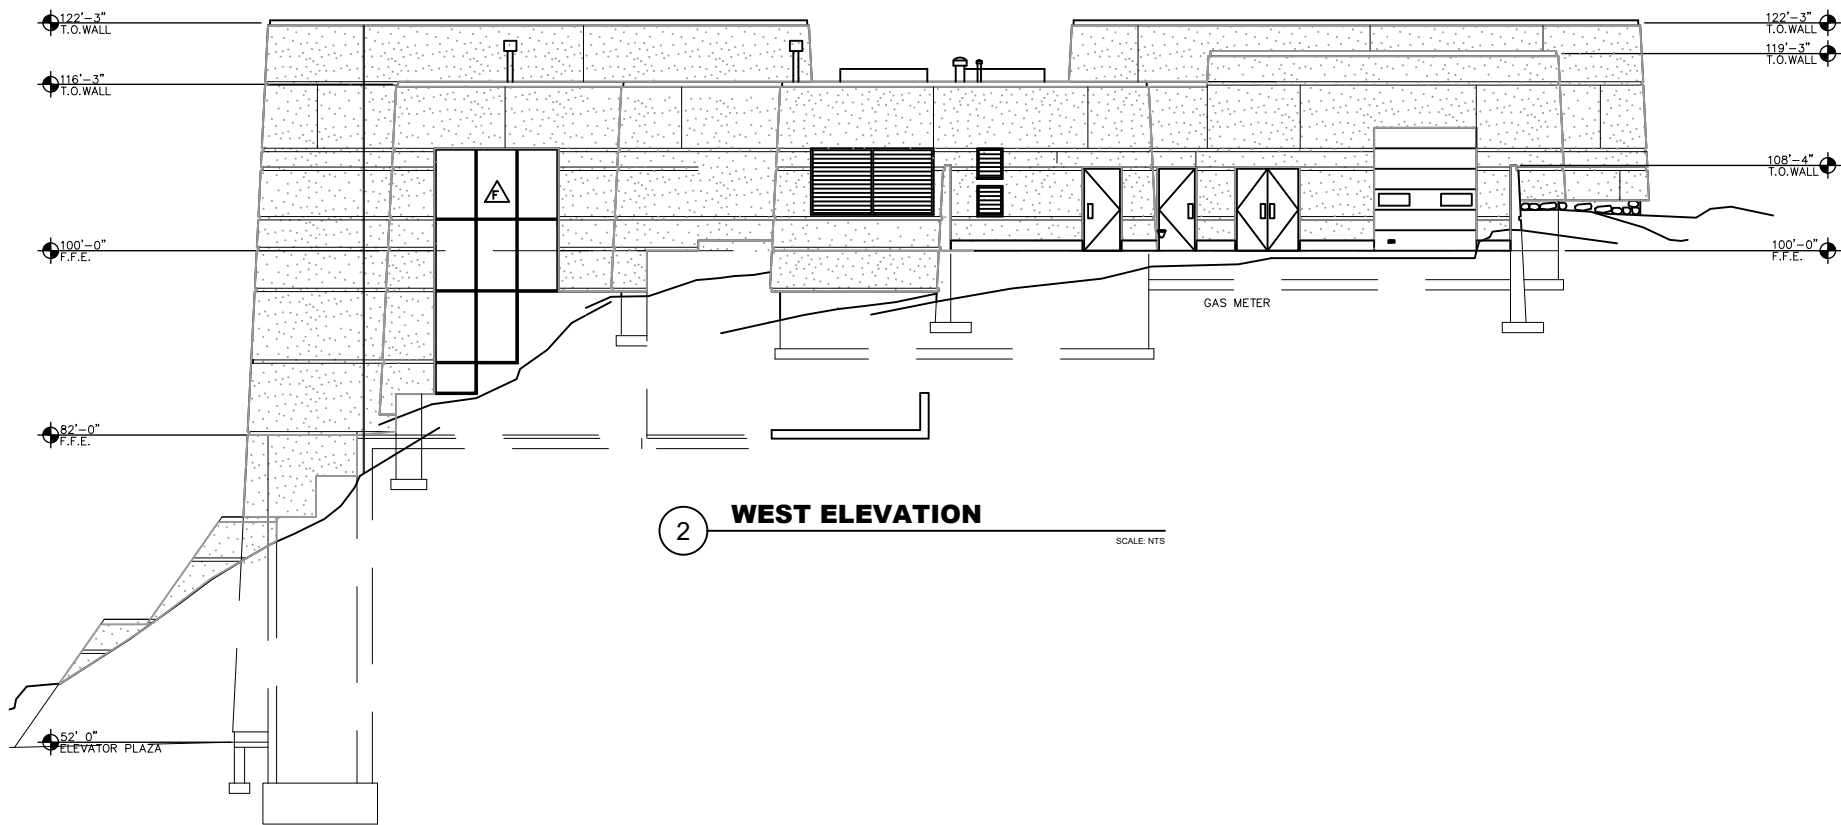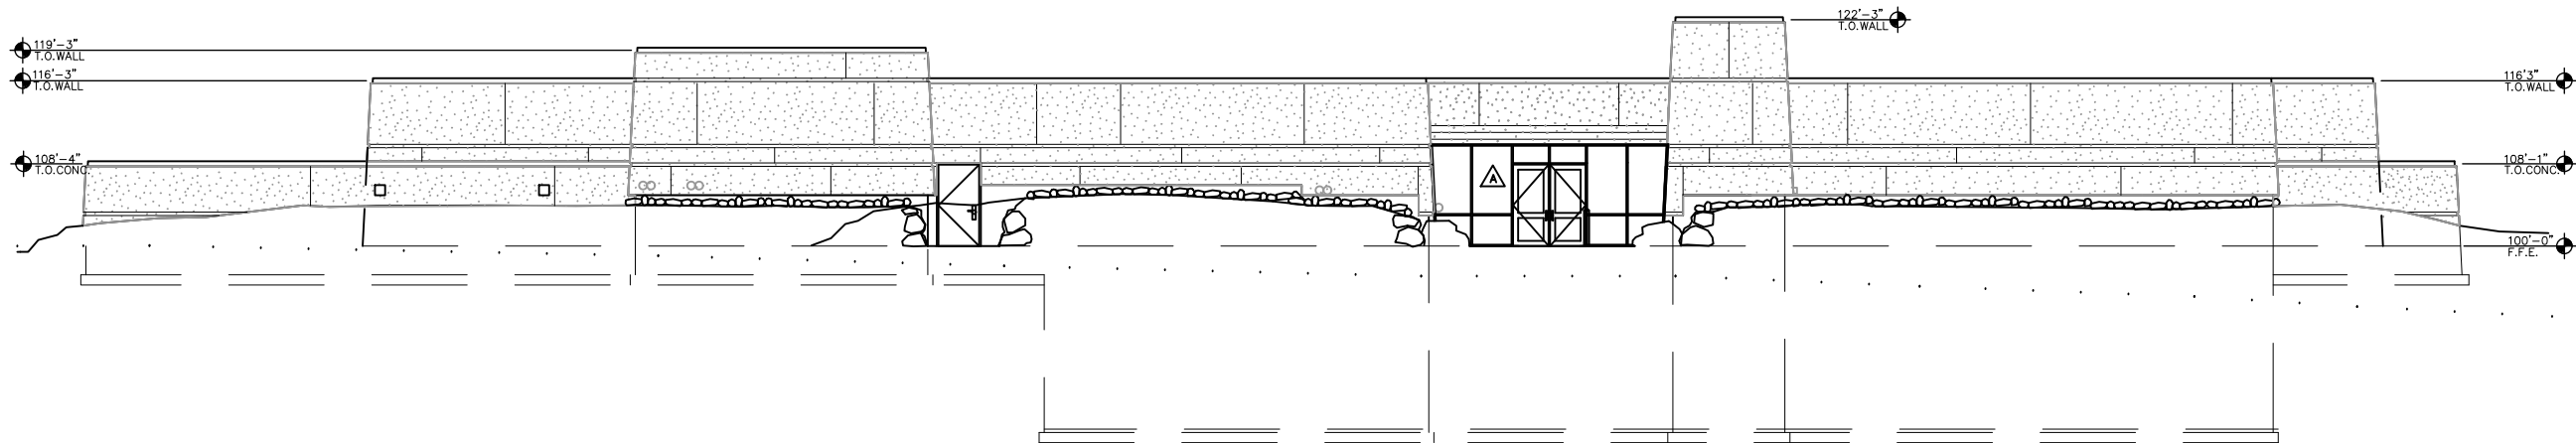

United States Department of Agriculture
Forest Service

(R01)
NORTHERN REGION

STAMPS, LOGOS, AND SEALS

△		
△		
△		
△		
NO.	REVISION / ISSUE	DATE

PROJECT NAME

LCIC
WINDOW
REPAIRS

HELENA-LEWIS AND
CLARK NATIONAL
FOREST

LEWIS & CLARK INTERPRETIVE
CENTER (LCIC)

DRAWING TITLE

ELEVATIONS
SOUTH & WEST

DATE 02/04/2026	ARCHIVE NO.
DESIGNER R. STOVALL	DRAWING SHEET NO. 05
DRAWN R. STOVALL	
CHECKED J. GANNON	
PROJECT NO.	SHEET 05 OF 10

A - MAIN ENTRY



MAIN ENTRY



WINDOW SCHEDULE		
A - MAIN ENTRY		
WINDOW	WIDTH	HEIGHT
A1	41"	25"
A2	38"	41"
A3	36"	41"
A4	38"	30"
A5	36"	30"
A6	42"	80"
A7	39"	34"
A8	44"	80"



SIDE WINDOWS



ENTRY WINDOWS AND DOORS

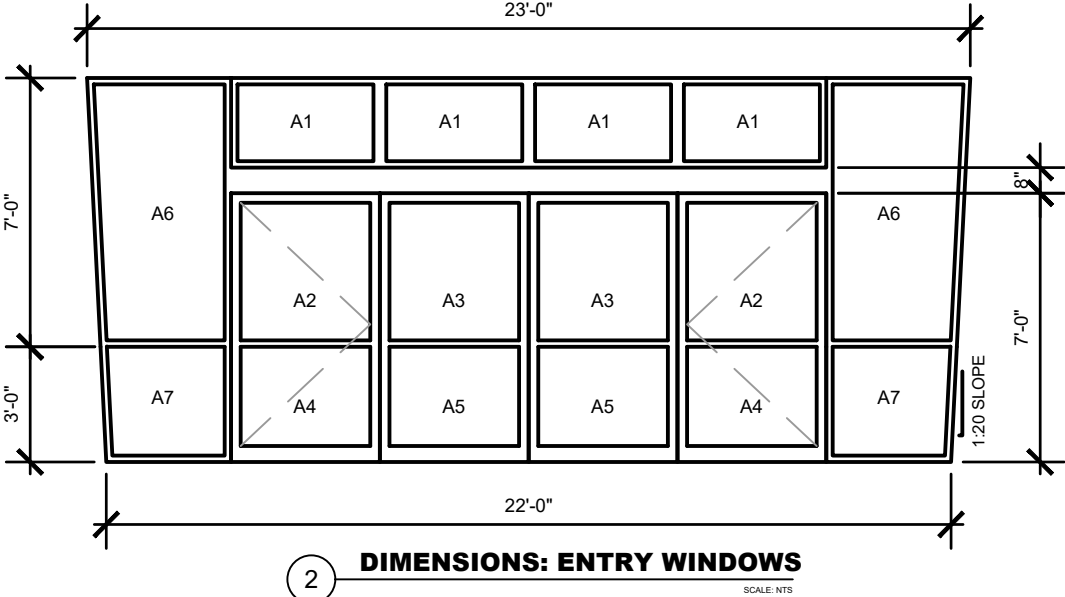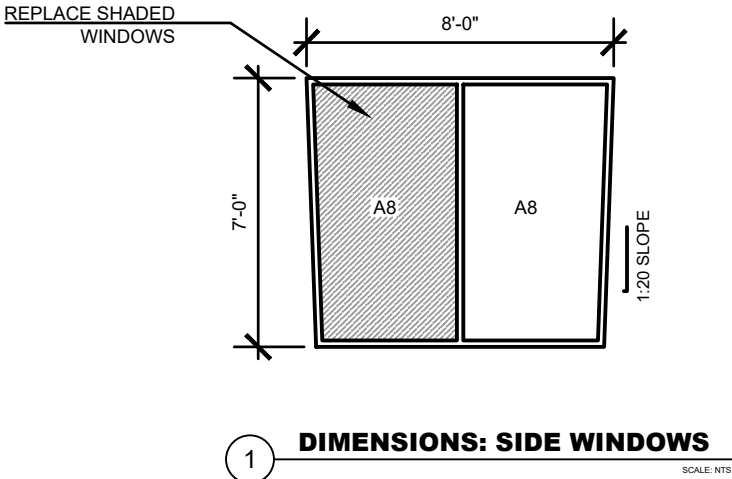

GENERAL NOTES:

1. DIMENSIONS ARE FOR ESTIMATING PURPOSES ONLY. CONTRACTOR SHALL VERIFY ALL DIMENSIONS PRIOR TO BIDDING OR ORDERING MATERIALS.



United States Department of Agriculture
Forest Service

(R01)
NORTHERN REGION

STAMPS, LOGOS, AND SEALS

NO.	REVISION / ISSUE	DATE

PROJECT NAME

LCIC
WINDOW
REPAIRS

HELENA-LEWIS AND
CLARK NATIONAL
FOREST



LEWIS & CLARK INTERPRETIVE
CENTER (LCIC)

DRAWING TITLE

DIMENSIONS
A

DATE 02/04/2026	ARCHIVE NO.
DESIGNER R. STOVALL	DRAWING SHEET NO. 06
DRAWN R. STOVALL	
CHECKED J. GANNON	
PROJECT NO.	SHEET 06 OF 10

B - LOBBY/GATHERING

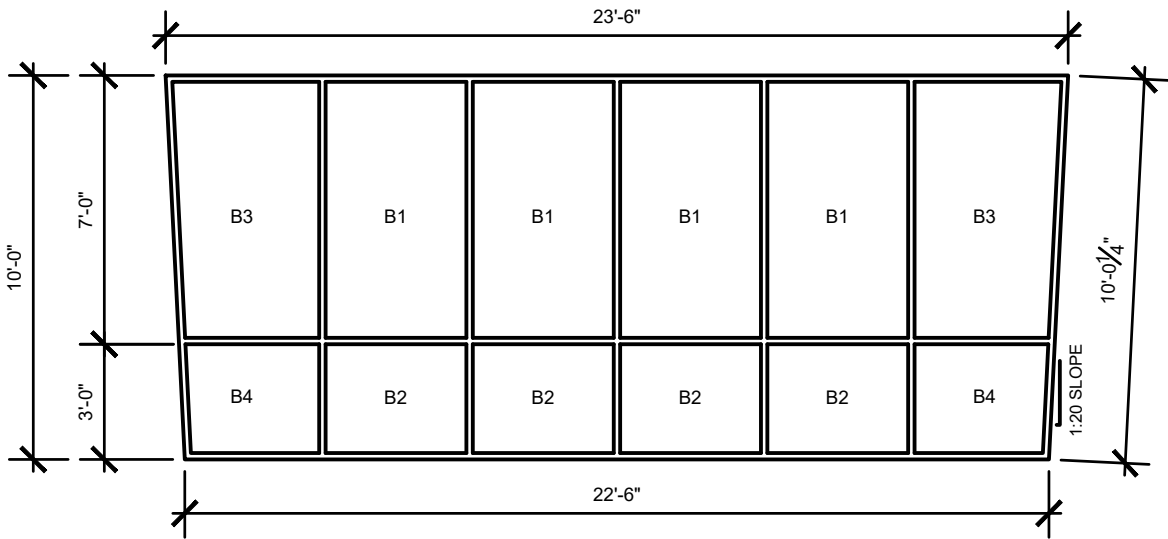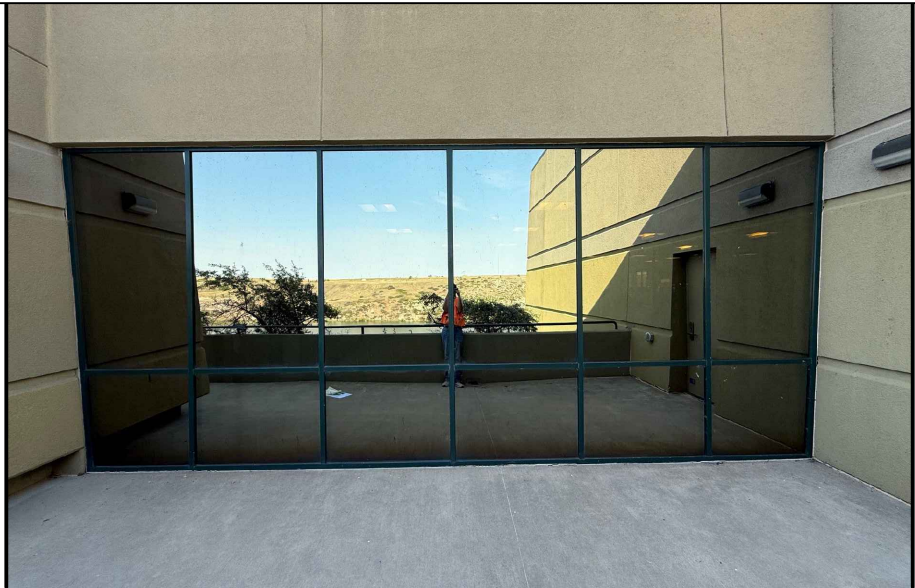

2 DIMENSIONS

WINDOWSCHEDULE		
B- LOBBY/GATHERING		
WINDOW/	WIDTH	HEIGHT
B1	46"	80"
B2	46"	34"
B3	42"	80"
B4	38"	34"

GENERAL NOTES:
1. DIMENSIONS ARE FOR ESTIMATING PURPOSES ONLY. CONTRACTOR SHALL VERIFY ALL DIMENSIONS PRIOR TO BIDDING OR ORDERING MATERIALS.

USDA

FOREST SERVICE

U.S.

DEPARTMENT OF AGRICULTURE

United States Department of Agriculture
Forest Service

(R01)
NORTHERN REGION

STAMPS, LOGOS, AND SEALS		
NO.	REVISION / ISSUE	DATE

PROJECT NAME

LCIC
WINDOW
REPAIRS

HELENA-LEWIS AND
CLARK NATIONAL
FOREST

LEWIS & CLARK INTERPRETIVE
CENTER (LCIC)


DRAWING TITLE

DIMENSIONS
B

DATE 02/04/2026	ARCHIVE NO.
DESIGNER R. STOVALL	DRAWING SHEET NO. 07
DRAWN R. STOVALL	
CHECKED J. GANNON	
PROJECT NO.	SHEET 07 OF 10

3/1/26 13:00 NZUCKER C:\USERS\NZUCKER\BUD\01 HLF 7000 ENGINEERING\HLF 7300 BUILDINGS AND OTHER STRUCTURES\PROJECTS\08_LCIC & GF\2026 WINDOWS\DRAWINGS\LCIC WINDOWS.DWG

C - PORTAGE EXHIBIT (NORTH)

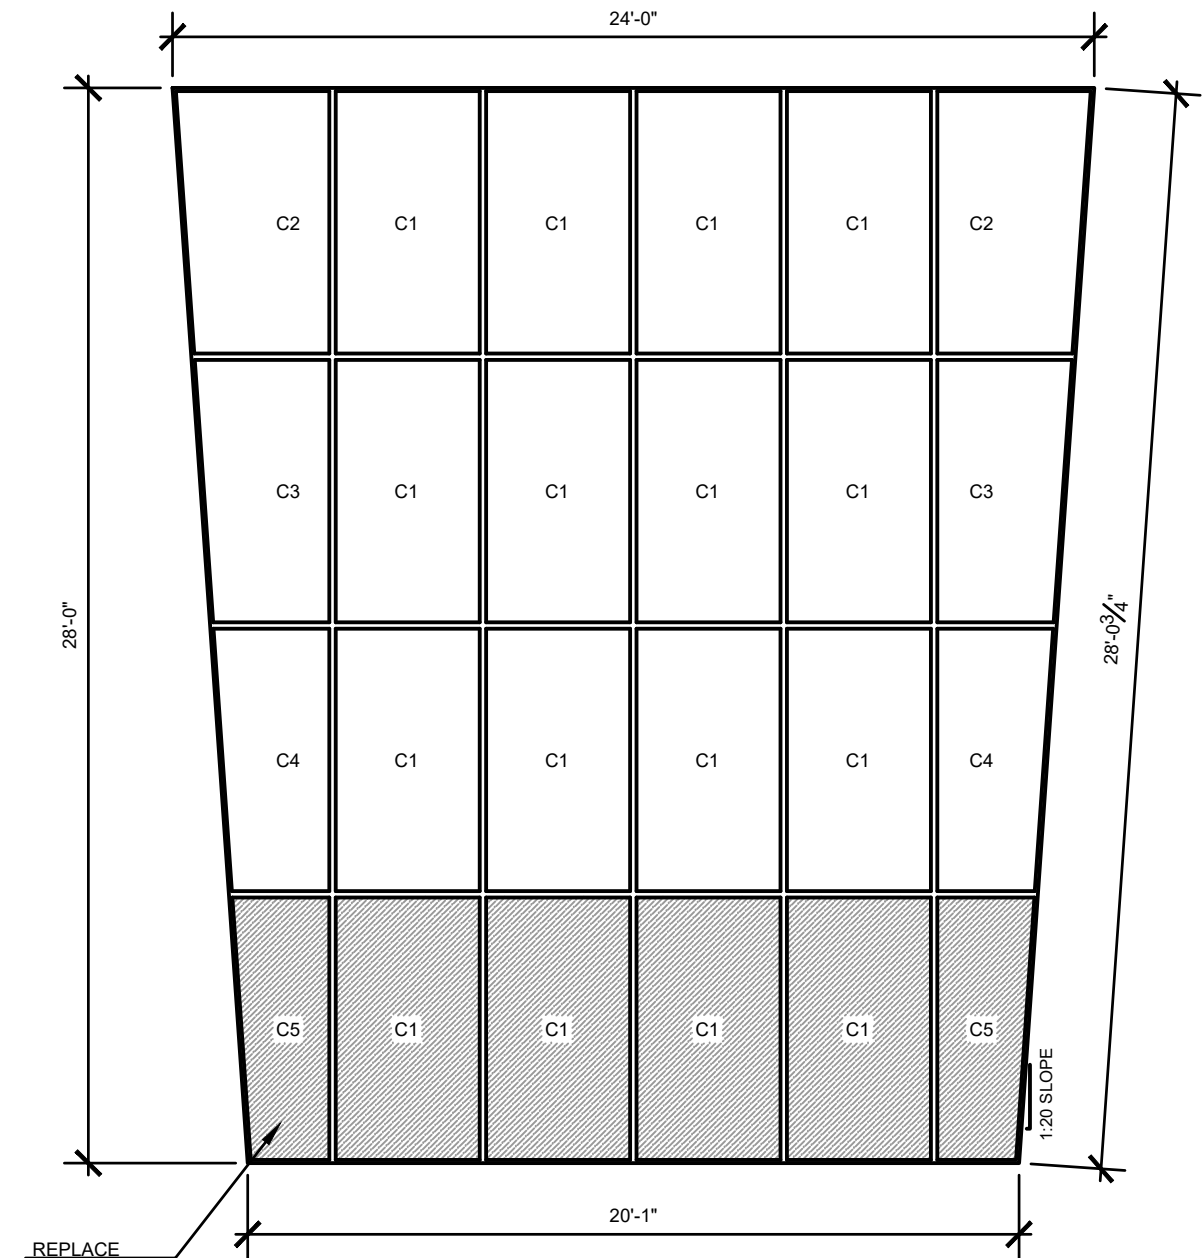

1 DIMENSIONS

WINDOW SCHEDULE		
C - PORTAGE EXHIBIT (N)		
WINDOW	WIDTH	HEIGHT
C1	47"	82"
C2	46"	82"
C3	40"	82"
C4	34"	82"
C5	28"	82"

GENERAL NOTES:
1. DIMENSIONS ARE FOR ESTIMATING PURPOSES ONLY. CONTRACTOR SHALL VERIFY ALL DIMENSIONS PRIOR TO BIDDING OR ORDERING MATERIALS.

C - PORTAGE EXHIBIT (NORTH)



United States Department of Agriculture
Forest Service

(R01)
NORTHERN REGION

STAMPS, LOGOS, AND SEALS

△		
△		
△		
△		
NO.	REVISION / ISSUE	DATE

PROJECT NAME

LCIC
WINDOW
REPAIRS

HELENA-LEWIS AND
CLARK NATIONAL
FOREST



LEWIS & CLARK INTERPRETIVE
CENTER (LCIC)

DRAWING TITLE

DIMENSIONS
C

DATE 02/04/2026	ARCHIVE NO.
DESIGNER R. STOVALL	DRAWING SHEET NO. 08
DRAWN R. STOVALL	
CHECKED J. GANNON	
PROJECT NO.	SHEET 08 OF 10

D - GIFT SHOP

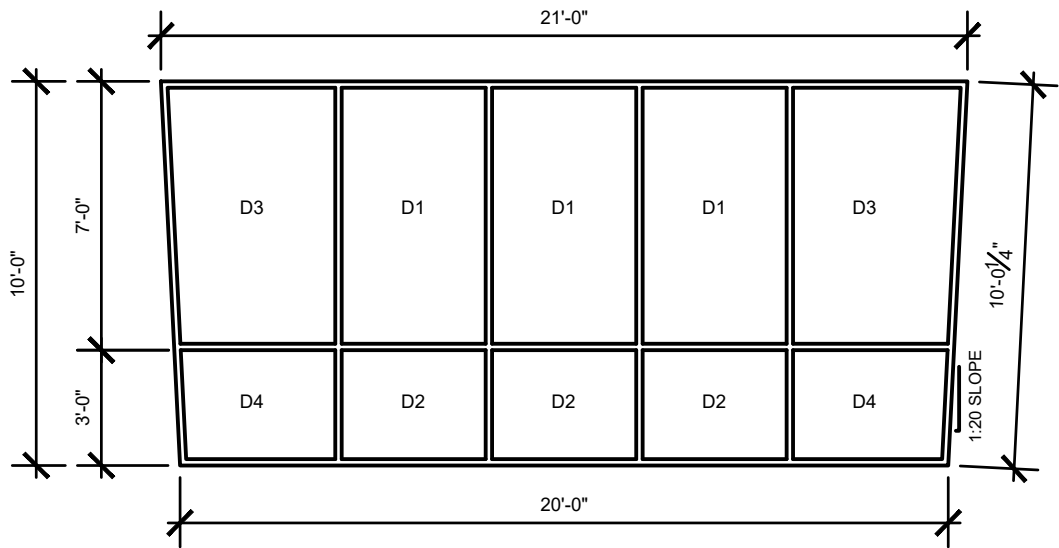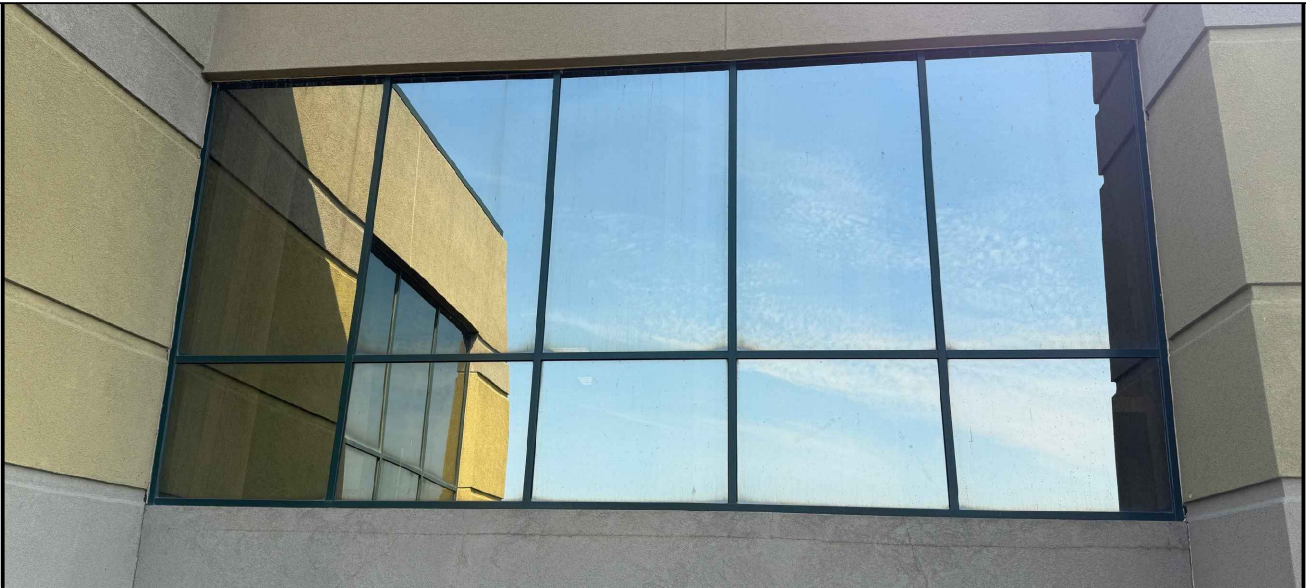


1 DIMENSIONS

SCALE: NTS

WINDOW SCHEDULE		
D - GIFT SHOP		
WINDOW	WIDTH	HEIGHT
D1	46"	80"
D2	46"	34"
D3	42"	80"
D4	38"	34"

GENERAL NOTES:
1. DIMENSIONS ARE FOR ESTIMATING PURPOSES ONLY. CONTRACTOR SHALL VERIFY ALL DIMENSIONS PRIOR TO BIDDING OR ORDERING MATERIALS.

E - ADMIN OFFICES

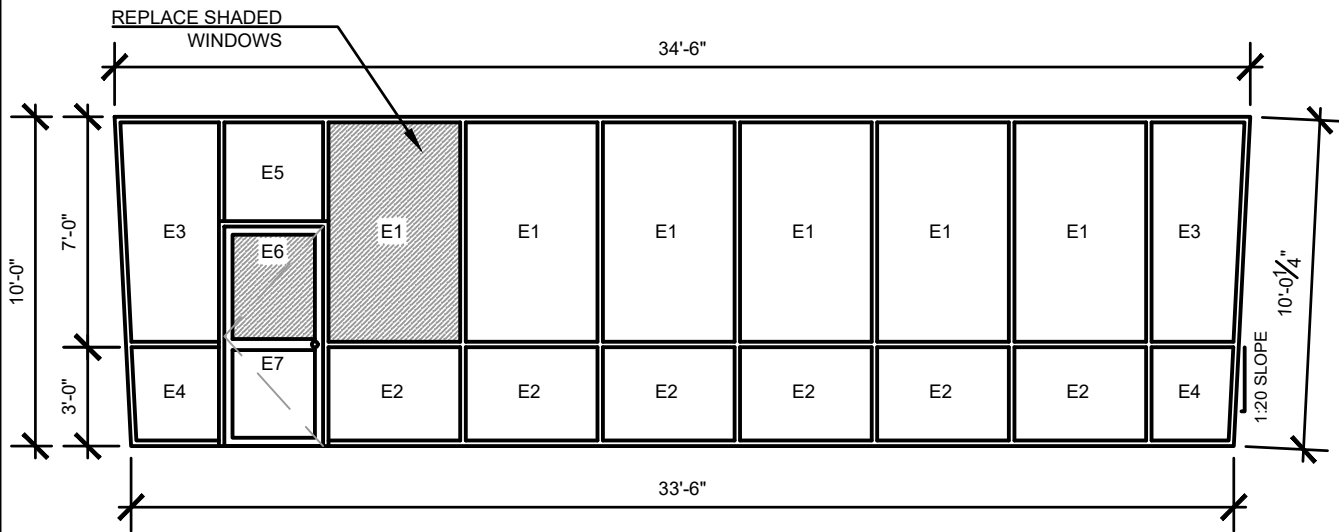

2 DIMENSIONS

SCALE: NTS

WINDOW SCHEDULE		
E - ADMIN OFFICES		
WINDOW	WIDTH	HEIGHT
E1	48"	80"
E2	48"	34"
E3	35"	80"
E4	32"	34"
E5	44"	19"
E6	30.5"	50"
E7	30.5"	27"



United States Department of Agriculture
Forest Service

(R01)
NORTHERN REGION

STAMPS, LOGOS, AND SEALS

NO.	REVISION / ISSUE	DATE

PROJECT NAME

LCIC
WINDOW
REPAIRS

HELENA-LEWIS AND
CLARK NATIONAL
FOREST

LEWIS & CLARK INTERPRETIVE
CENTER (LCIC)


DRAWING TITLE

DIMENSIONS
D&E

DATE 02/04/2026	ARCHIVE NO.
DESIGNER R. STOVALL	DRAWING SHEET NO. 09
DRAWN R. STOVALL	
CHECKED J. GANNON	
PROJECT NO.	SHEET 09 OF 10

3/1/26 13:00 NZUCKER C:\USERS\NZUCKER\BUDGET\1 HLF 7000 ENGINEERING\HLF 7300 BUILDINGS AND OTHER STRUCTURES\PROJECTS\08_LCIC & GE\2026 WINDOWS\DRAWINGS\LCICWINDOWS.DWG

F - PORTAGE EXHIBIT (WEST)

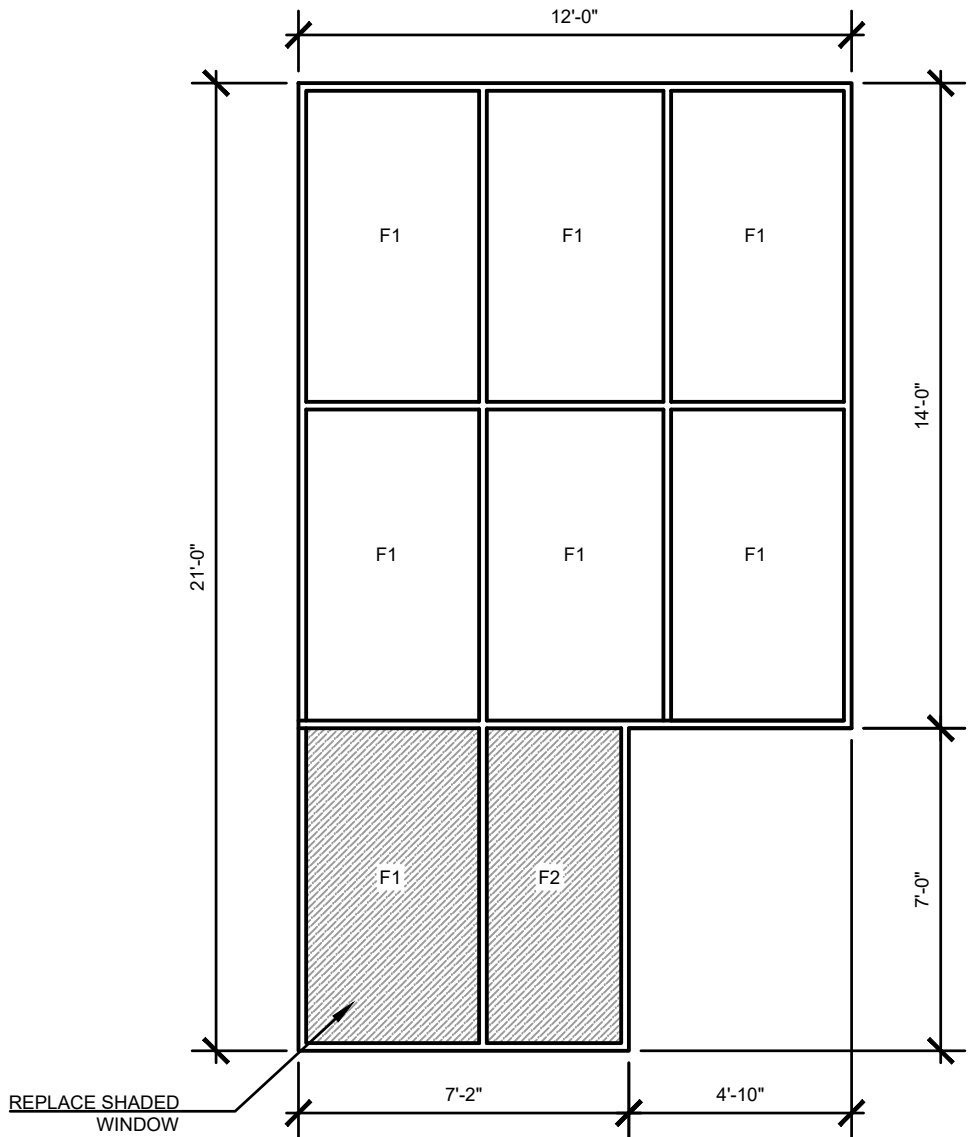

1 DIMENSIONS

SCALE: NTS

WINDOWSCHEDULE		
F - PORTAGE EXHIBIT (W)		
WINDOW	WIDTH	HEIGHT
F1	46"	82"
F2	35"	82"

GENERAL NOTES:

- DIMENSIONS ARE FOR ESTIMATING PURPOSES ONLY. CONTRACTOR SHALL VERIFY ALL DIMENSIONS PRIOR TO BIDDING OR ORDERING MATERIALS.

F - PORTAGE EXHIBIT (WEST)



United States Department of Agriculture
Forest Service

(R01)
NORTHERN REGION

STAMPS, LOGOS, AND SEALS

△		
△		
△		
△		
NO.	REVISION / ISSUE	DATE

PROJECT NAME

LCIC
WINDOW
REPAIRS

HELENA-LEWIS AND
CLARK NATIONAL
FOREST

LEWIS & CLARK INTERPRETIVE
CENTER (LCIC)

DRAWING TITLE

DIMENSIONS
F

DATE 02/04/2026	ARCHIVE NO.
DESIGNER R. STOVALL	DRAWING SHEET NO. 10
DRAWN R. STOVALL	
CHECKED J. GANNON	
PROJECT NO.	SHEET 10 OF 10